

# INTERIOR FINISH SCHEDULE

ROOM - TOILET (for Rector's Sacristy)  
 RM. No. - 124  
 FLOOR - CEMENT- INTEGRAL COLOR  
 BASE - WOOD- FLUSH  
 WALLS - INTERIOR STUCCO  
 WALL FINISH - "C" See Sh.#2  
 CEILING - INTERIOR STUCCO  
 CEILING HEIGHT - 8'-0"  
 CEIL. FINISH - "C" See Sh.#2  
 WARDROBE - 1/2" PLYWD. WALLS  
 (2 SIDES) & FLOOR ON  
 2"x3" S4S FRAME - 3/4" WD.  
 SHELF - WD. POLE  
 WOOD TRIM FIN. - "C" See Sh.#2

DOOR-OPNG. 120-A - TYPE "C" WOOD  
 2'-4"x7'-0"x1 3/4" - WOOD FRAME &  
 TRIM - ALUM. STRIP THRESHOLD  
 1/2" CLEAR AT BOTTOM OF DOOR.  
 PAINT FIN. - "E" See Sh.#2



# TOILET FIXTURES

TOILET - STANDARD "ONE-PIECE" ROUND FRONT F2005E  
 SIPHON VORTEX COMB'N. TANK AND BOWL WITH B1945  
 ADJUSTOR CONTROL WITH BACK FLOW PREVENTER -  
 SUPPLY PIPE WITH STOP TO WALL - CAPS - SCREWS ETC.  
 LAVATORY - STD. "LUCERNE" F369A-20"x18" VIT-  
 REOUS CHINA - CAST-IN SOAP DISH - WALL HANGERS -  
 B-729 3/8" SUPPLYs WITH STOPS TO WALL - B960 1/4" P-TRAP -  
 COMB. SUPPLY FITTING "SPRING-FLO" AERATOR - POP-UP DRAIN.  
 BATH CABINET - HALL-MACK #HL1618 - WALL OPENING  
 14"x24"x4" - CHROME BOUND MIRROR DOOR - OPEN  
 SHELF BELOW.  
 PAPER HOLDER - HALL-MACK #675 WITH CHROME ROLLER  
 TOWEL BAR - HALL-MACK #694 3/4" SQUARE CHROME-  
 PLATED SEAMLESS BRASS BAR 24"  
 VENTILATING BLOWER - CLIPPER #1201 SINGLE  
 WHEEL HORIZ. DISCH. 100 CFM - 60 CYC. - 1/75 HP - 4" &  
 METAL VENT DUCT ABOVE CEILING - TRANSITION TO  
 6"x6" VENT DUCT TO EXTERIOR - TOP OF DUCT AT TOP  
 OF 6" WIDE x 12" HIGH SCREENED METAL LOUVER  
 VENT AT EXT. - BOTTOM OF DUCT SPLAYED DOWN  
 TO BOT. OF LOUV. VENT & FLASHED TO EXTERIOR.  
 LOUVER VENT CENTERED VERTICALLY ON 18"  
 HIGH PANEL OF EXTERIOR VENEER AS SHOWN  
 ROCKWOOL BATS TO 8'-6" HEIGHT WHERE SHOWN

# PLUMBING NOTES

TOILET - 4" SOIL TO 4" SOIL - 4" VENT THRU ROOF  
 3/4" C.V. SUPPLY TO WALL  
 LAVATORY - 3/4" H.W. & 3/4" C.V. SUPPLY UNDER SLAB TO WALL  
 2" WASTE TO 4" SOIL - 1 1/2" VENT OVER TO 4" VENT ABOVE CEIL.

SEE PLAN SHEET NO 3 FOR TIE-IN

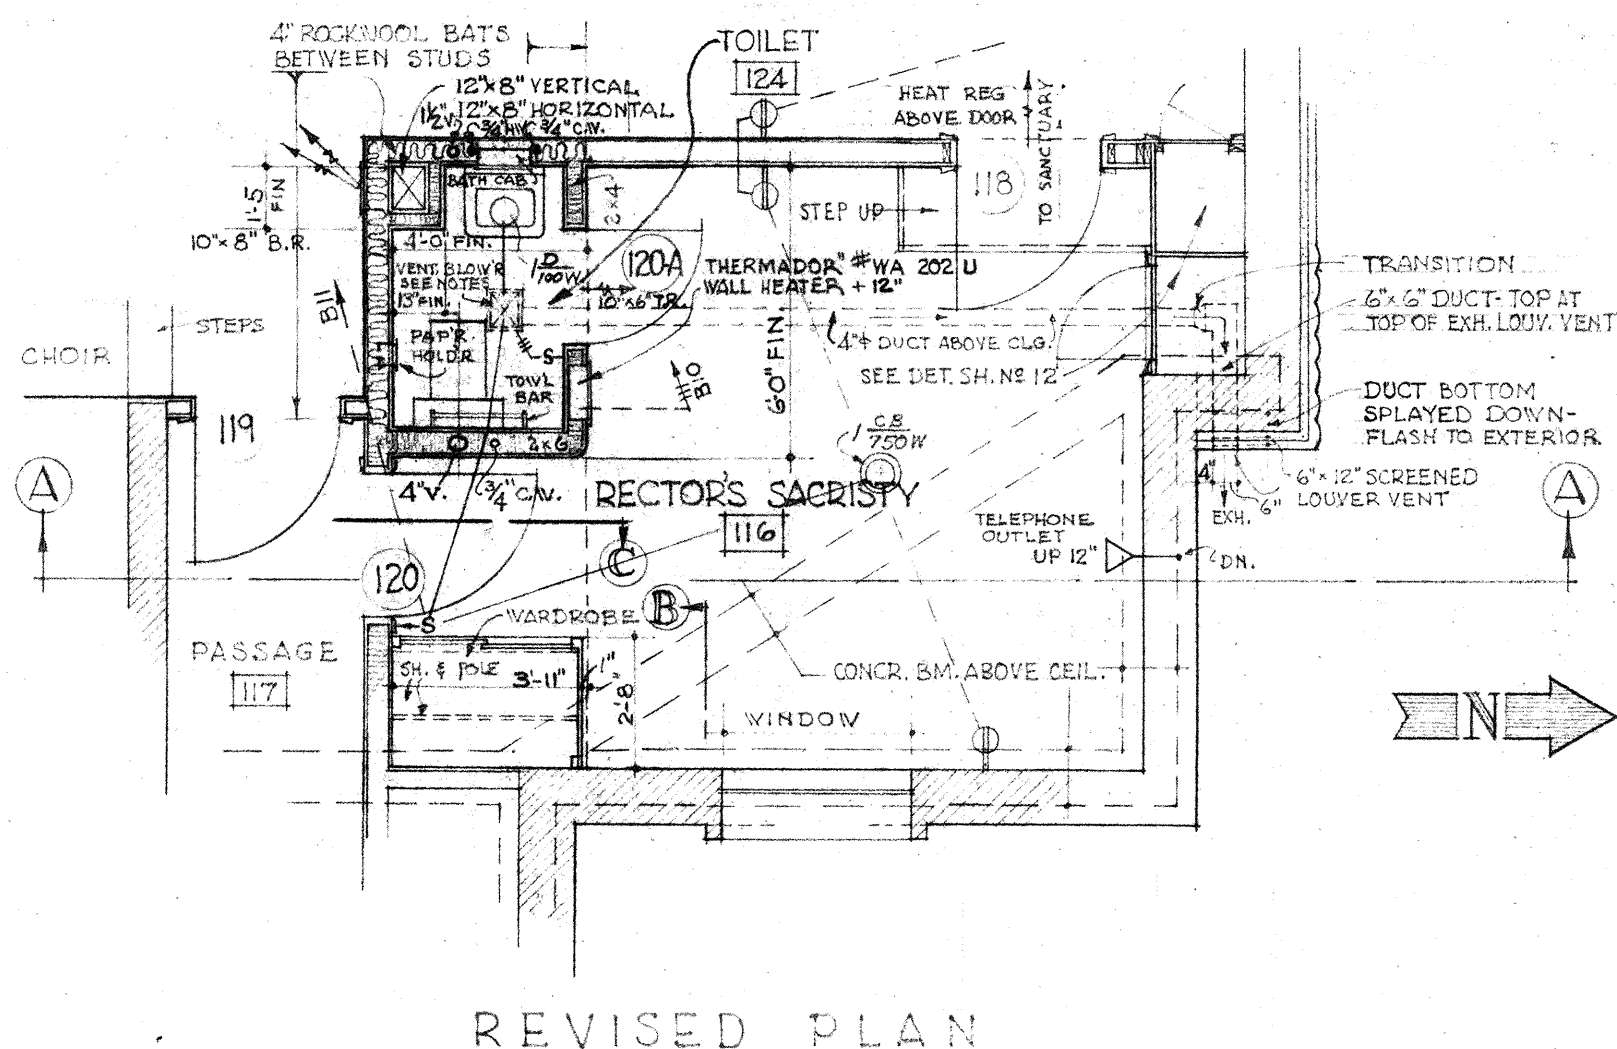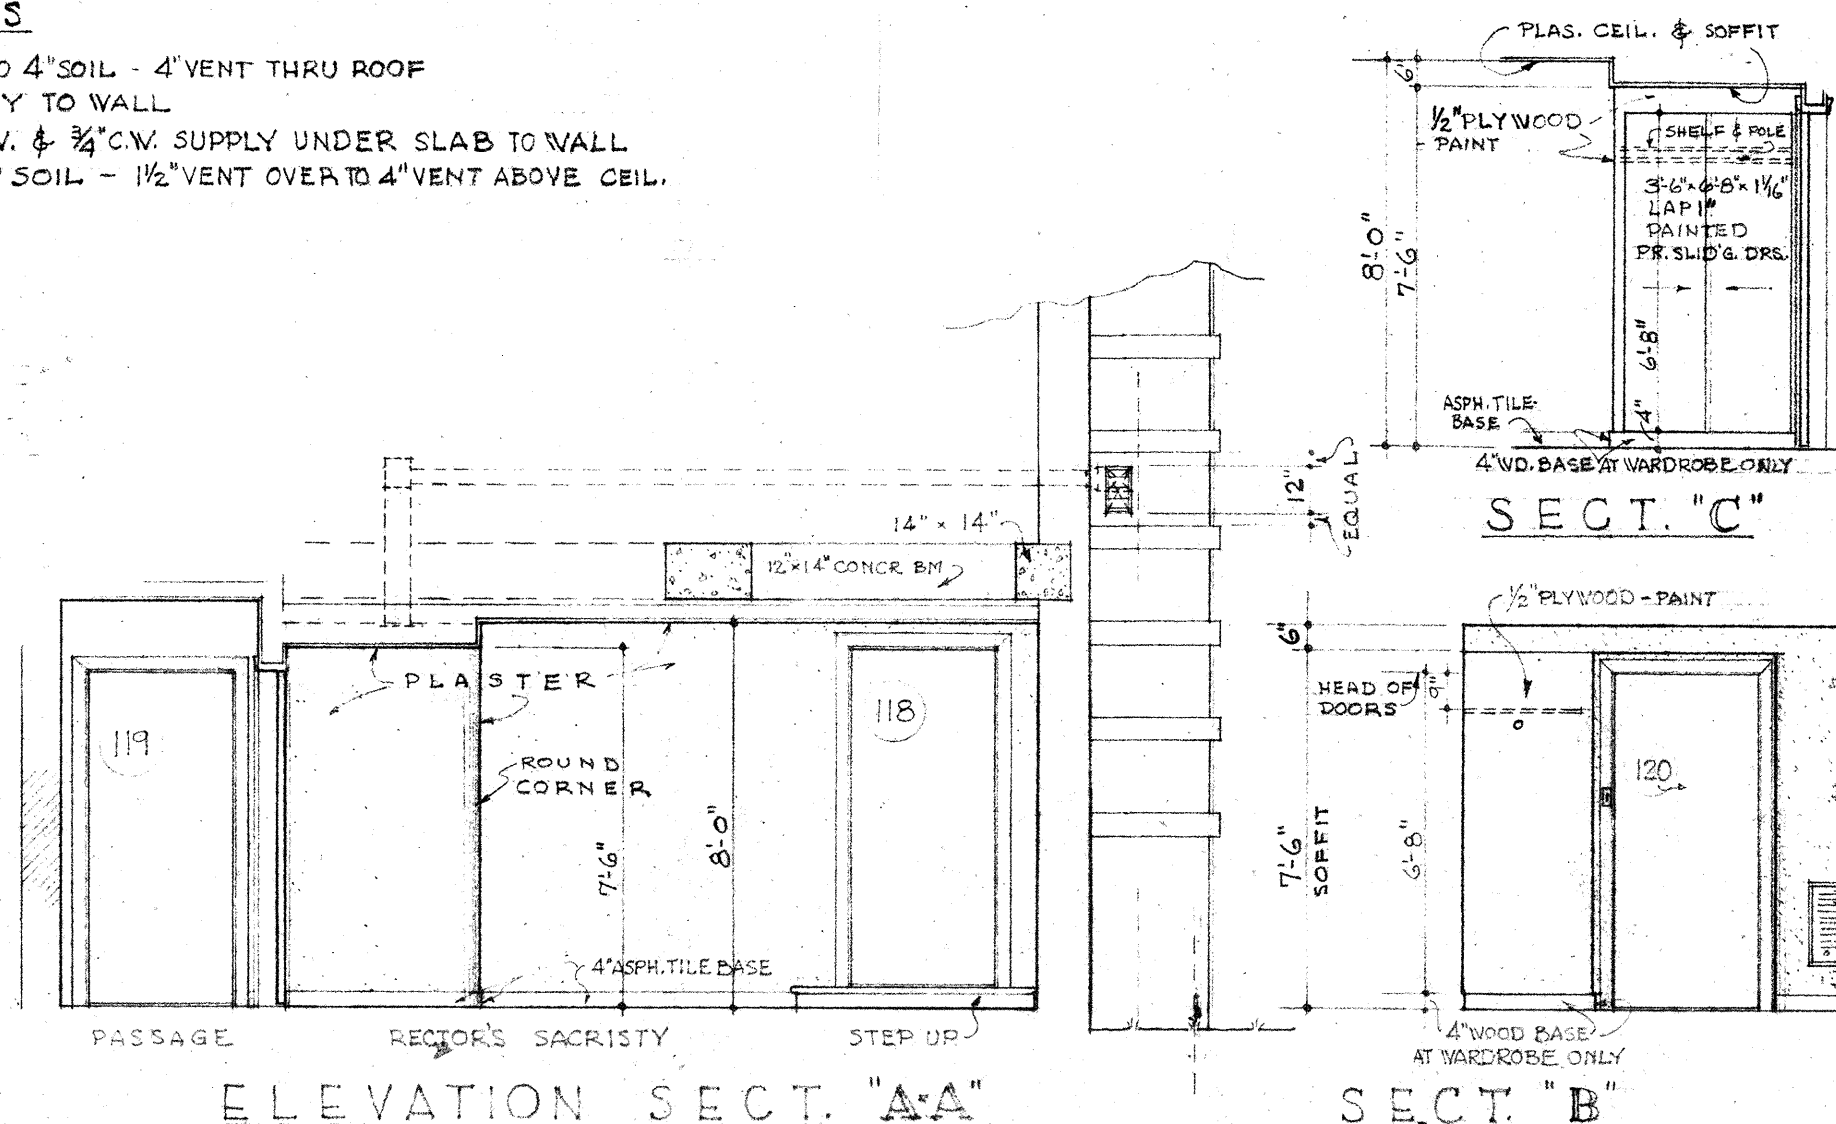

SCALE 1/4" = 1'-0"

**AUSTIN FIELD & IRY**  
 Architects

2311 WEST THIRD STREET

LOS ANGELES 5, CALIFORNIA

DUNKIRK 8-1326

TOILET FOR RECTOR'S SACRISTY  
 ST. EDMUND'S EPISCOPAL CHURCH  
 SAN MARINO - CALIFORNIA

DATE 10 JAN '52  
 COMM. 1061  
 SHEET NUMBER

**R-4**