


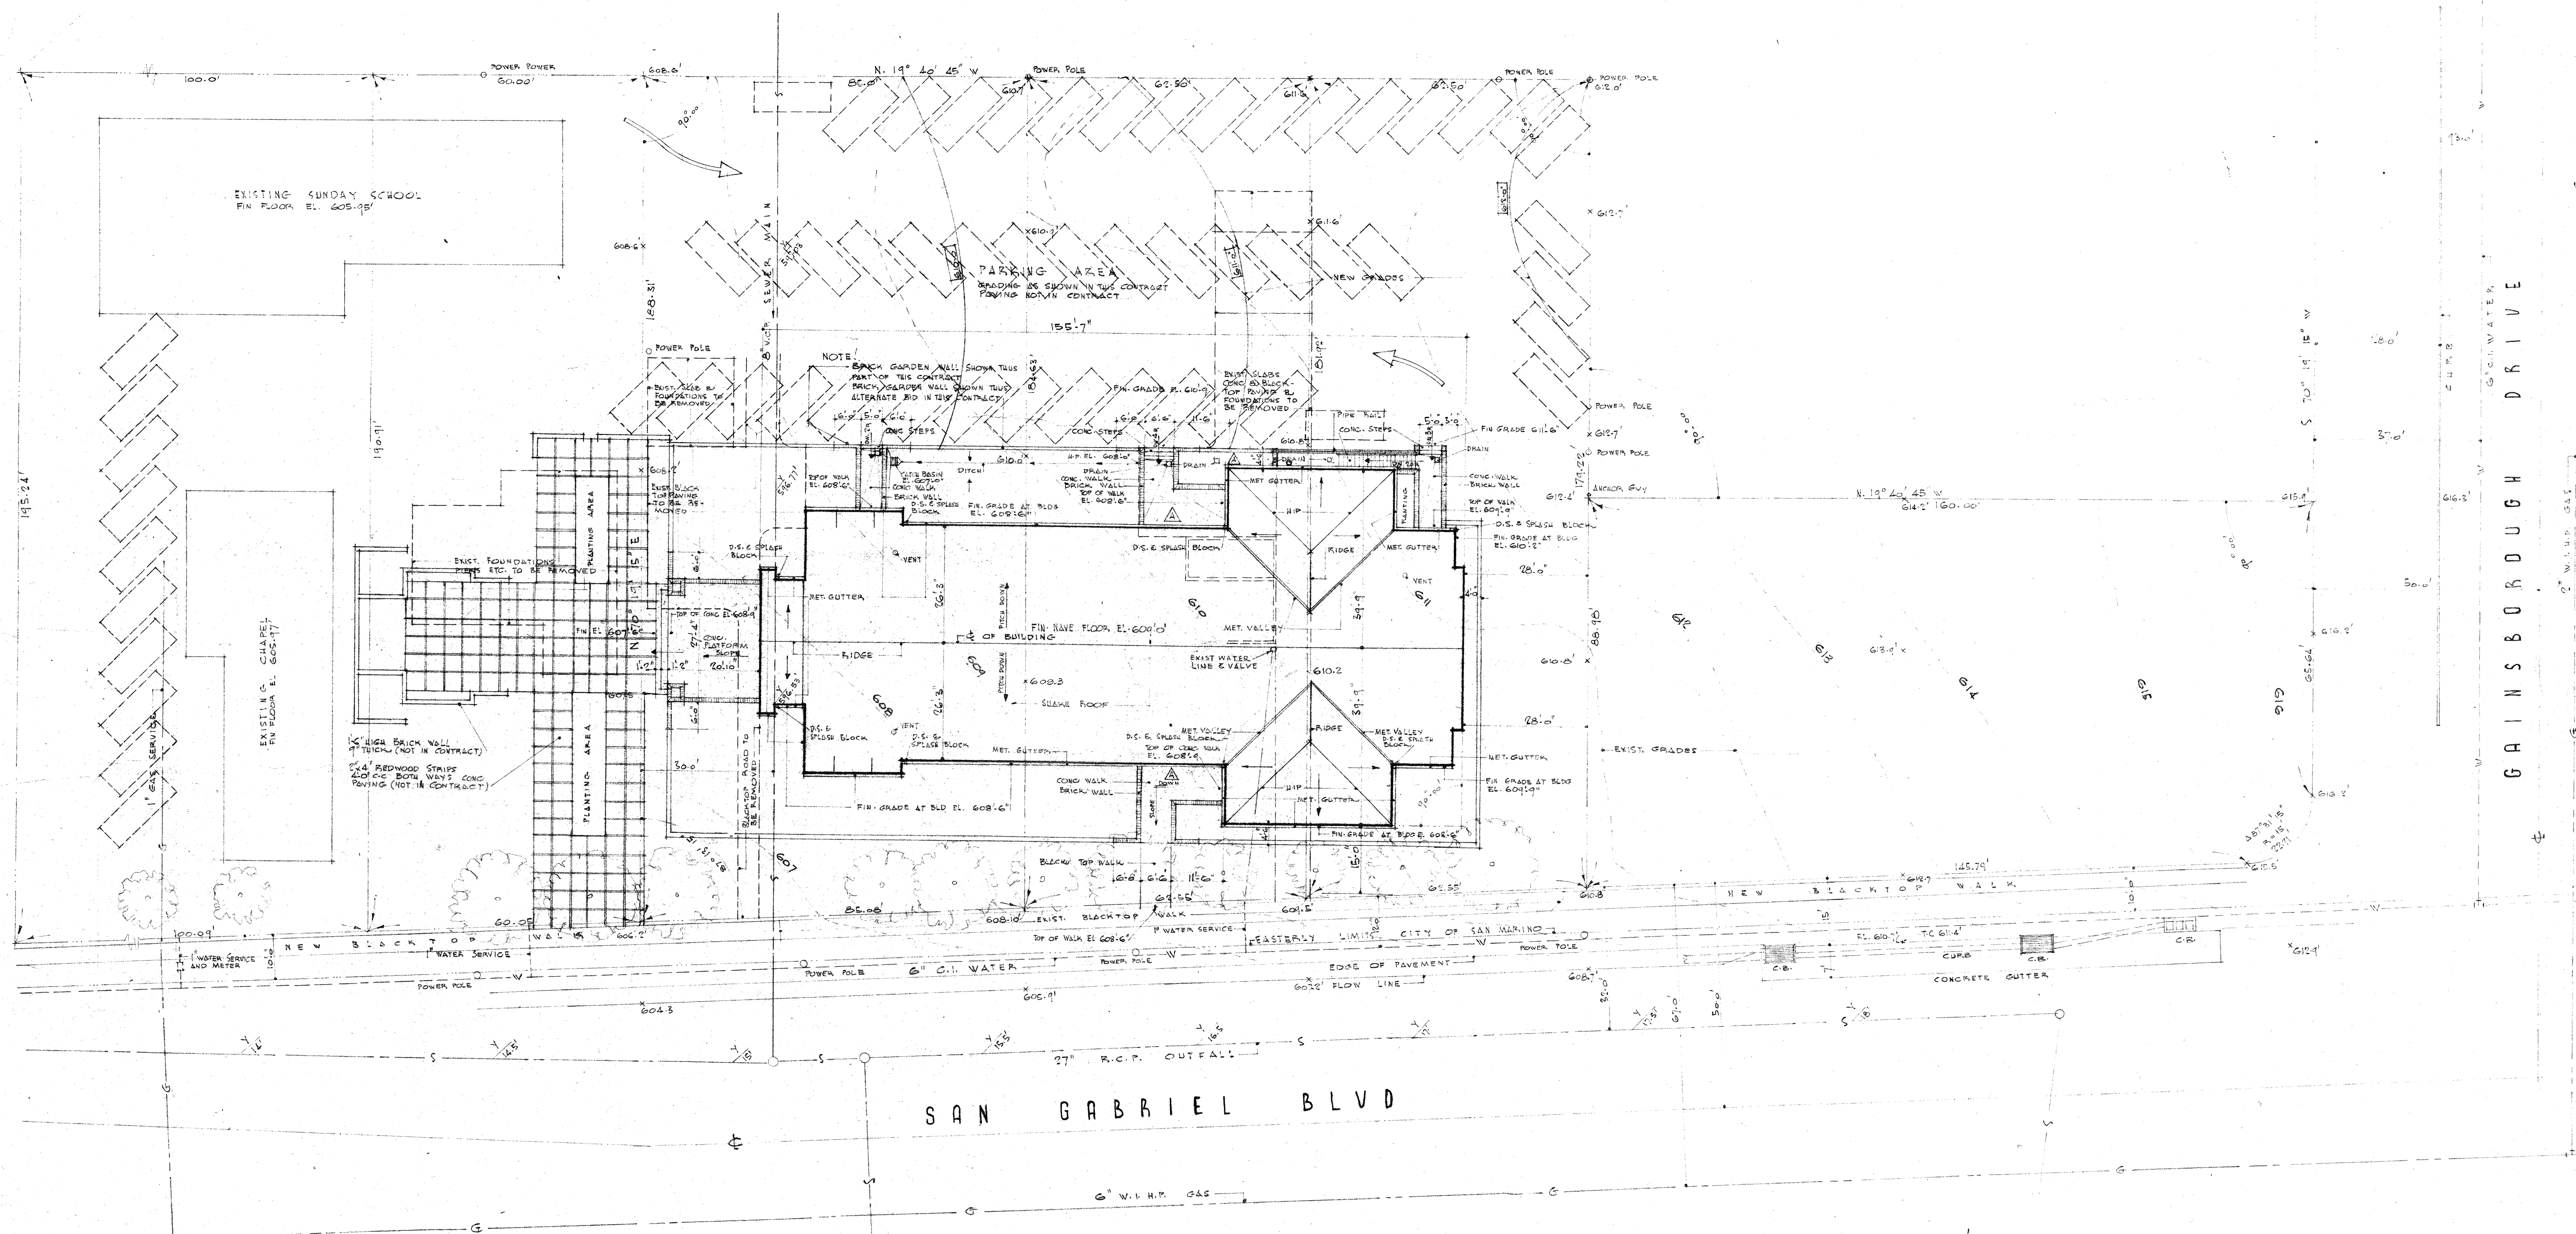

NOTE!
ALL TREES SHOWN & PLANTING IS GENERAL TO REMAIN
OR BE REMOVED AT THE DIRECTION OF THE ARCHITECTS

PLOT PLAN MADE FROM SURVEY FURNISHED BY BARNETT
HOPKIN & SMITH CIVIL ENGS & LAND SURVEYORS, DATED 25-JUN-51
BENCH MARK: BOLT IN E CURB RETURN S.E. CORNER DUNSTON
DRIVE & SAN GABRIEL BLVD. EL. 546.48' U.S.G.S. DATUM
FOR CONSTRUCTION BENCHMARK USE FLOOR OF EXISTING
CHURCH EL. 605.17'
PORTION LOT 'E' TR. 8839 M.B. 146-7
SAN MARINO, CALIF.

SCALE - 1/4" = 1'-0"

Remarks

Revisions Engineers Approvals

AUSTIN FIELD & IRY
architects
2311 WEST THIRD STREET • LOS ANGELES 5, CALIFORNIA • DUNKIRK 8-1326

PLOT AND ROOF PLAN
ST EDMUNDS EPISCOPAL CHURCH
SAN MARINO CALIF.

DATE: AUG-51
COMM: 1061
SHEET NUMBER: 1