


INTERIOR FINISH SCHEDULE											
NO.	ROOM	FLOOR	BASE	WALL FINISH				CEILING			
				NORTH	EAST	SOUTH	WEST	MAT'L	HGT.	FINISH	
101	BASEMENT	CEMENT	—	CONC.	CONC.	CONC.	CONC.	CONC.	8'-0"	C	
102	LADES	ASPHALT TILE	4" ASPH. TILE	INT. STUCCO	INT. STUCCO	INT. STUCCO	INT. STUCCO	INT. STUCCO	8'-0"	C	* PARASTONE PATTERNS B14 COLOR BASE
103	TOILET	CERAMIC TILE	6" CERAMIC TILE	INT. STUCCO	INT. STUCCO	INT. STUCCO	INT. STUCCO	INT. STUCCO	8'-0"	C	
104	FOYER	PARADE	6" PARADE	INT. STUCCO	INT. STUCCO	INT. STUCCO	INT. STUCCO	INT. STUCCO	8'-0"	C	* PARASTONE PATTERNS B14 DESIGN TO PARADE WALLS
105	CLOSET	CEMENT	WOOD	INT. STUCCO	INT. STUCCO	INT. STUCCO	INT. STUCCO	INT. STUCCO	8'-0"	C	
106	WASH	ASPHALT TILE	4" ASPH. TILE	INT. STUCCO	INT. STUCCO	INT. STUCCO	INT. STUCCO	INT. STUCCO	8'-0"	C	* PARASTONE PATTERNS B14 DESIGN TO PARADE WALLS
107	TOILET	CERAMIC TILE	6" CERAMIC TILE	INT. STUCCO	INT. STUCCO	INT. STUCCO	INT. STUCCO	INT. STUCCO	8'-0"	C	
108	NAVE	INTEGRAL COLOR	WOOD	INT. STUCCO	INT. STUCCO	INT. STUCCO	INT. STUCCO	INT. STUCCO	8'-0"	C	
109	VESTIBULE	INTEGRAL COLOR	WOOD	INT. STUCCO	INT. STUCCO	INT. STUCCO	INT. STUCCO	INT. STUCCO	8'-0"	C	
110	PASSAGE	INTEGRAL COLOR	WOOD	INT. STUCCO	INT. STUCCO	INT. STUCCO	INT. STUCCO	INT. STUCCO	8'-0"	C	
111	PASSAGE	INTEGRAL COLOR	WOOD	INT. STUCCO	INT. STUCCO	INT. STUCCO	INT. STUCCO	INT. STUCCO	8'-0"	C	
112	ORGAN	CEMENT	WOOD	INT. STUCCO	INT. STUCCO	INT. STUCCO	INT. STUCCO	INT. STUCCO	8'-0"	C	
113	SANCTUARY	ASPHALT TILE	4" ASPH. TILE	INT. STUCCO	INT. STUCCO	INT. STUCCO	INT. STUCCO	INT. STUCCO	8'-0"	C	
114	CHOR	INTEGRAL COLOR	WOOD	INT. STUCCO	INT. STUCCO	INT. STUCCO	INT. STUCCO	INT. STUCCO	8'-0"	C	
115	SANCTUARY	INTEGRAL COLOR	WOOD	INT. STUCCO	INT. STUCCO	INT. STUCCO	INT. STUCCO	INT. STUCCO	8'-0"	C	
116	ORGAN	CEMENT	WOOD	INT. STUCCO	INT. STUCCO	INT. STUCCO	INT. STUCCO	INT. STUCCO	8'-0"	C	
117	RECORDS	CEMENT	WOOD	INT. STUCCO	INT. STUCCO	INT. STUCCO	INT. STUCCO	INT. STUCCO	8'-0"	C	
118	PASSAGE	INTEGRAL COLOR	WOOD	INT. STUCCO	INT. STUCCO	INT. STUCCO	INT. STUCCO	INT. STUCCO	8'-0"	C	
119	PASSAGE	INTEGRAL COLOR	WOOD	INT. STUCCO	INT. STUCCO	INT. STUCCO	INT. STUCCO	INT. STUCCO	8'-0"	C	
120	PASSAGE	INTEGRAL COLOR	WOOD	INT. STUCCO	INT. STUCCO	INT. STUCCO	INT. STUCCO	INT. STUCCO	8'-0"	C	
121	VESTIBULE	INTEGRAL COLOR	WOOD	INT. STUCCO	INT. STUCCO	INT. STUCCO	INT. STUCCO	INT. STUCCO	8'-0"	C	
122	CLOSET	CEMENT	WOOD	INT. STUCCO	INT. STUCCO	INT. STUCCO	INT. STUCCO	INT. STUCCO	8'-0"	C	
123	CLOSET	CEMENT	WOOD	INT. STUCCO	INT. STUCCO	INT. STUCCO	INT. STUCCO	INT. STUCCO	8'-0"	C	
124	CLOSET	CEMENT	WOOD	INT. STUCCO	INT. STUCCO	INT. STUCCO	INT. STUCCO	INT. STUCCO	8'-0"	C	
125	CLOSET	CEMENT	WOOD	INT. STUCCO	INT. STUCCO	INT. STUCCO	INT. STUCCO	INT. STUCCO	8'-0"	C	
201	BALCONY	FACTORY MAPLE	WOOD	—	—	—	—	—	10'-0"	C	
202	STORAGE	D.F.	—	—	—	—	—	—	10'-0"	C	
203	STORAGE	D.F.	—	—	—	—	—	—	10'-0"	C	
204	STORAGE	D.F.	—	—	—	—	—	—	10'-0"	C	

DOOR AND OPENING SCHEDULE											
OPENING NUMBER	DOOR TYPE	MATERIAL	THICKNESS	WIDTH	HEIGHT	PAIR	FRAME	FINISH	REVISIONS	REMARKS	
100	D	WD	1 3/4"	3'-0"	7'-0"		WD	WD			
101	A	WD	2 1/2"	3'-0"	7'-0"		WD	WD			
102	A	WD	2 1/2"	3'-0"	7'-0"		WD	WD			
103	C	WD	1 3/4"	3'-0"	7'-0"		WD	WD			
104	C	WD	1 3/4"	3'-0"	7'-0"		WD	WD			
105	B	WD	2 1/2"	3'-0"	7'-0"		WD	WD			
106	B	WD	2 1/2"	3'-0"	7'-0"		WD	WD			
107	B	WD	2 1/2"	3'-0"	7'-0"		WD	WD			
108	E	WD	1 3/4"	3'-0"	7'-0"		WD	WD			
109	C	WD	1 3/4"	3'-0"	7'-0"		WD	WD			
110	C	WD	1 3/4"	3'-0"	7'-0"		WD	WD			
111	A	WD	2 1/2"	3'-0"	7'-0"		WD	WD			
112	C	WD	1 3/4"	3'-0"	7'-0"		WD	WD			
113	C	WD	1 3/4"	3'-0"	7'-0"		WD	WD			
114	C	WD	1 3/4"	3'-0"	7'-0"		WD	WD			
115	C	WD	1 3/4"	3'-0"	7'-0"		WD	WD			
116	E	WD	1 3/4"	3'-0"	7'-0"		WD	WD			
117	C	WD	1 3/4"	3'-0"	7'-0"		WD	WD			
118	C	WD	1 3/4"	3'-0"	7'-0"		WD	WD			
119	C	WD	1 3/4"	3'-0"	7'-0"		WD	WD			
120	C	WD	1 3/4"	3'-0"	7'-0"		WD	WD			
121	C	WD	1 3/4"	3'-0"	7'-0"		WD	WD			
122	C	WD	1 3/4"	3'-0"	7'-0"		WD	WD			
123	A	WD	2 1/2"	3'-0"	7'-0"		WD	WD			
124	C	WD	1 3/4"	3'-0"	7'-0"		WD	WD			
125	C	WD	1 3/4"	3'-0"	7'-0"		WD	WD			
126	C	WD	1 3/4"	3'-0"	7'-0"		WD	WD			
127	C	WD	1 3/4"	3'-0"	7'-0"		WD	WD			
128	C	WD	1 3/4"	3'-0"	7'-0"		WD	WD			
201	C	WD	1 3/4"	3'-0"	7'-0"		WD	WD			
202	C	WD	1 3/4"	3'-0"	7'-0"		WD	WD			
203	C	WD	1 3/4"	3'-0"	7'-0"		WD	WD			

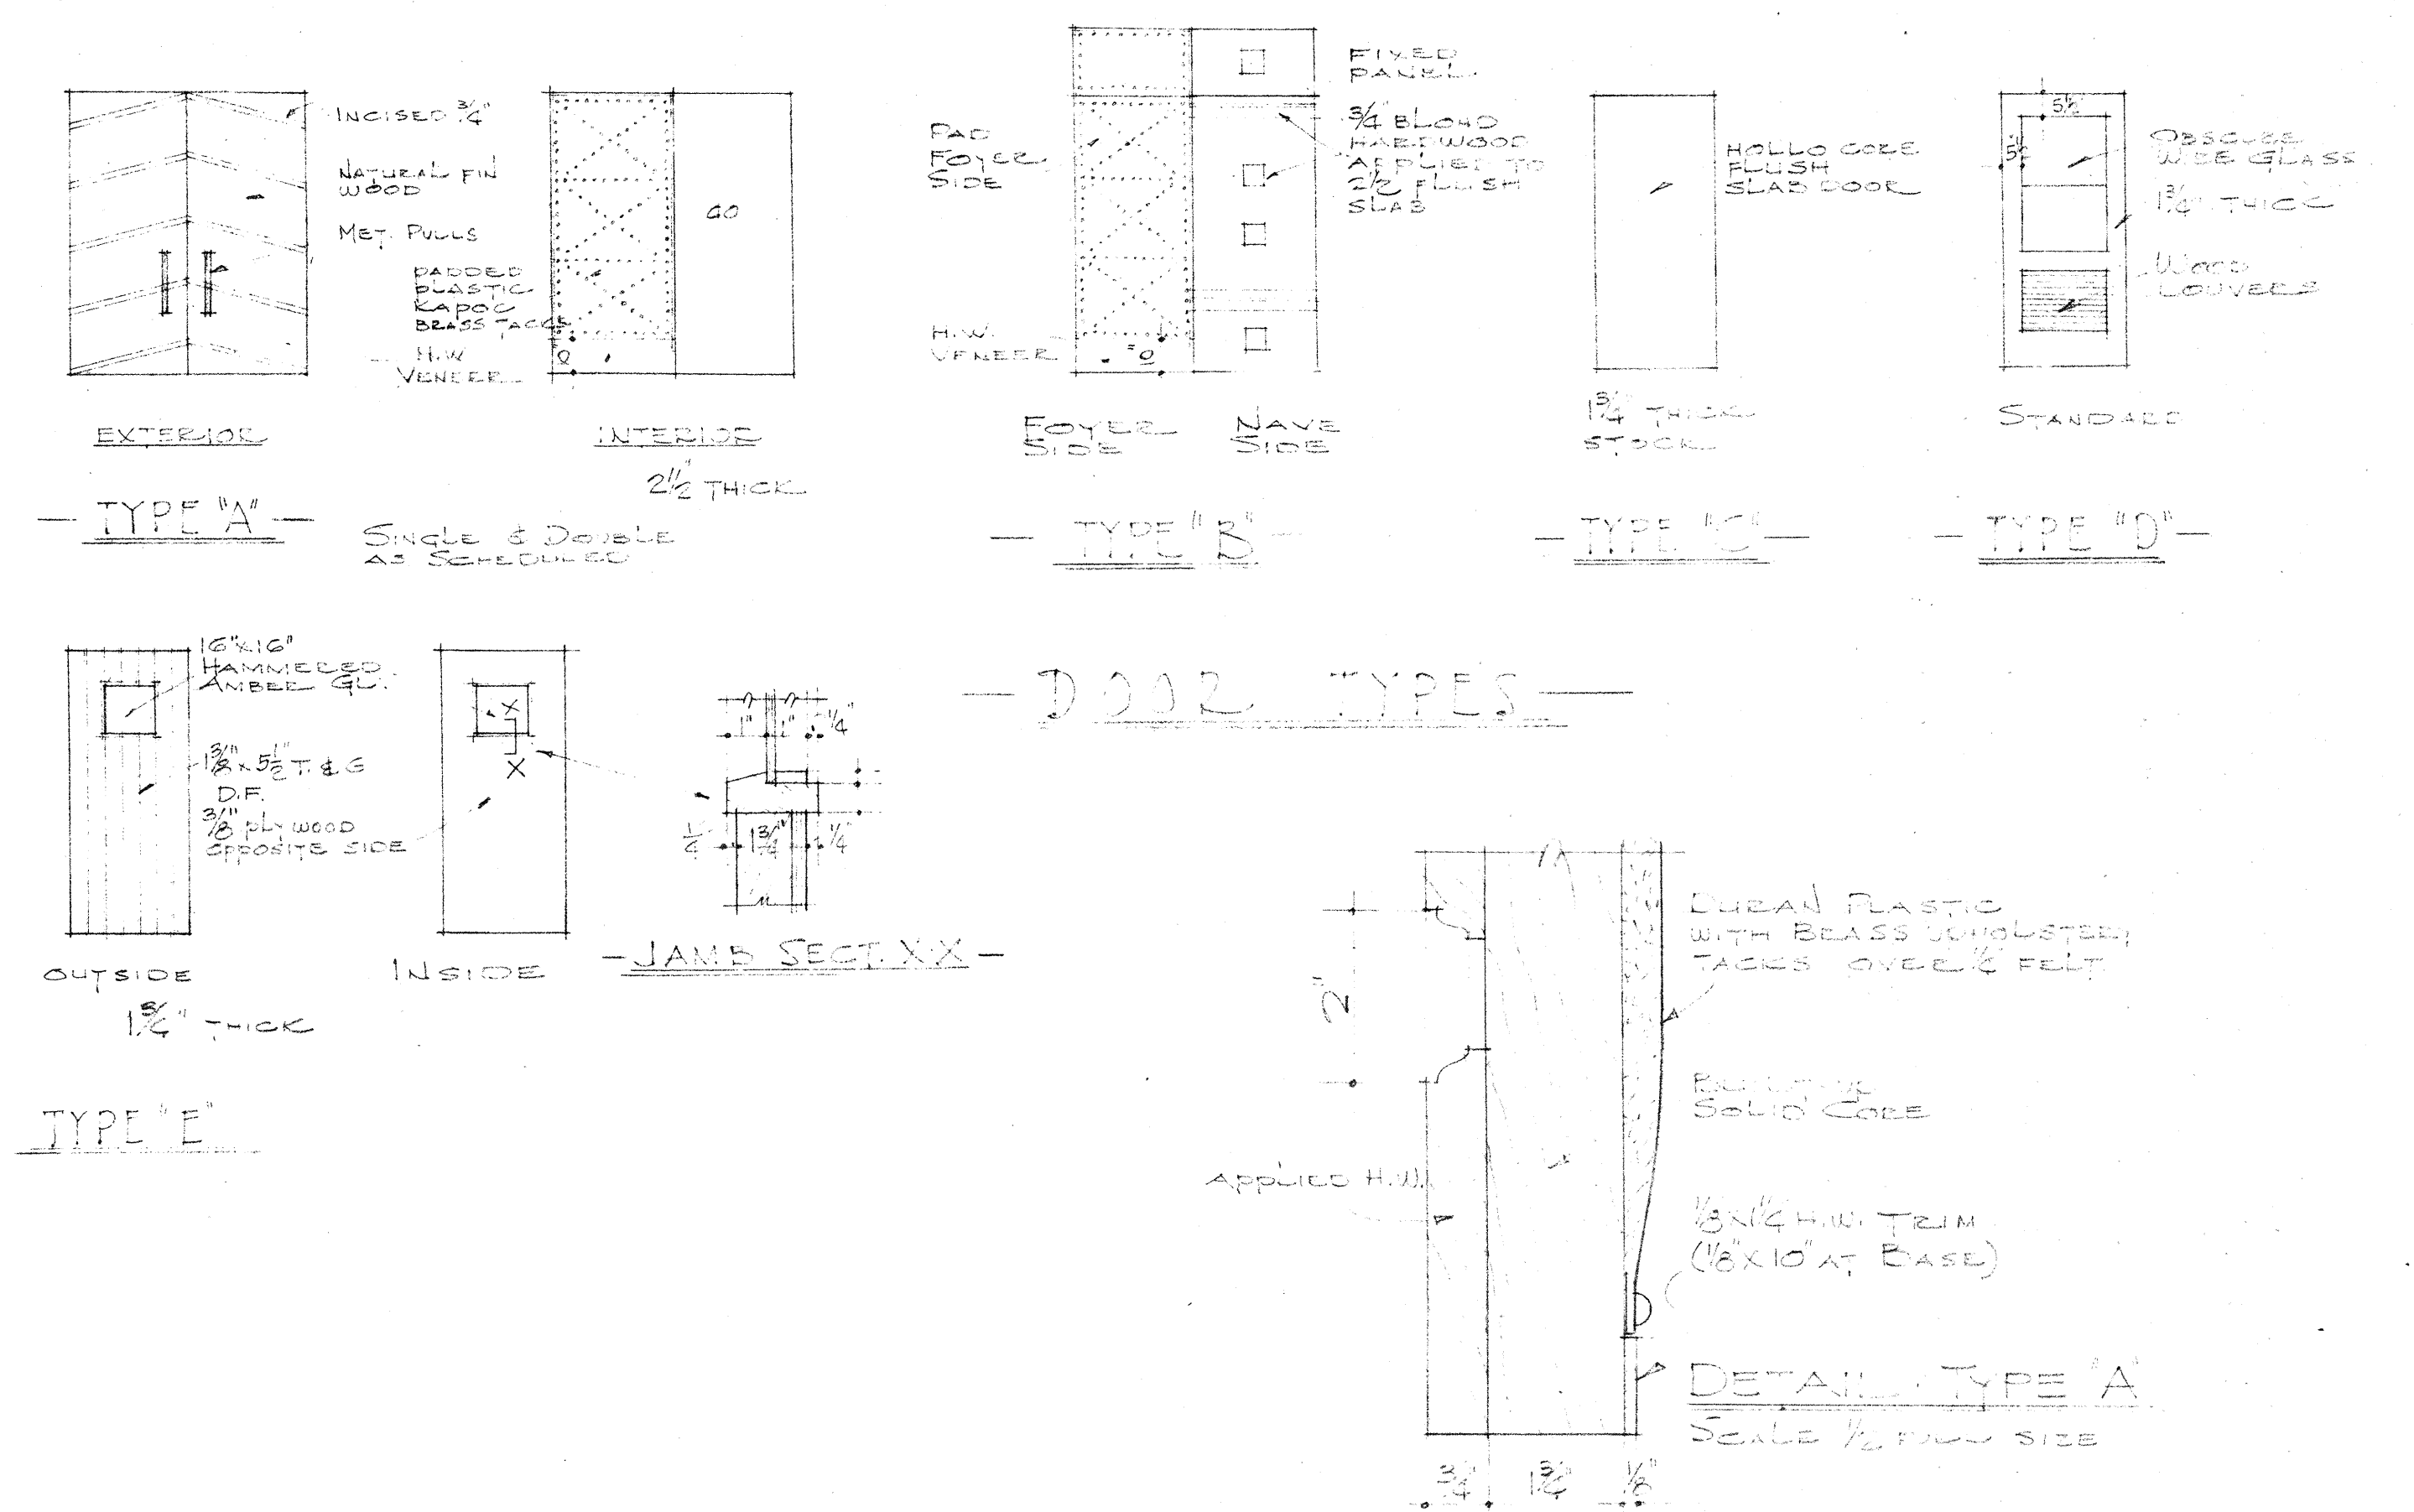

GENERAL NOTES:

G.N.1. ALL ASPHALT TILE TO BE GROUP "C".

G.N.2. ALL ASPHALT TILE TO BE 3/4" THICK.

G.N.3. 1/2" PLYWOOD NAT. FINISHED, SHALL BE PHILIPPINE MAHOGANY.

G.N.4. ALL INTERIOR EXPOSED BRICK WALLS SHALL BE PAINTED.

G.N.5. ALL EXPOSED INTERIOR BRICK WALLS SHALL NOT HAVE A BRICK EXCEPT AS OTHER WISE SHOWN.

G.N.6. ORGAN ROOMS SHALL BE PLASTERED WITH KEELERS (CONC.) PLASTER SMOOTH TROWELED.

G.N.7. ALL CONC. STEPS SHALL HAVE ABRASIVE HARDENER IN THE TREAD & NOODING.

FINISH SYMBOLS:



F = FLAT WALL PAINT

E = EGGSHELL ENAMEL

N = NATURAL FINISH

C = INTEGRAL COLOR

WINDOW SCHEDULE											
TYPE	MATERIAL	WIDTH	HEIGHT	GLASS	FRAME				FINISH	REMARKS	
					MATERIAL	WEED	UNAD	SILL			
A	STEEL	4'-0"	6'-0"	6	CONC.	CONC.	STE	NO	E	E	STOCK NO. 2224 X V
B	STEEL	4'-0"	4'-0"	D.S.	CONC.	STE	NO	E	E	E	STOCK NO. 2224 X V
C	STEEL	8'-0"	4'-0"	D.S.	CONC.	DETAILS	NO	E	E	E	STOCK NO. 2224 X V
D	STEEL	6'-0"	4'-0"	D.S.	CONC.	SHIT 9	NO	E	E	E	STOCK NO. 2224 X V
E	CONC.	8'-0"	DIAM	STAND	BRICK	SEE DETAIL	NO	E	E	E	SPEC. PRECAST CONC. ROSE WINDOW
B ₁	SAME AS TYPE B - SET WOOD FRAME										

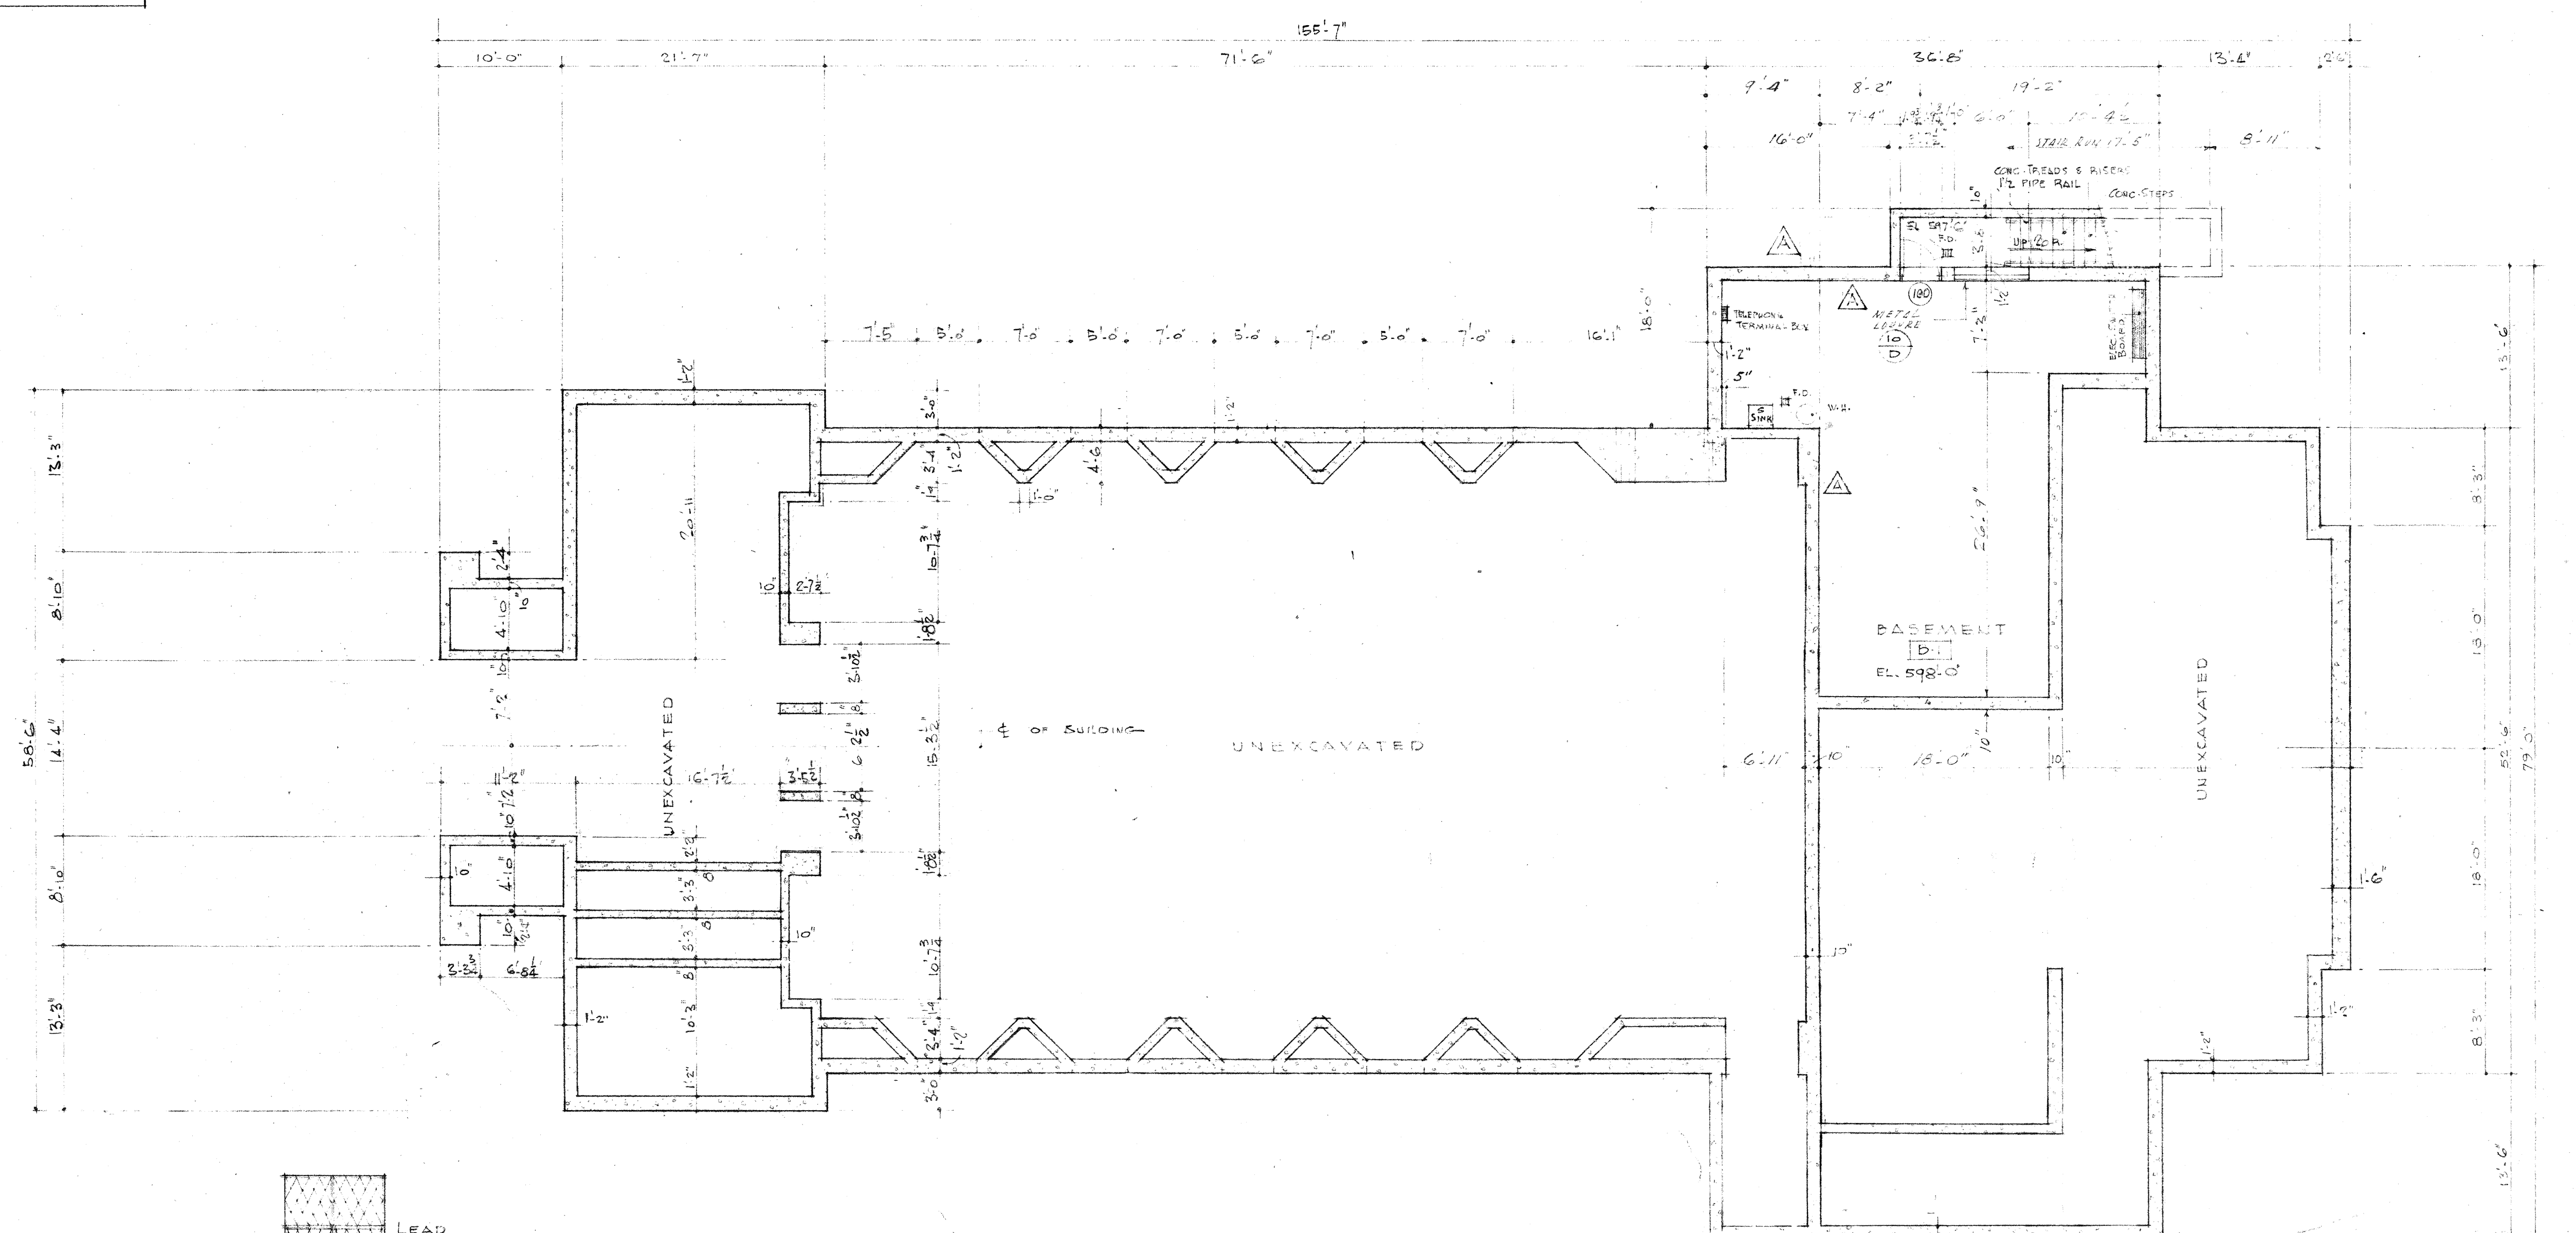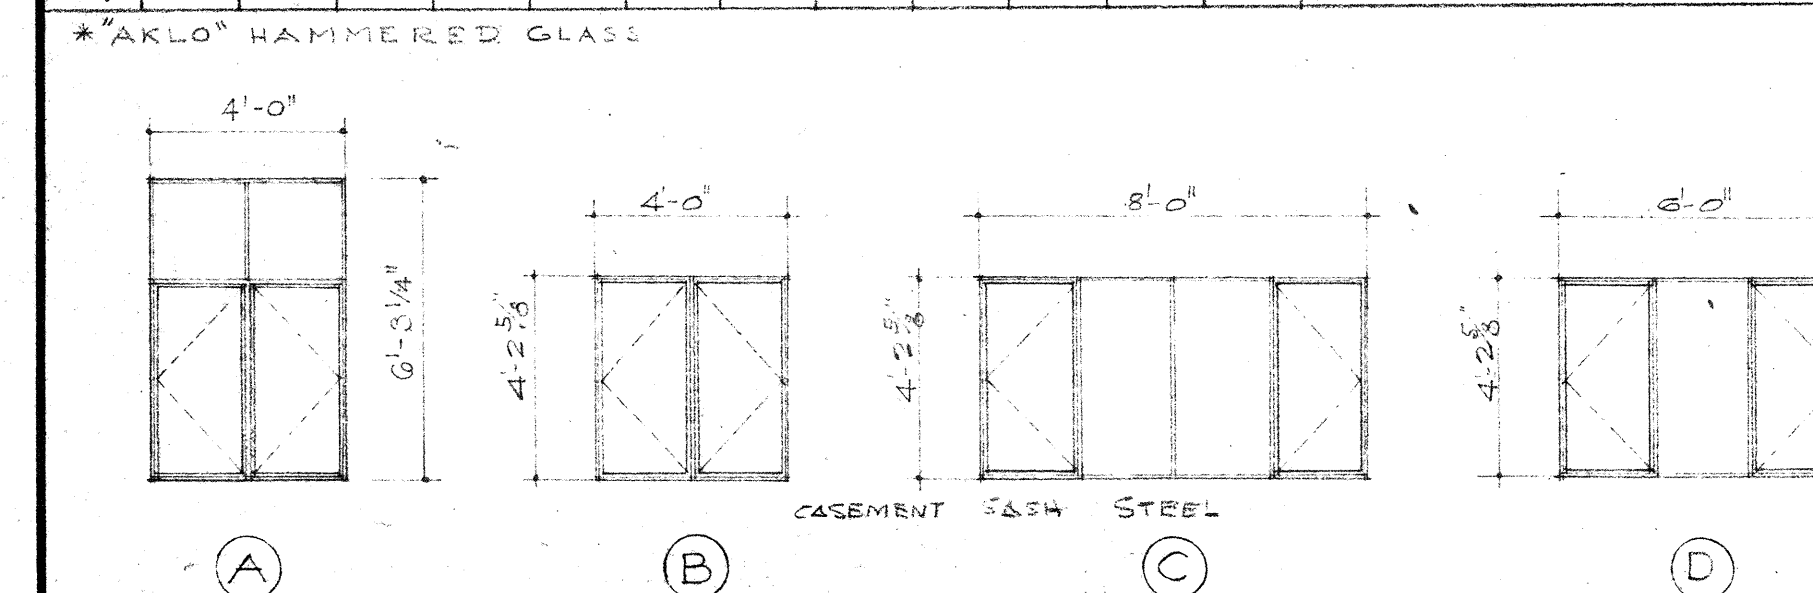

BASEMENT PLAN
SCALE 1/8" = 1'-0"