

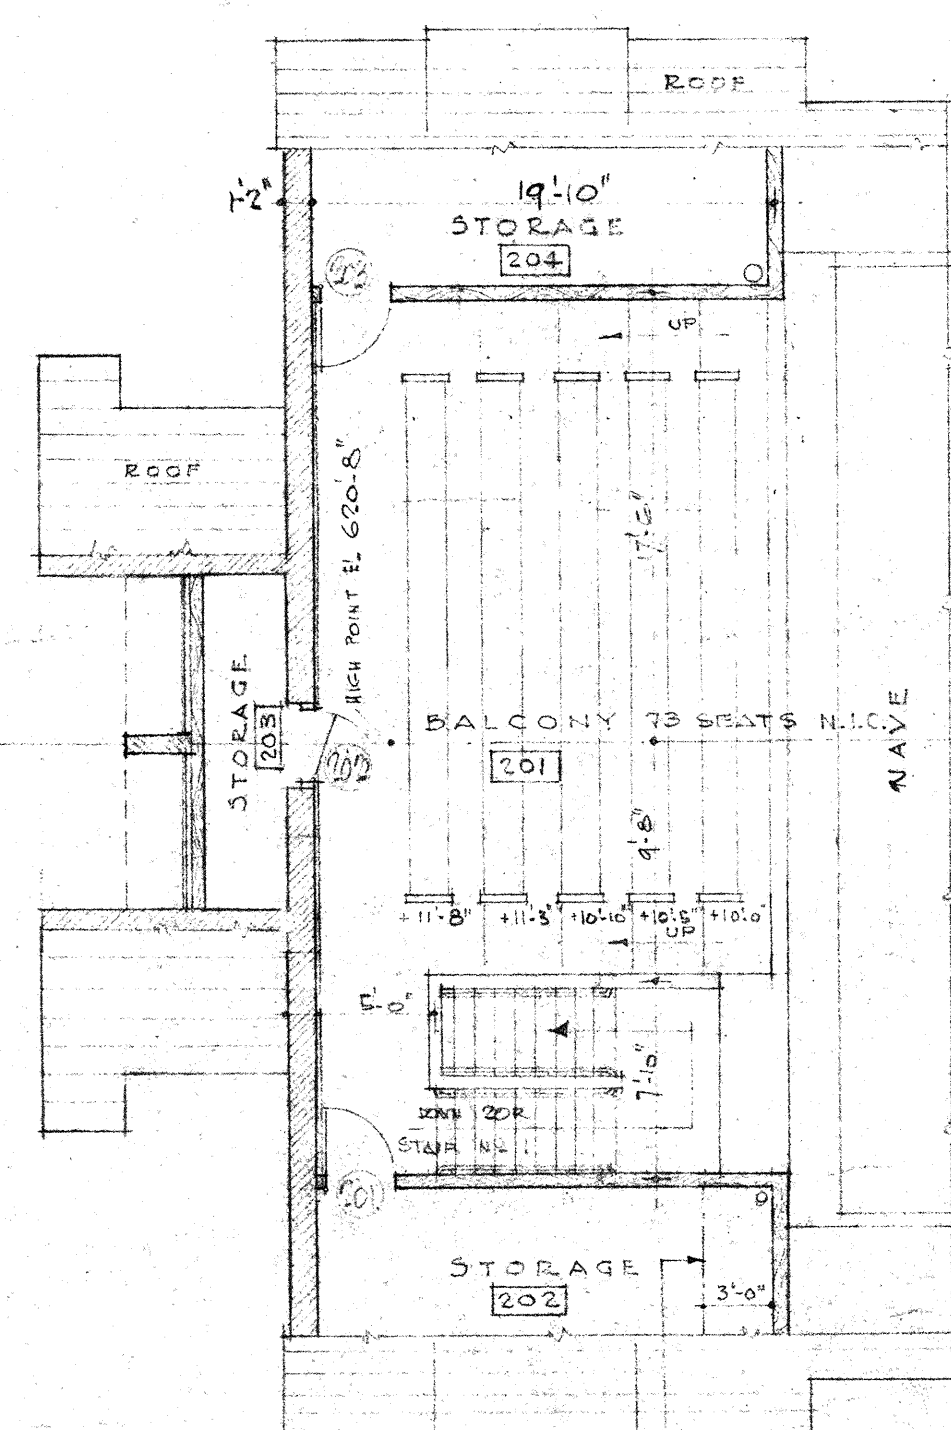


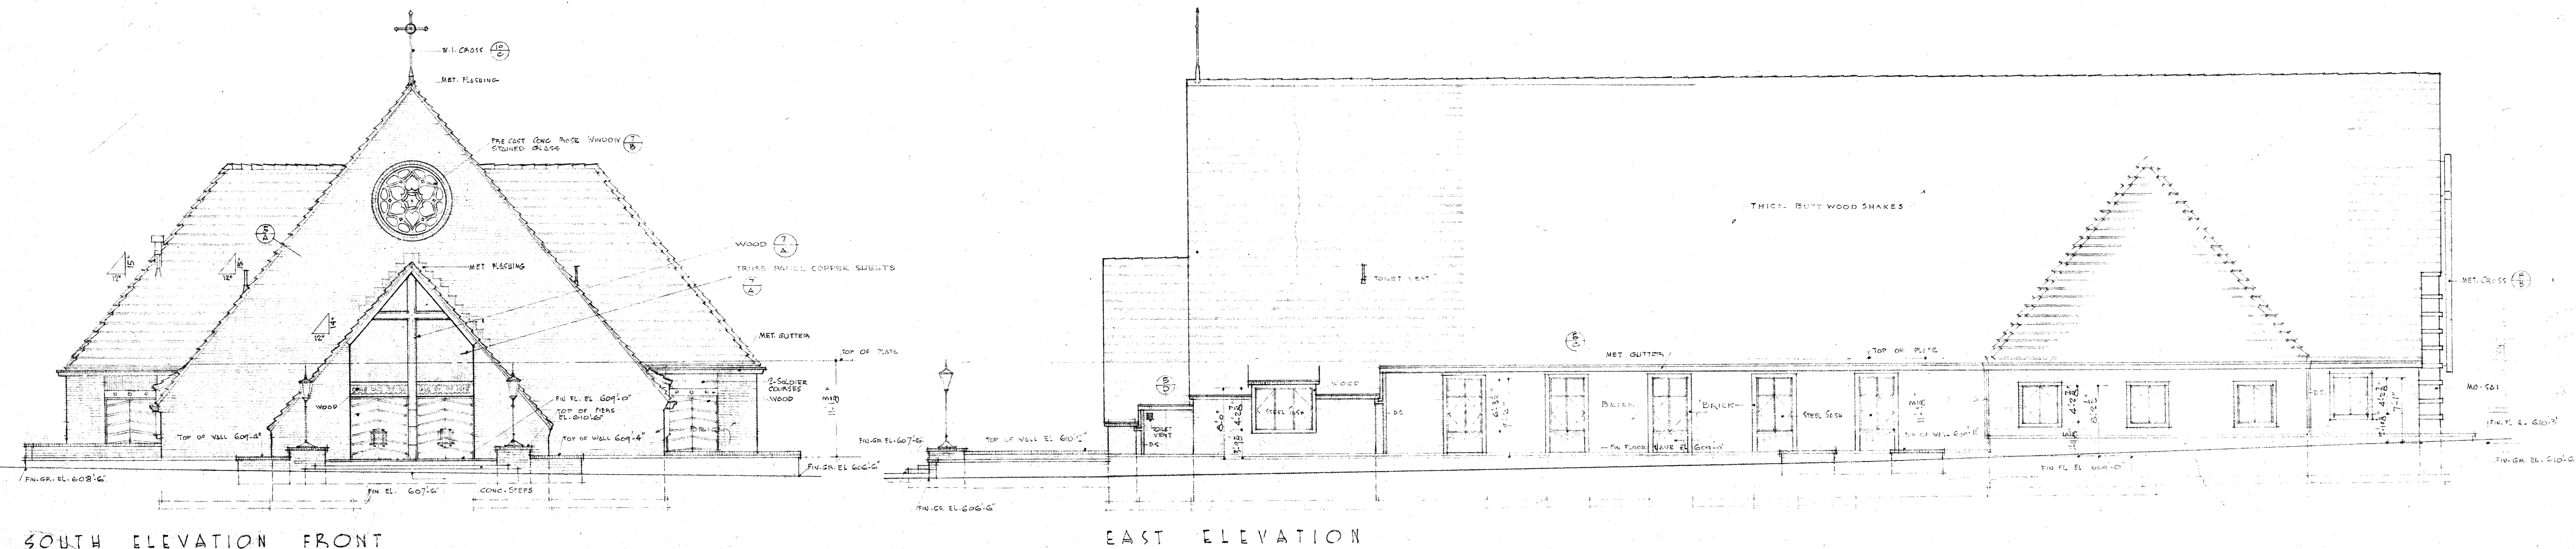

ELECTRIC LIGHT DIMMERS:
PROTECT WITH SCREEN MADE OF 1/2" x 1/2" x 1/4"
B WELDED FRAME WITH 1/4" x 1/4" x 1/4" DIAMOND
MESH SCREENING. ENTIRE UNIT REMOVABLE
BY REMOVING WOOD SCREENS.

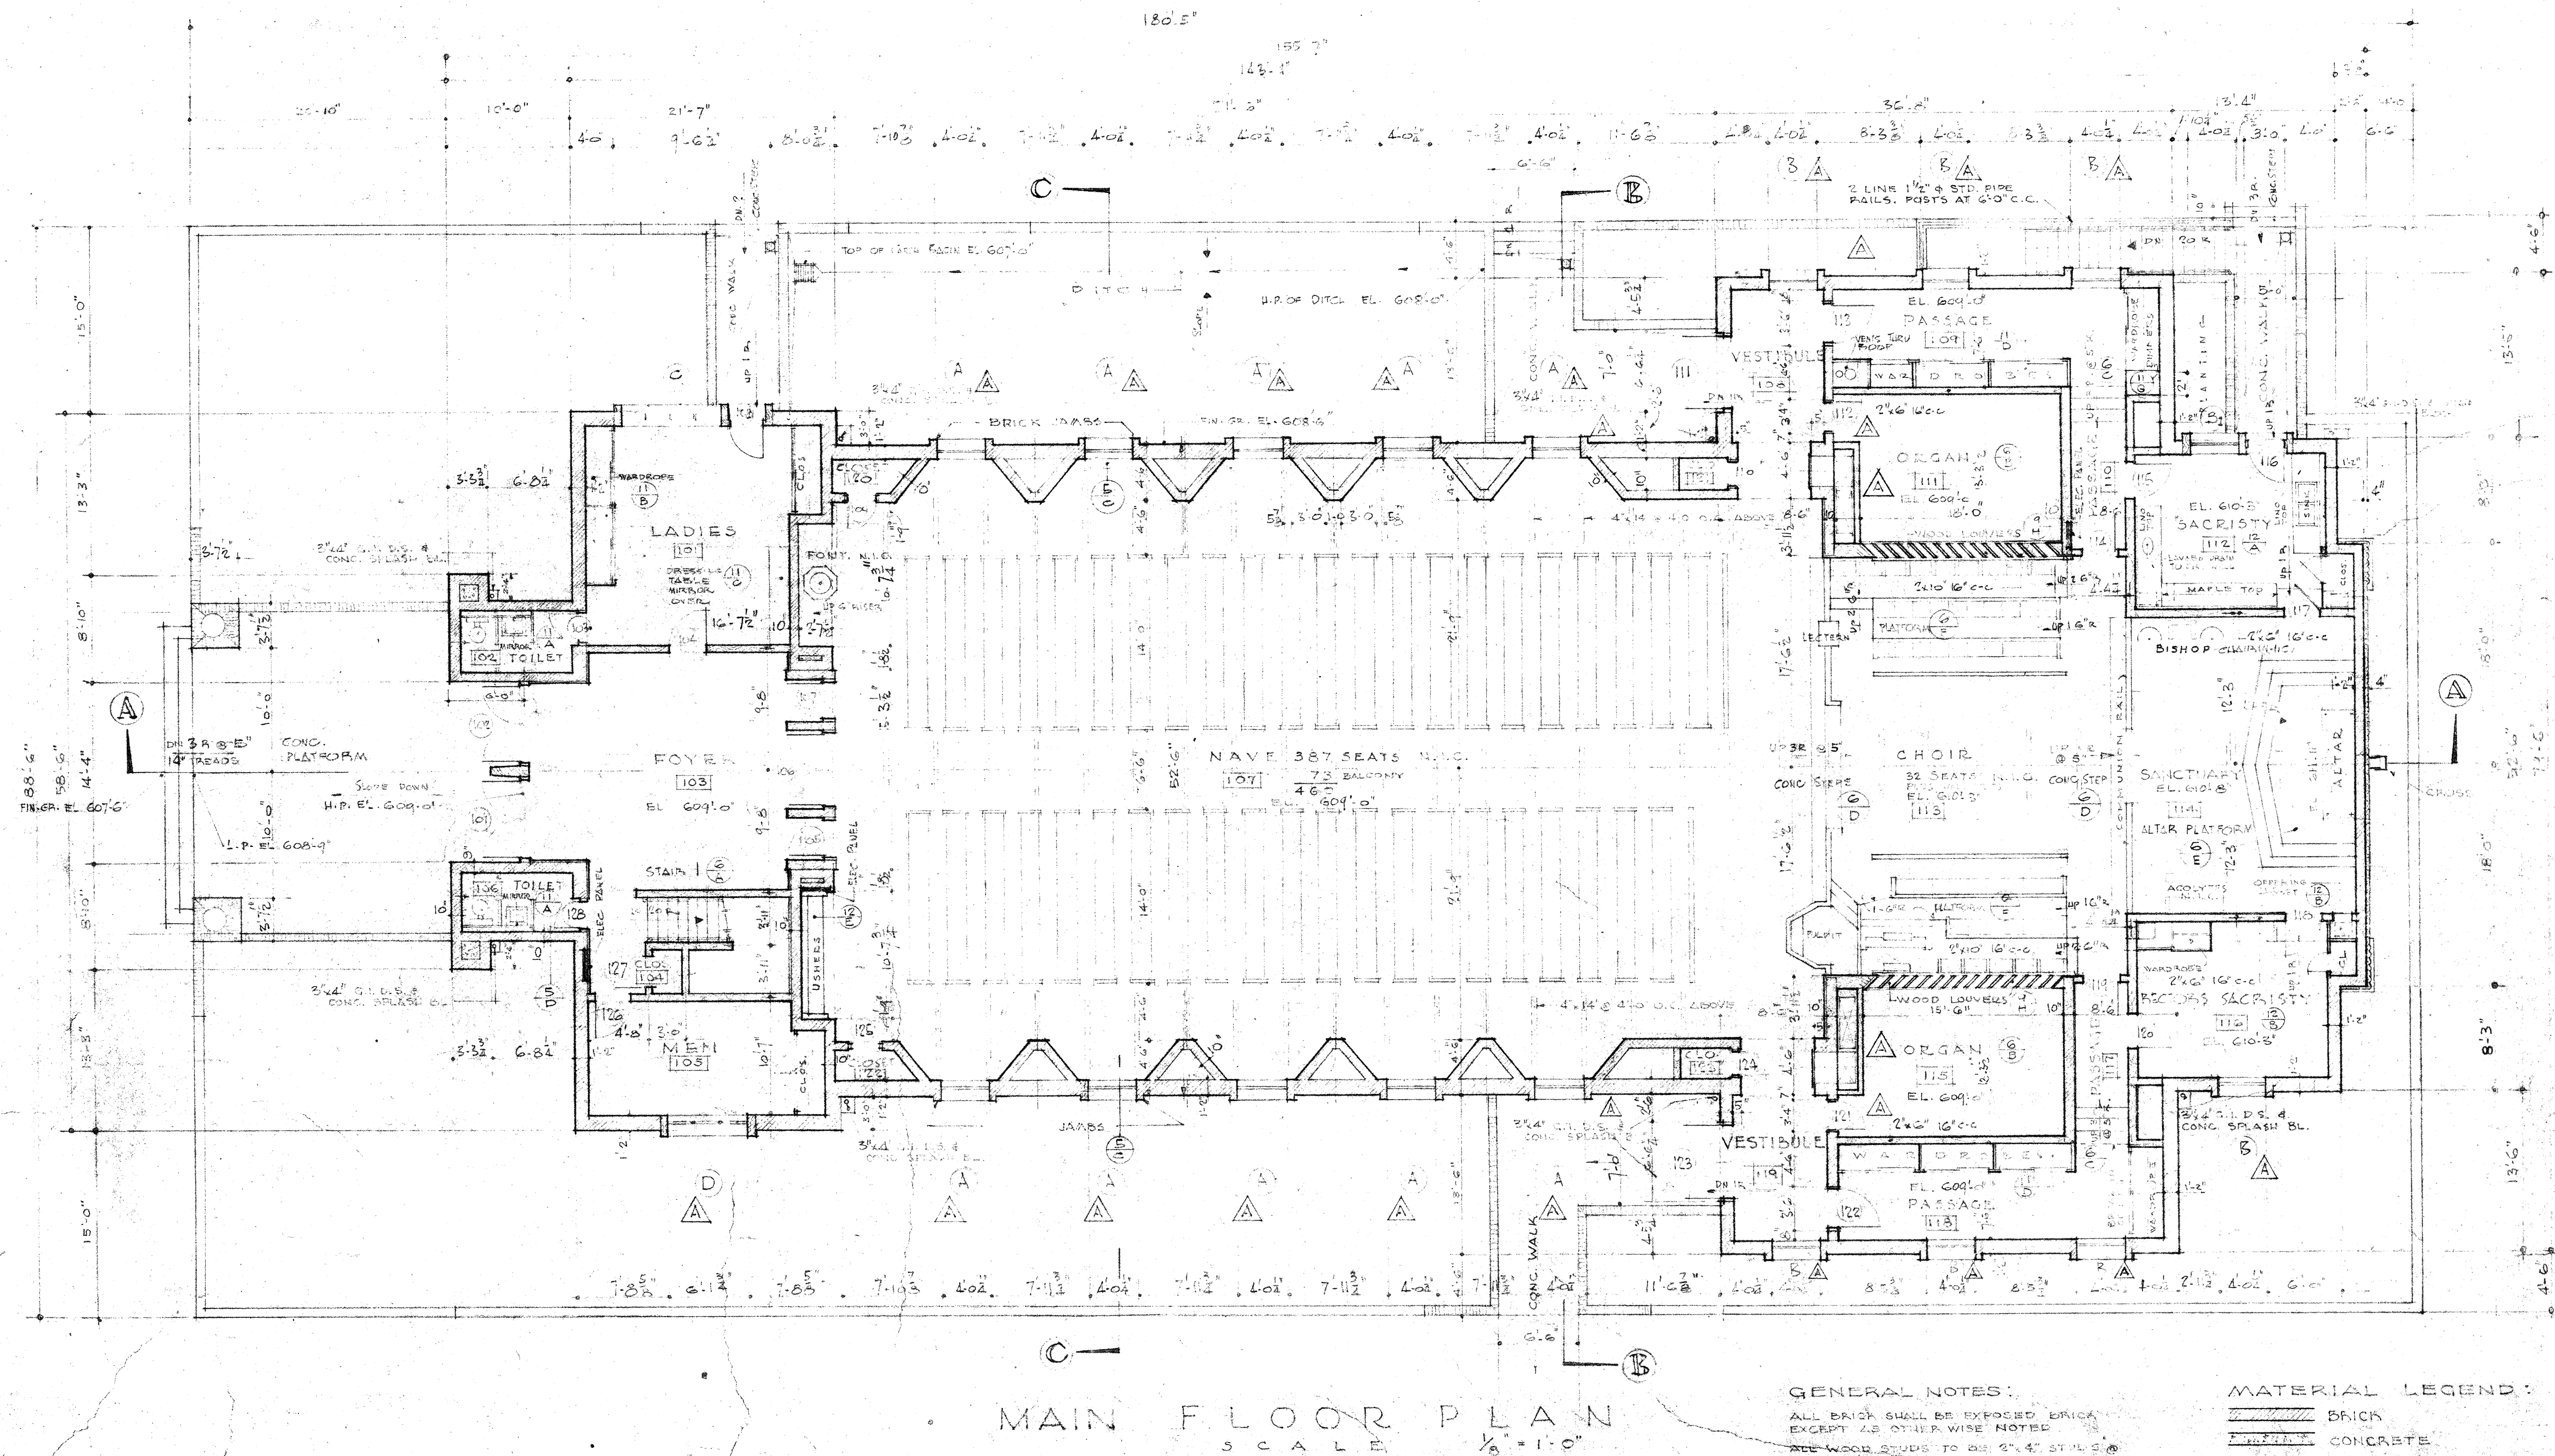

GENERAL NOTES:
ALL BRICK SHALL BE EXPOSED BRICK
EXCEPT AS OTHERWISE NOTED
RED WOOD STUDS TO BE 2" x 4" STUDS
10' C.C. SPACING UNLESS OTHERWISE NOTED
ALL WOOD STUDS TO BE PLASTERED
EXCEPT AS OTHERWISE NOTED
ALL STUDS SHOWN IN LIVES, CLOSET, BALCONY,
ETC. NOT IN CONTRACT, EXCEPT WHERE SHOWN

MATERIAL LEGEND:
BRICK
CONCRETE
WOOD STUD
MO-SAI

BALCONY PLAN
SCALE 1/8" = 1'-0"

Remarks

Revisions Engineers Approvals

AUSTIN FIELD & IRY
architects
2311 WEST THIRD STREET • LOS ANGELES 5, CALIFORNIA • DUNKIRK 8-1326

FLOOR PLAN & ELEVATIONS
STEDMUND'S EPISCOPAL CHURCH
SAN MARINO, CALIF.

DATE: AUG-51
COM'D BY: CFI
SHEET NUMBER: 3