




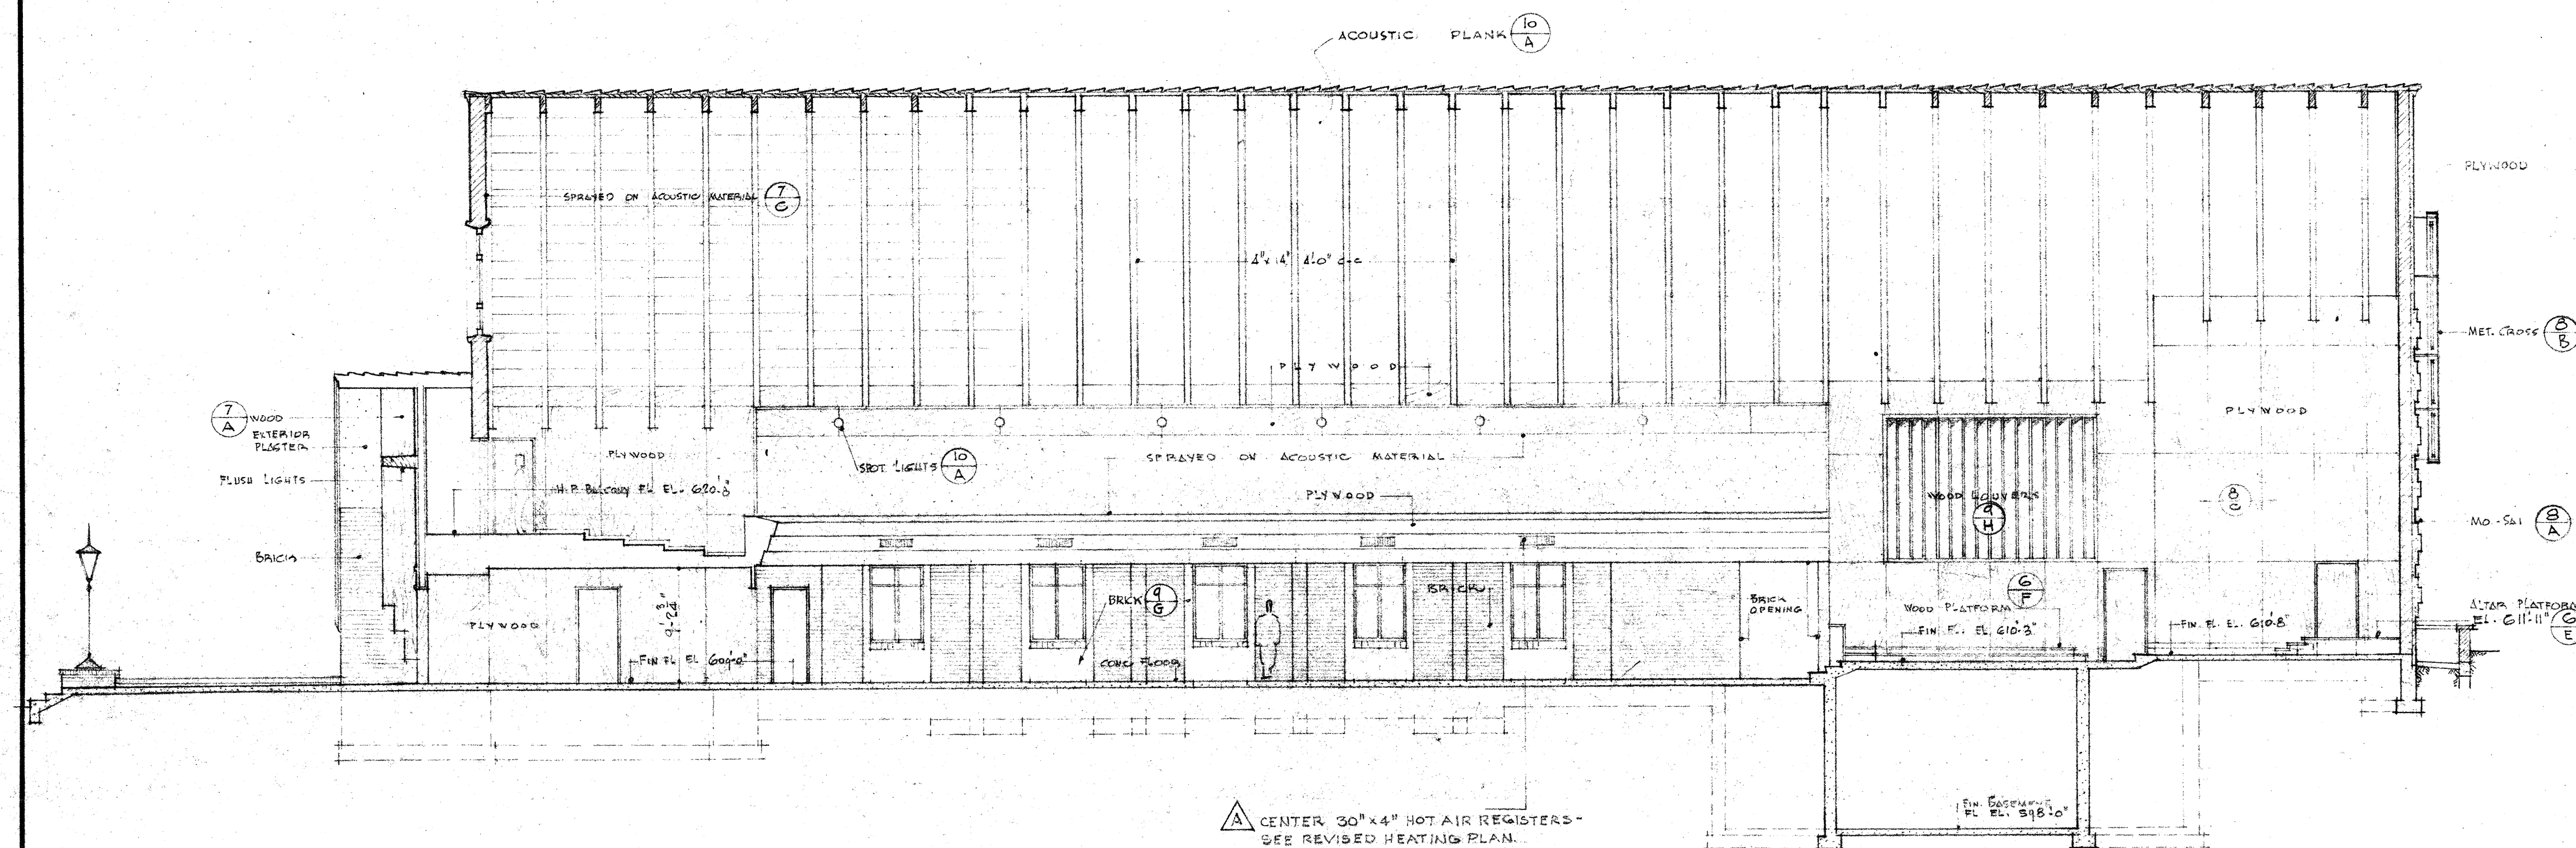


LONGITUDINAL SECTION A A

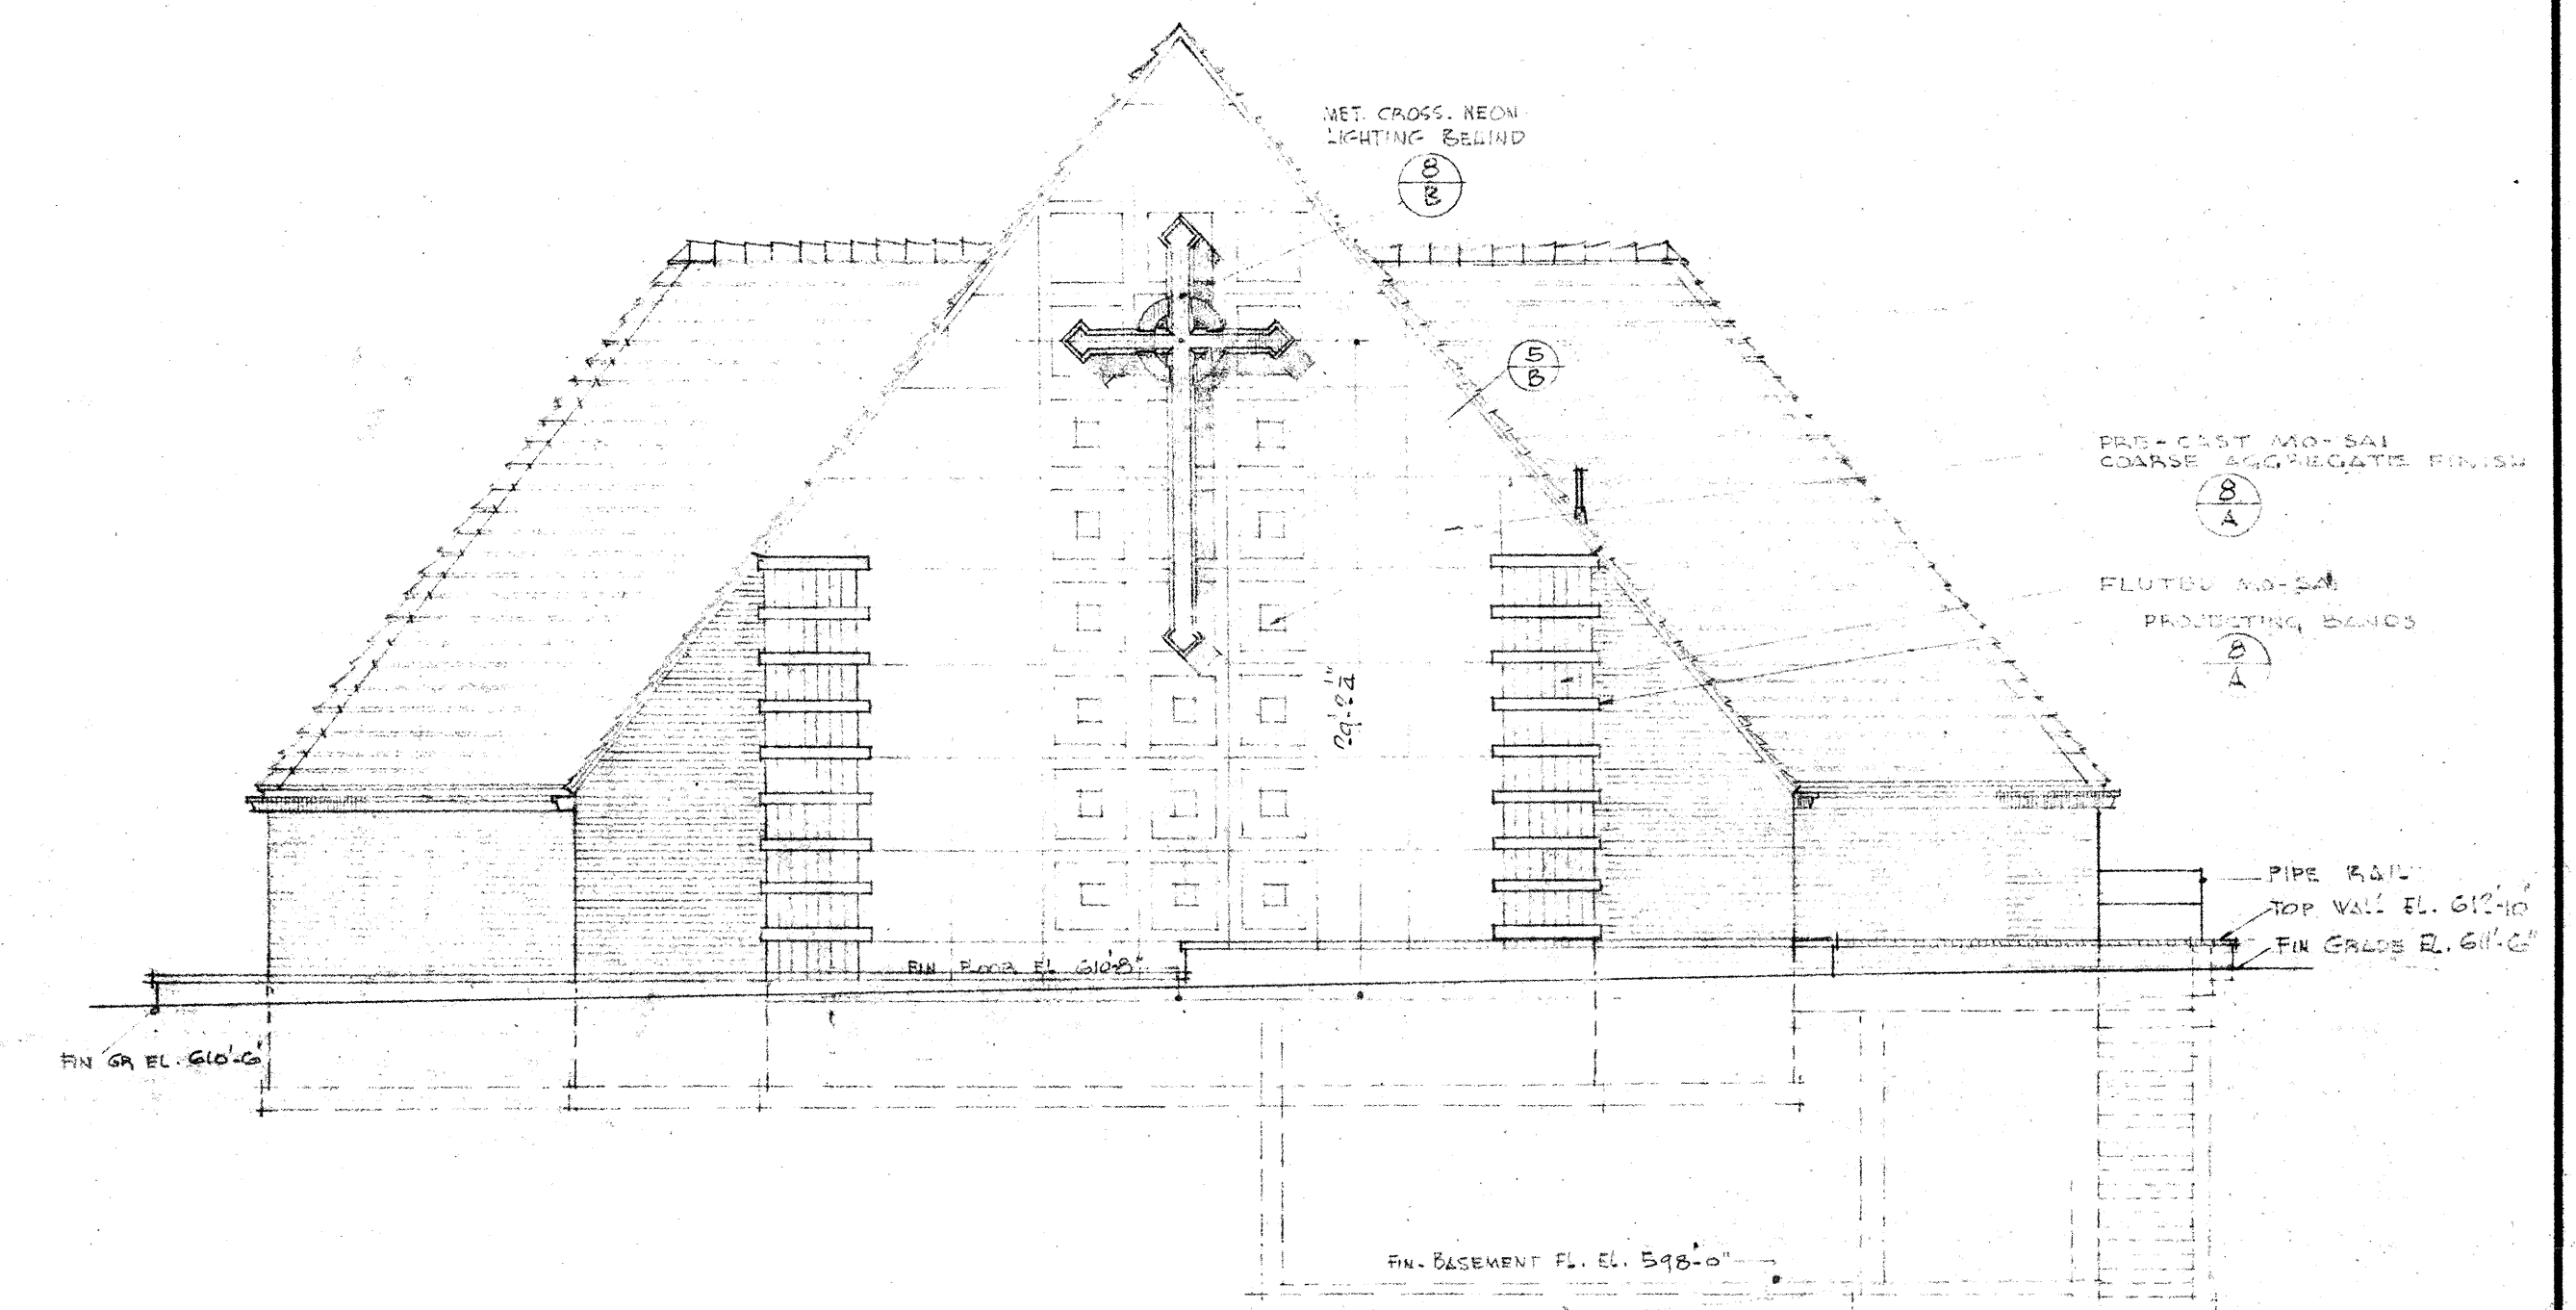

NORTH ELEVATION REAR

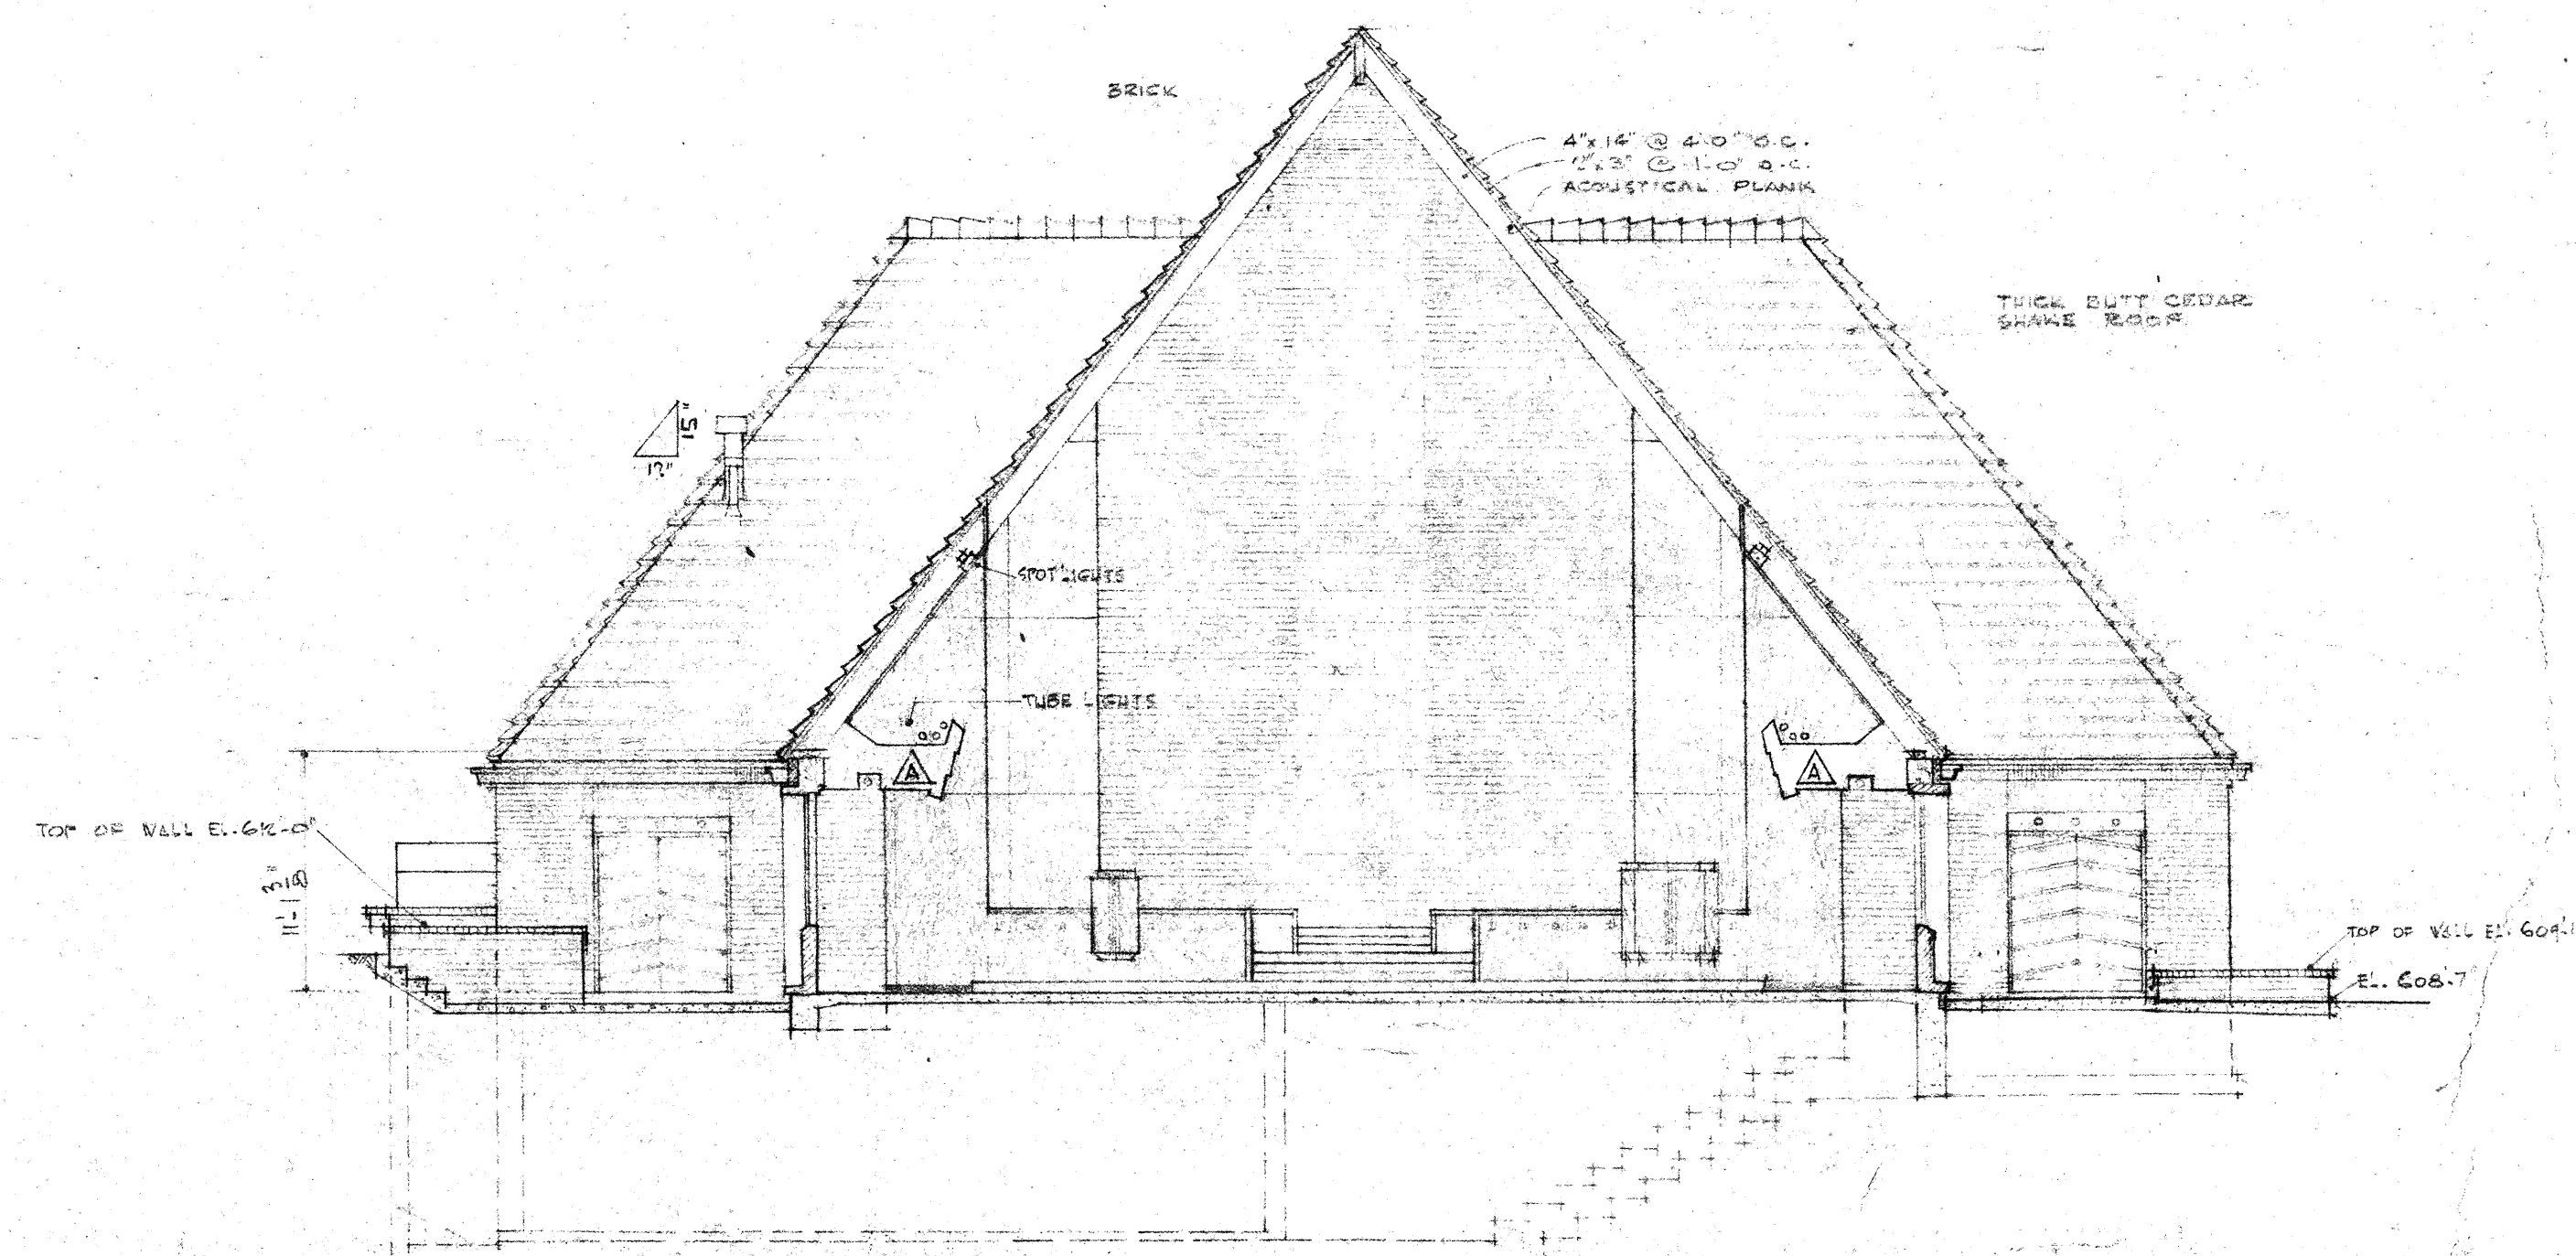

CROSS SECTION B B

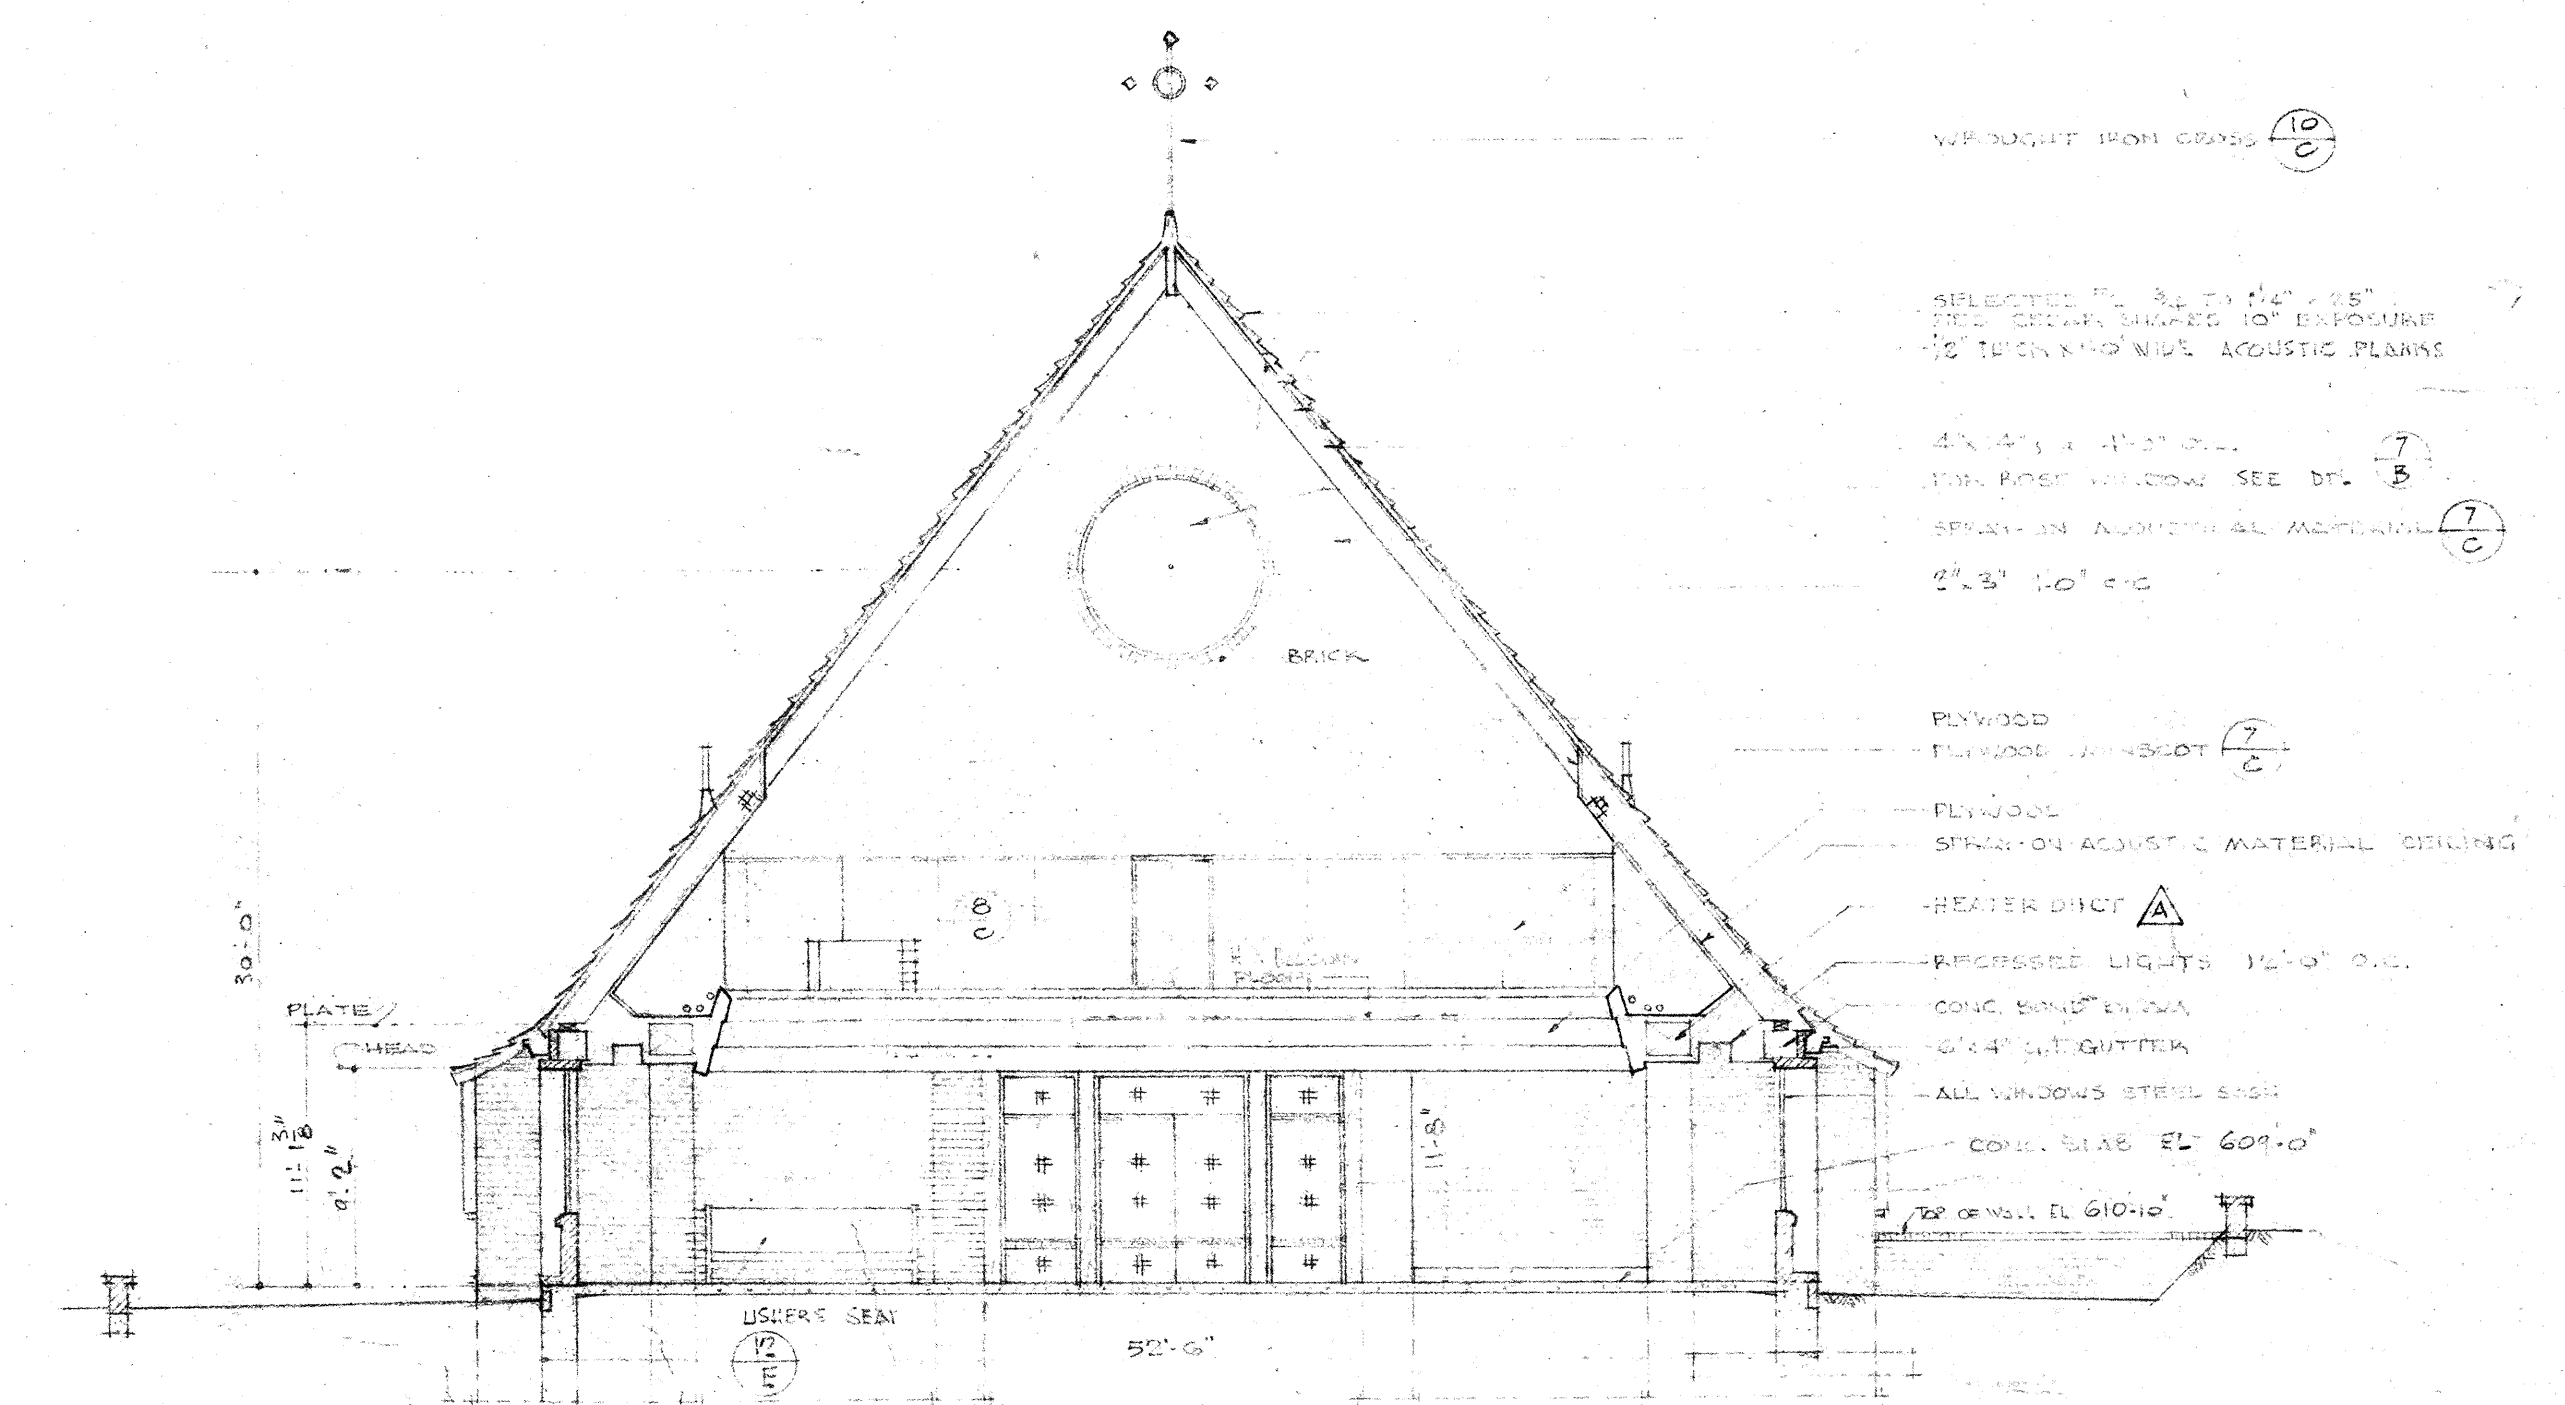

CROSS SECTION C C

Remarks _____ _____ _____		Revisions _____ _____ _____		Engineers _____ _____ _____		Approvals _____ _____ _____		AUSTIN FIELD & IRY Architects 2311 WEST THIRD STREET • LOS ANGELES 5, CALIFORNIA • DUNKIRK 8-1326		SECTIONS & ELEVATIONS ST. EDMUND'S EPISCOPAL CHURCH SAN MARINO, CALIFORNIA		PAGE 4 OF 11 SHEET NUMBER 4
------------------------------------	--	--------------------------------------	--	--------------------------------------	--	--------------------------------------	--	--	--	--	--	--