
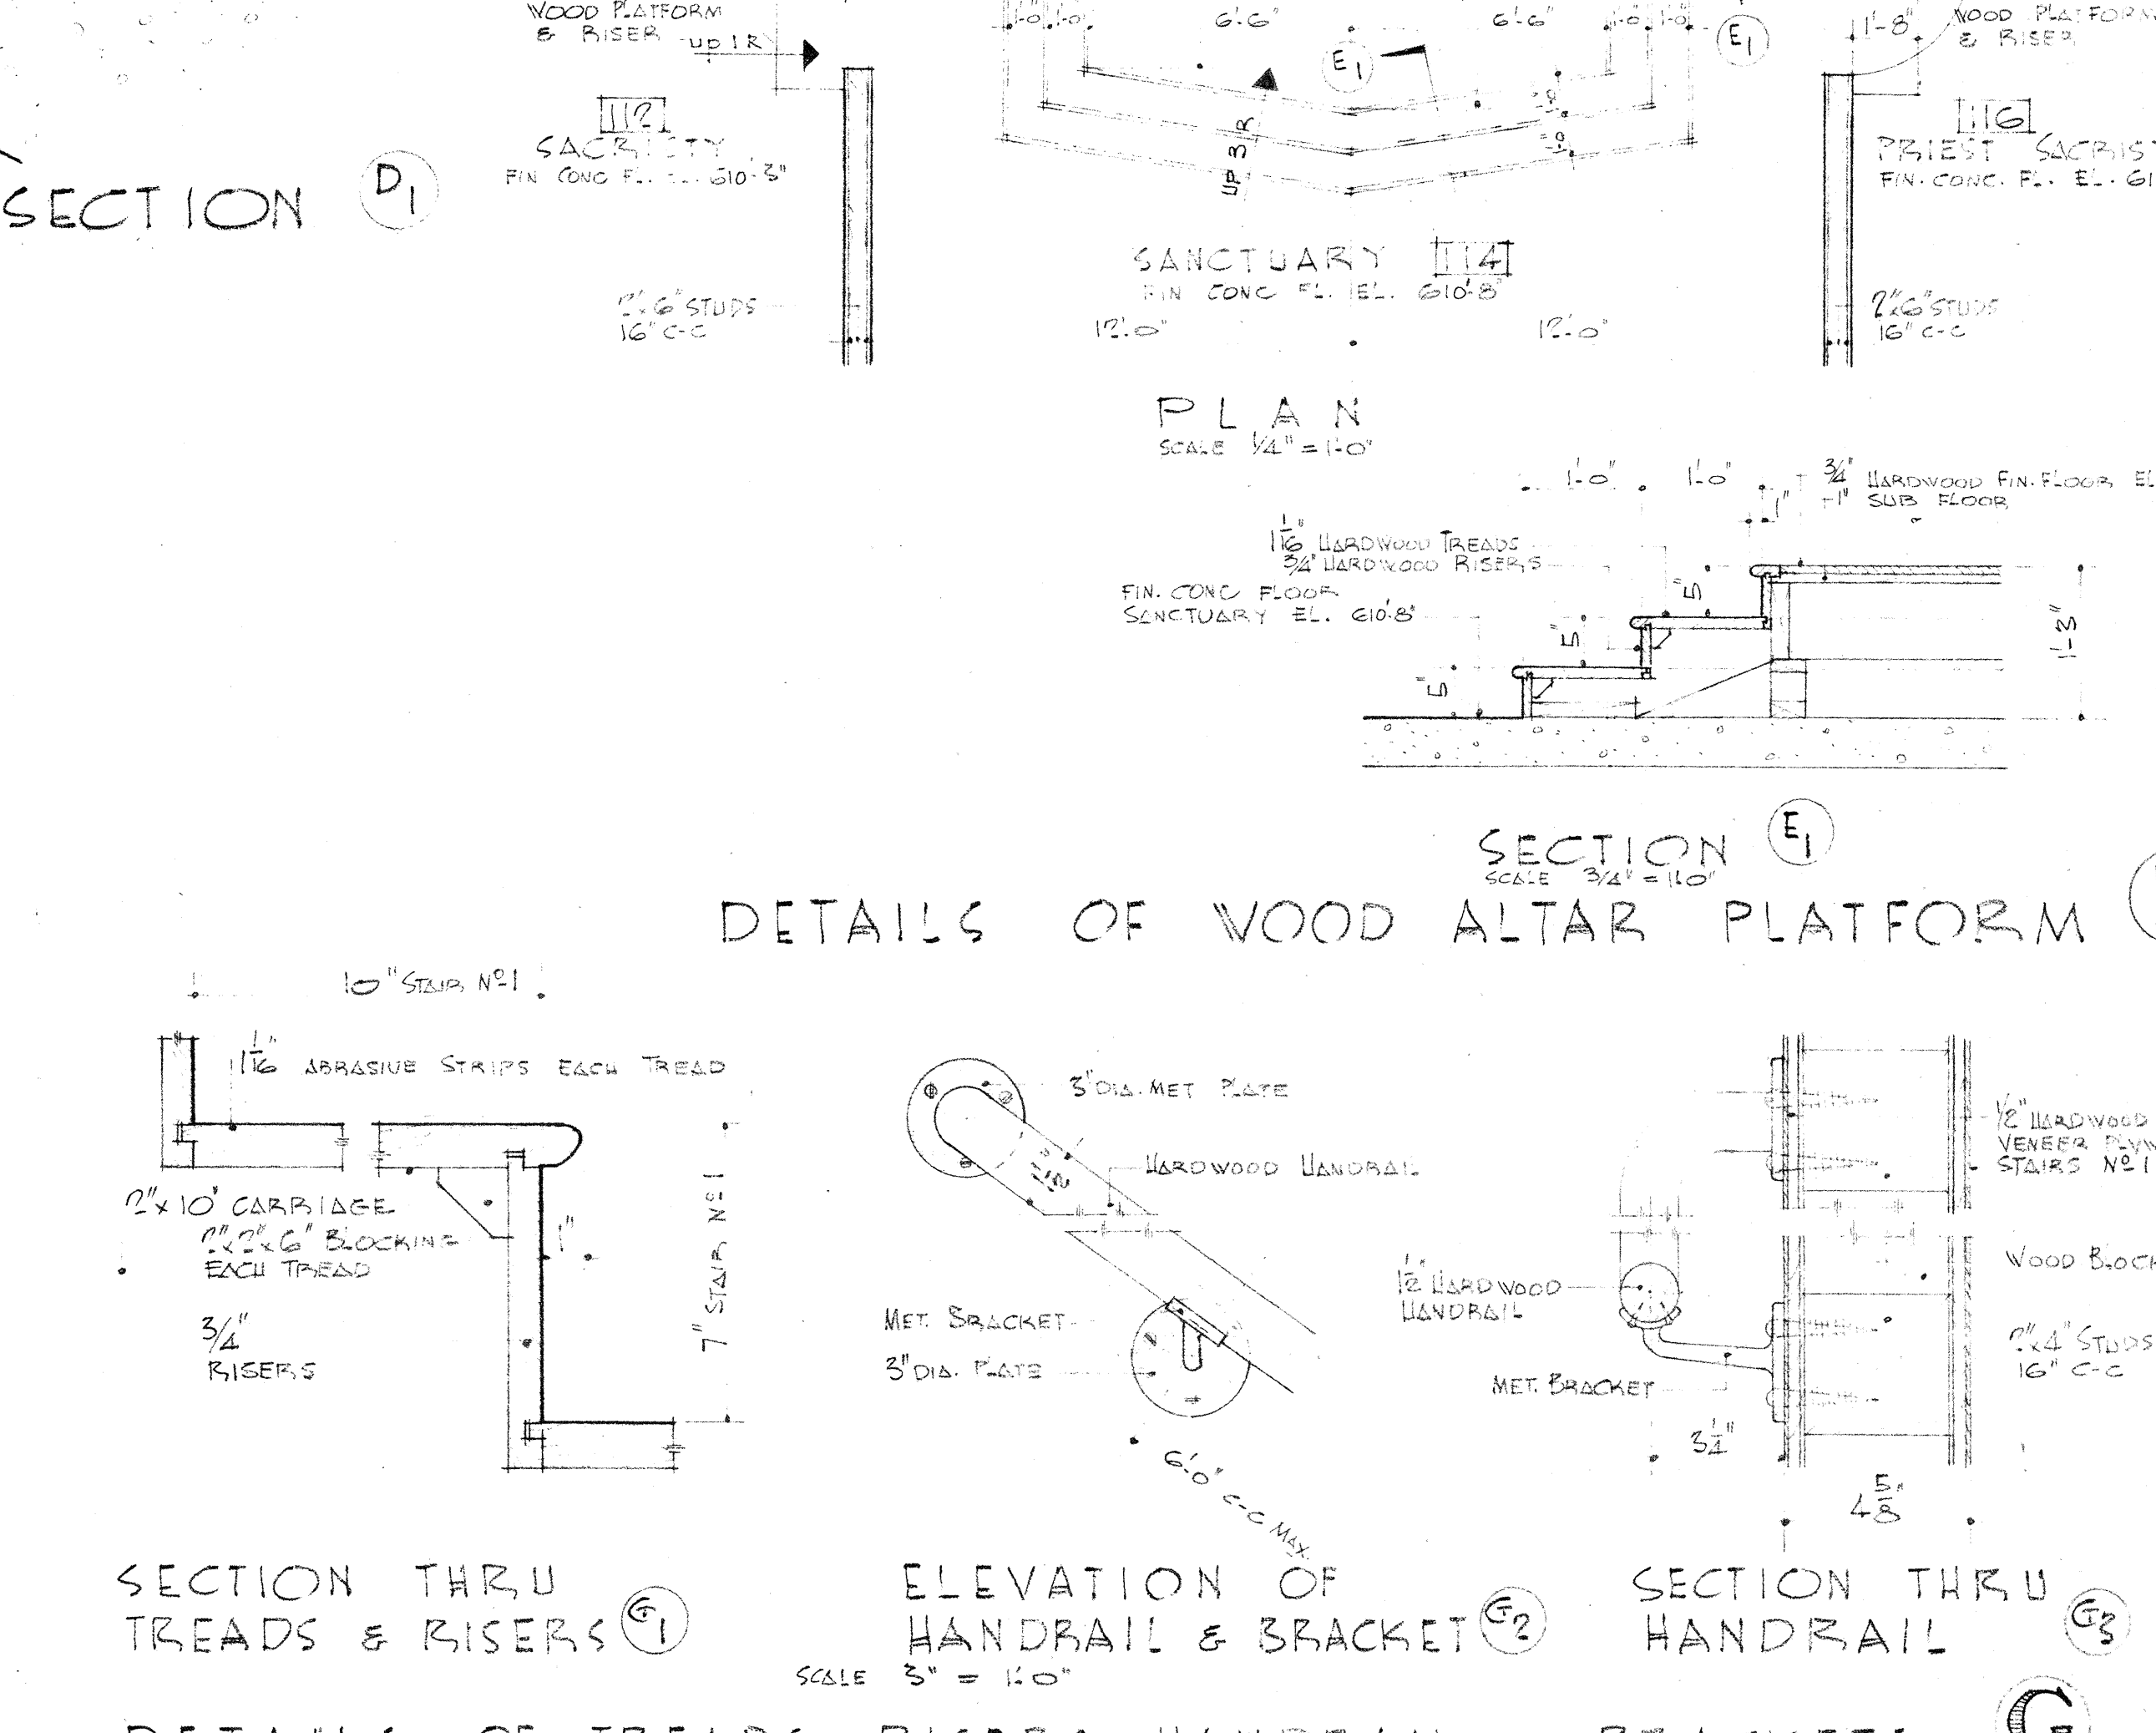
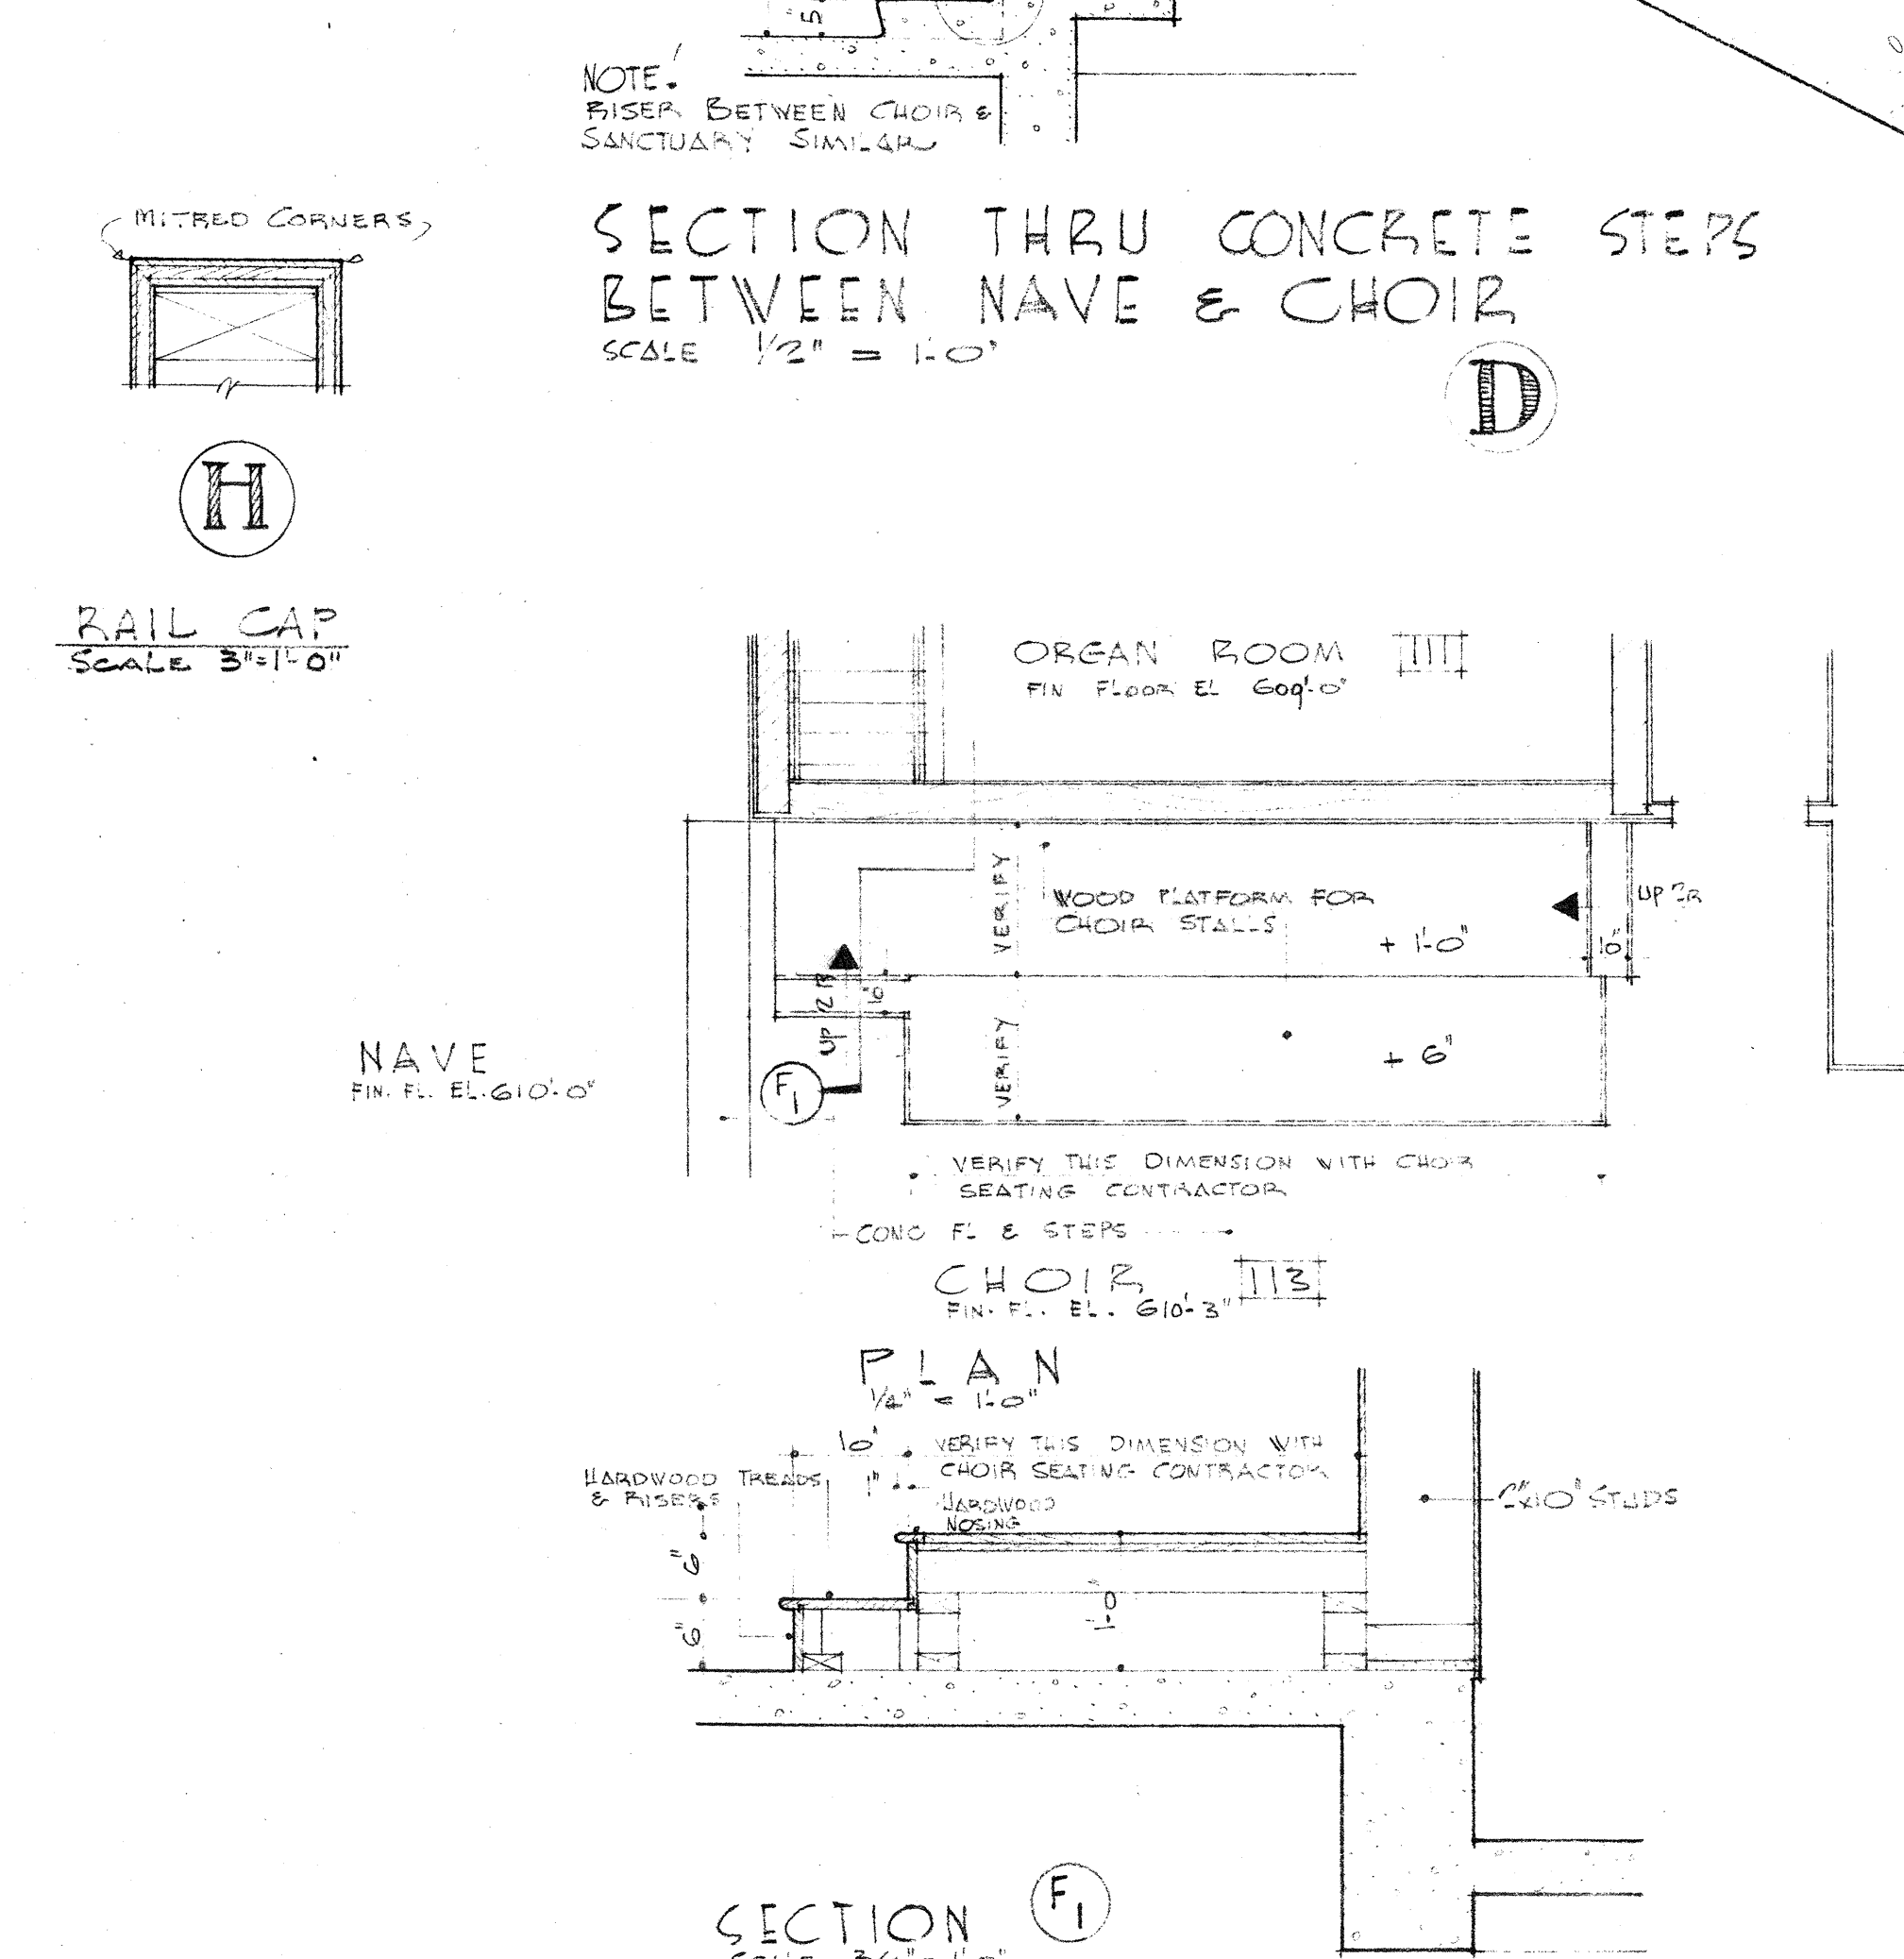
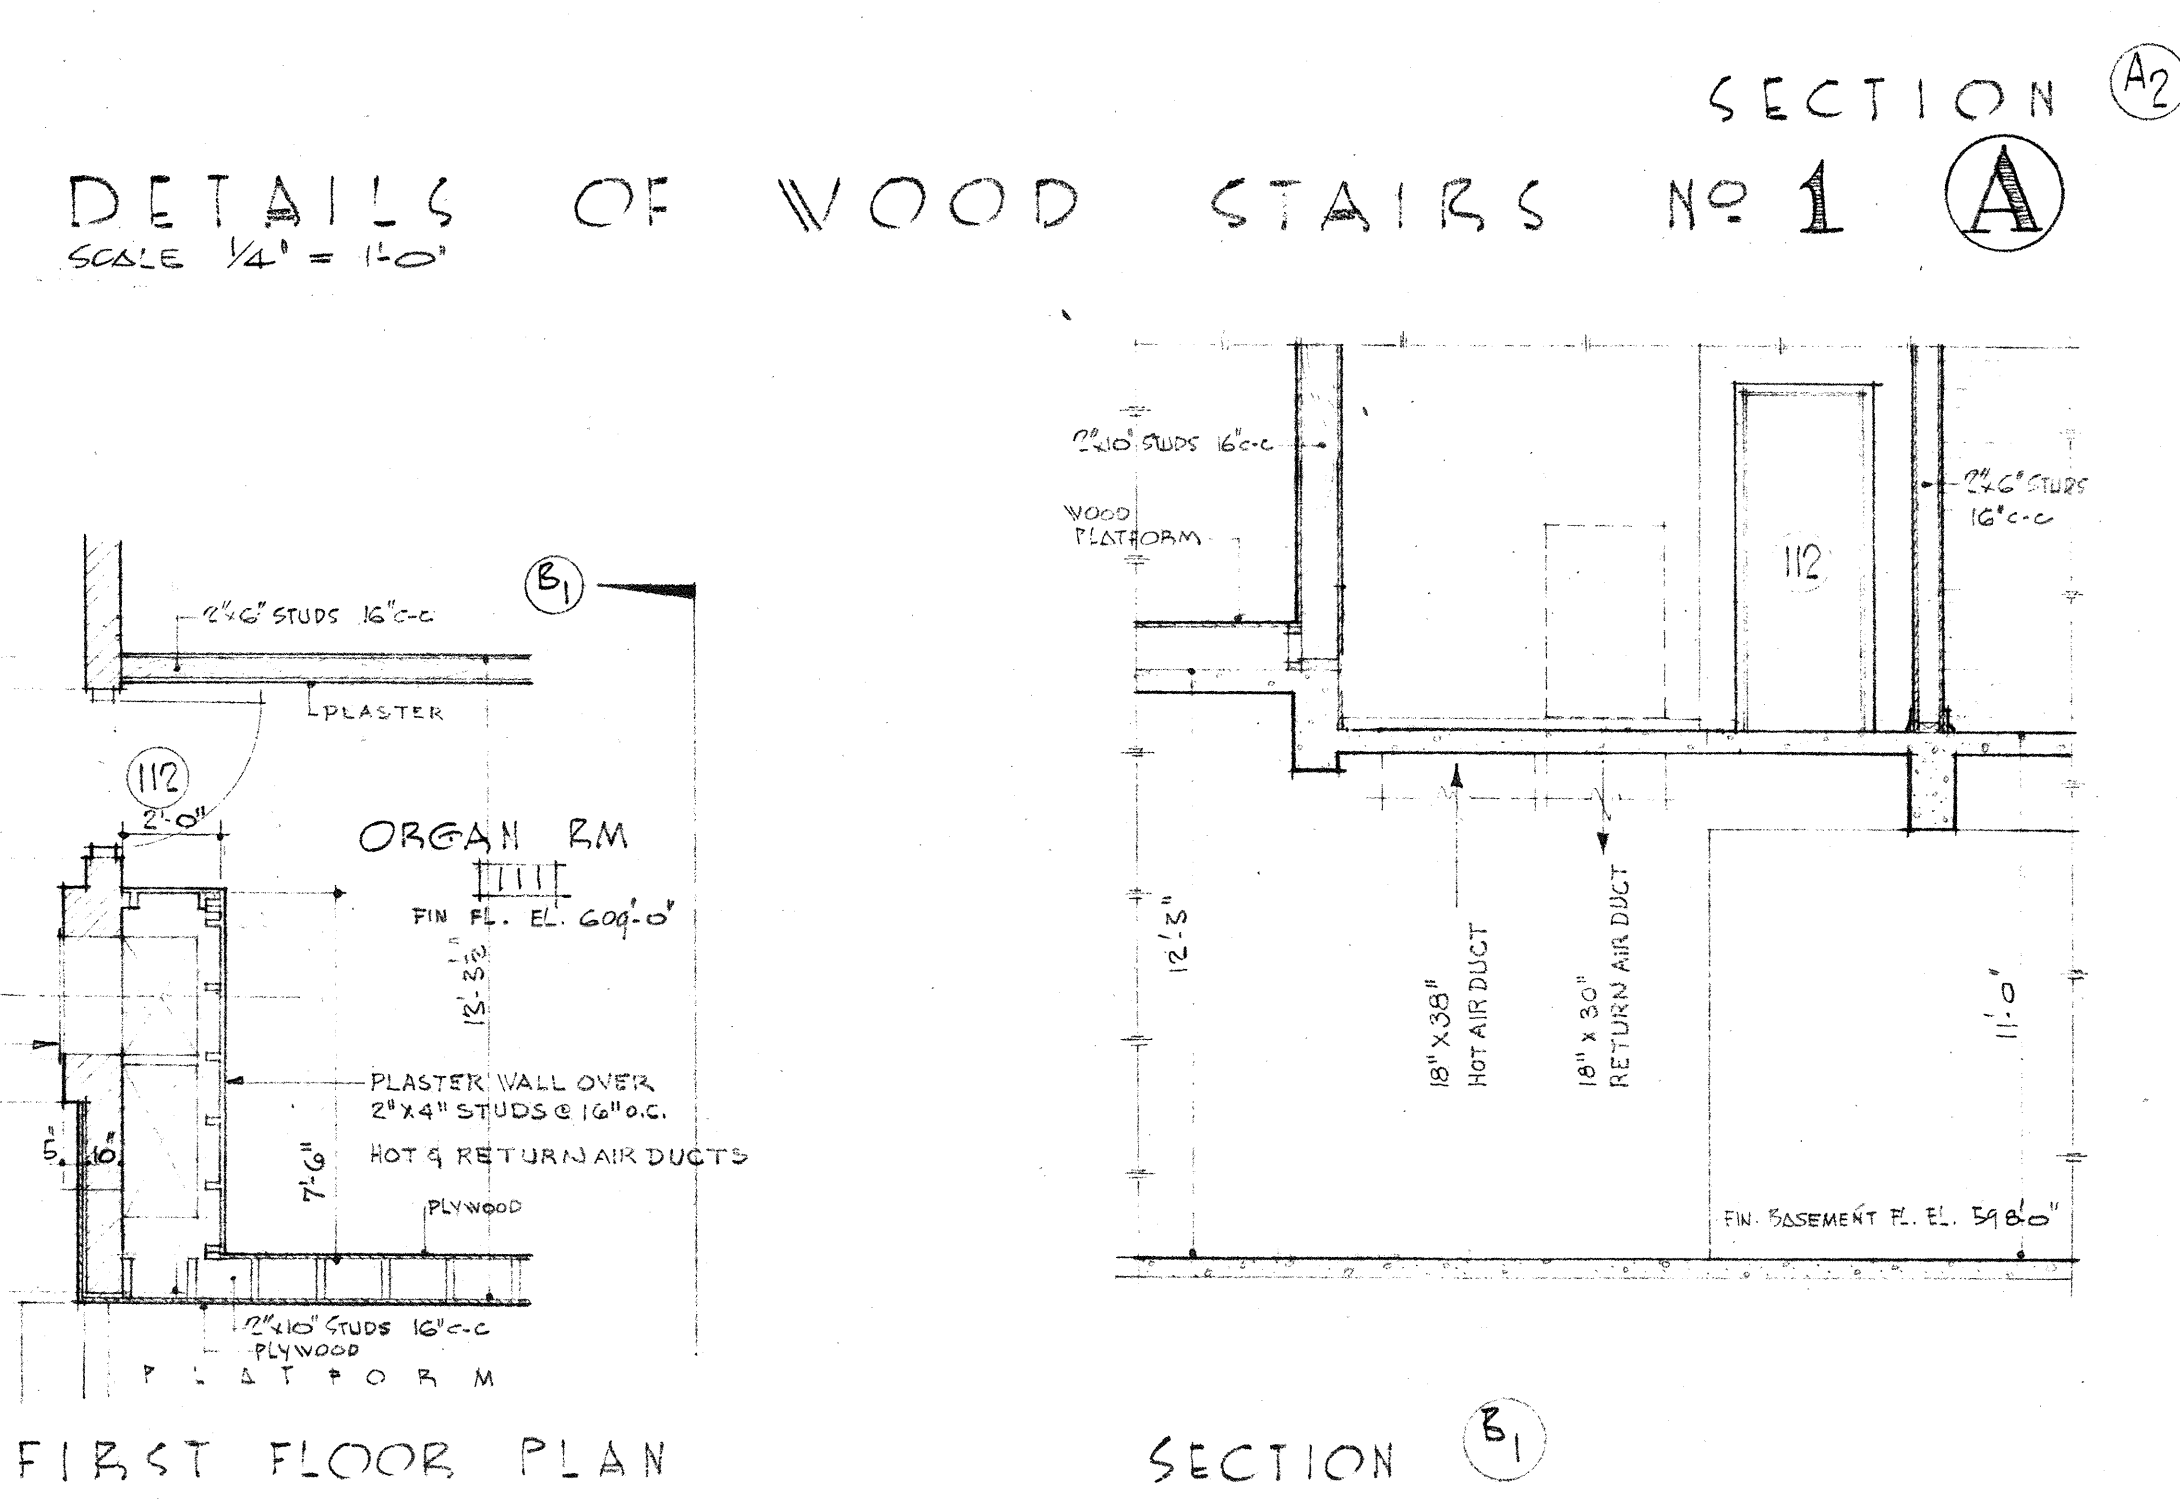
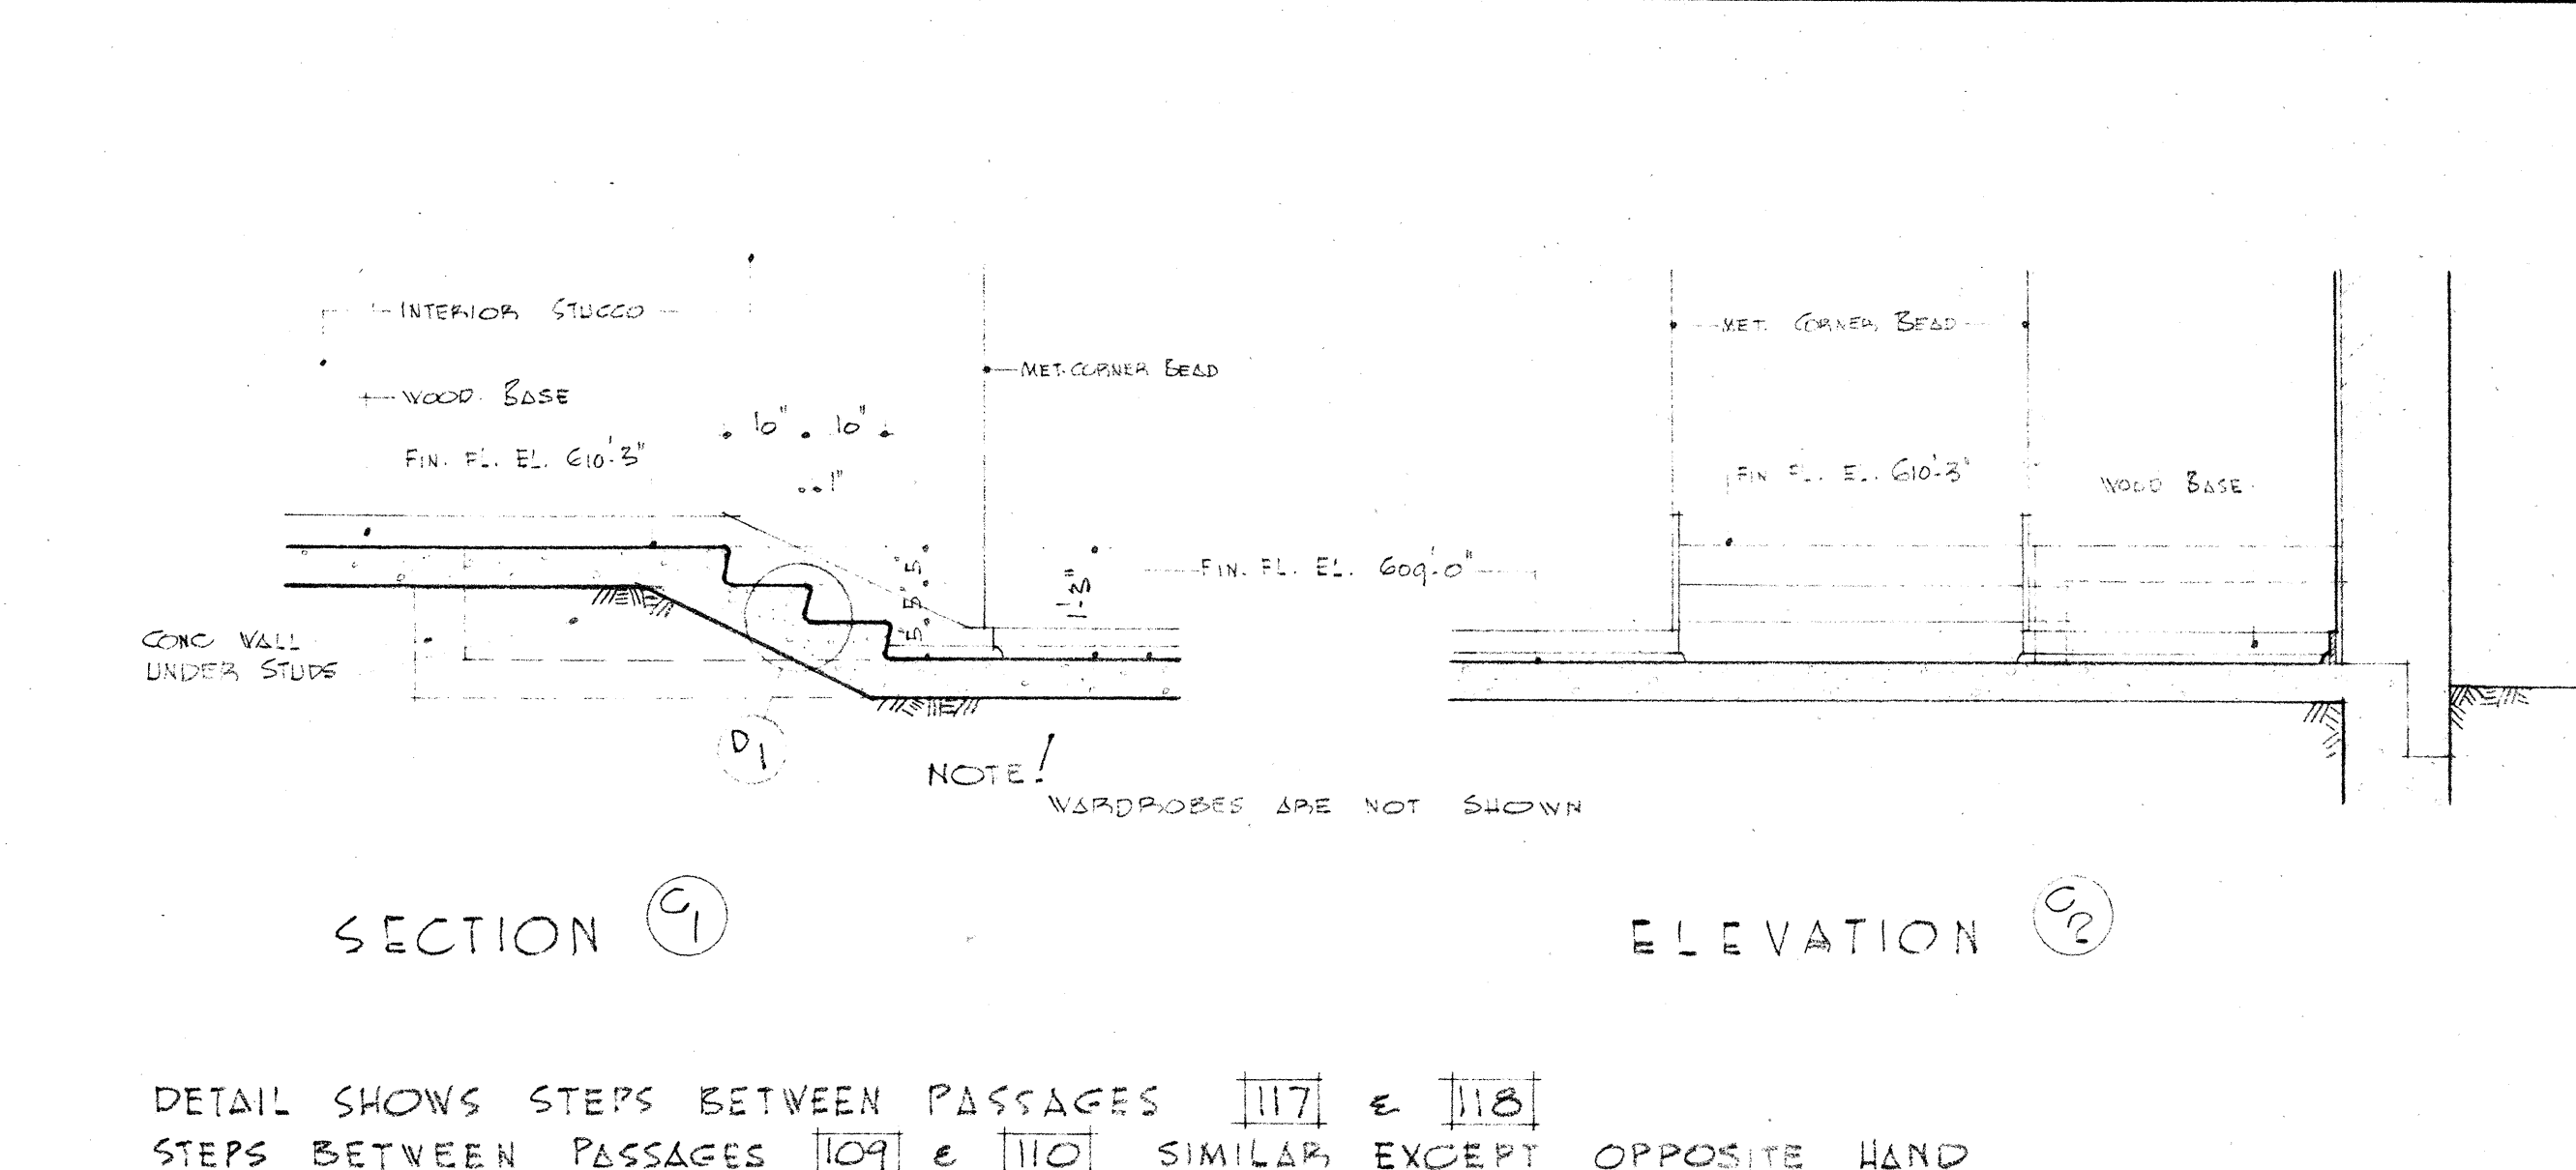
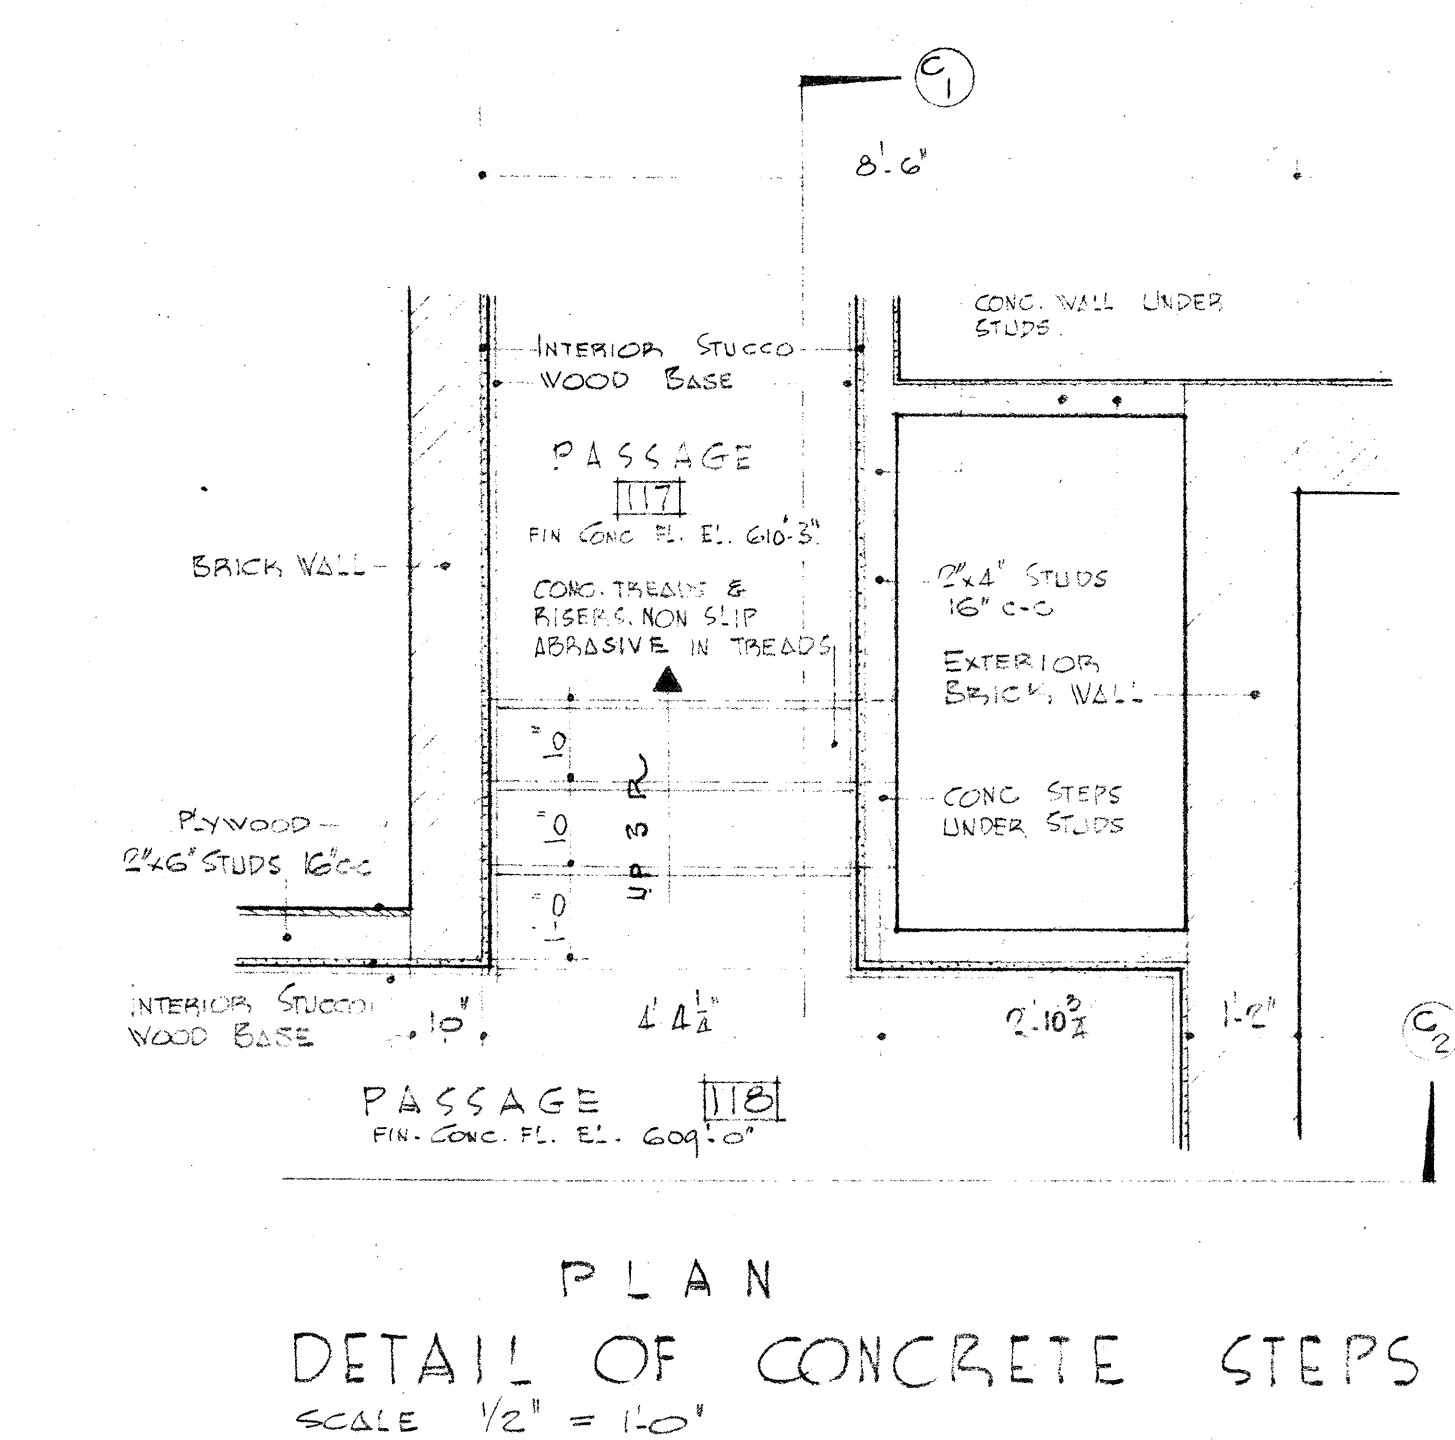
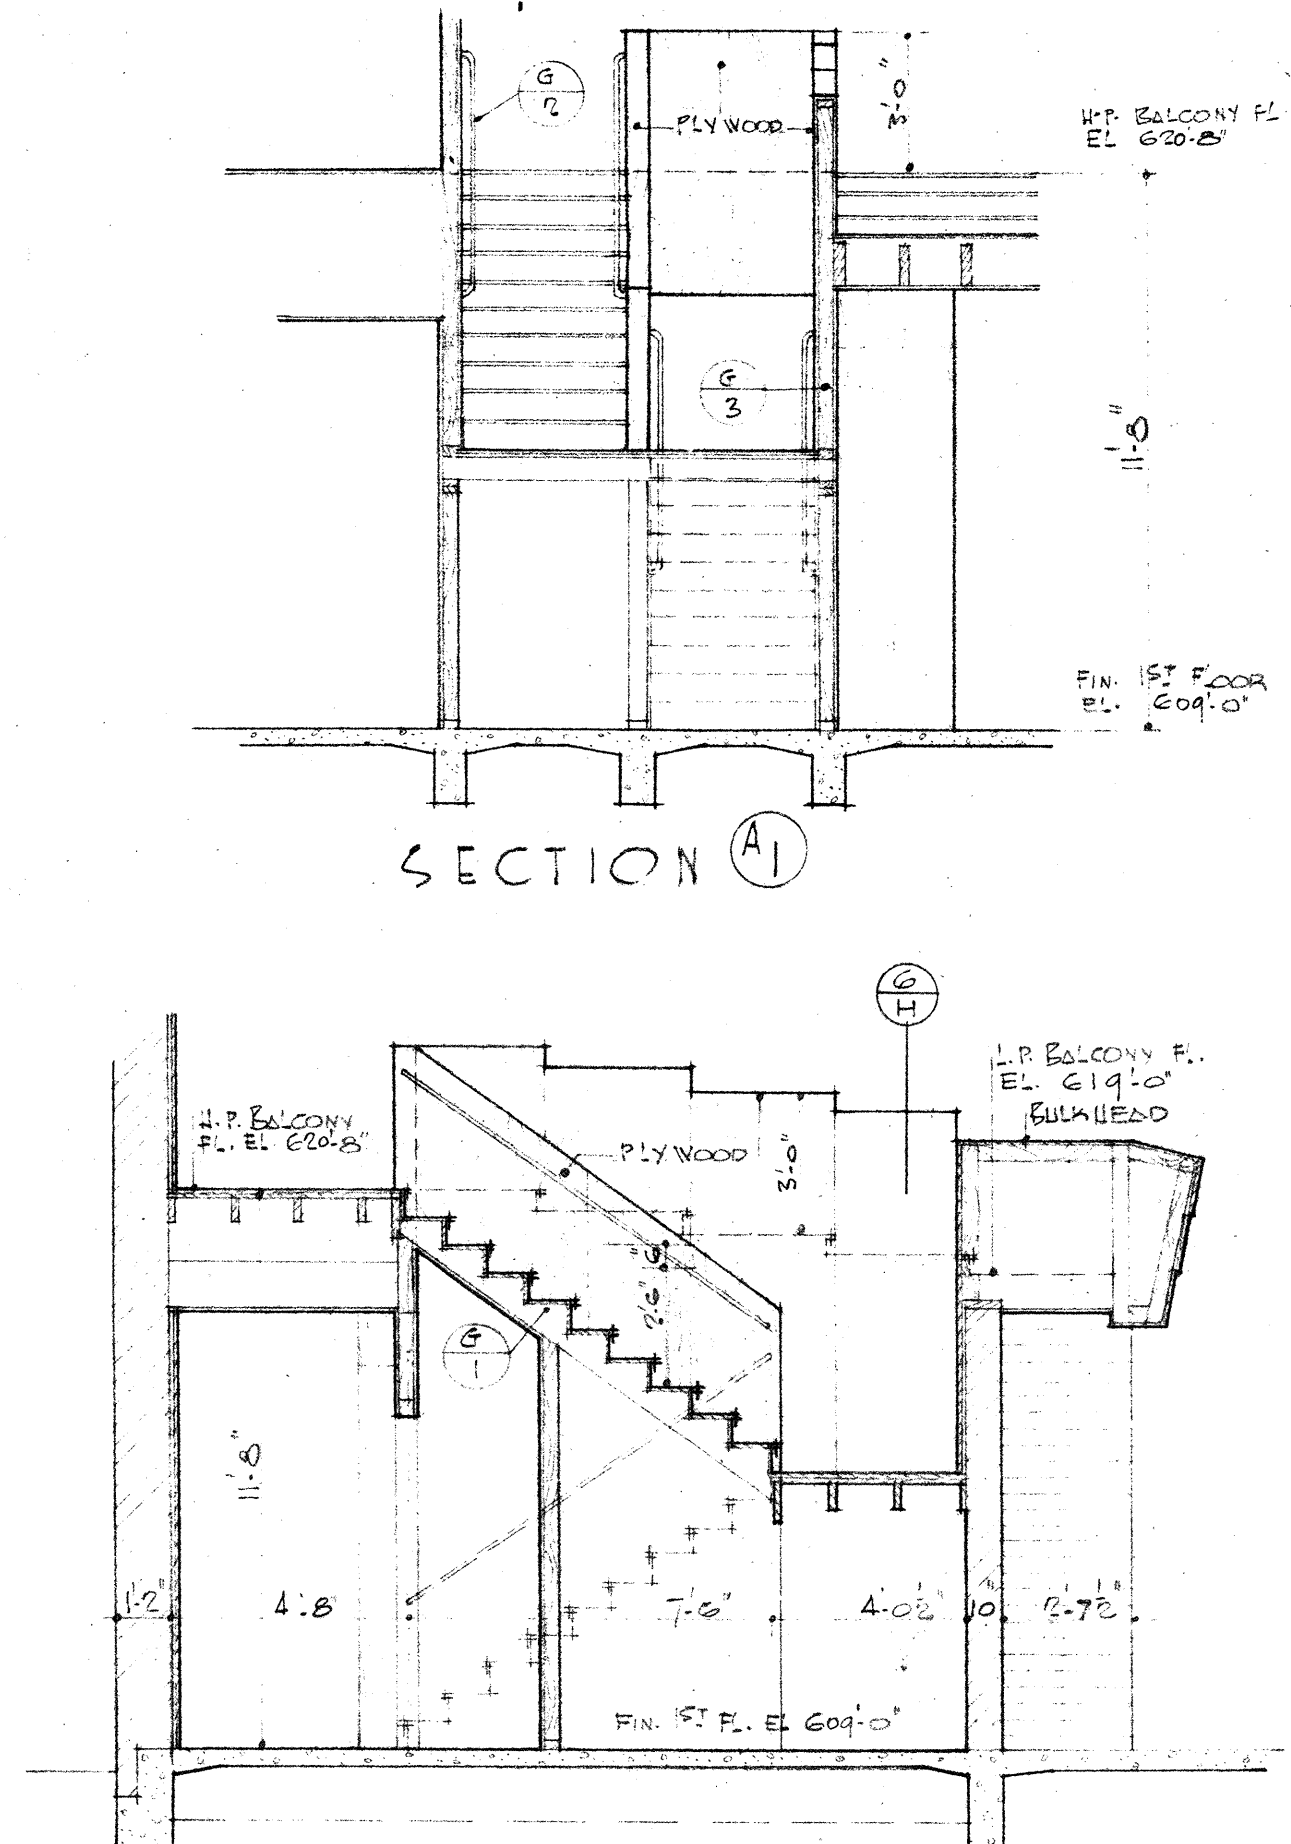


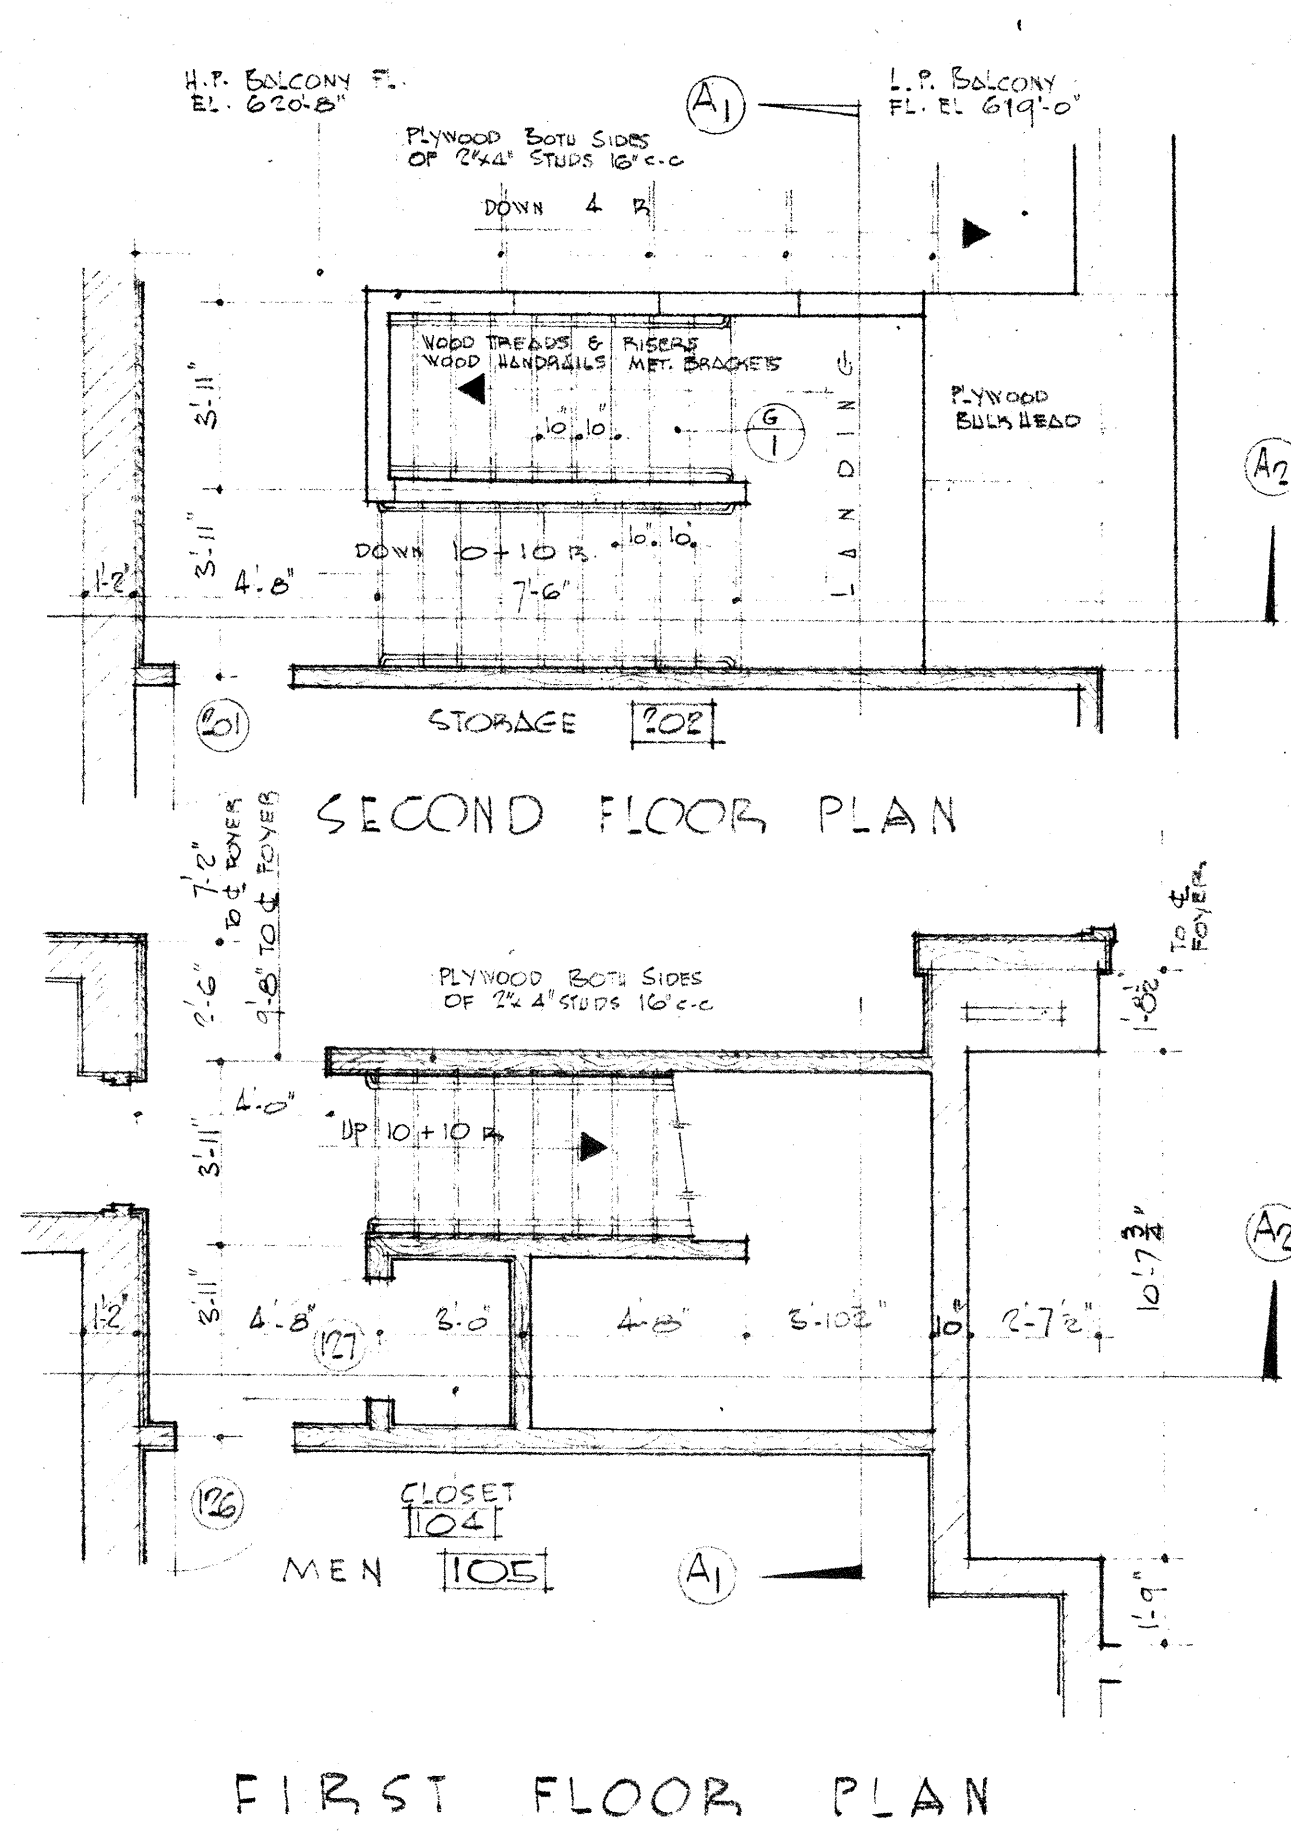

DETAILS OF DUCT PASSAGE AT ORGAN RNS

DETAILS OF WOOD PLATFORM FOR CHOIR STALLS

DETAILS OF TREADS-RISERS HANDRAIL & BRACKETS