

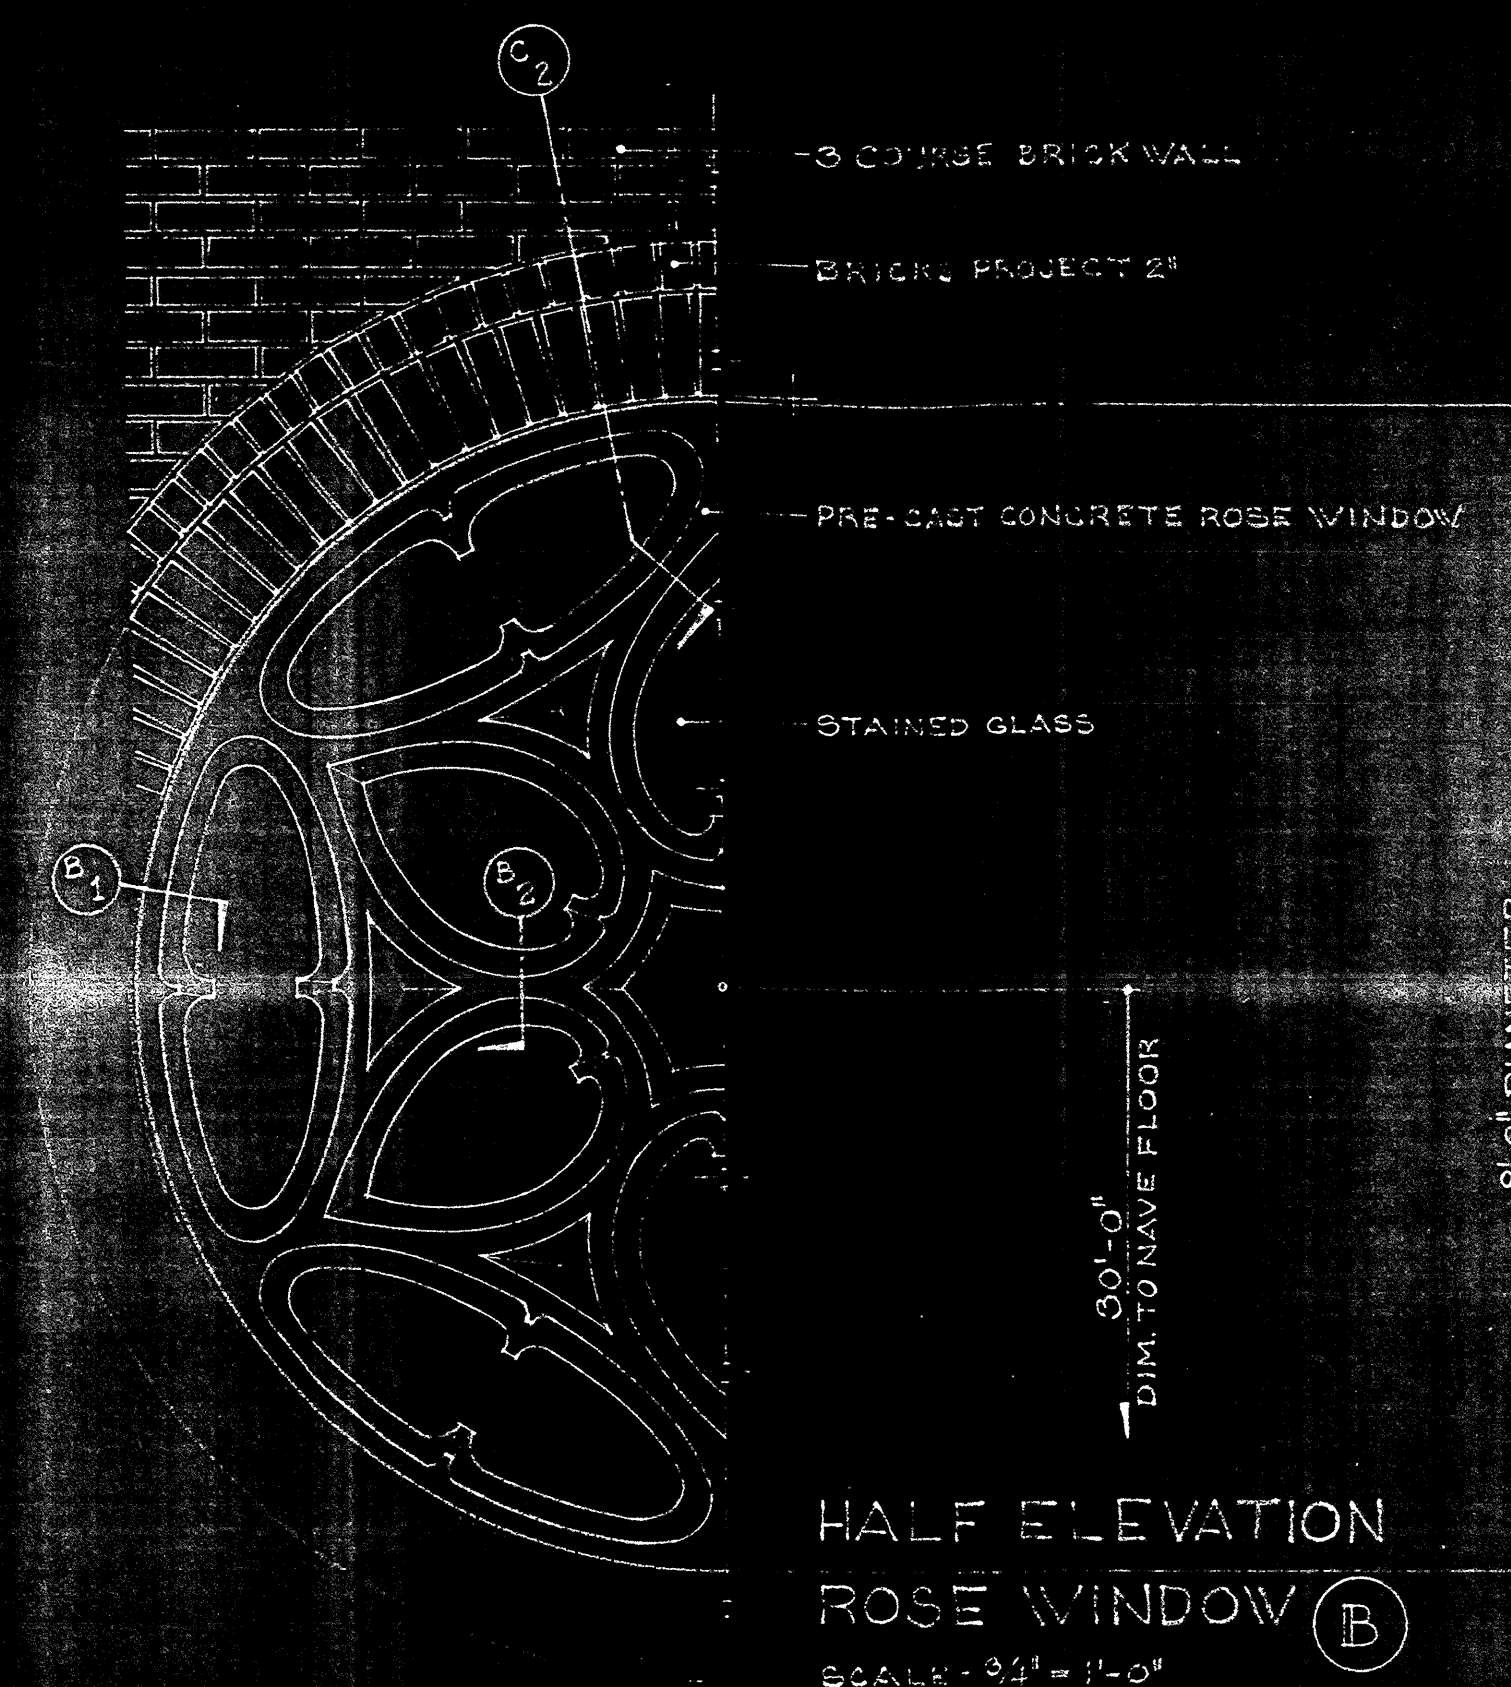
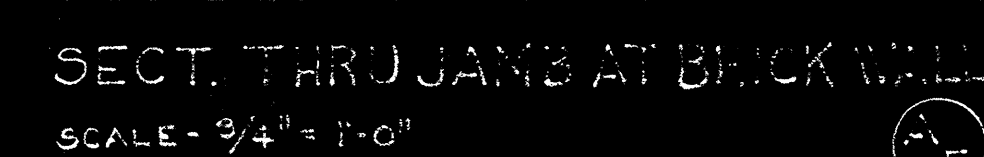
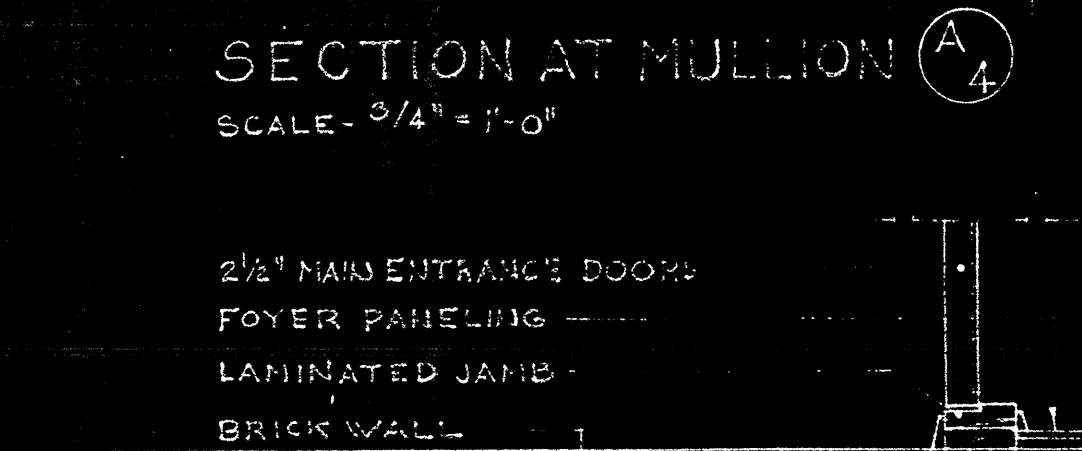
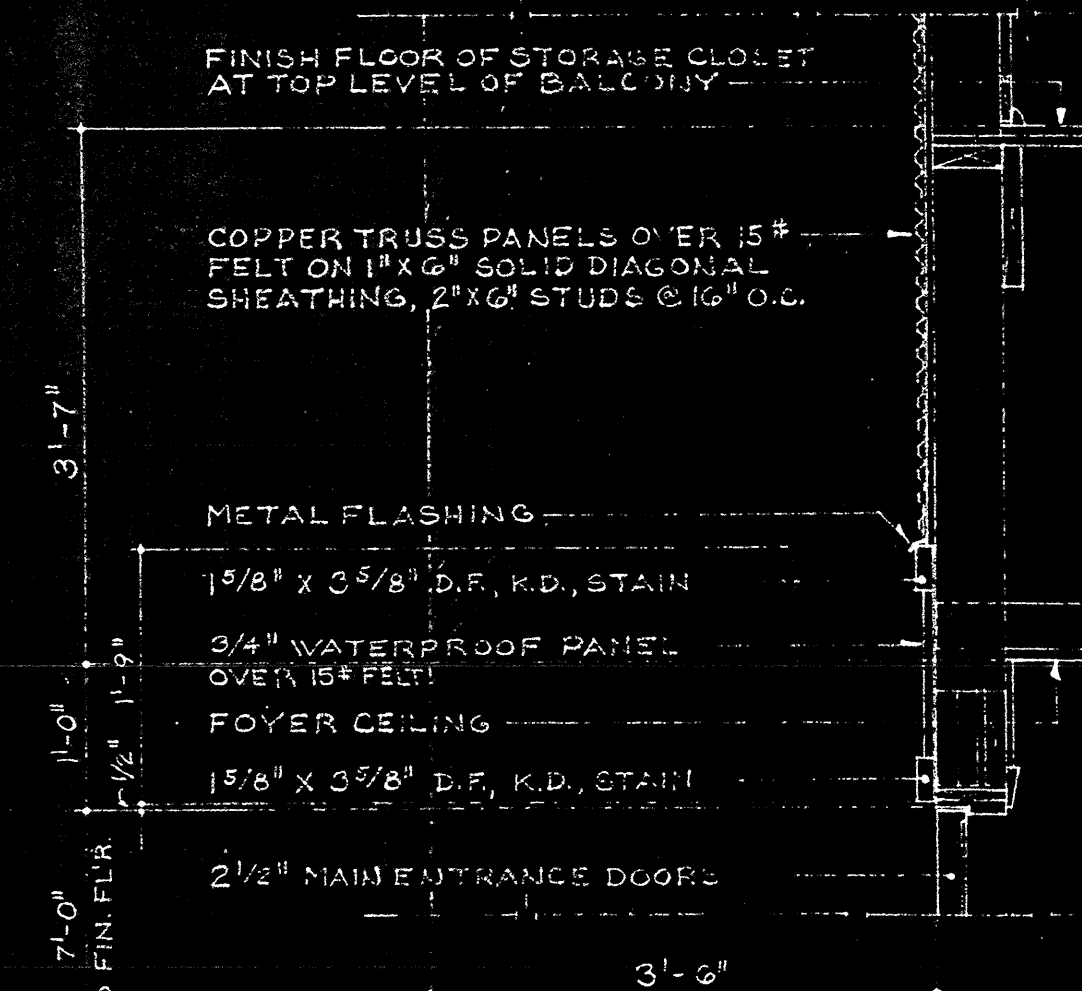
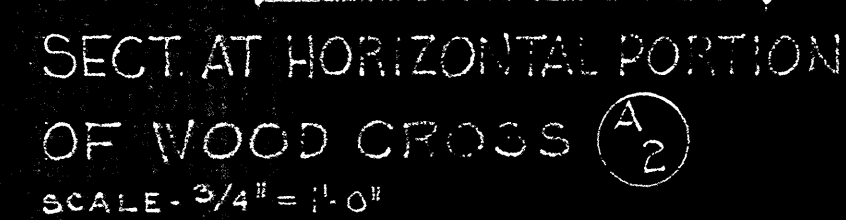
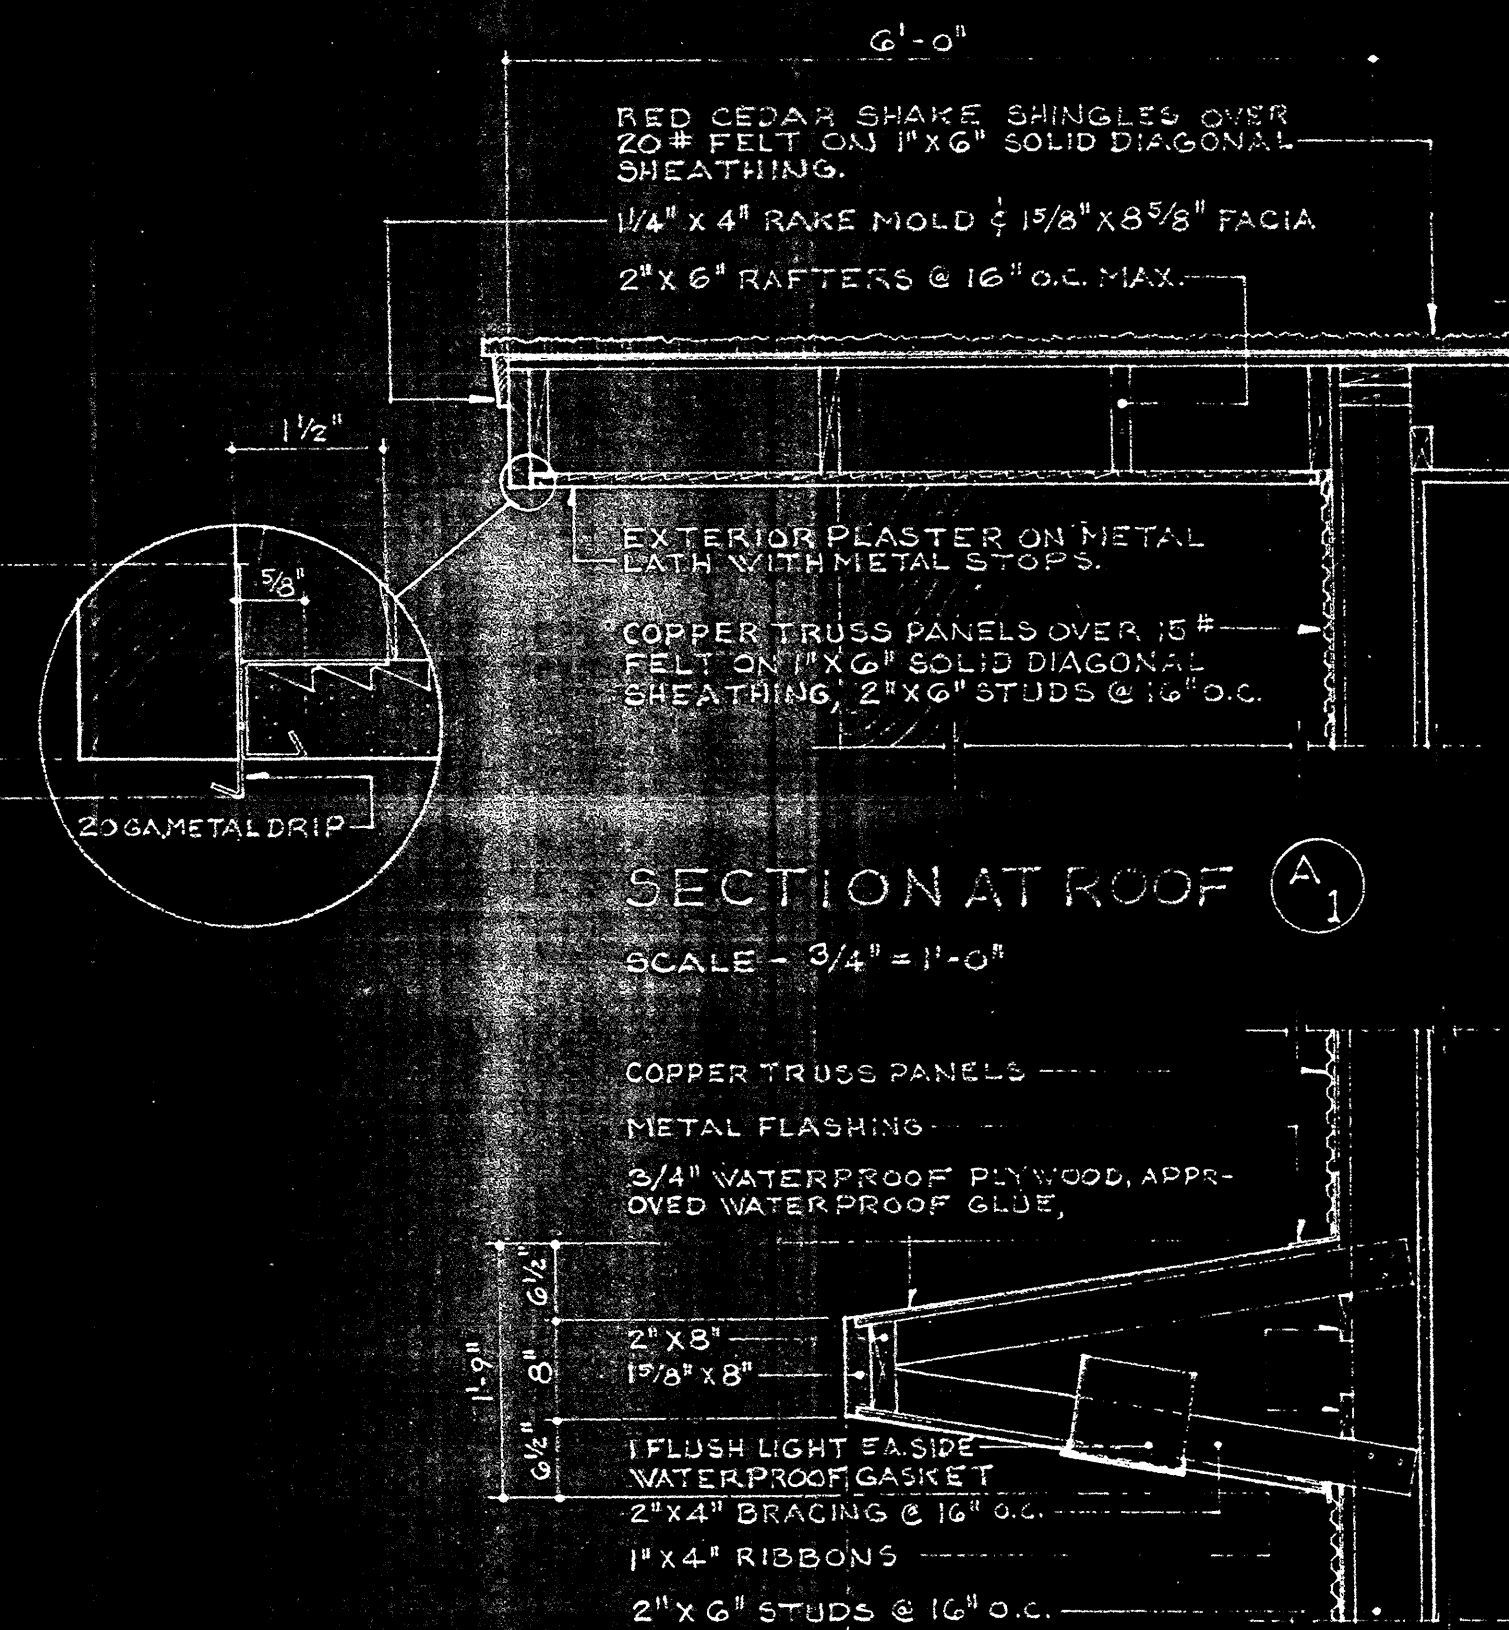
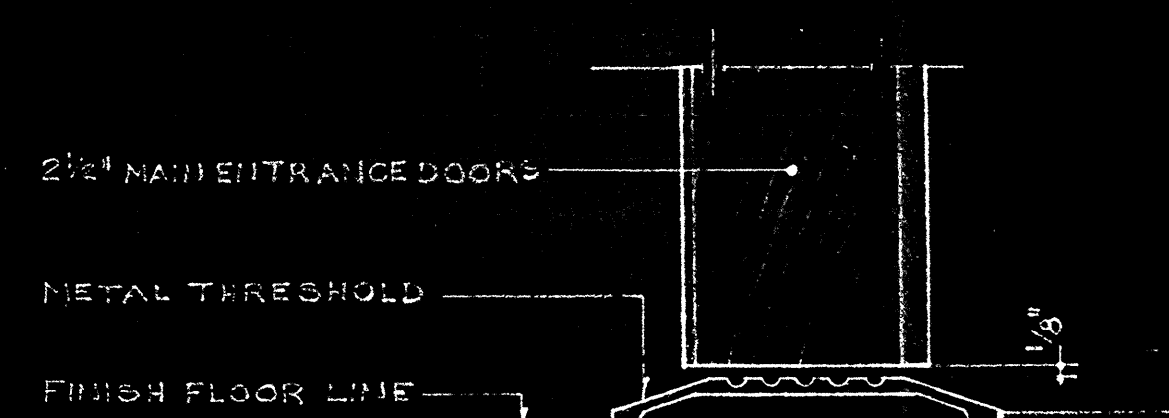
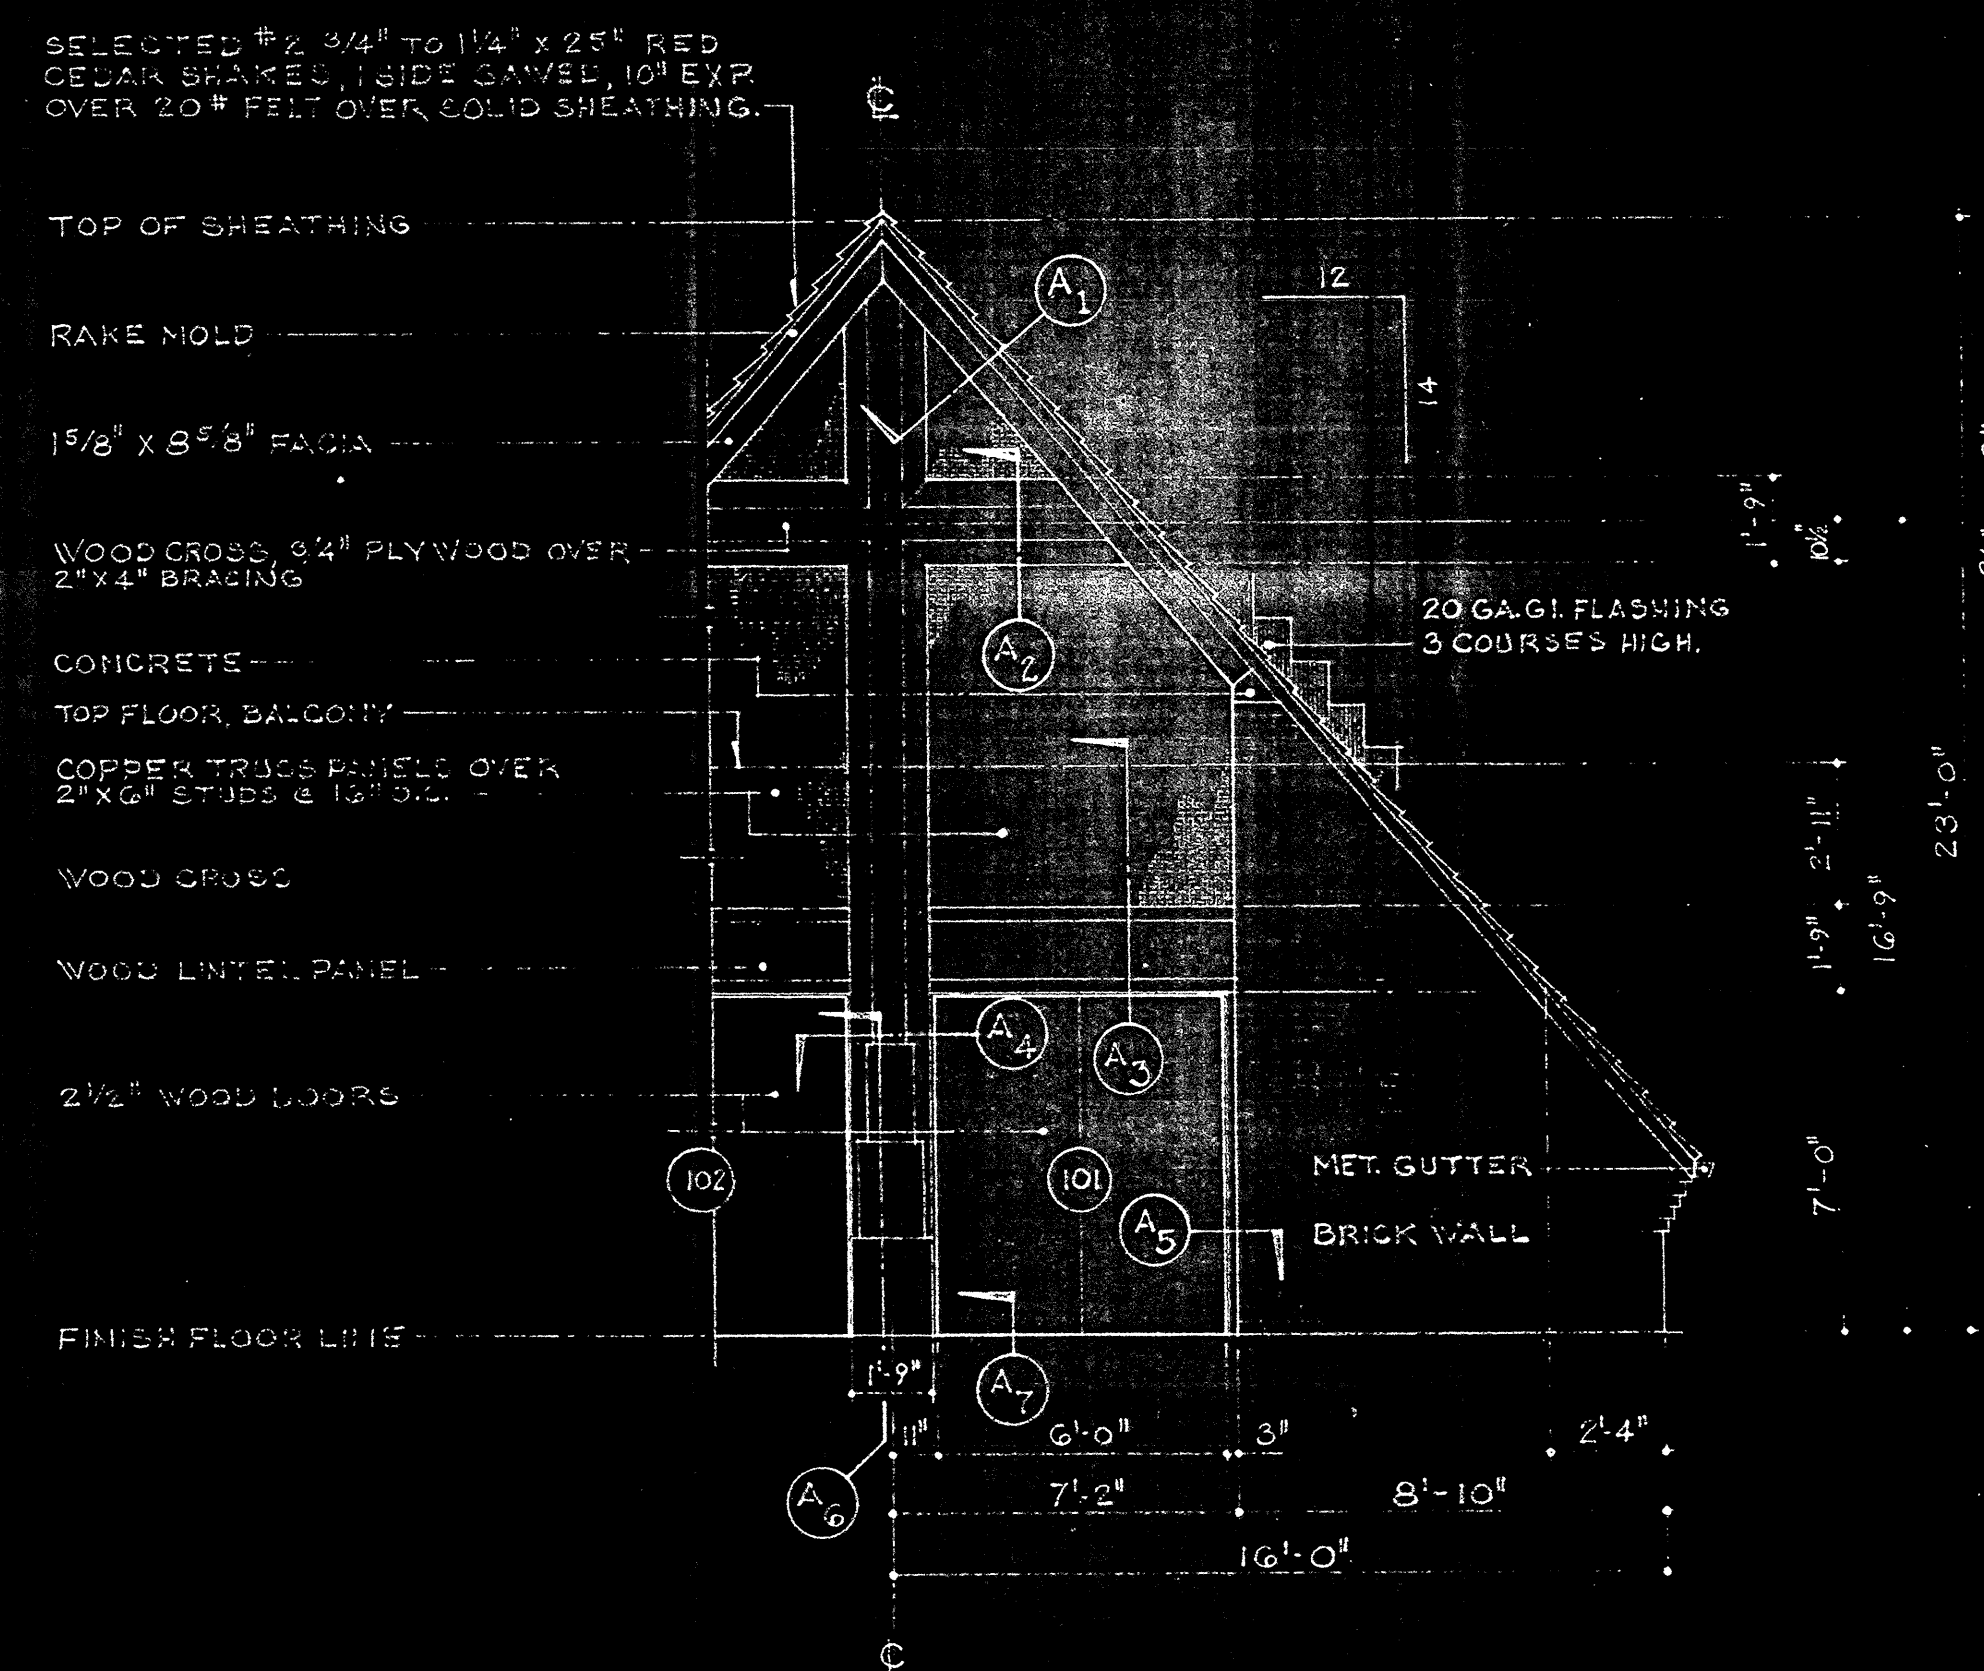
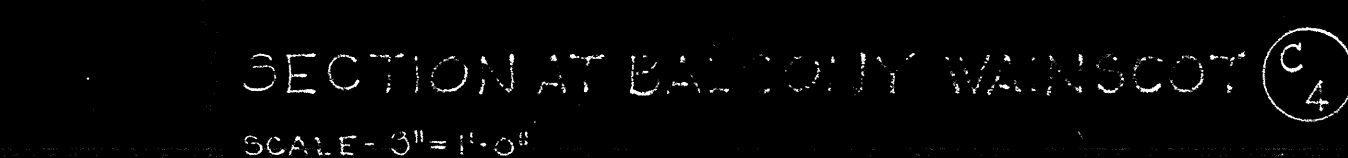


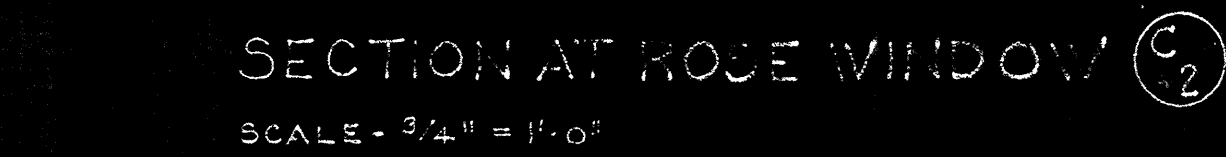

PRE-CAST SECTIONS-ROSE WINDOW

PERIMETER SEGMENT-AC BROWN (B)

INNER SEGMENTS - AS NOTED (3)

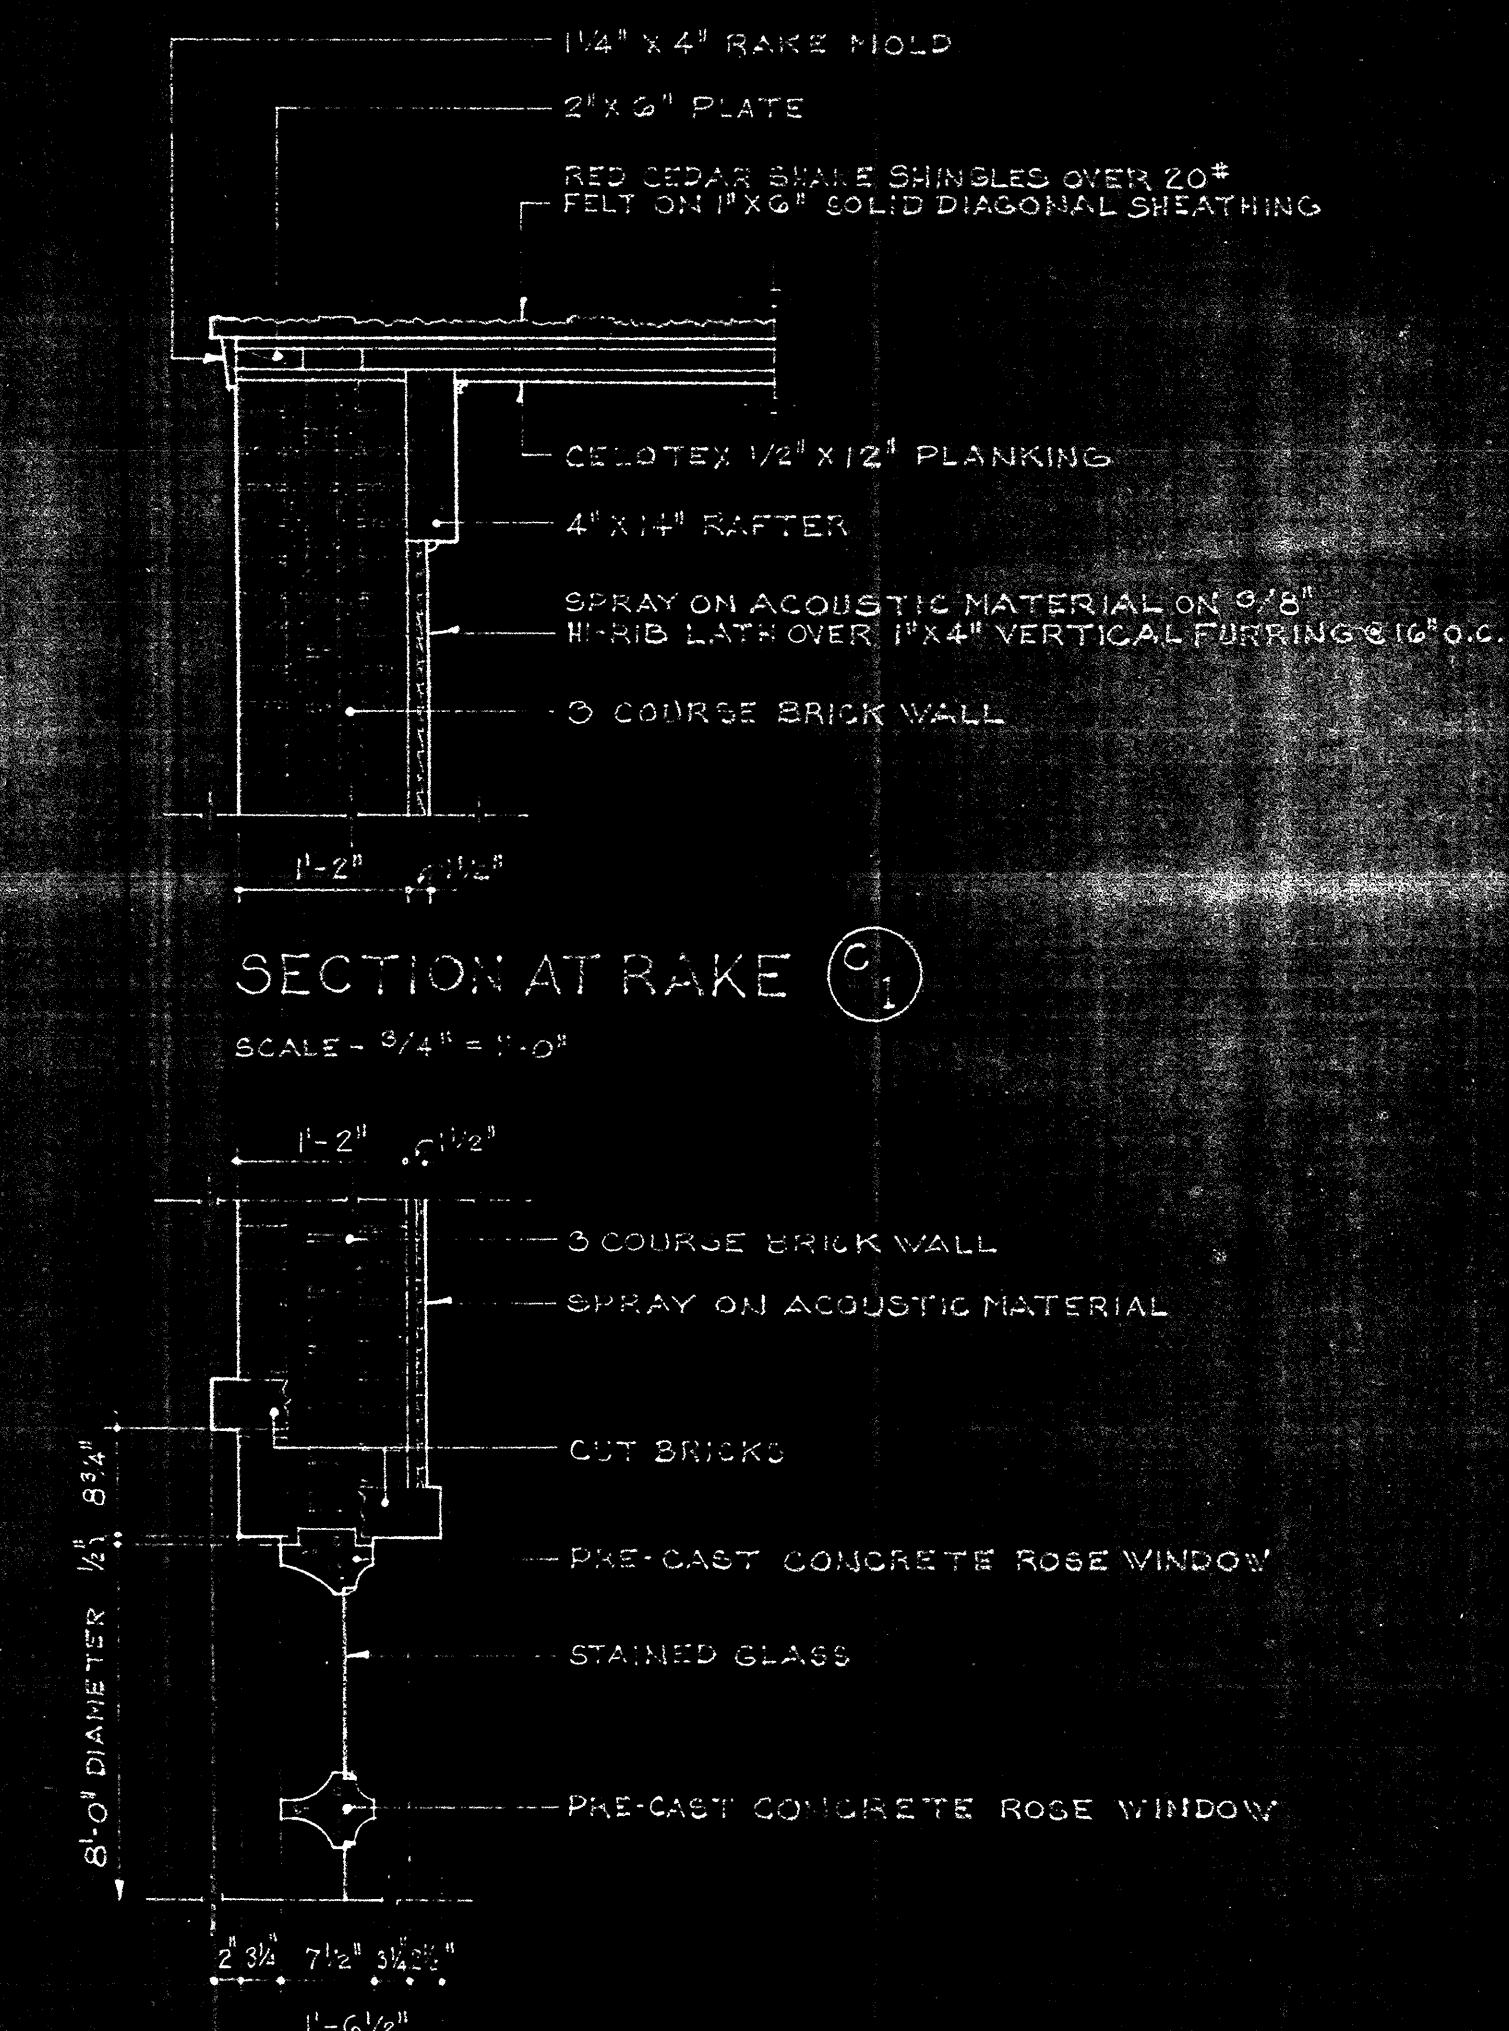

DETAILS AT ROSE LINDOW WALL ©

Remarks

Revisions

—Engineers

Approval

AUSTIN FIELD & FRY

2311 WEST THIRD STREET • LOS ANGELES 5, CALIFORNIA • DUNKIRK 8-1326

DETAILS OF SOUTH WALL & ROSE WINDOW WALL
ST. EDMUNDS EPISCOPAL CHURCH
SAN MARINO, CALIF.

DATE 2-8-82
COMM. 106
SHEET NUM 7