

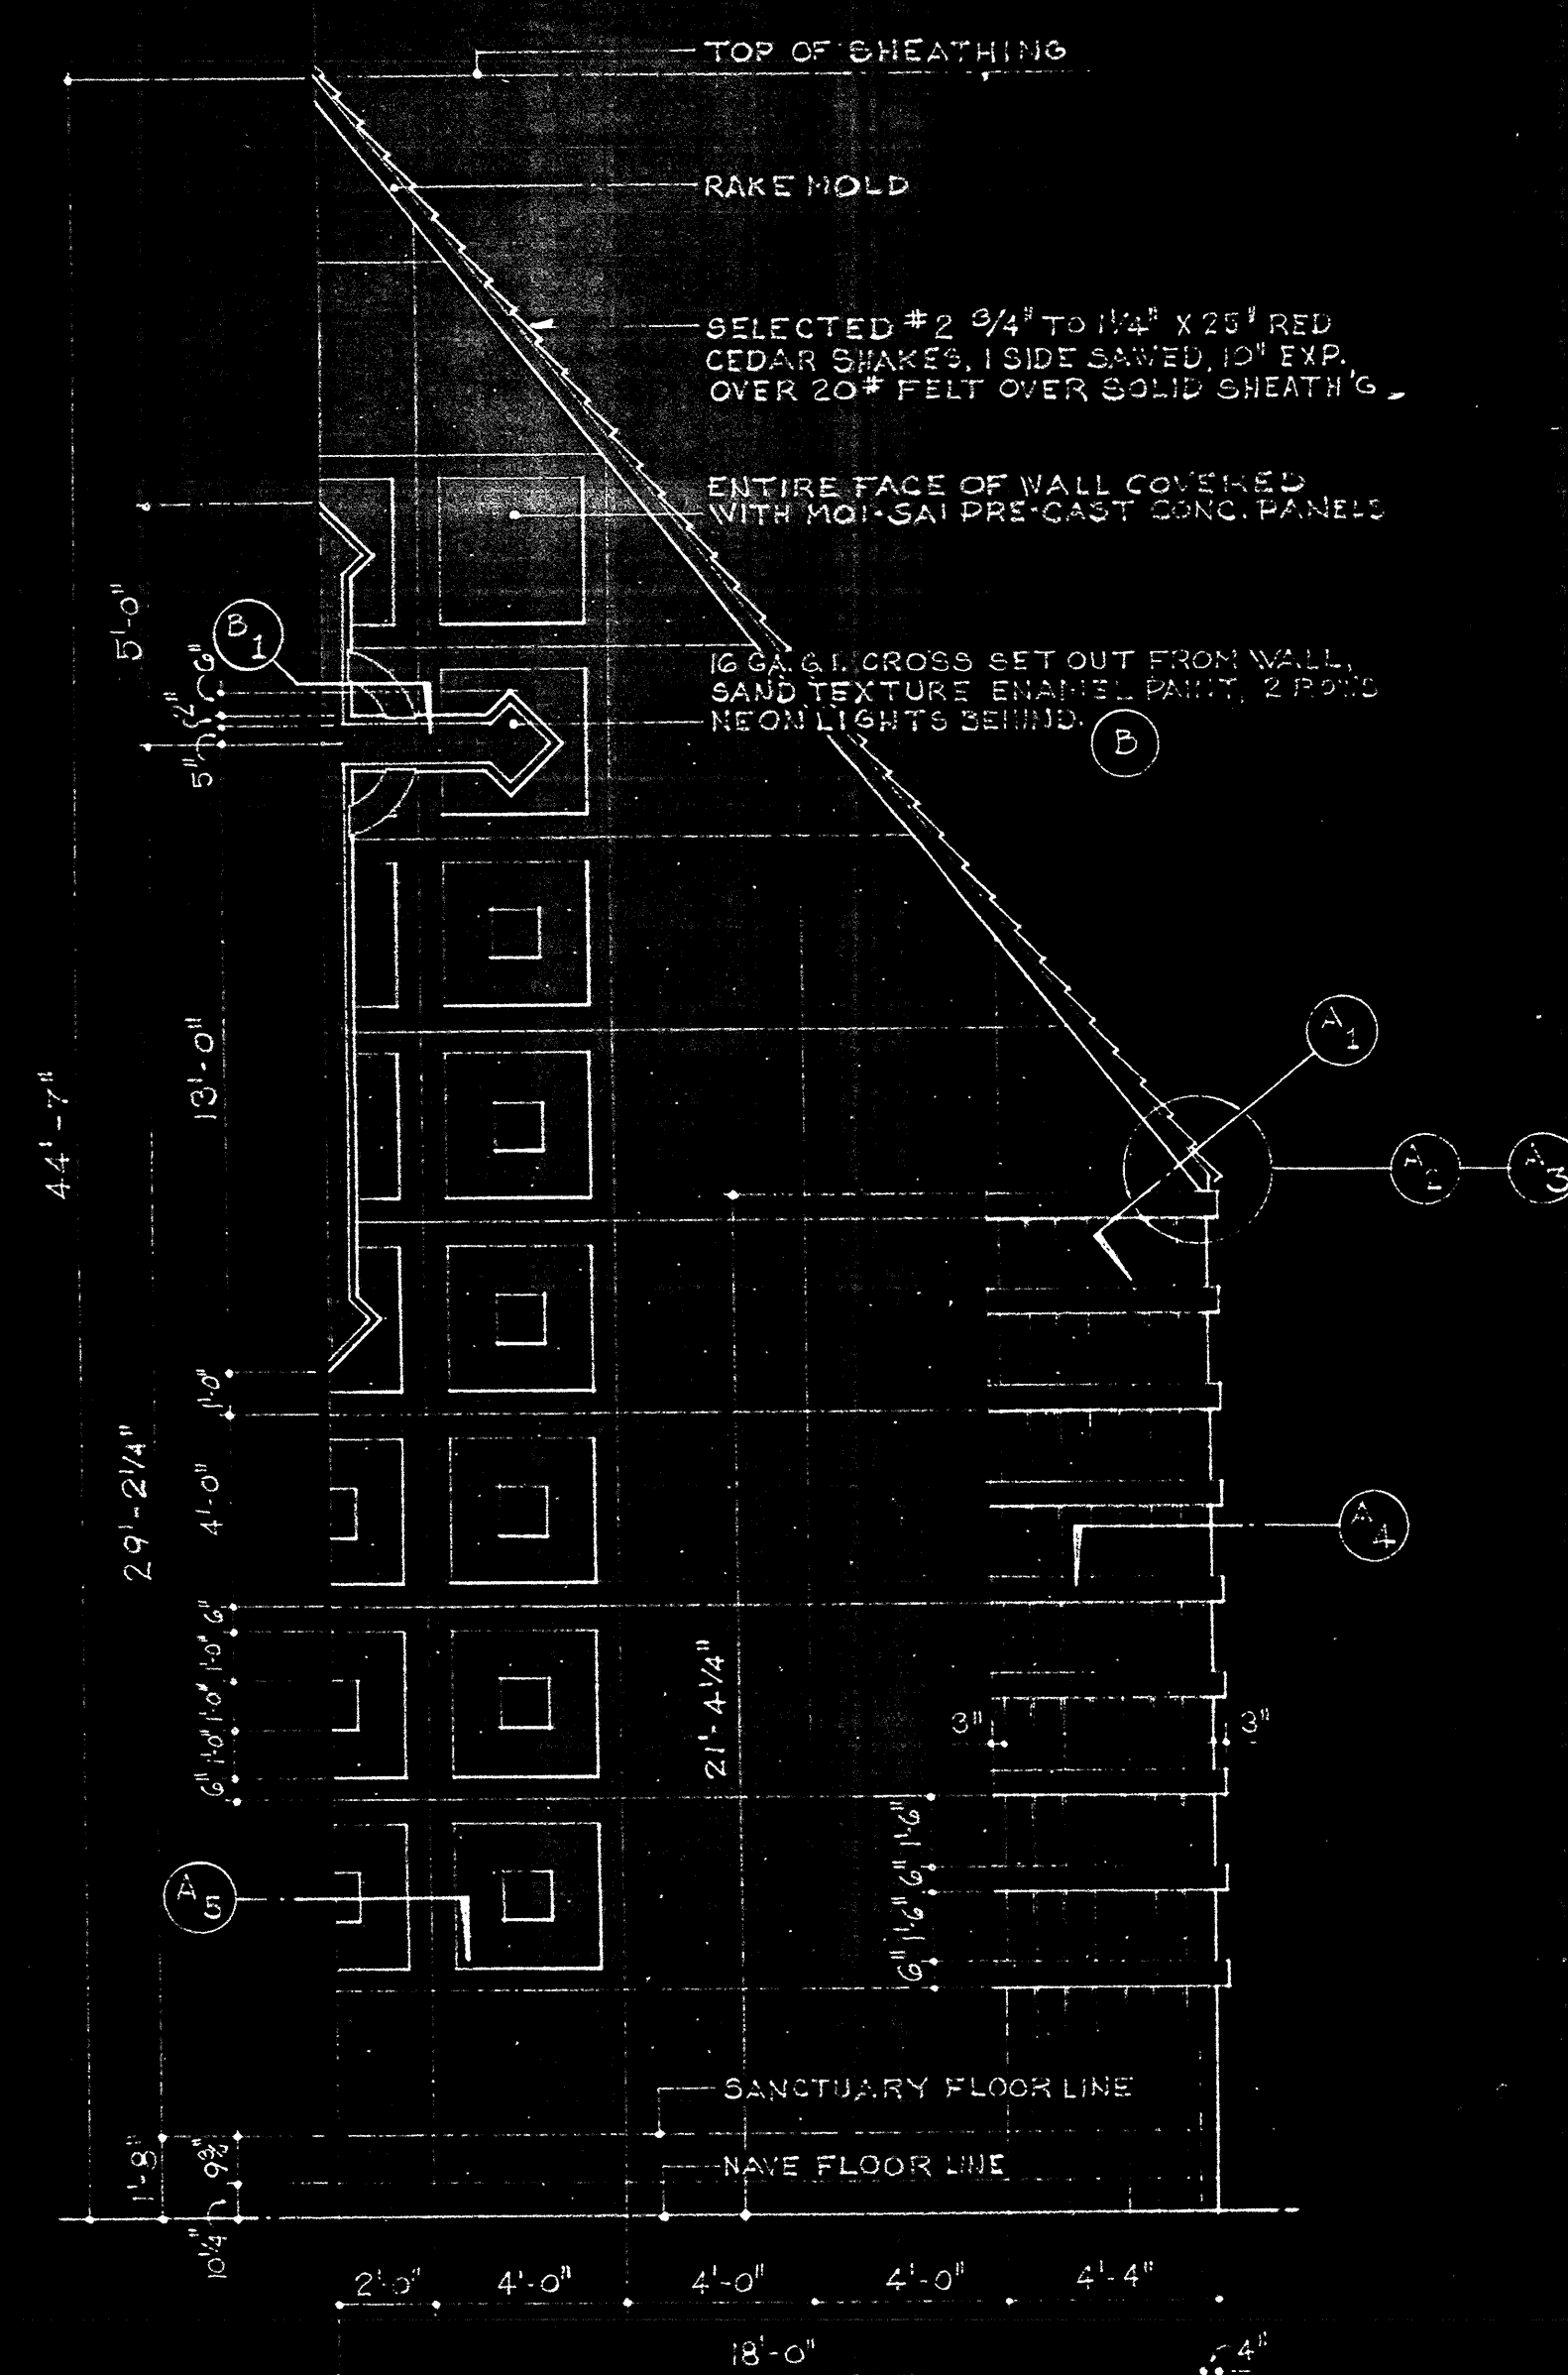


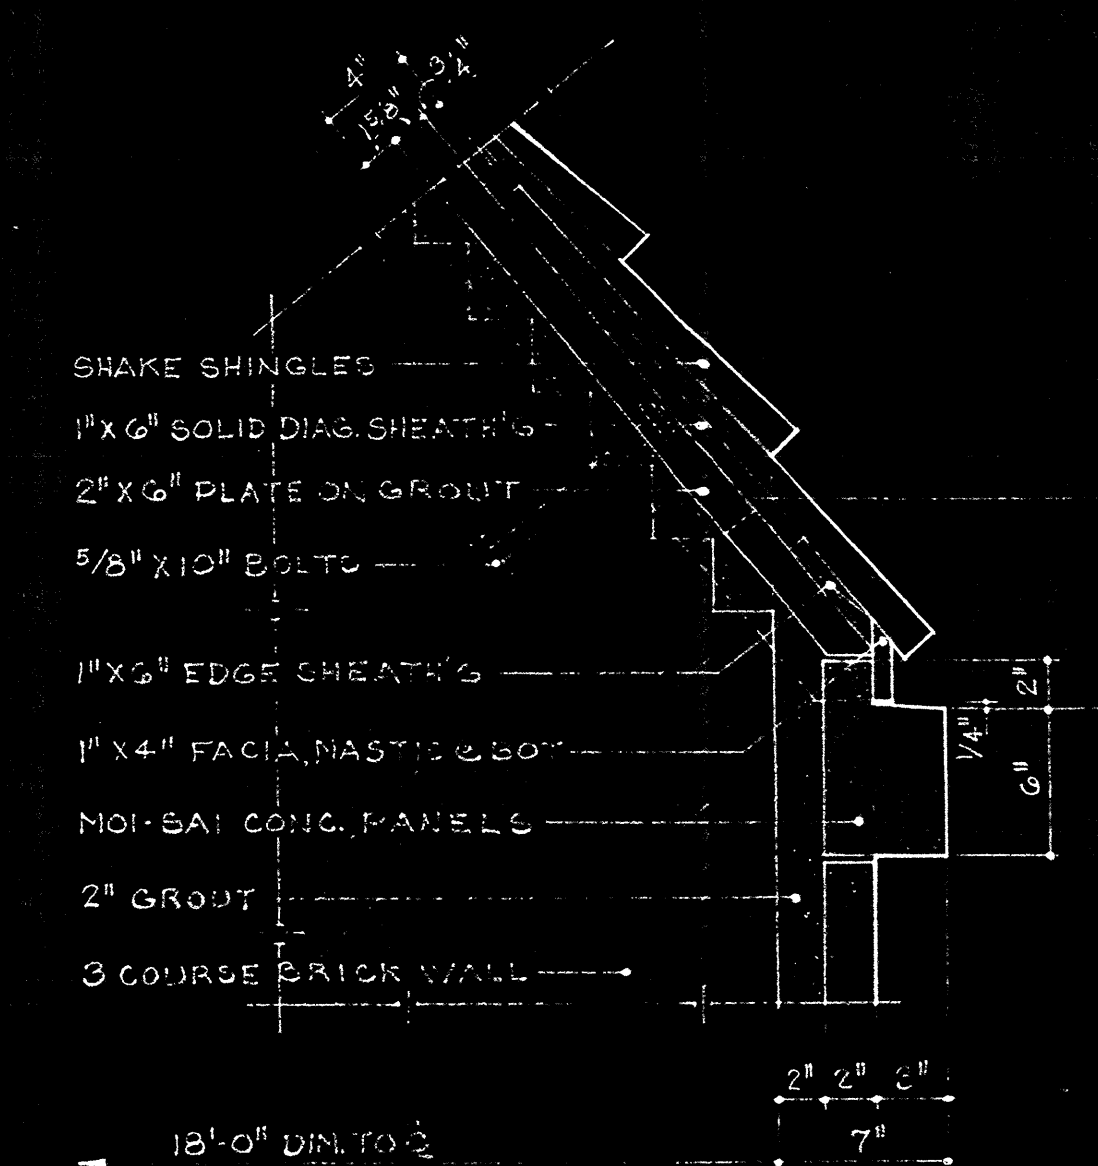



HALF ELEVATION NORTH WALL (A)

SECTION AT CORNER (A)₄


SECTION AT CENTER (A)

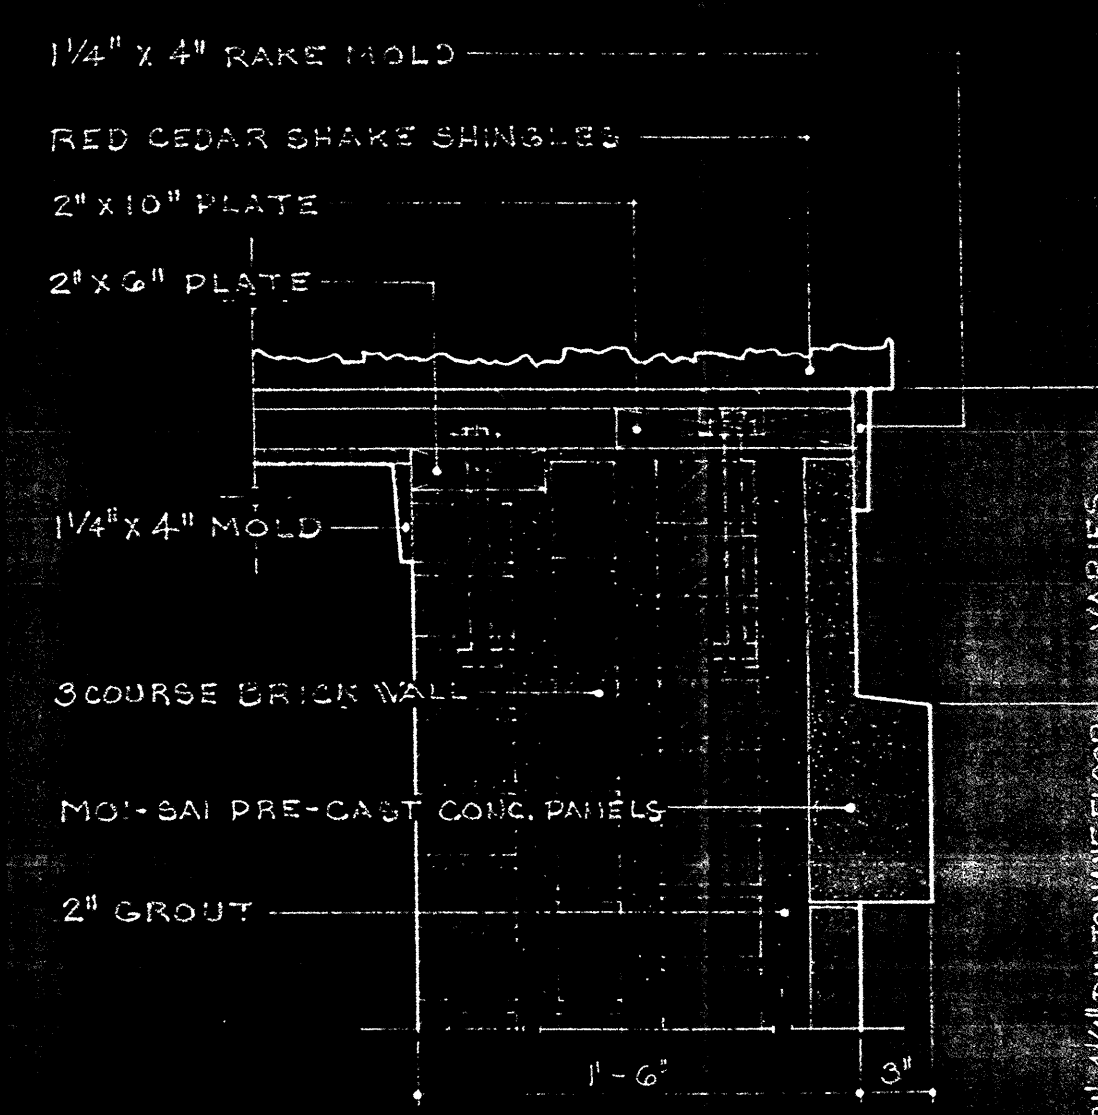

SECTION AIR LEAVE (A)

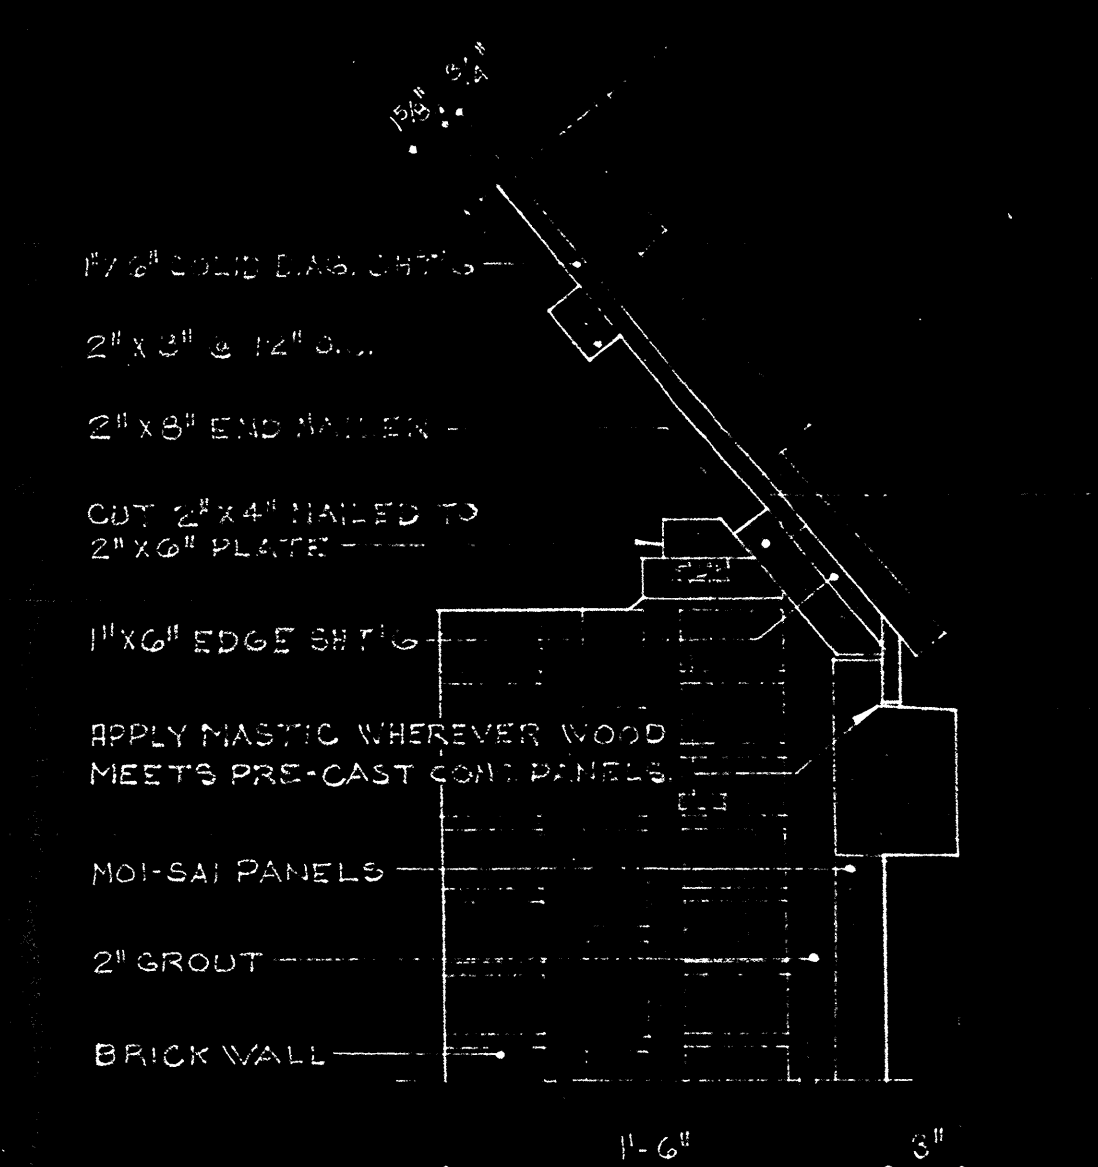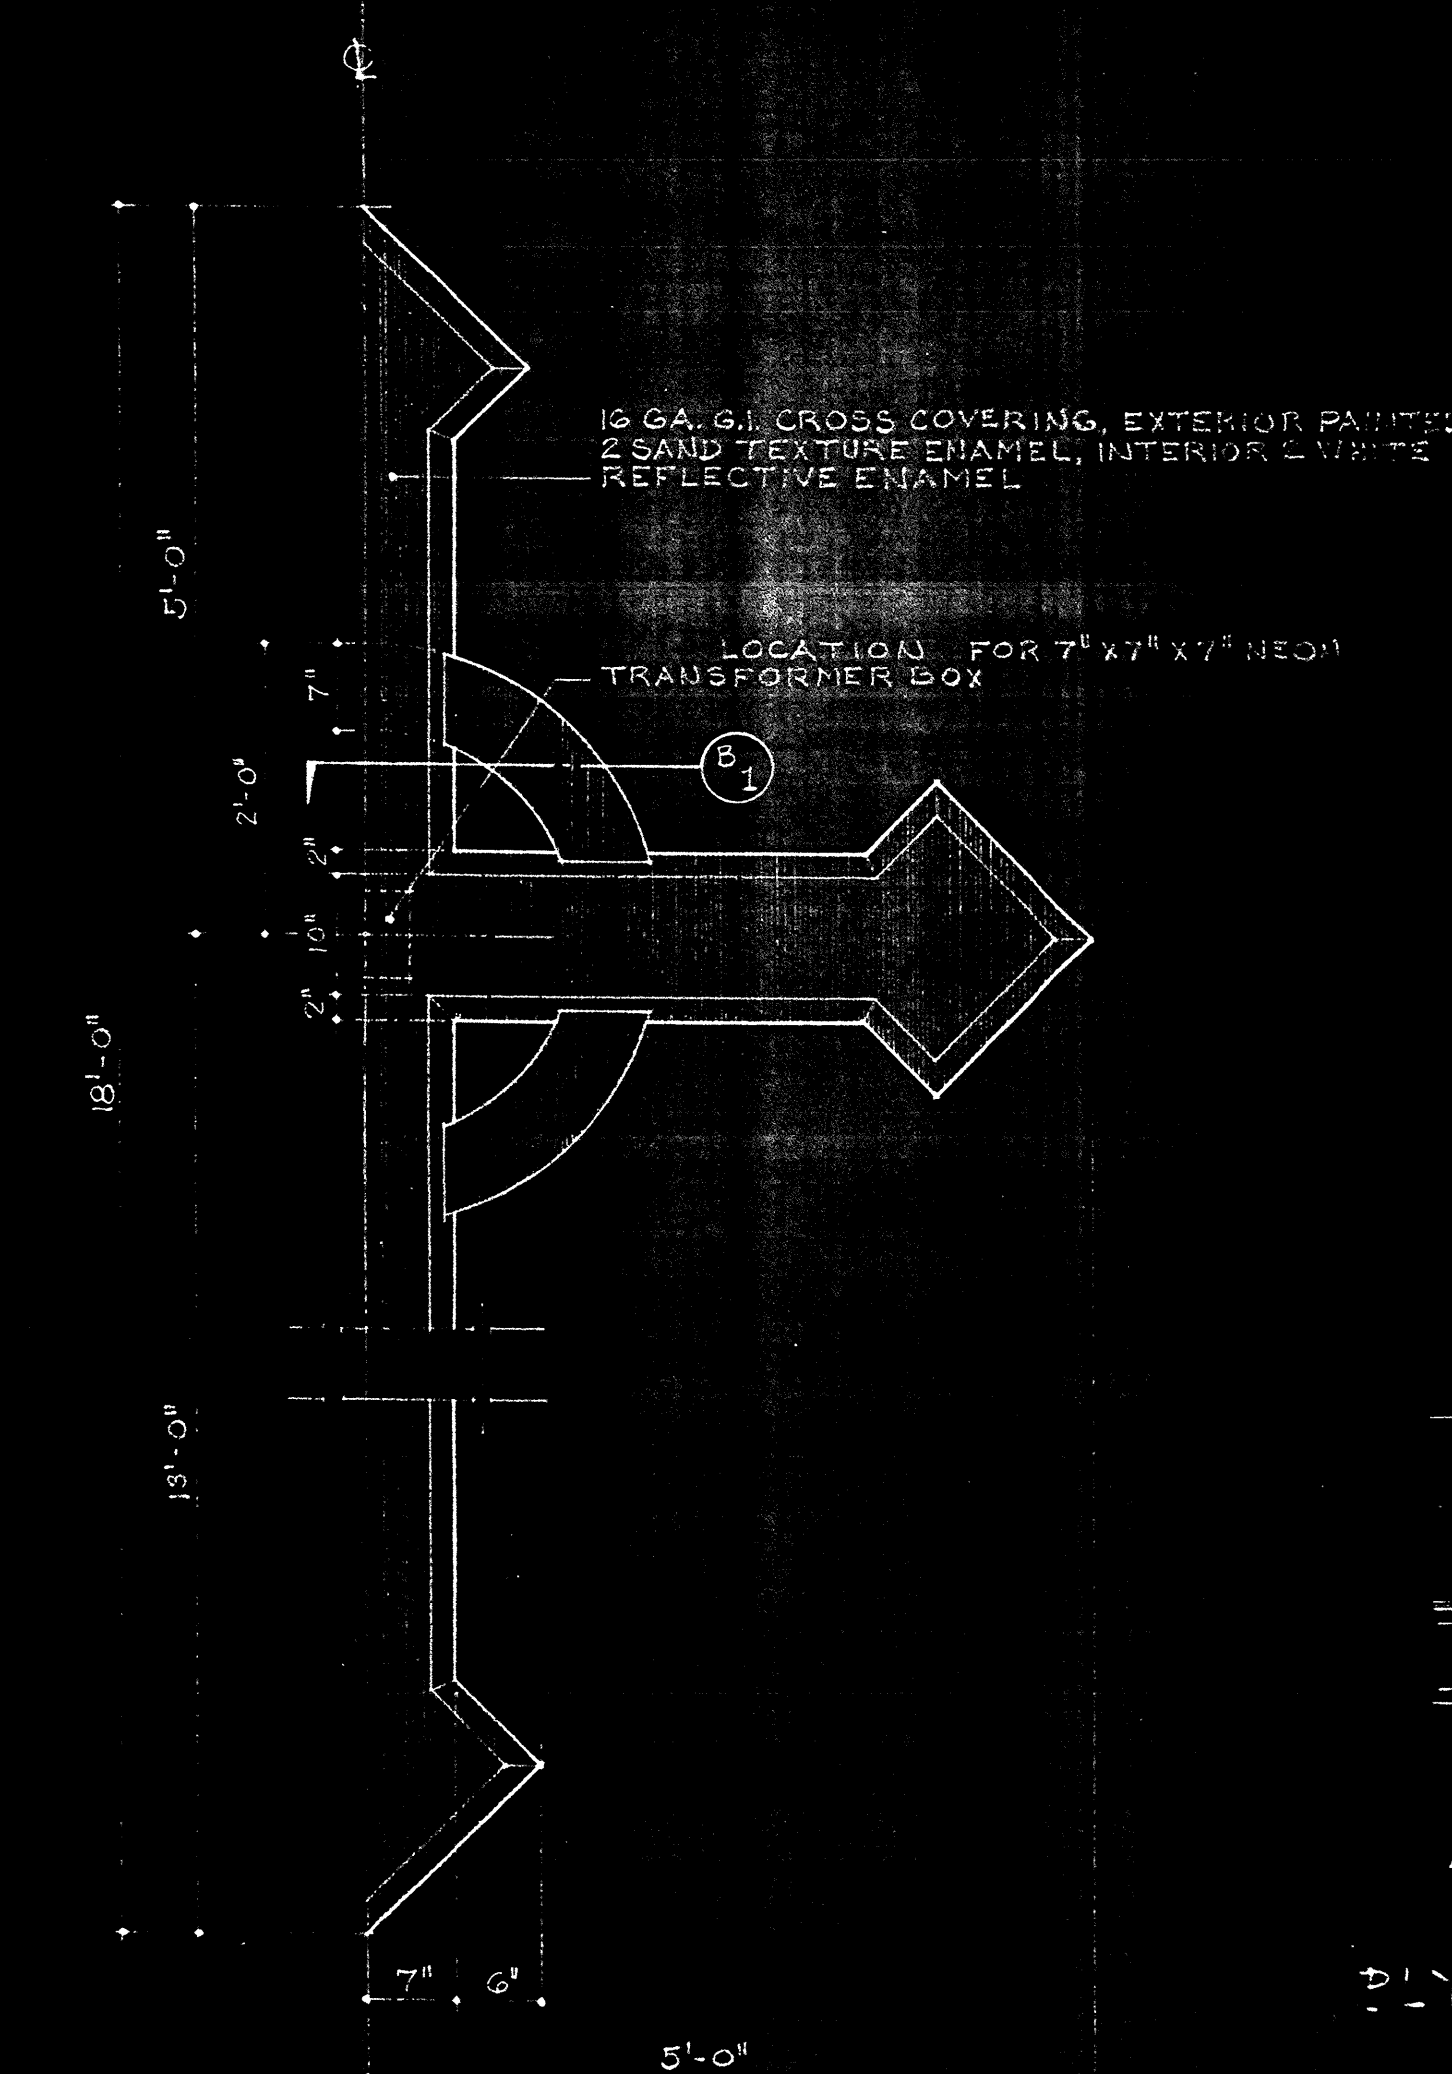SECTION AT EAVE 

HALF ELEVATION, NORTH WALL CROSS (B)

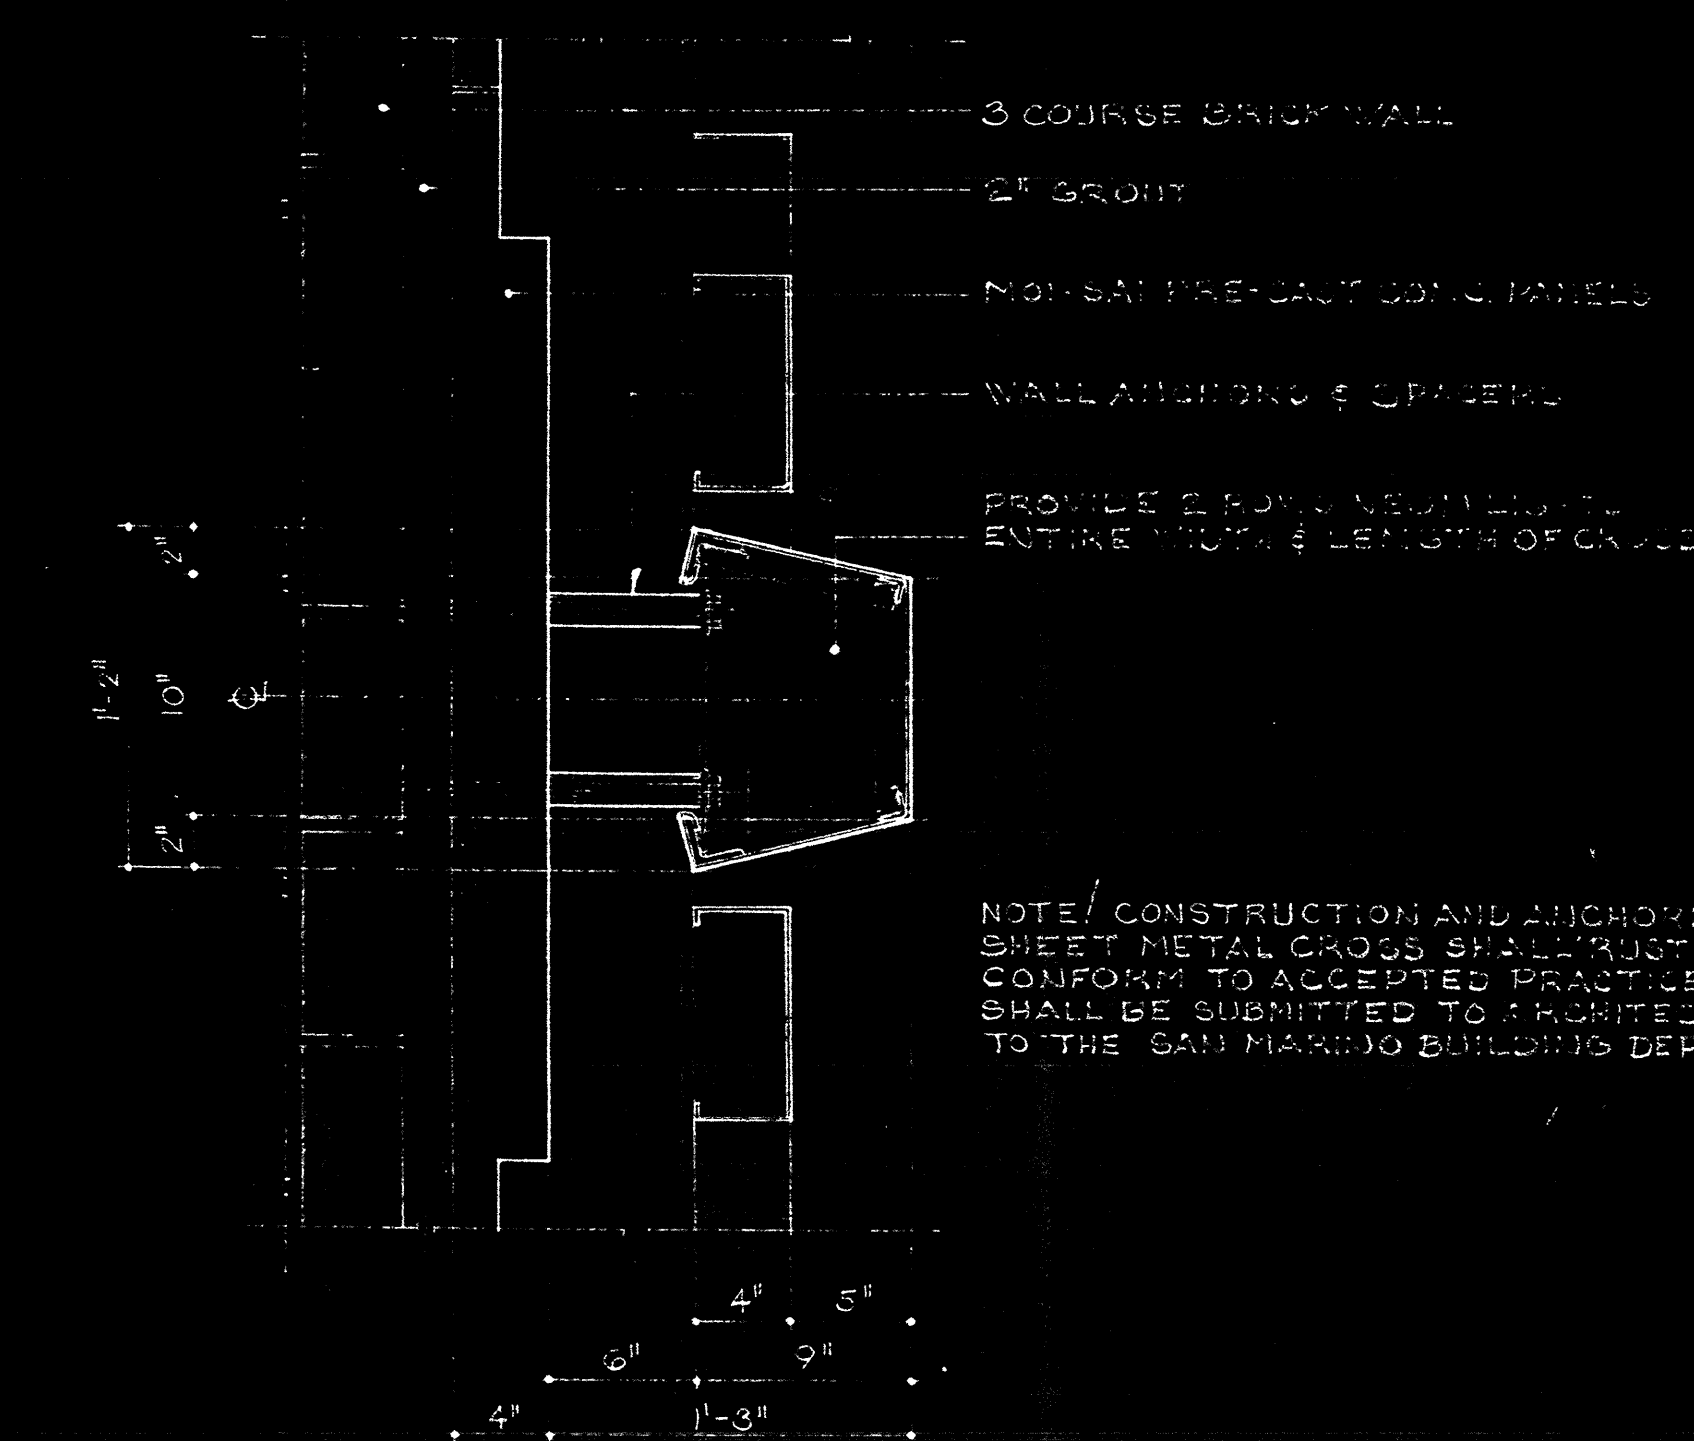

SECTION AT NORTH VALLEY CROSSING

NOTE: CONSTRUCTION AND ANCHORING OF THE SHEET METAL CROSS SHALL PROOF & SHALL CONFORM TO ACCEPTED PRACTICES. SHOP DRAWINGS SHALL BE SUBMITTED TO ARCHITECT AND ACCEPTABLE TO THE SAN MARINO BUILDING DEPARTMENT.

Remarks	Revisions	Engineers	Approvals	AUSTIN FIELD & IRY <i>Architects</i> 2311 WEST THIRD STREET • LOS ANGELES 5, CALIFORNIA • DUNKIRK 8-1326	DETAILS OF NORTH WALL ST. EDMUNDS EPISCOPAL CHURCH SAN MARINO CALIF.	DATE DRAWN BY COMM. SHEET NUMBER 8
			DRAWN FRY SR ARCHITECT—LICENSE #	CHECK'D JH1206		