




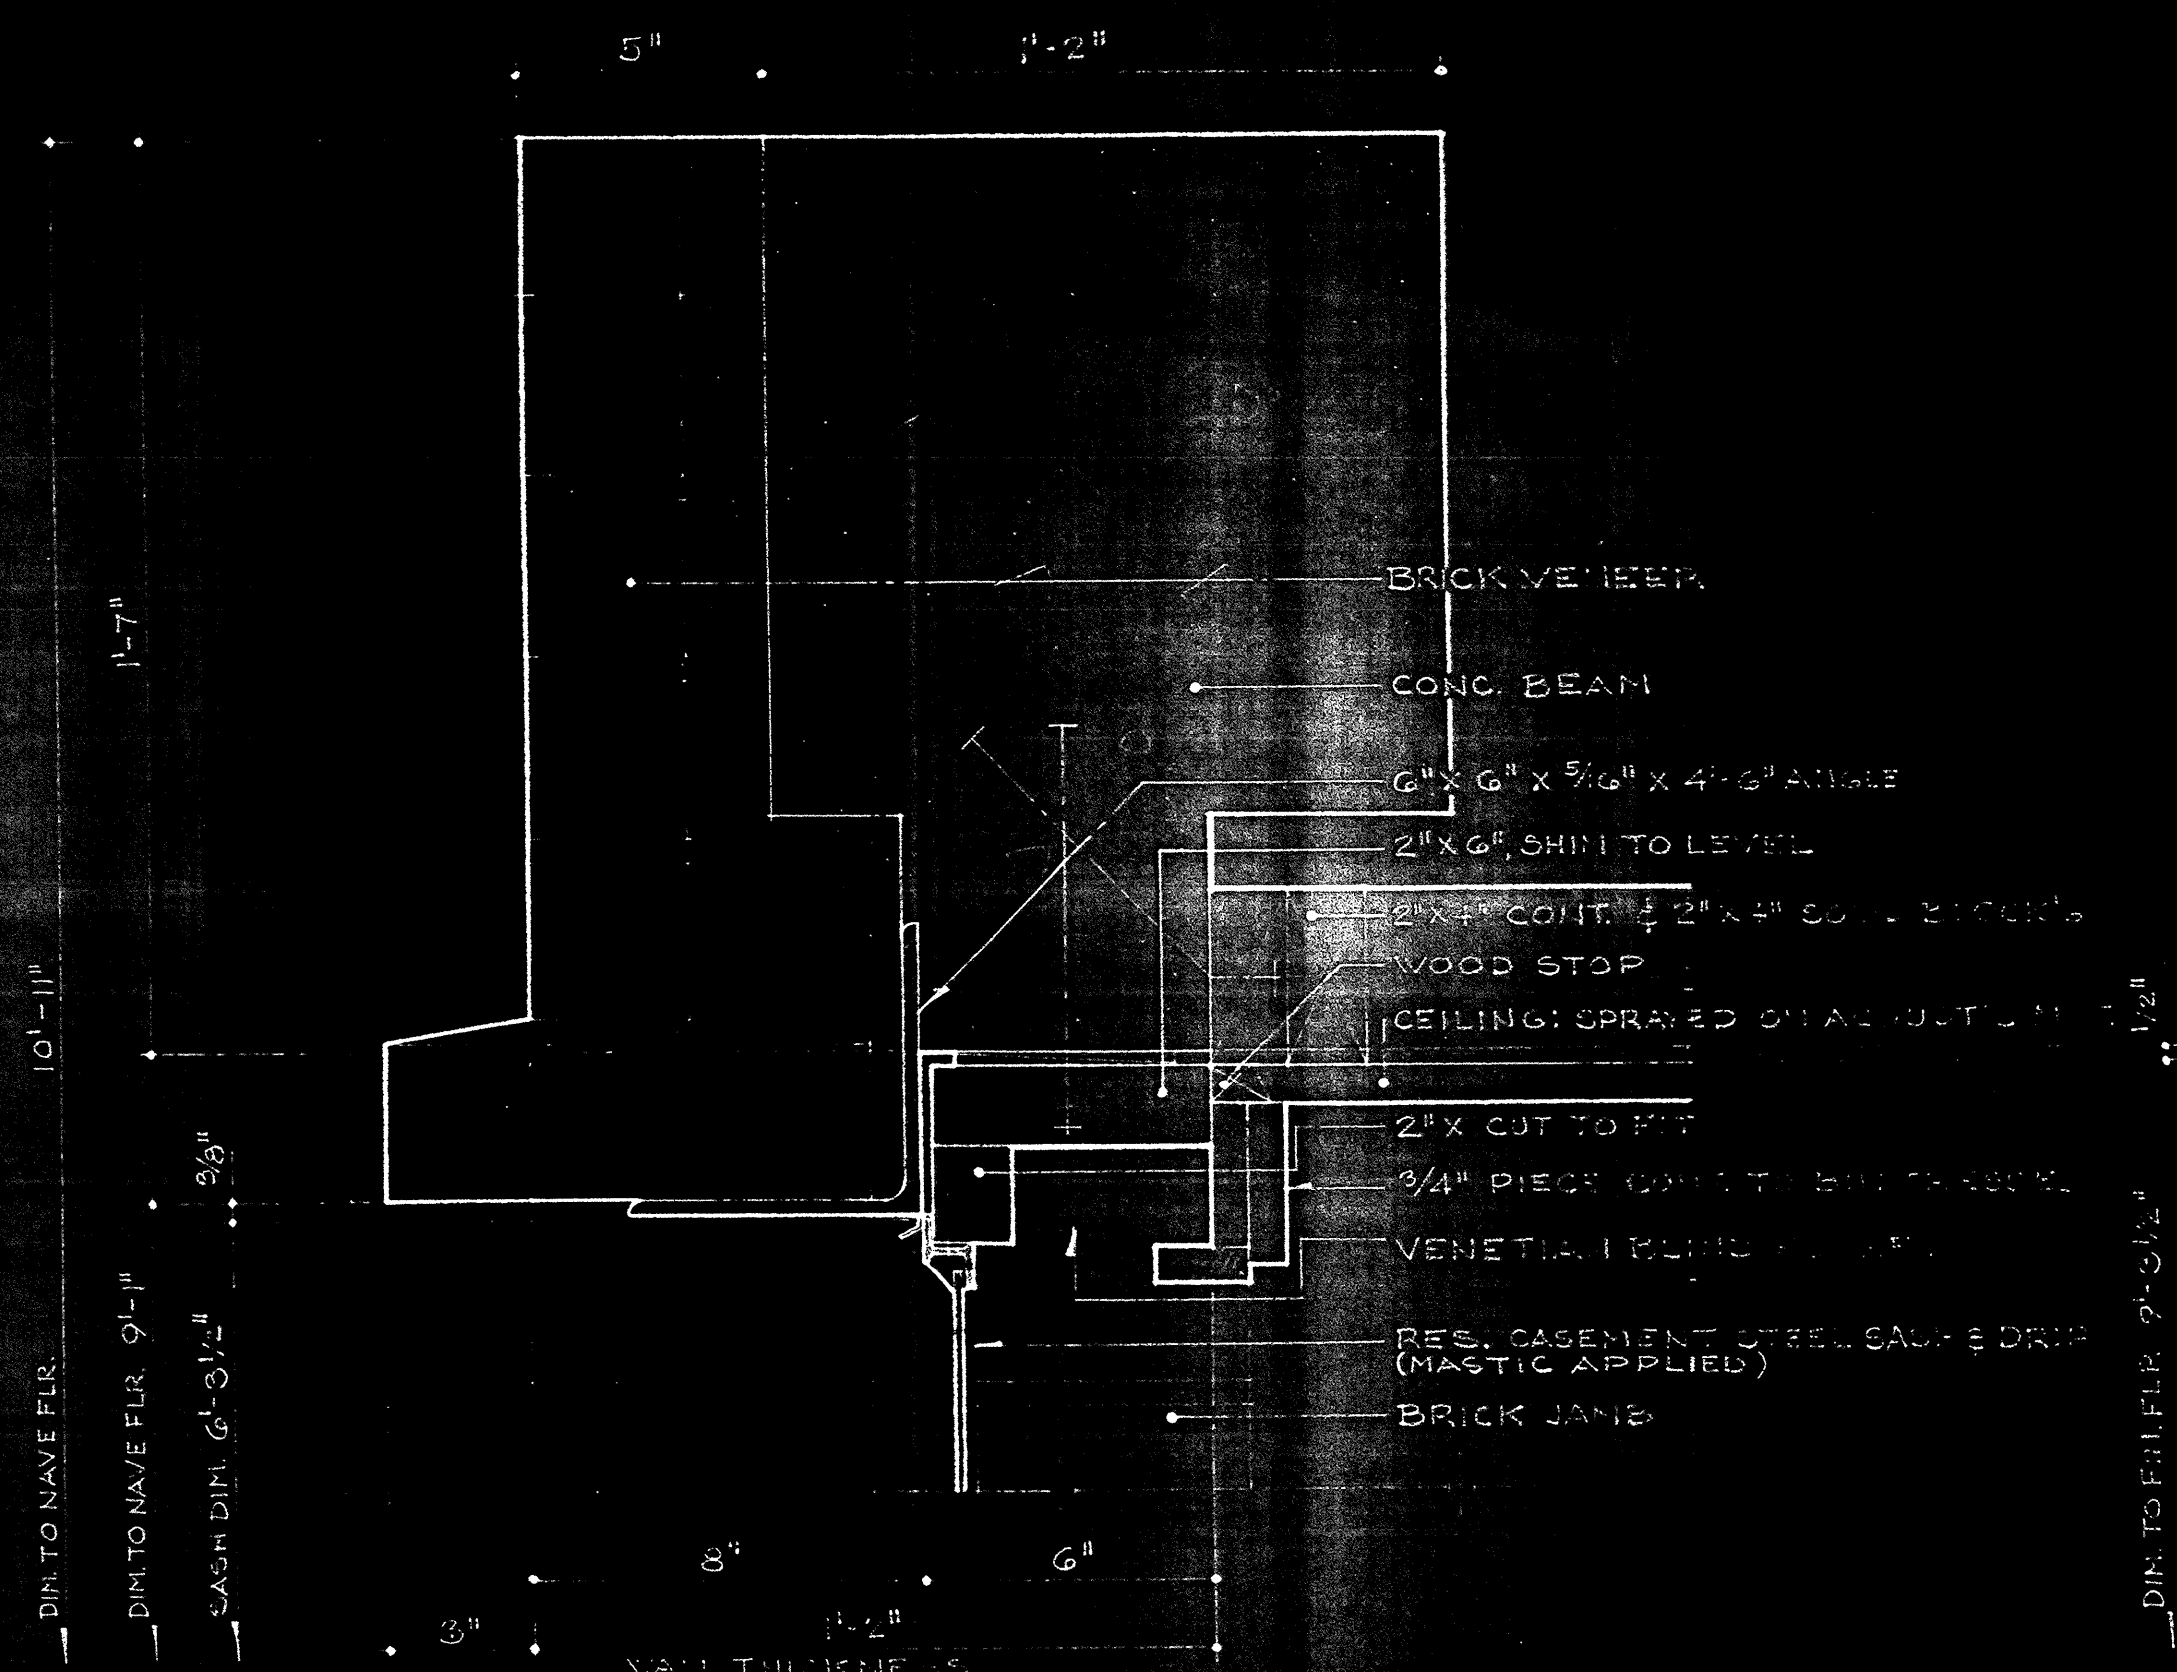

HEAD
SCALE - 3/8" = 1'-0"

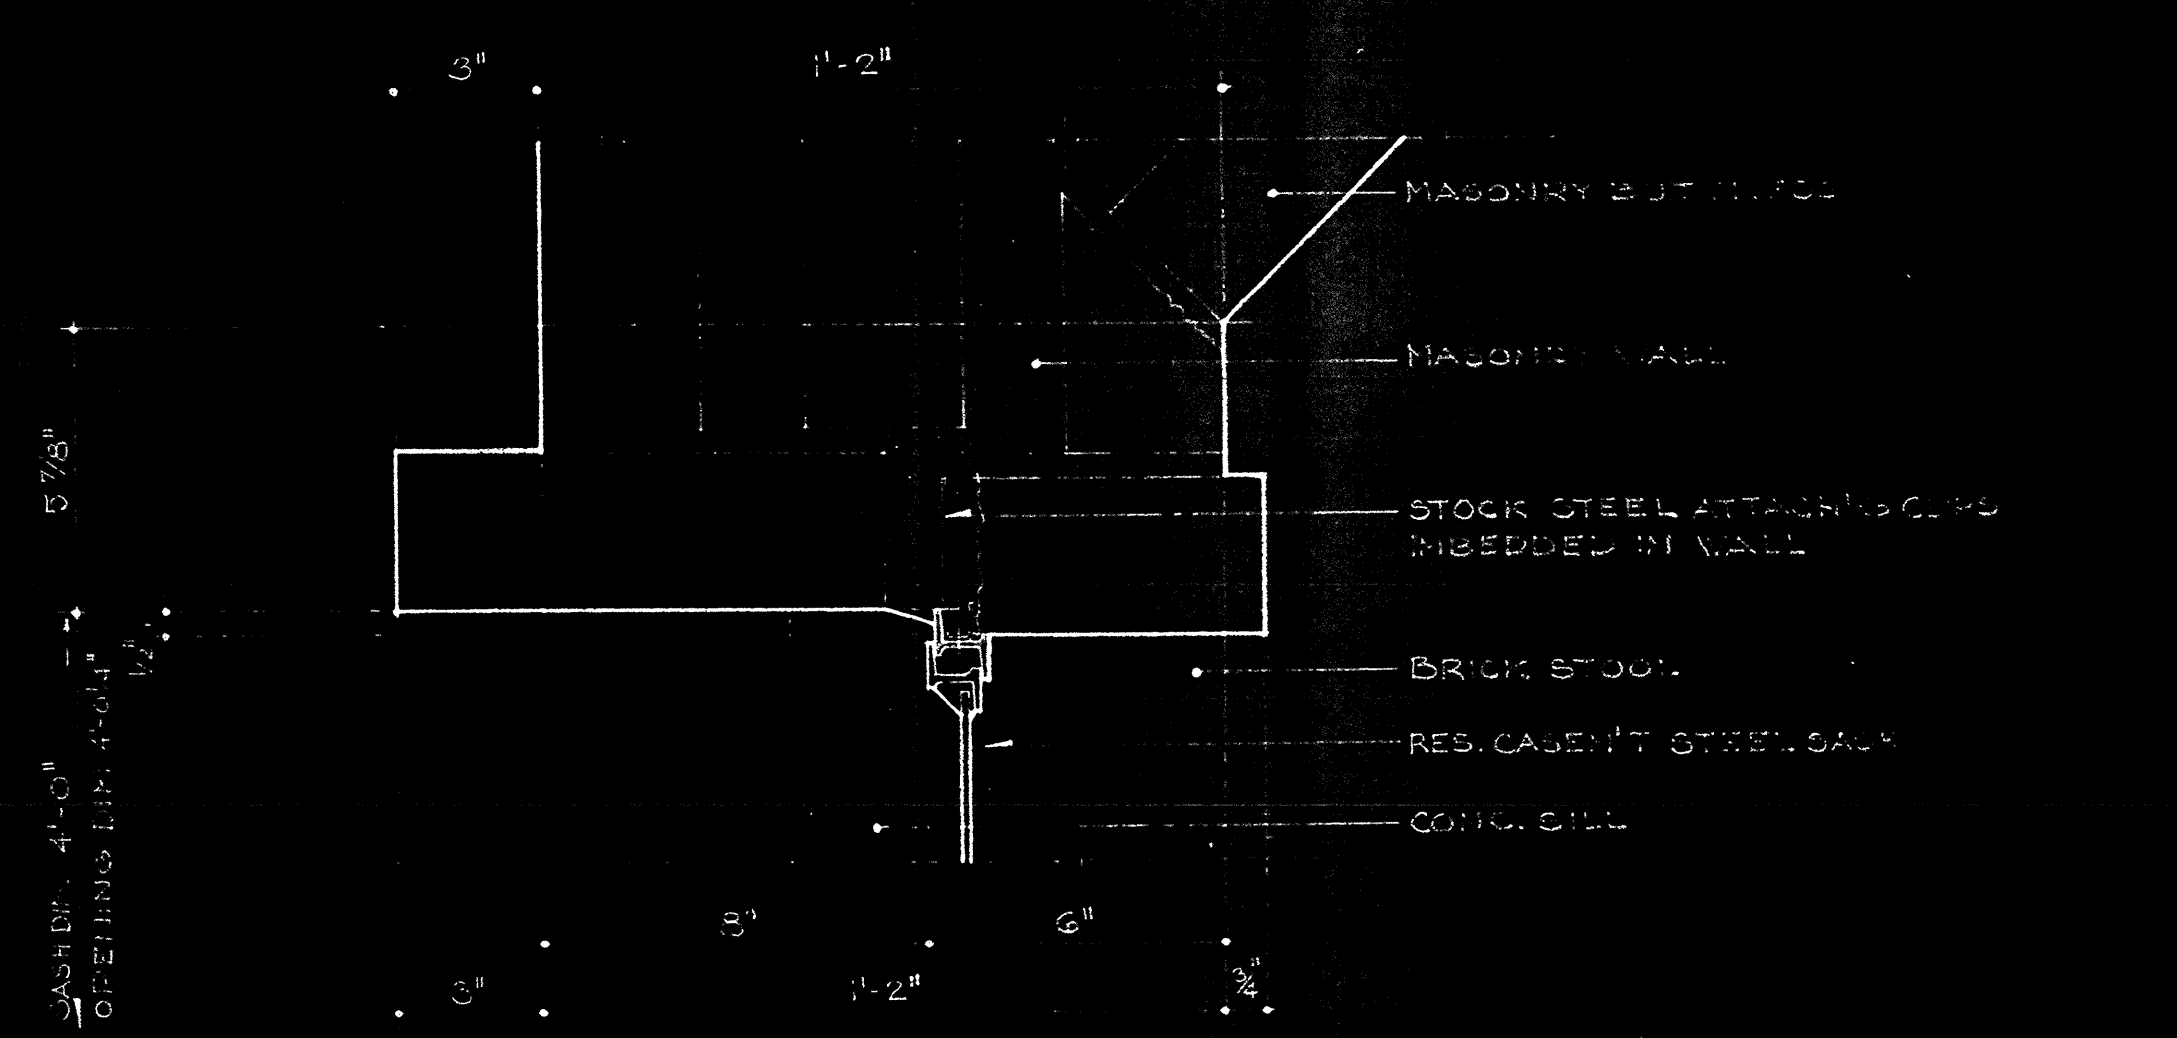


JAMB
SCALE - 3/8" = 1'-0"

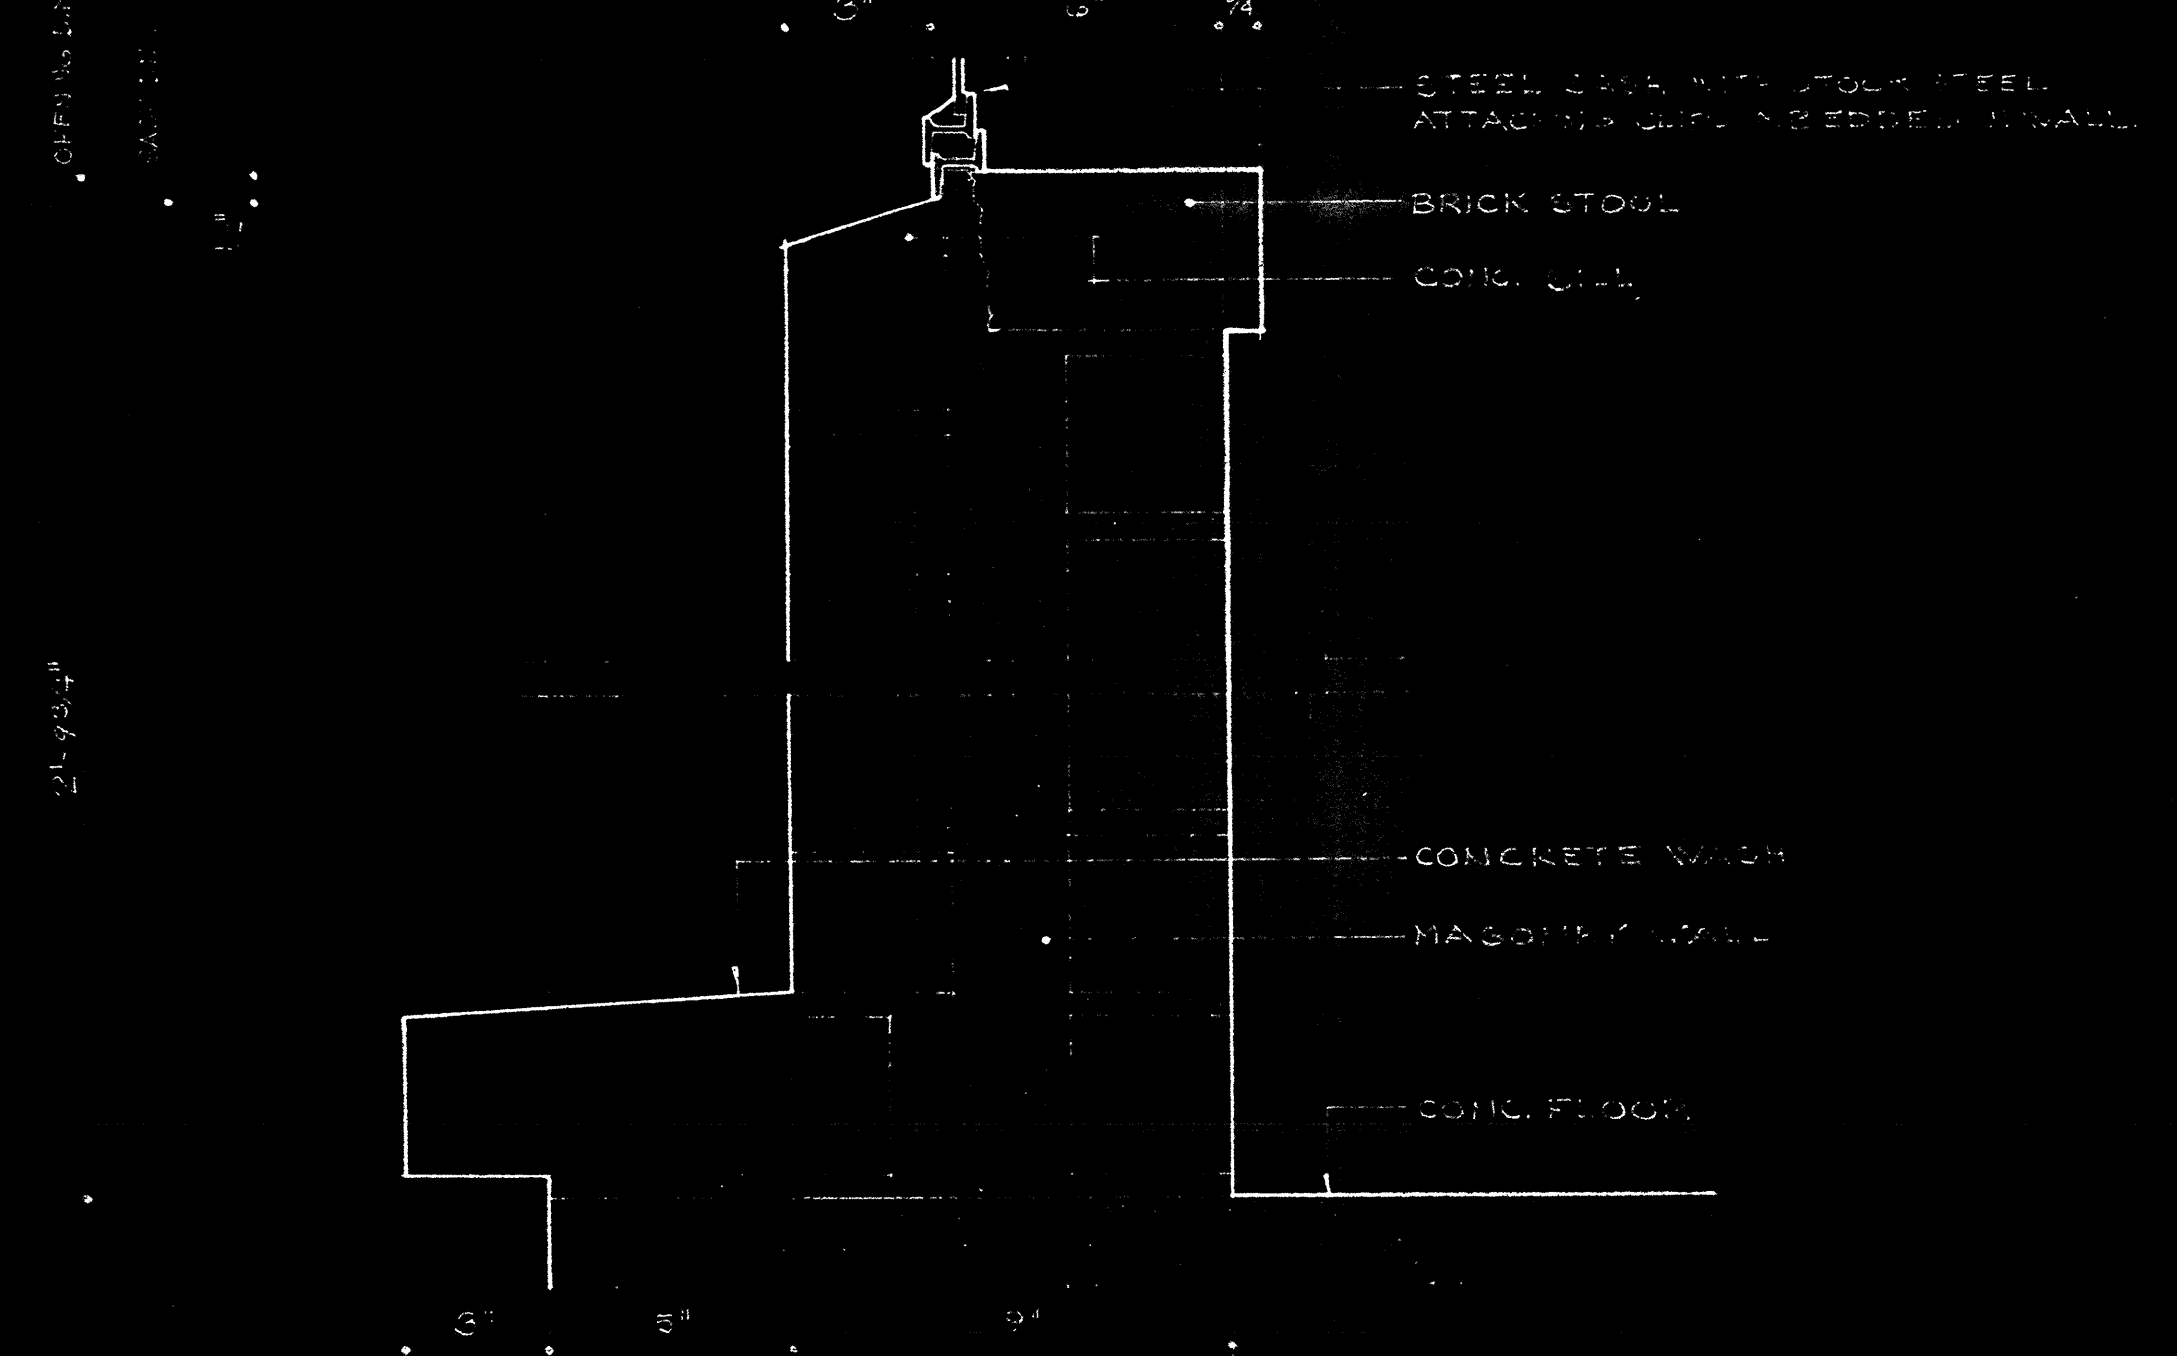


SILL
SCALE - 3/8" = 1'-0"

Window Details (A)

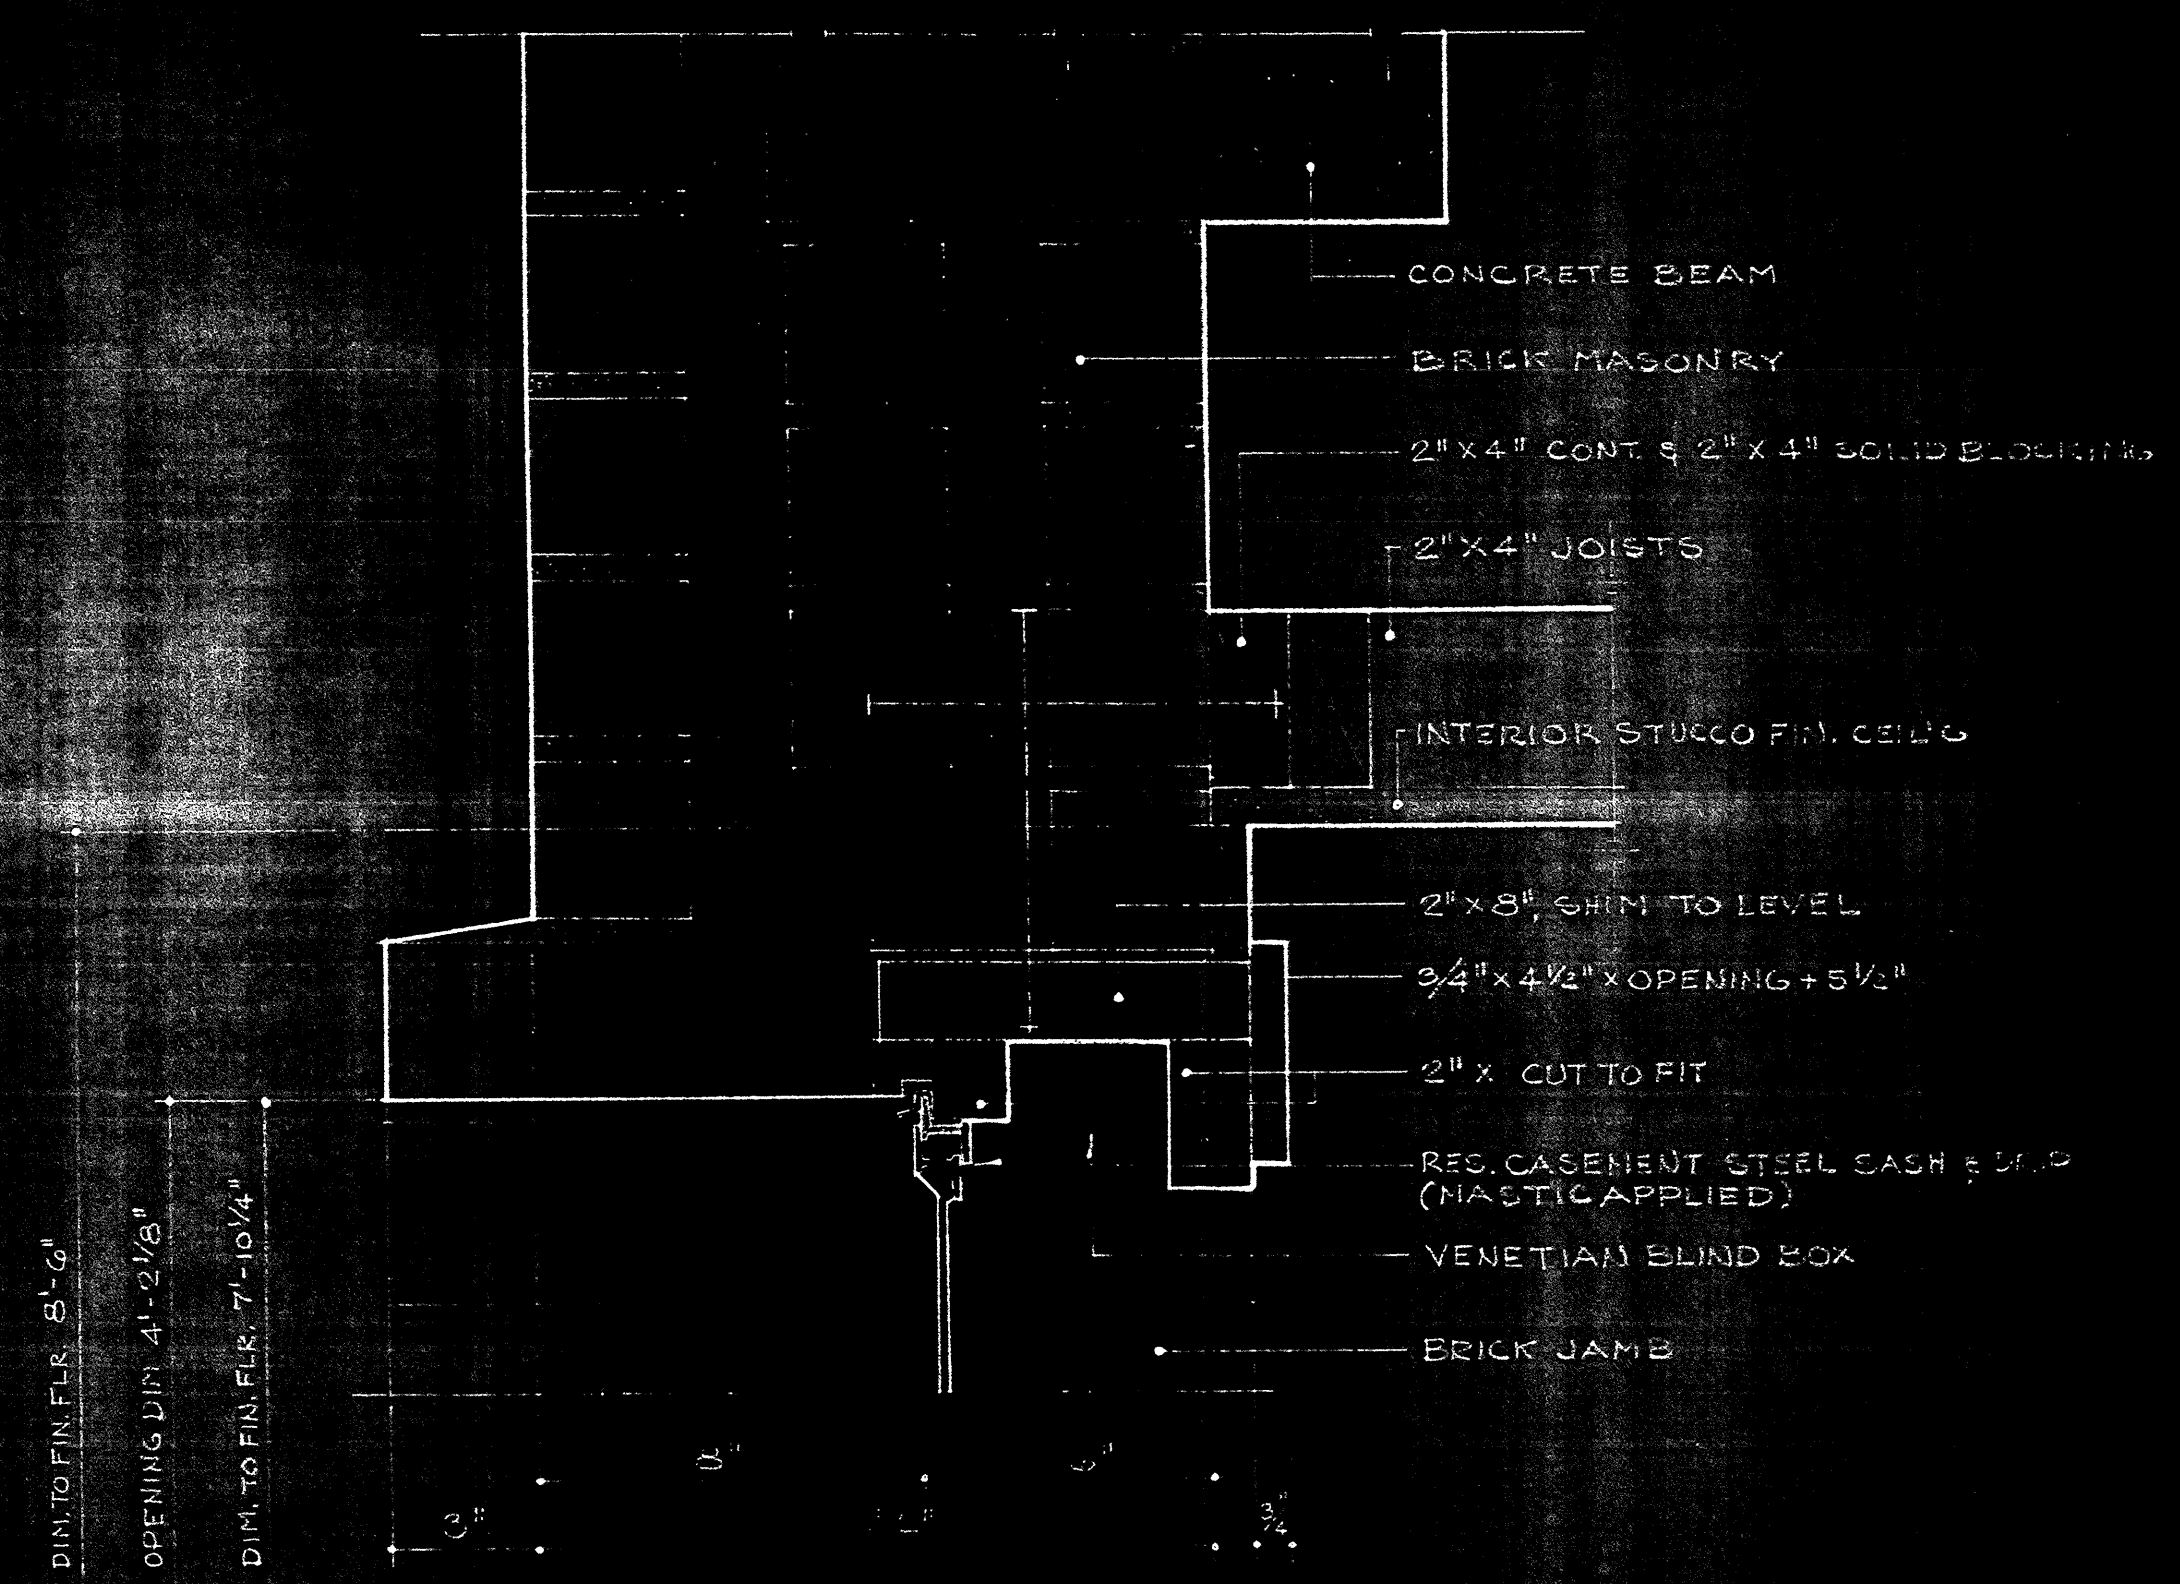


HEAD
SCALE - 3/8" = 1'-0"

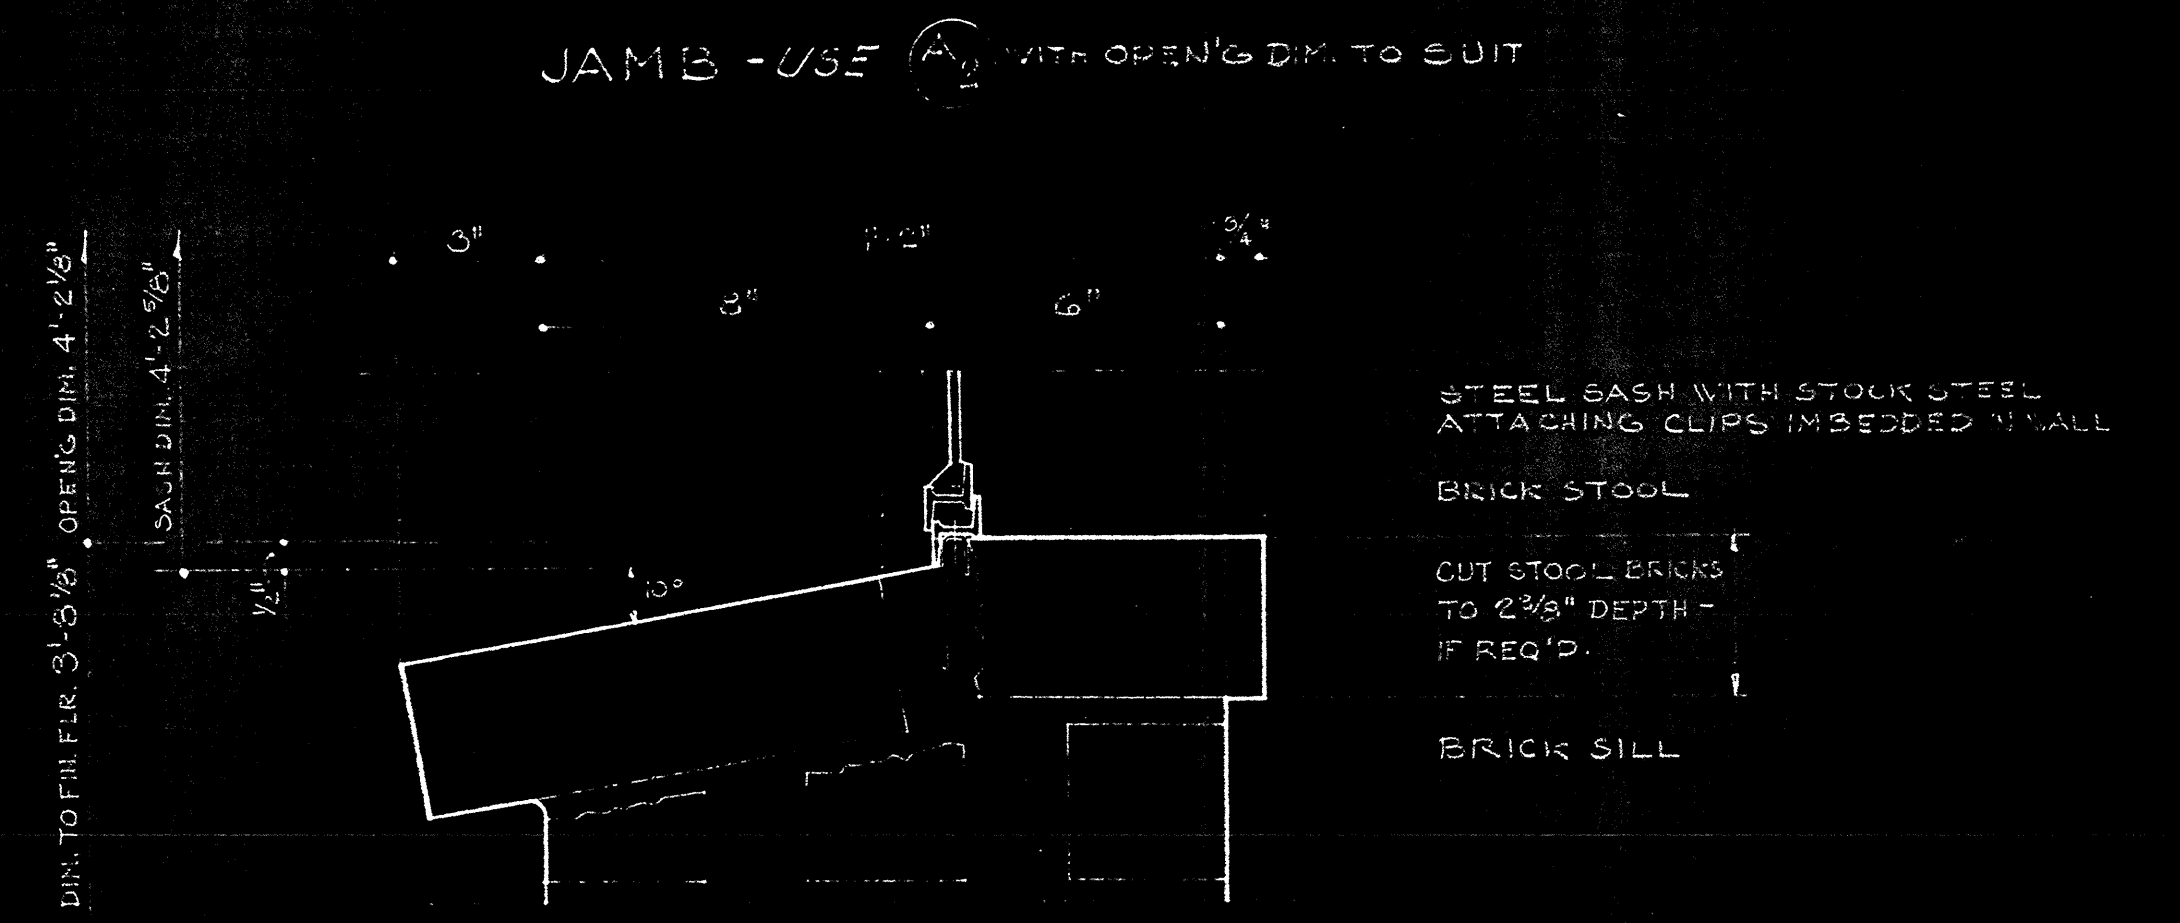

SILL
SCALE - 3/8" = 1'-0"

Window Details (B)

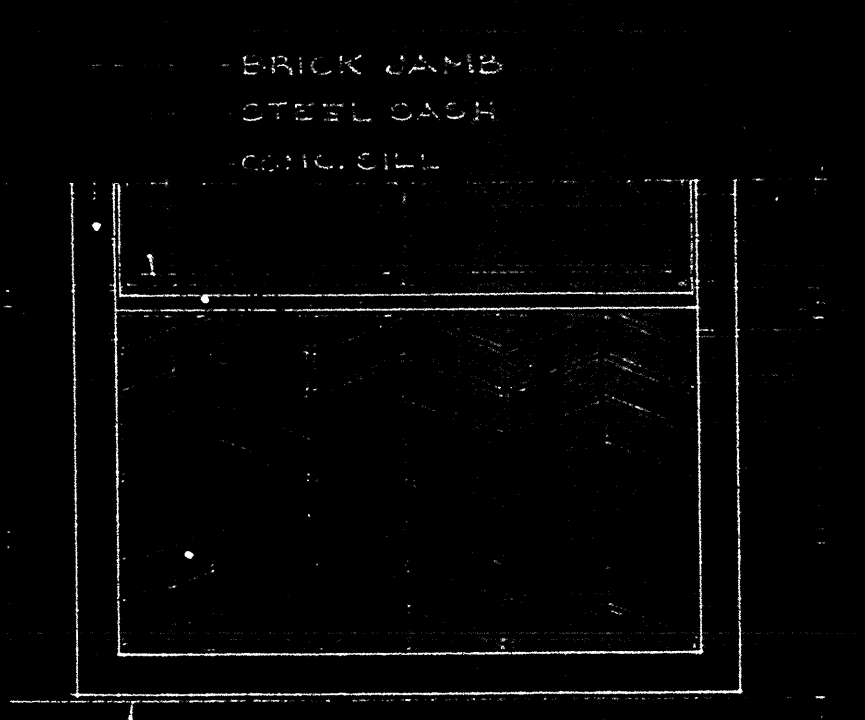

SILL ELEVATION (A)
SCALE - 3/8" = 1'-0"