
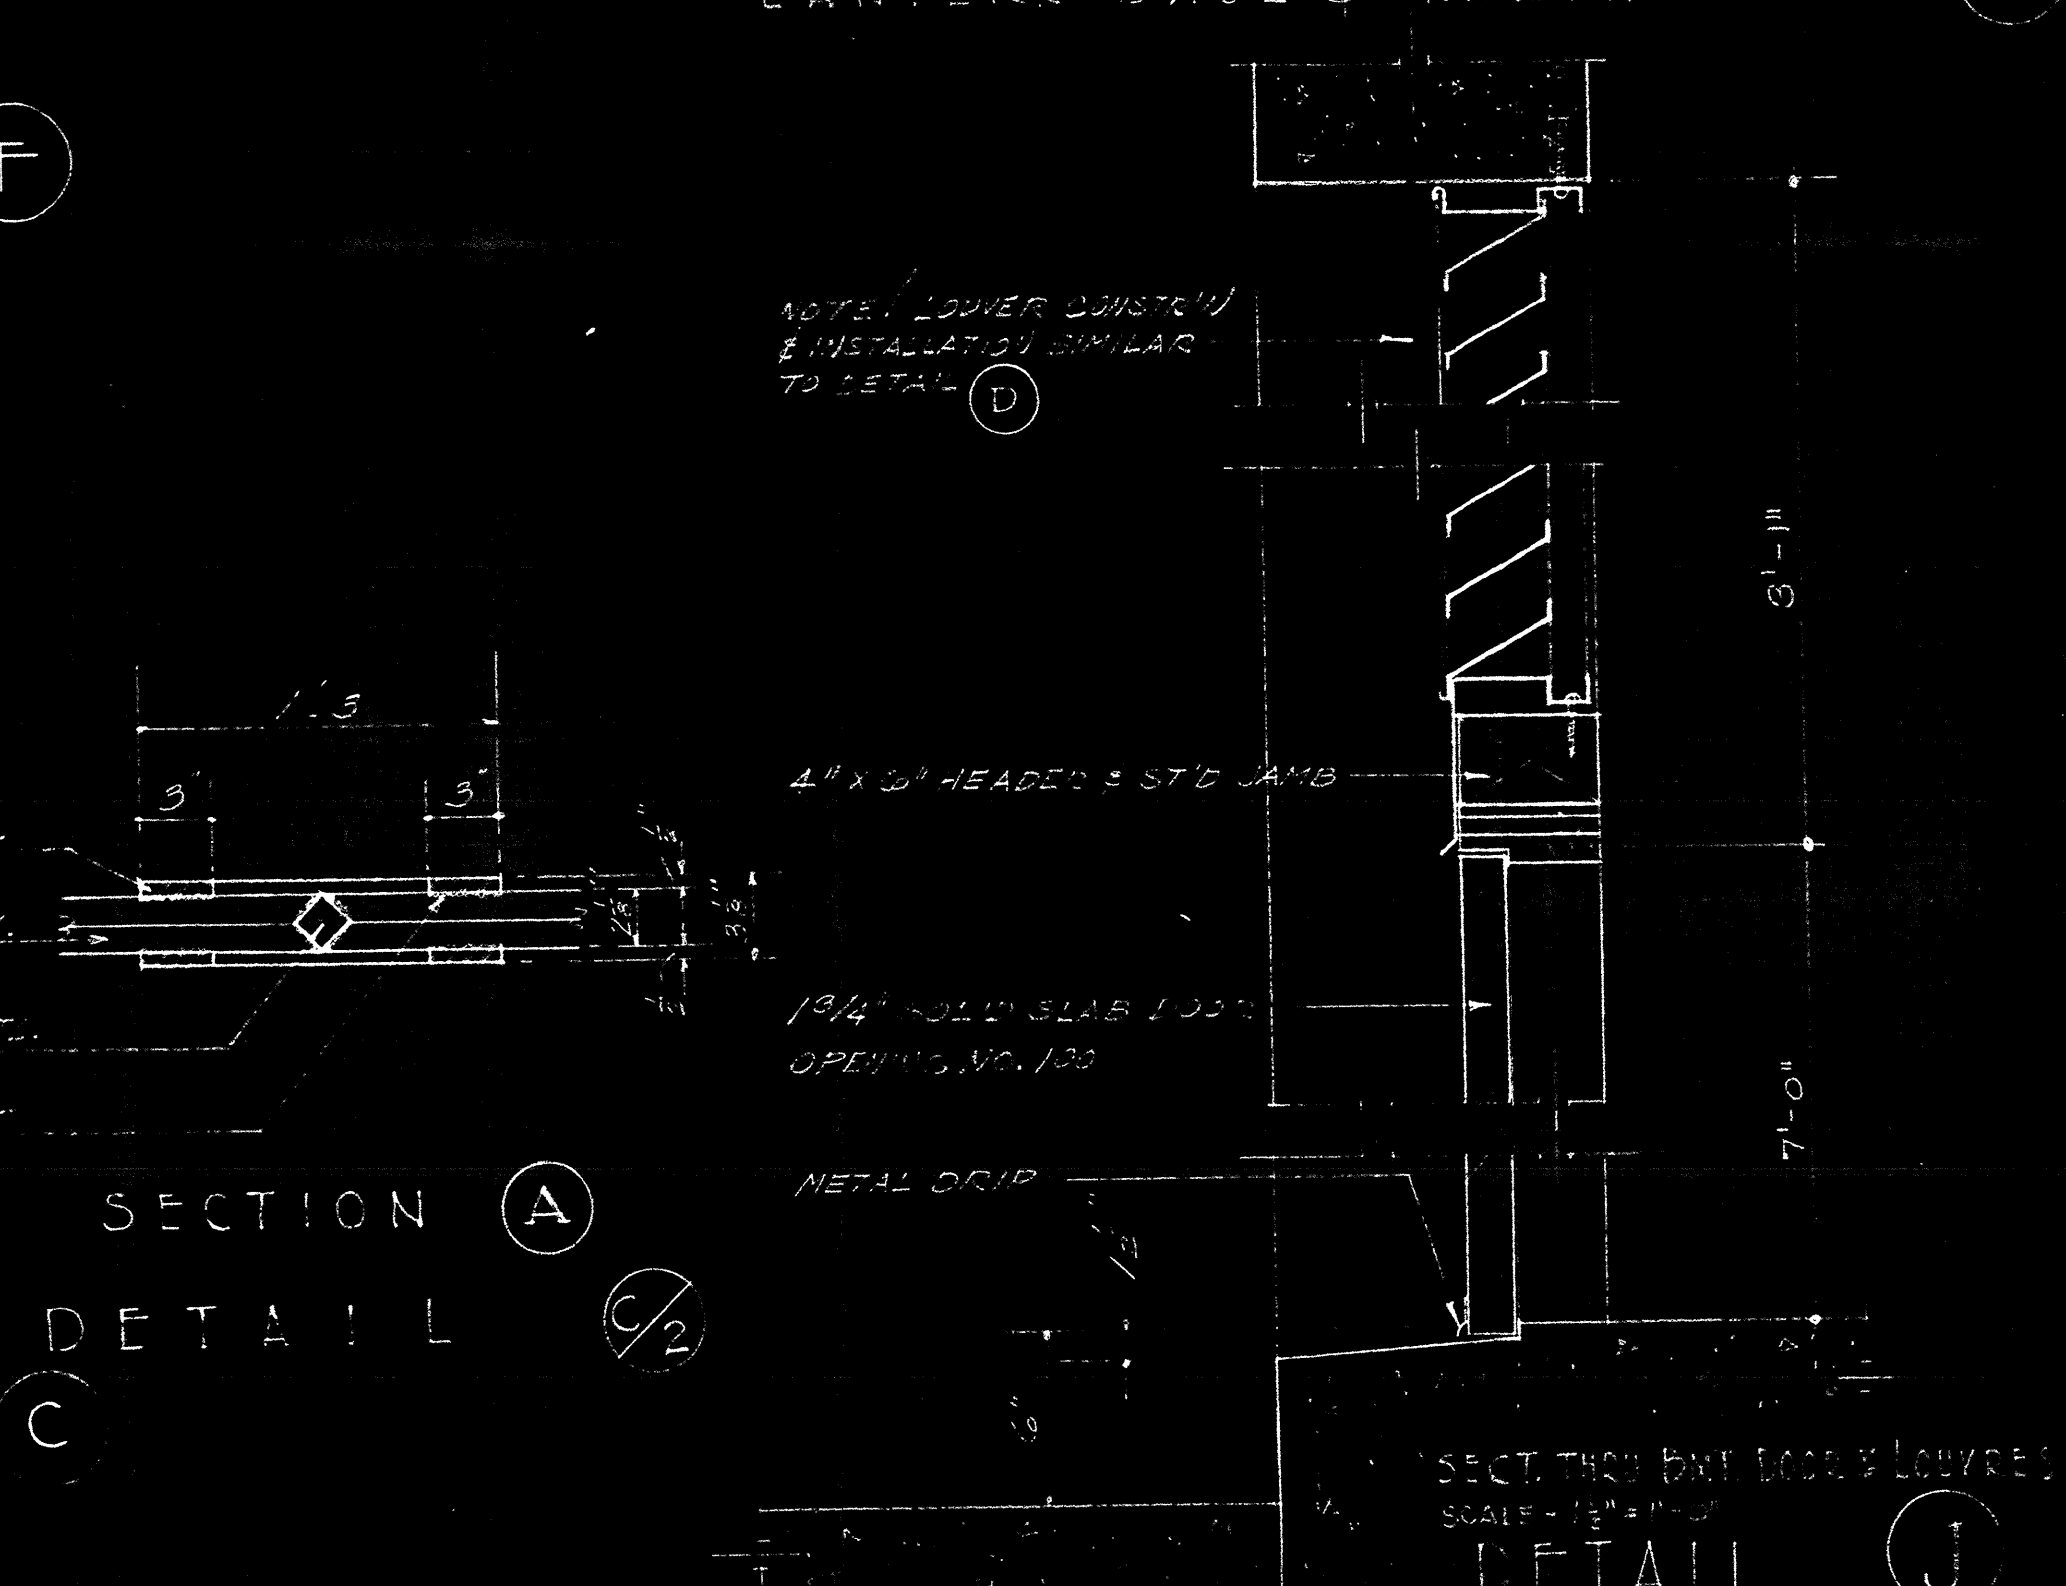
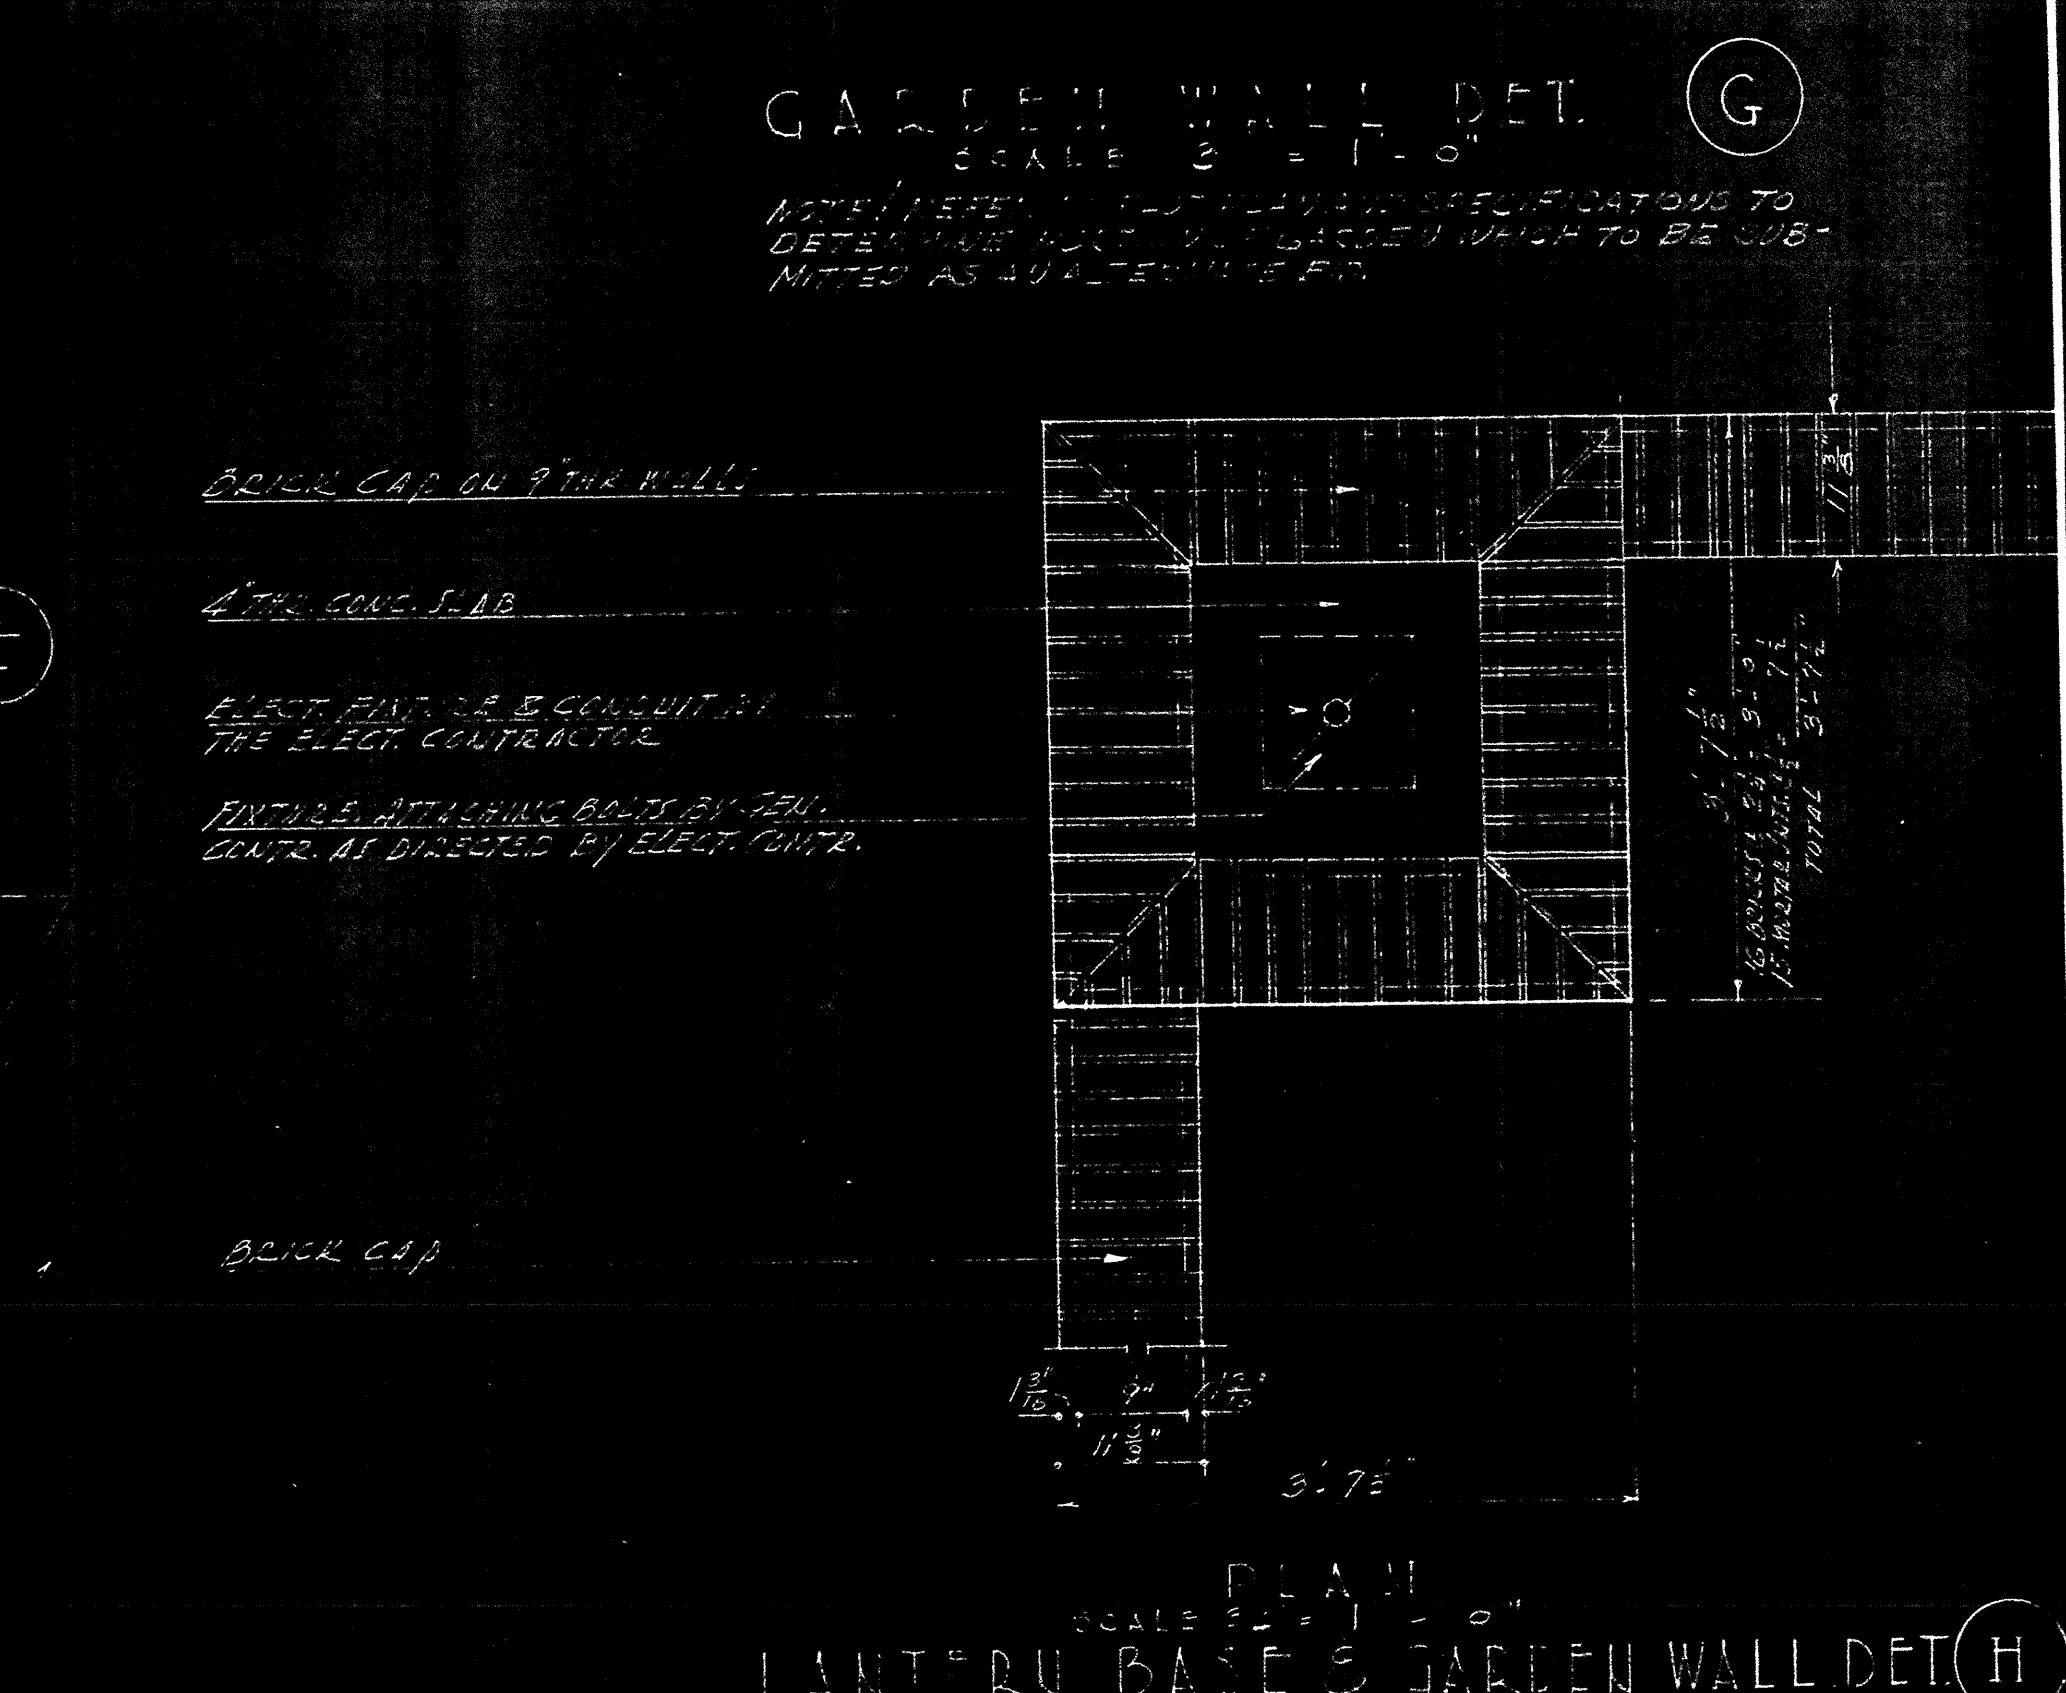
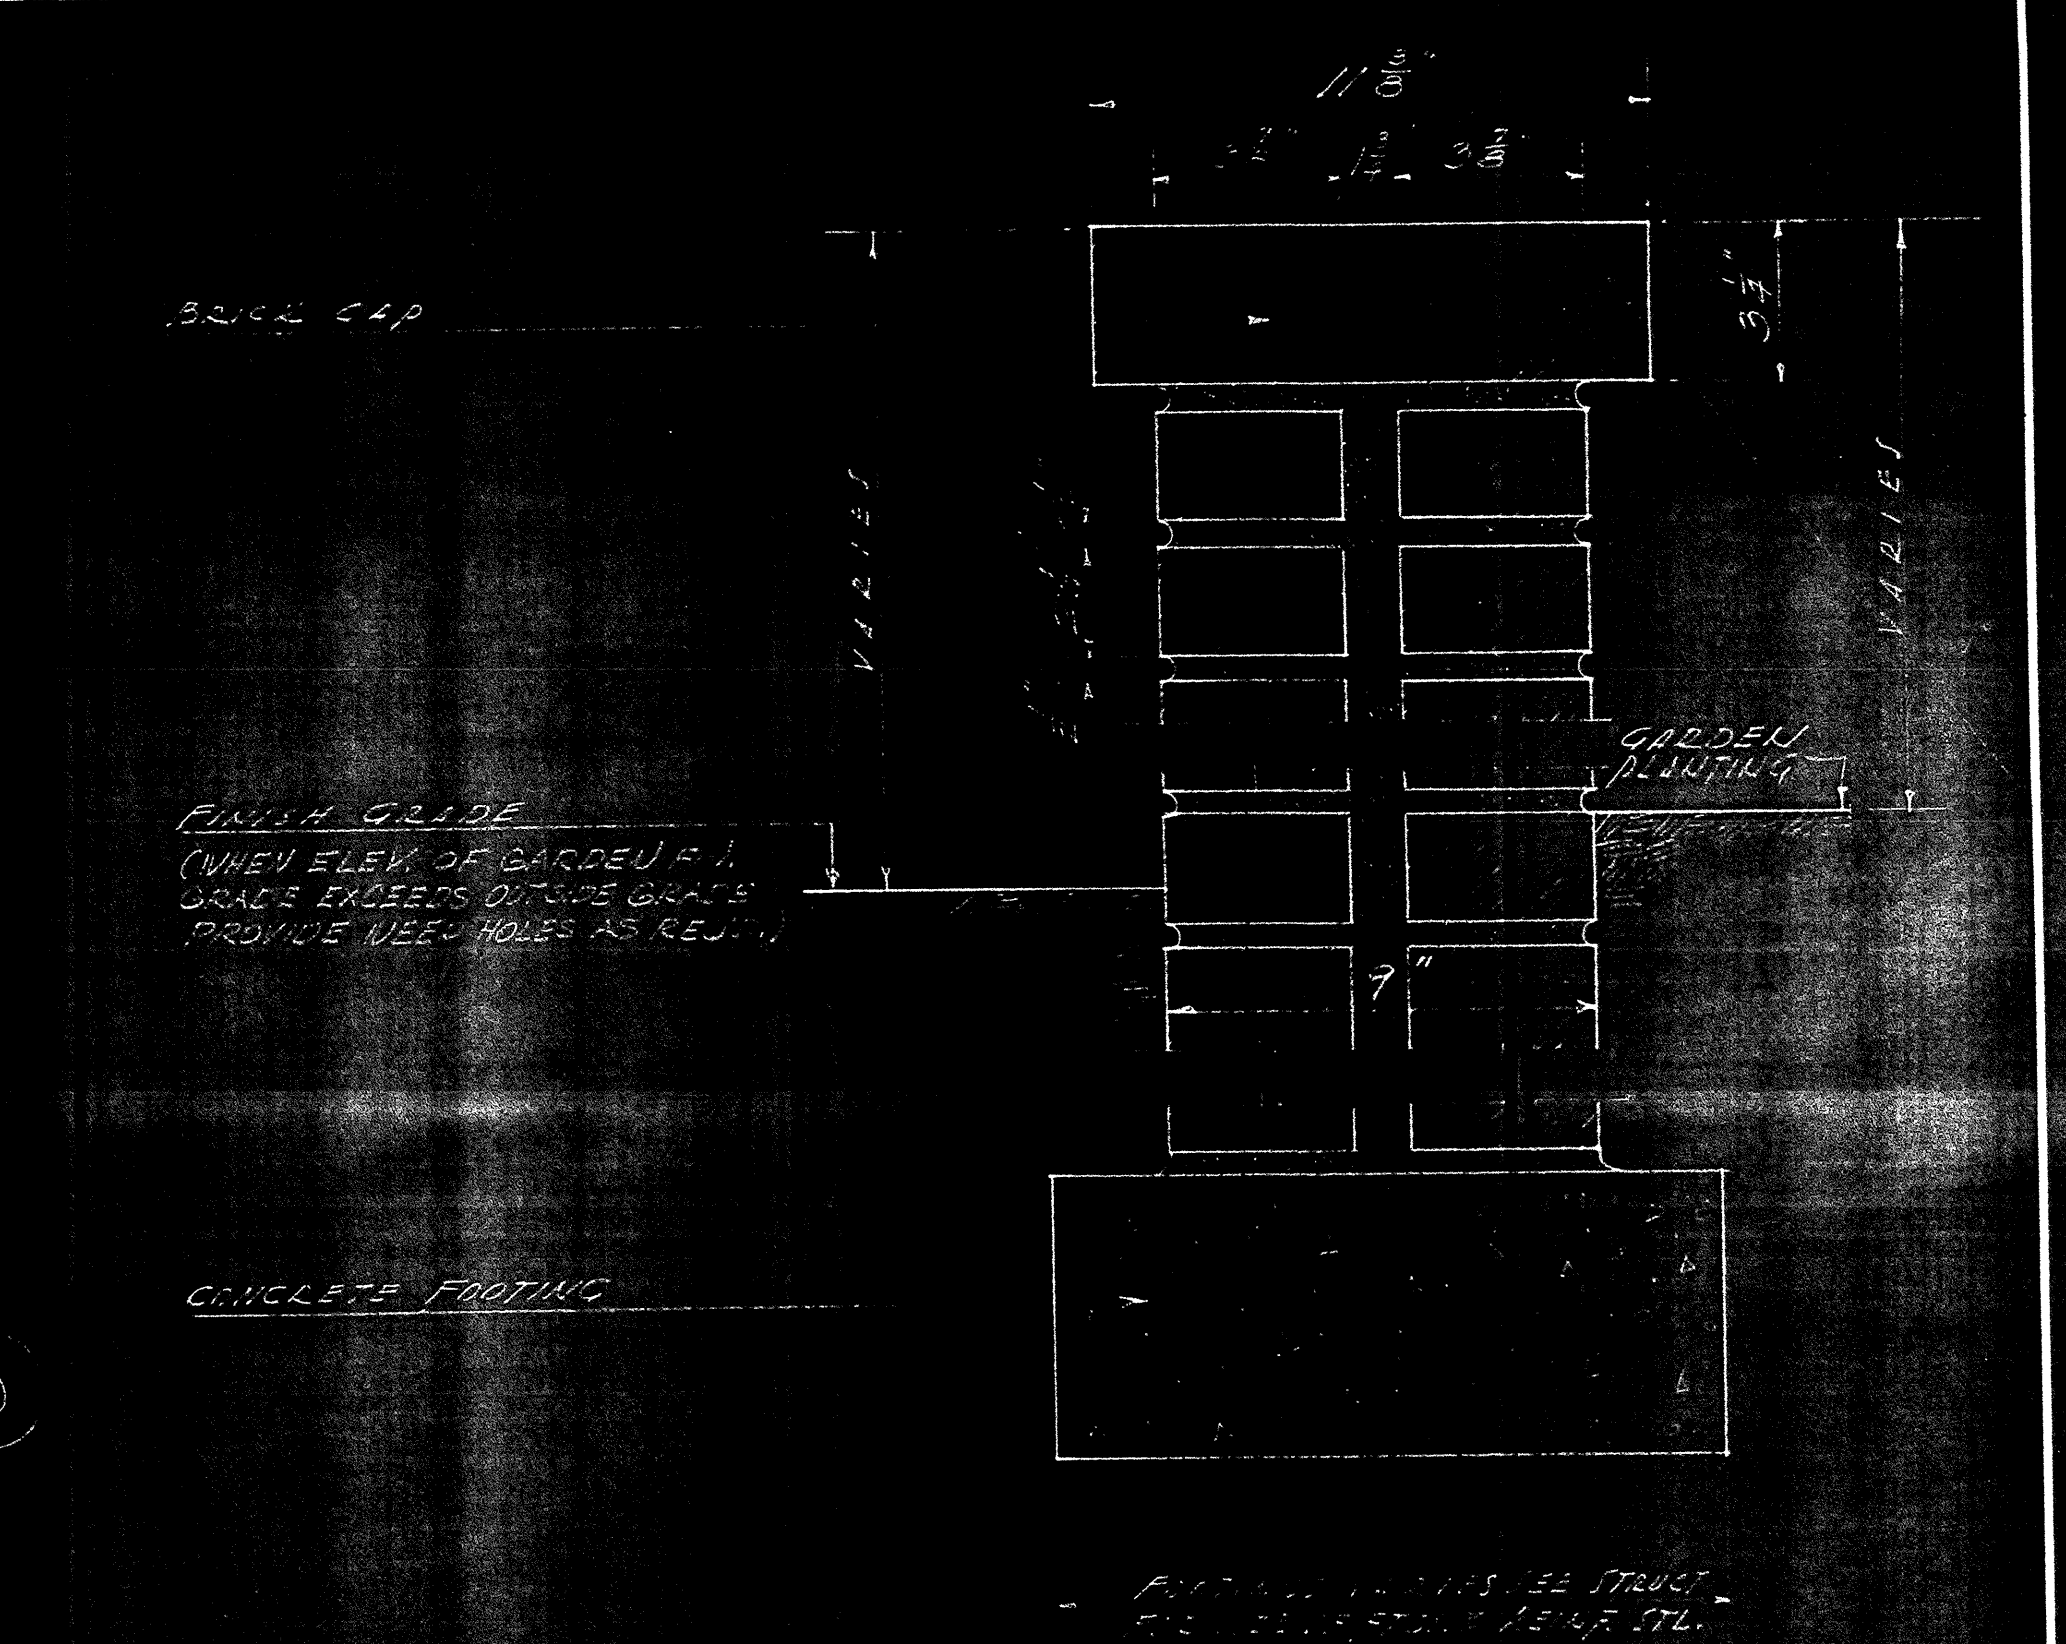
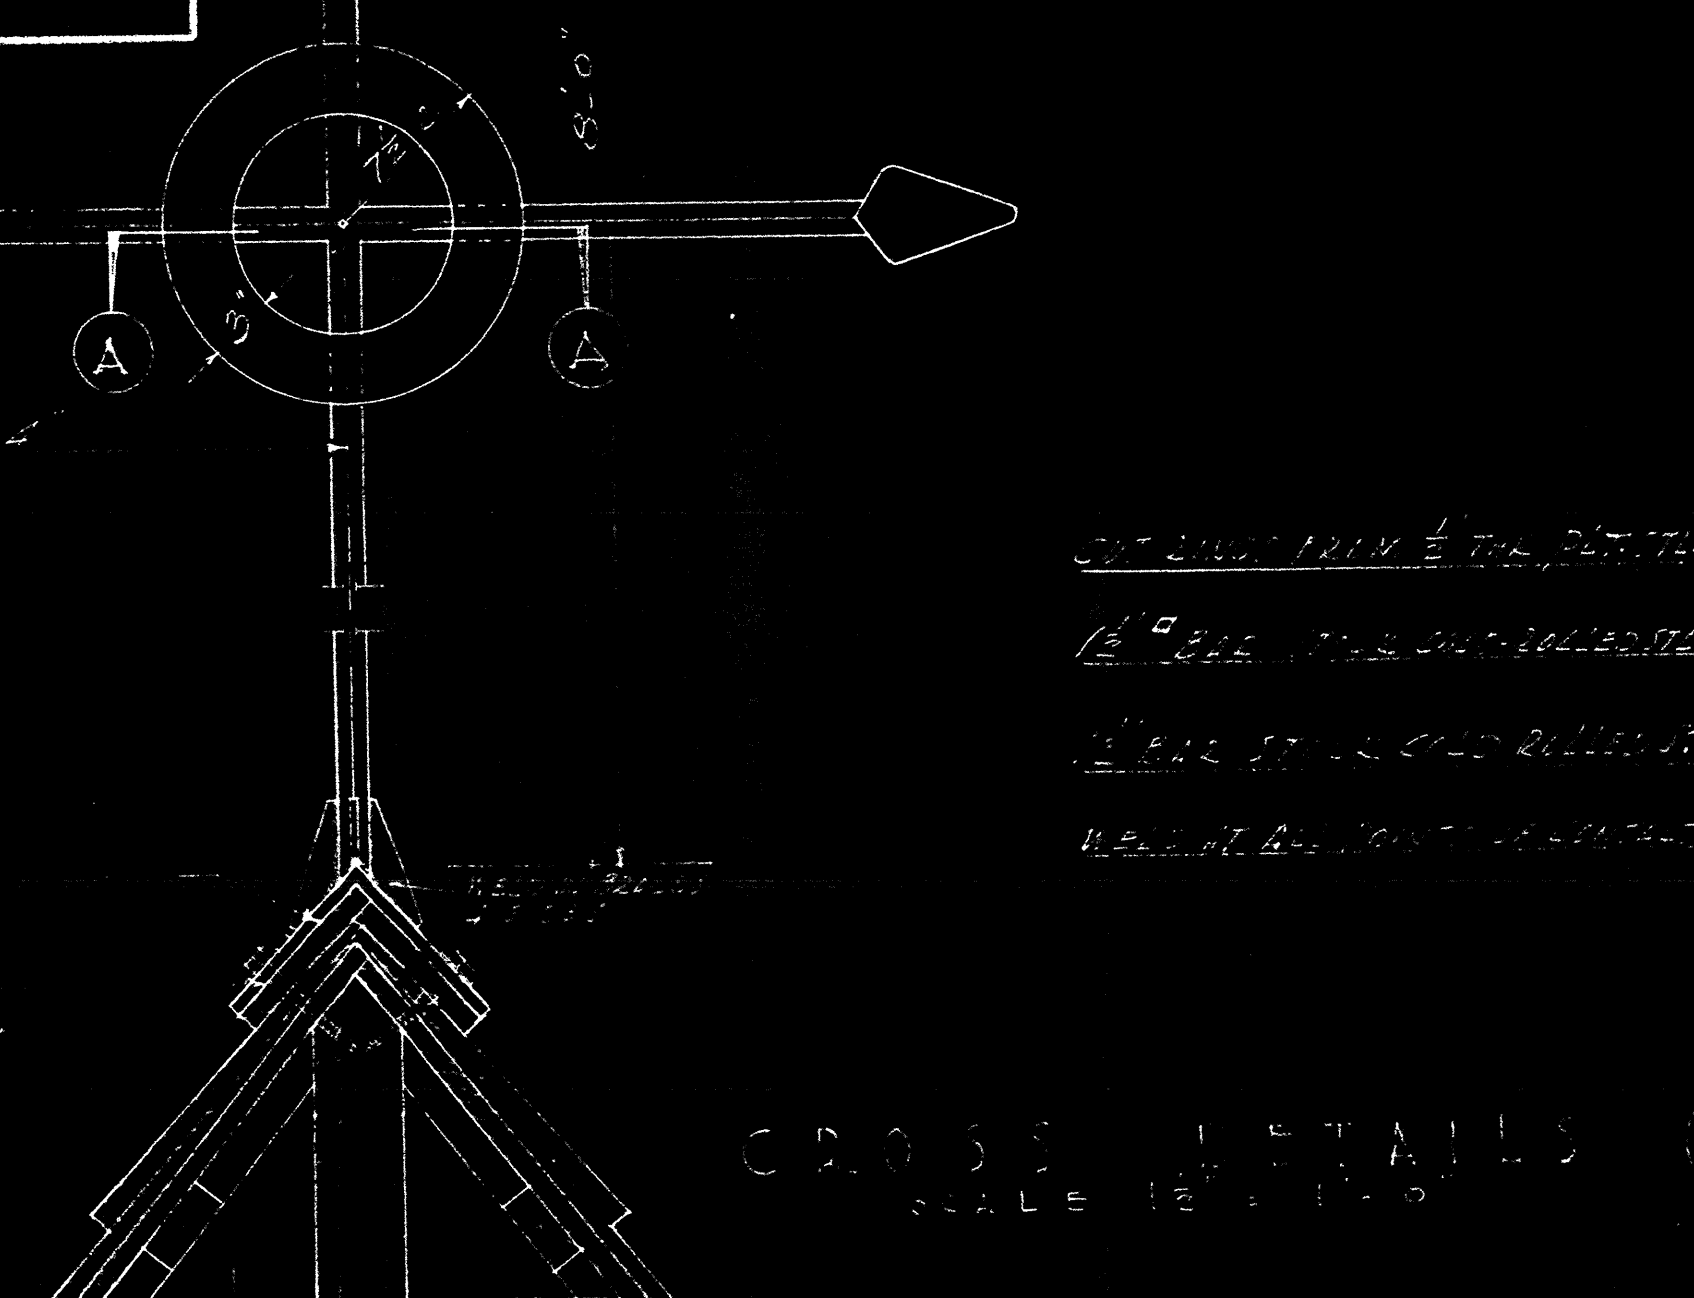
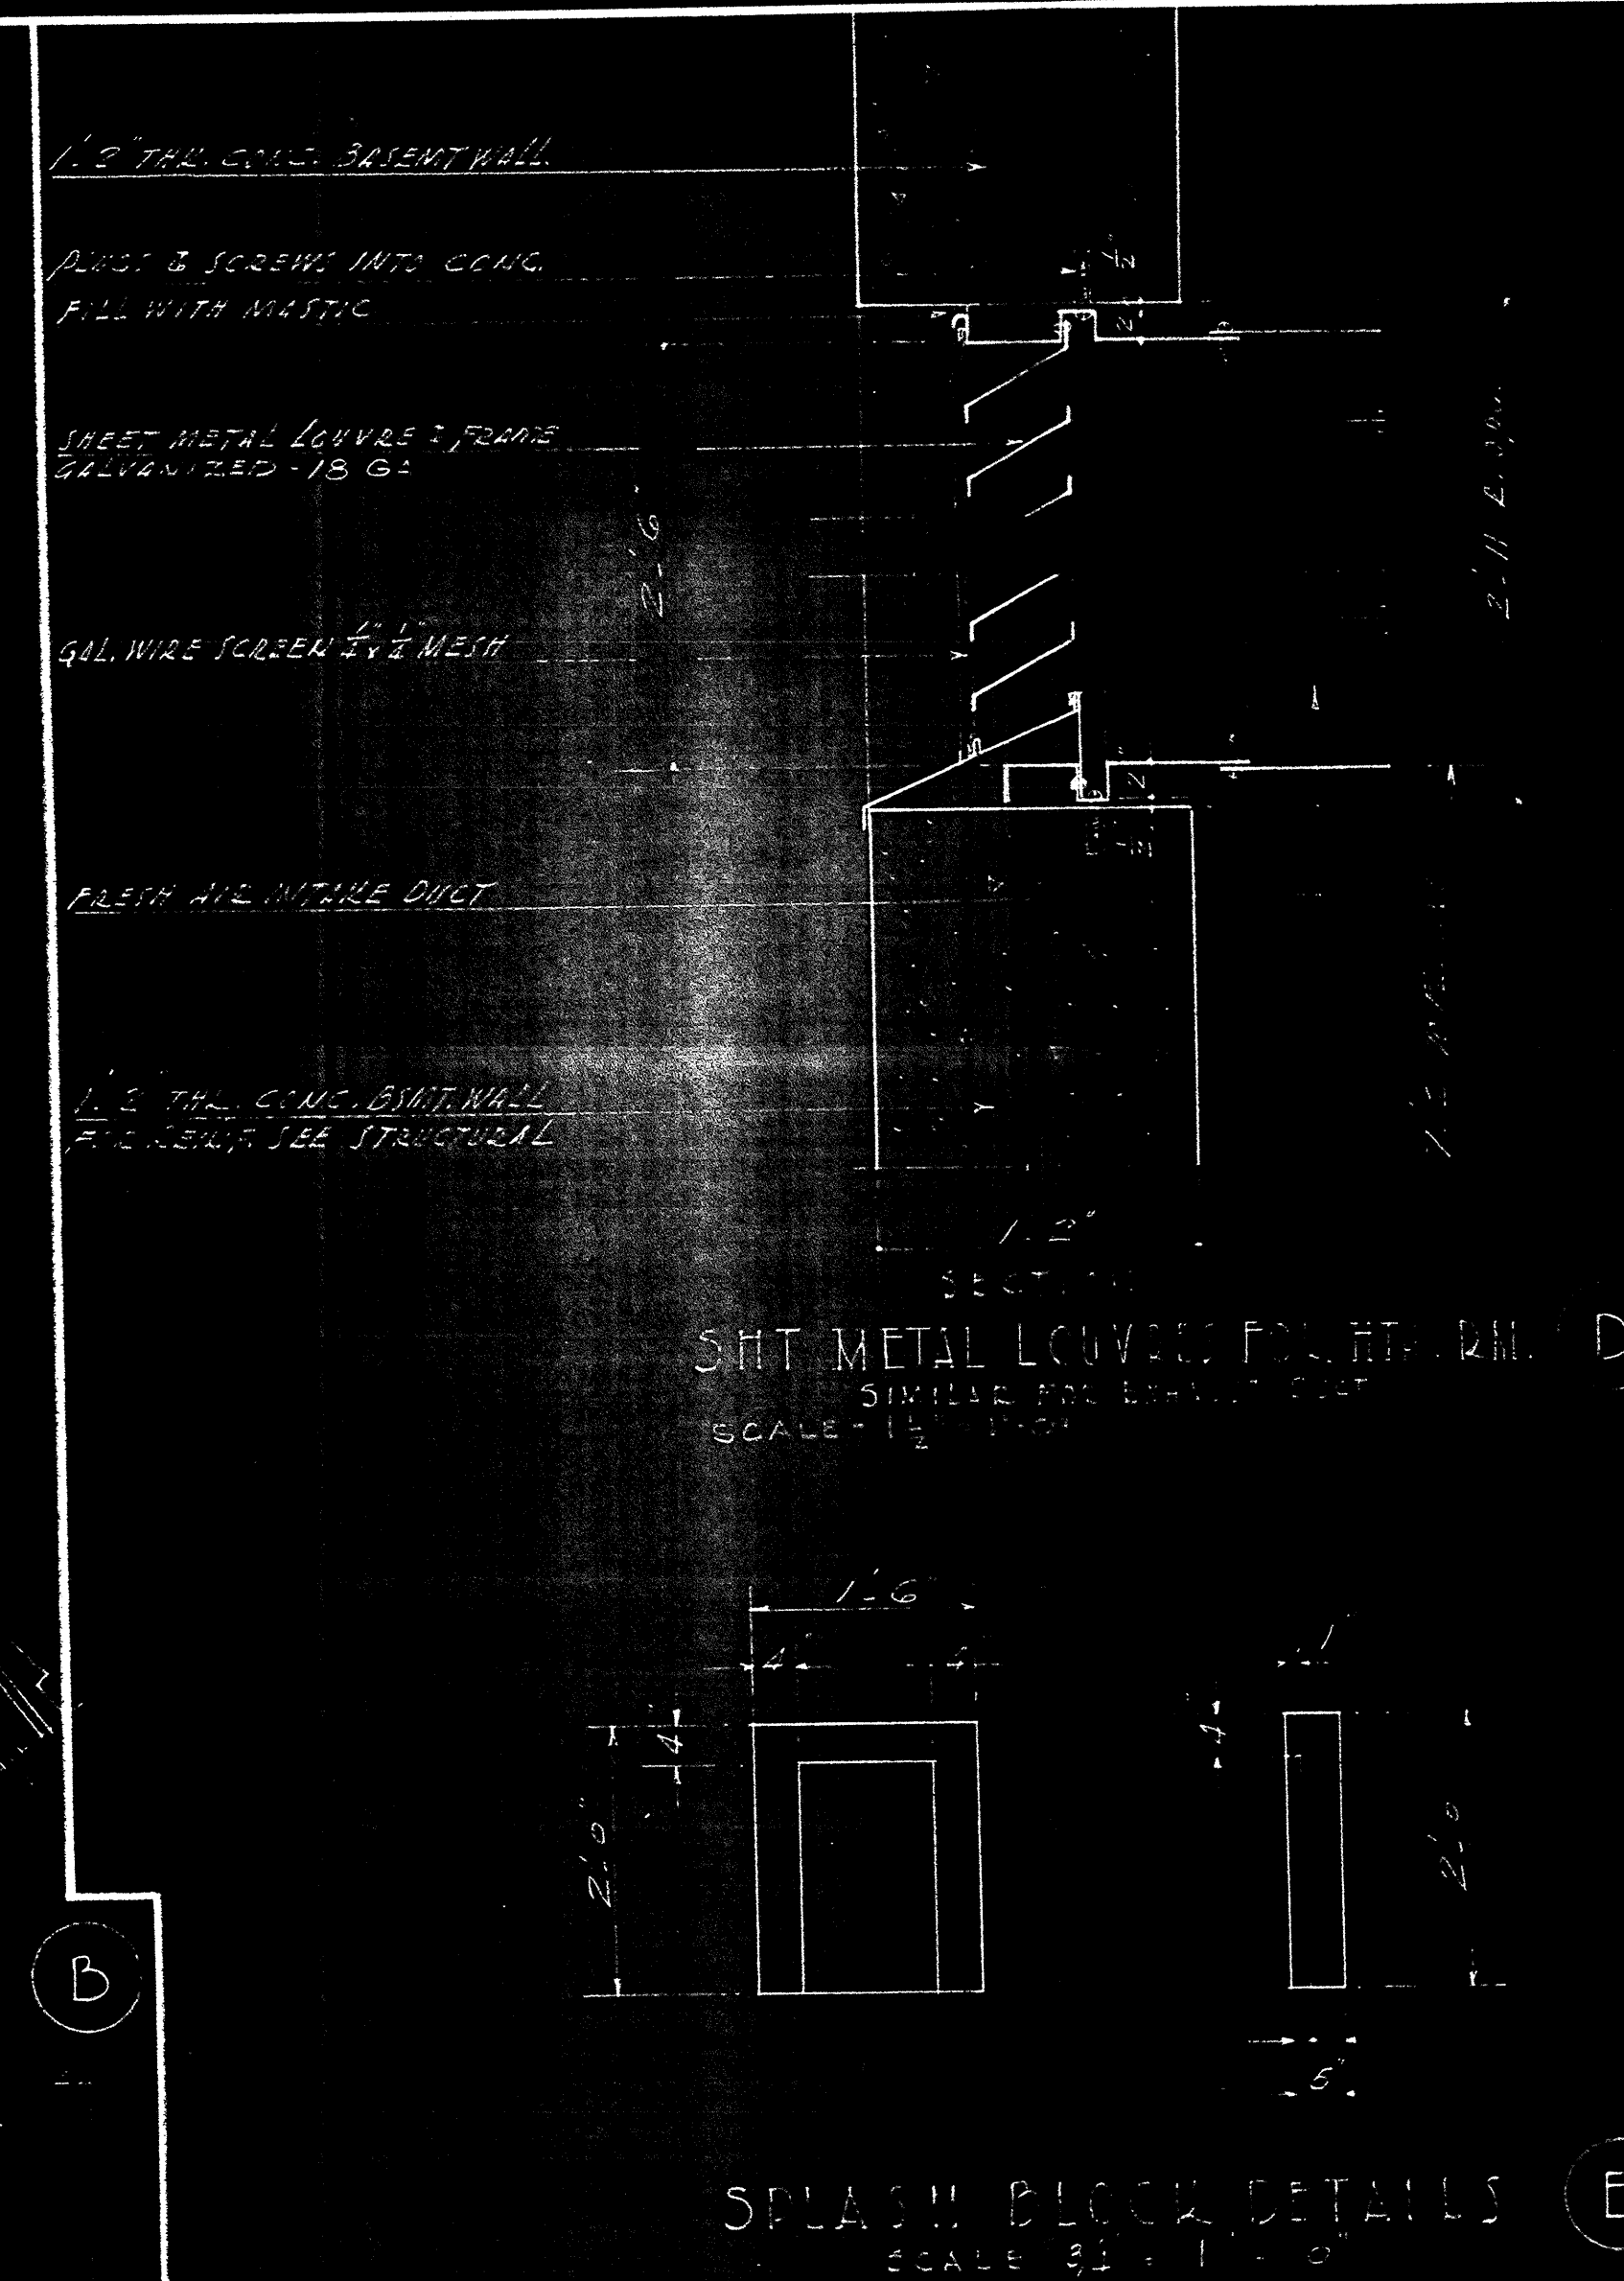
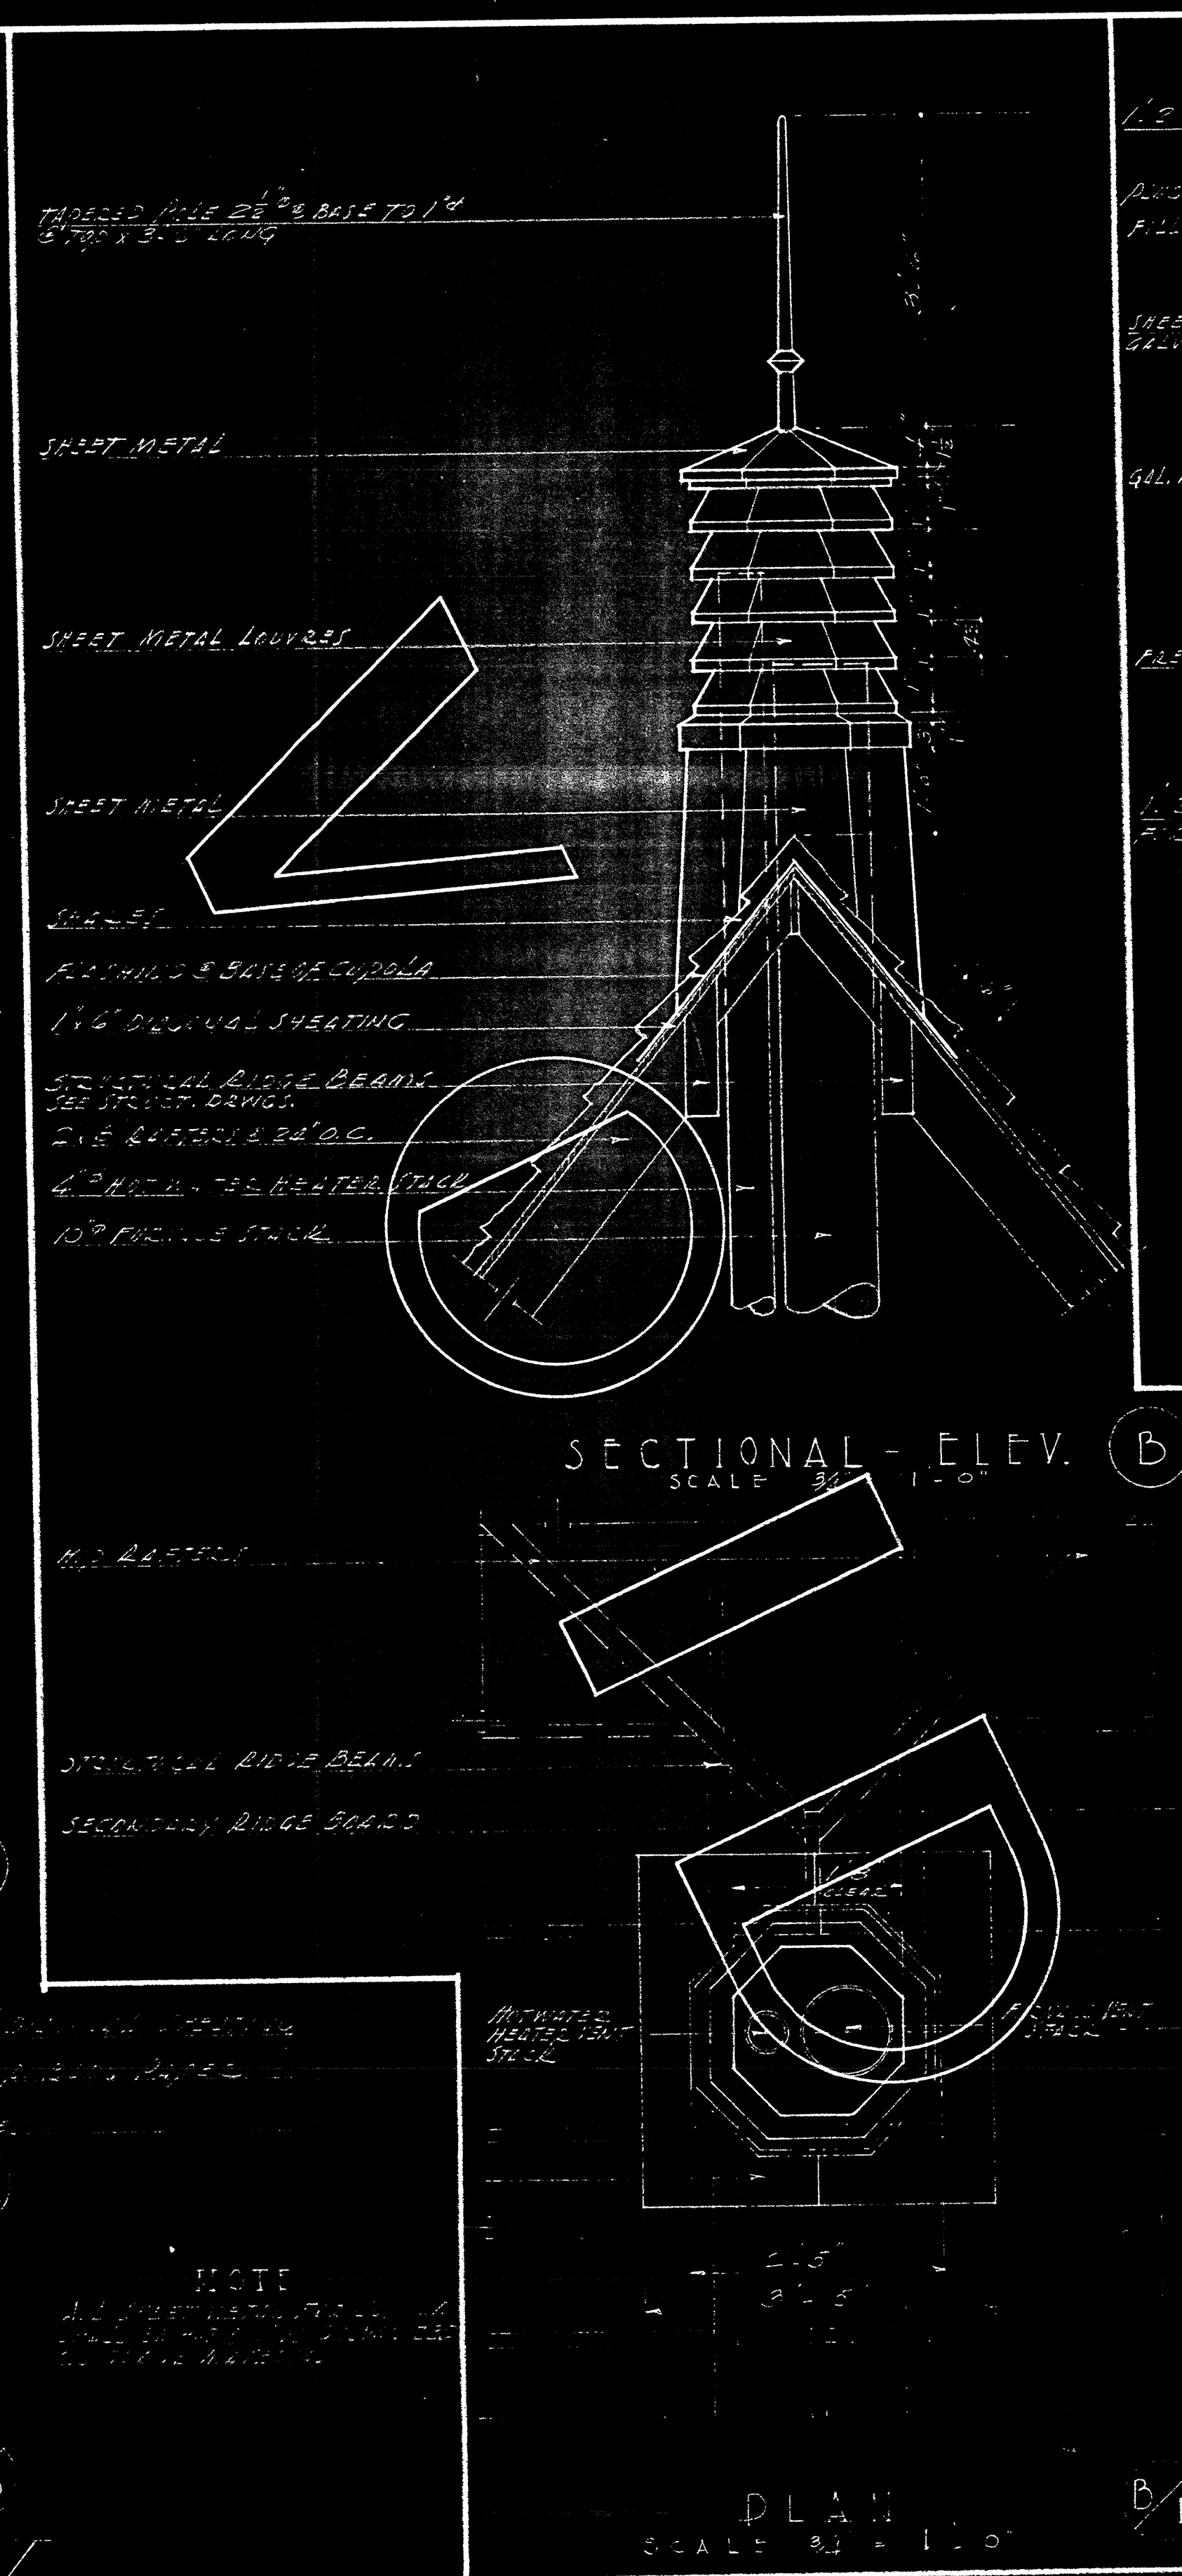
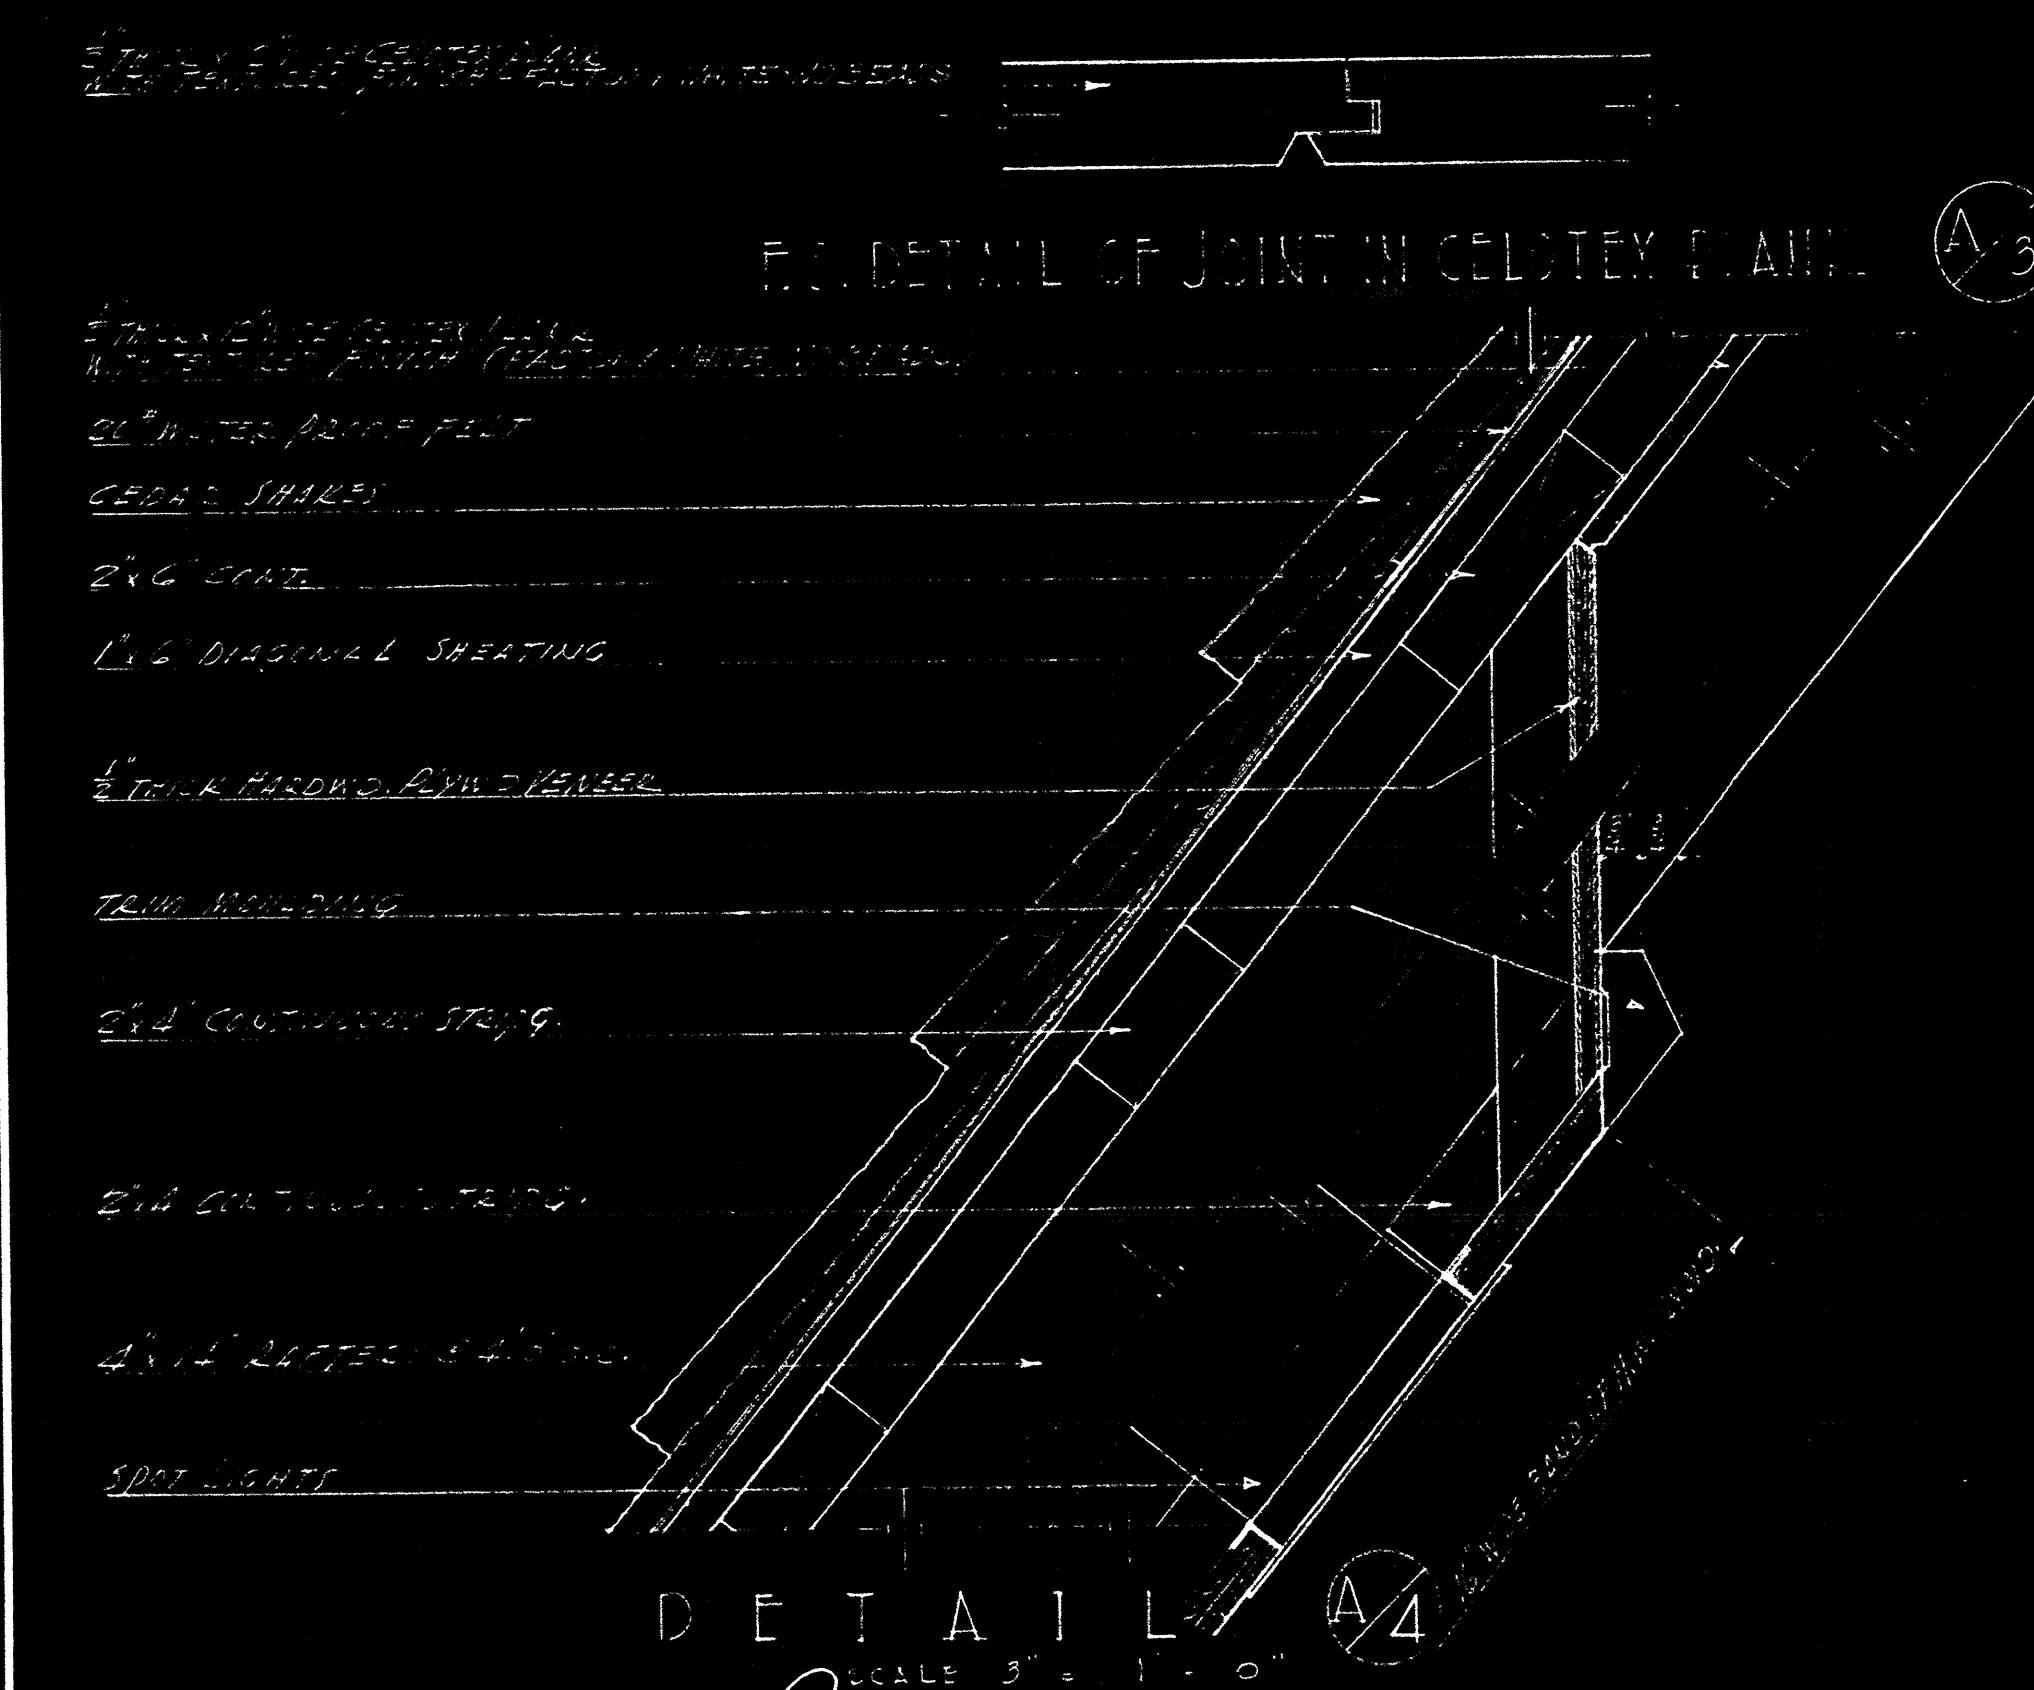
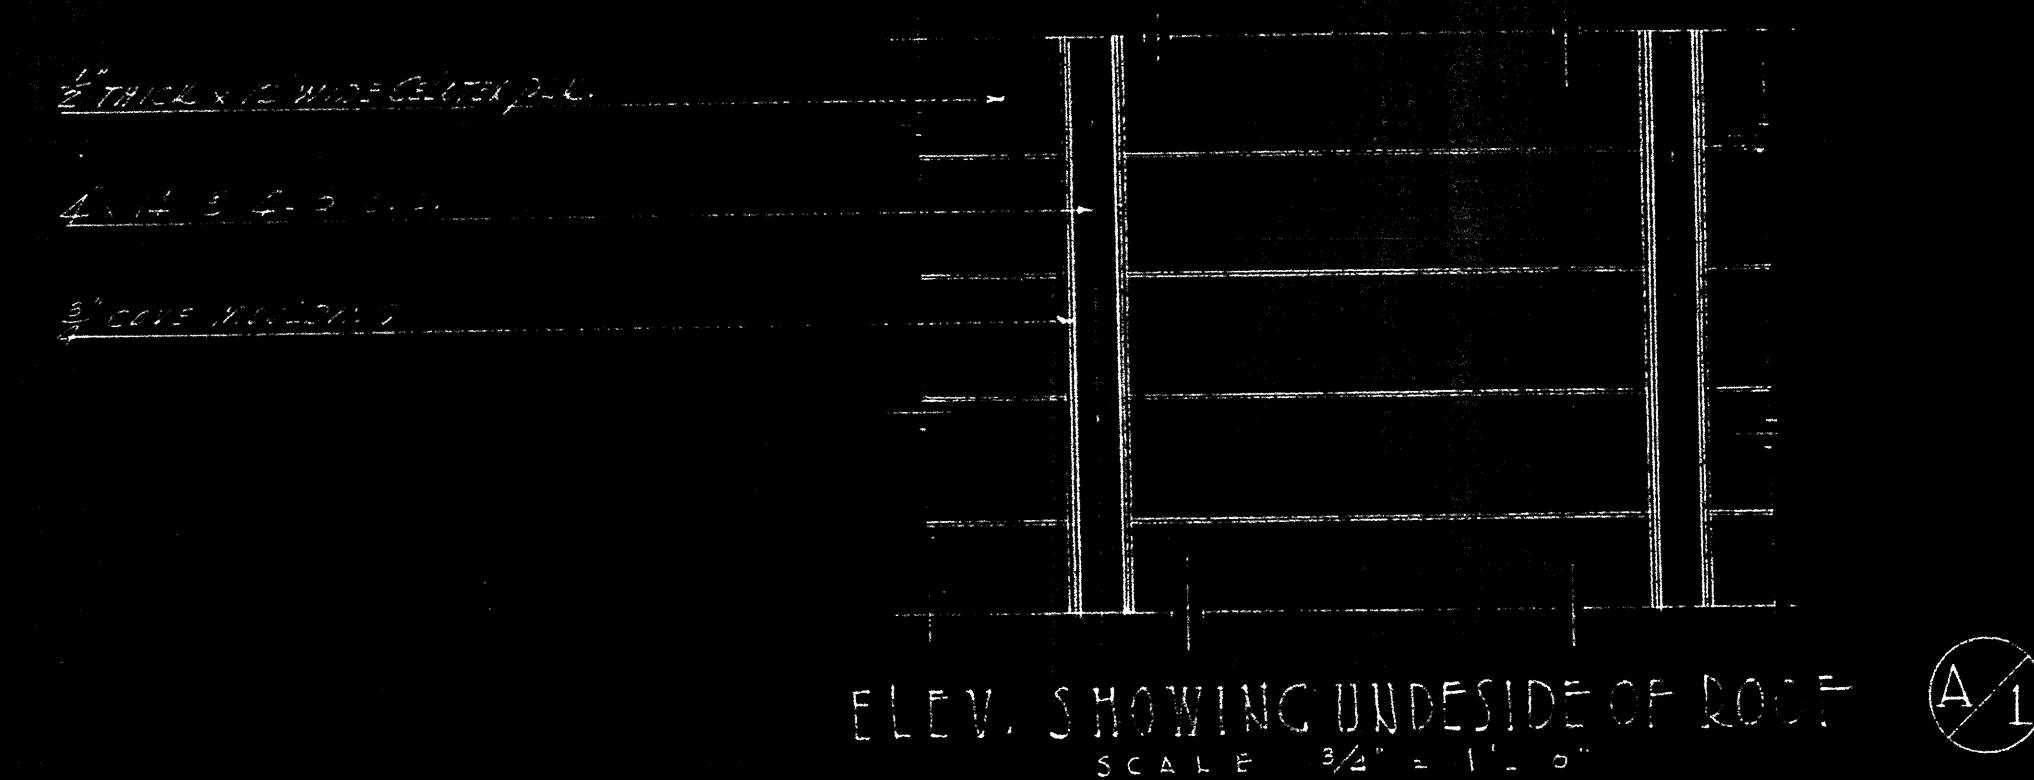


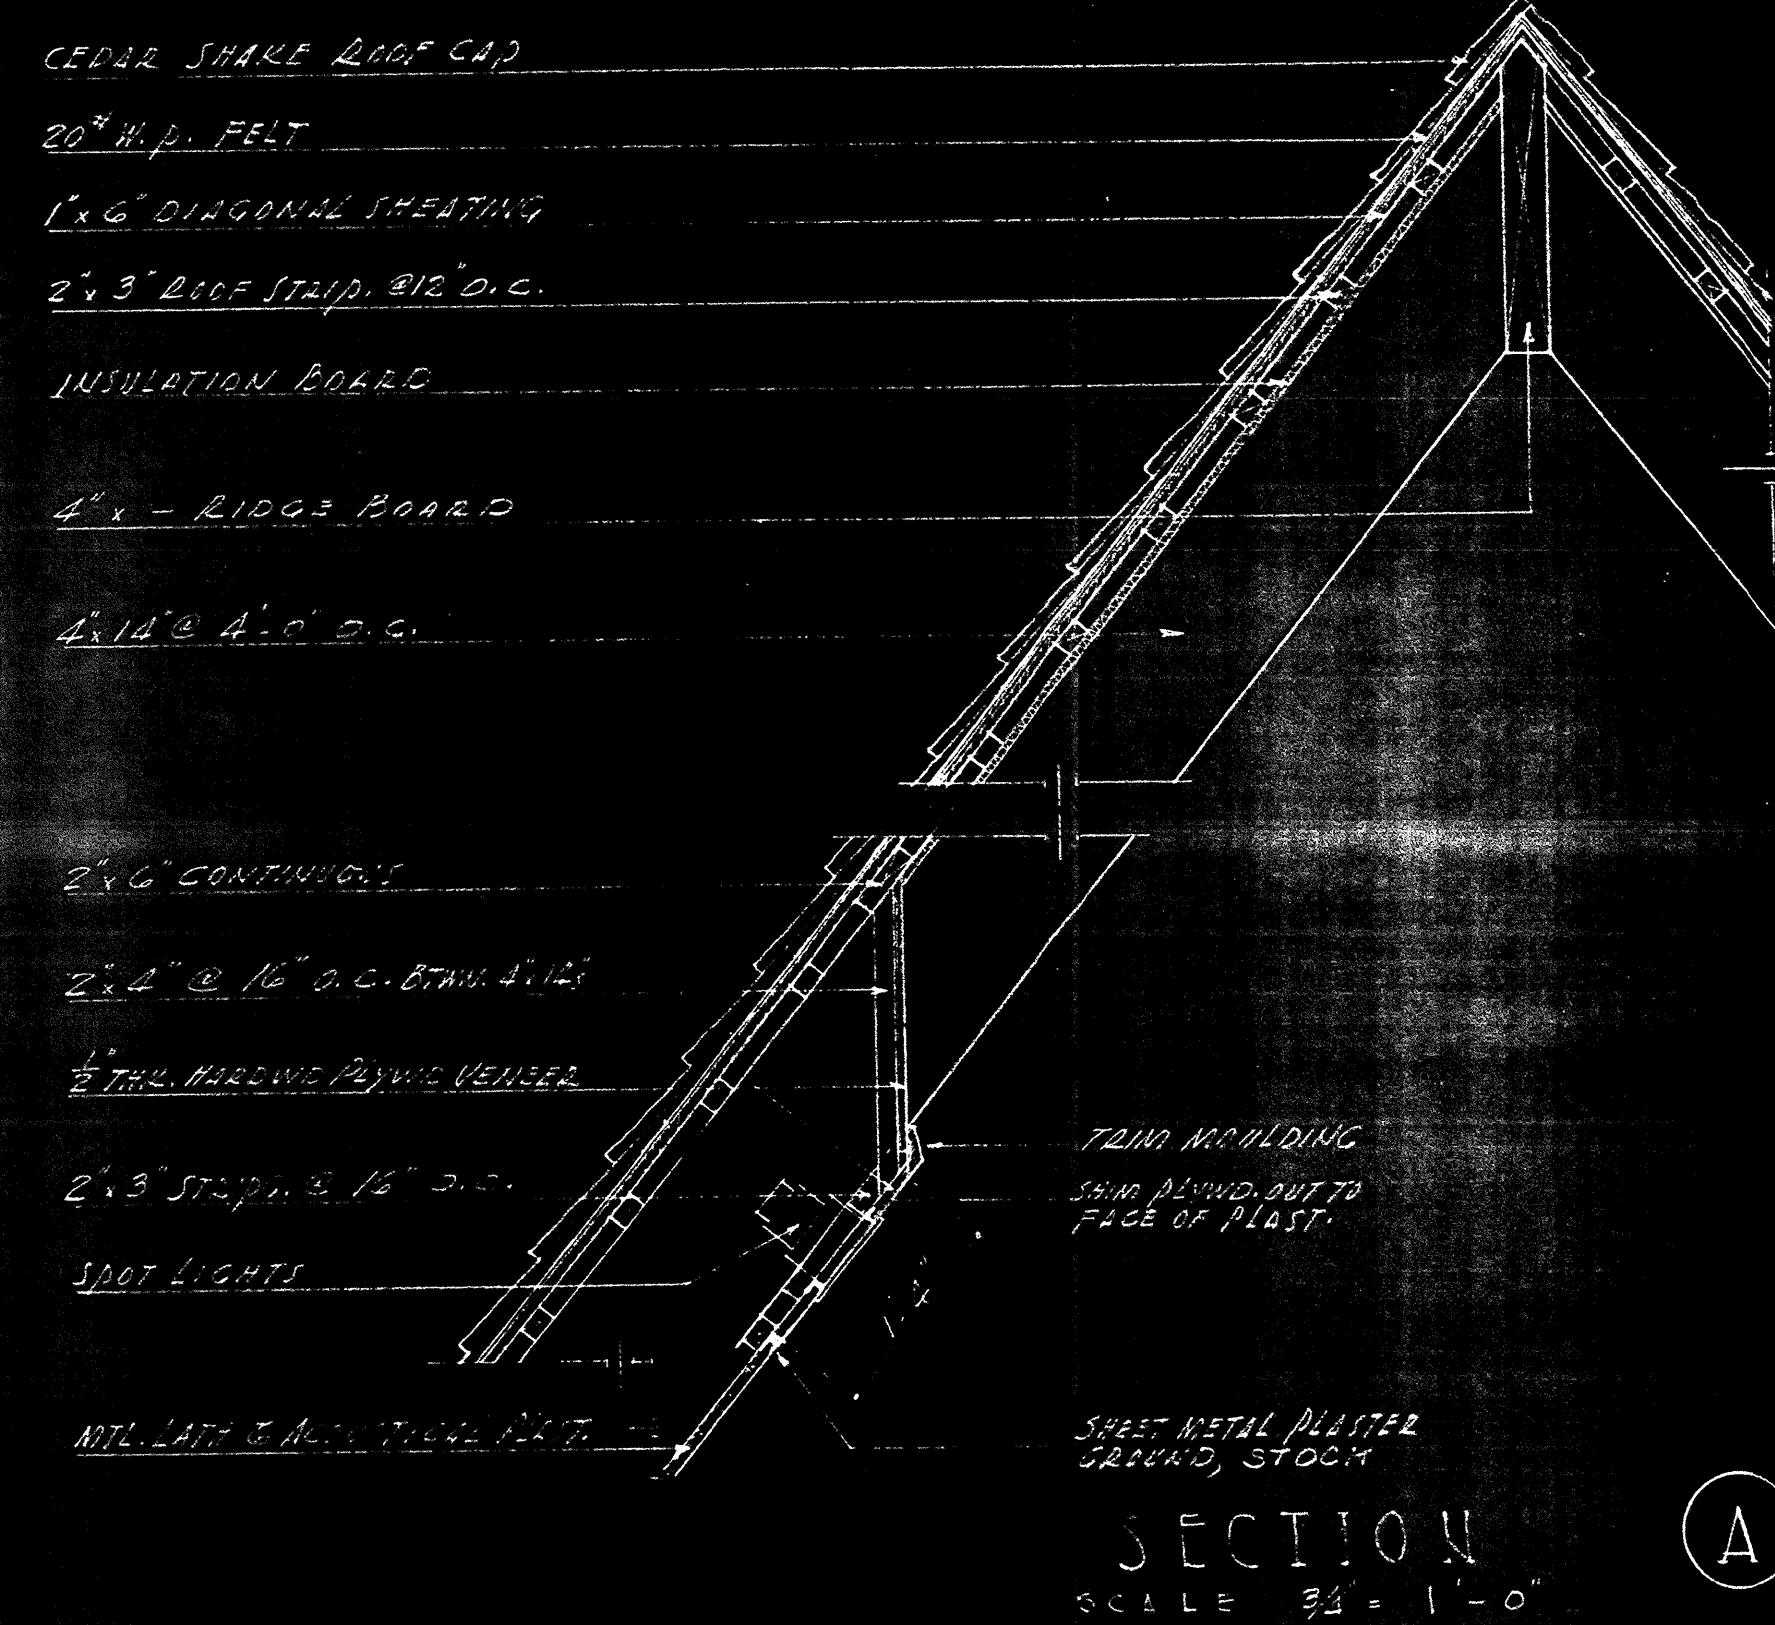

Remarks	Revisions	Engineers	Approval
---	---	---	--

AUSTIN FIELD & IRY
Architects
2311 WEST THIRD STREET • LOS ANGELES 5, CALIFORNIA • DUNKIRK 8-1326

MISCELLANEOUS DETAILS		DATE 10/1/68
ST. EDMUNDS EPISCOPAL CHURCH		COMPL 10/1/68
SAN MARINO CALIF.		SHEET NUMBER 10