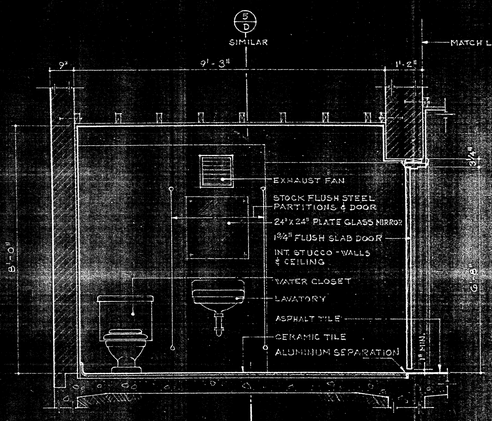

ELEVATION AT ROOM 102 (A)
SCALE - 1/2" = 1'-0"

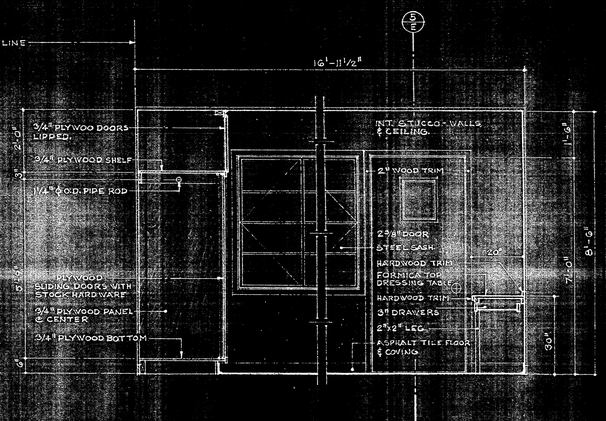

ELEVATION & CABINET SECTION - WEST VIEW ROOM 101 (B)
SCALE - 1/2" = 1'-0"

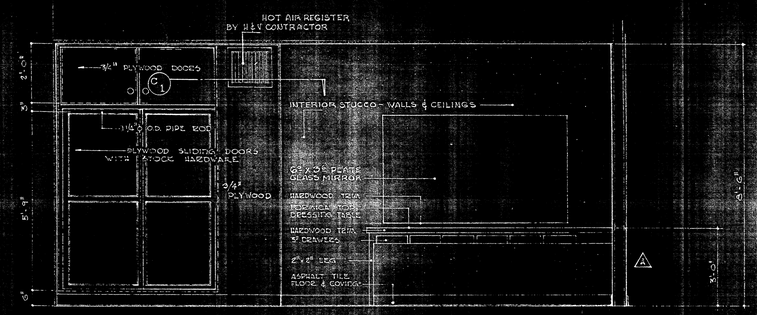

ELEVATION - NORTH VIEW ROOM 101 (C)
SCALE - 1/2" = 1'-0"

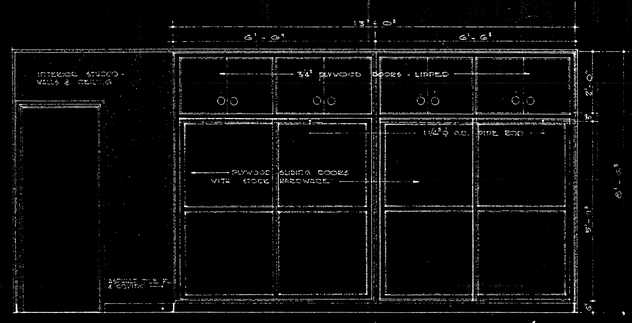

ELEVATION - SOUTH VIEW ROOM 101 (D)
SCALE - 1/2" = 1'-0"

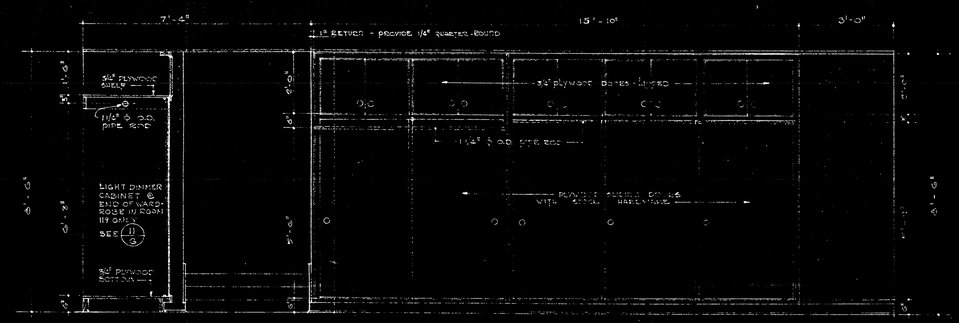

ELEVATION - EAST VIEW ROOM 109 (E) ... RM. 116 SIMILAR
SCALE - 1/2" = 1'-0"

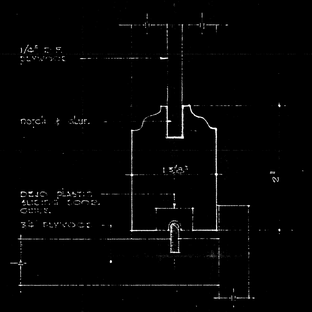

SLIDING DOOR & GUIDE
SCALE - FULL SIZE
(F)

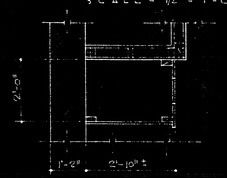

ACCOMODATE 2 ELECTRIC LIGHT DIMMER UNITS (END OF ROOM 109). ONE UNIT SETS ON CONC. FLOOR, THE OTHER SETS ON 2"x4" SHELF 4'-0" ABOVE FLR. SHELF SUPPORTED ON 2"x4"'S (HEIGHT 75")

3/4" PLYWOOD PANEL, REMOVABLE, ATTACH WITH WOOD SCREWS, SET 10"x6" PERFORATED SHEET METAL VENTS @ 1'-0" & 5'-0"

LIGHT DIMMER CABINET (G)
SCALE - 1/2" = 1'-0"

Remarks

Revisions
△ DELETE HOT AIR REGISTER AT RM. 101
W. FRYER 1 NOV. 51

Engineers

Approvals

DRAWN FRYER
CHECK'D
ARCHITECT — LICENSE #

AUSTIN, FIELD & FRY
Architects
2311 WEST THIRD STREET · LOS ANGELES 5, CALIFORNIA · DUNKIRK 8-1326

INTERIOR ELEVATIONS I
ST EDMUNDS EPISCOPAL CHURCH
SAN MARINO CALIF

DATE 30-MAR-51
COMM. 1061
SHEET NUMBER 11