

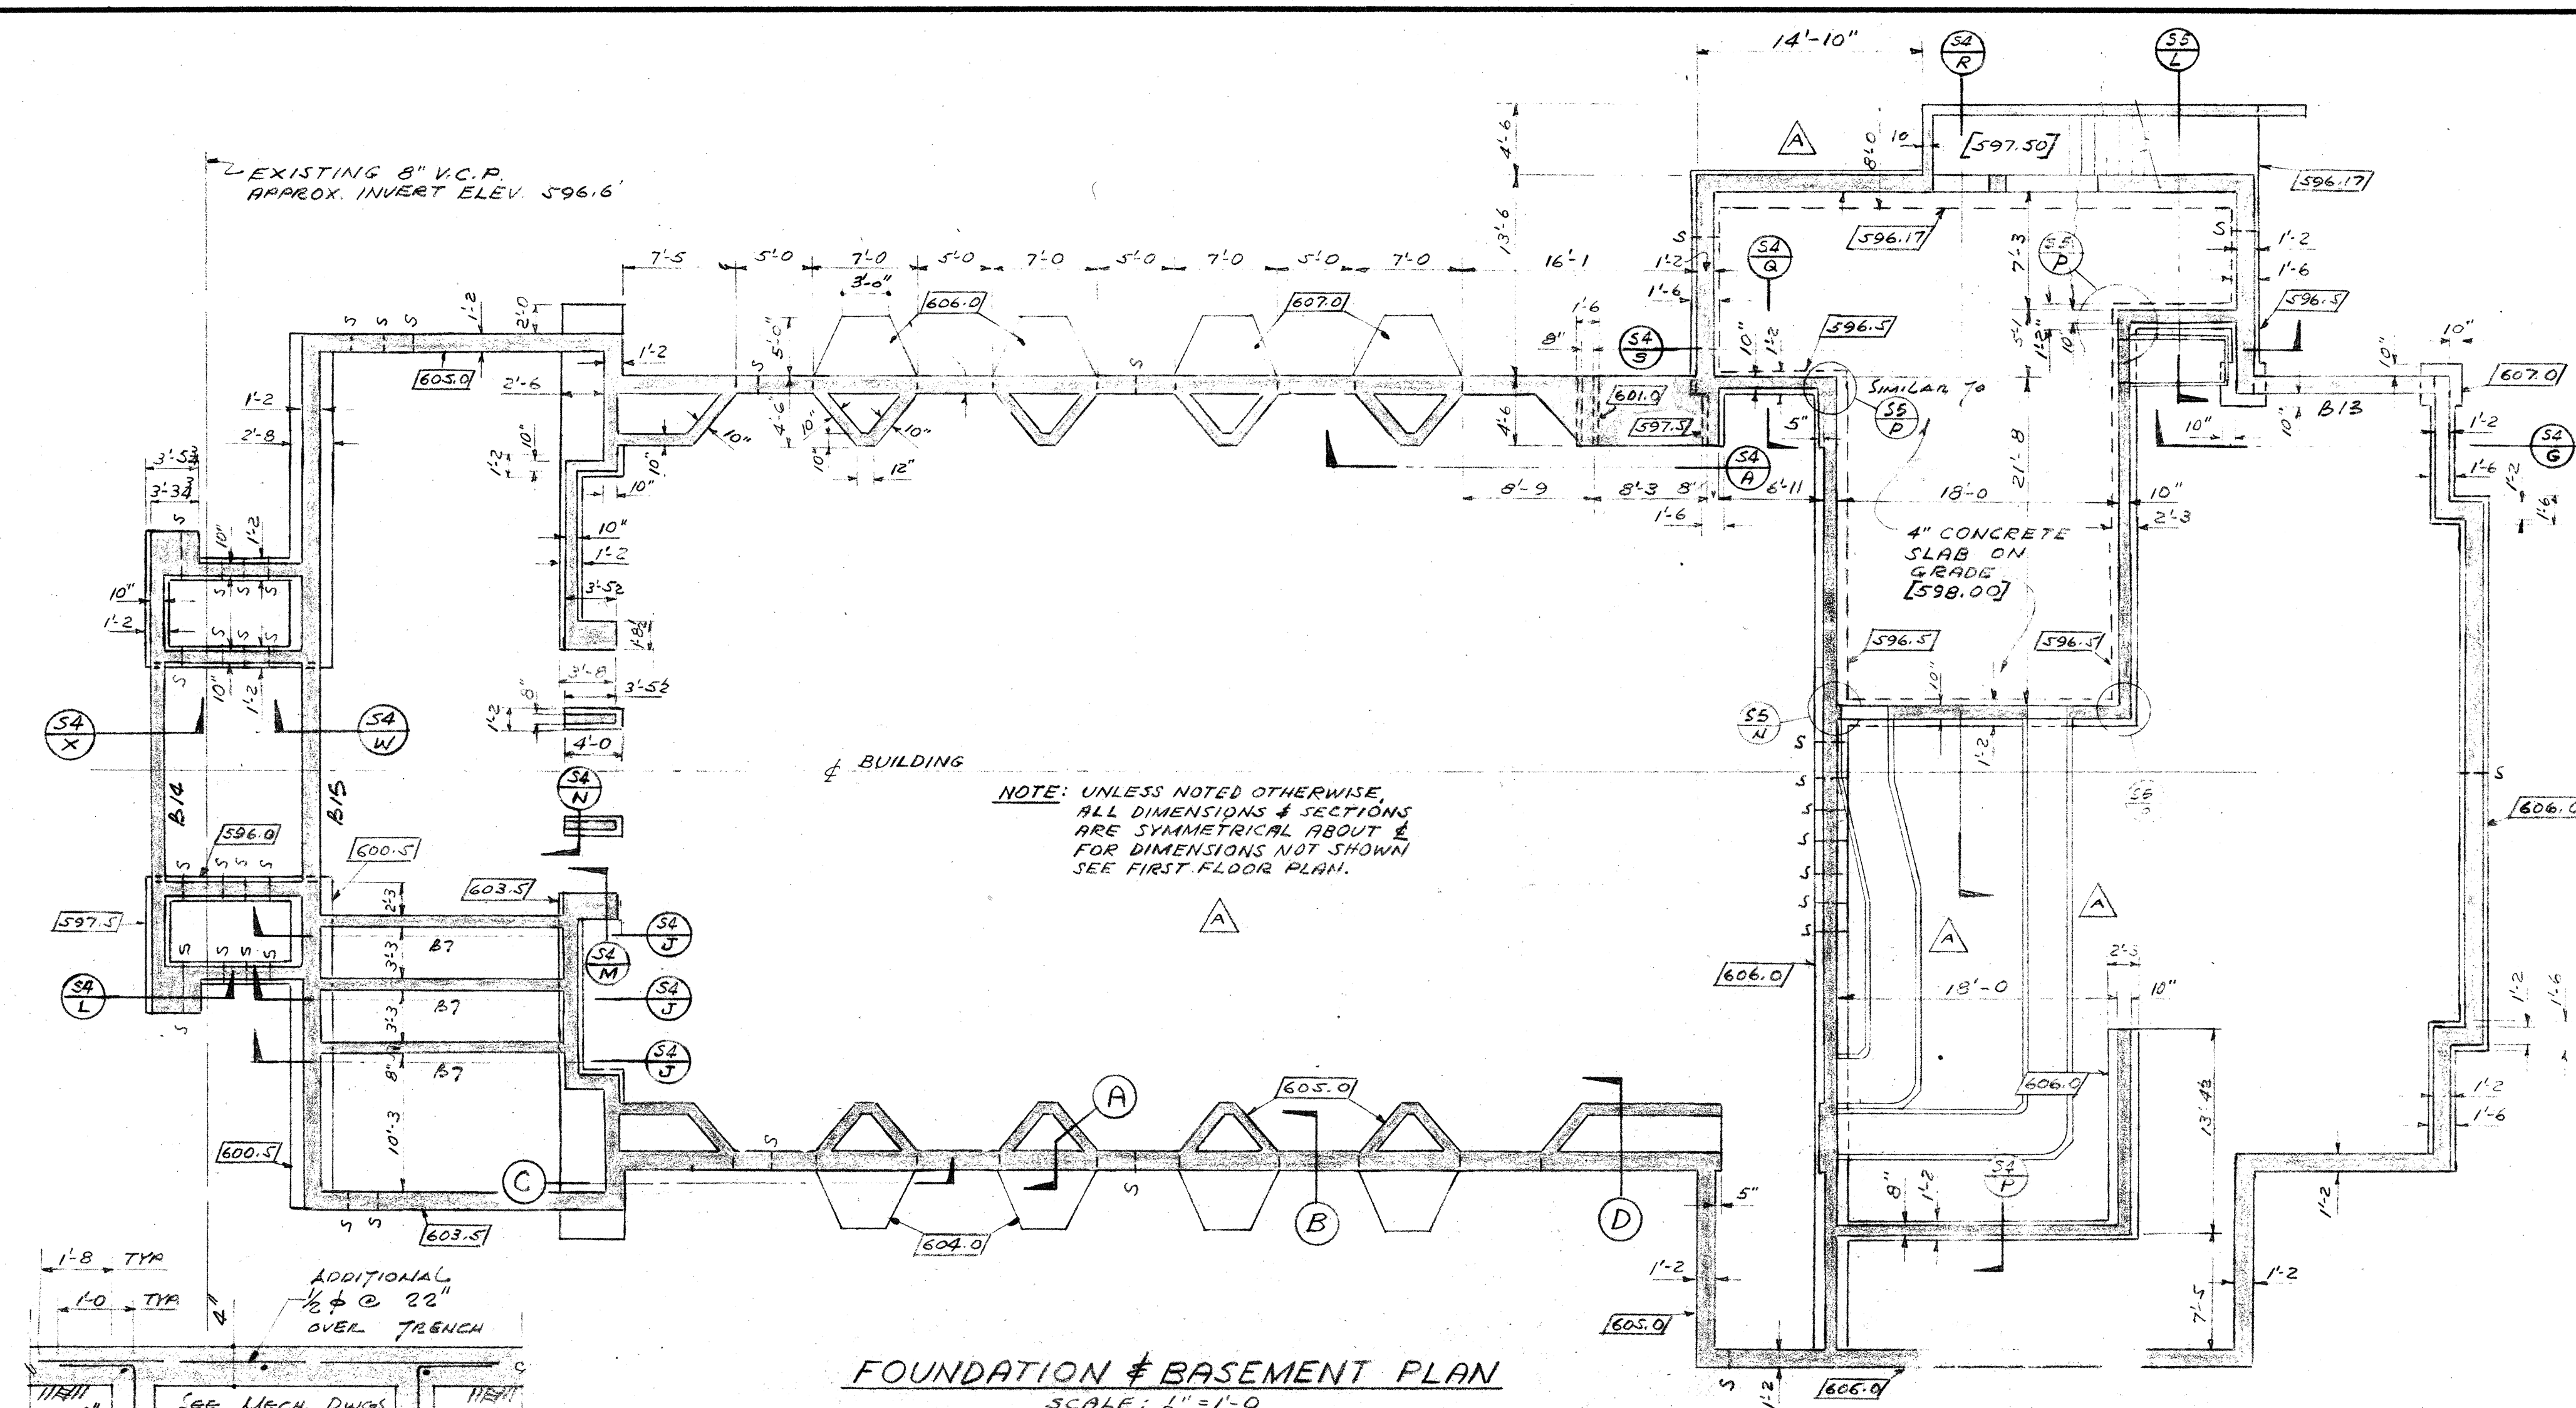
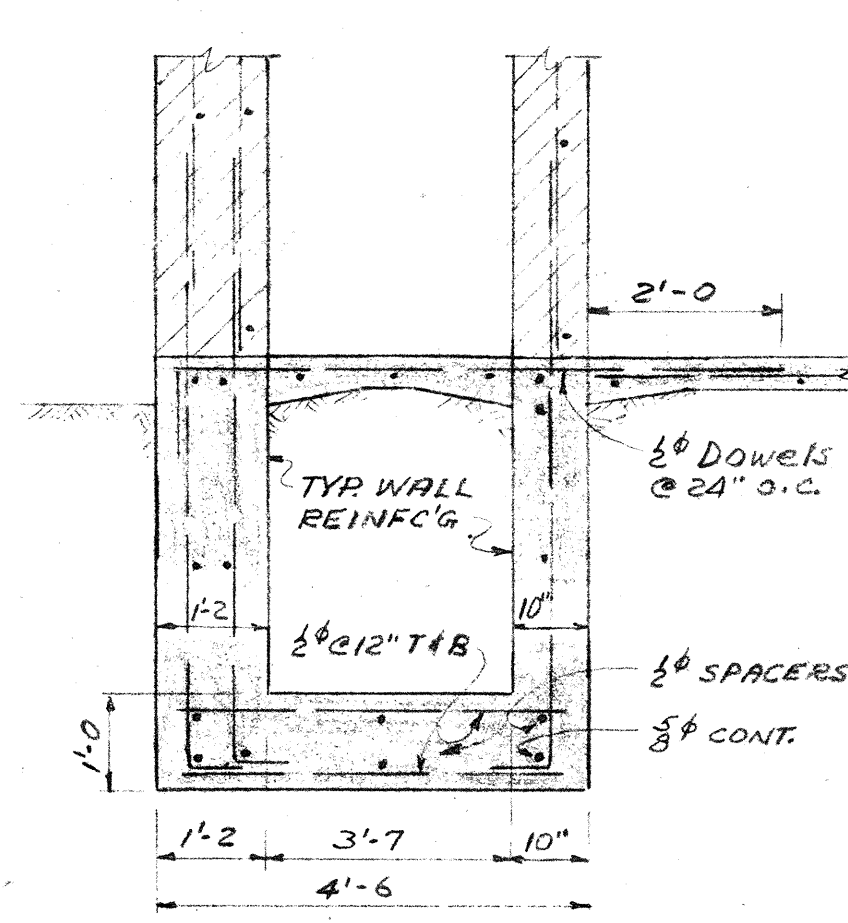
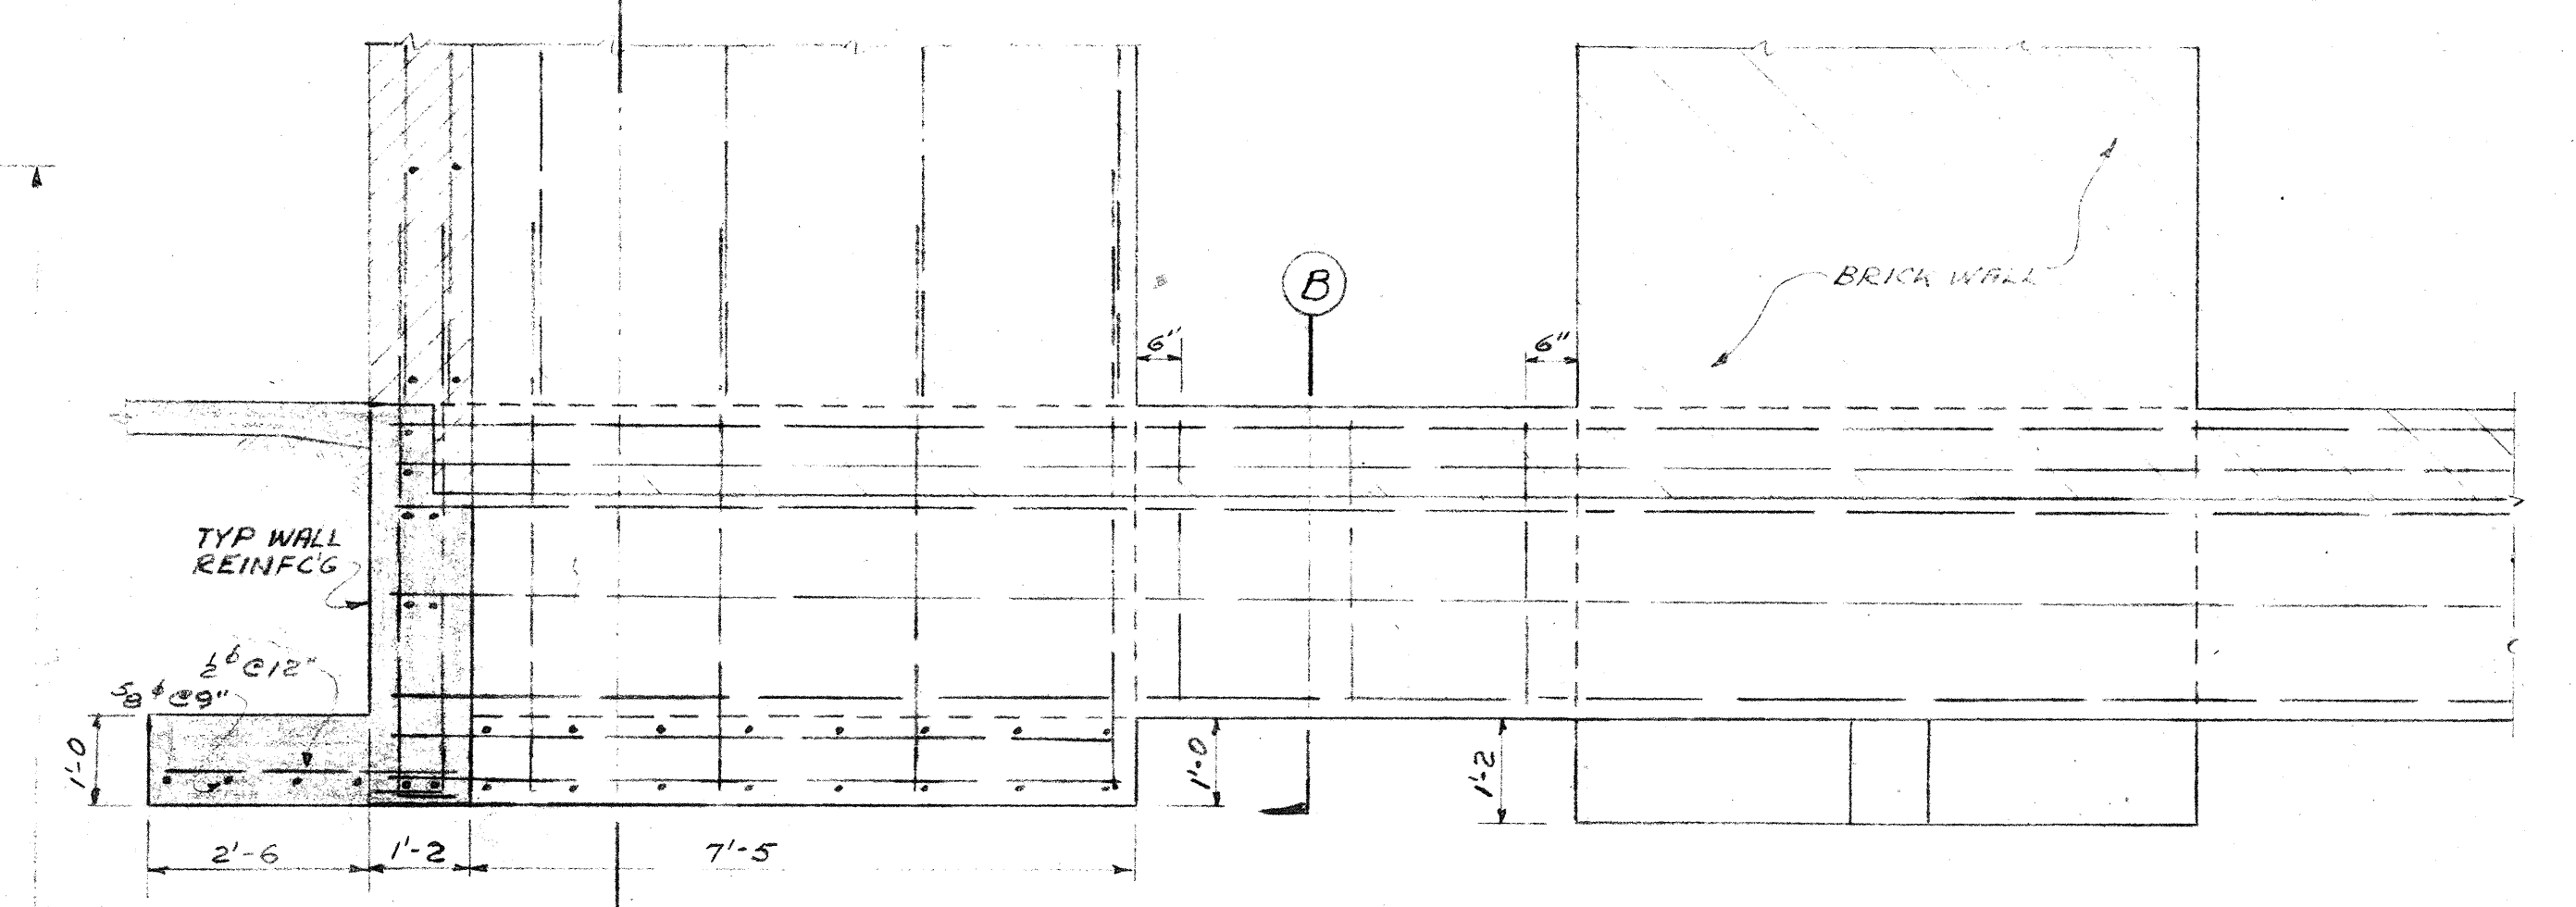
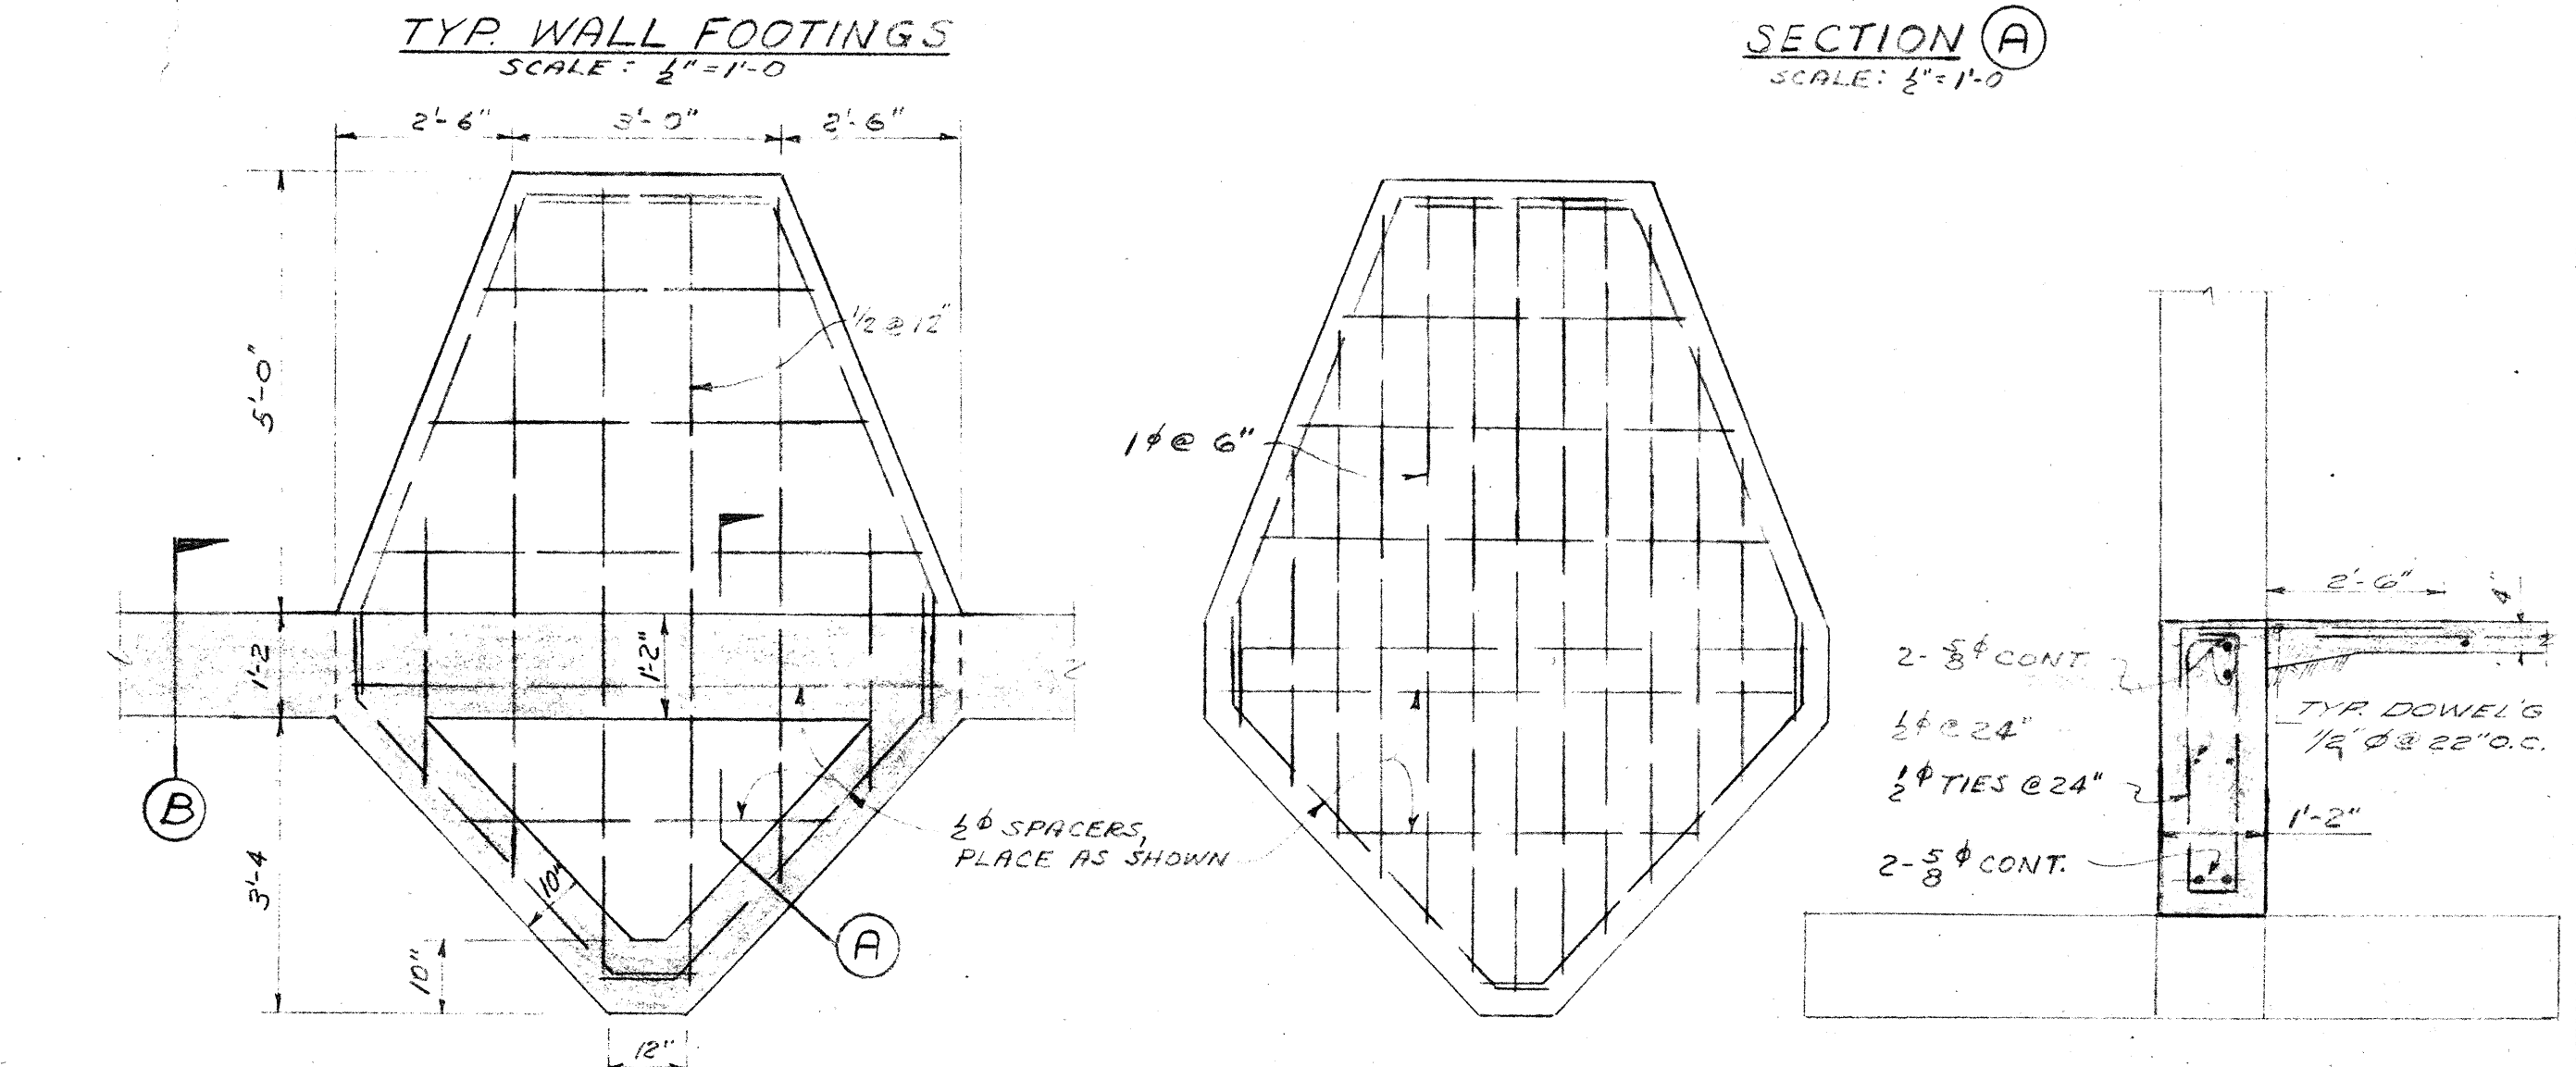
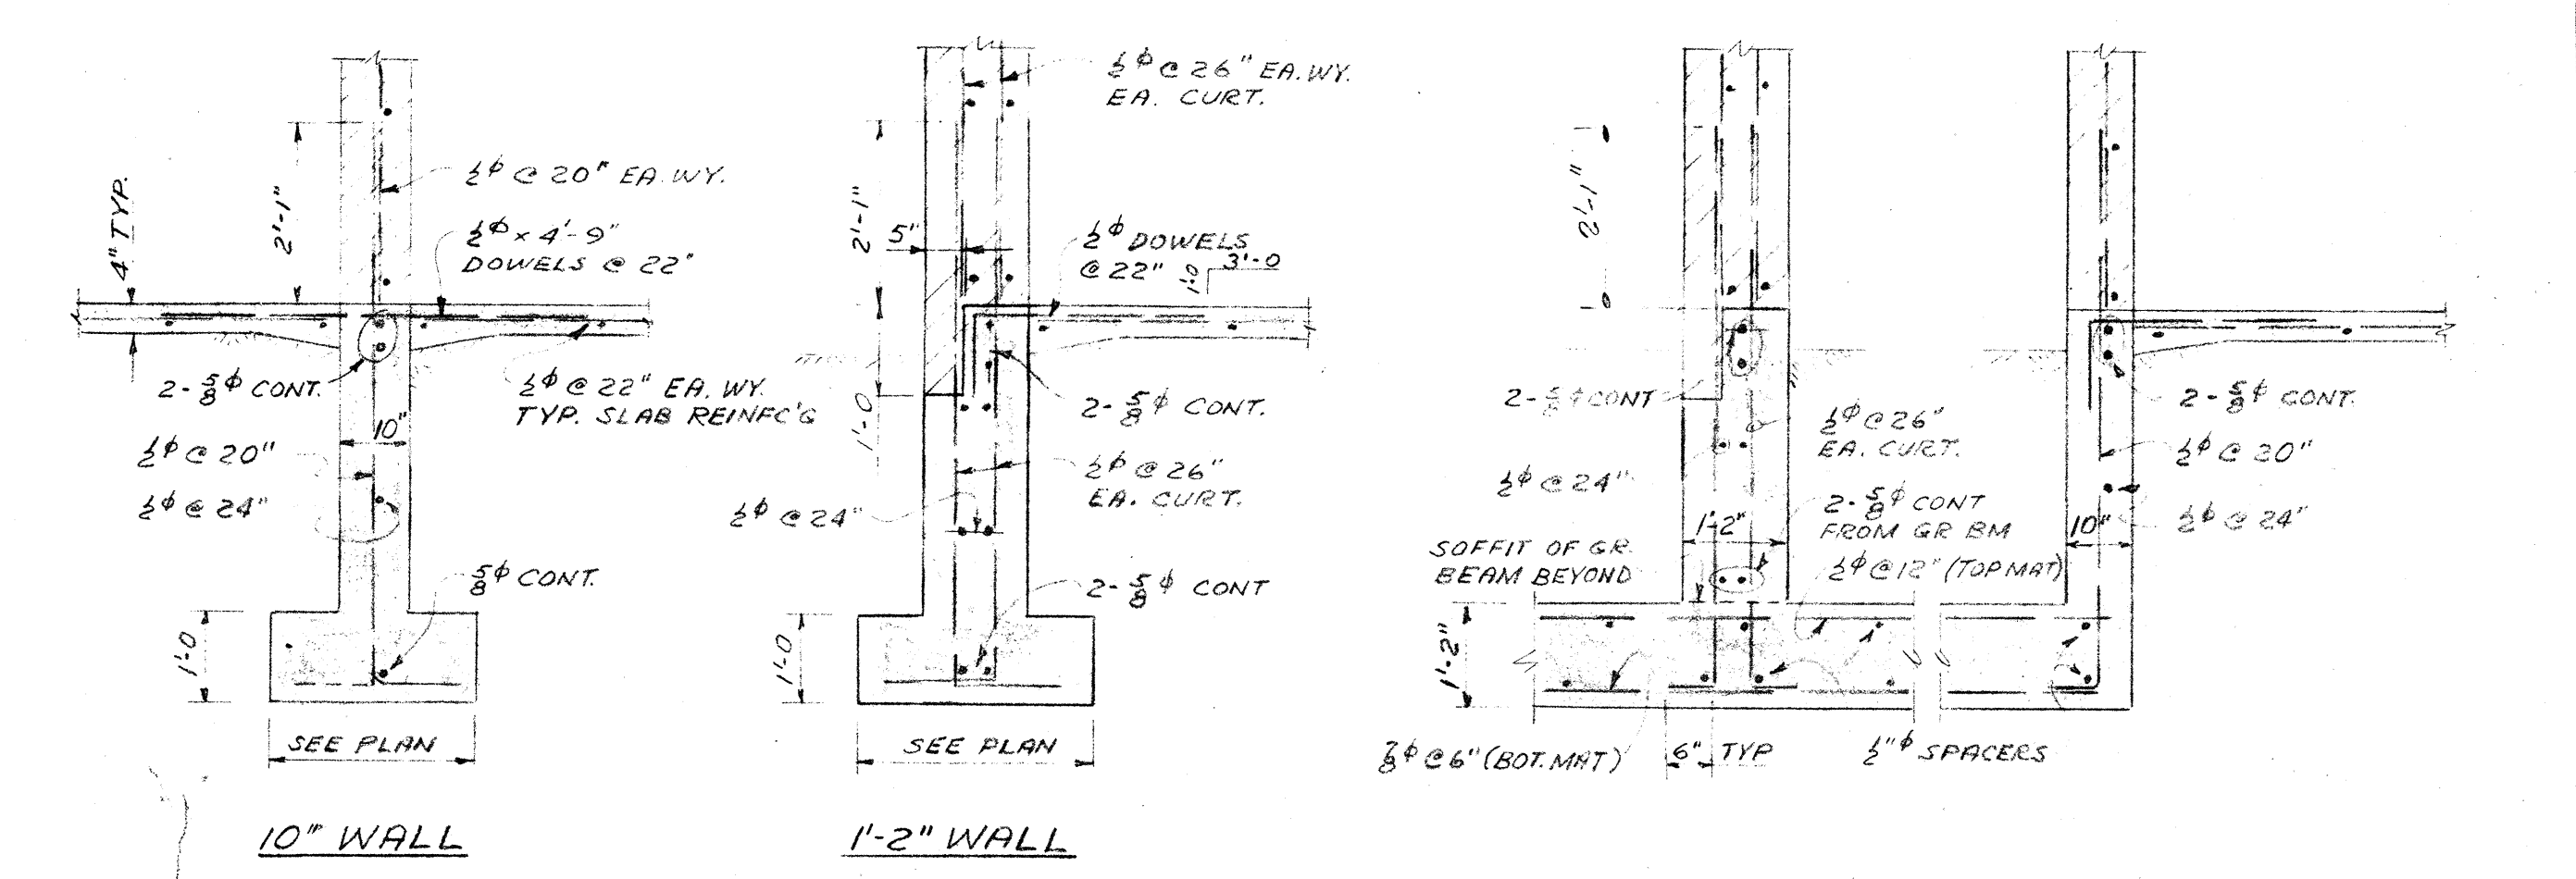


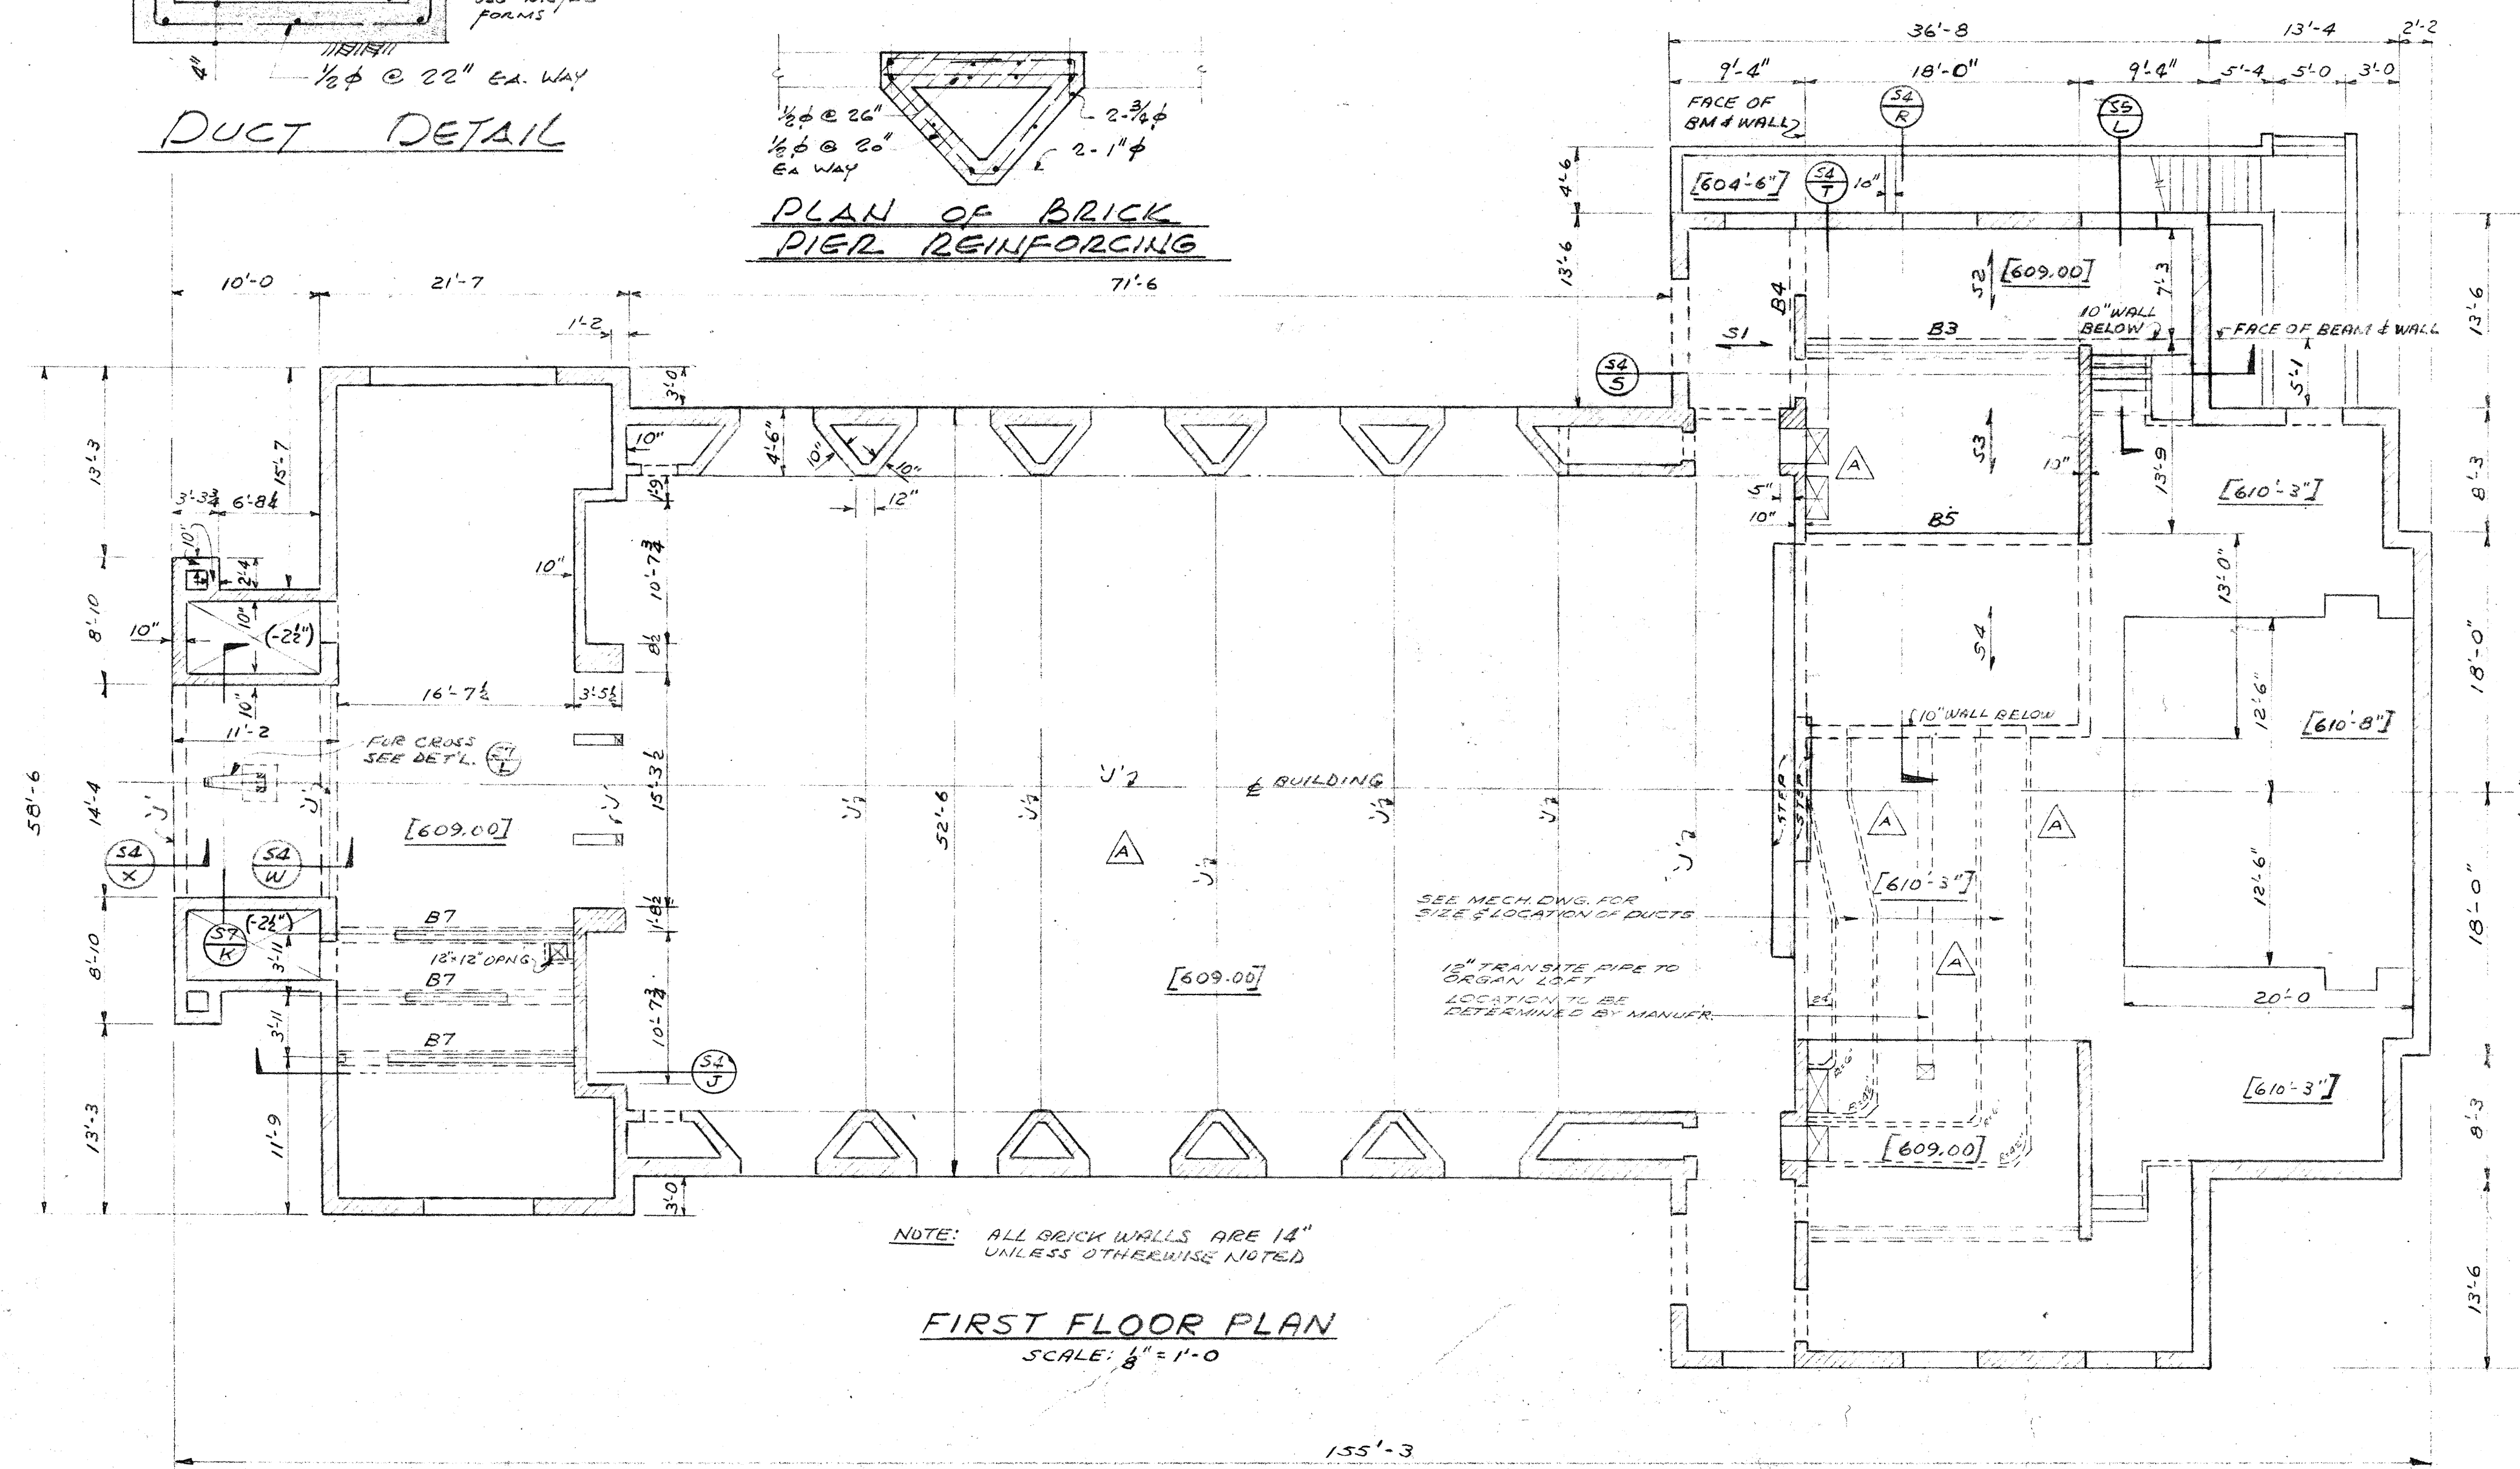

DUCT DETAIL

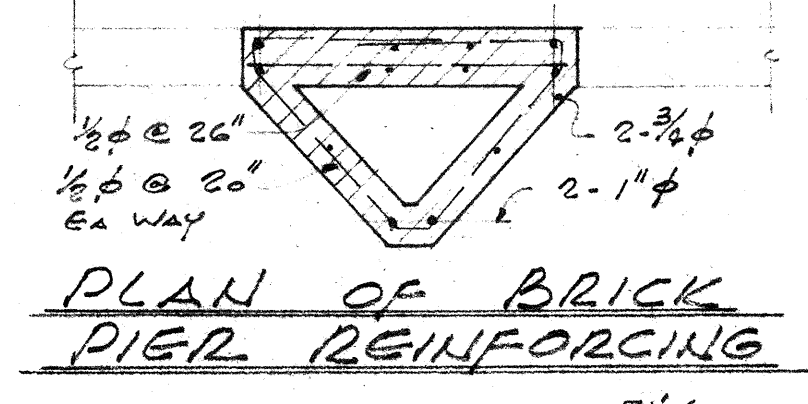

- NOTES:
1. ALL FOOTINGS SHALL BE CARRIED DOWN TO A MIN. OF 4'-0" BELOW EXISTING GRADE.
 2. THERE SHALL BE A MIN. OF 2" OF SAND UNDER ALL SLABS ON GRADE.
 3. S INDICATES A FOOTING STEP.
 4. [606.0] INDICATES ELEVATION OF BOTTOM OF FOOTING.
 5. [609.0] INDICATES ELEVATION OF FINISHED FLOOR.
 6. (-2'-0") INDICATES A DROPPED SLAB AND THE AMOUNT OF DROP BELOW THE FINISHED FLOOR.
 7. J1 REPRESENTS A JOINT IN THE SLAB AS DETAILED ON SH. 5-1.
 8. FOR SIZES OF ALL CONCRETE DUCTS SEE MECHANICAL DWGS.
 9. FOOTING ELEVATIONS ARE FOR ESTIMATING PURPOSES ONLY. ALL FOOTINGS MUST BE BROUGHT DOWN TO FIRM UNDISTURBED SOIL.