




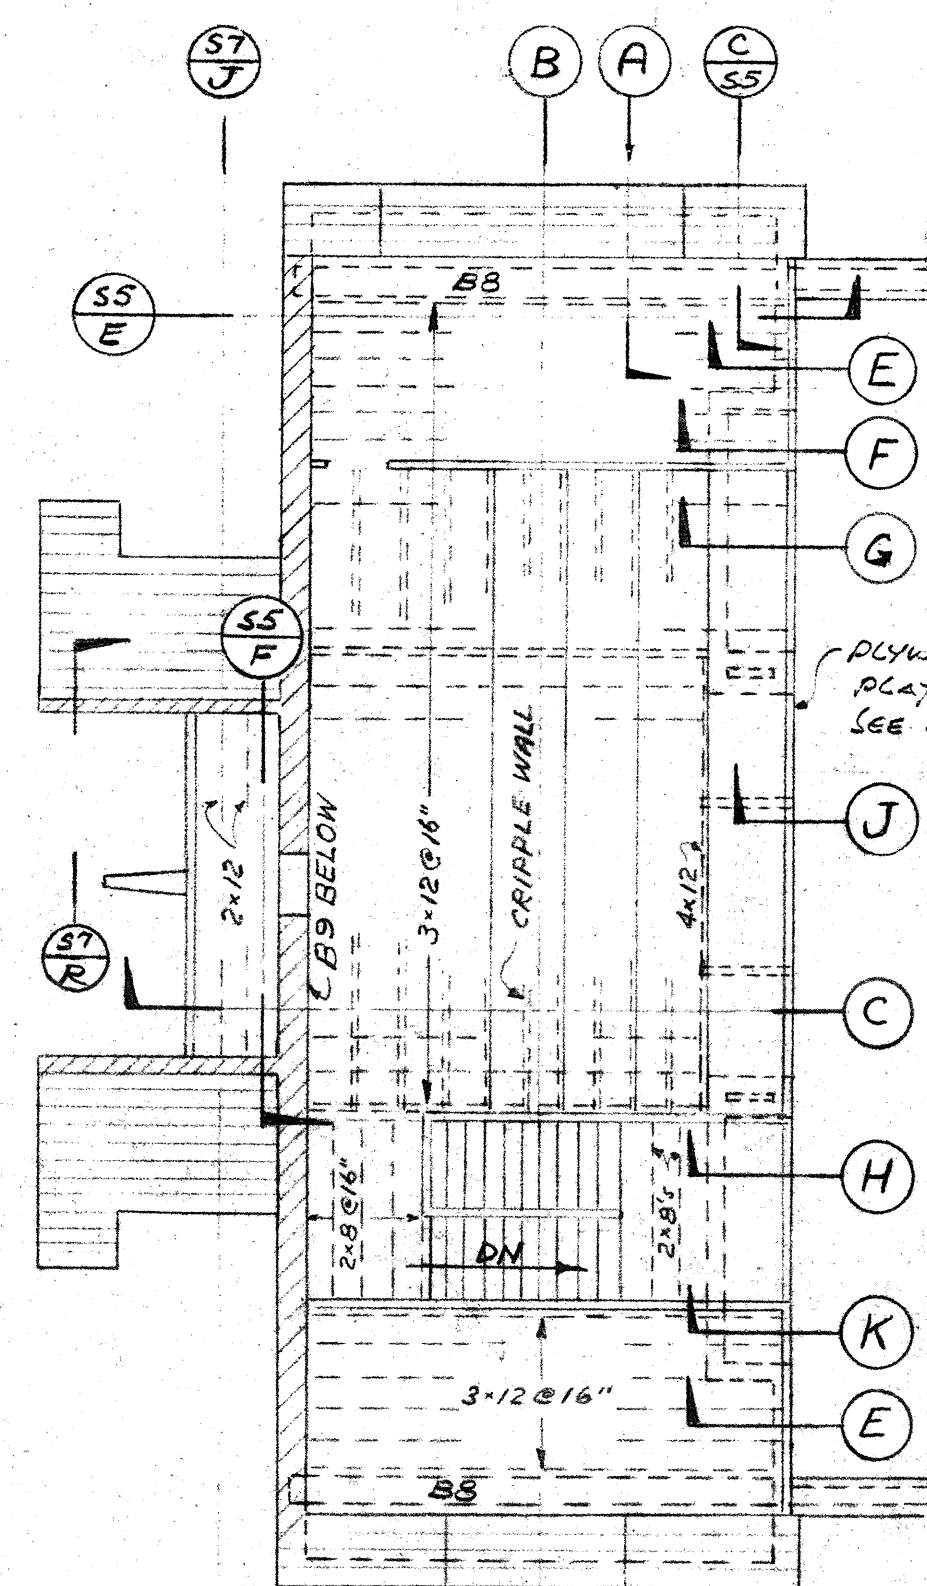


BALCONY FRAMING PLAN
SCALE: 3/8"=1'-0"

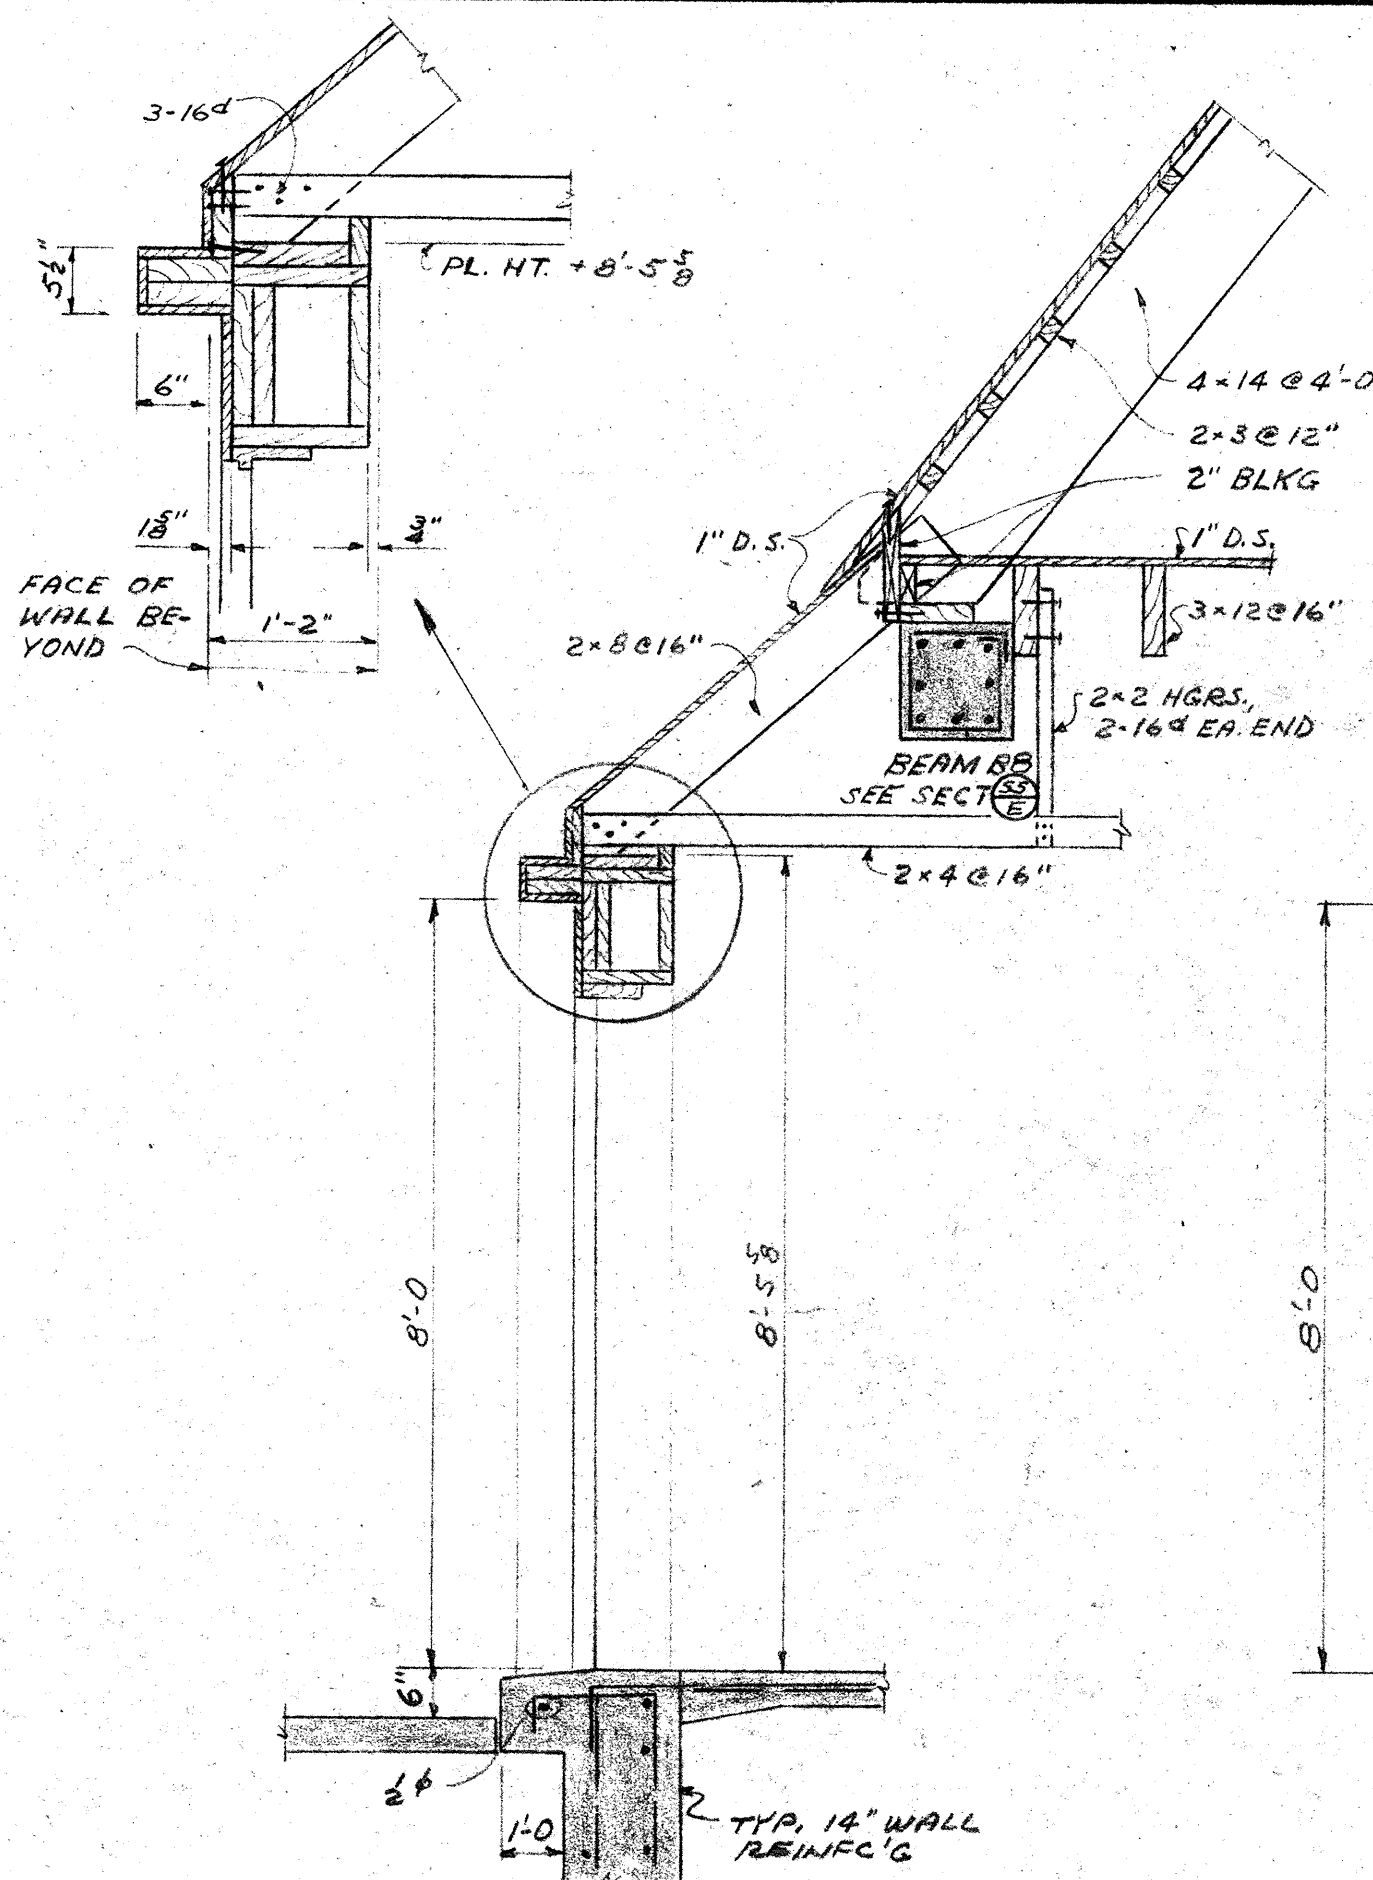


SECTION A
SCALE: 1/2"=1'-0"

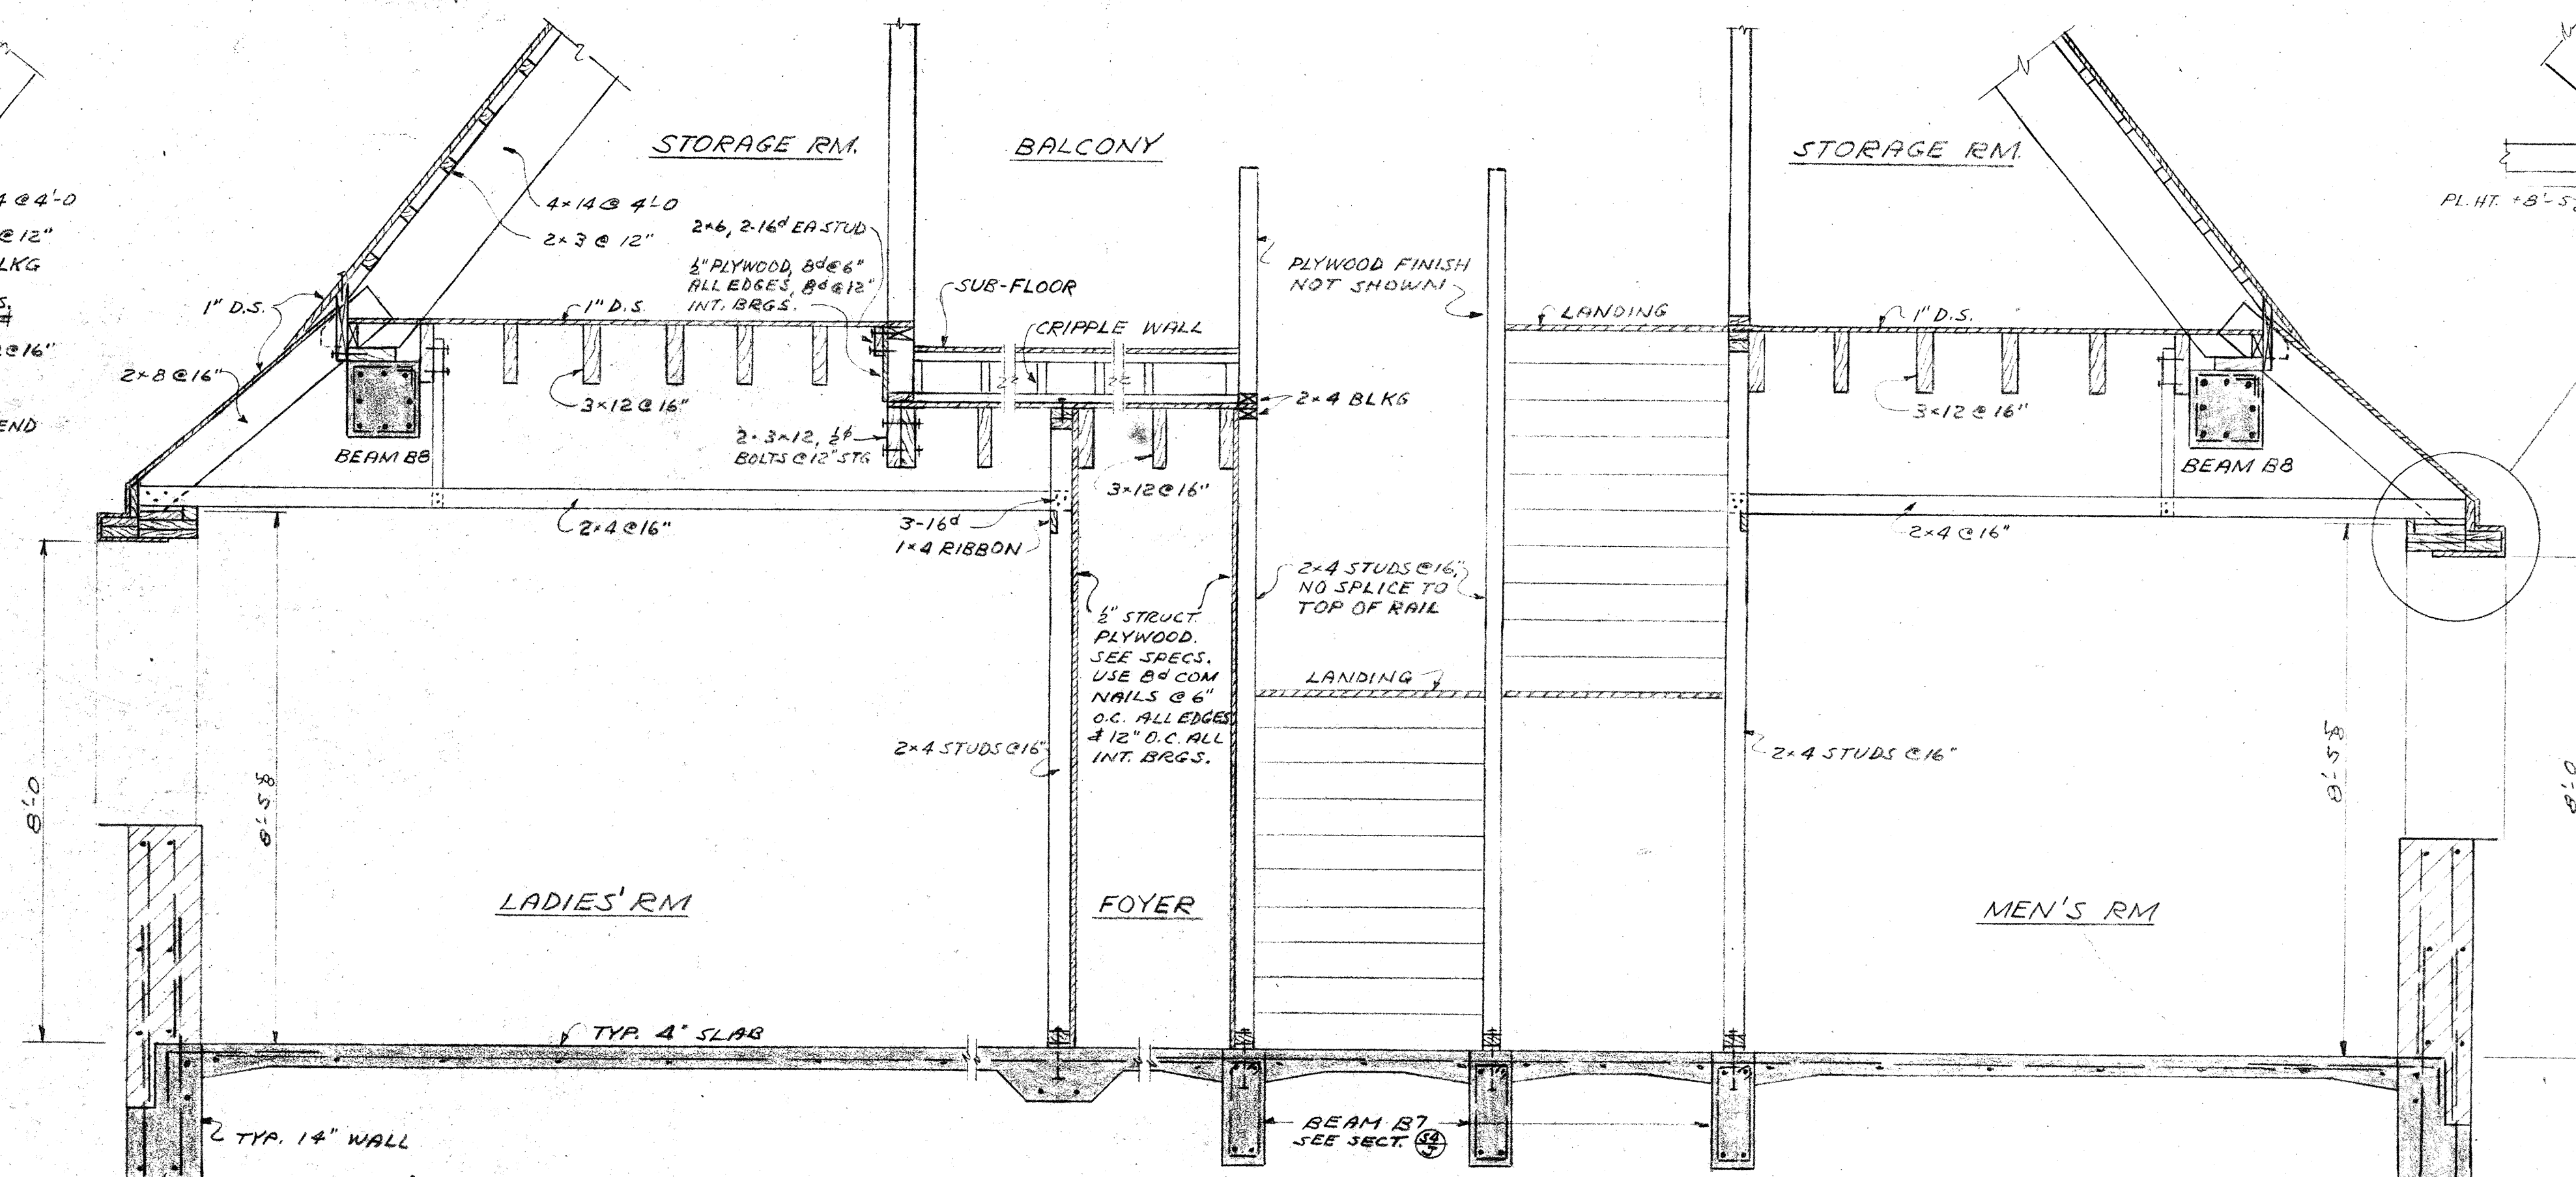


SECTION B
SCALE: 3/8"=1'-0"

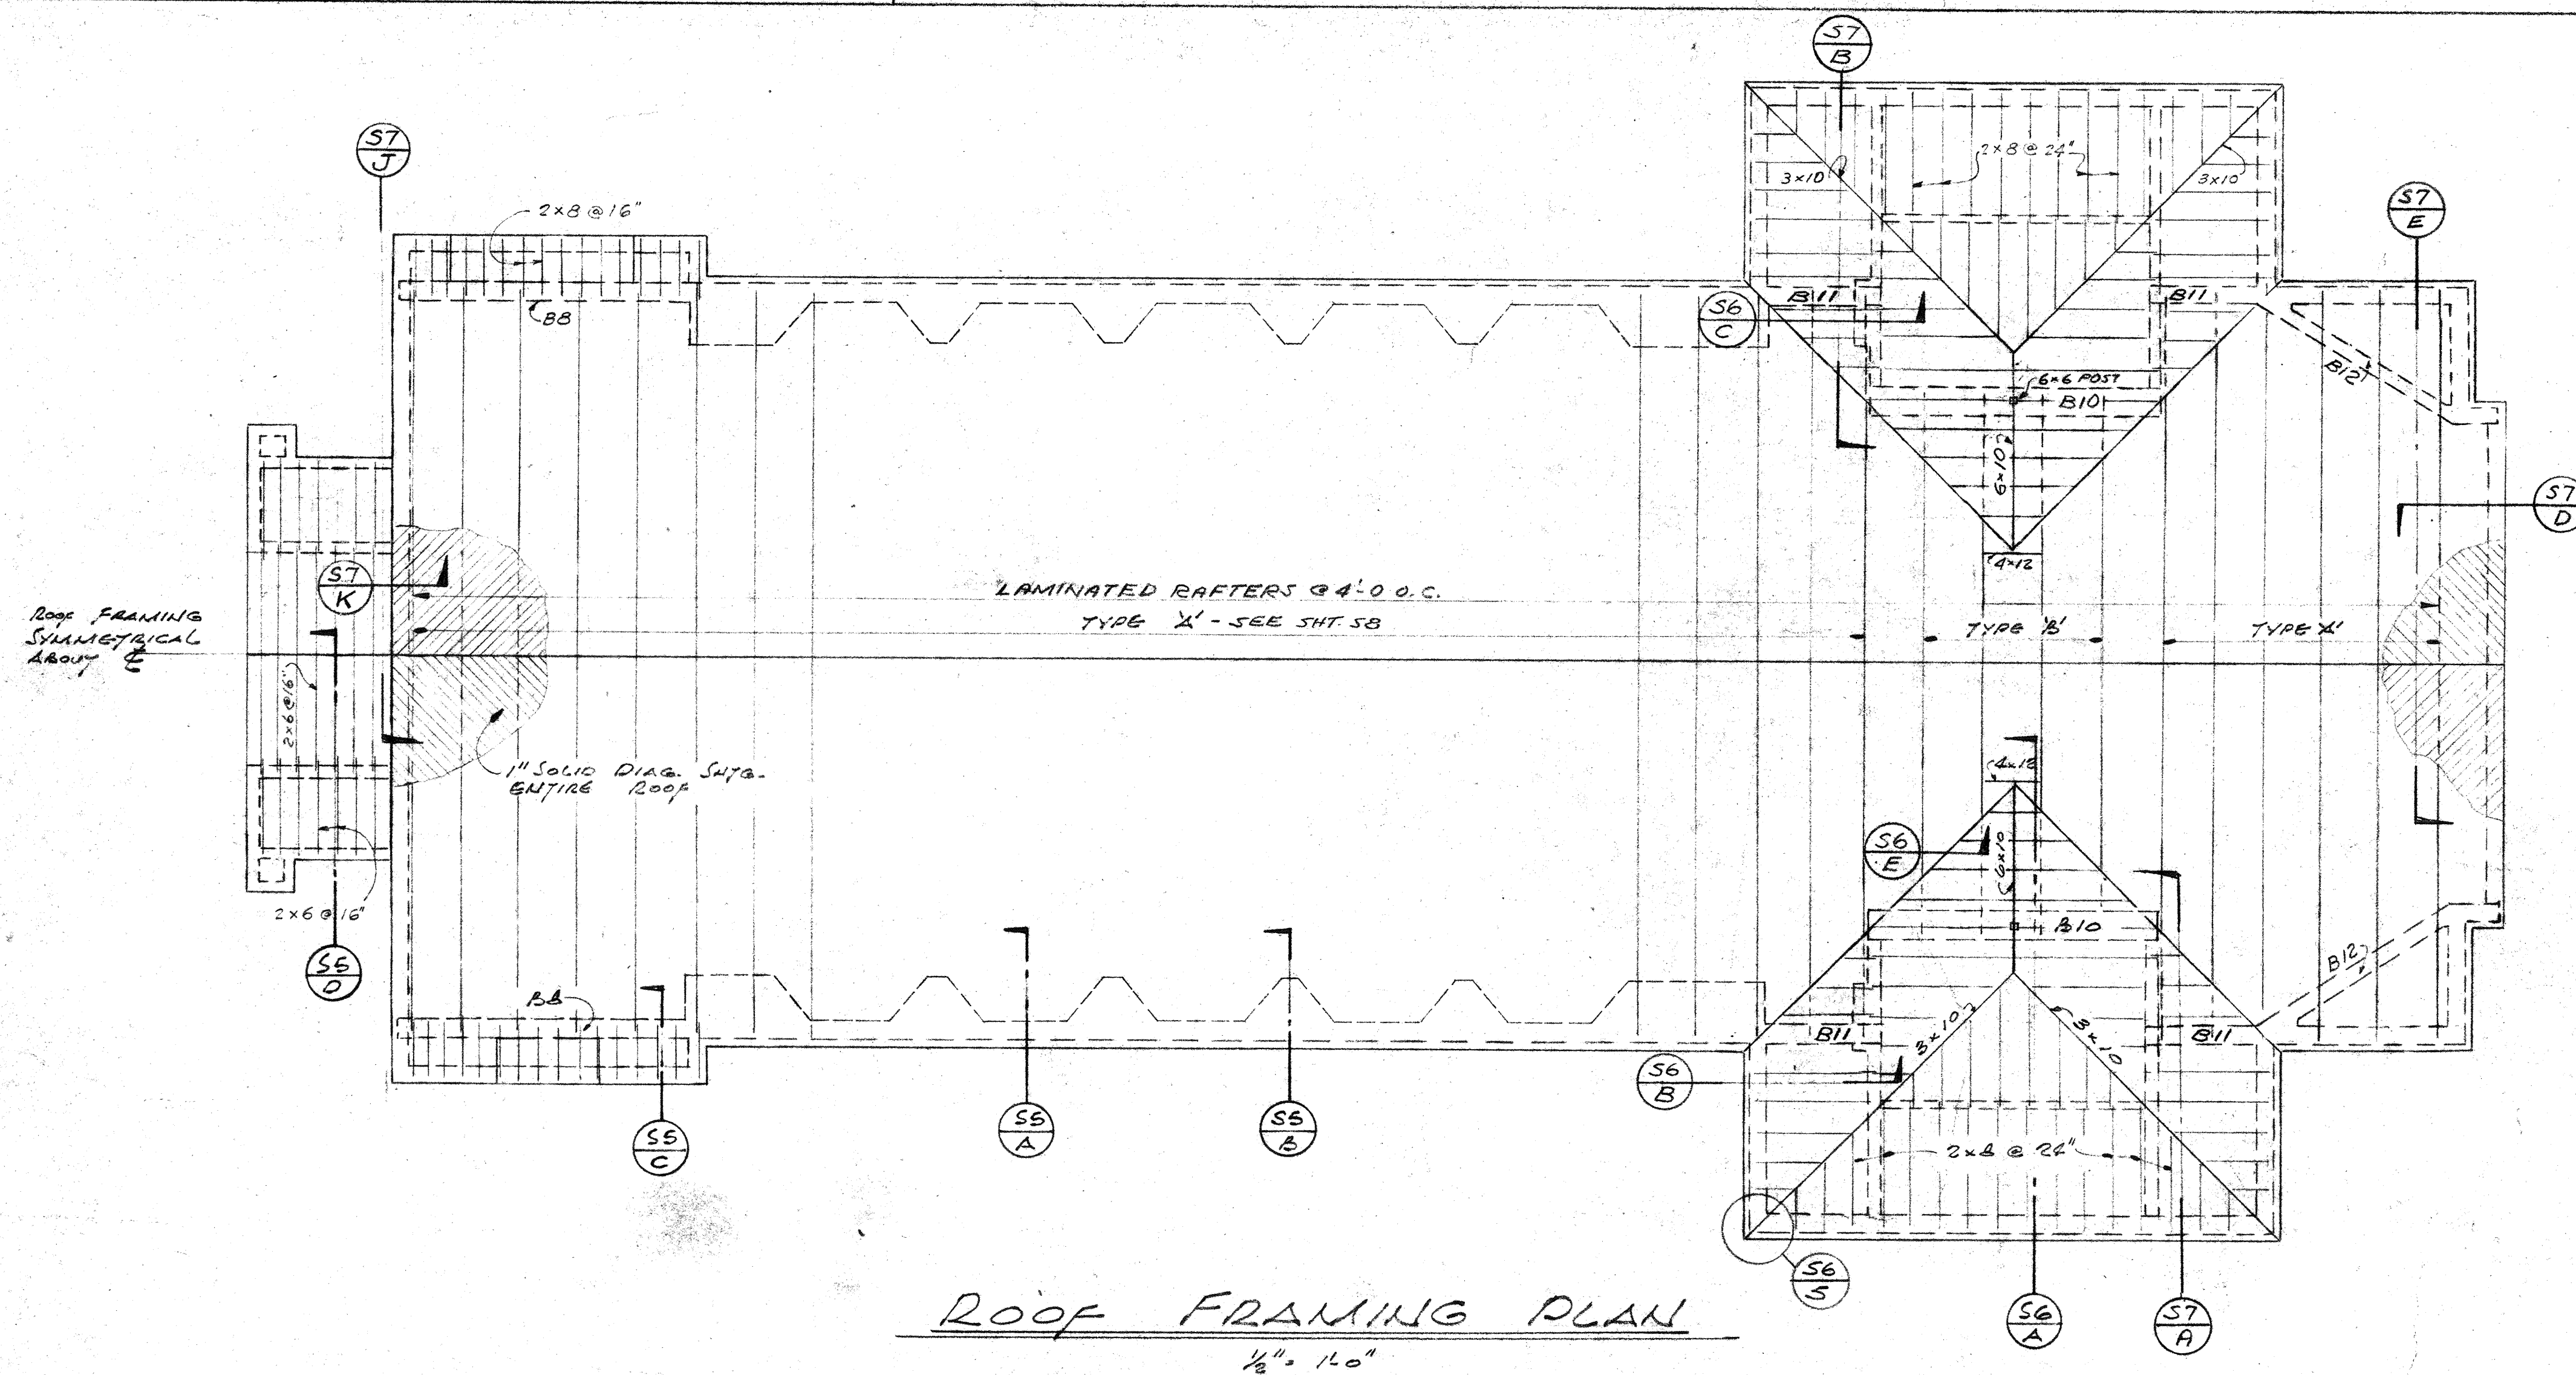


ROOF FRAMING PLAN
1/8"=1'-0"

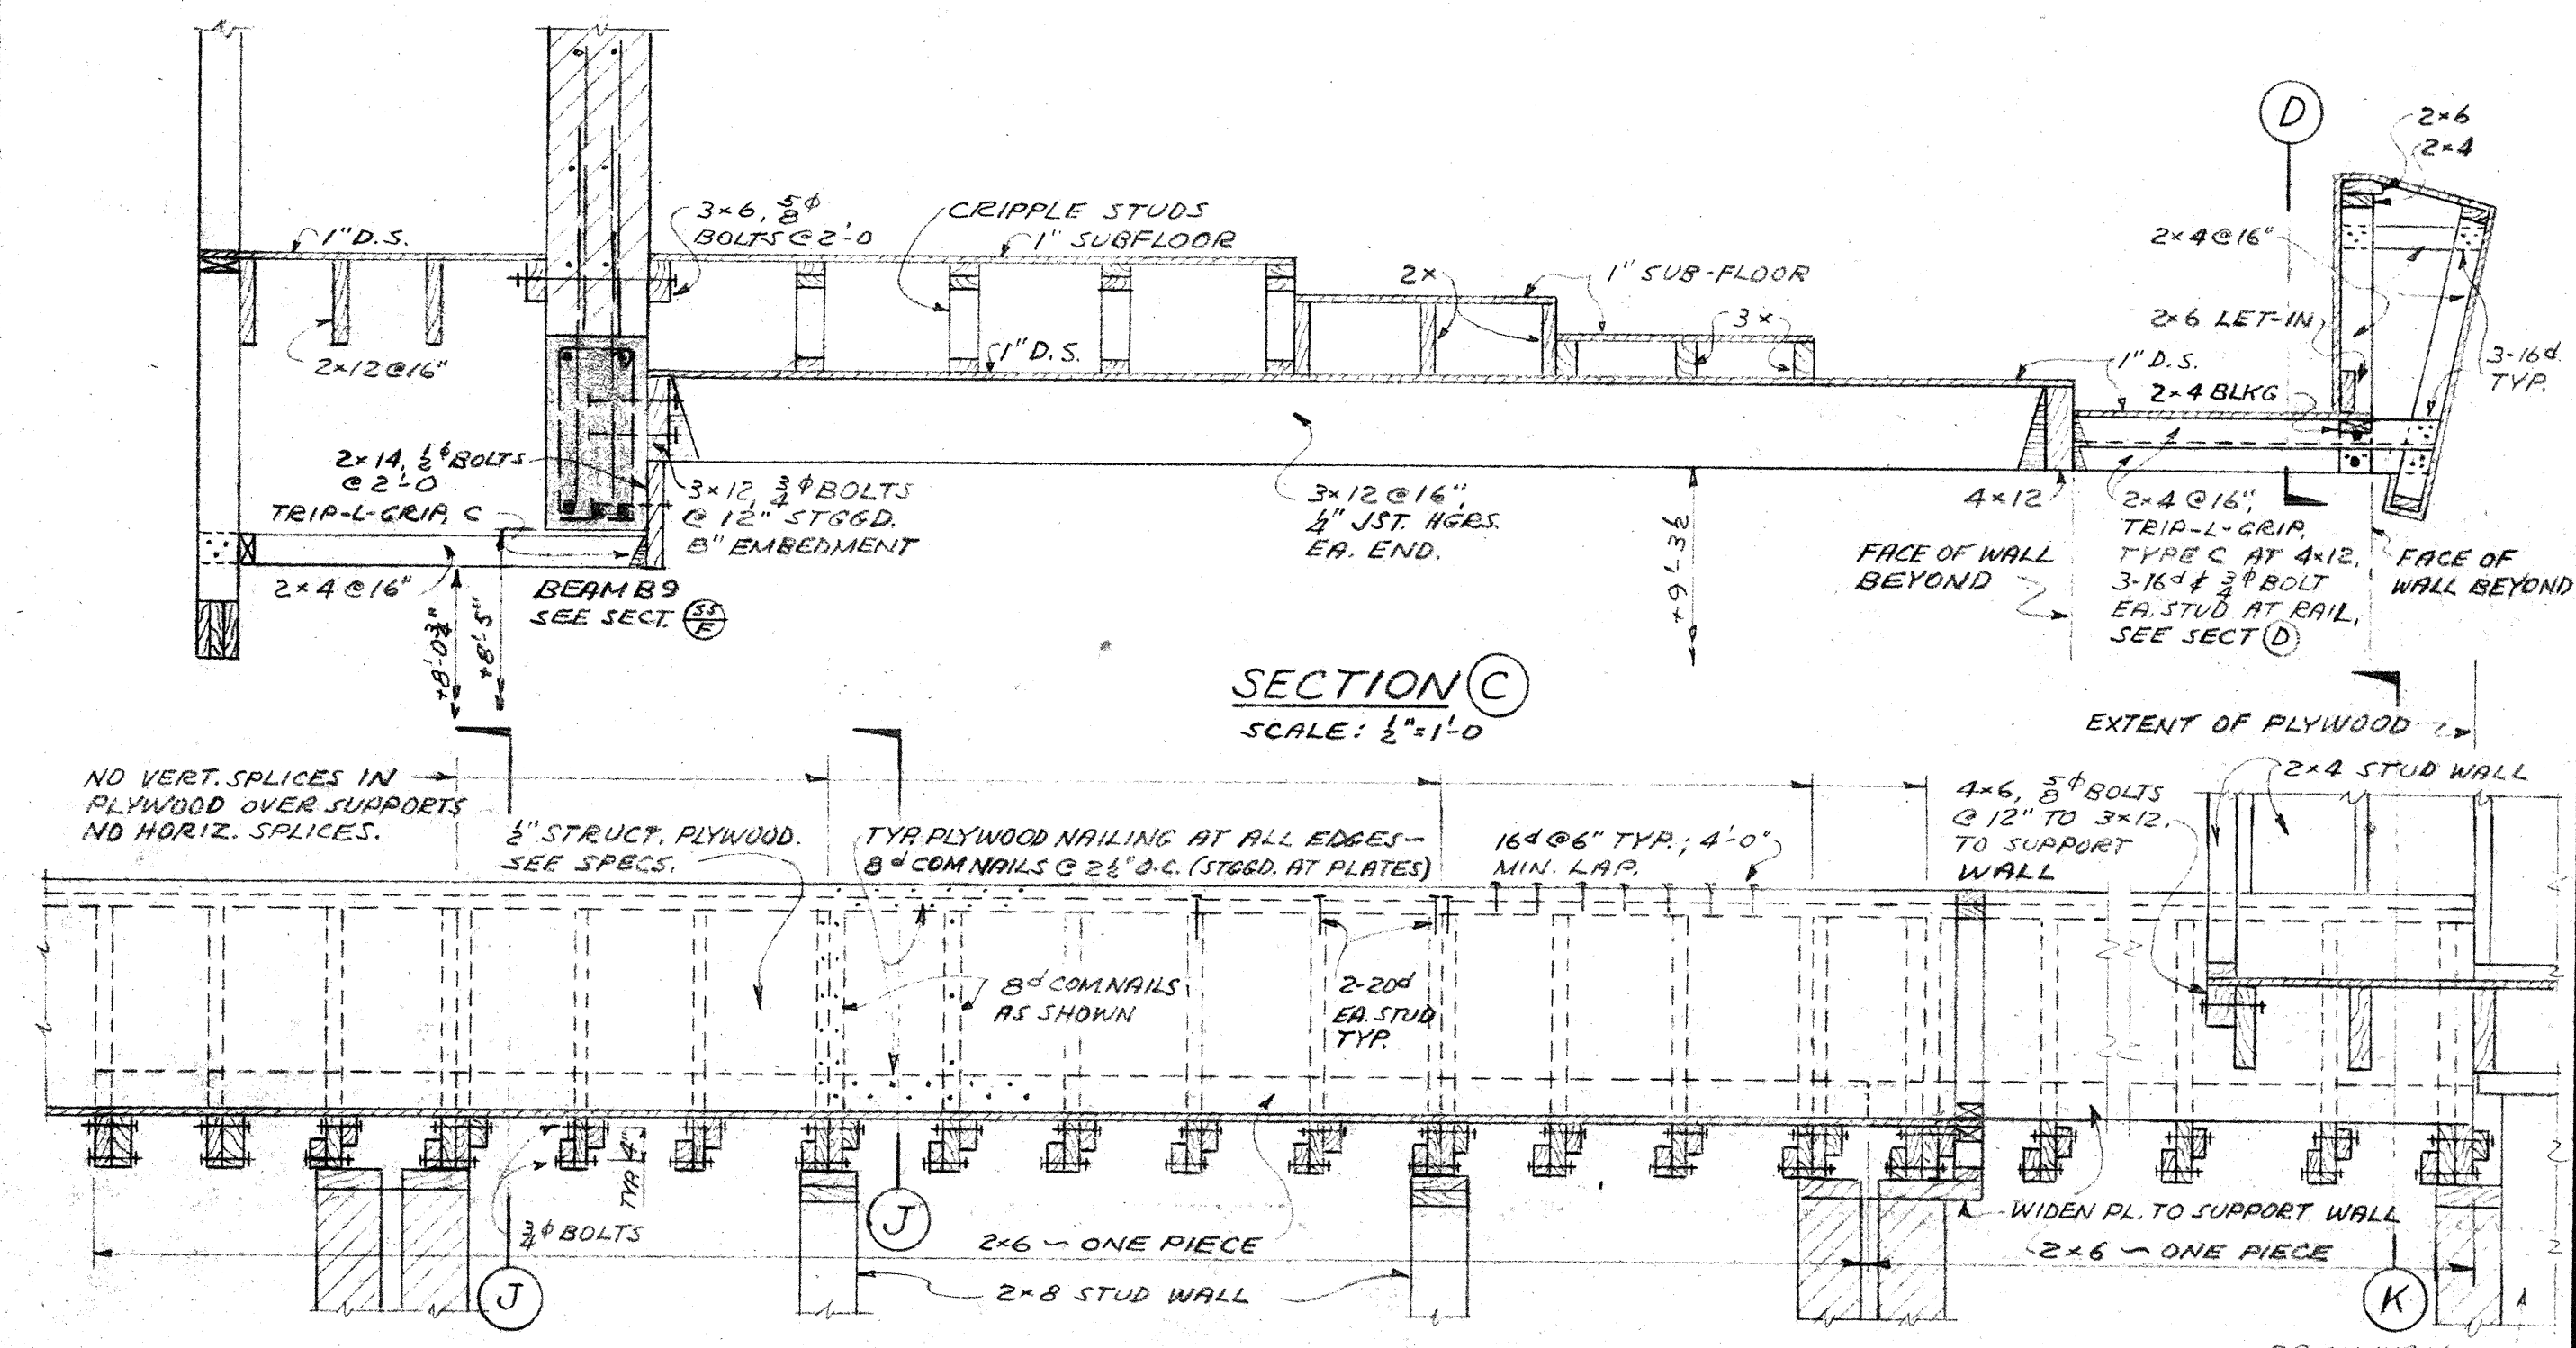

SECTION C
SCALE: 3/8"=1'-0"

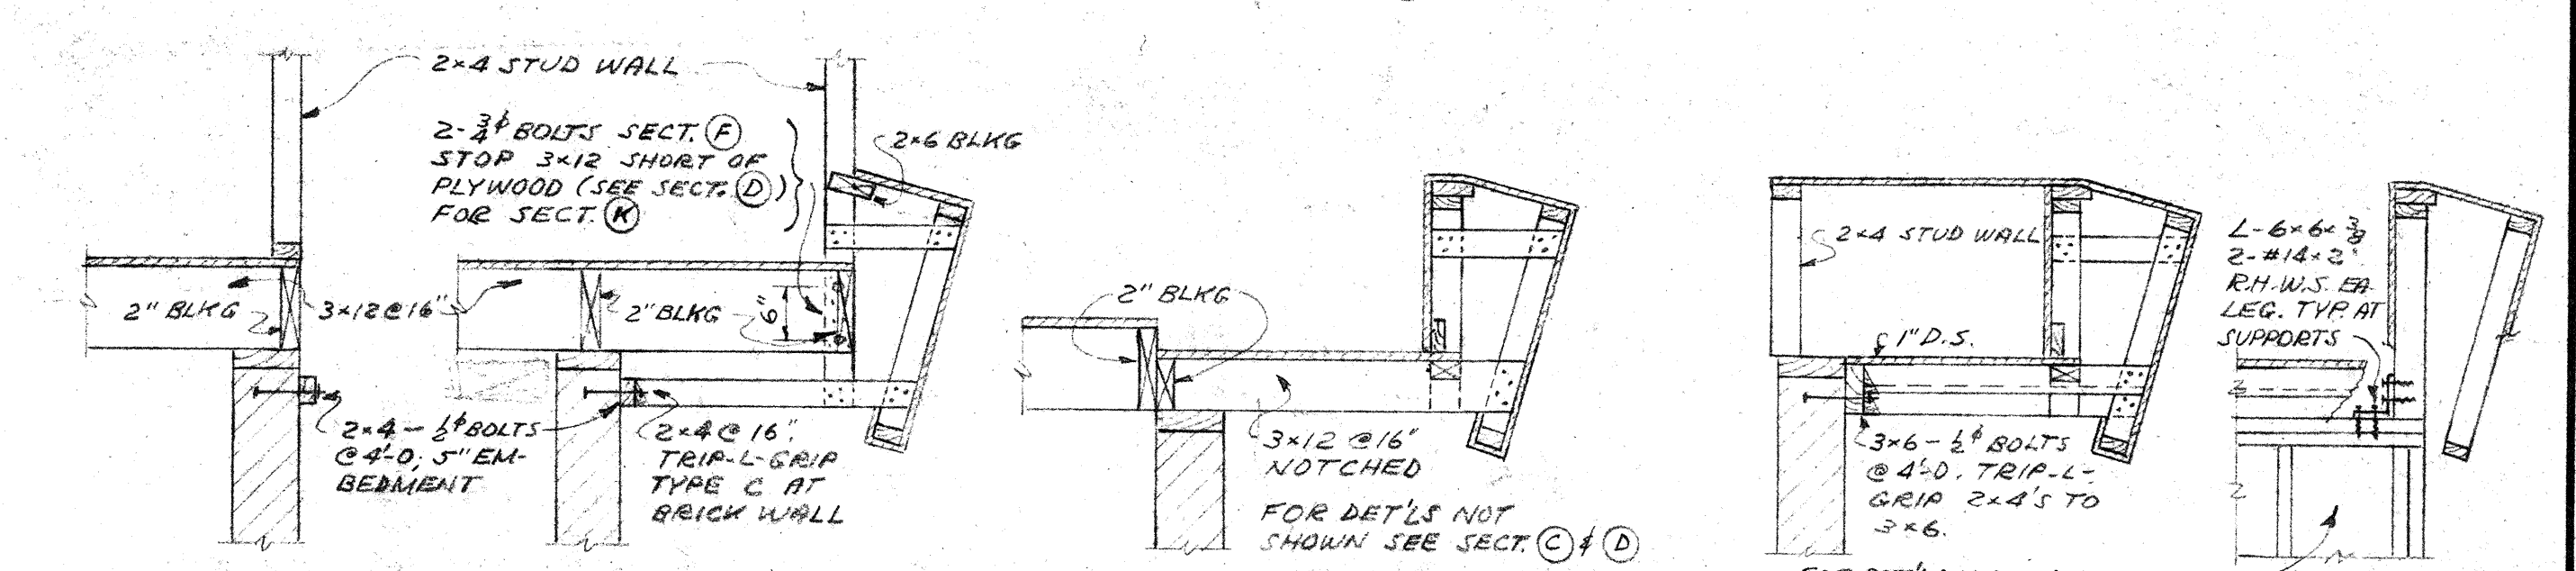

SECTION D
SCALE: 3/8"=1'-0"

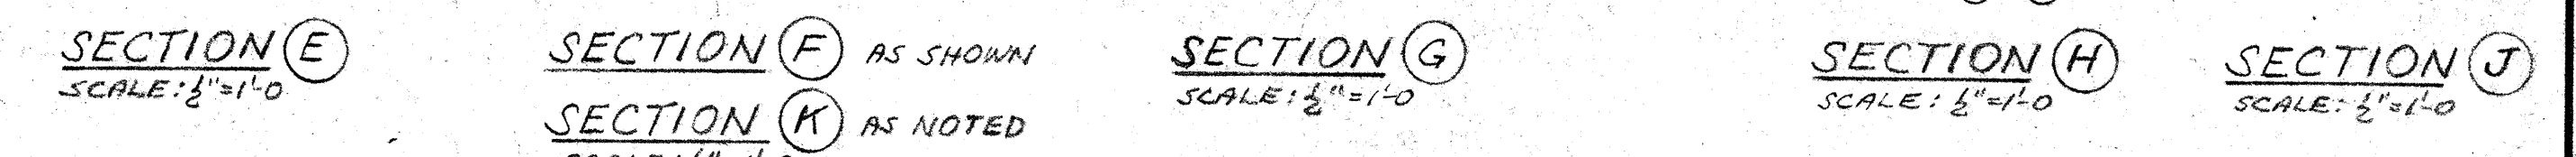

SECTION E SCALE: 1/2"=1'-0"
SECTION F AS SHOWN
SECTION G SCALE: 1/2"=1'-0"
SECTION H SCALE: 1/2"=1'-0"
SECTION J SCALE: 1/2"=1'-0"

Remarks

Revisions

Engineers

Approvals

AUSTIN FIELD & IRY
architects
2311 WEST THIRD STREET • LOS ANGELES 5, CALIFORNIA • DUNKIRK 8-1326

ROOF & BALCONY FRAMING PLANS - BALCONY SECTIONS
ST. EDMUND'S EPISCOPAL CHURCH
SAN MARINO, CALIF.

100-AUG-51
1061
SHEET NUMBER
53