

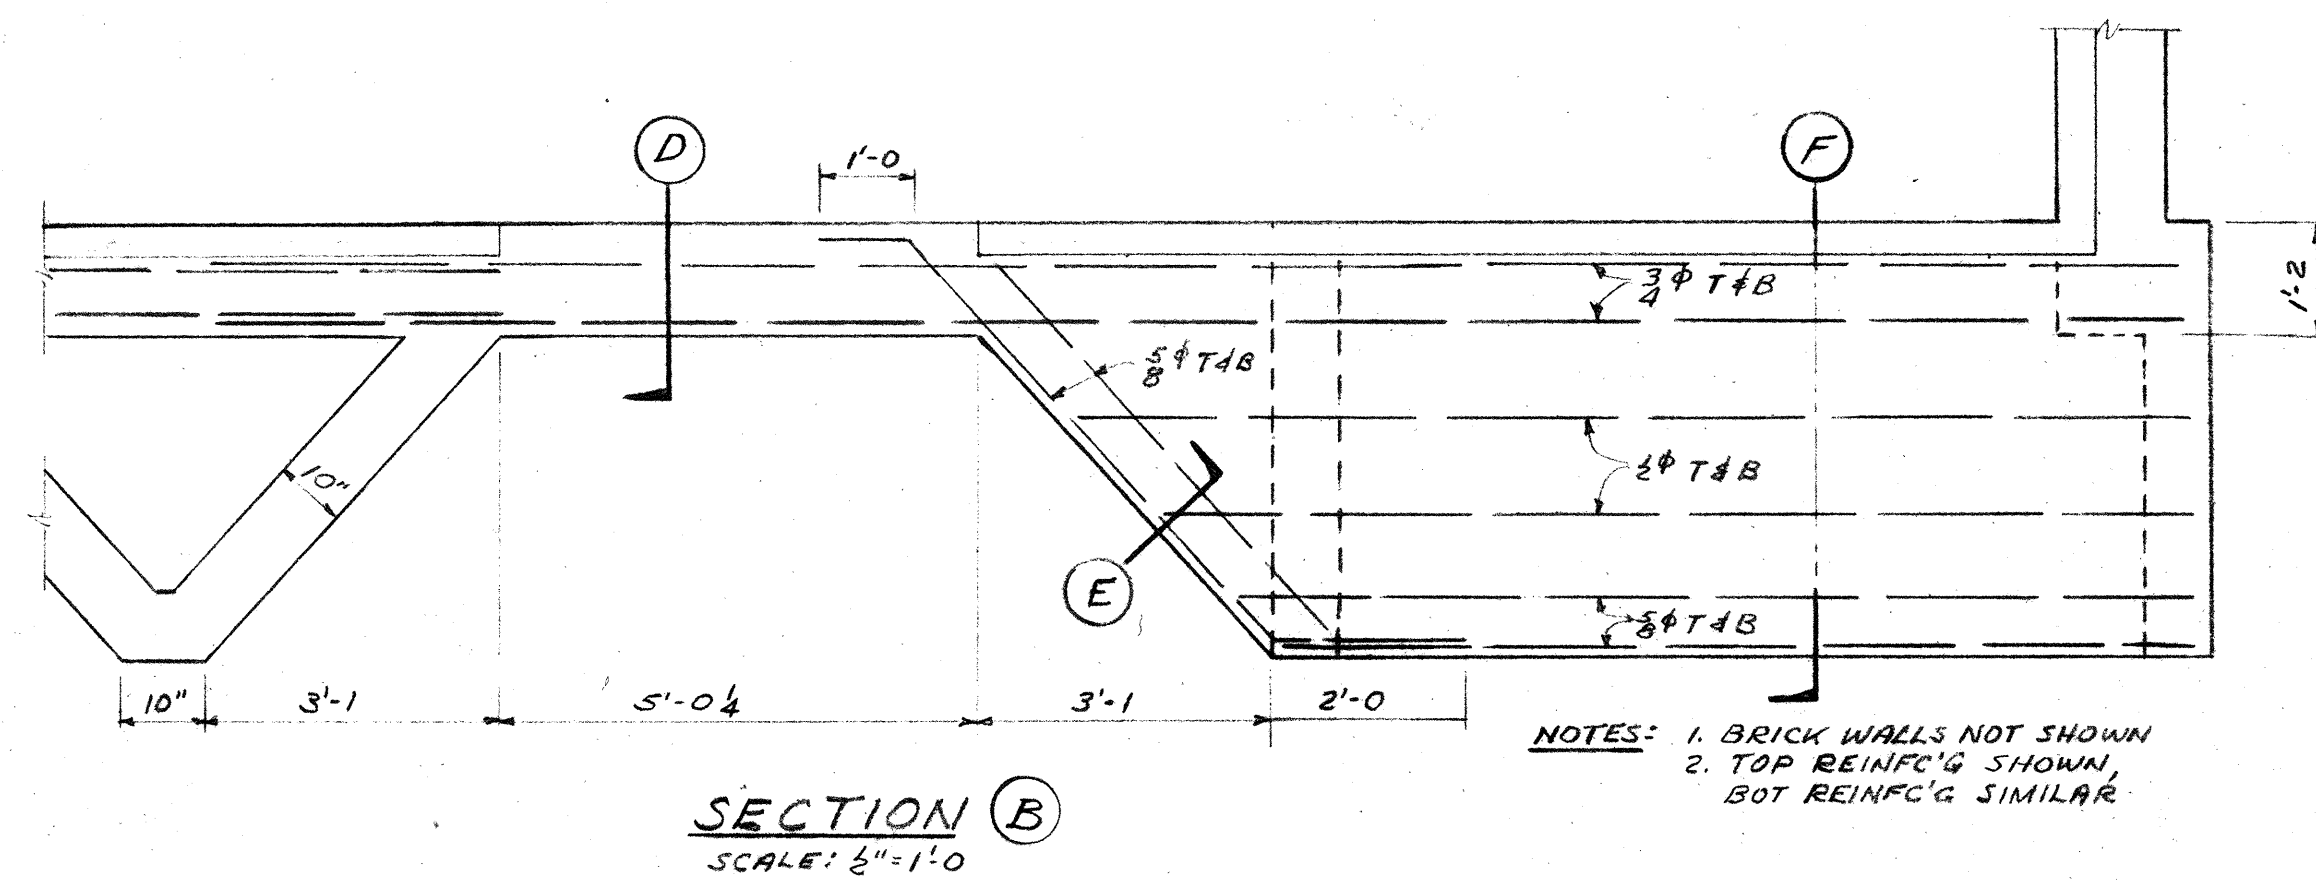
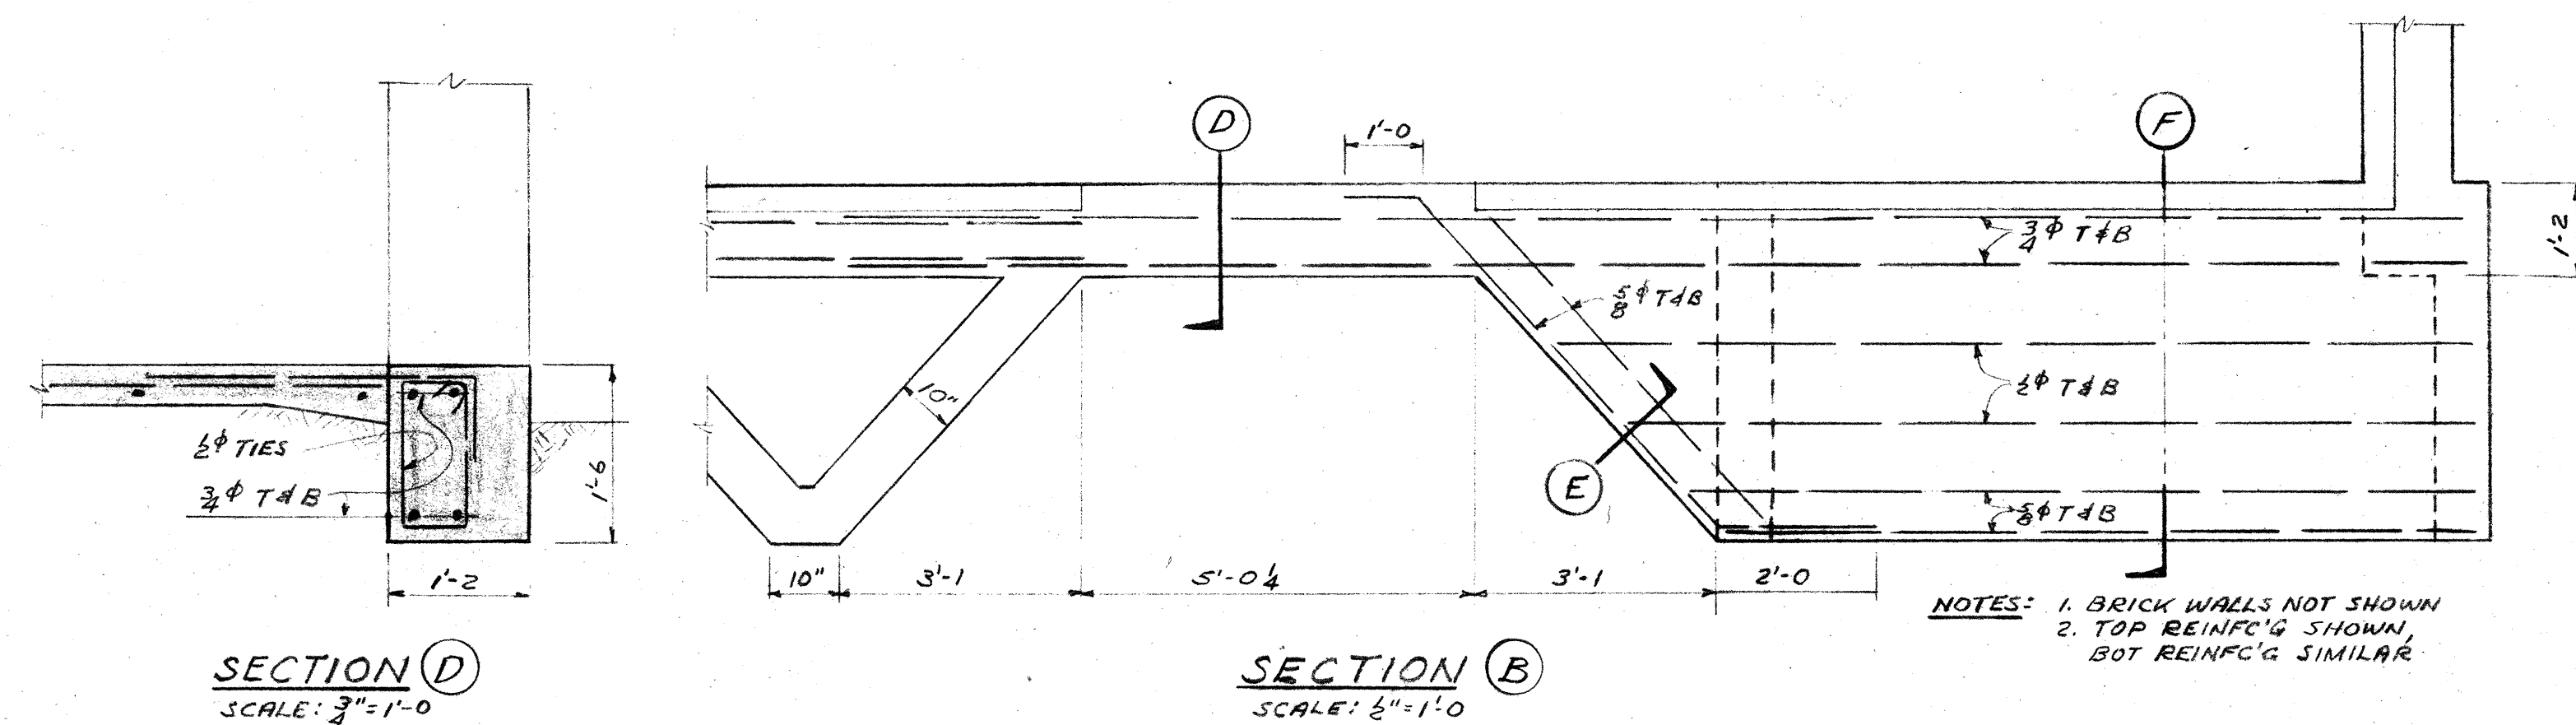
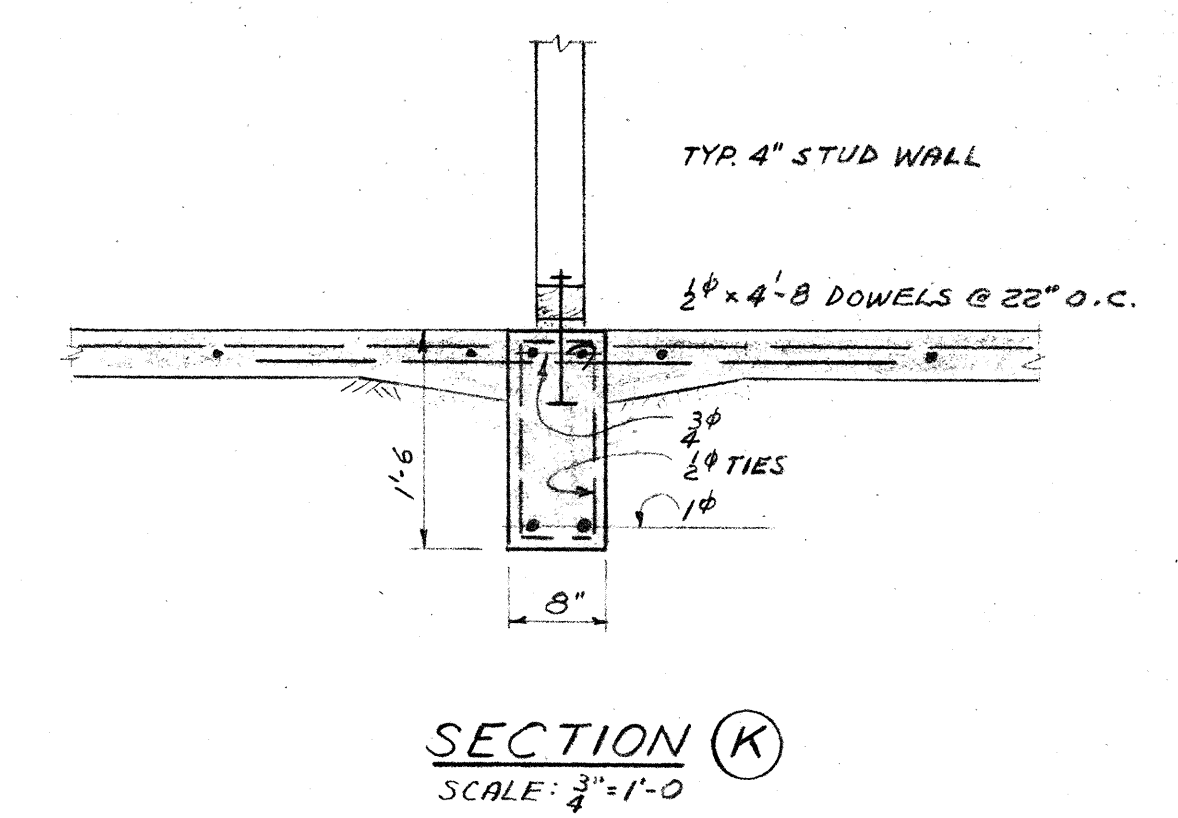
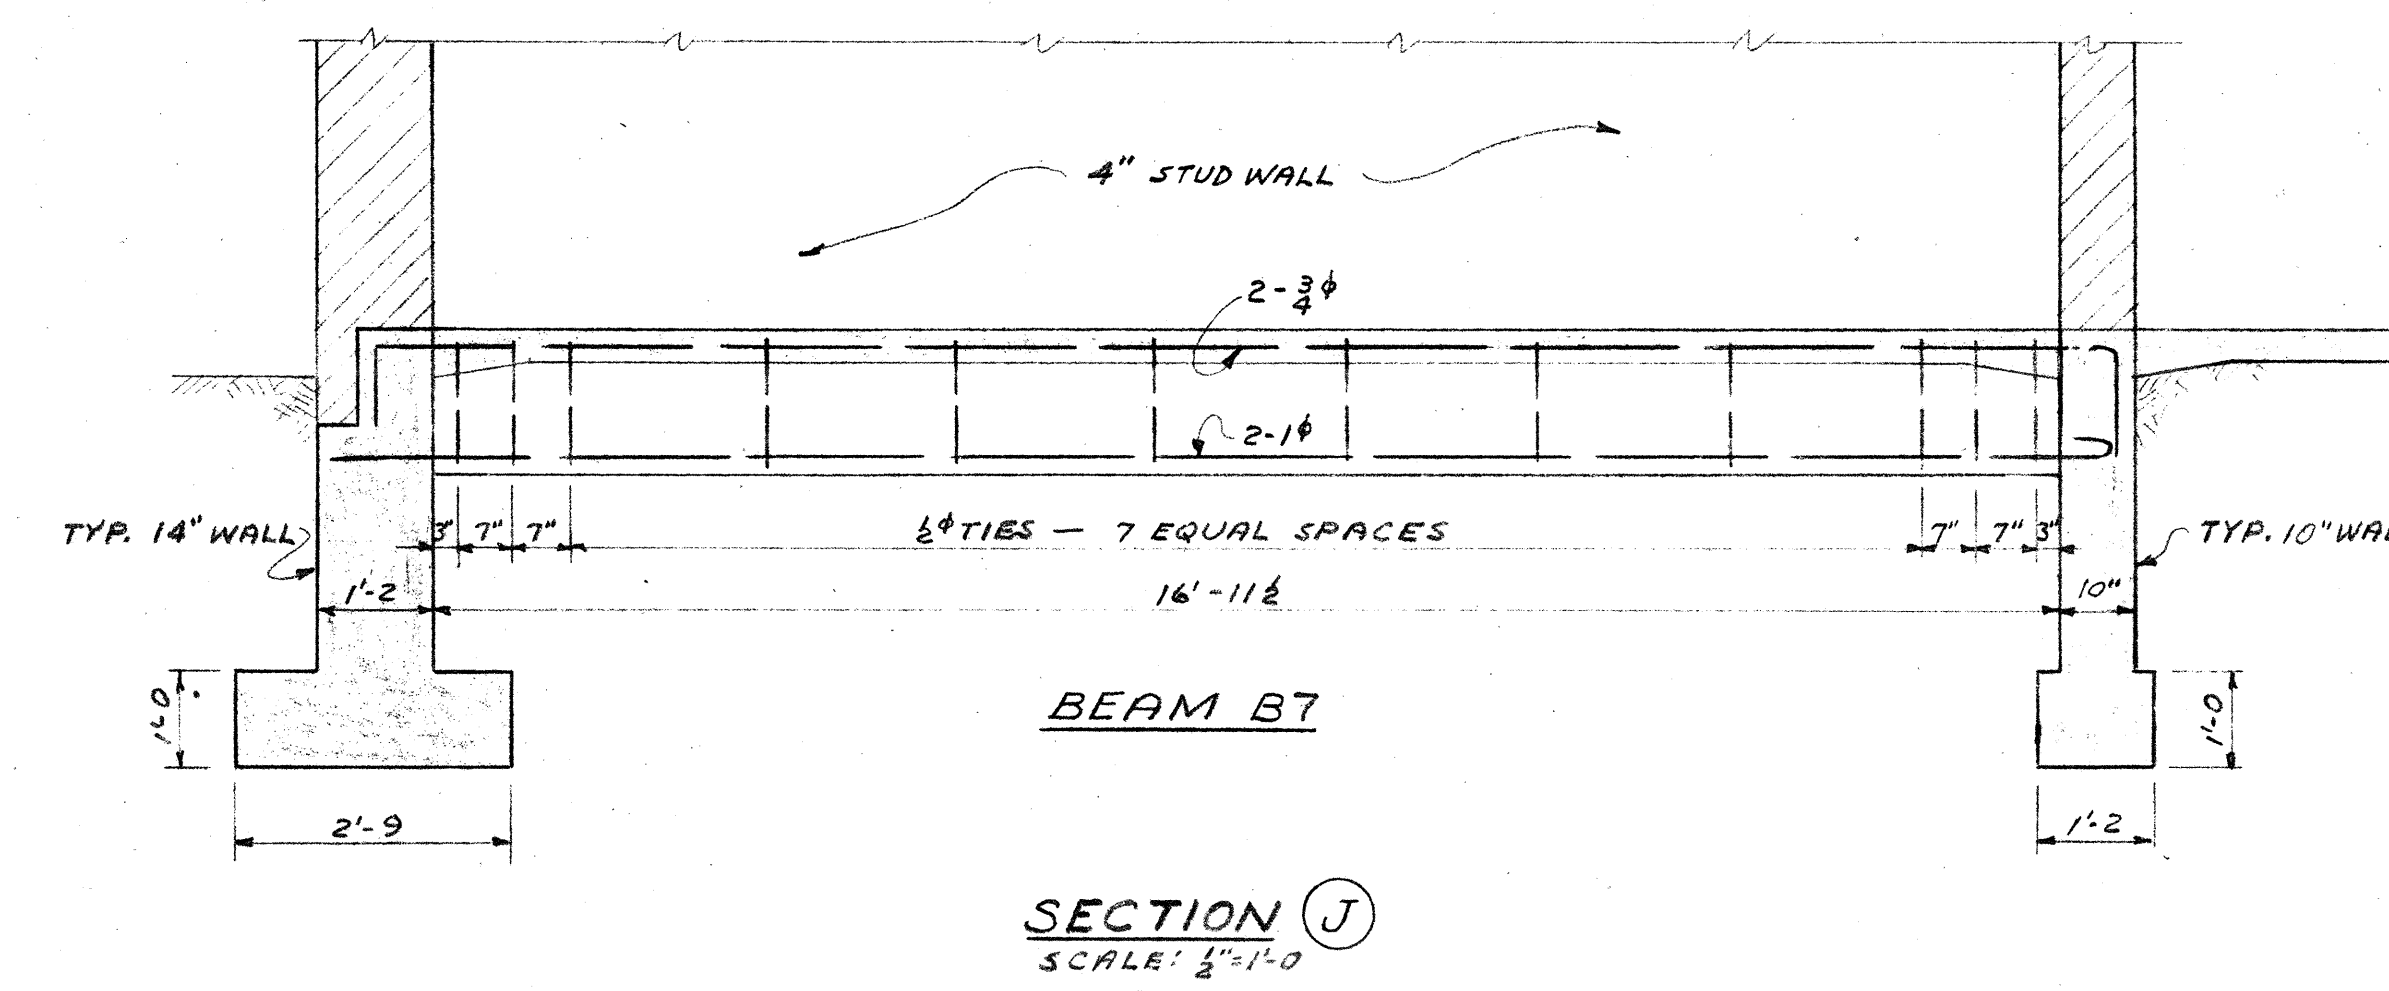
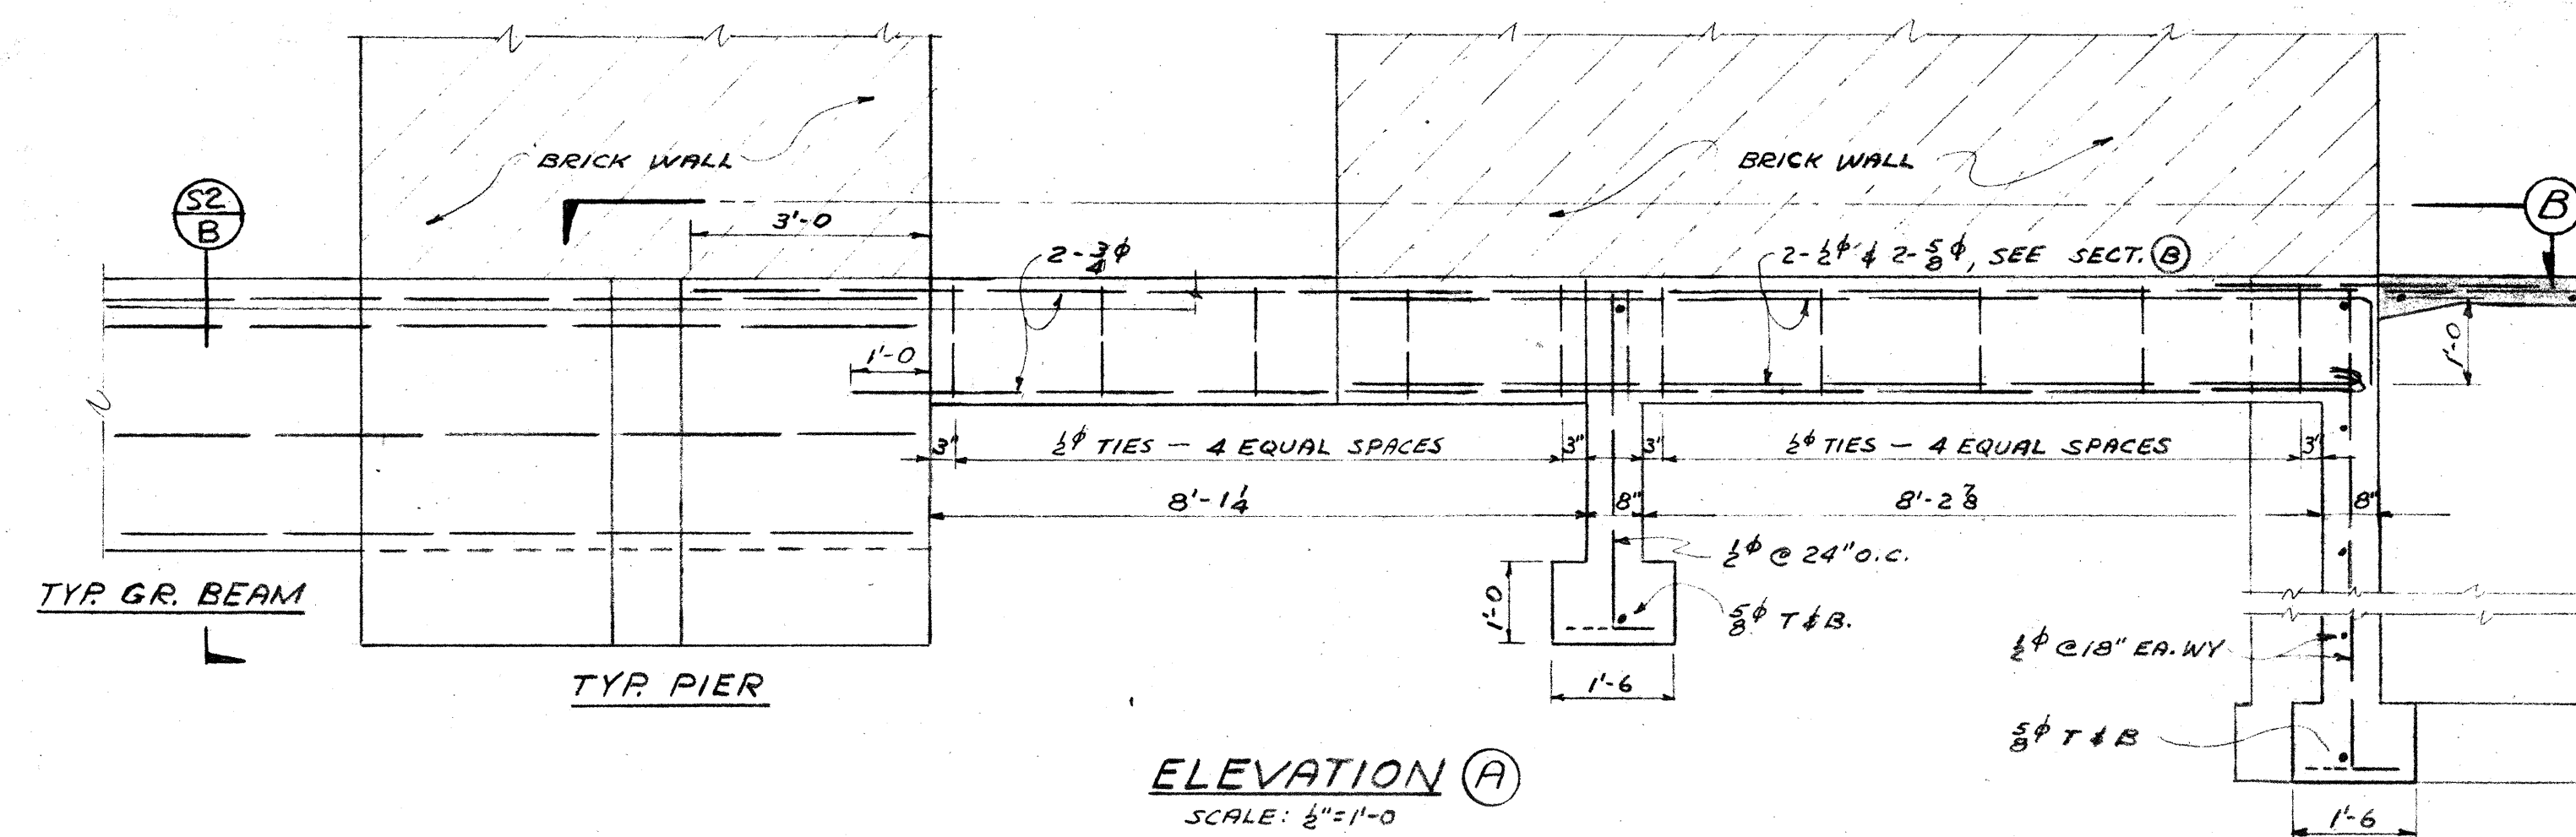
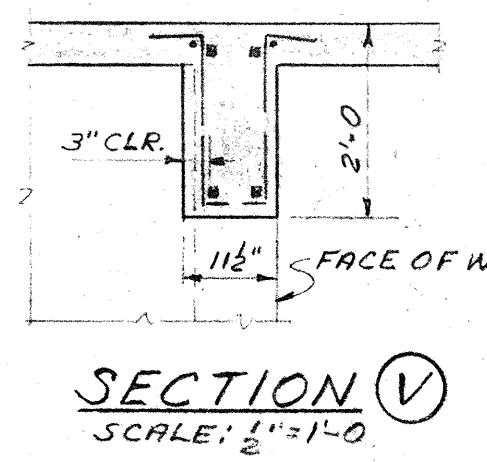
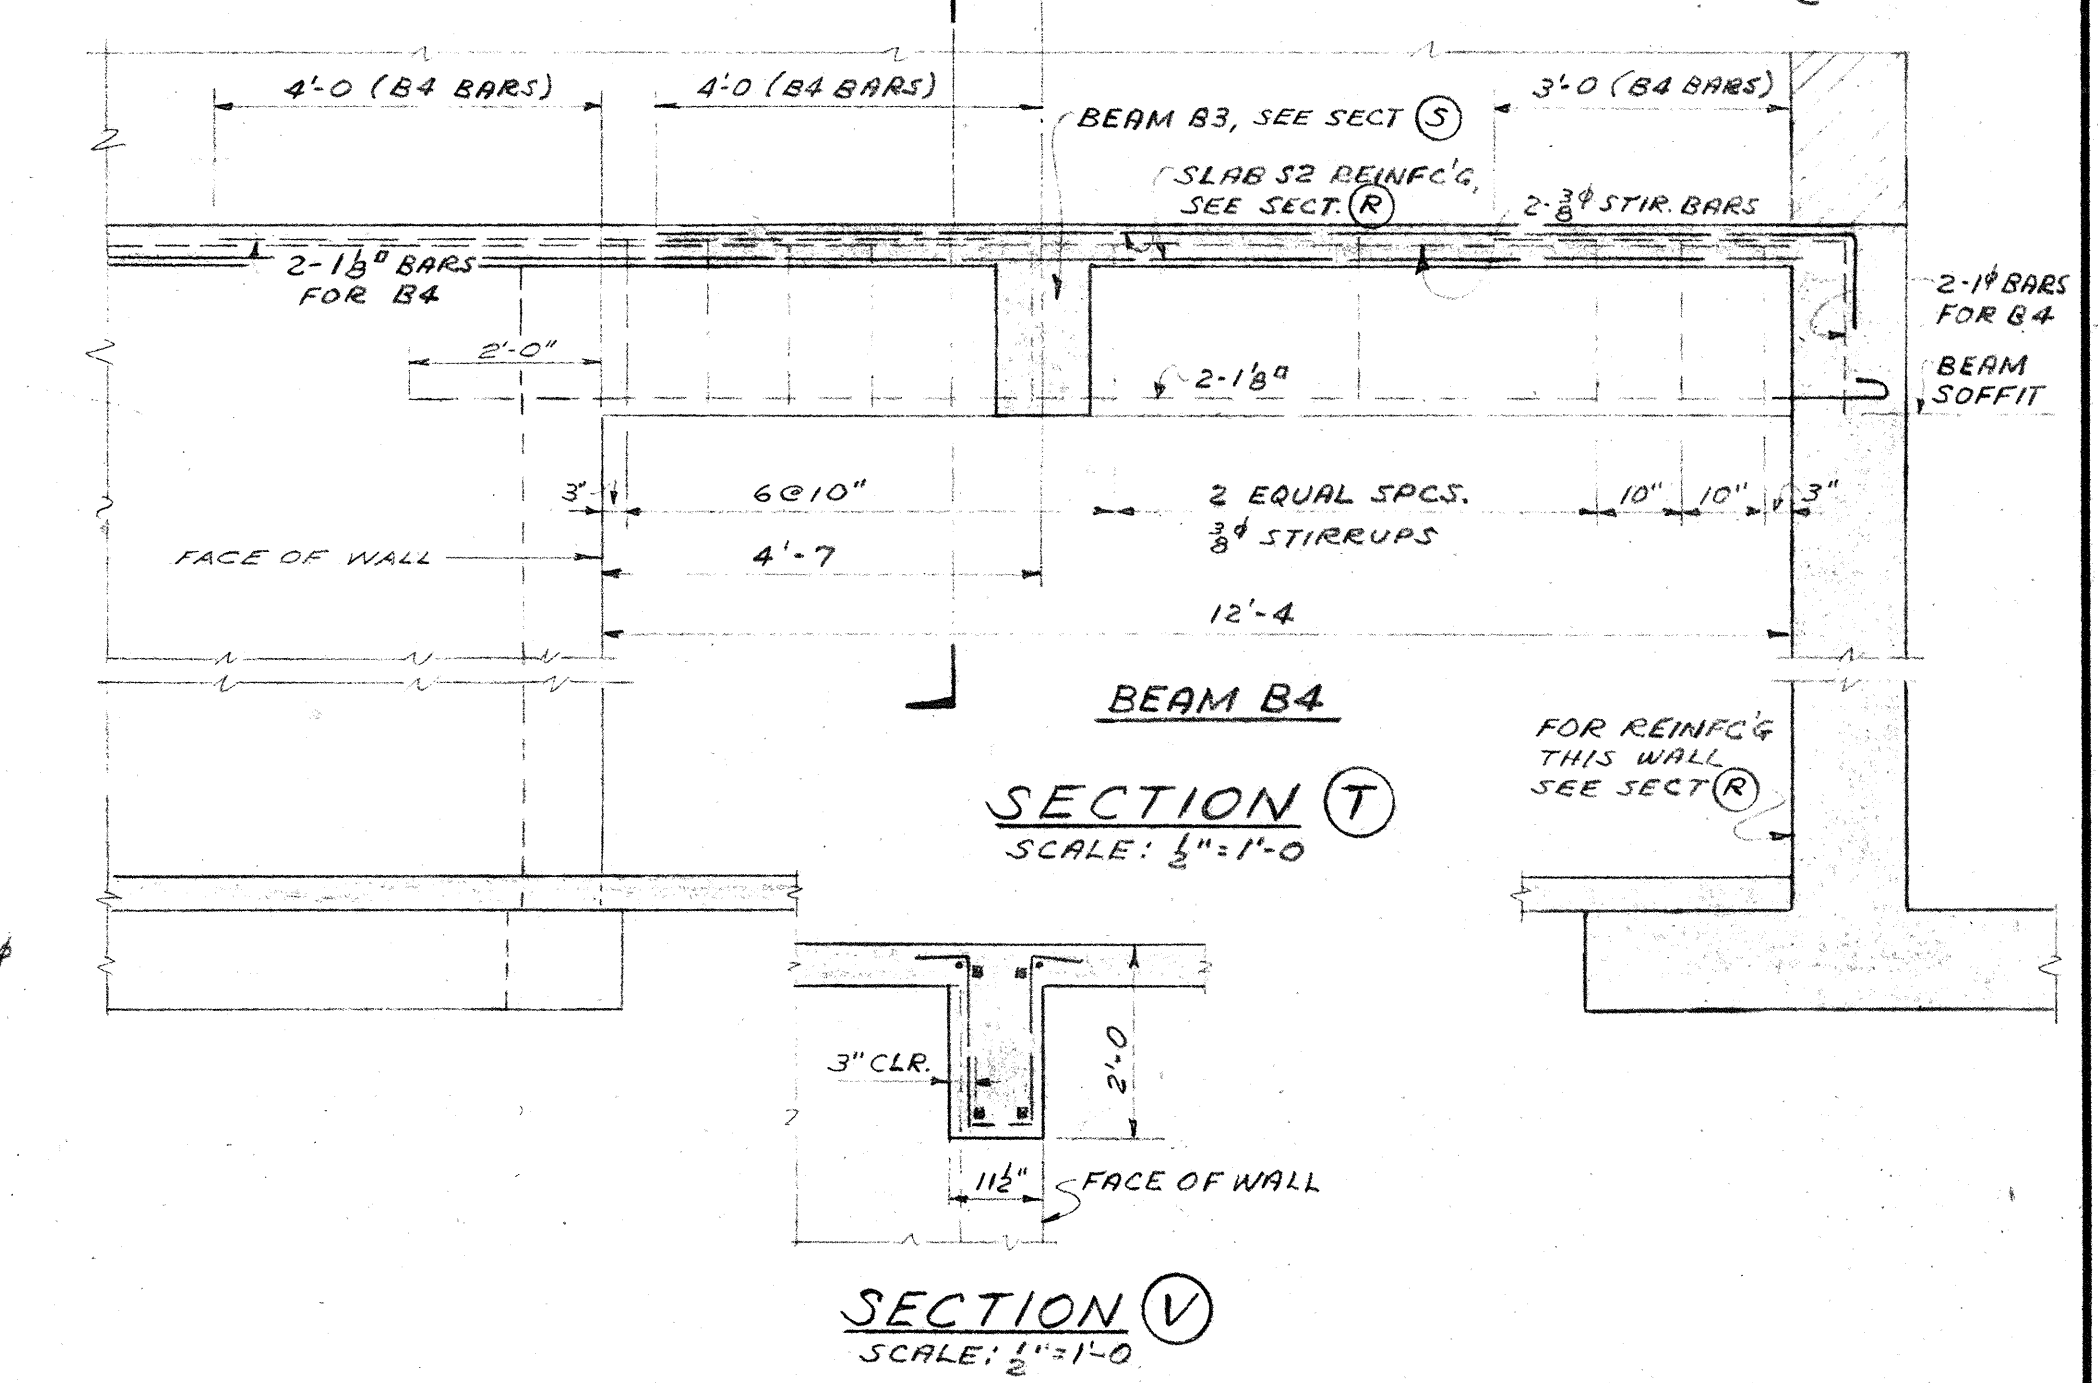
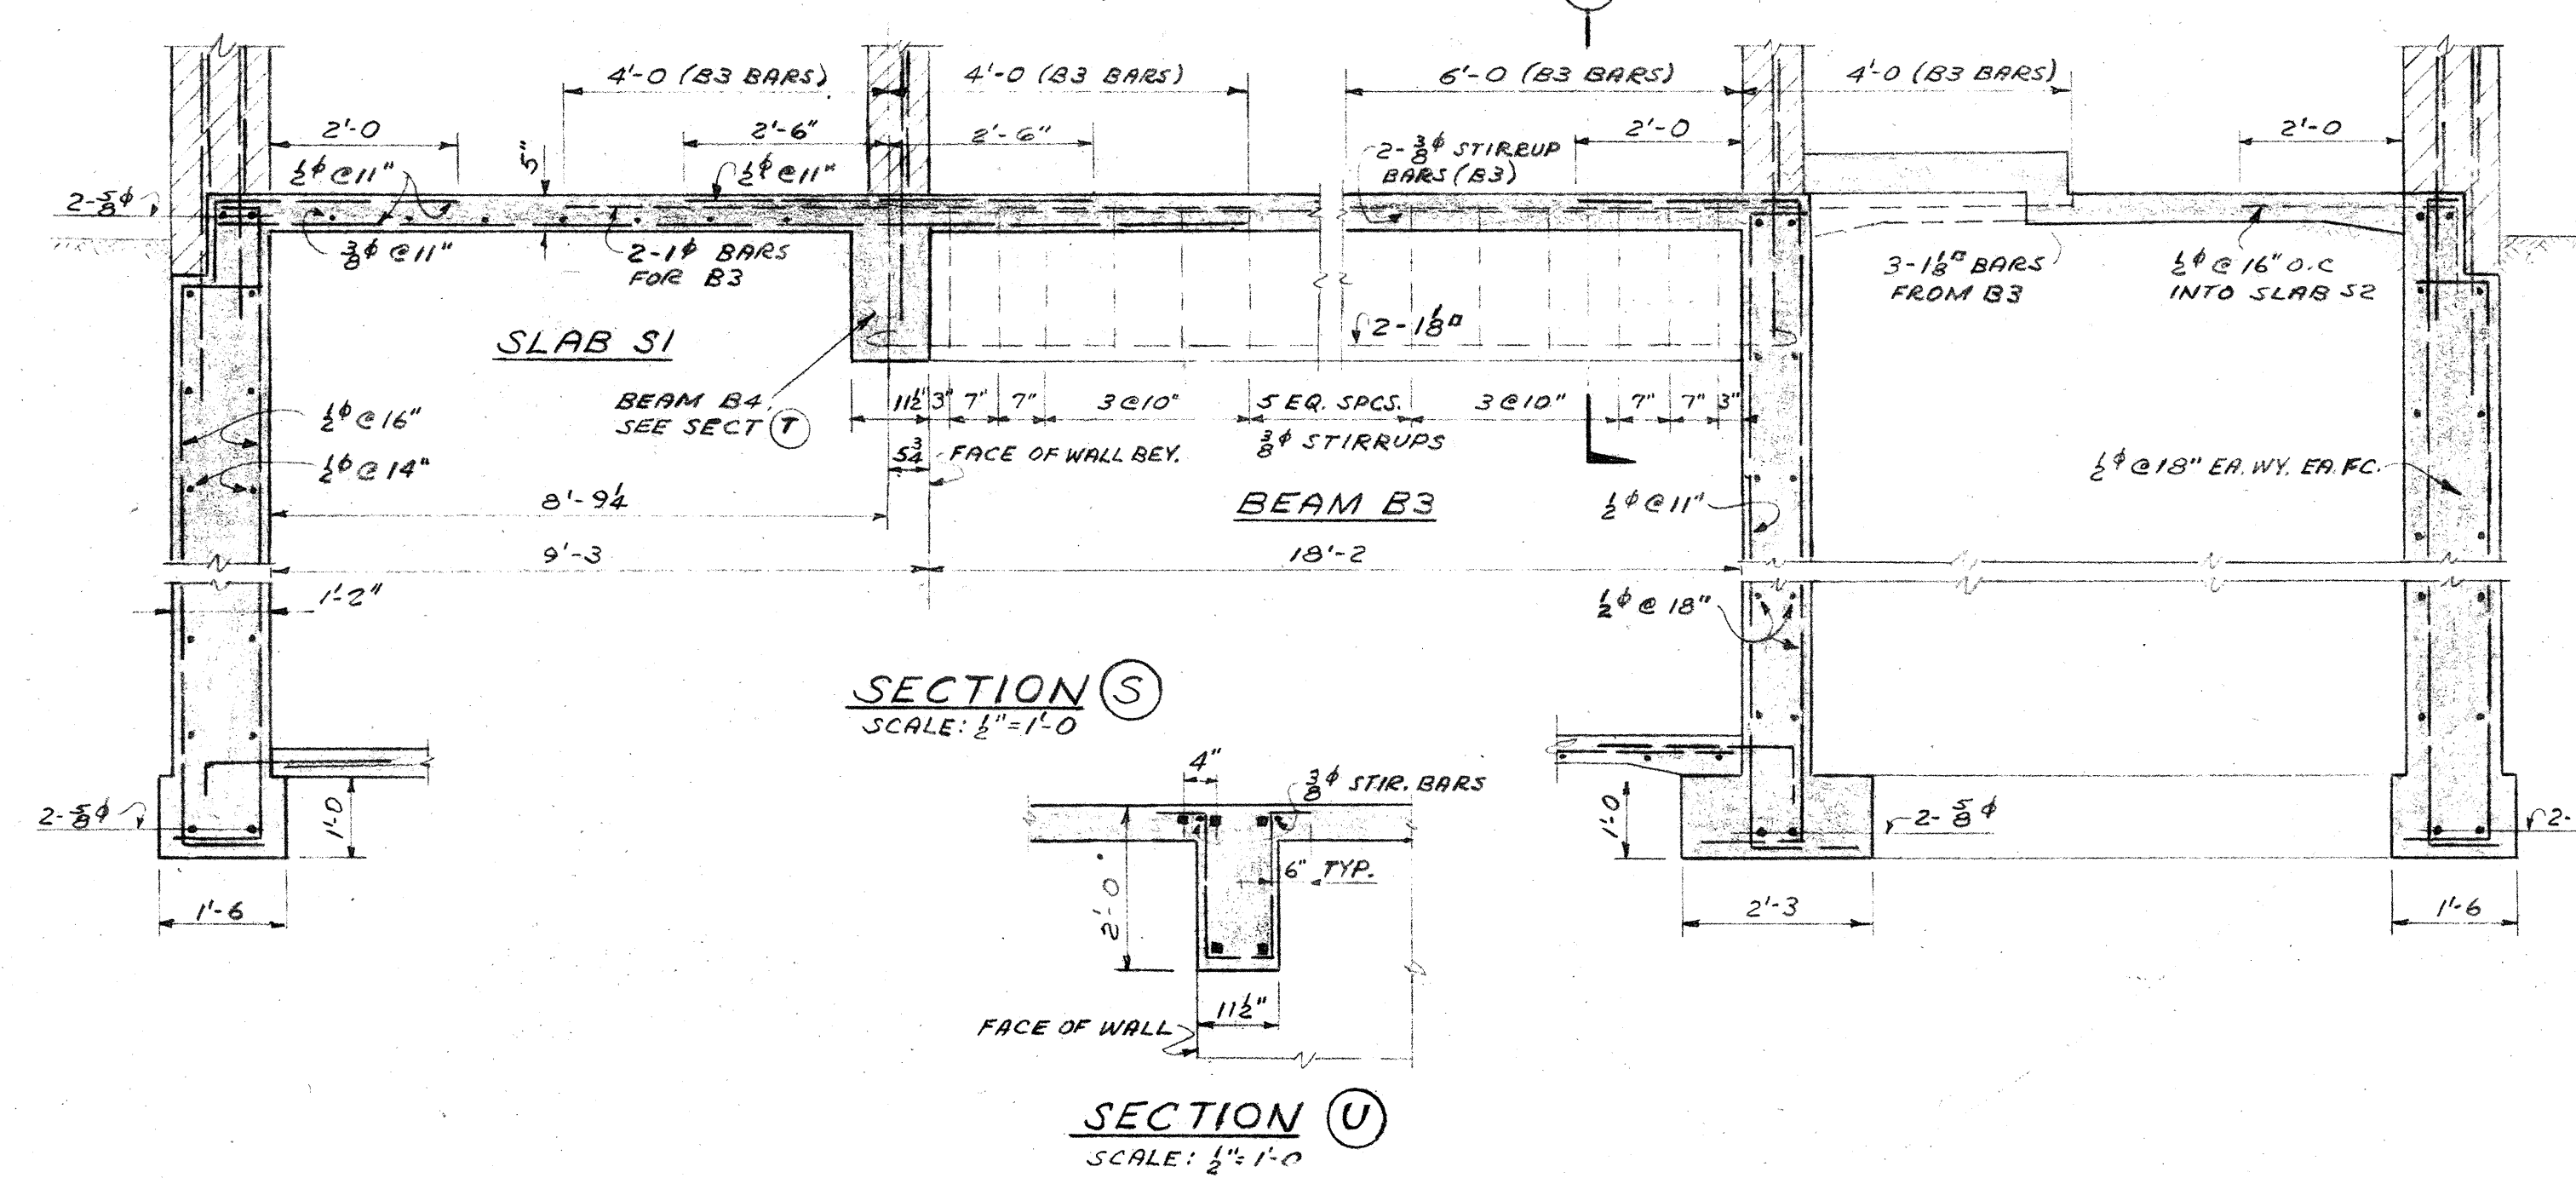
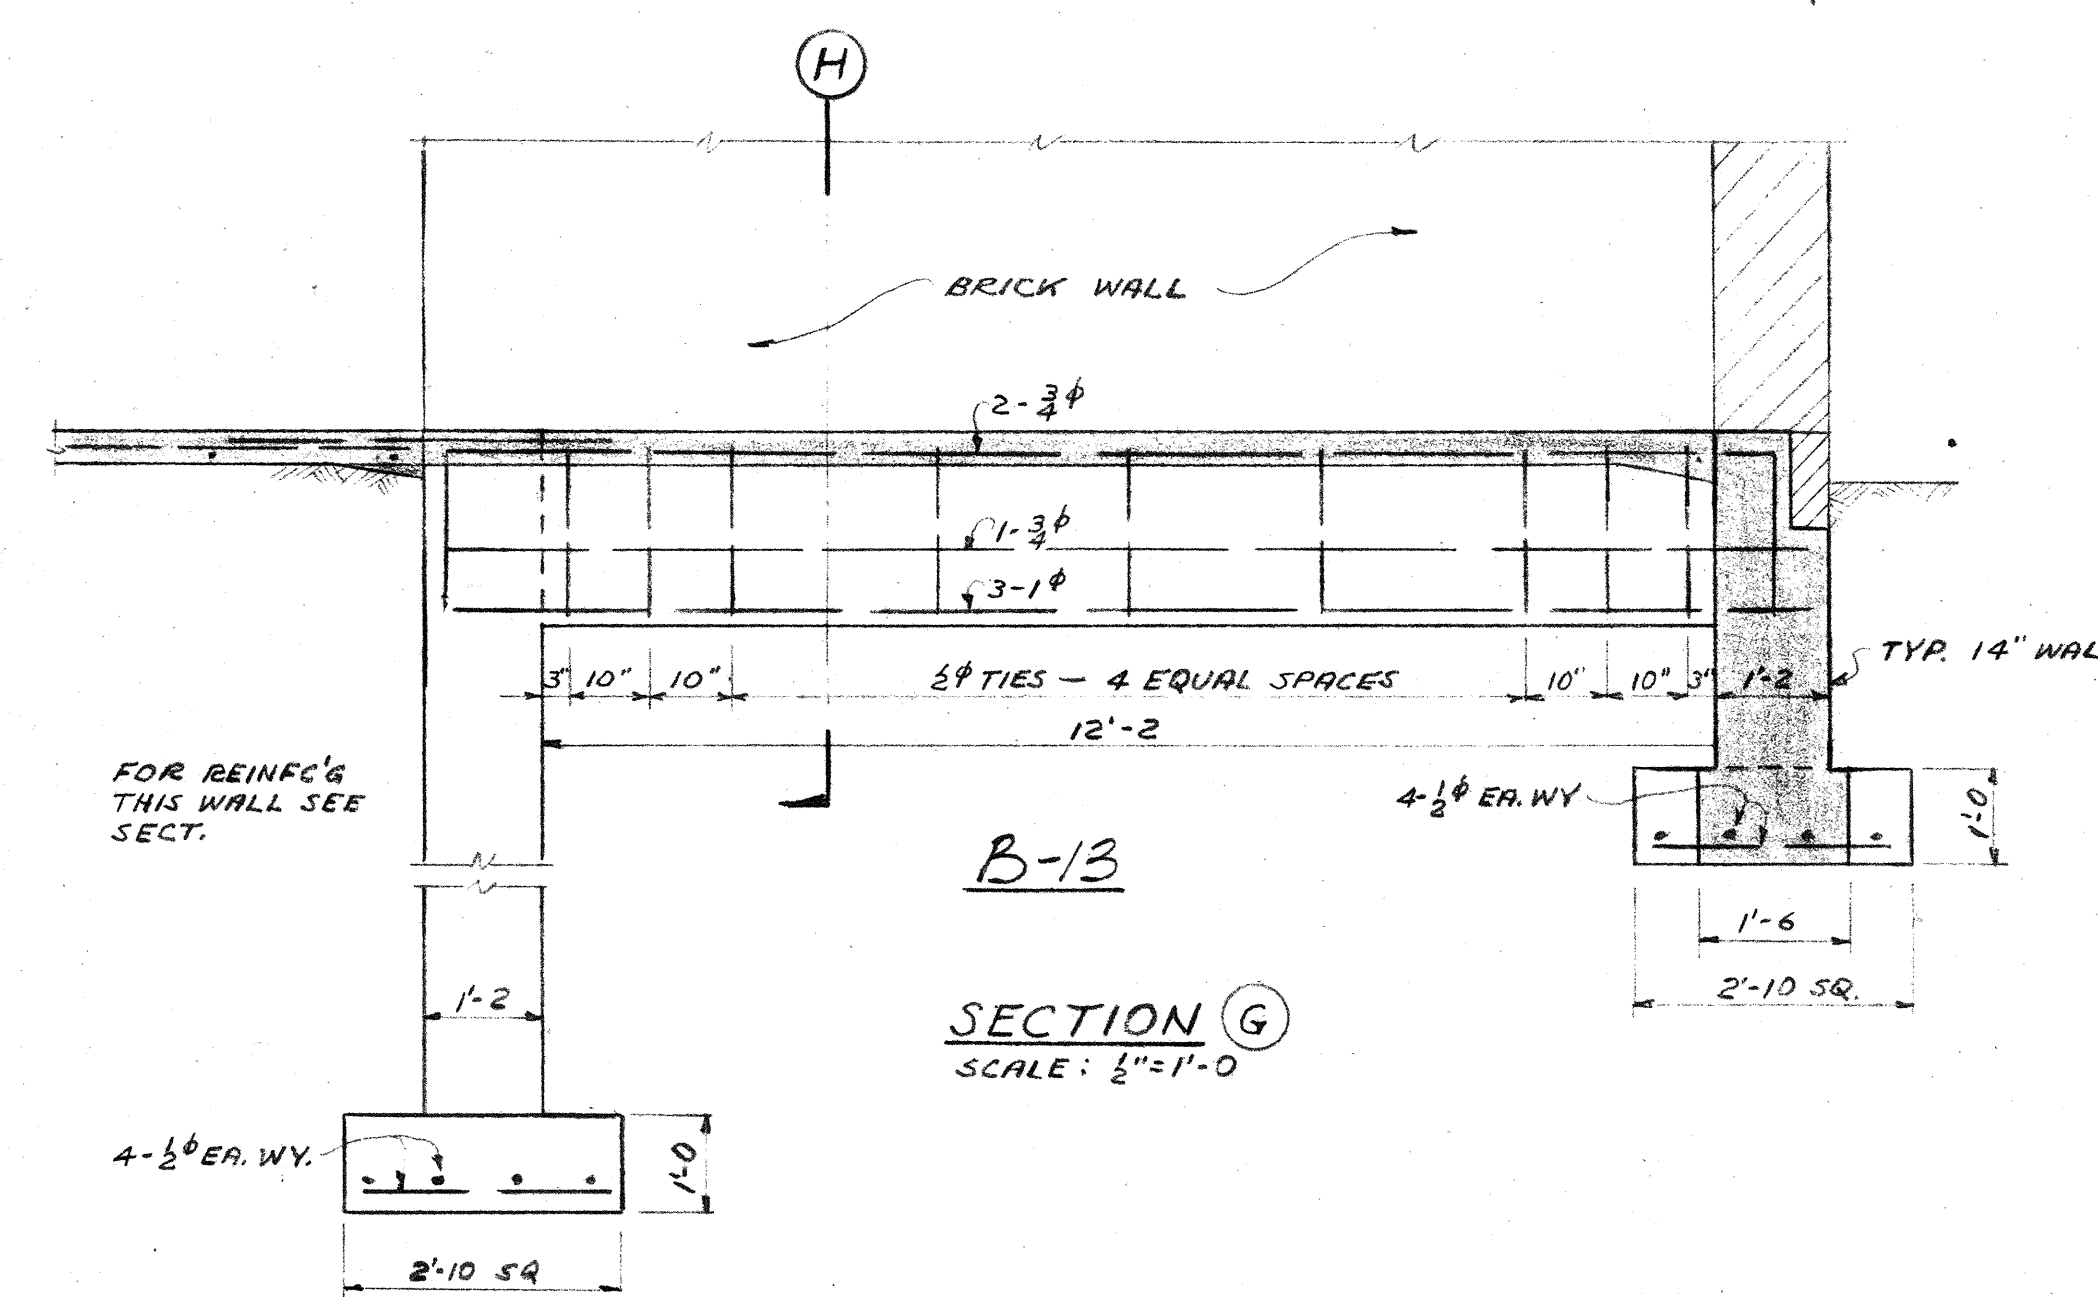
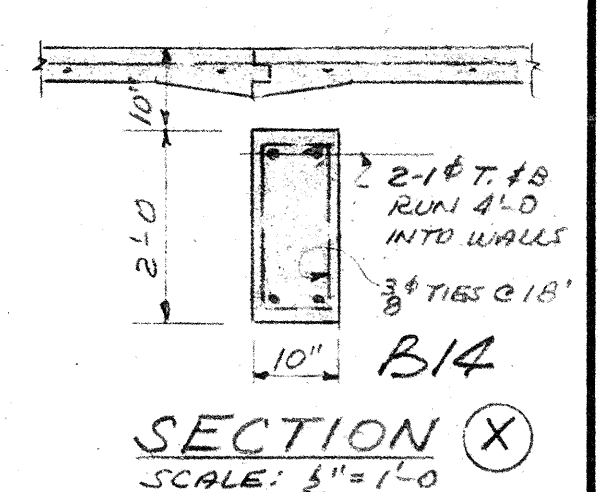
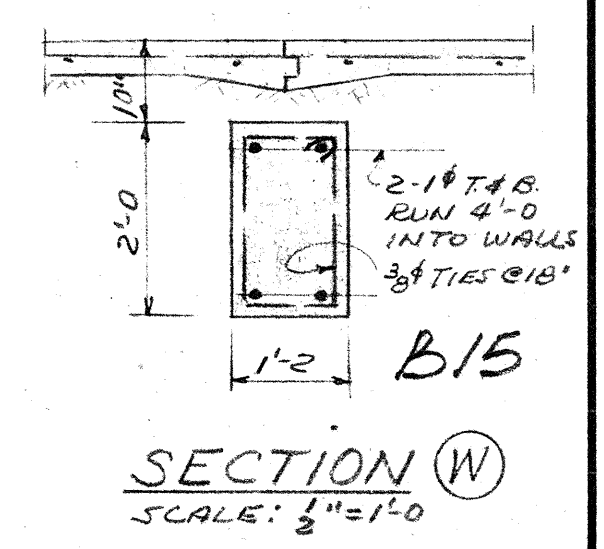
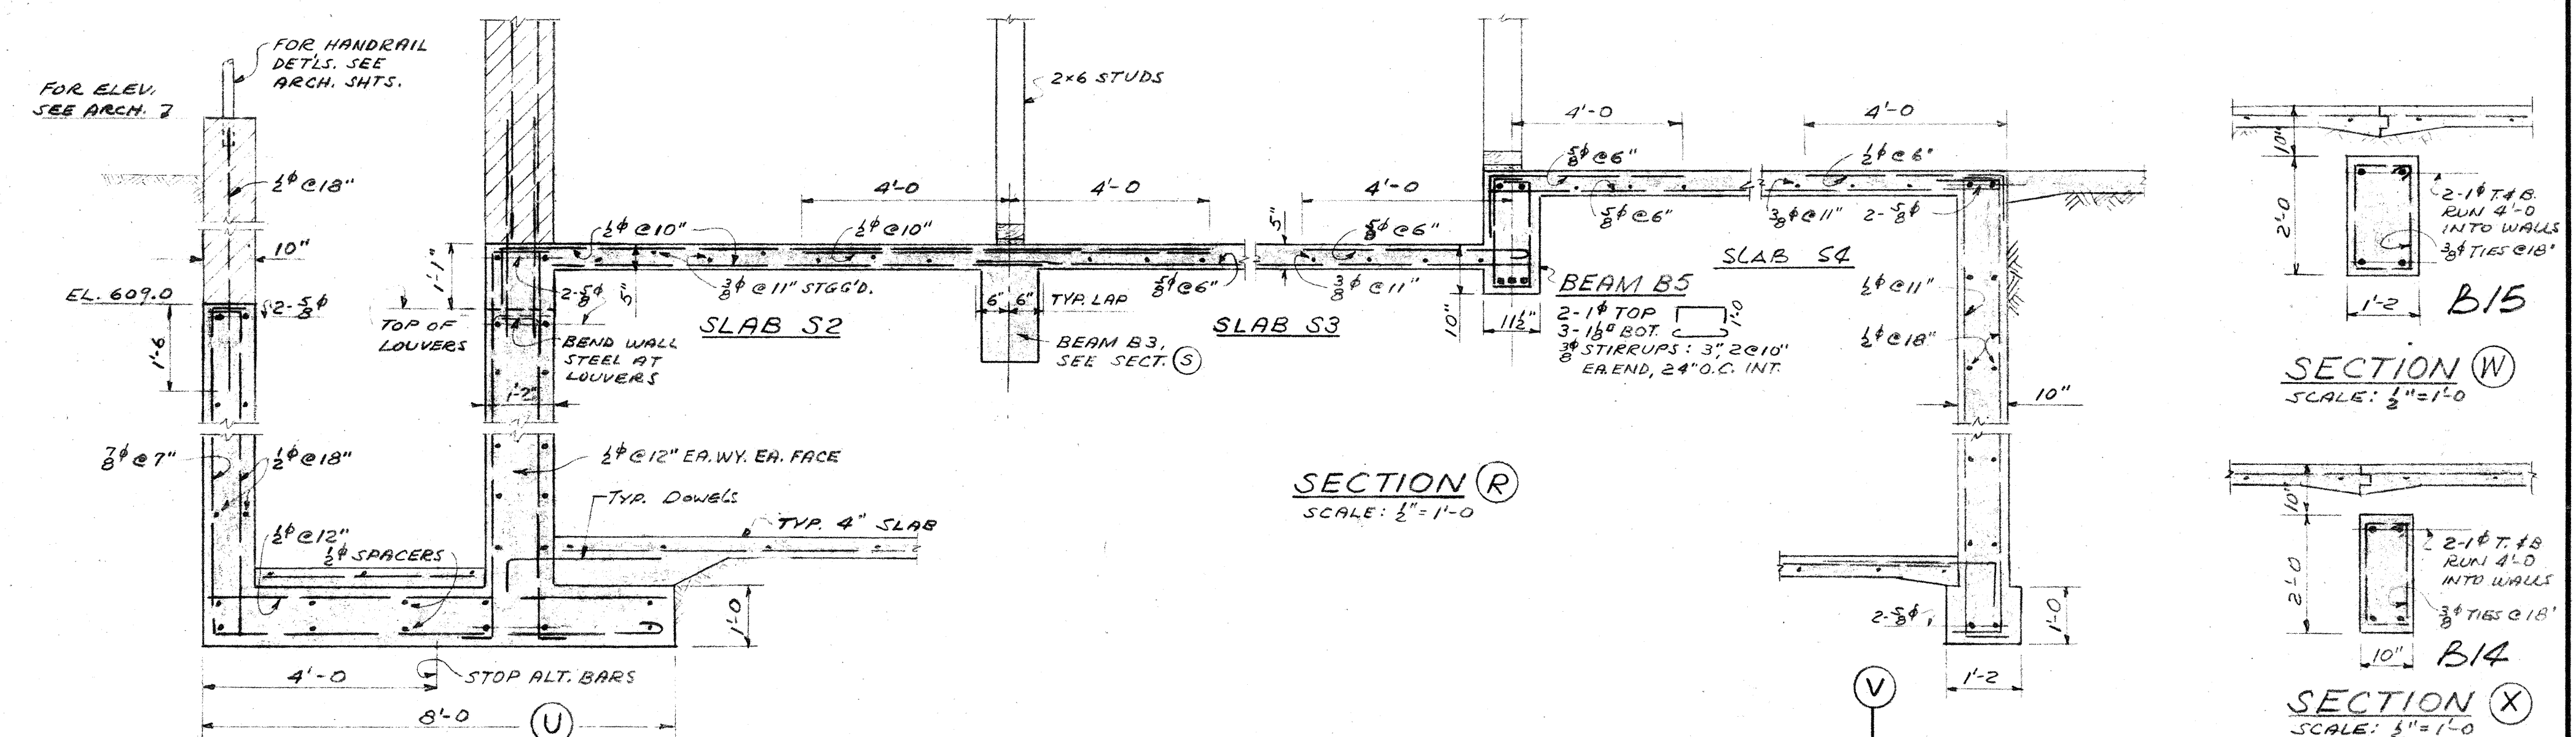
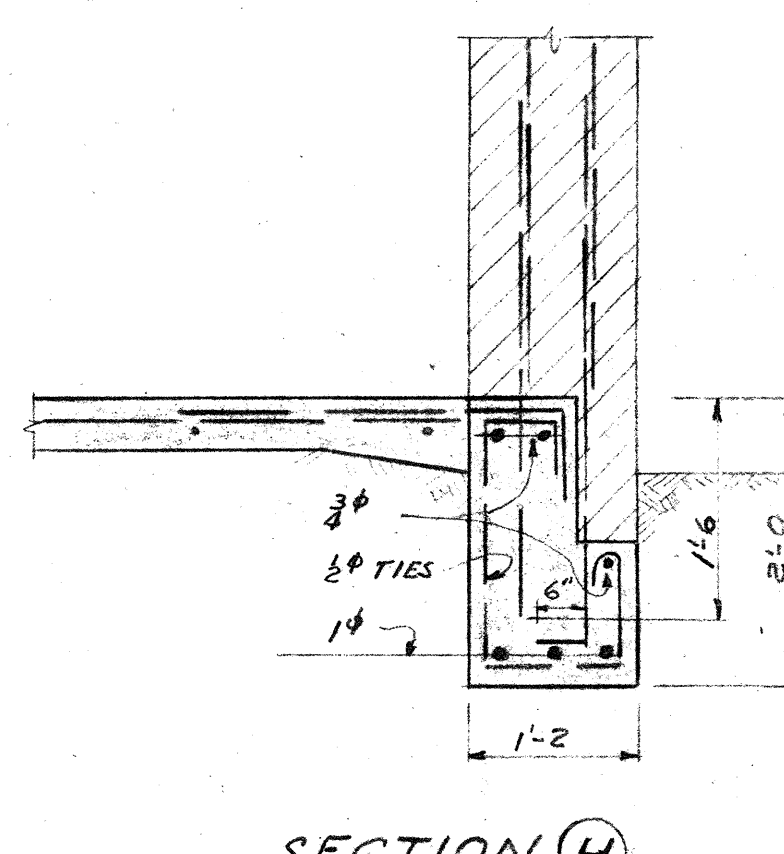
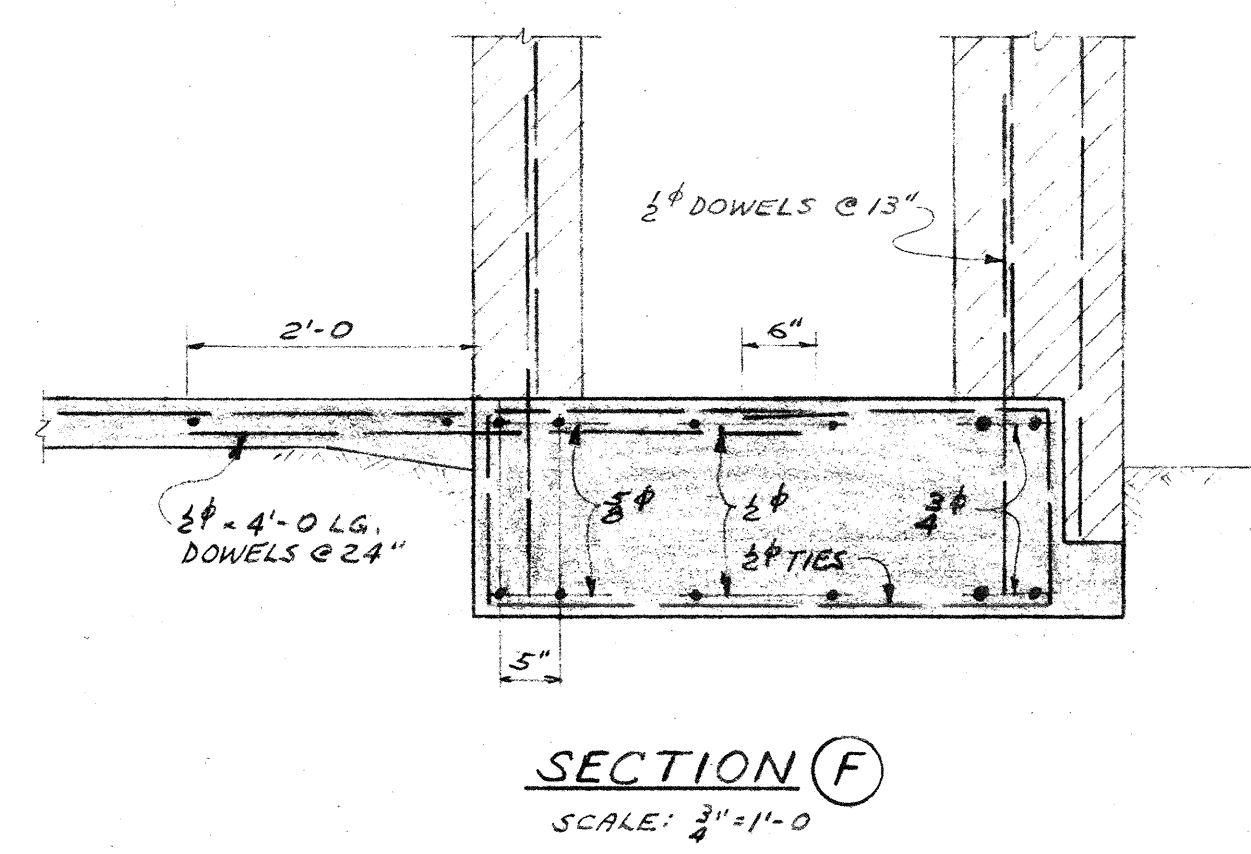
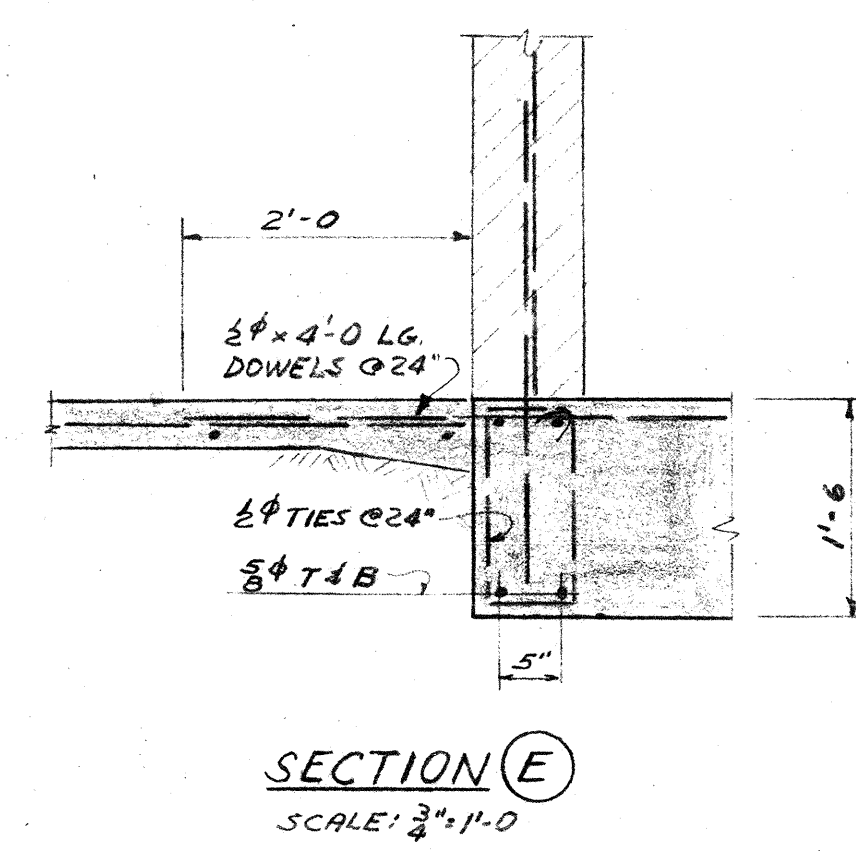
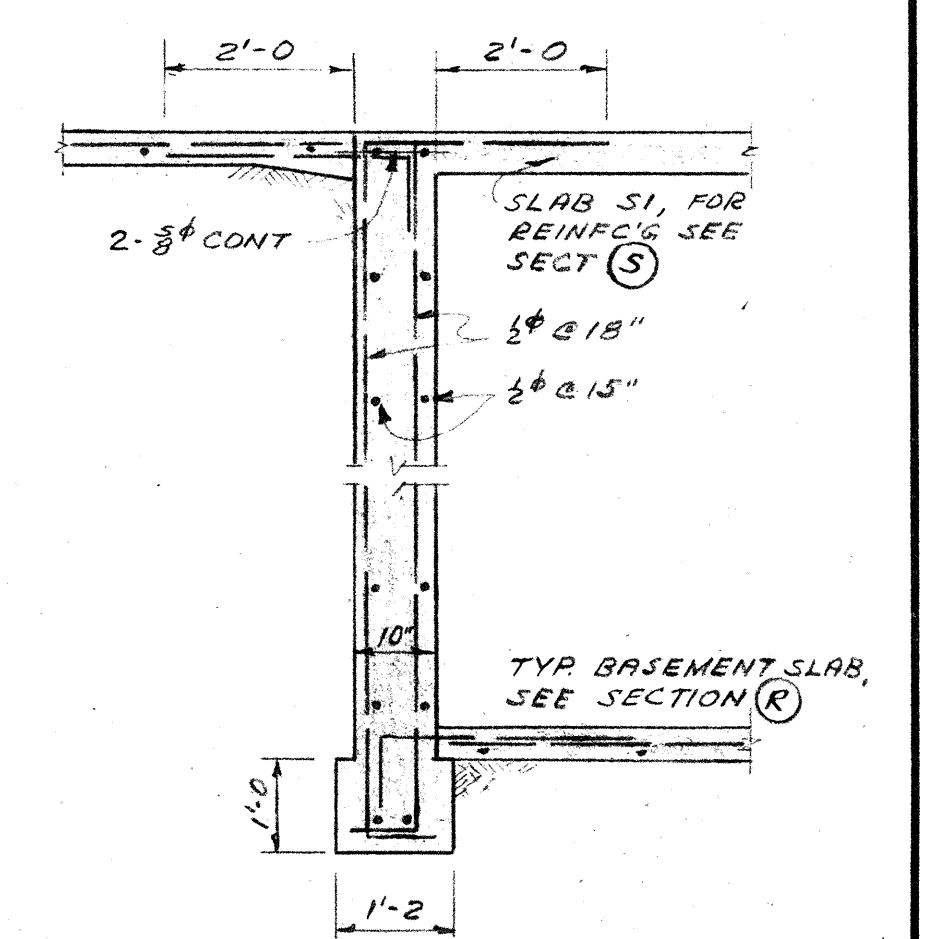
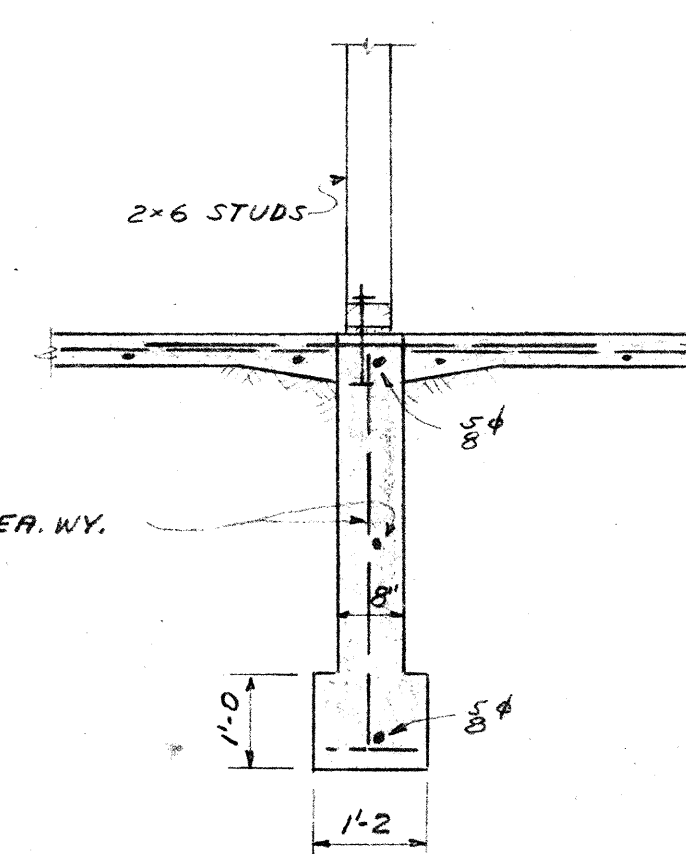
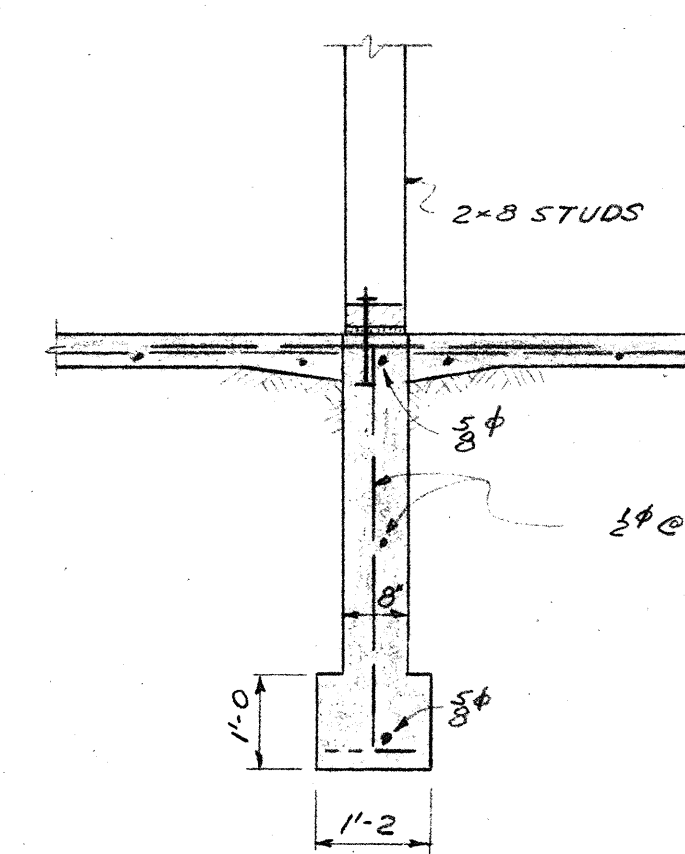


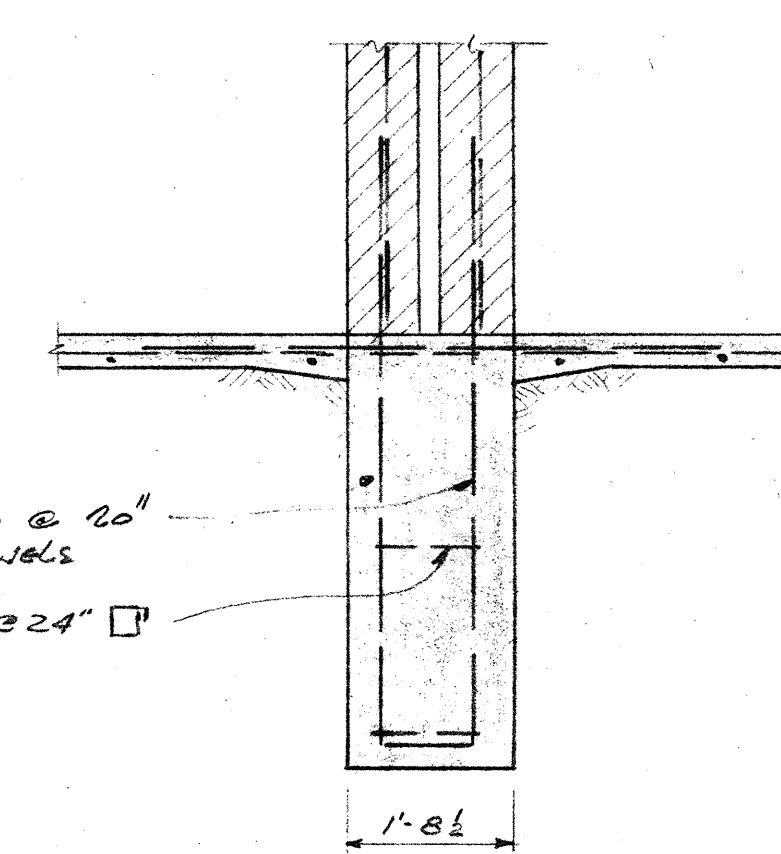

NOTES: 1. BRICK WALLS NOT SHOWN
2. TOP REINFC'G SHOWN,
BOT REINFC'G SIMILAR.

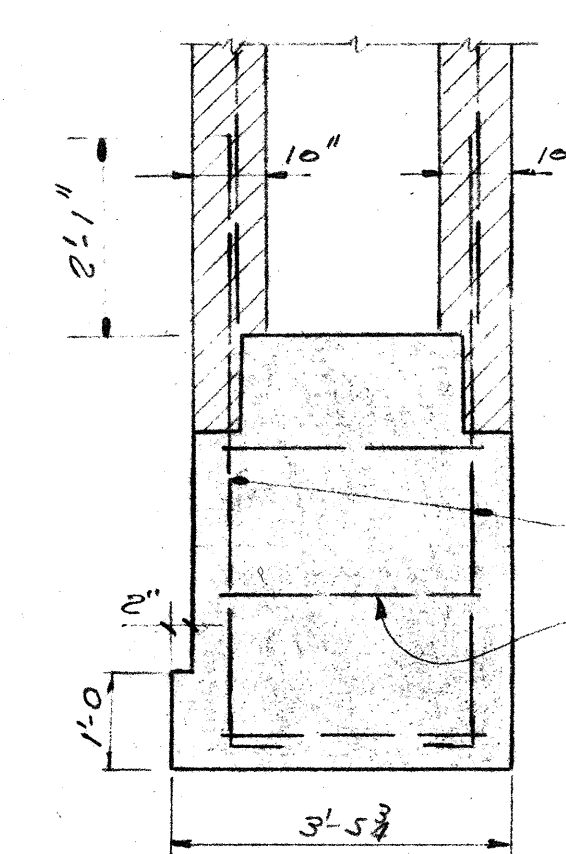

Remarks	Revisions	Engineer ERNEST H. LEE Professional Engineer No. 1061 State of California Ernest H. Lee	Approval	AUSTIN FIELD & IRY Architects 2311 WEST THIRD STREET • LOS ANGELES 5, CALIFORNIA • DUNKIRK 8-1326	ELEVATIONS & SECTIONS ST. EDMUND'S EPISCOPAL CHURCH SAN MARINO, CALIF.	DATE 20-AUG-51
						DRAWN RER ARCHITECT - LICENSE #