
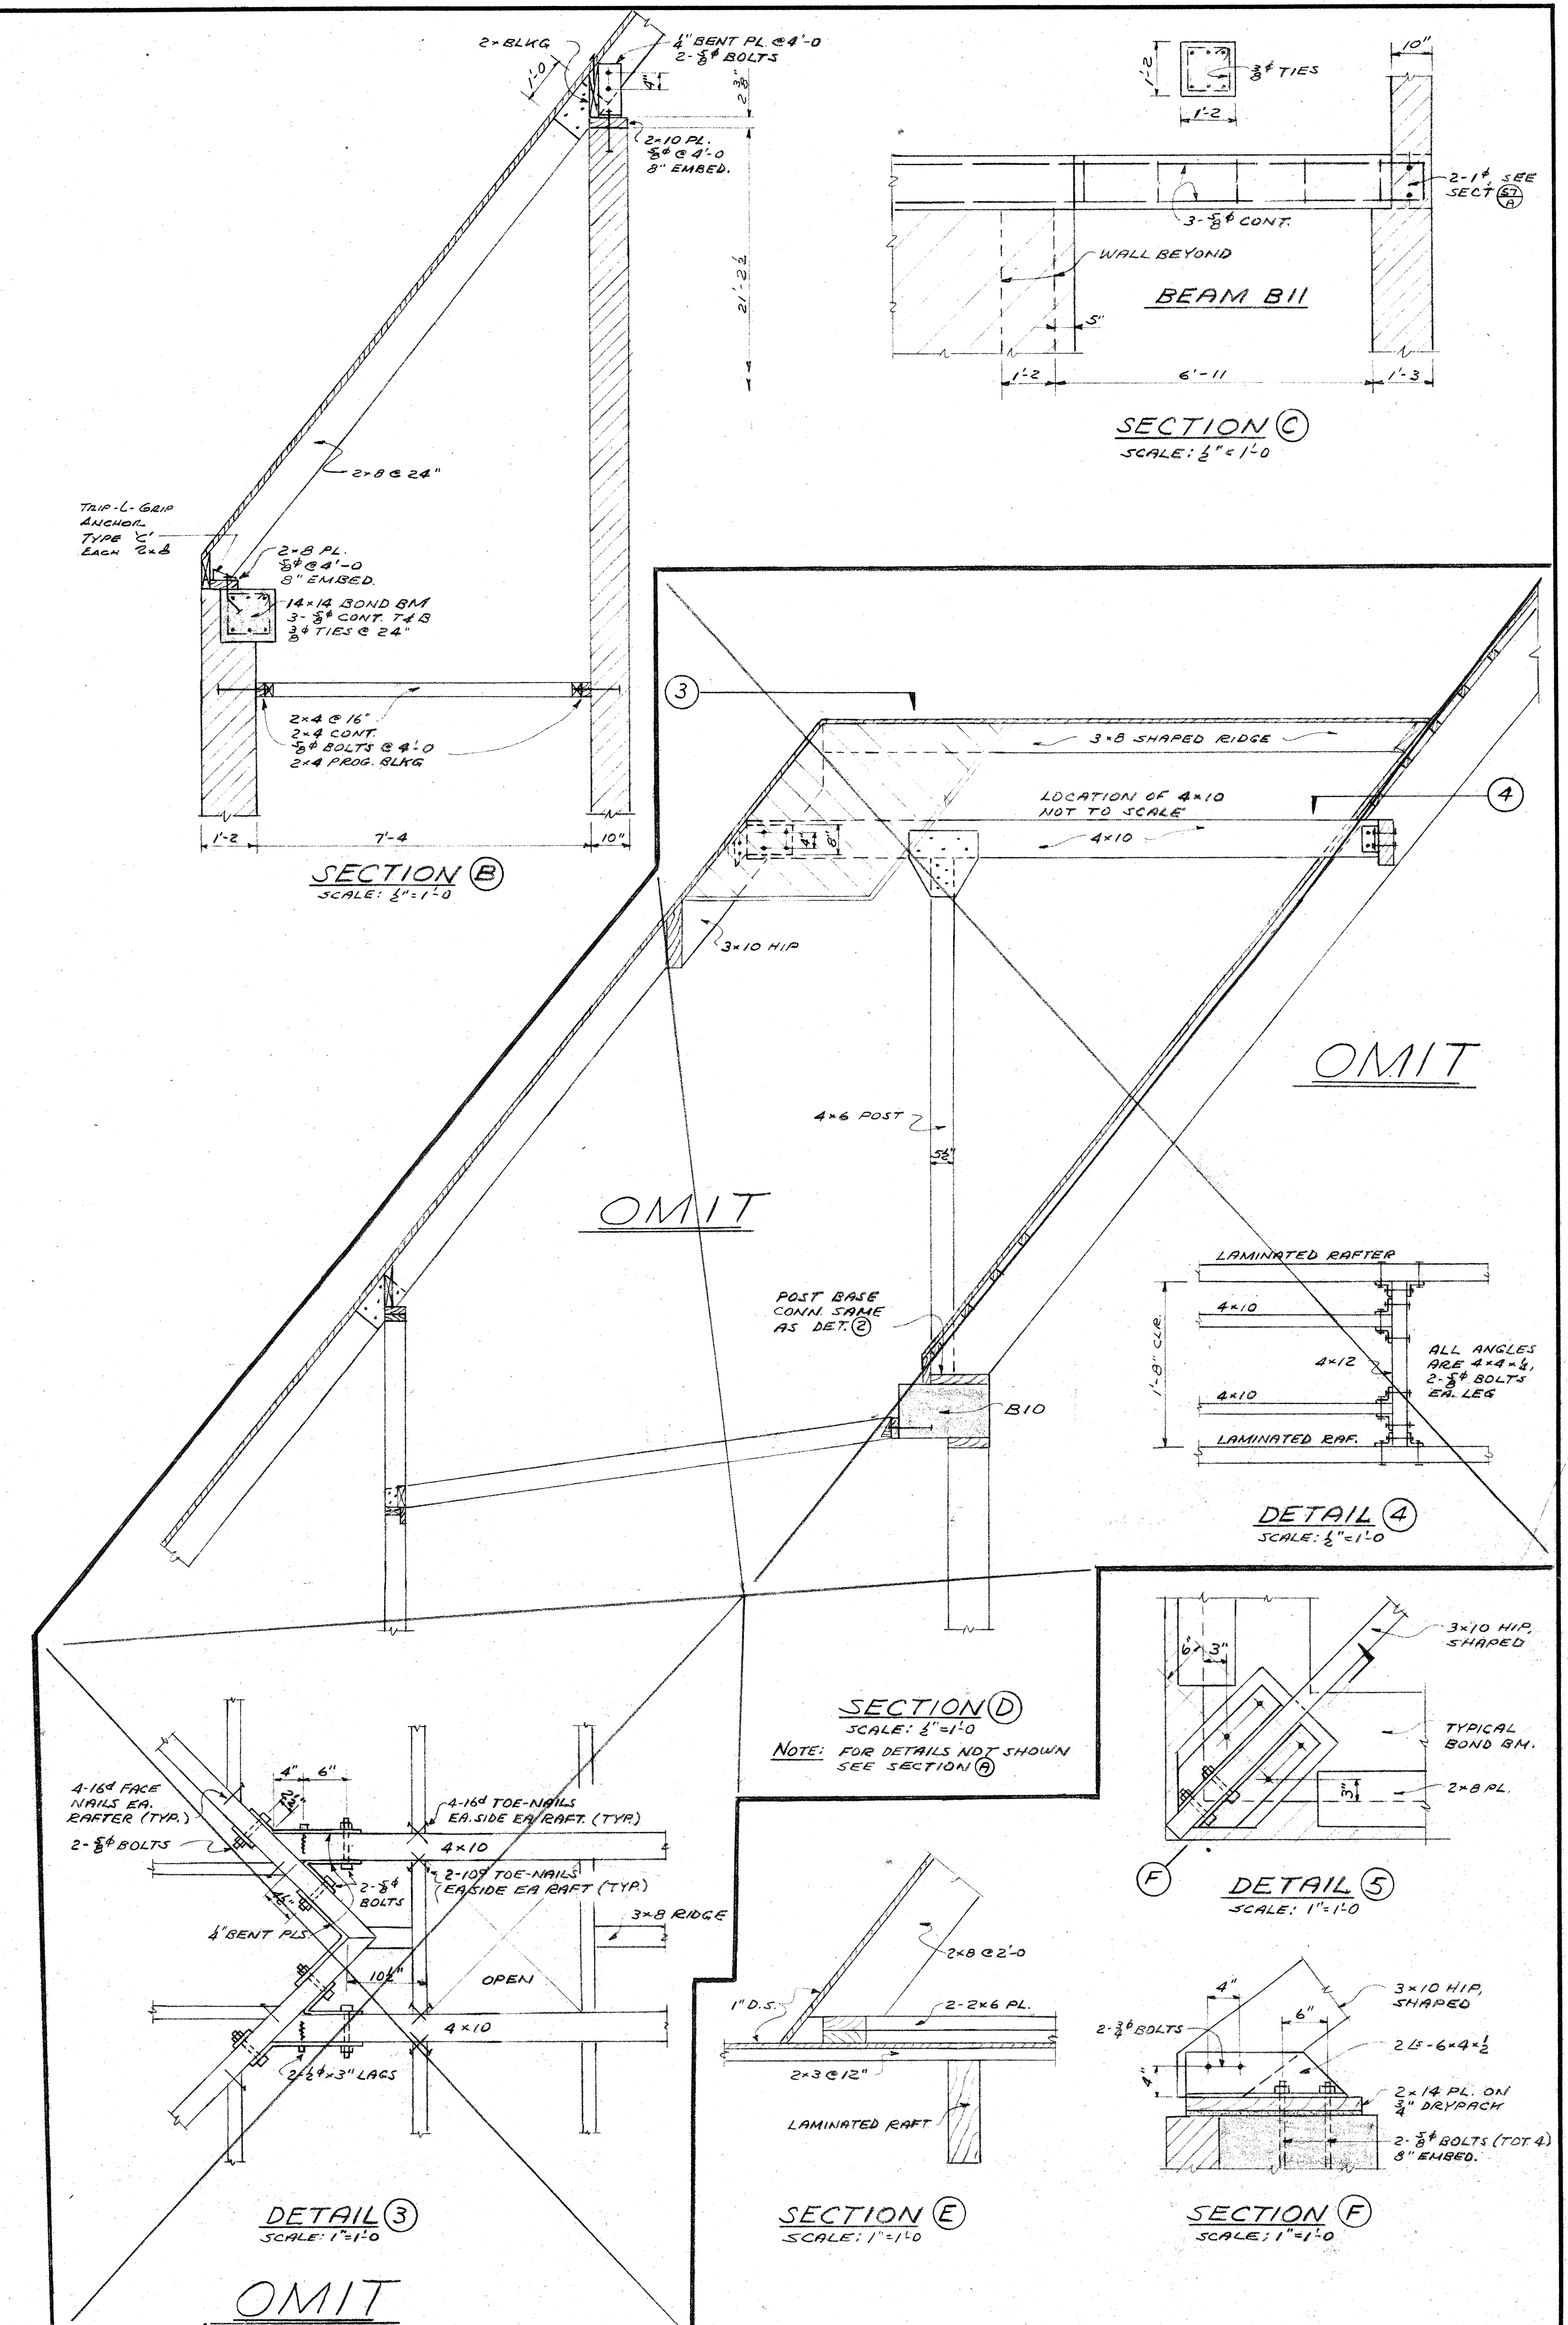


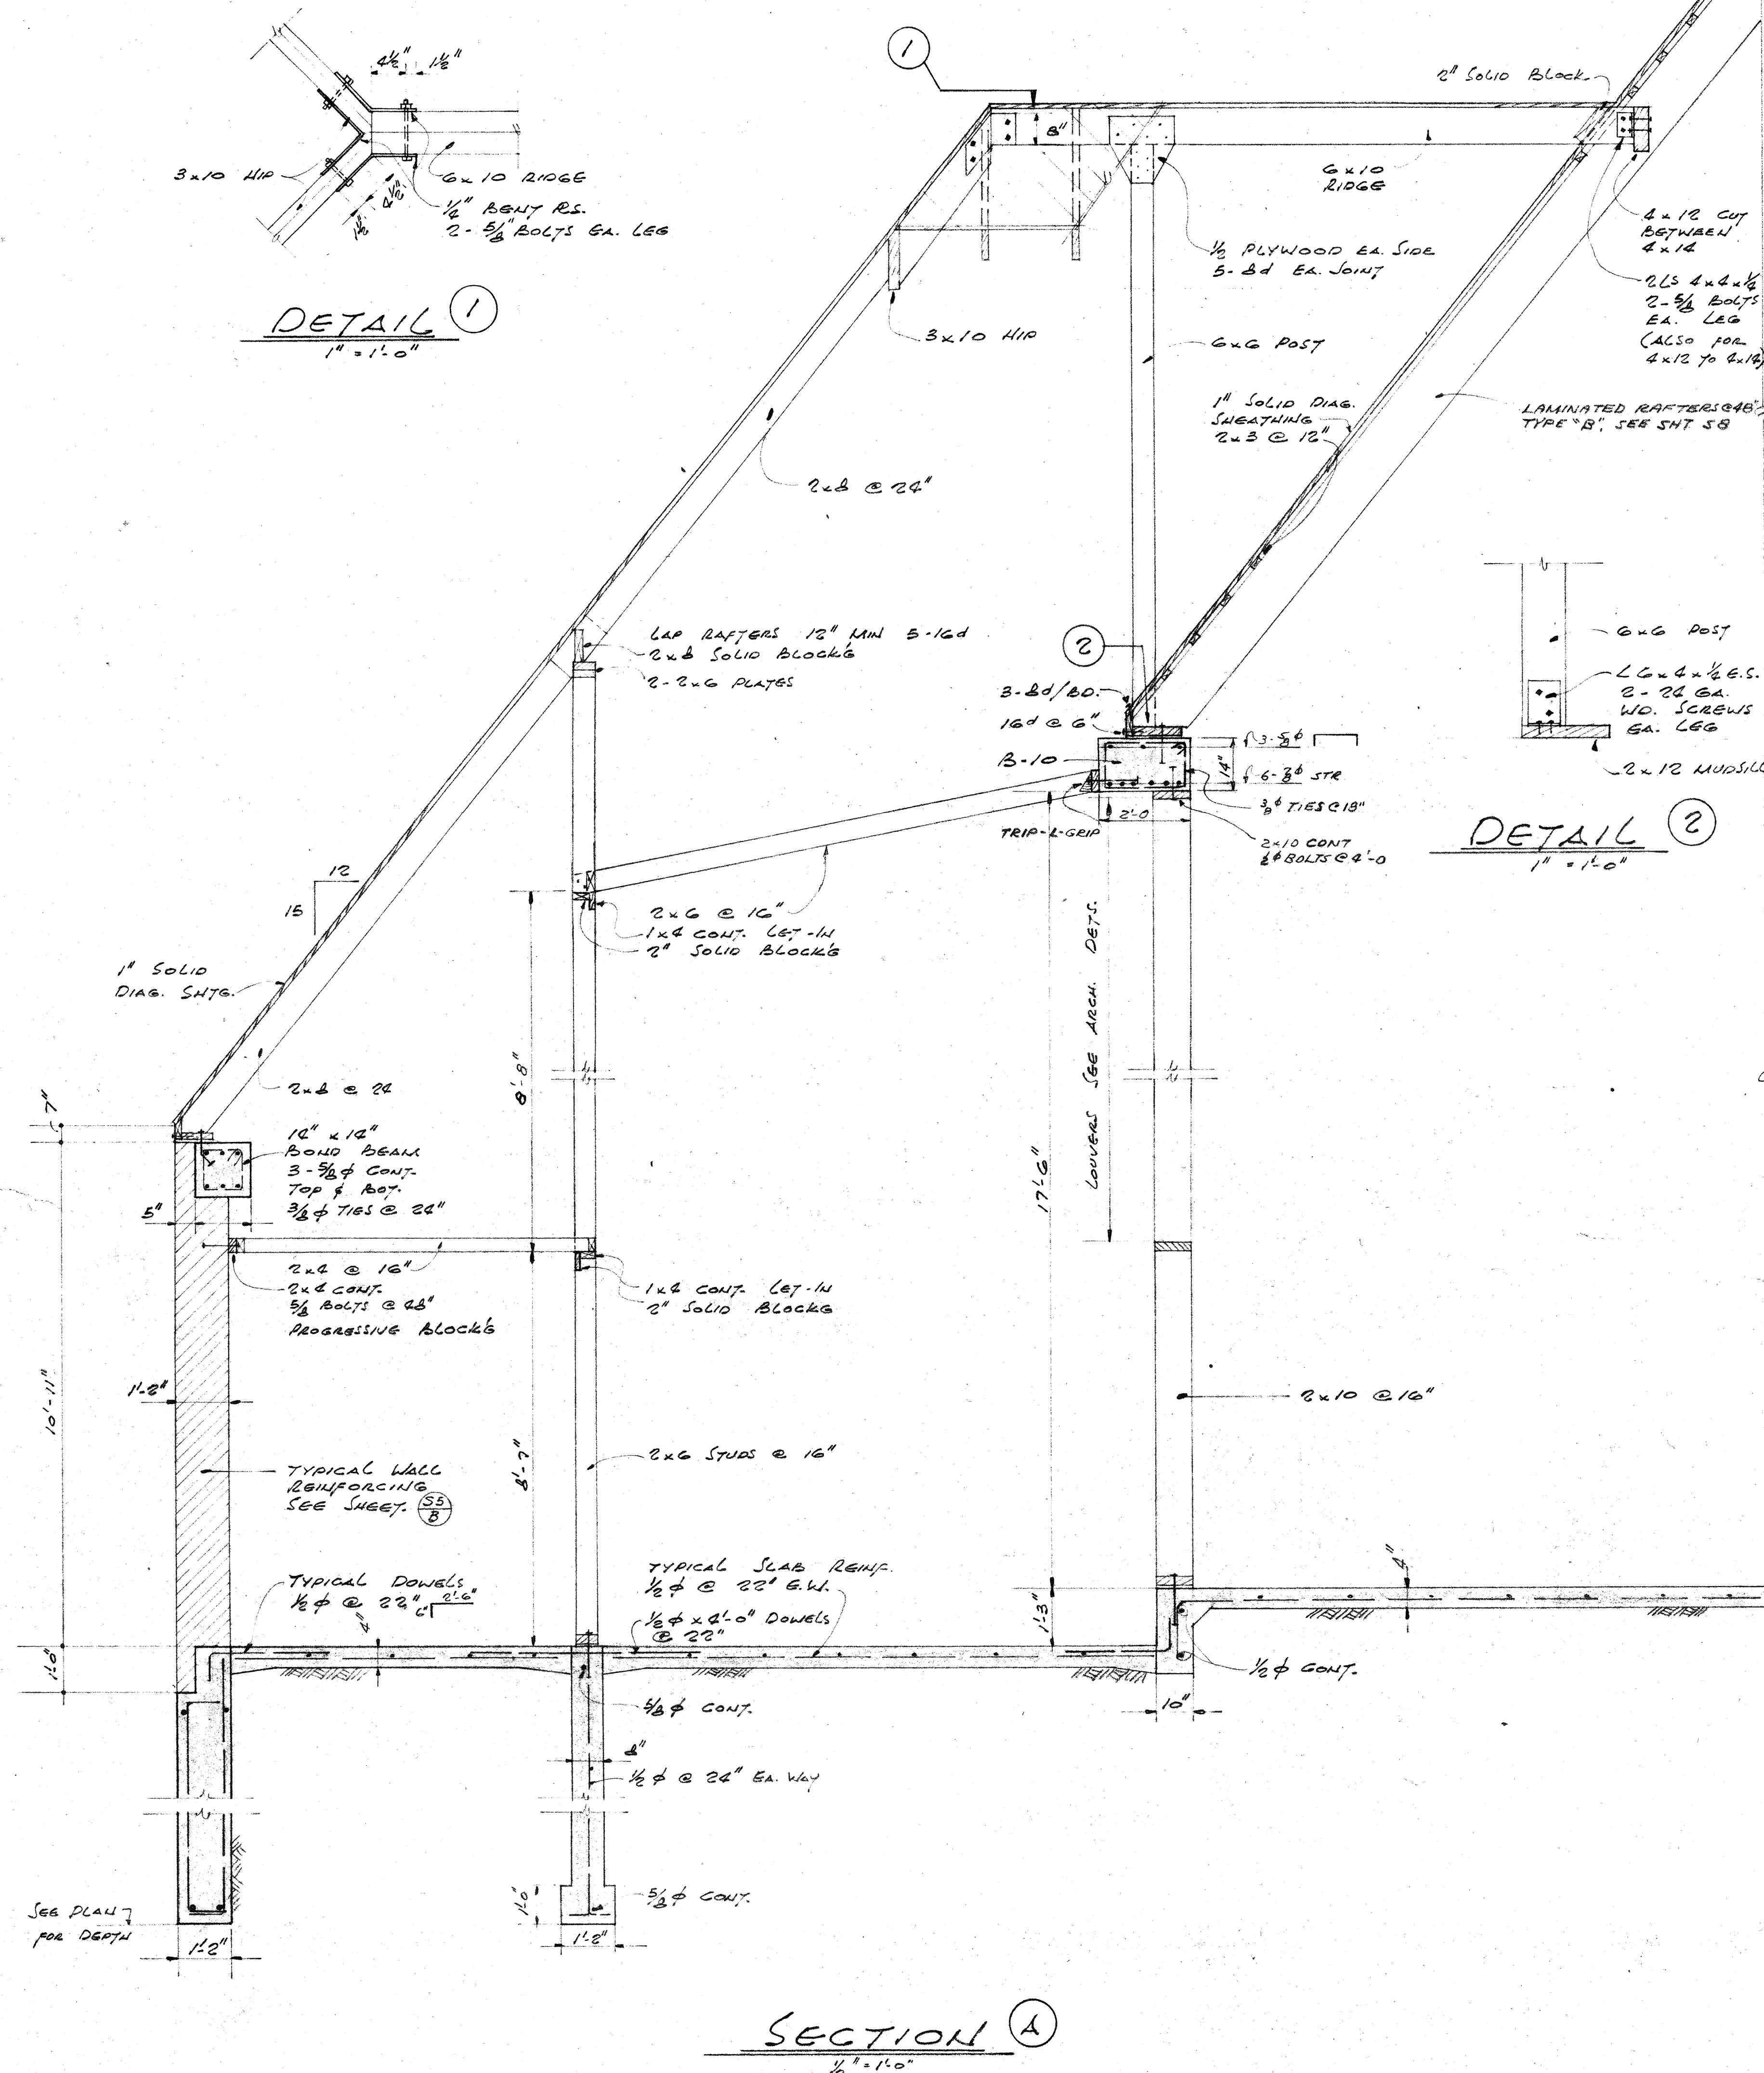

Remarks	Revisions	Engineers ERIN ST. HILL ARCHITECTS, INC. DUNKIRK, CALIF.	Approvals	 AUSTIN FIELD & IRY ARCHITECTS 2311 WEST THIRD STREET • LOS ANGELES 5, CALIFORNIA • DUNKIRK 8-1326	SECTIONS & DETAILS ST. EDMUNDS EPISCOPAL CHURCH SAN MARINO, CALIF.	DATE AUG-91 COM. 1061 SHEET NUMBER SC
---------	-----------	---	-----------	--	--	---