



SCARF JOINT
SEE SPECIFICATIONS

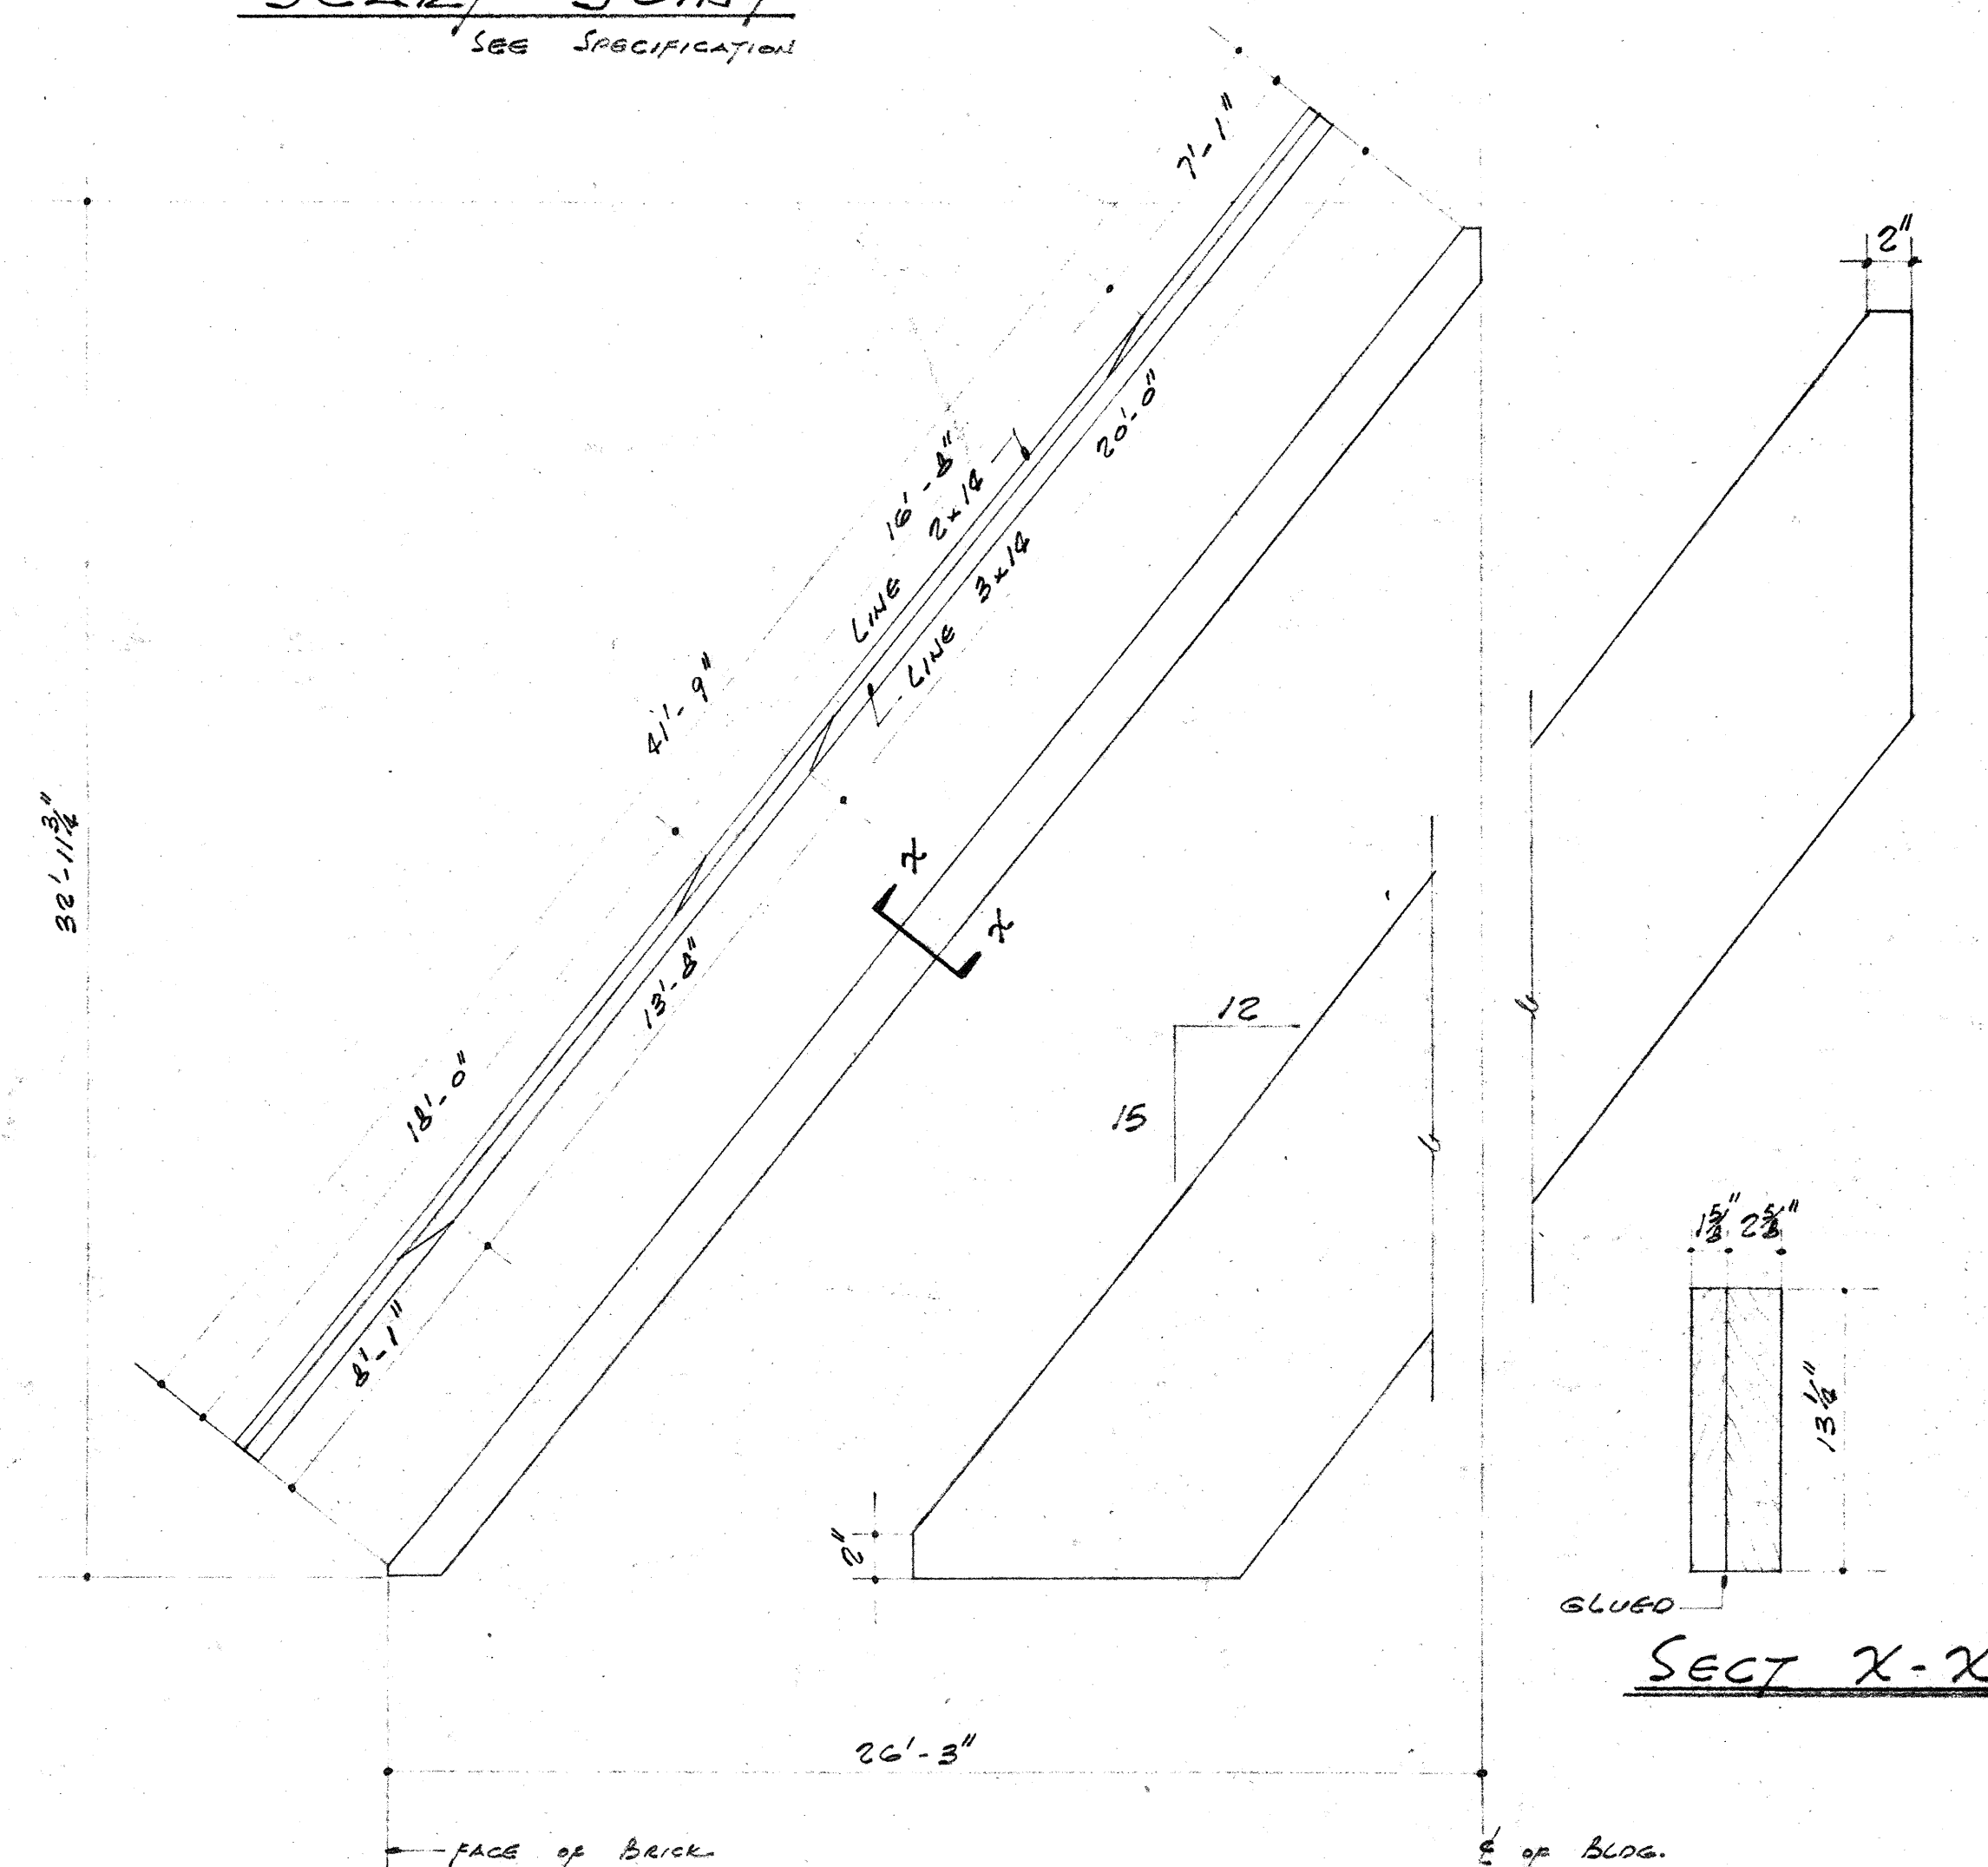


TYPE 'A'


LAMINATED RAFTER DETAILS
SEE SPECIFICATIONS FOR FABRICATION AND ERECTION REQUIREMENTS

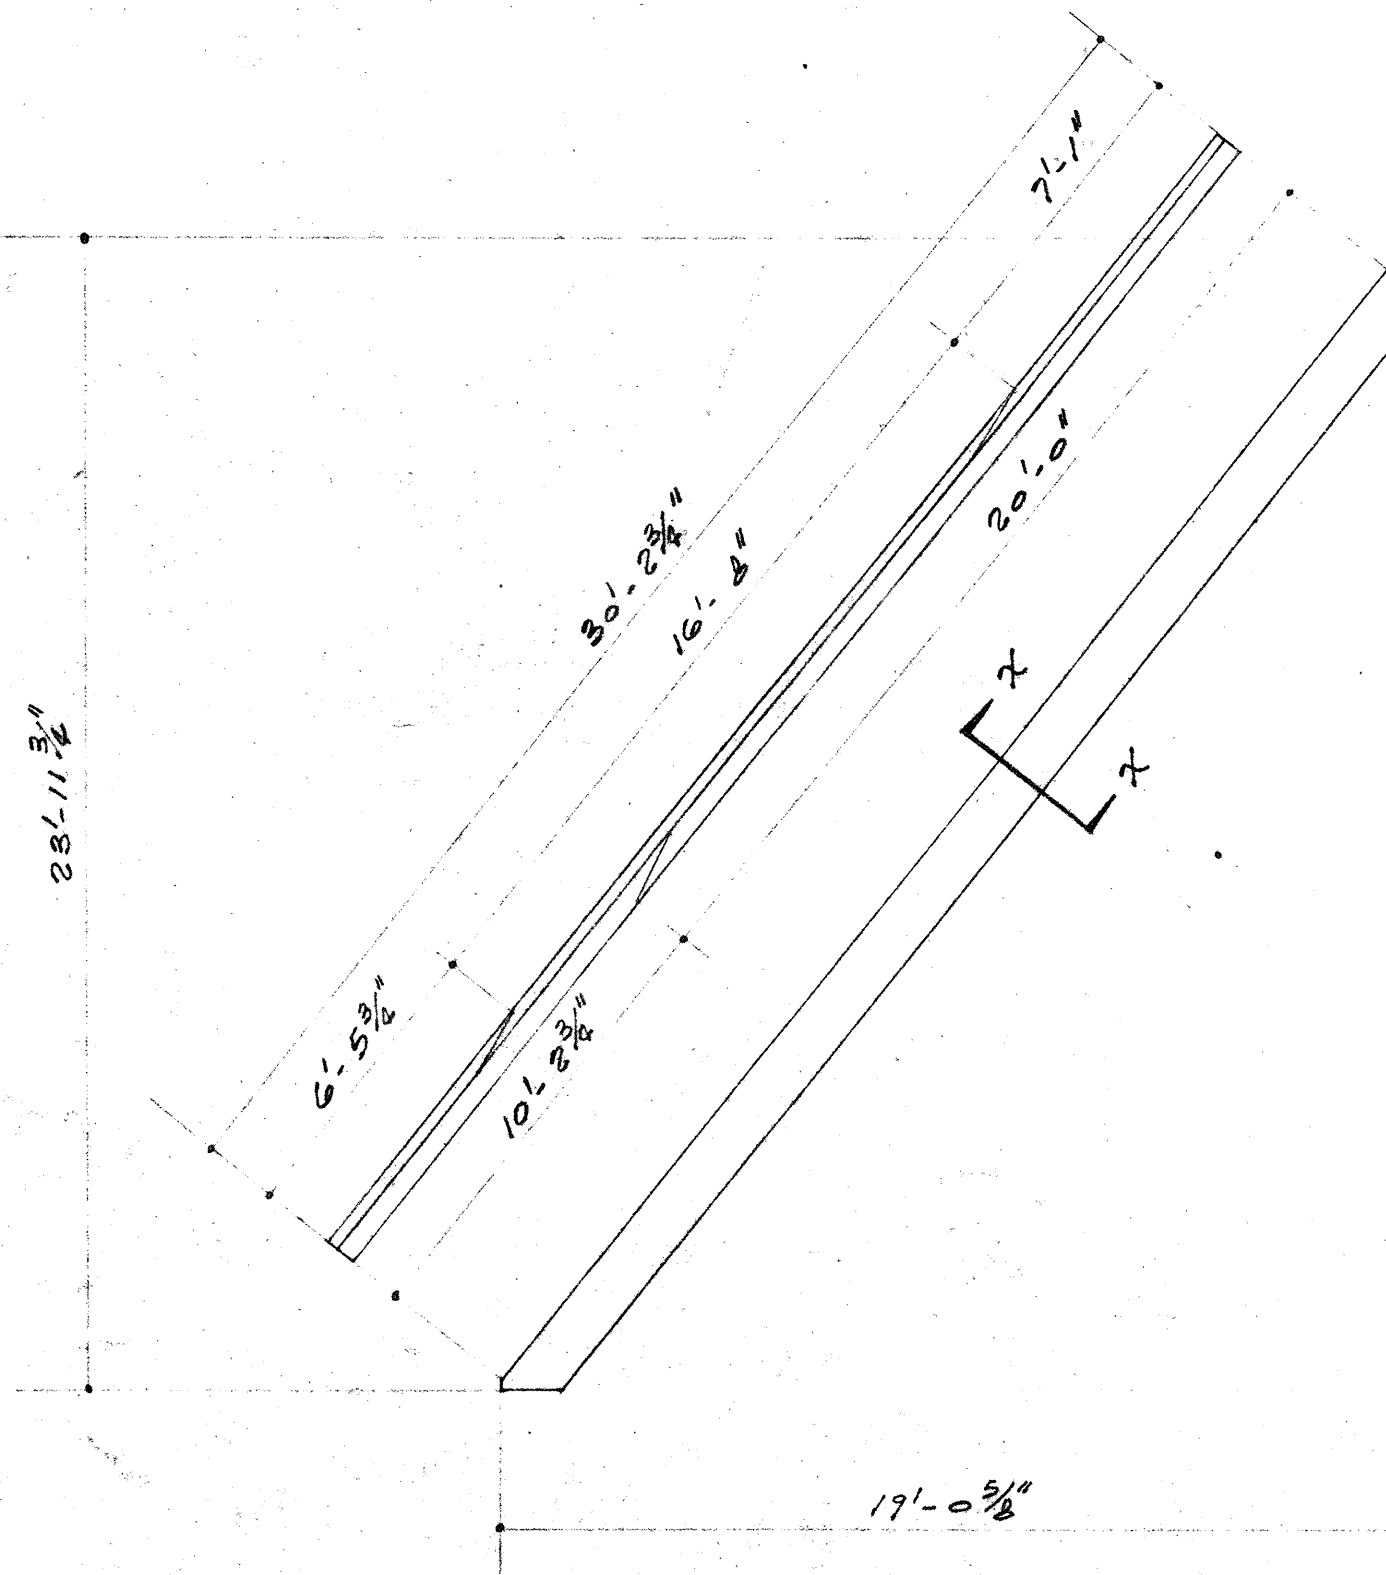

TYPE 'B'

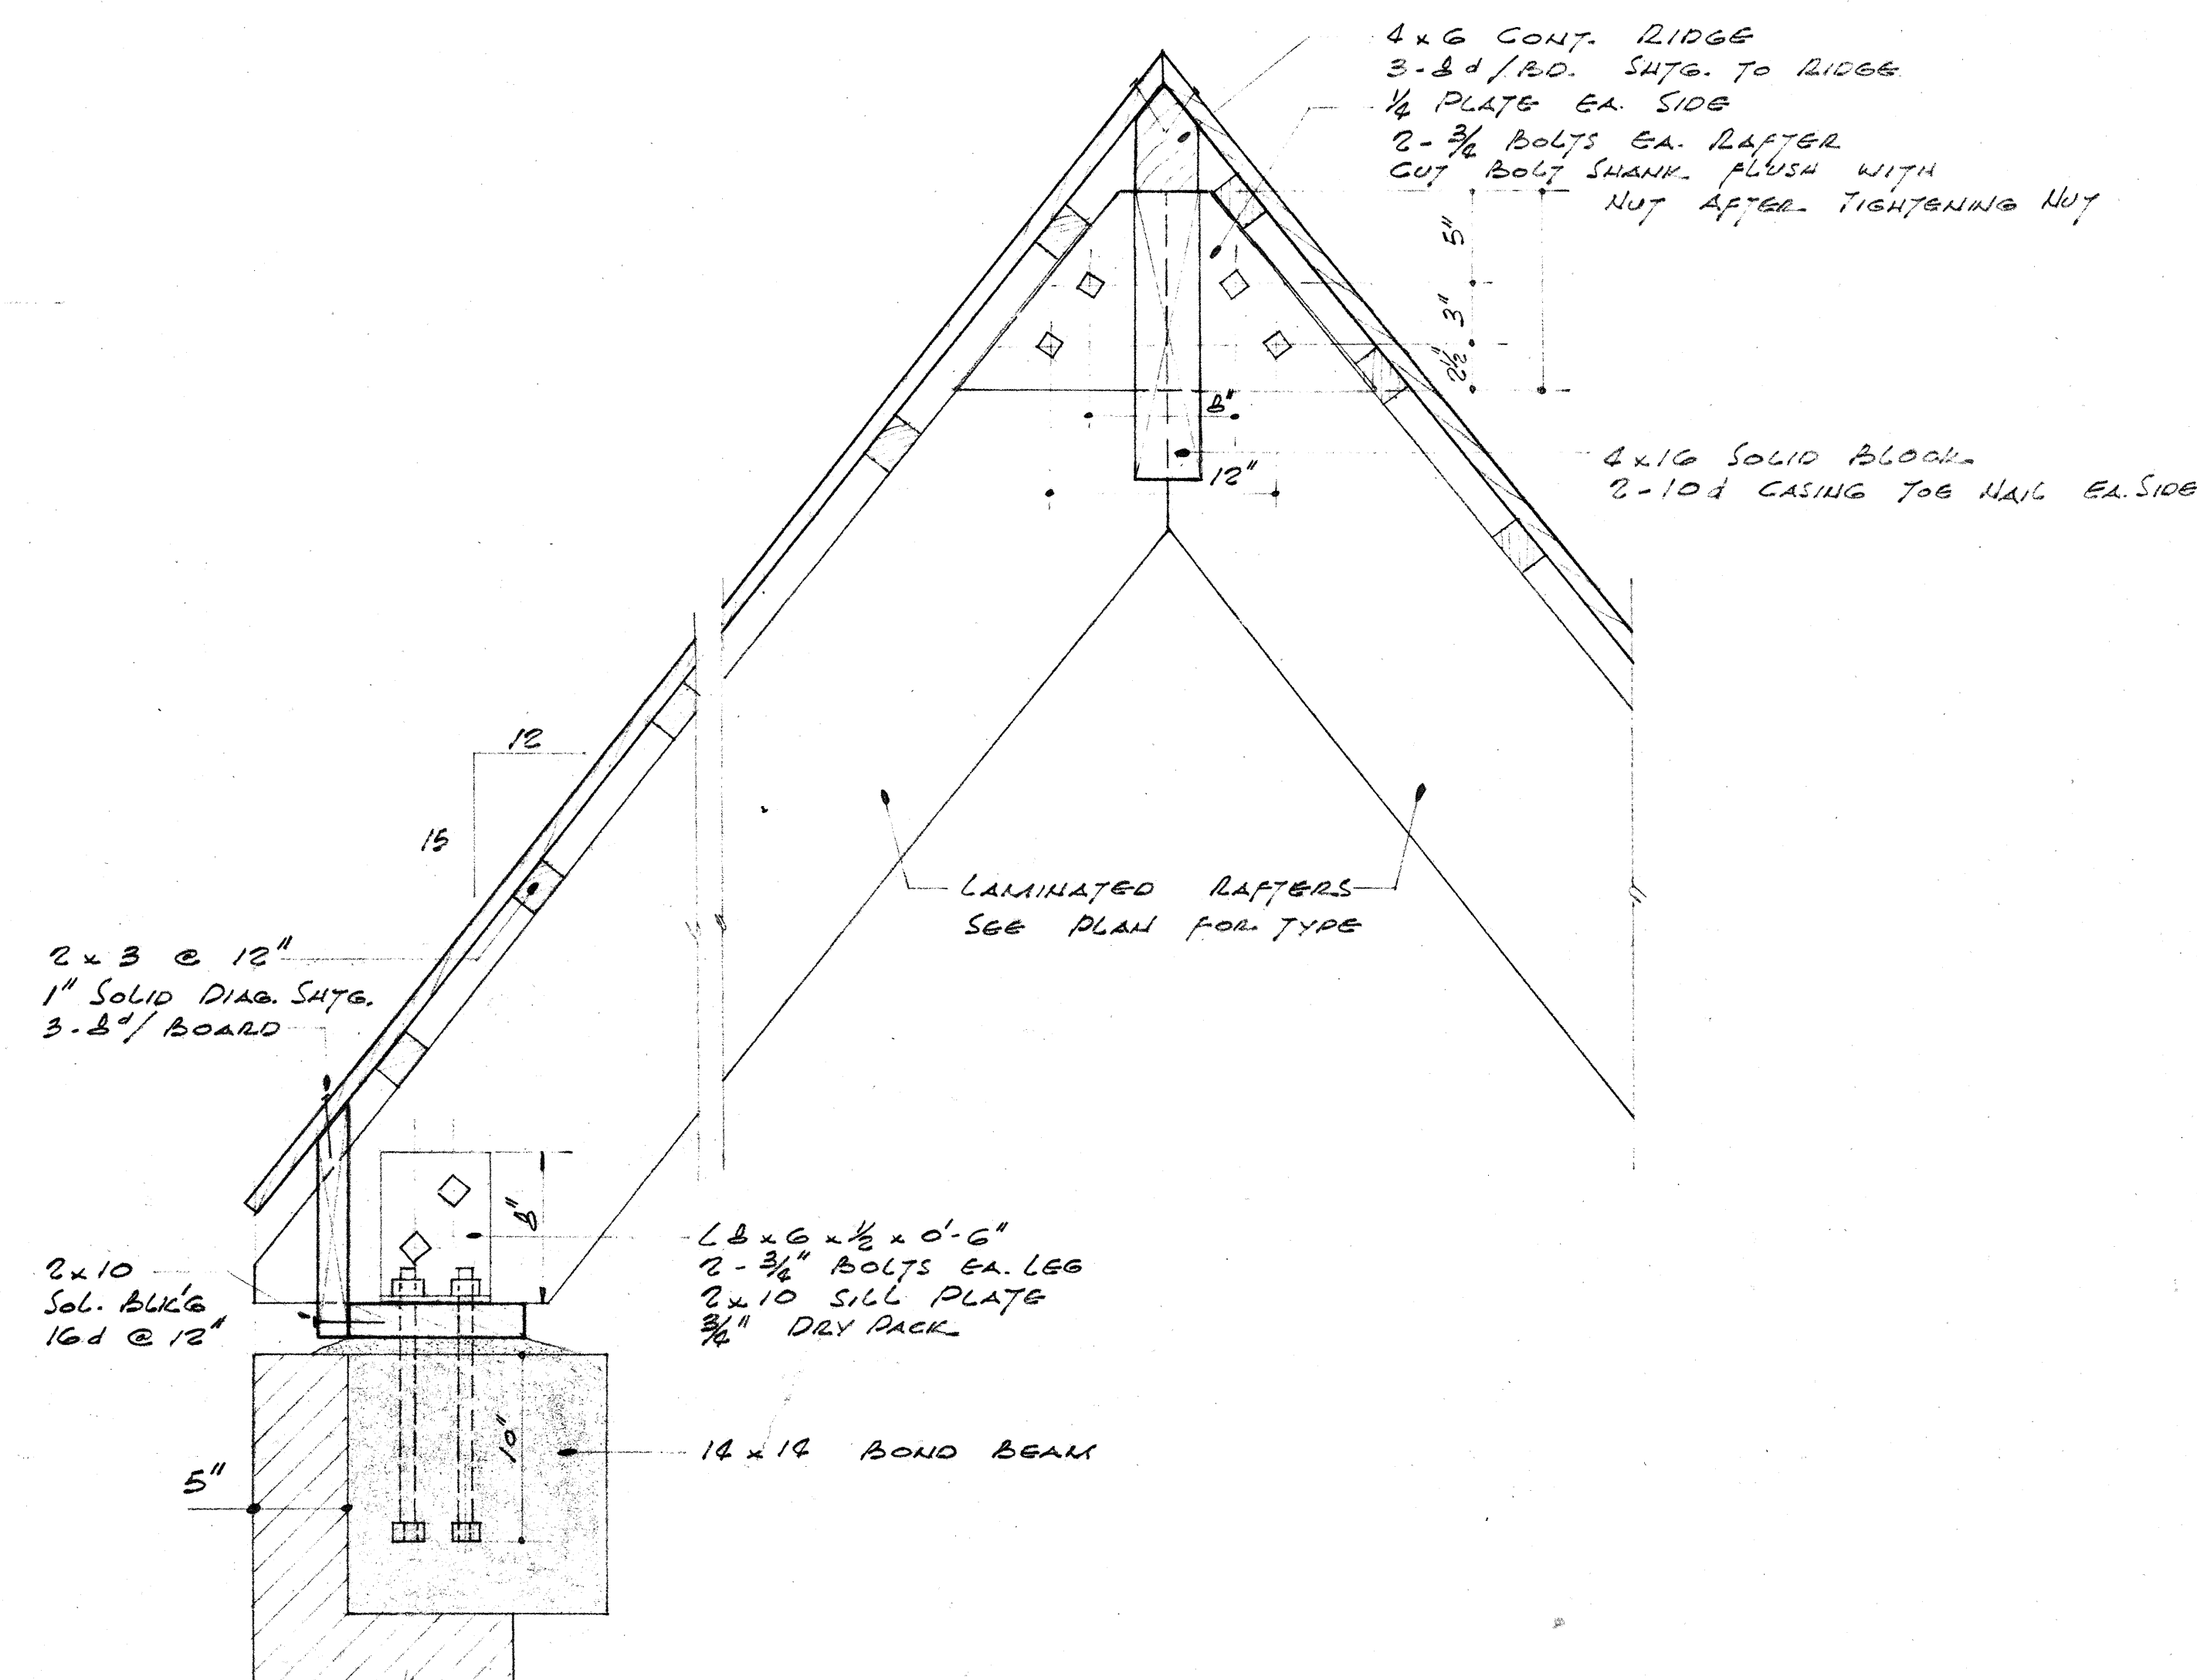


TYPICAL RAFTER CONNECTION AT WALL AND RIDGE
1/2" x 1'-0"

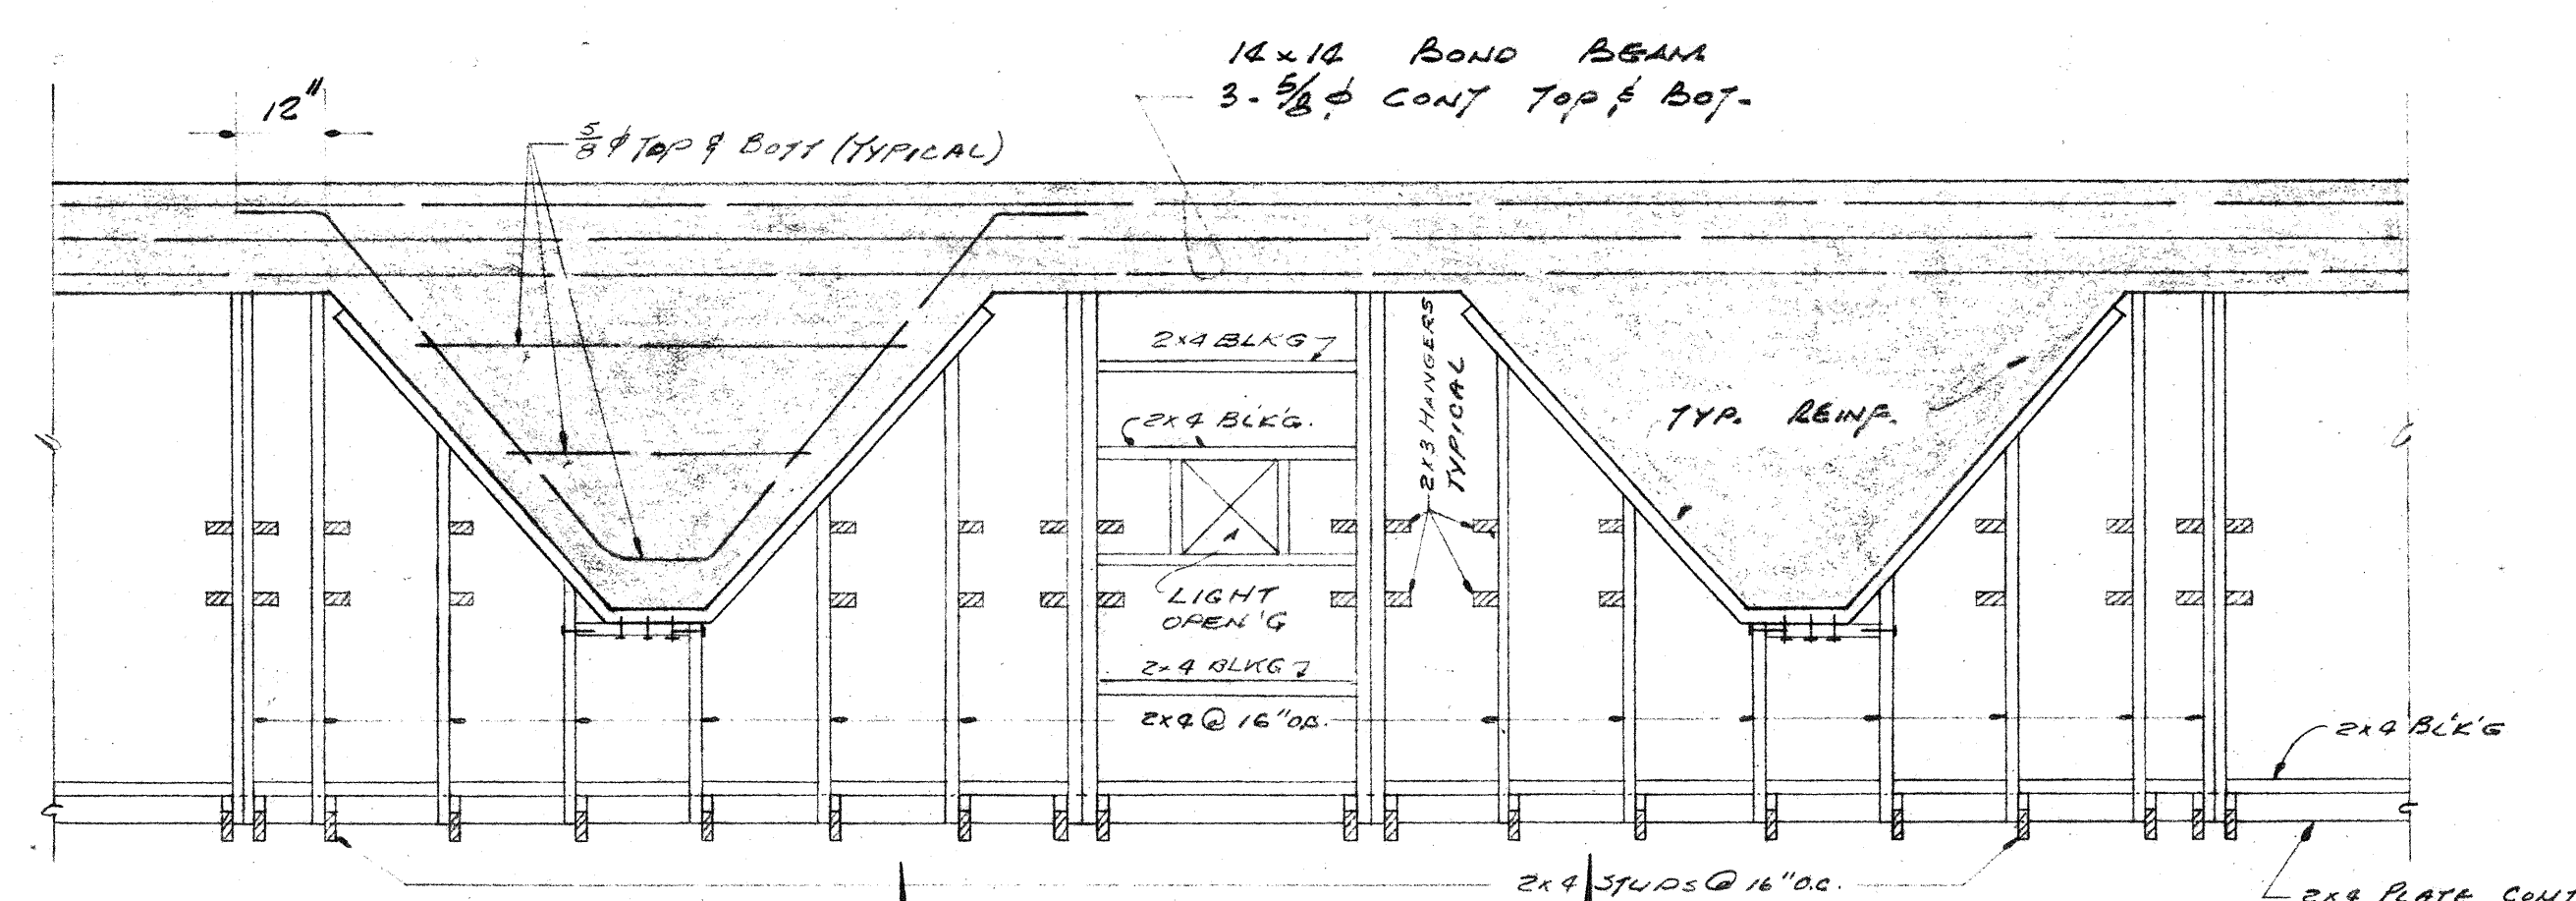

PLAN OF BOND BEAM REINFORCING & LIGHT TROUGH BRACING
1/2" x 1'-0"

SECTION C

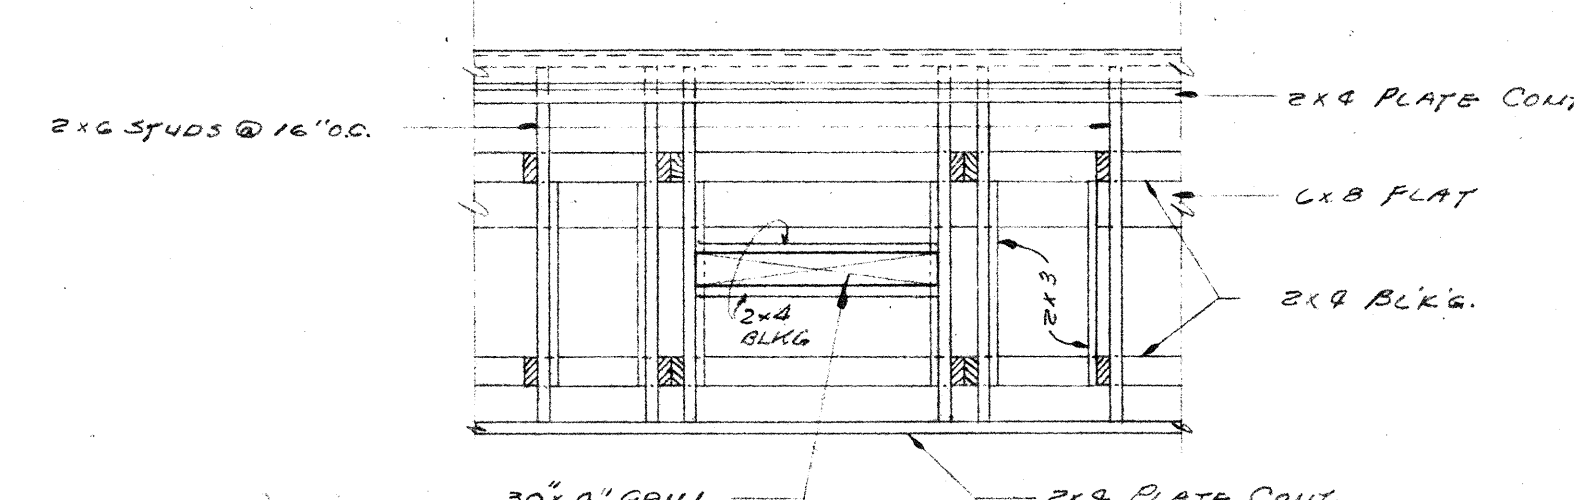

ELEVATION 1
ELEVATION AT EACH GRILL
1/2" x 1'-0"

Remarks

Revisions

Engineers

Approval

AUSTIN FIELD & IRY
2311 WEST THIRD STREET • LOS ANGELES 5, CALIFORNIA • DUNKIRK 8-1326

SECTIONS & DETAILS
ST. EDMUNDS EPISCOPAL CHURCH
SAN MARINO, CALIF.

DATE: AUG-51
COM: 1061
SHEET NUMBER: 58