


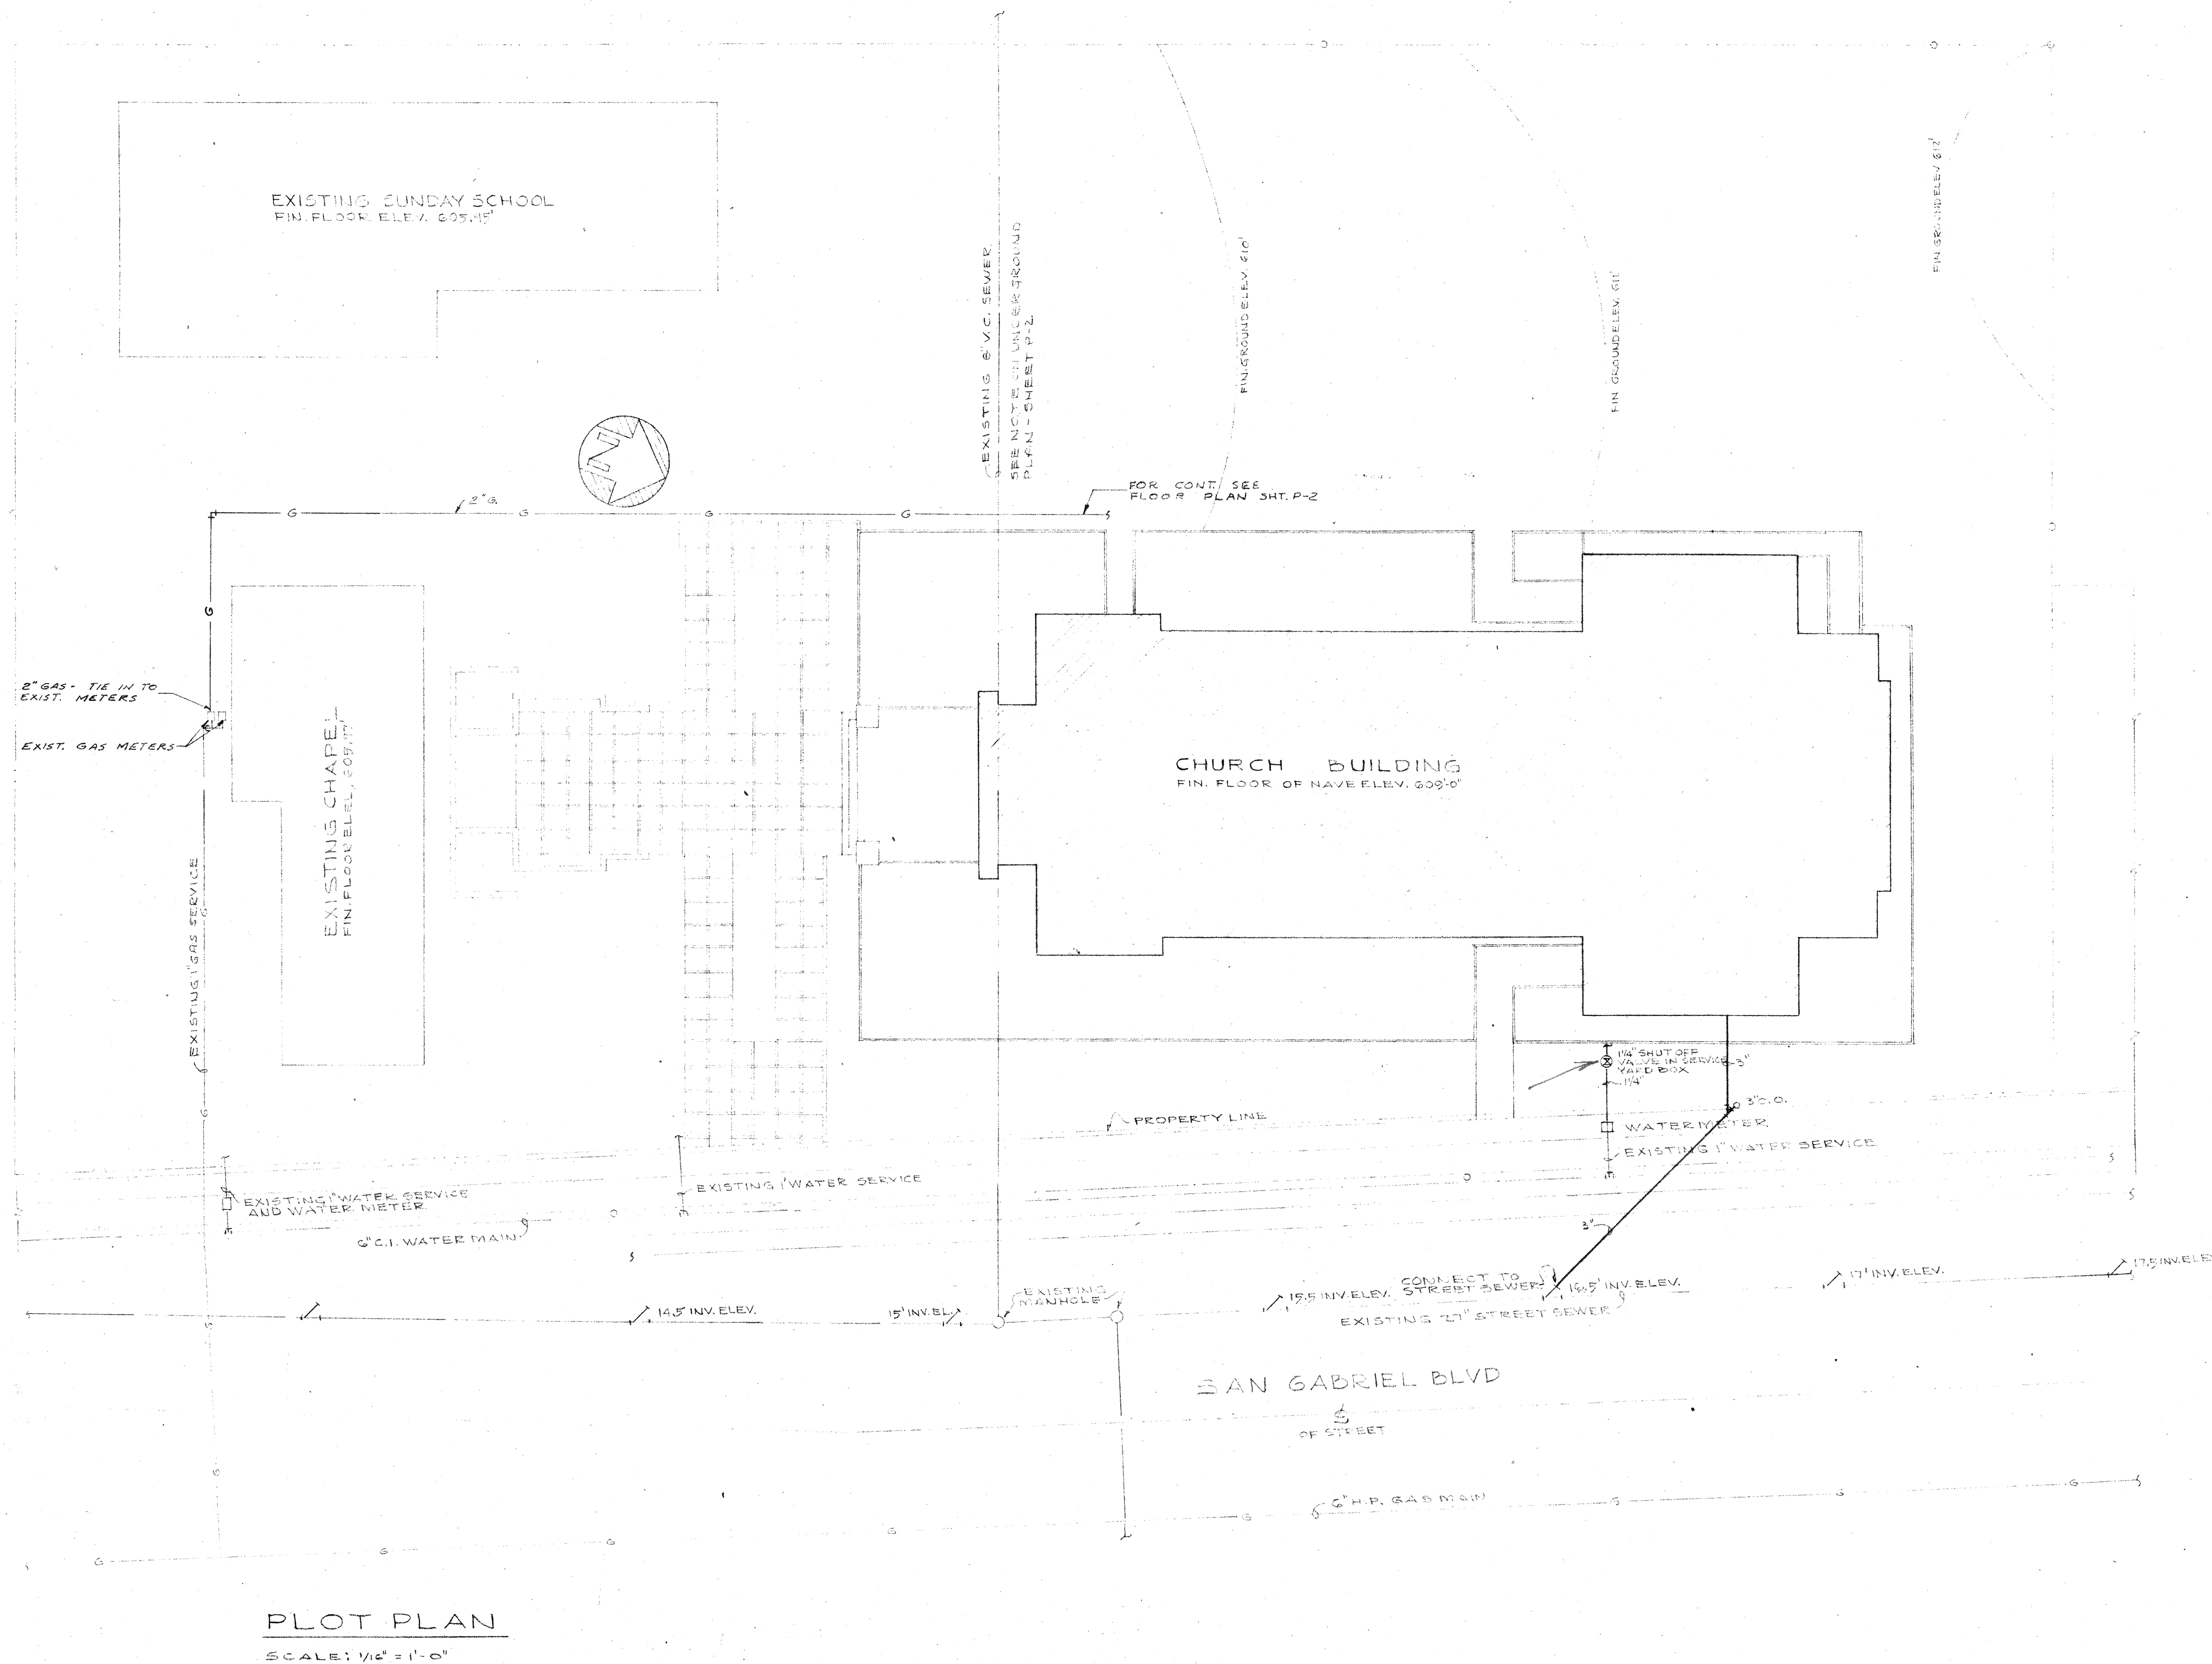

SCHEDULE OF PLUMBING FIXTURE CONNECTIONS							
FIXTURES	ABBR.	WASTE	TRAP	VENT	C.W.	H.W.	REMARKS
WATER CLOSET	W.C.	4"		2 3/4"	1/2"		FLUSH TANK
LAVATORY	L	2"	1 1/2"	1 1/2"	1/2"		
LAVABO		2"	1 1/2"				DRAIN TO DRY WELL
SERVICE SINK	S.S.	3"	2"	2"	3/4"	1/4"	
SINK	S	2"	1 1/2"	1 1/2"	3/4"	1/4"	
HOSE BIBB	H.B.				3/4"		
FLOOR DRAIN	F.D.	2"	2"	1 1/2"			
AREA DRAIN	A.D.	3"	3"				

LEGEND

— S & W	SEWER OR WASTE PIPING
— S	EXISTING SEWER
— V	VENT PIPING
— C.W.	COLD WATER PIPING
— H.W.	HOT WATER PIPING
— G	GAS PIPING
V.T.R.	VENT THRU ROOF
C.O.	CLEAN OUT
O.H.	OVERHEAD
C.I.	CAST IRON
V.C.	VITRIFIED CLAY
C.B.	CATCH BASIN
G.V.	GATE VALVE
C.V.	CHECK VALVE
G.C.	GAS COCK
D.W.	DRY WELL
N.I.C.	NOT IN CONTRACT

PLOT PLAN
SCALE: 1/8" = 1'-0"

Remarks	Revisions	Engineers	Approvals	AUSTIN FIELD & IRY Architects 2311 WEST THIRD STREET • LOS ANGELES 5, CALIFORNIA • DUNKIRK 8-1326	PLUMBING - PLOT PLAN ST. EDMUND'S EPISCOPAL CHURCH SAN MARINO CALIF.	DATE: 2-10-76 COMD: JCG SHEET NUMBER: P-1
				DRAWN: E.A.S. ARCHITECT - LICENSE #		
				CHECKED:		