




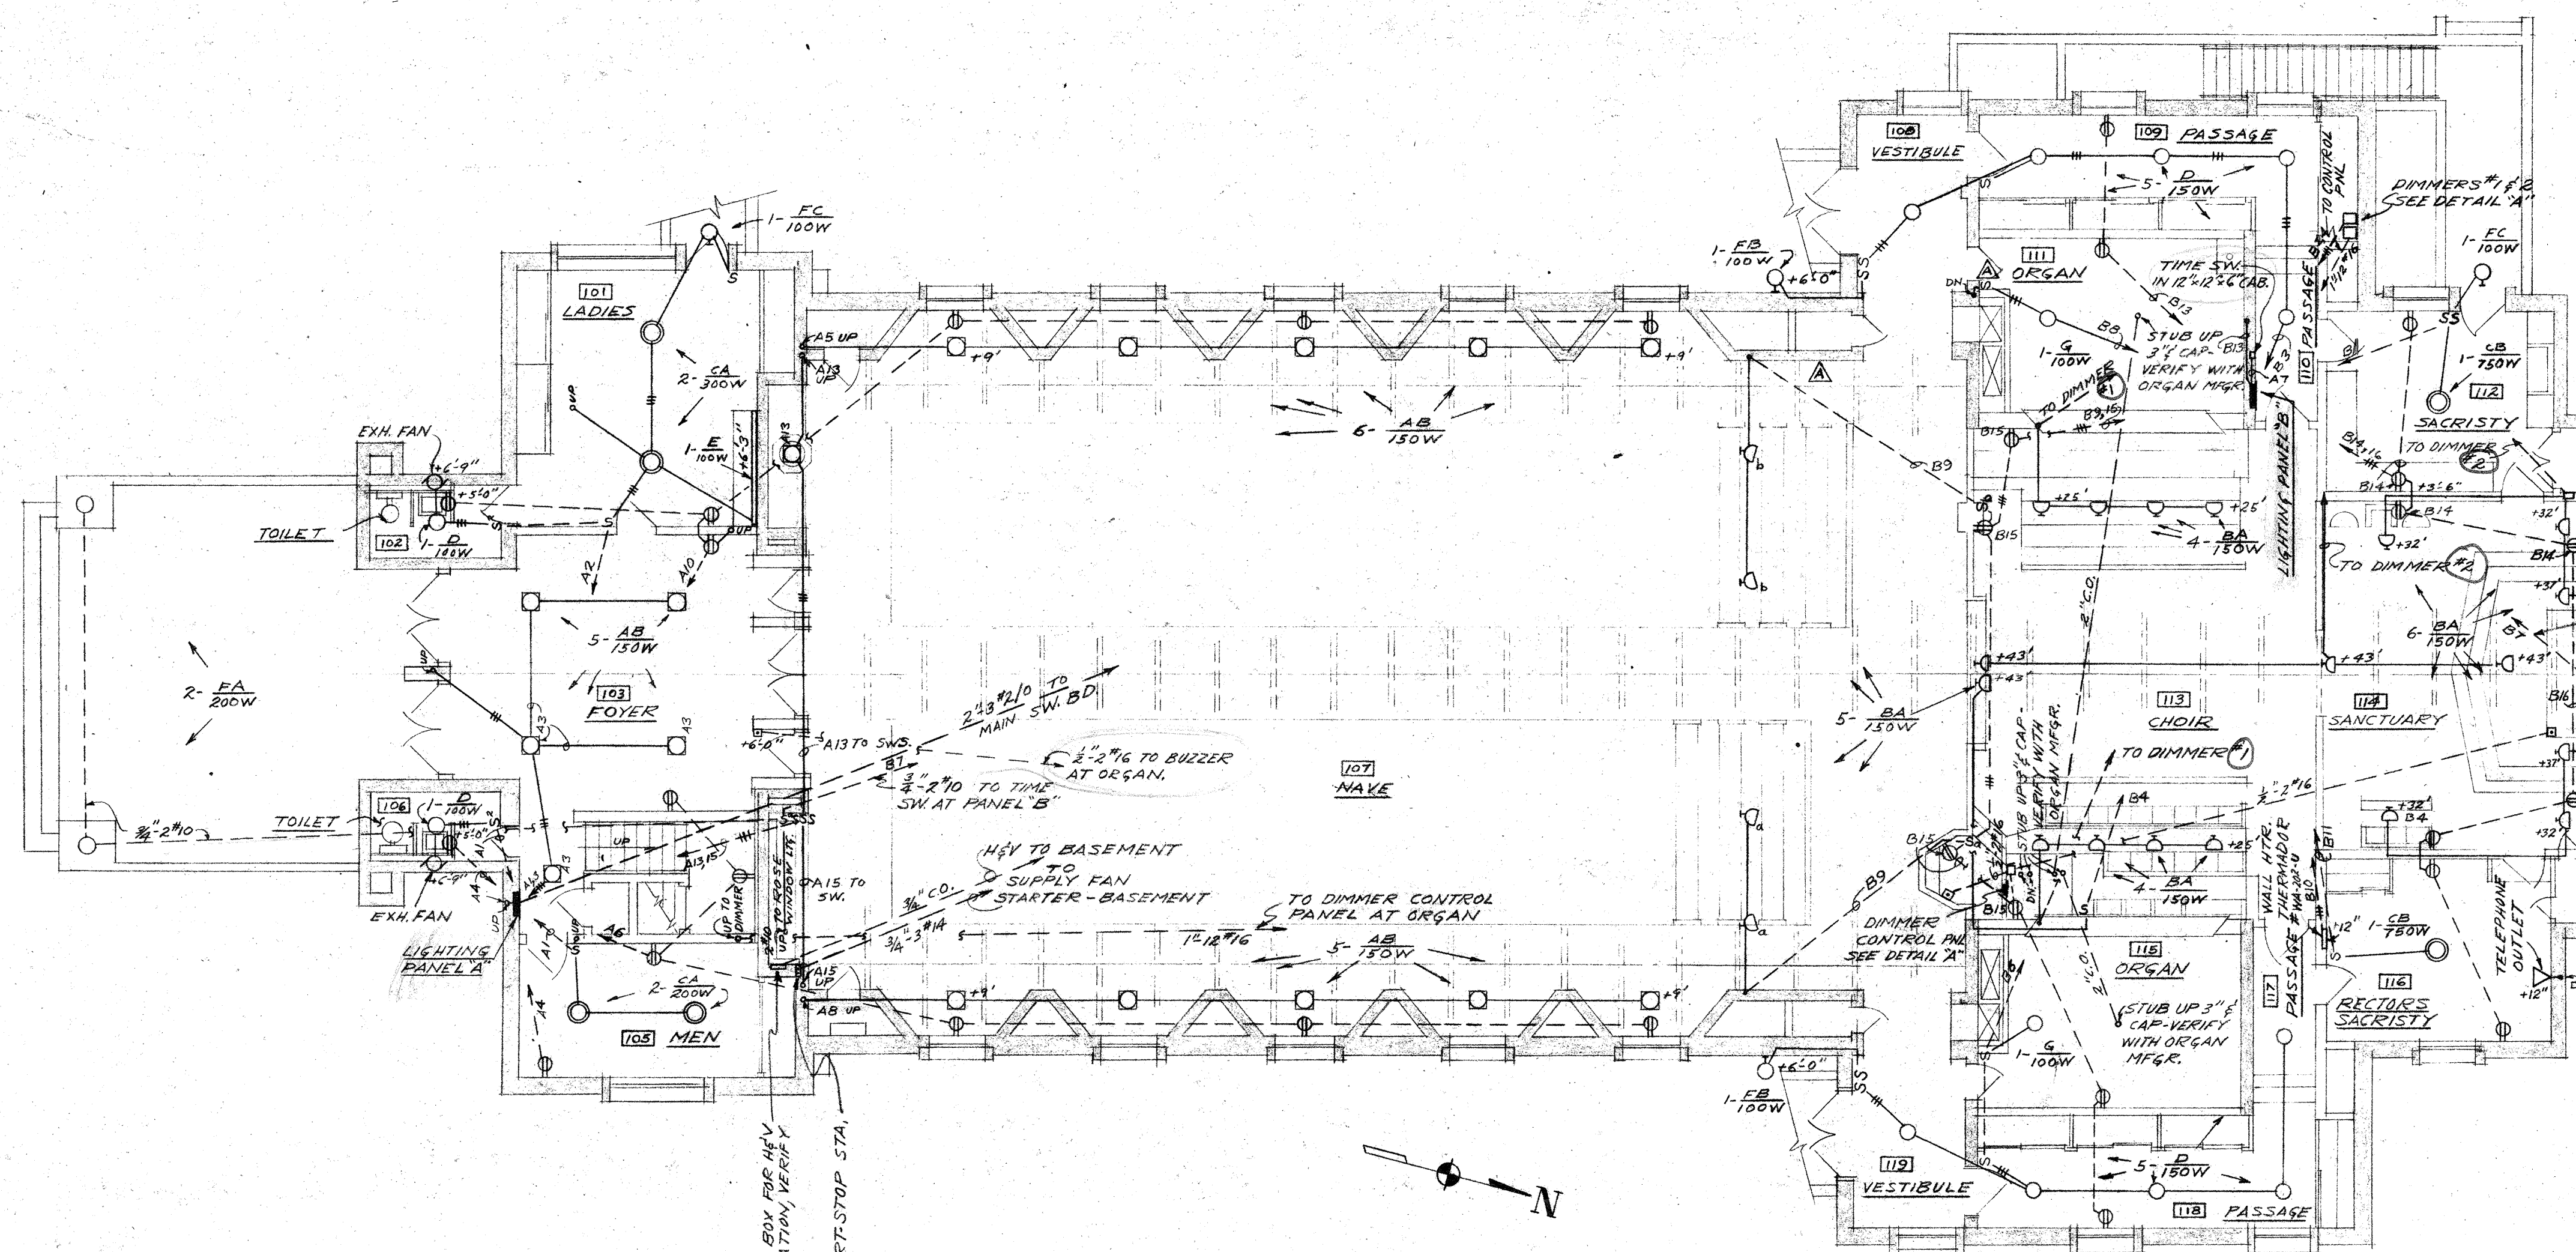

PLAN - MAIN FLOOR
SCALE: 1/8" = 1'-0"

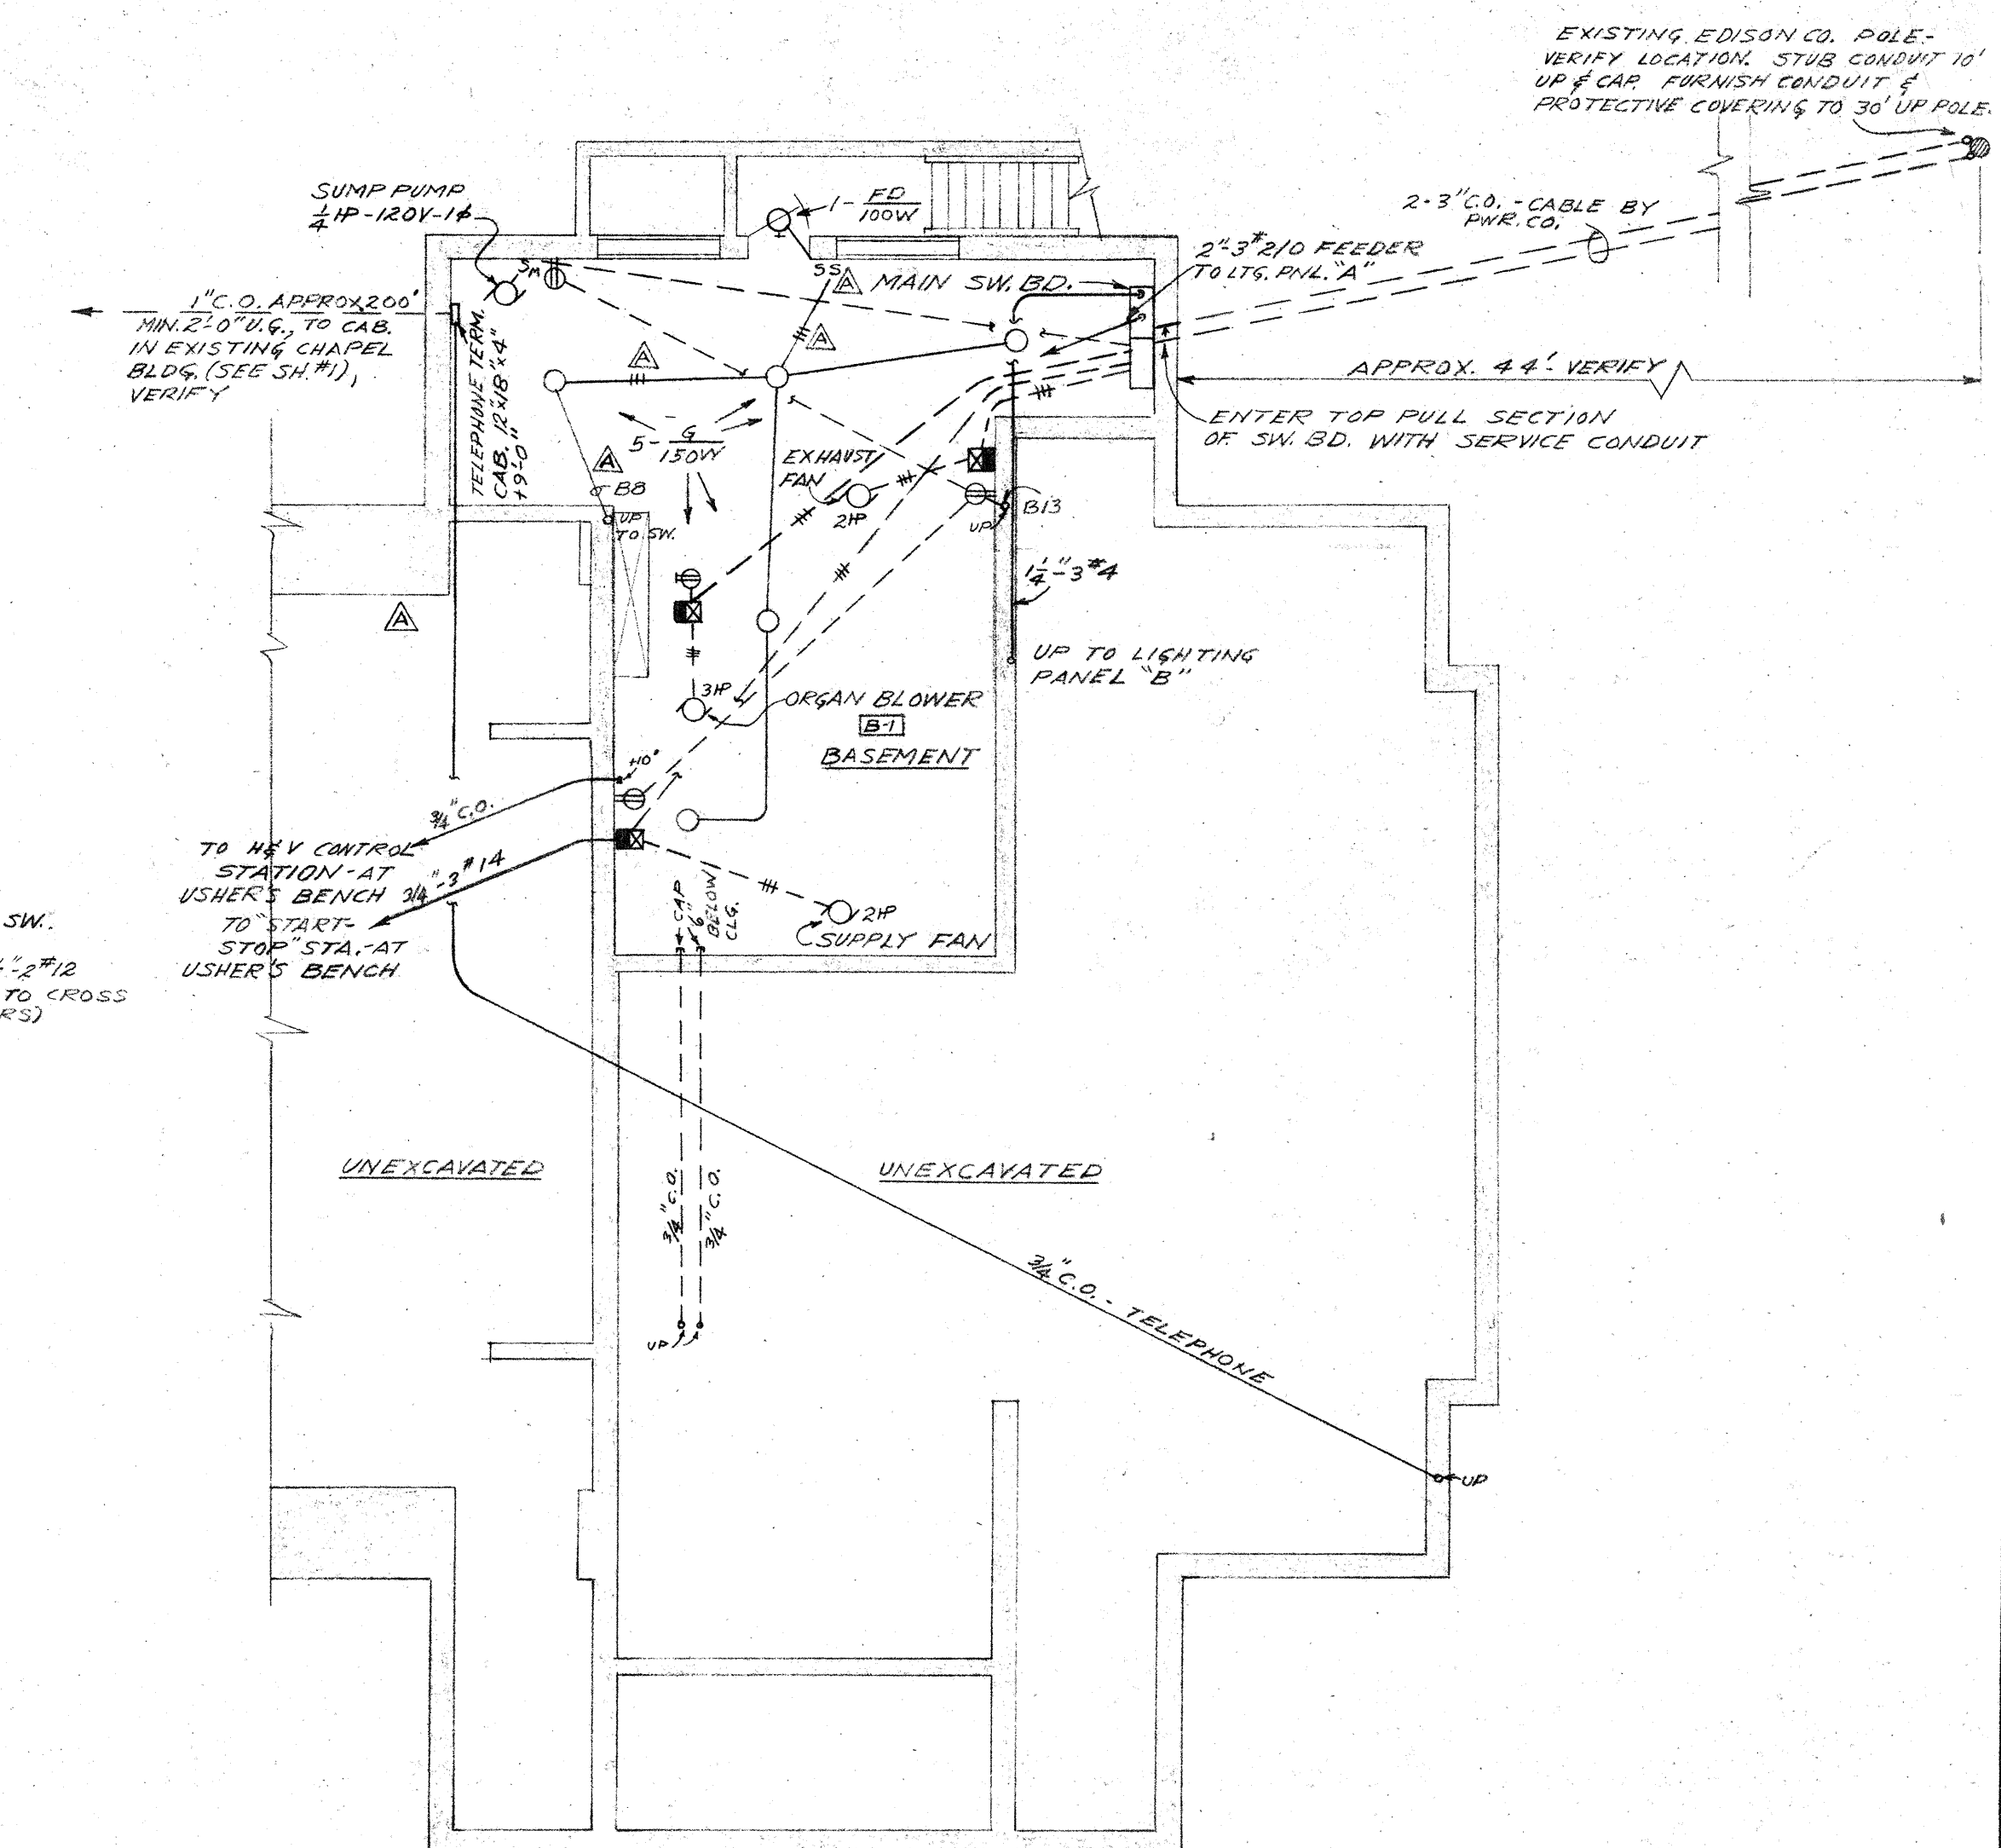

PLAN - BASEMENT
SCALE: 1/8" = 1'-0"

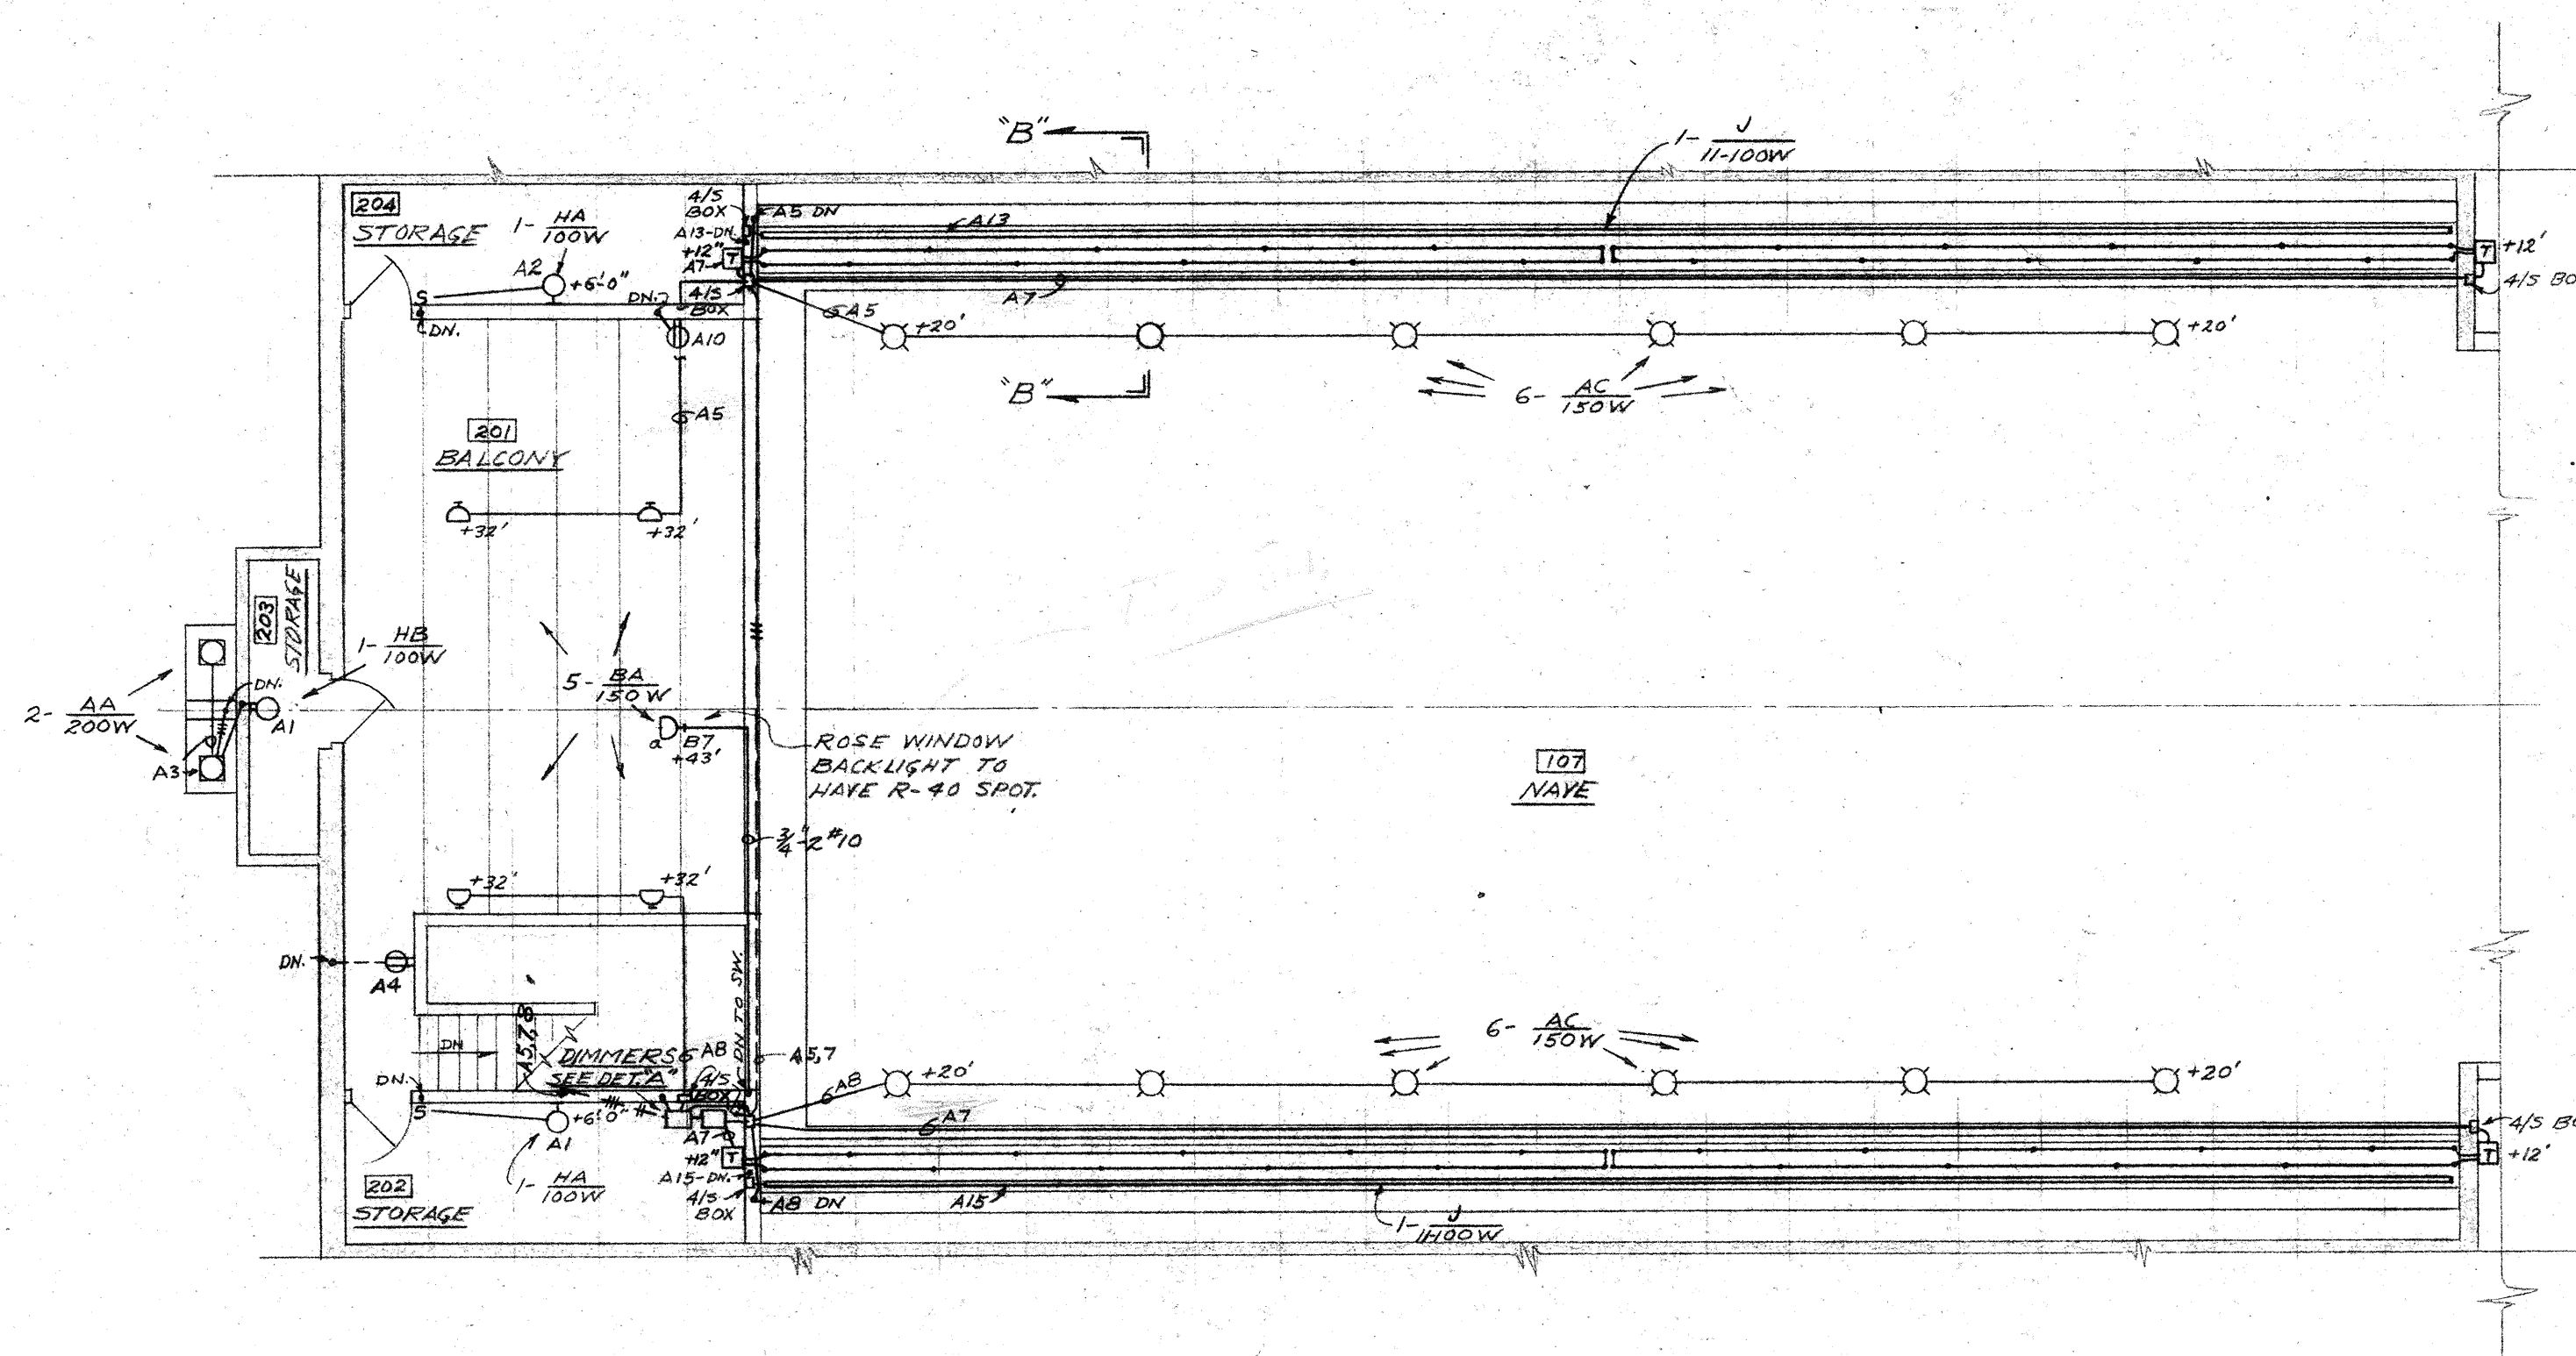

PLAN - BALCONY & LIGHT COVES
SCALE: 1/8" = 1'-0"

- NOTE:-
1. ALL SWITCHES IN NAVE & CHOIR AREAS TO BE MERCURY TYPE SPST 125V, 10A. WITH BROWN HANDLES.
 2. EXPOSED UNDERGROUND CONDUIT SHALL BE PAINTED WITH A COAT OF ASPHALTUM WHICH SHALL BE THOROUGHLY DRY BEFORE BACKFILLING.
 3. TWO FRONT L.T.G. STANDARDS, LT. AT ROSE WINDOW & CROSS TO BE ON TIME SW.
 4. ALL EQUIP. TO BE AS INDICATED OR EQUAL.

Remarks

Revisions

Engineers

Approvals

AUSTIN FIELD & IRY
architects
2311 WEST THIRD STREET • LOS ANGELES 5, CALIFORNIA • DUNKIRK 8-1326

ELECTRICAL PLAN
ST. EDMUNDS EPISCOPAL CHURCH
SAN MARINO CALIF.

DATE: 10-19-51
COMD: 1061
SHEET NUMBER: E-1