




FIXTURE TYPE	DESCRIPTION	QTY	BASE	WATTS
A A	RECESSED CEILING TYPE HOLOPLATE # F1769 CULV # 1 WITH WATER TIGHT GASKET	1	AED	200
A B	RECESSED CEILING TYPE VAGNEE-WOODRUFF # 2982F	1	AED	150
A C	RECESSED CEILING TYPE GOTHAM # 381	1	AED	150
B A	BULLET TYPE IND. REFLECTOR VAGNEE-WOODRUFF # 29122	1	E-40	150
B B	BULLET TYPE IND. REFLECTOR VAGNEE-WOODRUFF # 29500	1	SPOT	300
C A	CONCENTRIC RING FIXTURE VAGNEE-WOODRUFF # 28189/305	1	AED	200
C B	CONCENTRIC RING FIXTURE VAGNEE-WOODRUFF # 28189/1000	1	AED	750
D	CEILING SURFACE MTD DEBA TYPE SACOT-HOLLAND # LHM10	2	AED	75
E	FITTING ROOM FIXTURE VAGNEE-WOODRUFF # 30866	1	ARMURE	100
F A	LANTERN STANDARD VAGNEE-WOODRUFF # 30862	1	AED	200
F B	LANTERN - BRACKET VAGNEE-WOODRUFF # 30862	1	AED	150
F C	LANTERN - BRACKET VAGNEE-WOODRUFF # 30864	1	AED	150
F D	W.P. BRACKET FIXTURE HOLOPLATE # 840	1	AED	100
G	STANDARD DOOR BLA SACOT-HOLLAND # 81406	1	AED	150
H A	PORCELAIN REC. W/PULL SWITCH ALBAX # AL 8140	1	AED	100
H B	PORCELAIN REC. W/PULL SWITCH ALBAX # AL 8140	1	AED	100
J	STRIP LIGHTING 30-DARK BLUE COLOR VAGNEE-WOODRUFF # 30865	11	RUNNER	100

ELECTRICAL SYMBOLS

CONDUIT IN CEILING OR IN WALL
(2" x 12" UNLESS NOTED)
3" x 12"
4" x 12", ETC.
CONDUIT CONCEALED IN FLOOR
HOLE END TO PANELBOARDED
LIGHTING PANEL
SWITCH BOARDS
COMBINATION MOTOR STARTER
CEILING LIGHT OUTLET - SURFACE MOUNTED
RECESSED CEILING LIGHT
RECESSED CEILING LIGHT W/ LOUVERES
CONCENTRIC RING FIXTURE
BRACKET LIGHTING OUTLET
BULLET TYPE REFLECTOR - IND. CEILING MTD.
COLD CATHODE STRIP LIGHTING
2500A 120 MA W/ CATHODE FITTINGS
DOUBLE CONVENIENCE OUTLET
MOTOR - BY OTHERS
WALL SWITCH - SINGLE POLE, LUTER (A) REDUCED CONTROL
MOTOR CONTROL SW. - TRUMBELL TYPE "TT"
WALL SWITCH DOUBLE POLE
PUSH SWITCH - THREE WAY
PUSH BUTTON (FOR BUTTER)
FUSE
AUXILIARY CONTACT START-STOP PUSH BUTTON STATION-PUSH MOUNTED
+ HEIGHT ABOVE FINISHED FLOOR

CIRC. BREAKER NO.		USE		WATTS	
NBR	AMPS POLES	OUTL		PLA PLB	
1	15 1	6	MEN'S AREA, CLOSETS	900	
2	15 1	7	WOMEN'S AREA, CLOSETS	1200	
3	15 1	6	LOBBY & ENTRANCE	1150	
4	10 1	3 REC	ALTH'S AREA	540	
5	20 1	10	DIMMER #5 (WEST HALL)	1850	
6	20 1	6 REC	MEN'S AREA & EAST HALL	1080	
7	20 1	4	DIMMER #4 (DOVE LITG)	2000	
8	20 1	10	DIMMER #5 (EAST HALL)	1850	
9	20 1		SPARE	1200	
10	20 1	7 REC	WOMEN'S AREA & WEST HALL	1260	
11	20 1		SPARE	1000	
12	15 1		SPARE	1000	
13	15 1	12	DIMMER #6 (EAST HALL)	1800	
14	15 1		SPARE	1000	
15	15 1	11	DIMMER #6 (EAST HALL)	1800	
16	20 1		SPARE	1000	
TOTAL		WATTS	19,450	9140	9140

CIRC. BREAKER NO.	USE	WATTS	
NBR	AMPS POLES OUTL.	PLA PLB	
1	15 1 2	SACRISTY & PORCH	300
2	15 1 9	DIMMER #3 (DOVE & SACRISTY)	1800
3	15 1 5	W. PASSAGE, PORCH	900
4	15 1 9	DIMMER #1 (DOVE & HALLS)	1550
5	15 1	SPARE	1000
6	15 1 7	E. PASSAGE, PORCH & PORCH	1050
7	15 1 4	EXTERIOR CROSS, PORCH, & ROSE GRT	1050
8	15 1 7	W. ORGATE & BASEMENT	1050
9	15 1 4	DUST & LECTURE SPOTS	500
10	15 2 1	WALL HEATER	1000
11	15 1 1	PREST. SACRISTY	750
12	15 1	SPARE	1000
13	20 1 5	BASEMENT & W. PASSAGE REC	900
14	20 1 1	SACRISTY & W. SACRISTY REC	720
15	20 1 6	CHURCH & W. PASSAGE REC	1000
16	20 1 4	PREST. SACRISTY & E. SACRISTY REC	720
17	15 1	SPARE	1000
18	20 1	SPARE	1000
19	15 1	SPARE	1000
20	20 1	SPARE	1000
21	15 1	SPARE	1000
22	15 1	"	1000
23	15 1	"	1000
24	15 1	"	1000
TOTAL	WATTS	19,870	9170 9170

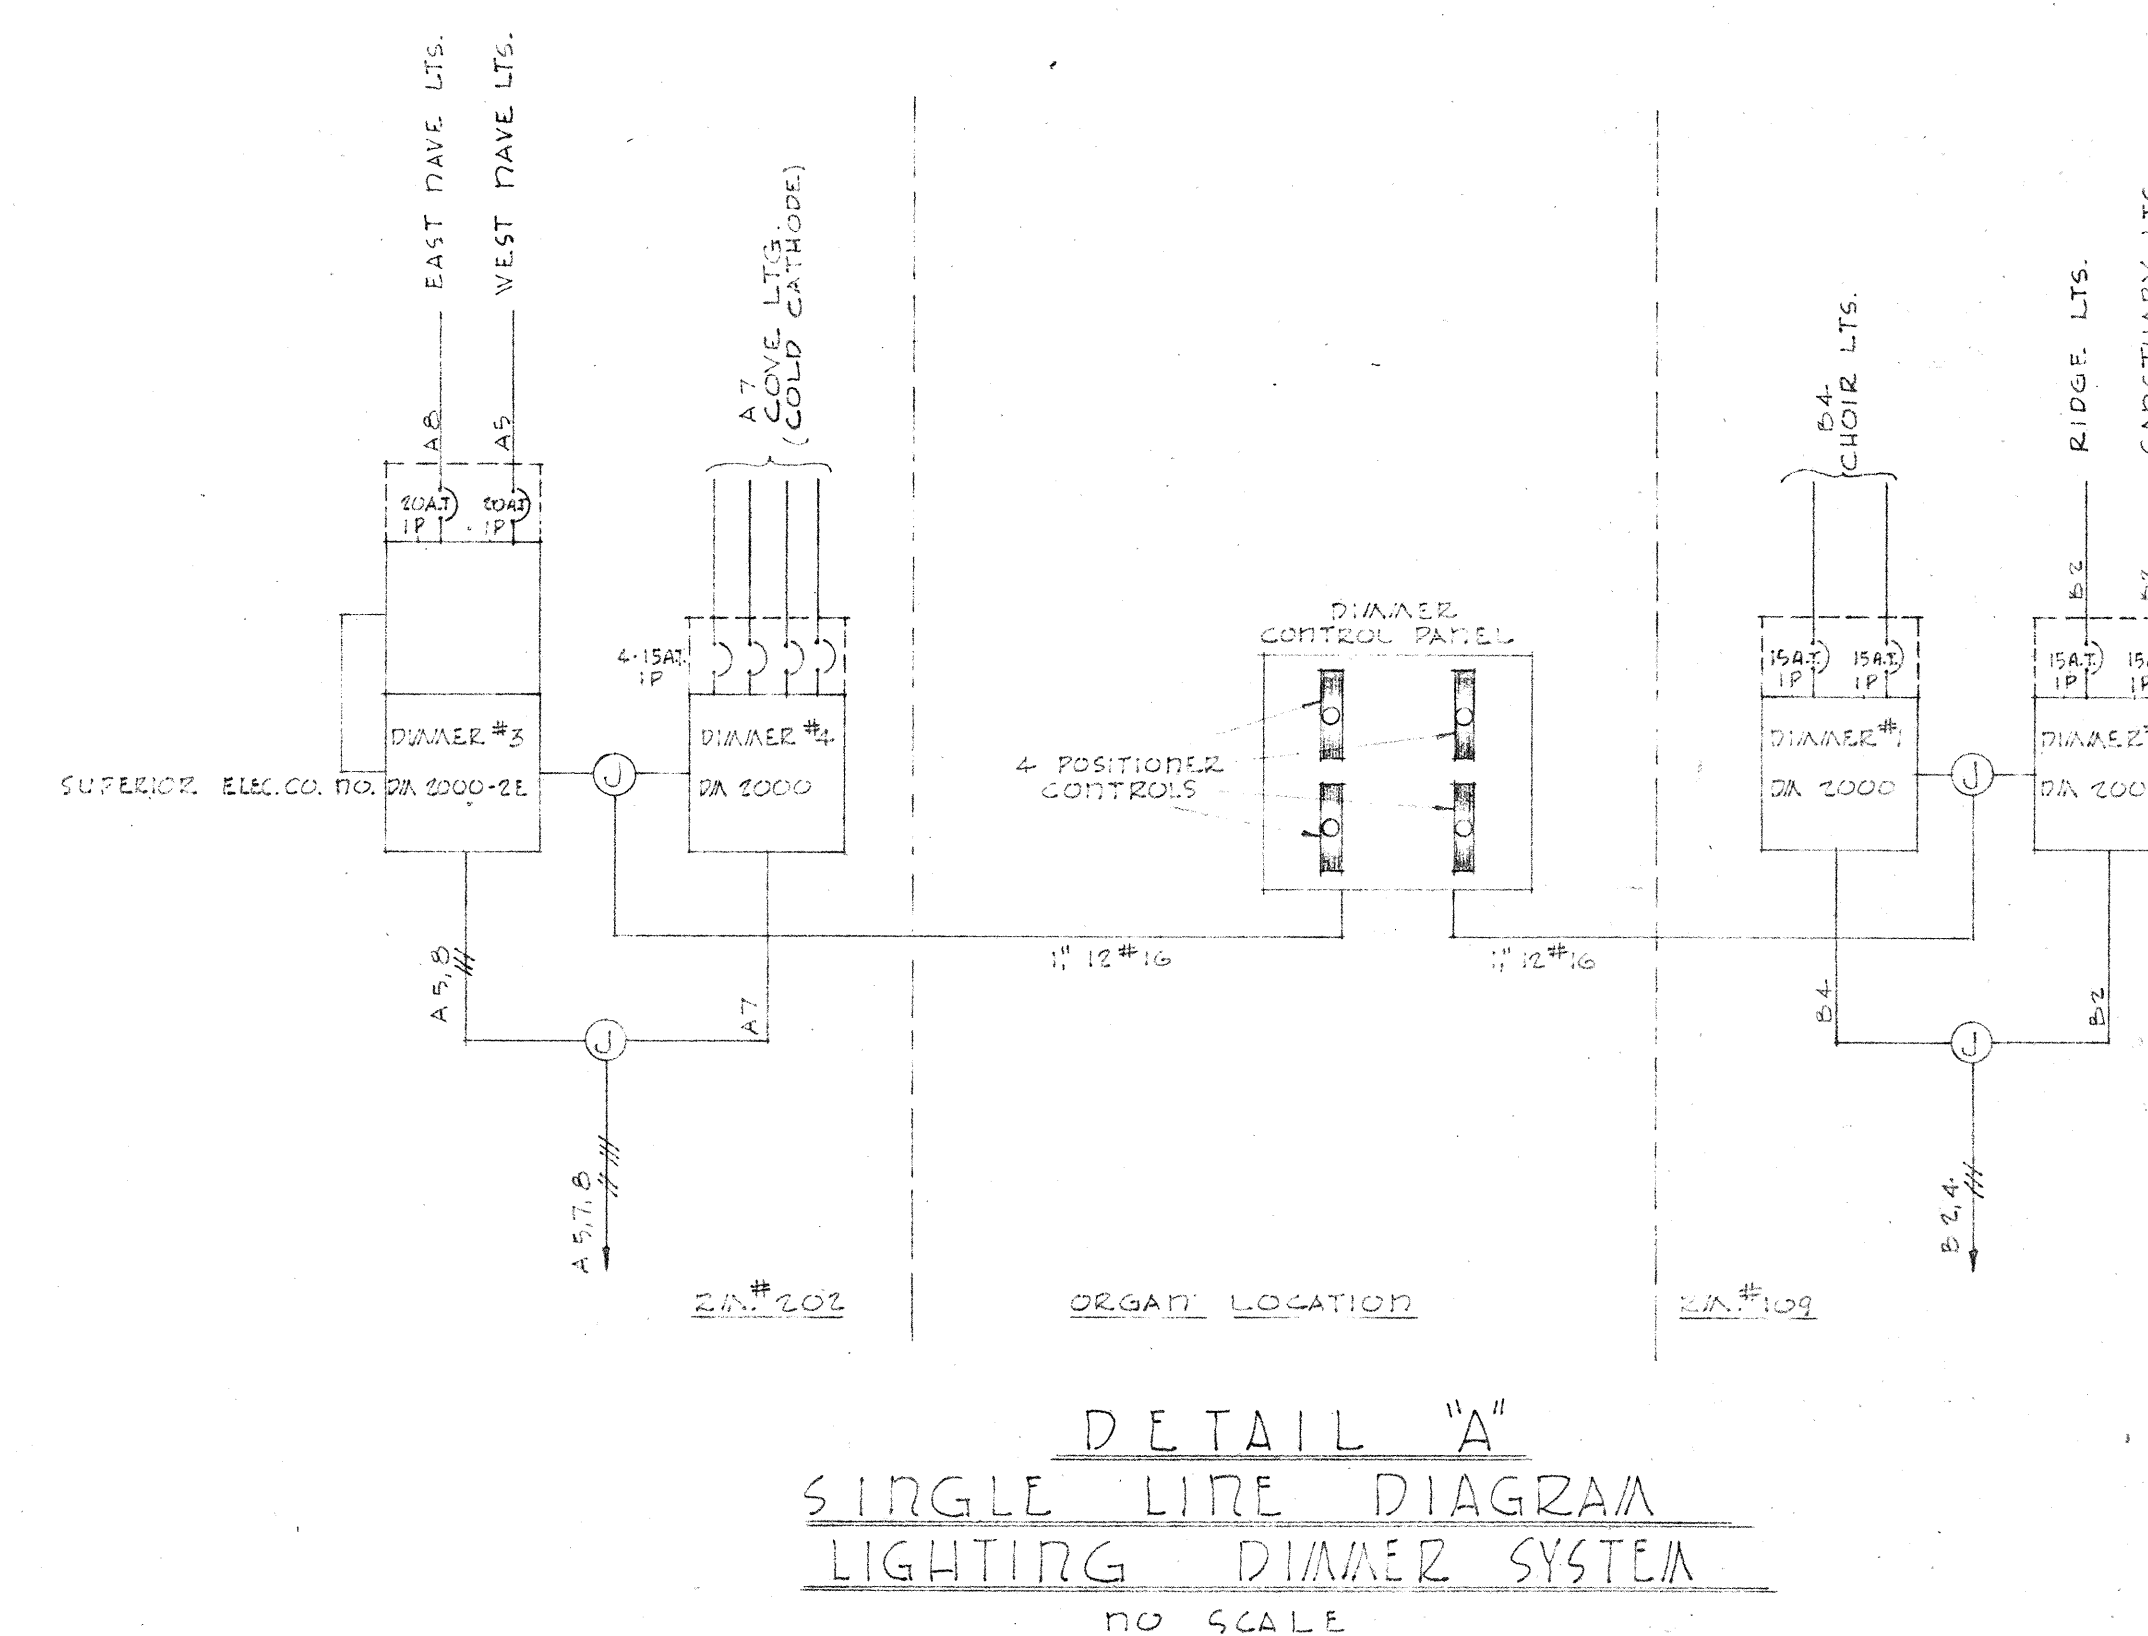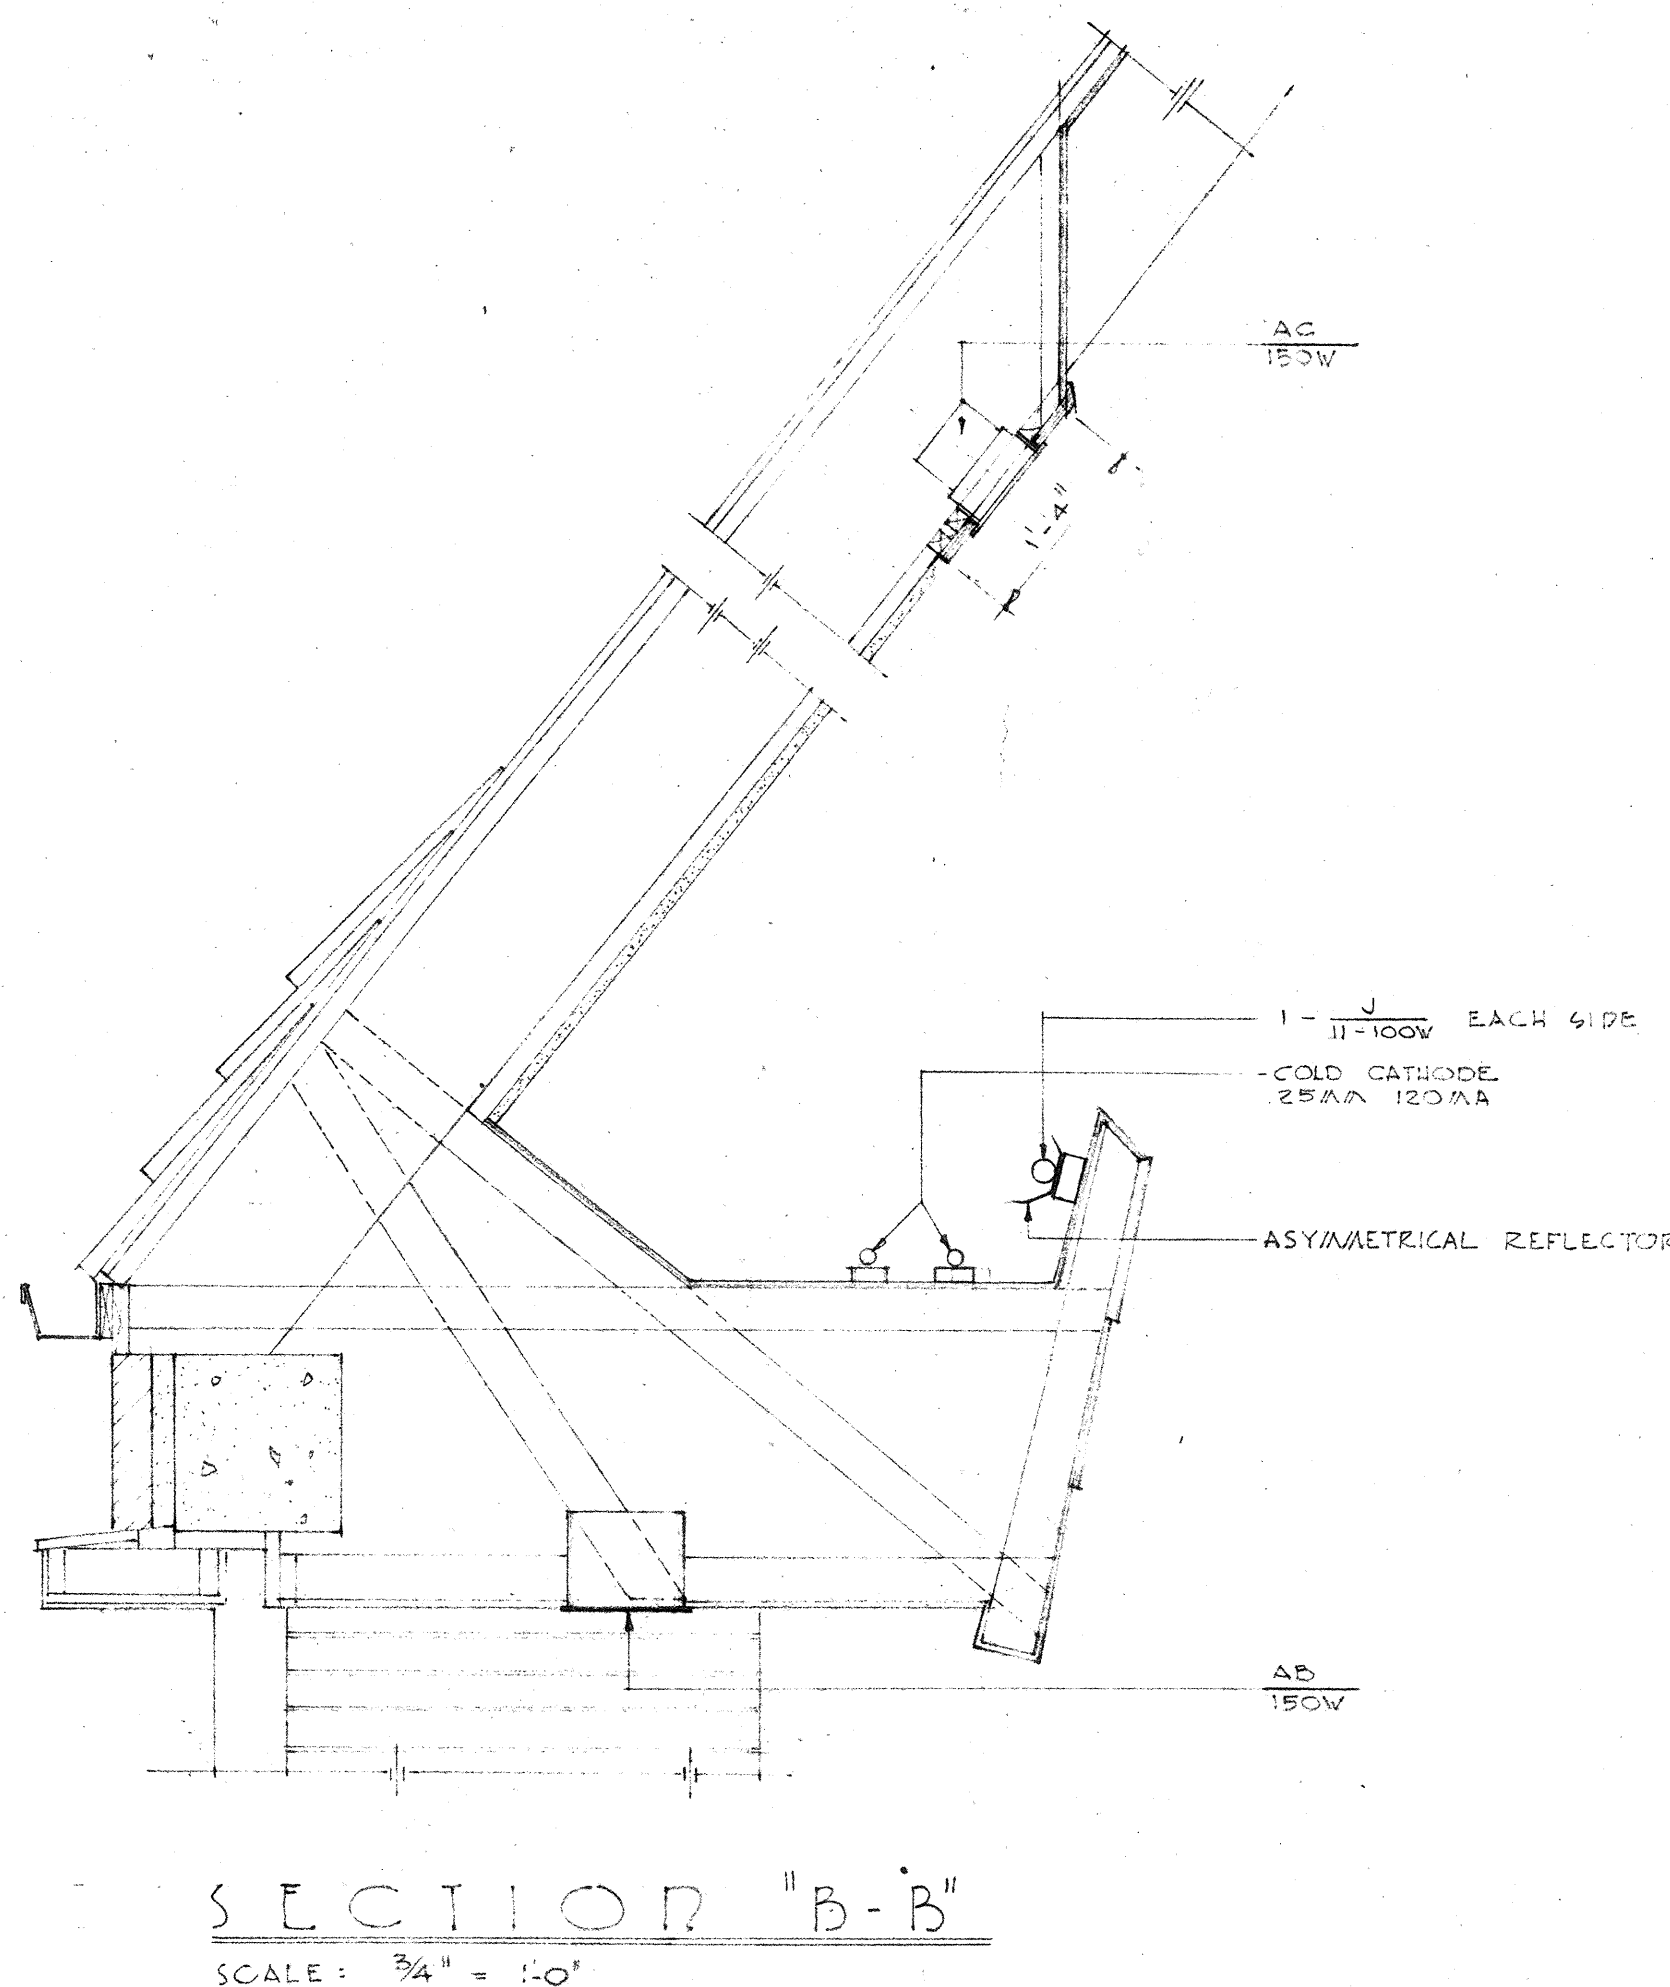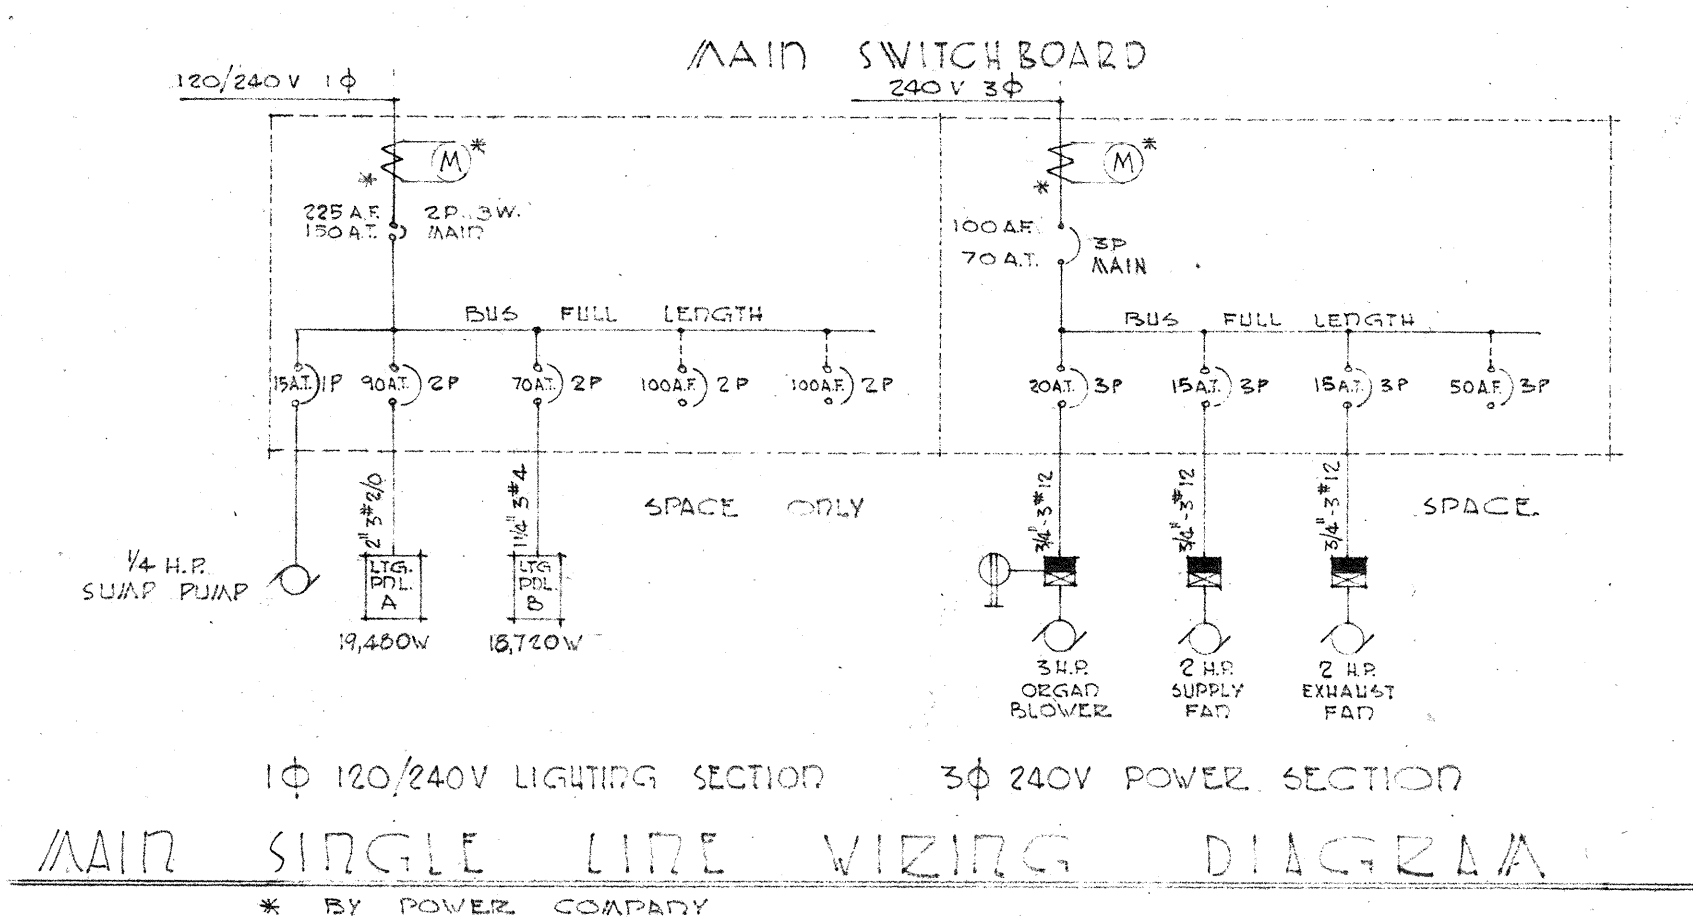

Remarks

Revisions

Engineers

Approvals

AUSTIN FIELD & IRY
Architects
2311 WEST THIRD STREET • LOS ANGELES 5, CALIFORNIA • DUNKIRK 8-1326

ELECTRICAL DETAILS & SCHEDULES
ST. EDMUNDS EPISCOPAL CHURCH
SAN MARINO, CALIF

DATE: 10/1/54
COMD:
SHEET NUMBER
E-2