

SEE 9901
ST. EDMUND'S
EPISC. CHURCH
RENOVATION
CONSTRUCTION
SET (As Approved)

RENOVATION PROJECT

FOR

SAINT EDMUNDS EPISCOPAL CHURCH

1175 SAN GABRIEL BLVD., SAN MARINO, CA., 91108-8048

Onuma & Associates

Architecture, Planning, Consulting
511 Mission Street
South Pasadena, CA 91030
tel 626.799.9920
fax 626.799.8260
e-mail: info@onuma.com


Consultants

RENOVATION PROJECT
FOR

SAINT EDMUND'S
EPISCOPAL CHURCH

1175 SAN GABRIEL BLVD., SAN MARINO, CA., 91108-8048

STAMPS

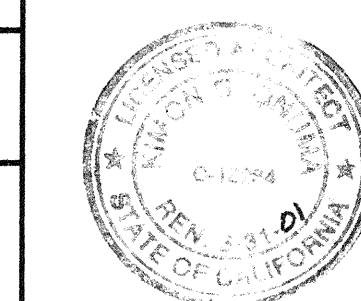

REVISIONS

DESCRIPTION	DATE BY

PROJECT NUMBER
2000

SCALE
AS NOTED

PRINTED
8/24/2000


TITLE

TITLE PAGE

SHEET

T0

1 OF 4 (45)

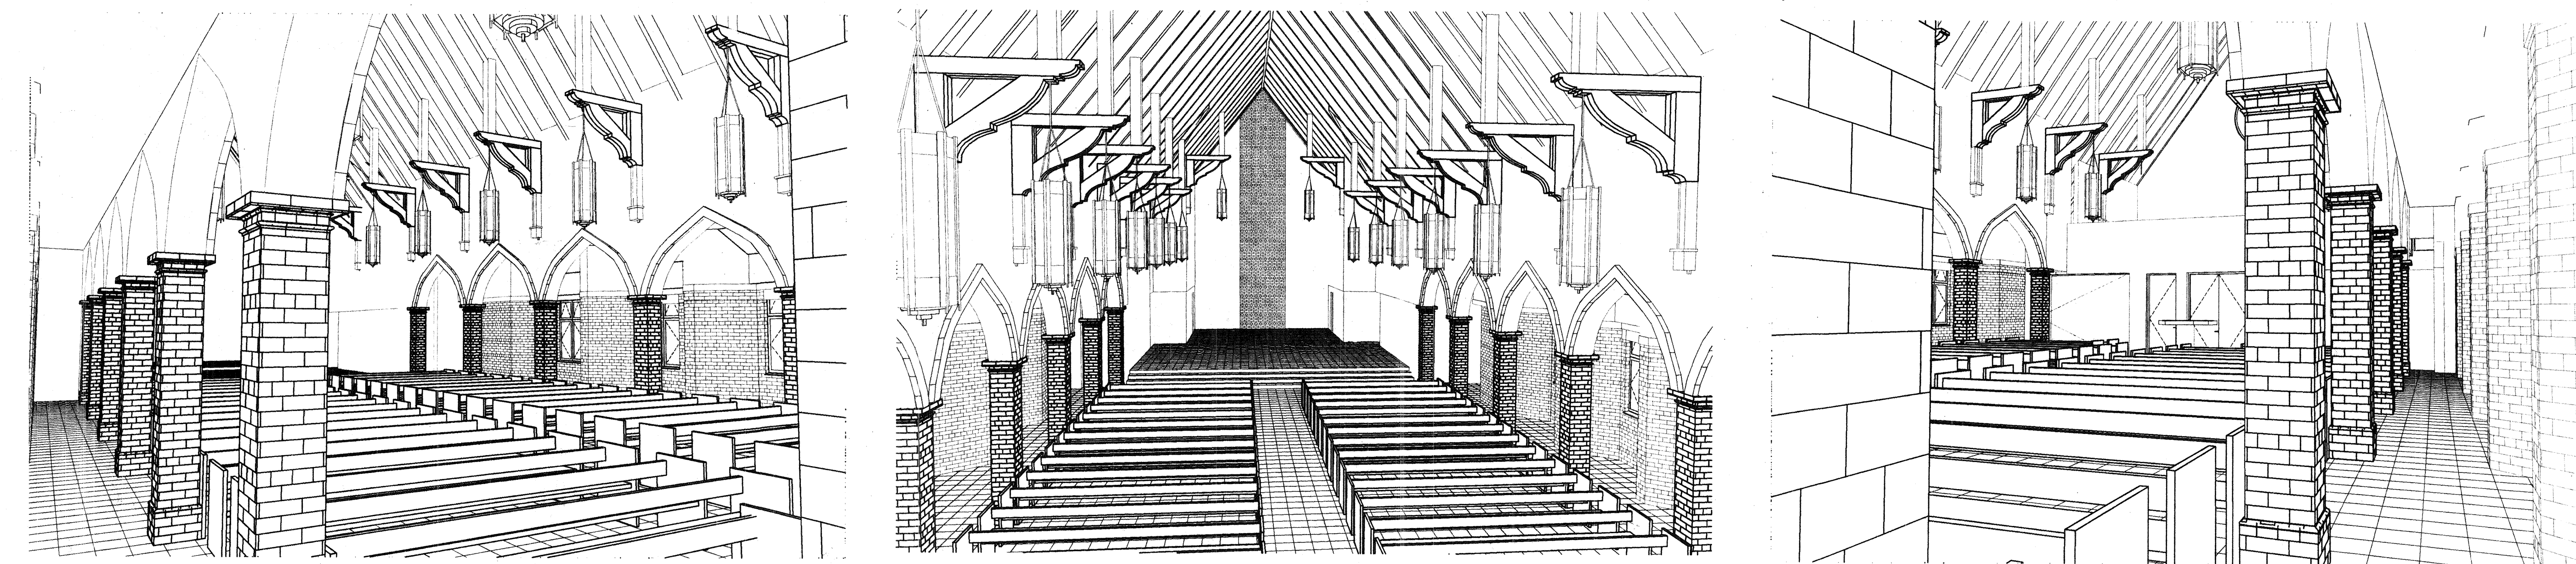

CONSULTING TEAM

Architectural

ONUMA & ASSOCIATES

Architecture, Planning, Consulting
511 Mission Street, South Pasadena, Ca 91030
Tel: (626) 799-9920 Fax: (626) 799-8260
e-mail: info@onuma.com

Structural

Kanda & Tso Associates

511 Mission Street,
South Pasadena, Ca 91030
Tel: (626) 441-1211
Fax: (626) 441-1011

Interior Design

Rhett Judice

2644 San Pasqual Street,
Pasadena, Ca 91107
Tel: (626) 449-7548
Fax: (626) 449-5817

Mechanical

Debibi & Roshanian, Inc.,


4741 Laurel Canyon Blvd.,
Suite 202,
North Hollywood, Ca 91607
Tel: (818) 980-0837
Fax: (818) 508-1251

Electrical

Randall Engineering

2908 Allesandro Street,
Los Angeles, Ca 90039
Tel: (323) 667-9081
Fax: (323) 667-9083

VICINITY MAP

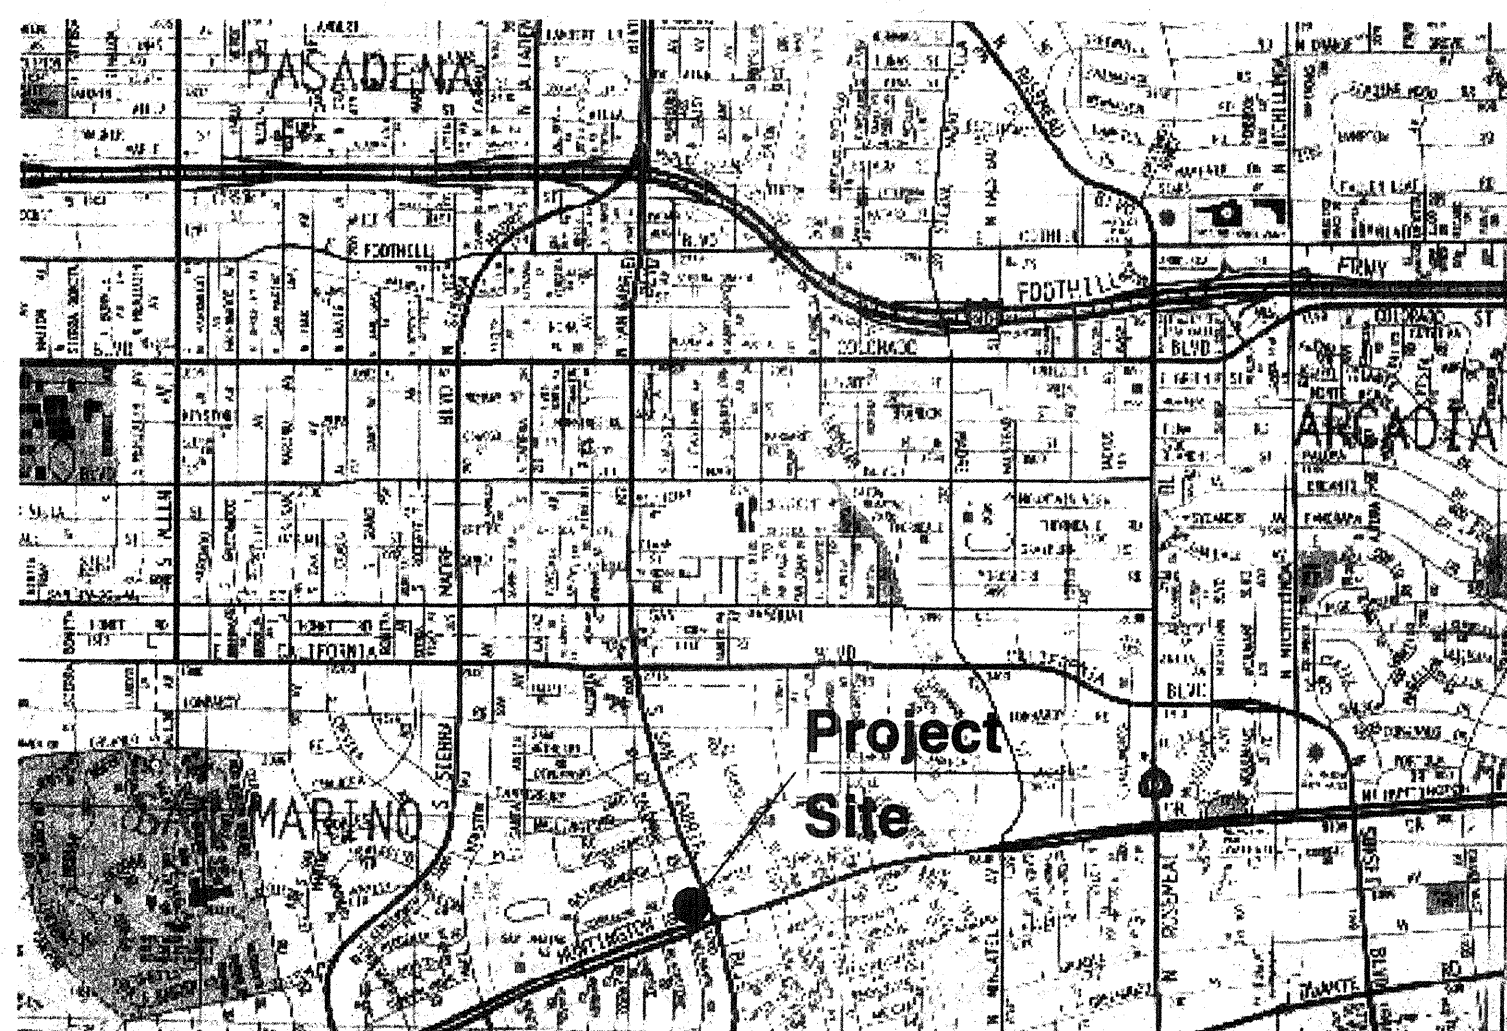

BUILDING DATA

Occupancy: **A-2.1**
Number of Stories: **1**
Building Heights: **45'**

Type of Construction:

Building - Type V - 1hr
**Structure - Concrete Foundation,
Masonry & Wood Frame**
Walls - Masonry & Wood Frame
Floor - Concrete
Roof - Wood Frame

One-Story Existing Building Area

1st floor 8,936 sf
Mezzanine/storage 989 sf
Basement 932 sf
Total: 9,957 sf
Allowable: 10,500 sf

INDEX OF DRAWINGS

Title Sheet
T0 1 OF 44
T1 2 OF 44
T2 3 OF 44

Title Sheet
General Notes
General Notes & Schedules

Structural

S1 23 OF 44 Foundation/First Floor Framing & details
S2 24 OF 44 New Interior Wall Elevations & Sections
S3 25 OF 44 Sections and Details

Mechanical

M-0.1 26 OF 44 Mechanical Specifications
M-1 27 OF 44 Equipment Schedule, Symbols & Abbreviations
M-2 28 OF 44 Mechanical Details
M-3 29 OF 44 Mechanical Details
M-4 30 OF 44 Mechanical Room Control Diagram
M-5 31 OF 44 Basement A/C Plan
M-6 32 OF 44 First Floor Plan
M-7 33 OF 44 First Floor A/C Plan
M-8 34 OF 44 Mechanical Forms

Plumbing

P-0.1 35 OF 44 Plumbing Specifications
P-1 36 OF 44 First Floor Plumbing Plan

Electrical

E-1 37 OF 44 Electrical Symbols & General Notes
E-2 38 OF 44 Single Line Diagram & Elevation
E-3 39 OF 44 Electrical Site Plan & Details
E-4 40 OF 44 Demolition Floor Plan & Details
E-5 41 OF 44 Lighting Floor Plan
E-6 42 OF 44 Communication Floor Plan
E-7 43 OF 44 Basement Power Plan & Demolition Plan
E-8 44 OF 44 Panel Schedules & Dimmer Plan "DP"
E-9 45 OF 45 SOUND SYSTEM & MOUNTING DETAILS

Architectural
A1 4 OF 44 Site Plan
A2 5 OF 44 Demolition Floor Plans
A3 6 OF 44 First & Storage Level Floor Plans
A4 7 OF 44 Basement & Reflected Ceiling Plans
A5 8 OF 44 Building Sections
A6 9 OF 44 Building Sections
A7 10 OF 44 Building Sections
A8 11 OF 44 Enlarge Toilet Plans & Interior Elevations
A9 12 OF 44 Enlarge Stair Plan & Details
A10 13 OF 44 Enlarge Ramps & Stair Plans & Details
A11 14 OF 44 Details
A12 15 OF 44 Details

The drawings and/or specifications and/or calculations for the items listed below have been prepared by other design professionals or consultants who are licensed and/or authorized to prepare such drawings in this state. These documents have been examined by me for design intent and have been found to meet the appropriate requirements of Title 24, California Code of Regulations and the project specifications prepared by me.

Interior Design

ID-1 16 OF 44 Arcade Bay Detail & Coved Millwork
ID-2 17 OF 44 Paneling, organ grill & lanterns
ID-3 18 OF 44 Wainscott & door design
ID-4 19 OF 44 Section of West wall Paneling Design
ID-5 20 OF 44 Narthex Doors Details
ID-6 21 OF 44 Floor Tile Plan
ID-7 22 OF 44 Floor and Wall Tile Bathrooms