
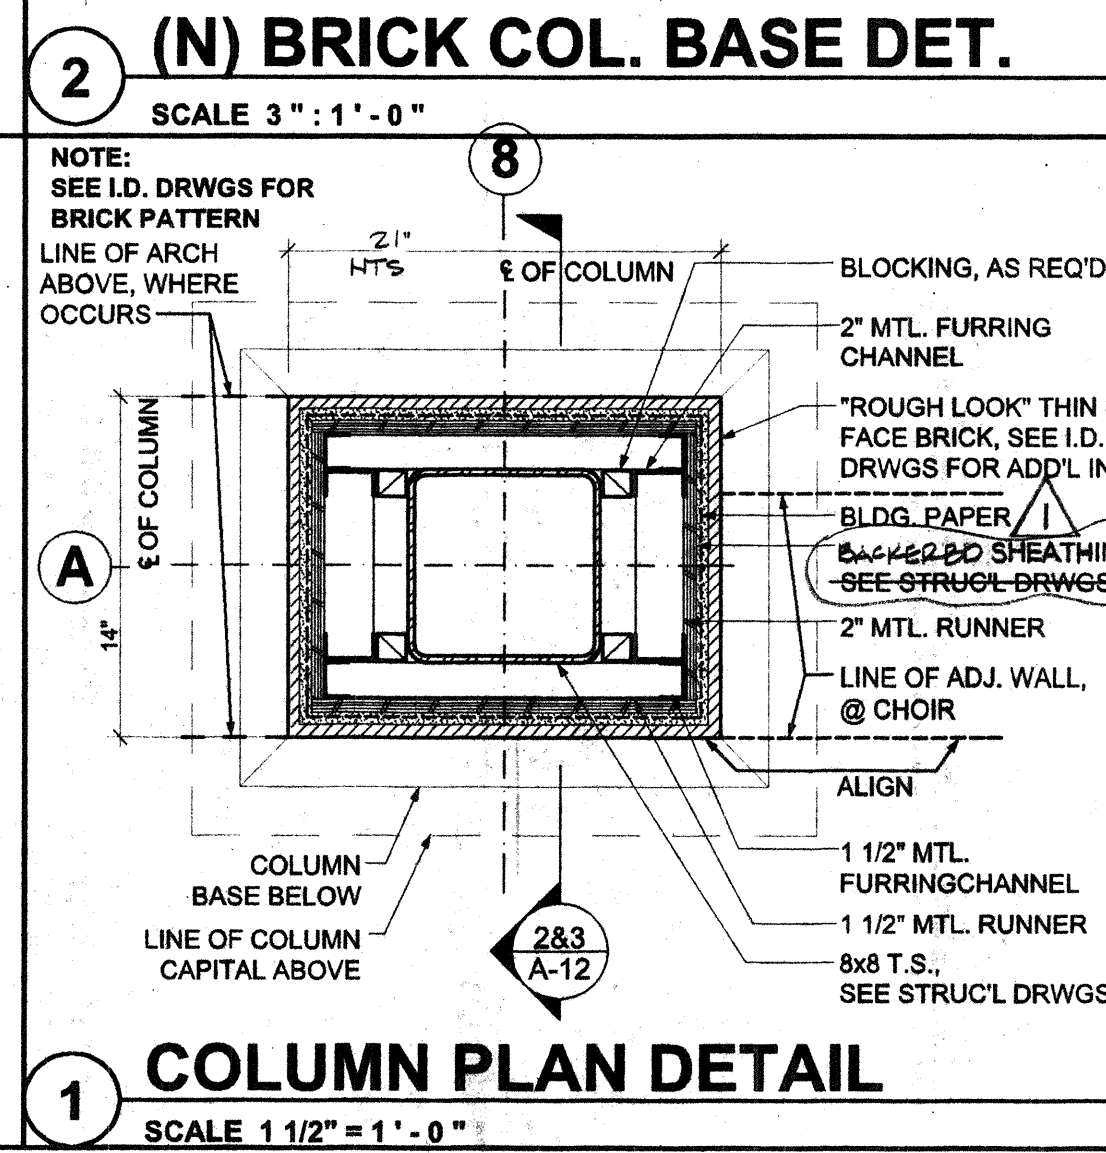
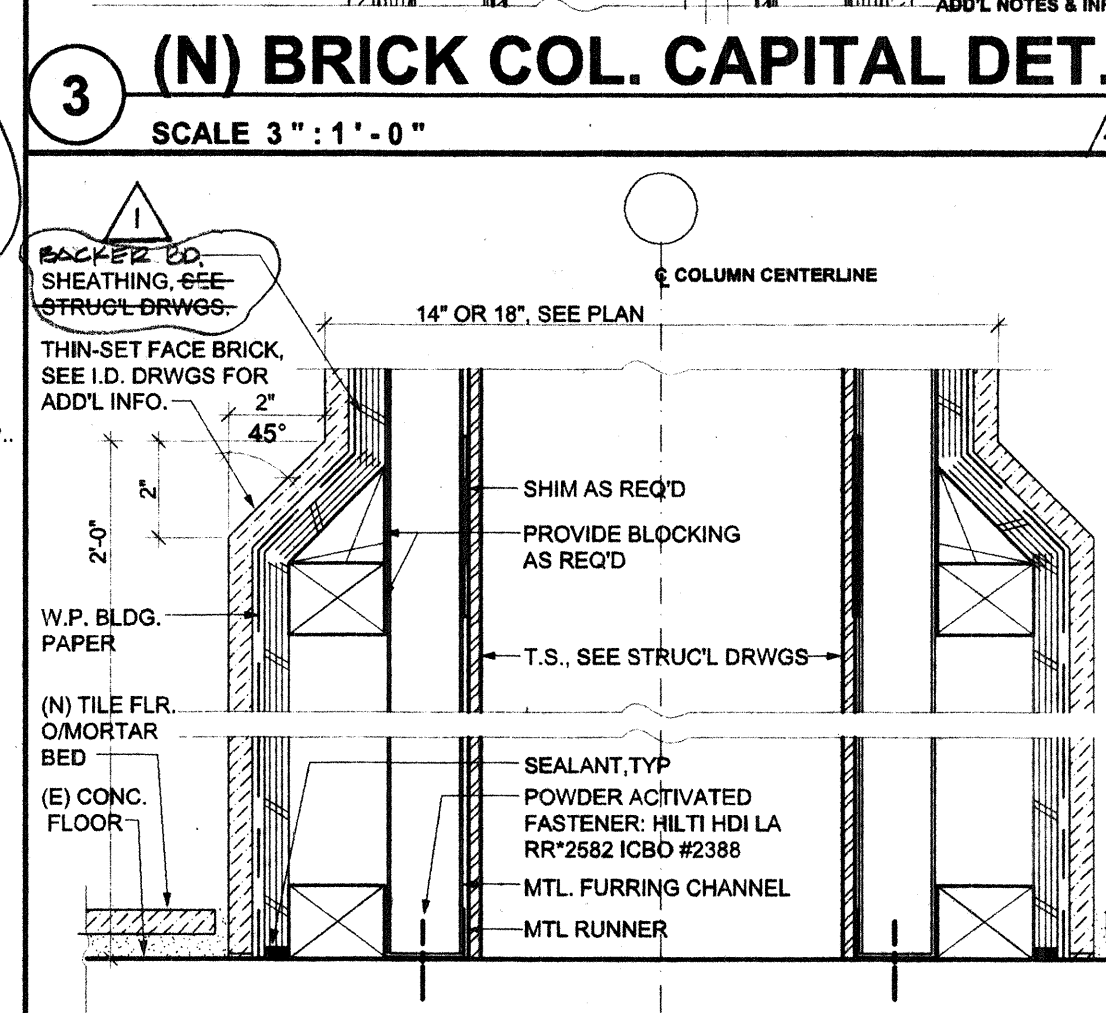
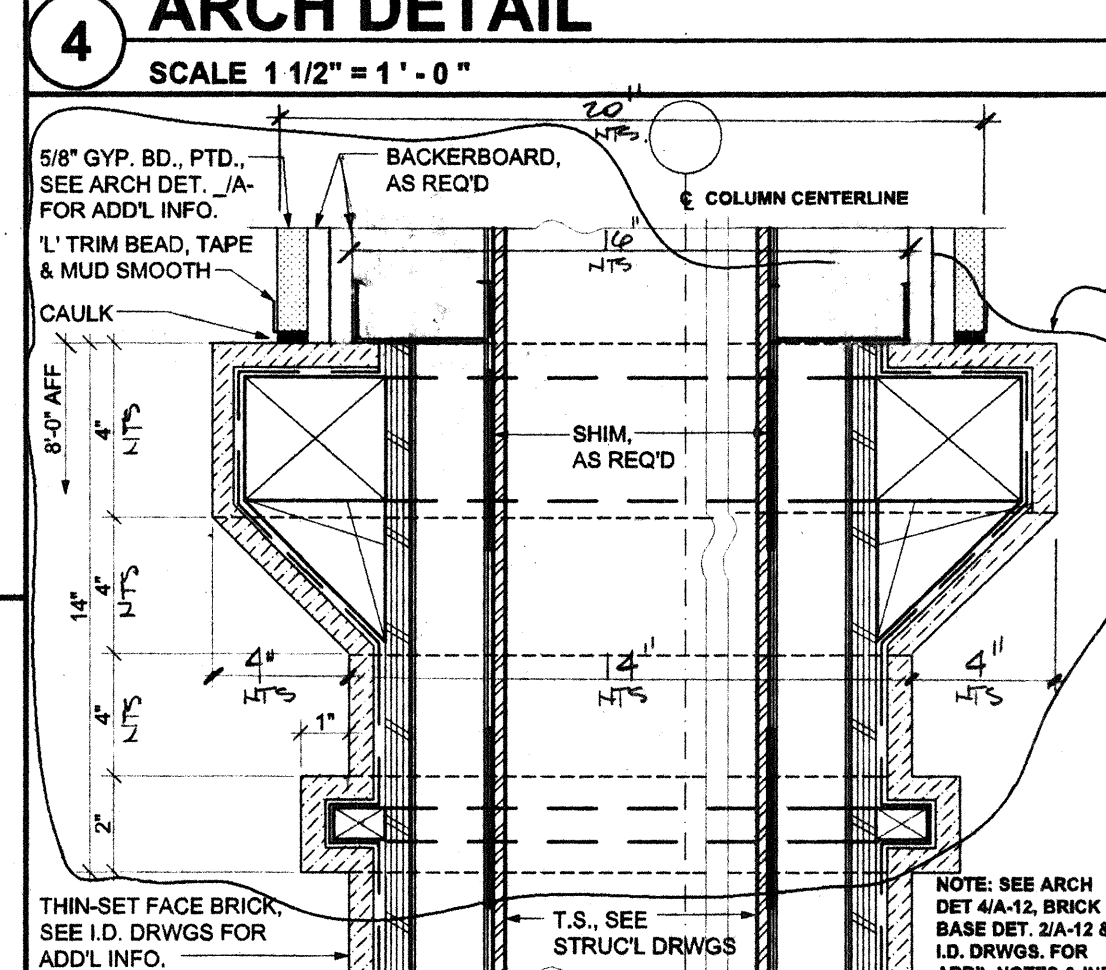
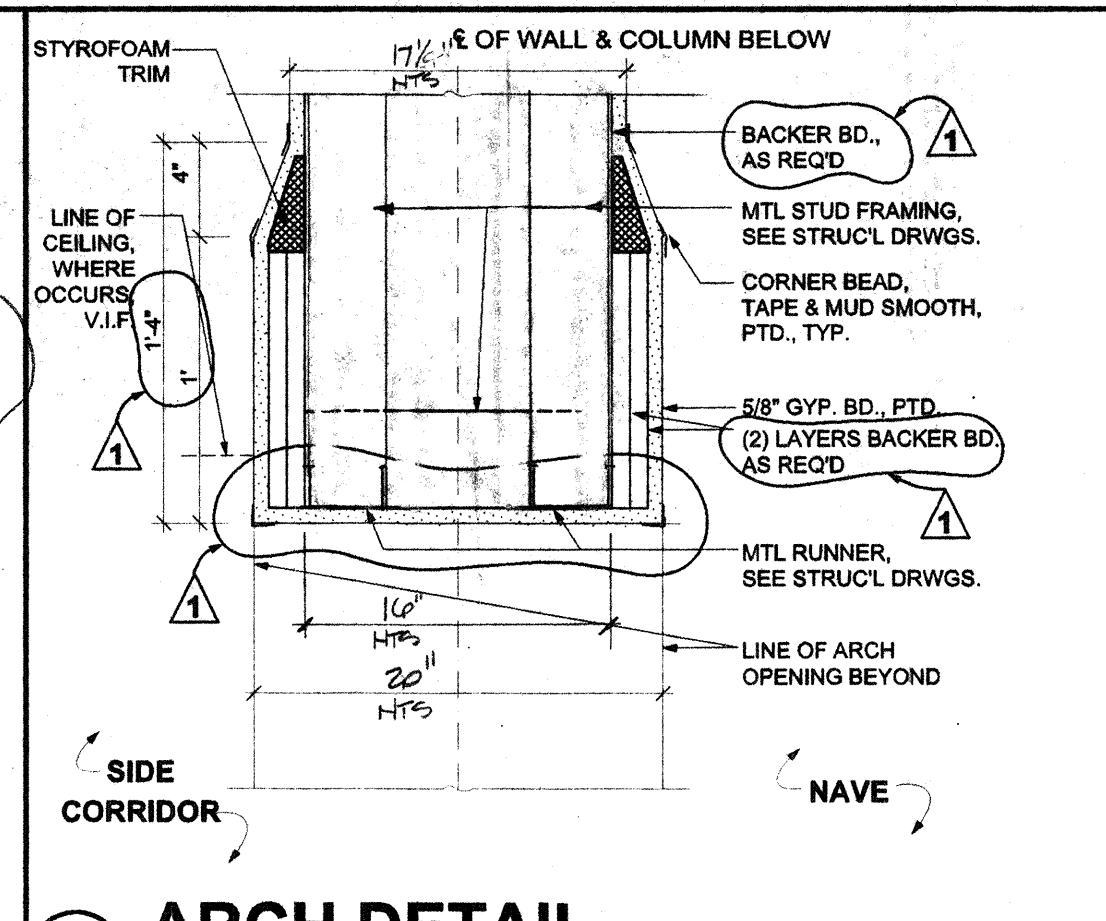
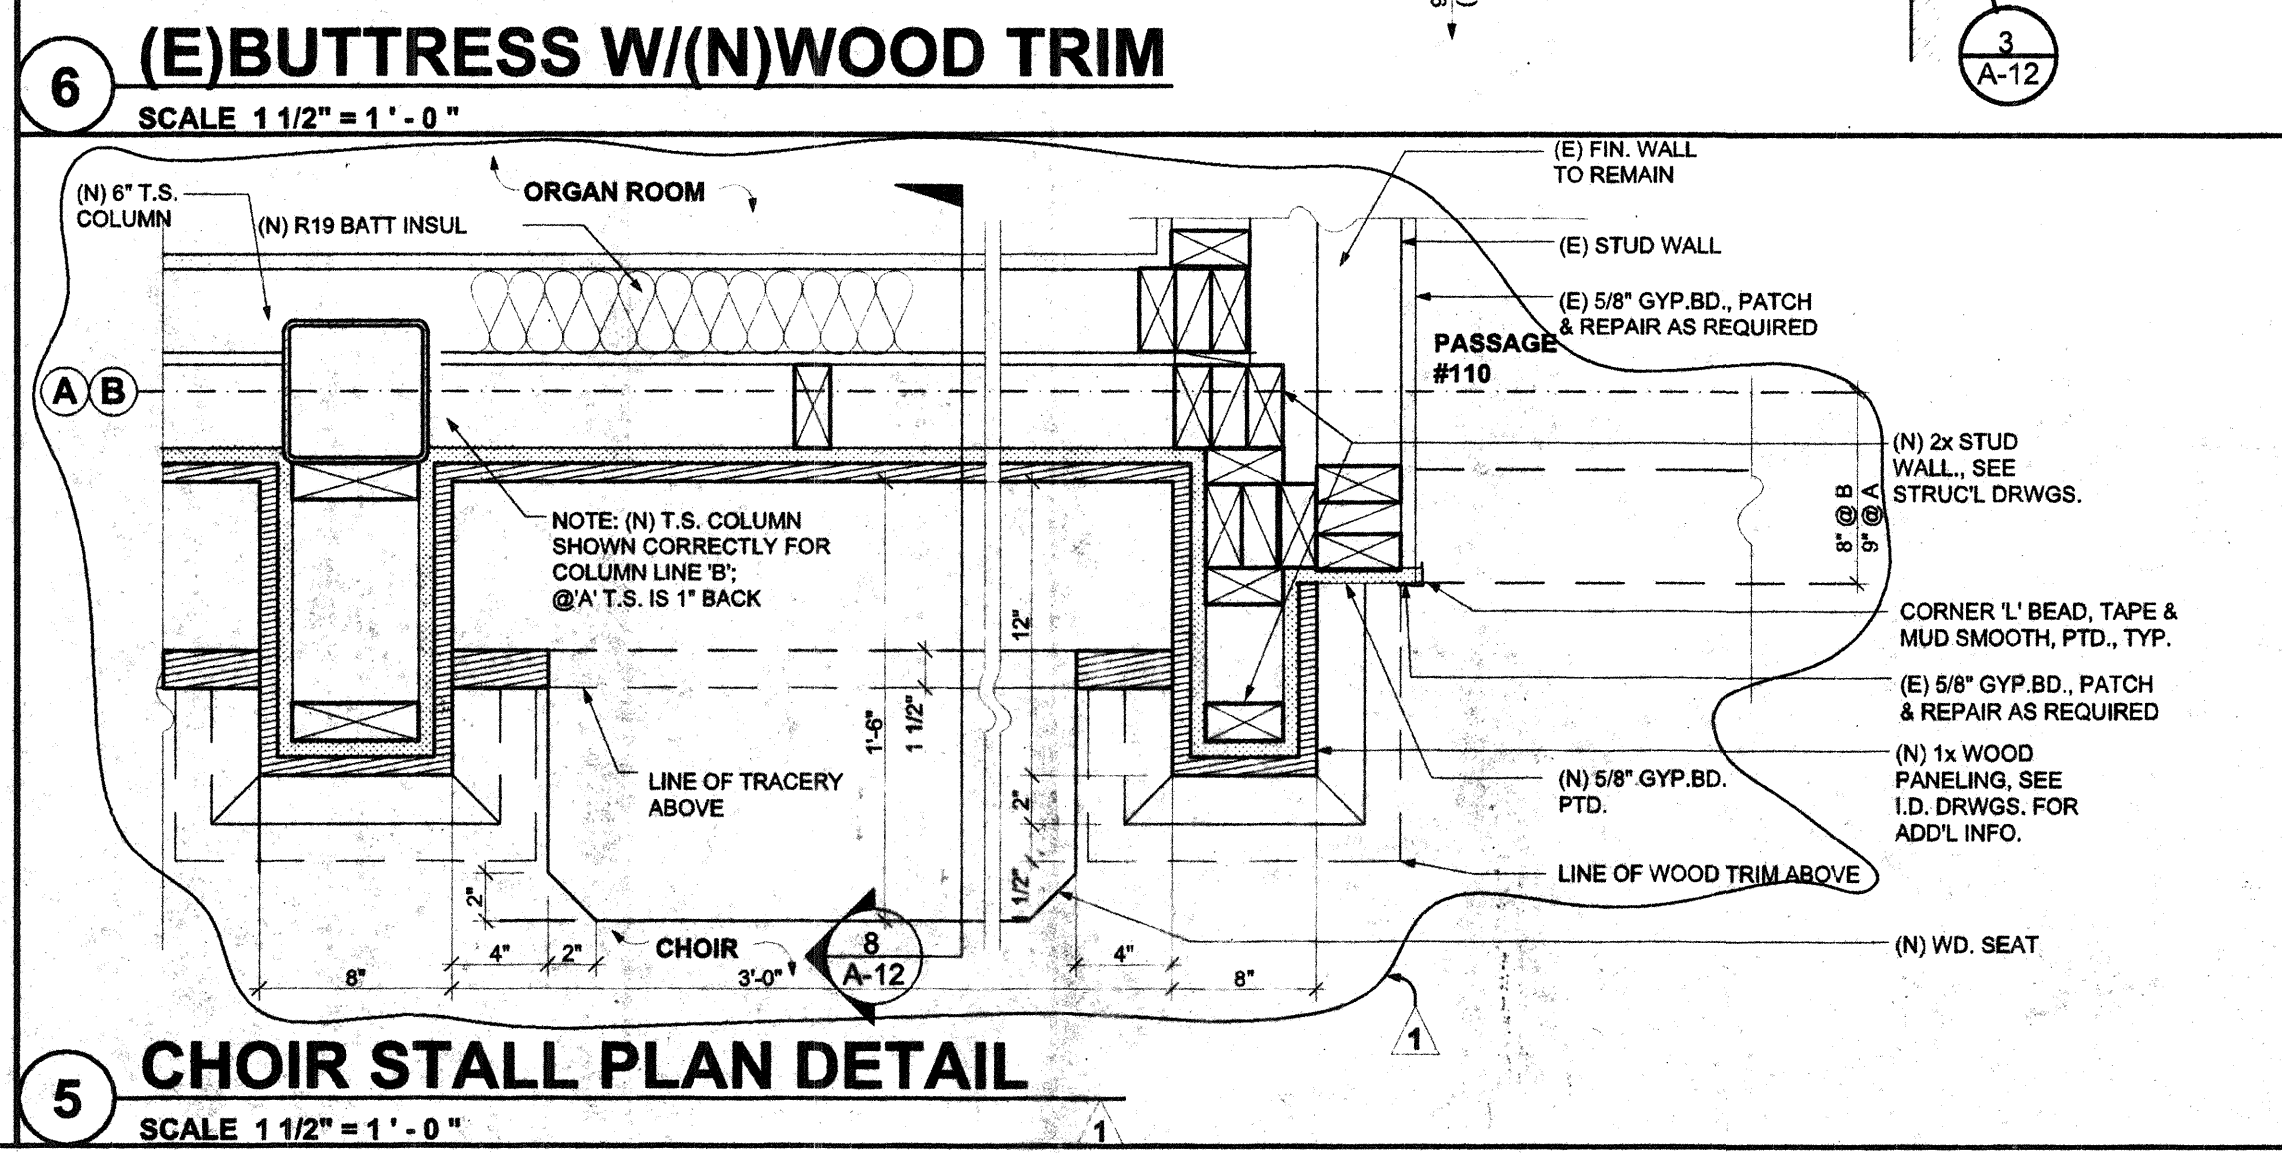
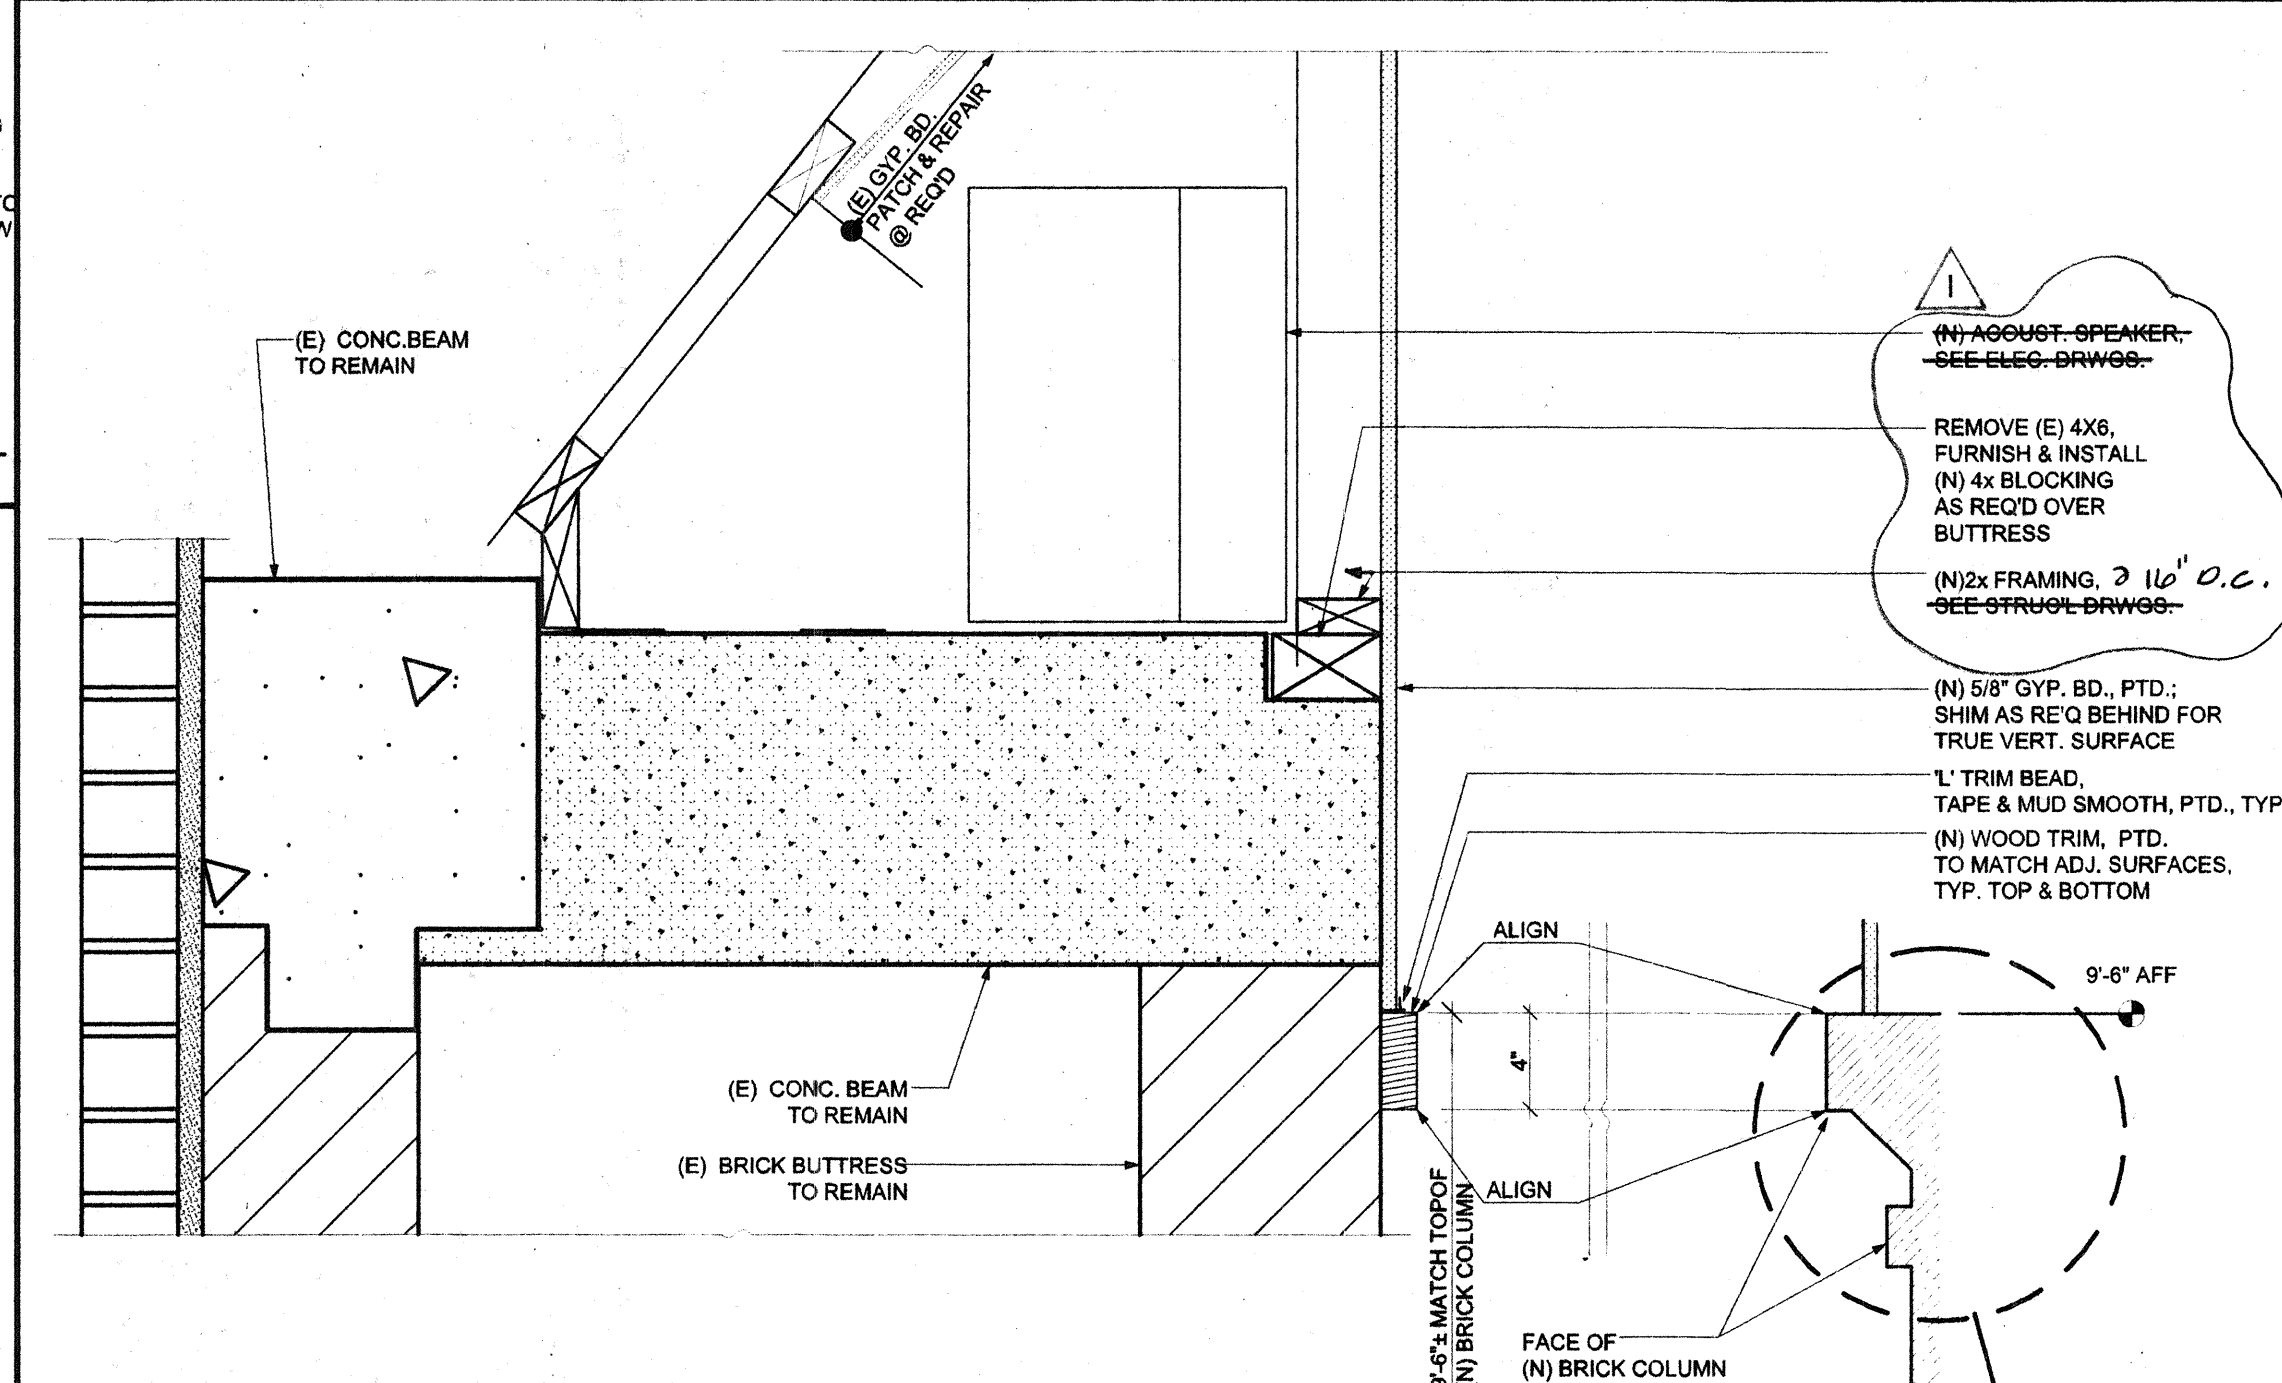
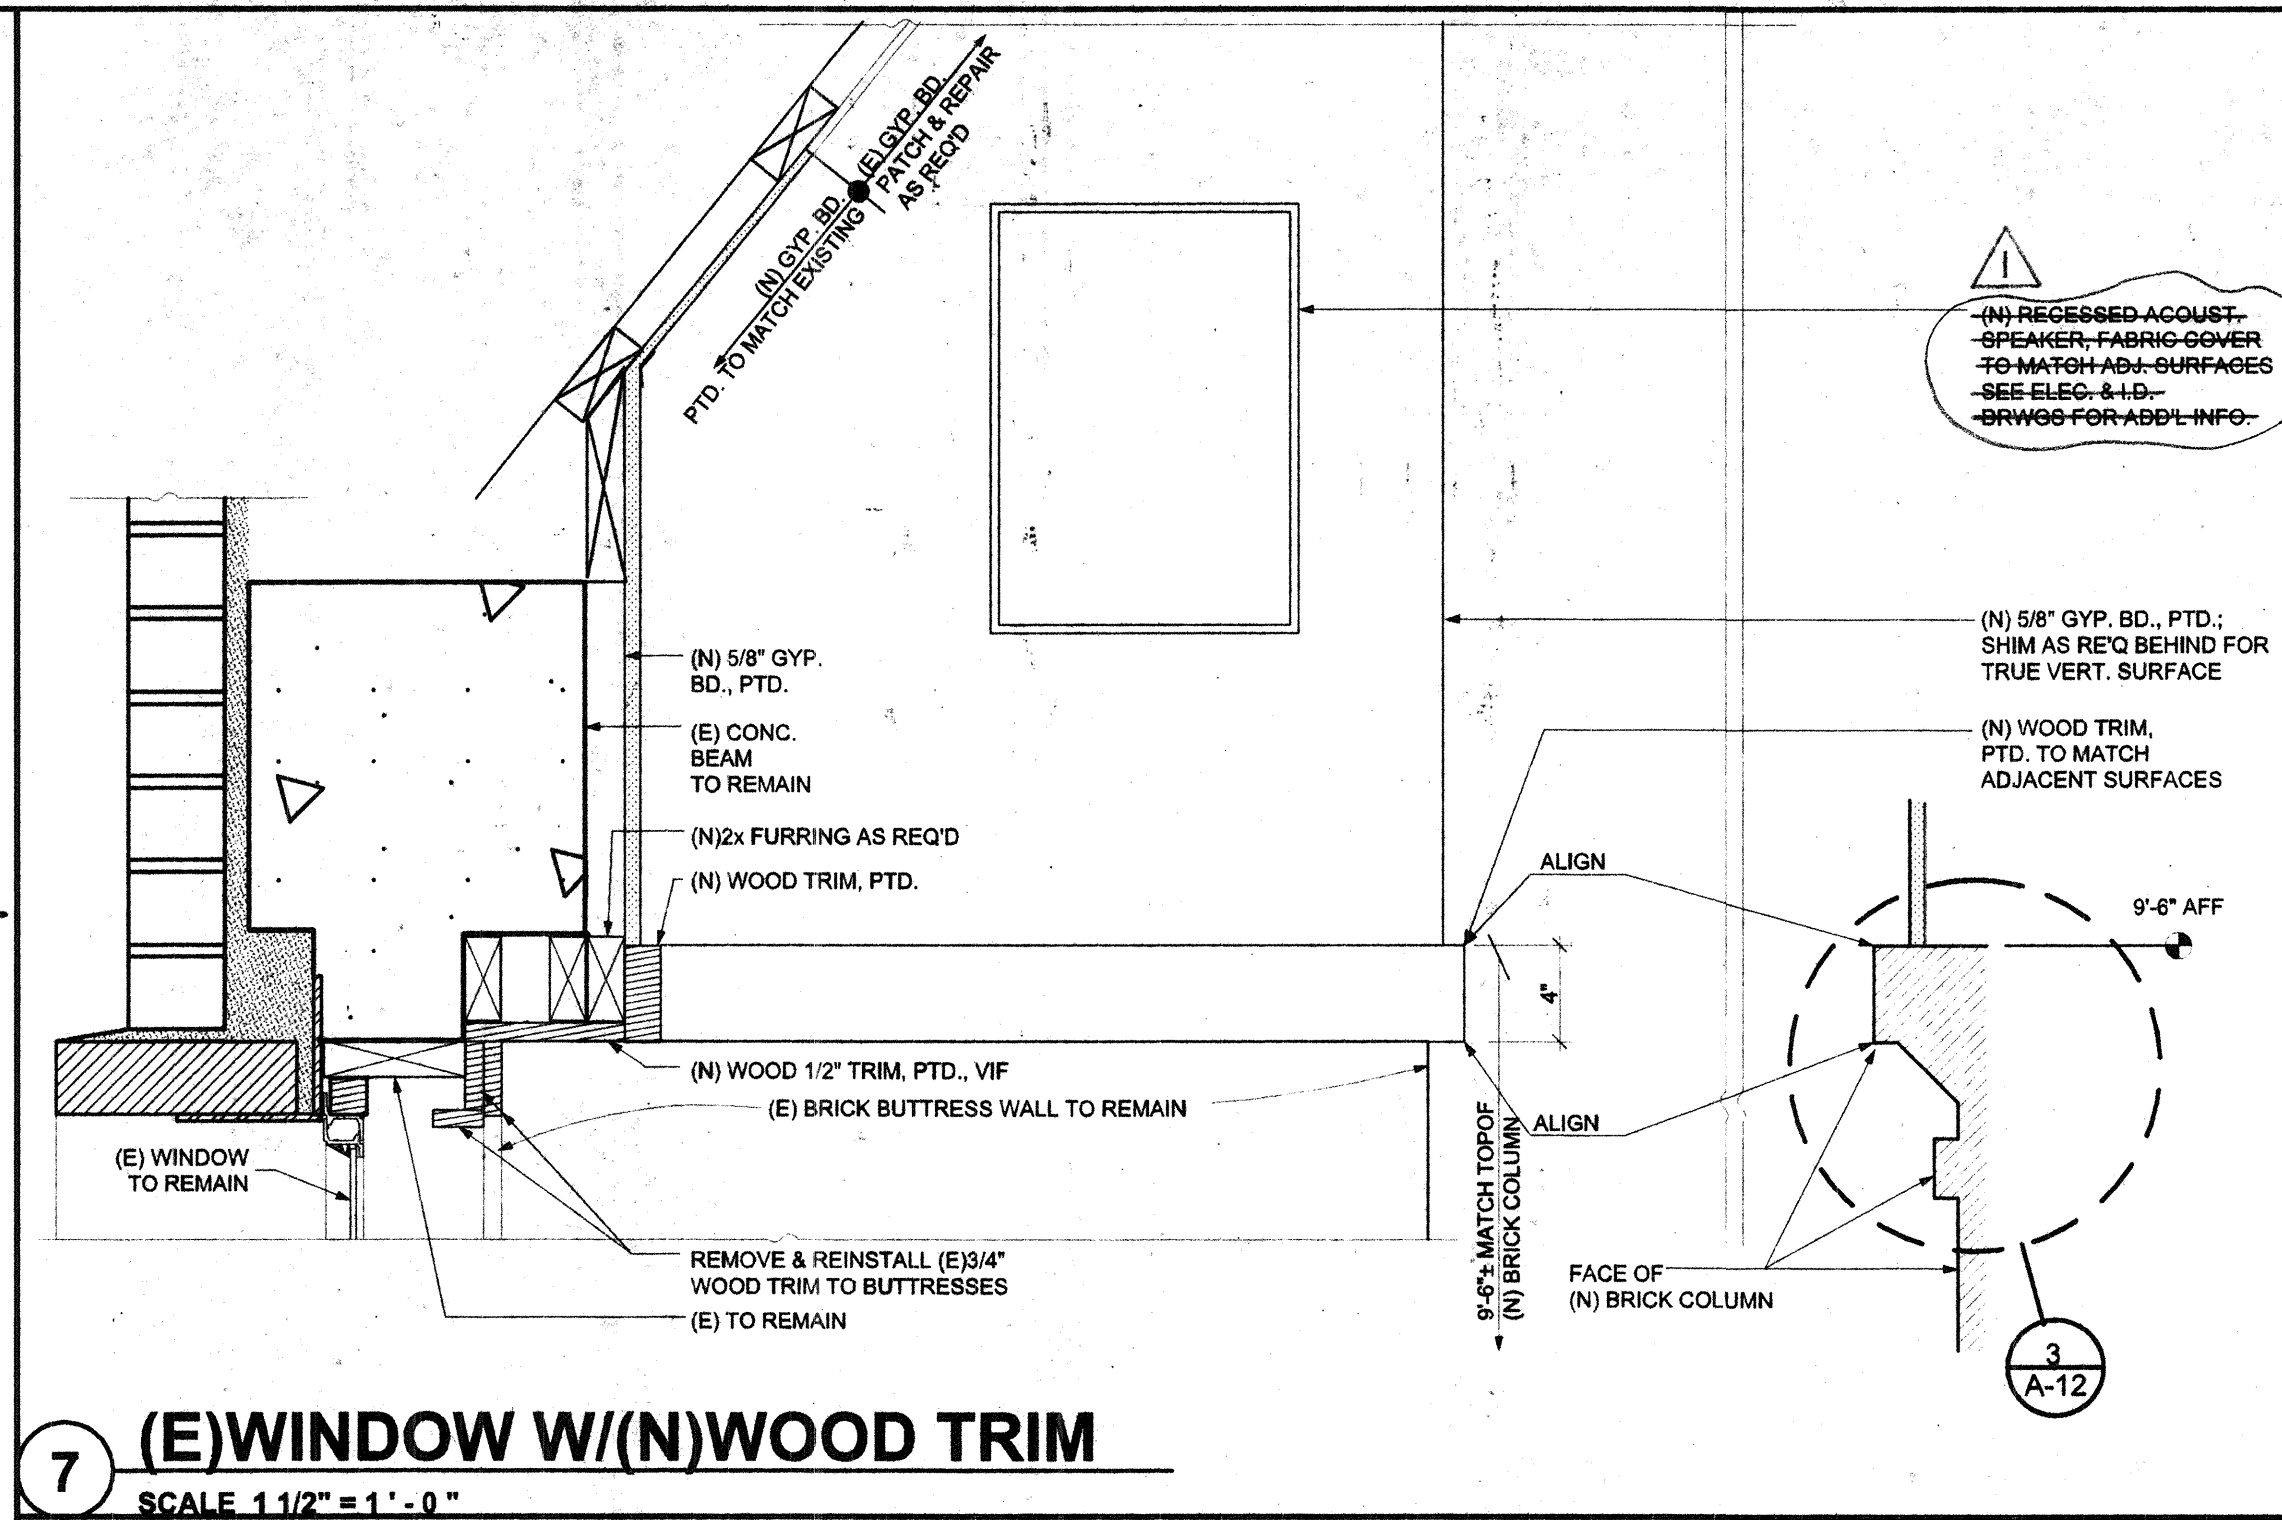
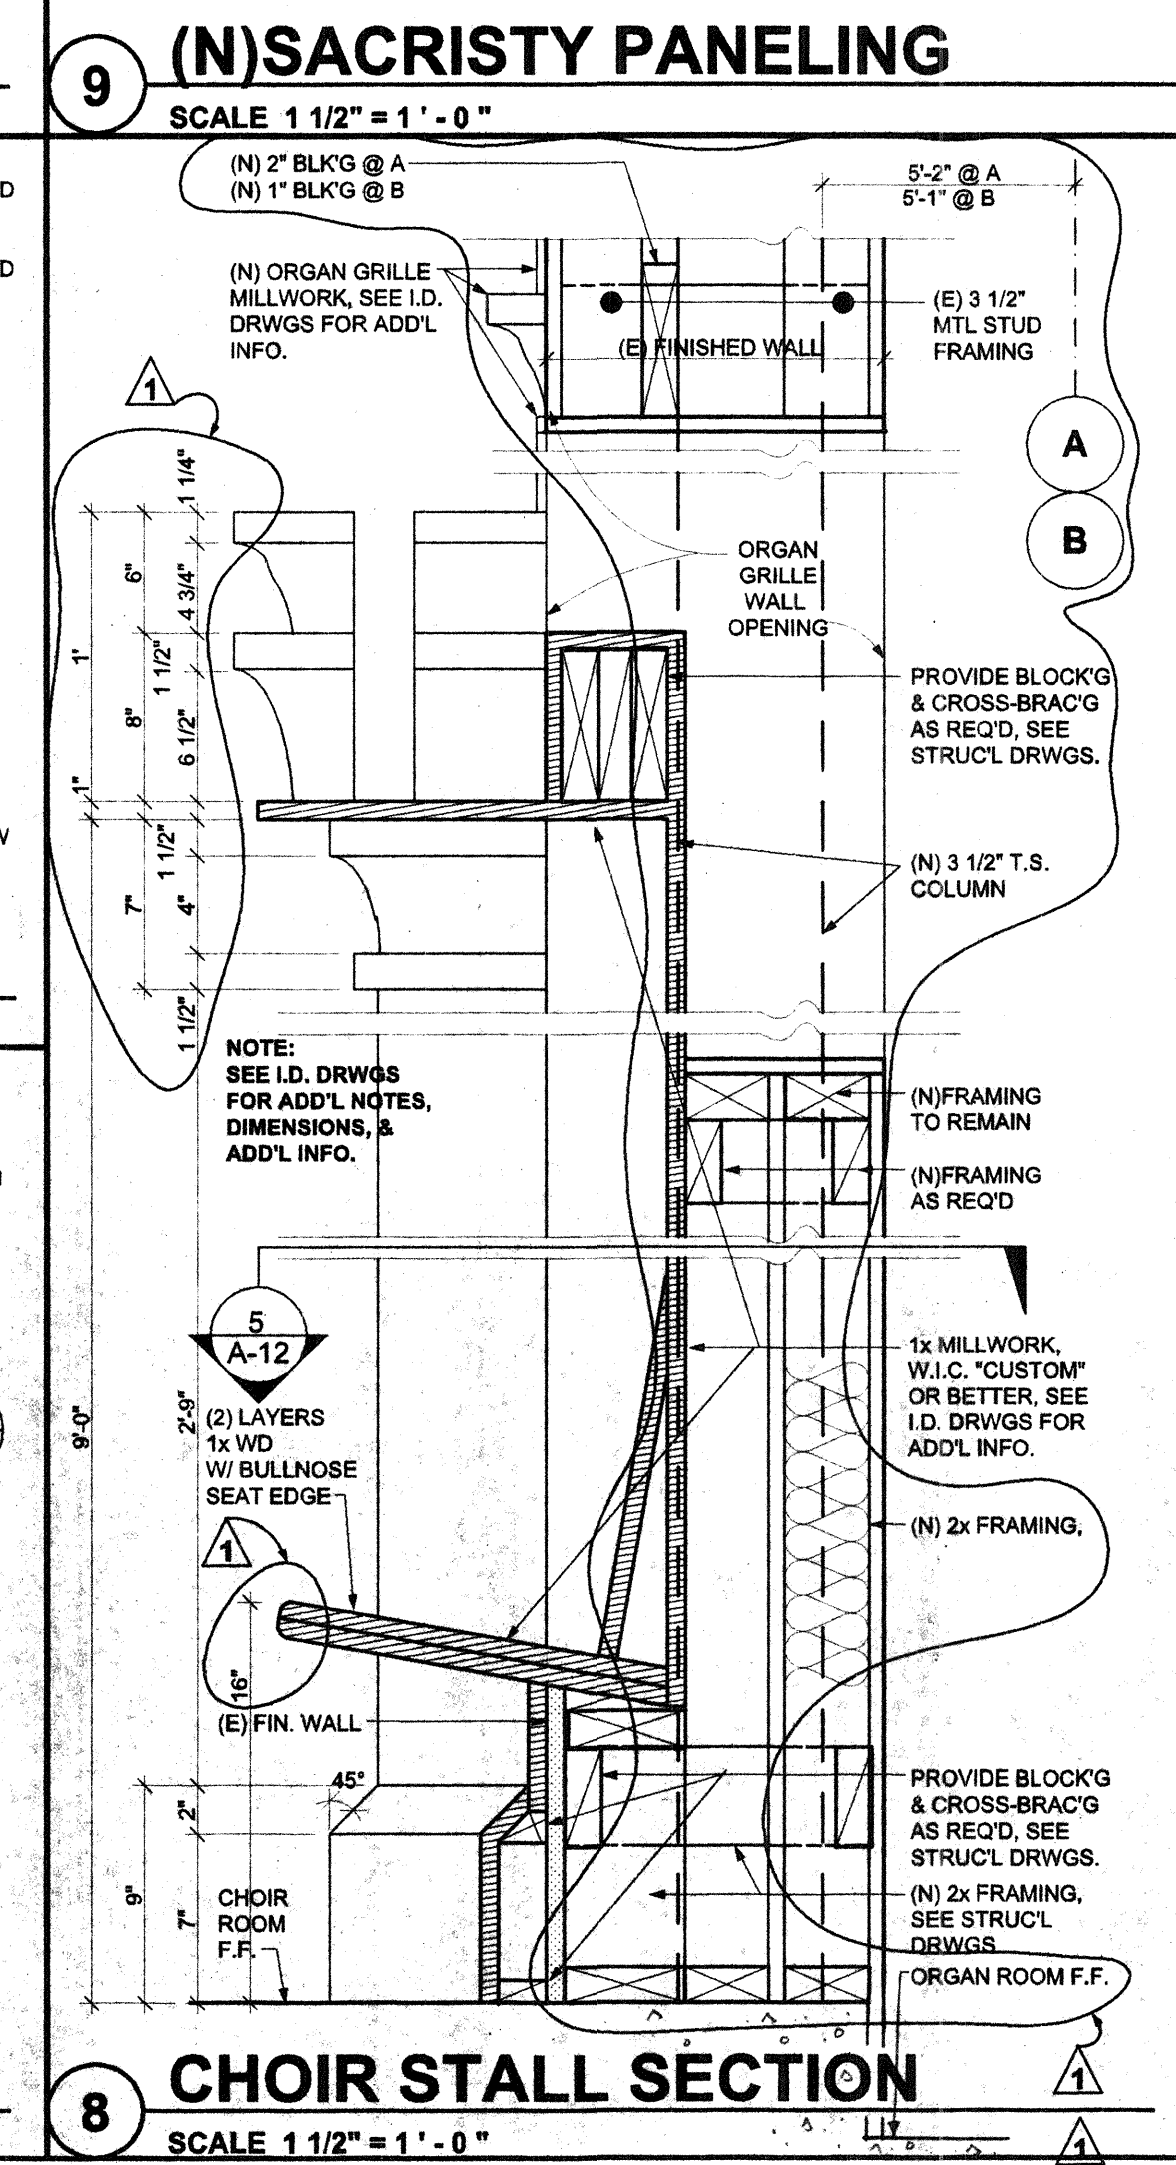
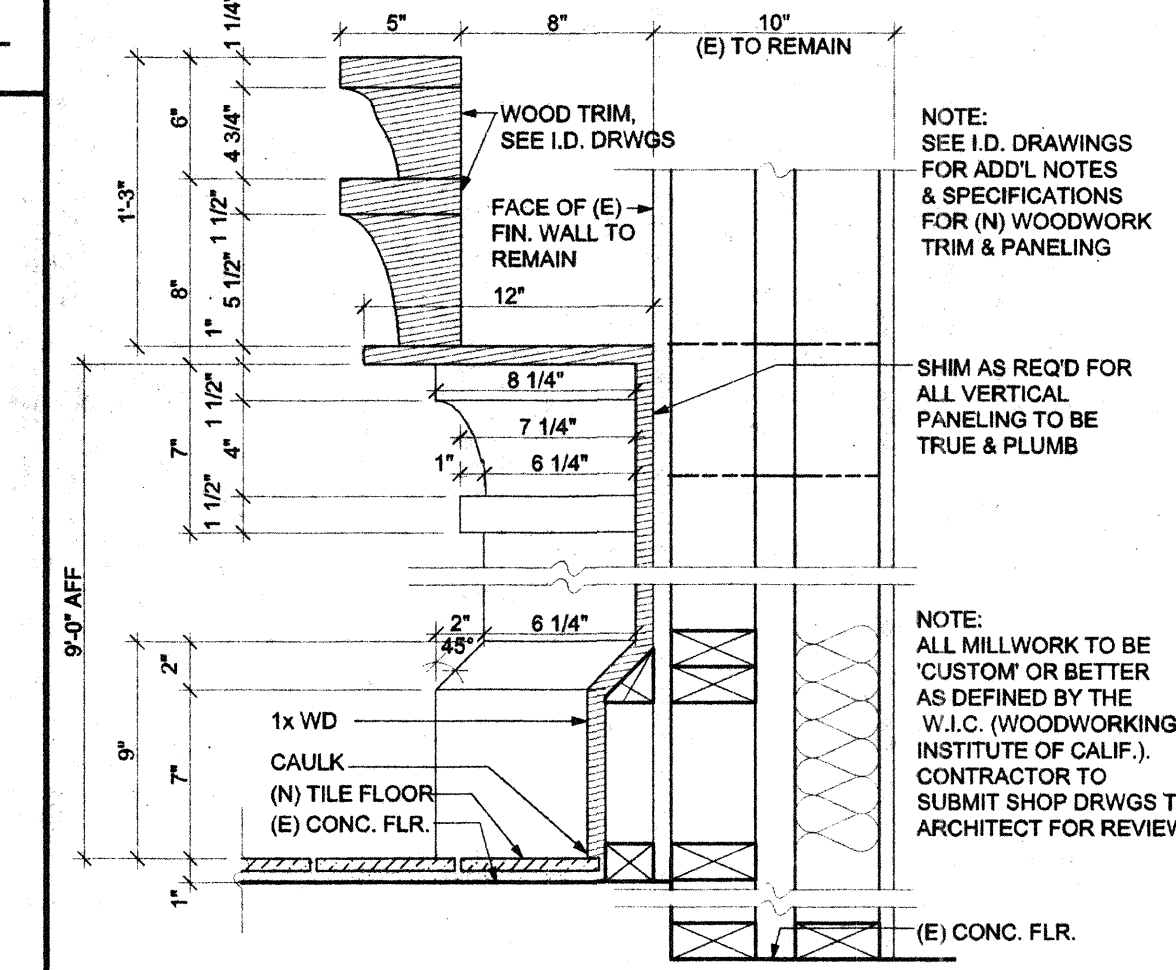
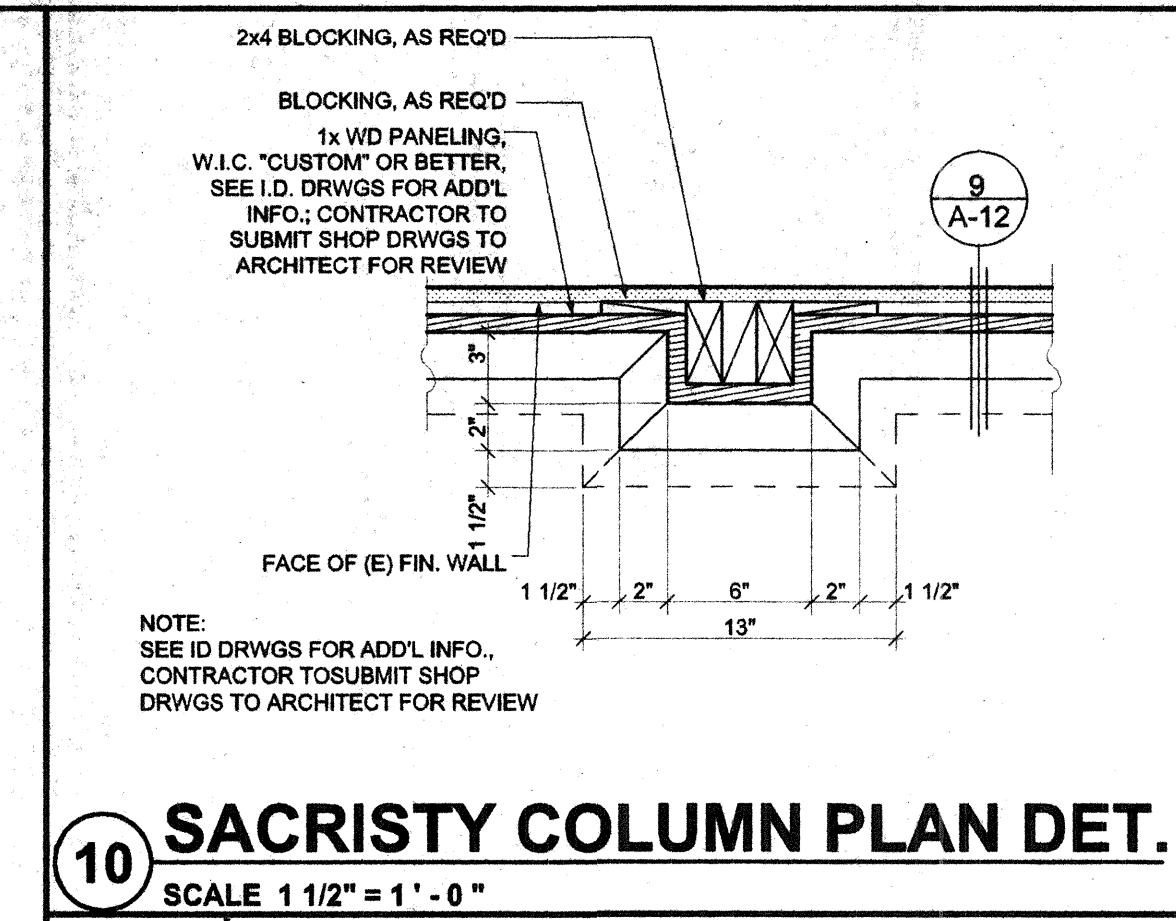
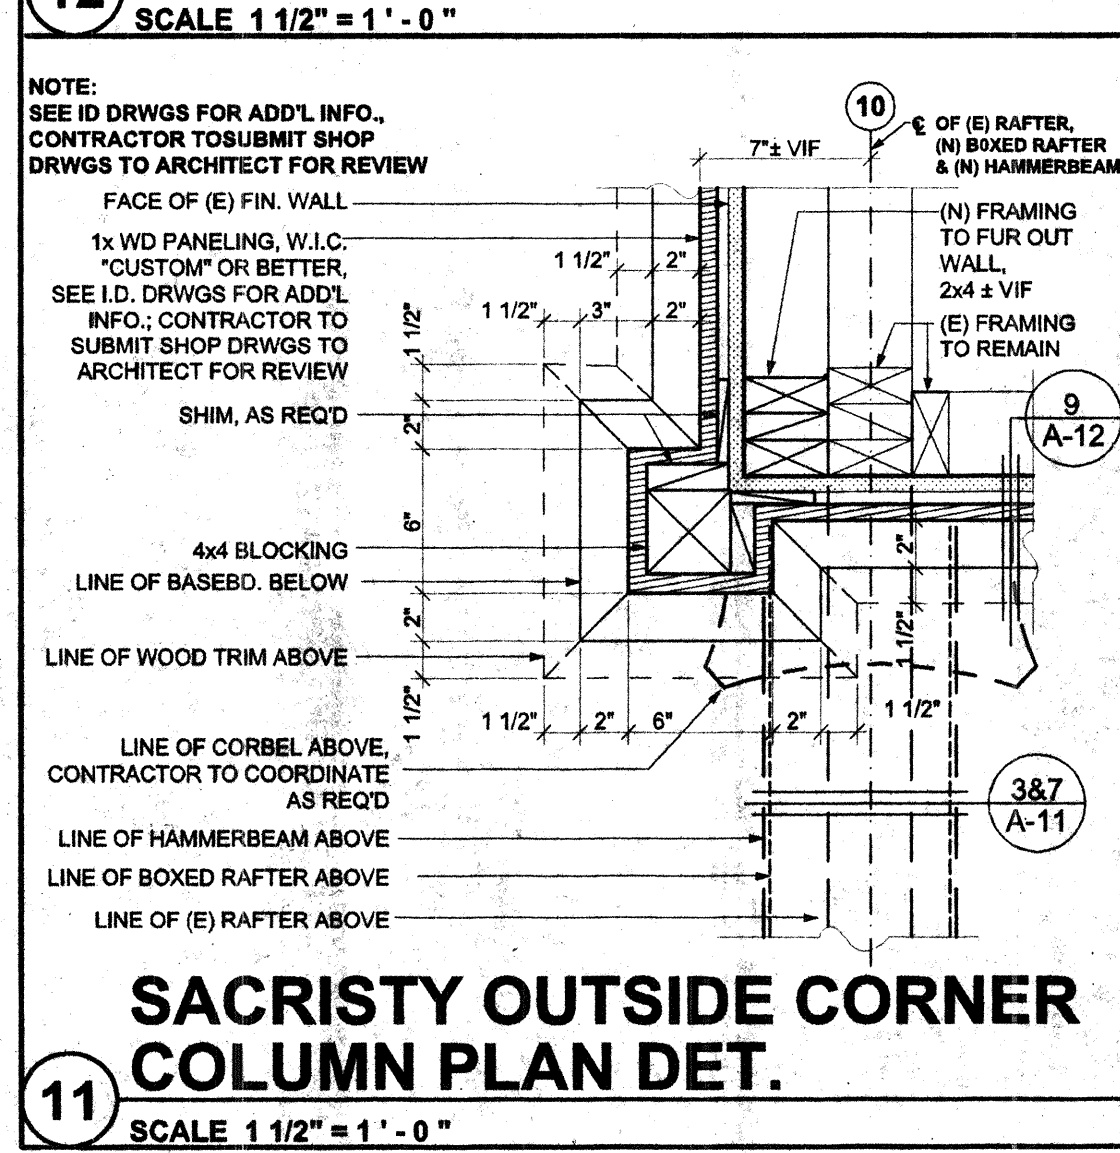
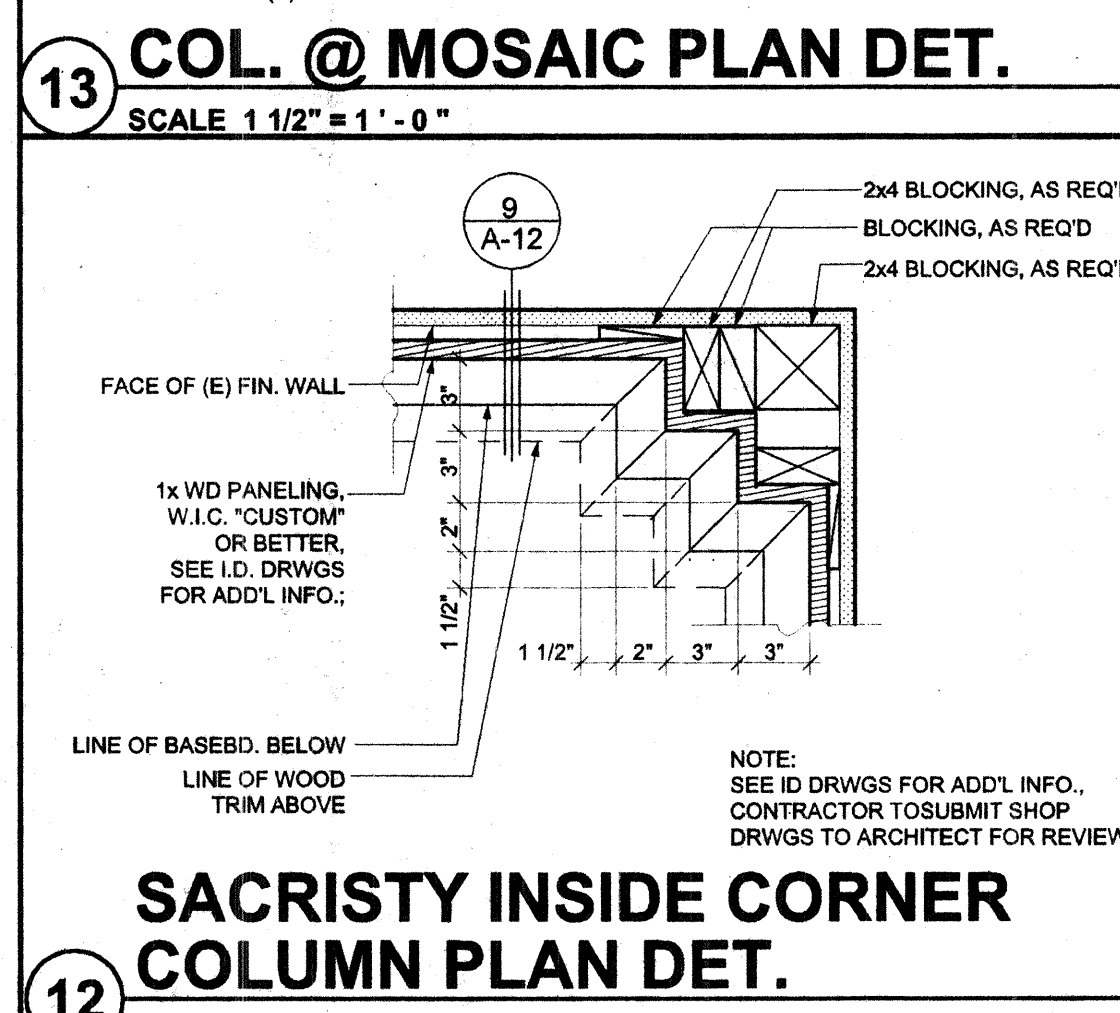
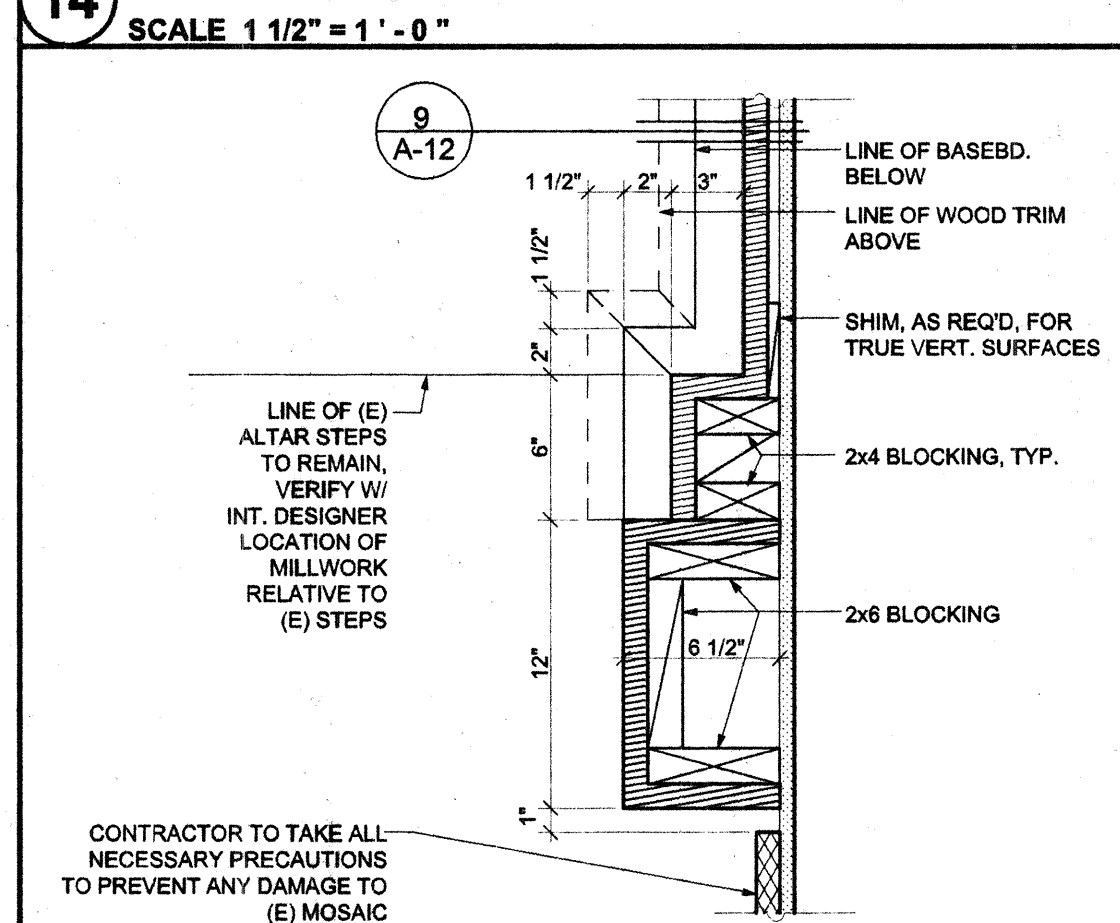


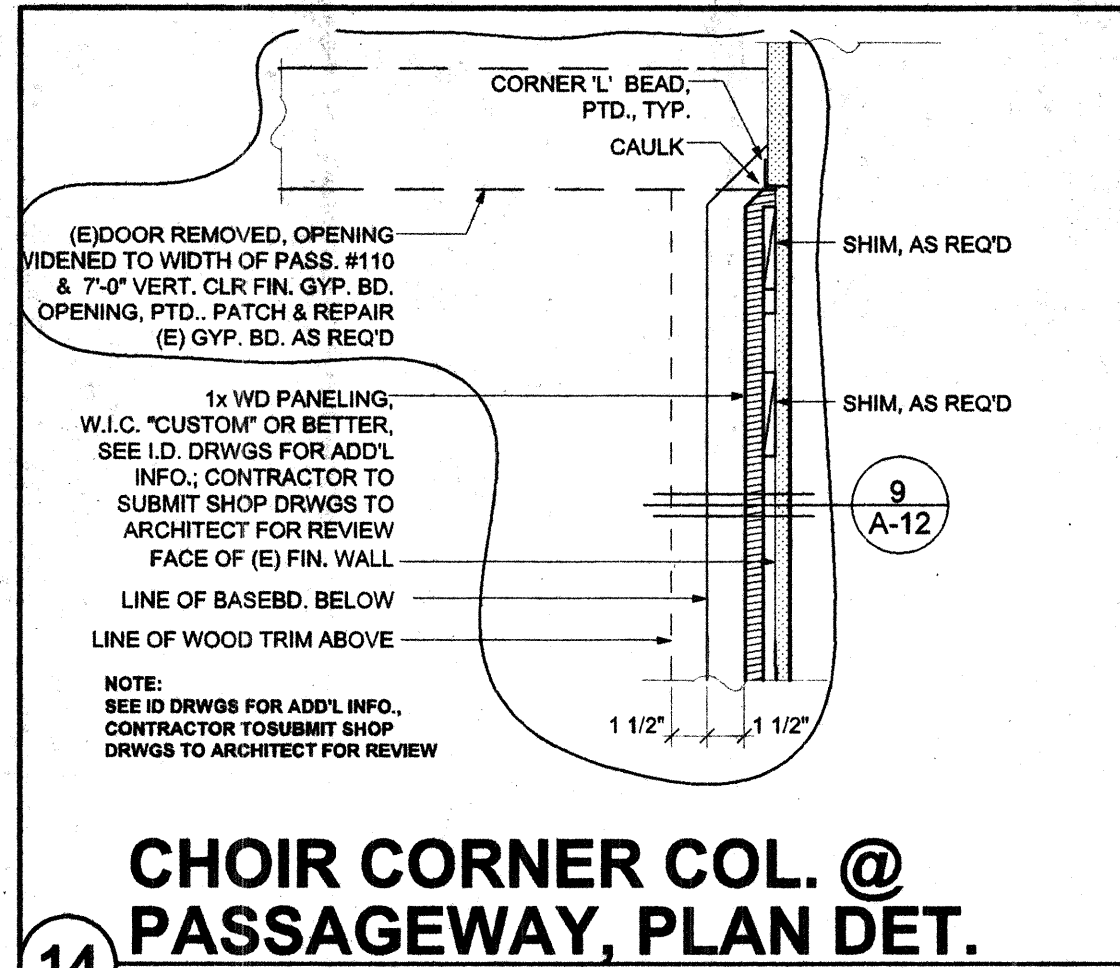

**Onuma & Associates**  
Architecture, Planning, Consulting  
511 Mission Street  
South Pasadena, CA 91030  
tel 626.799.9920  
fax 626.799.8260  
e-mail: info@onuma.com

Consultants

**RENOVATION PROJECT**  
FOR  
**SAINT EDMUND'S**  
**EPISCOPAL CHURCH**  
1175 SAN GABRIEL BLVD., SAN MARINO, CA., 91108-8048

STAMPS

REVISIONS

| DESCRIPTION | DATE | BY |
|-------------|------|----|
| PLAN CHECK  |      |    |

PROJECT NUMBER  
**2000**

SCALE  
**AS NOTED**

PRINTED  
**11/16/00**

TITLE  
**DETAILS**

SHEET  
**A-12**

15 OF 44