


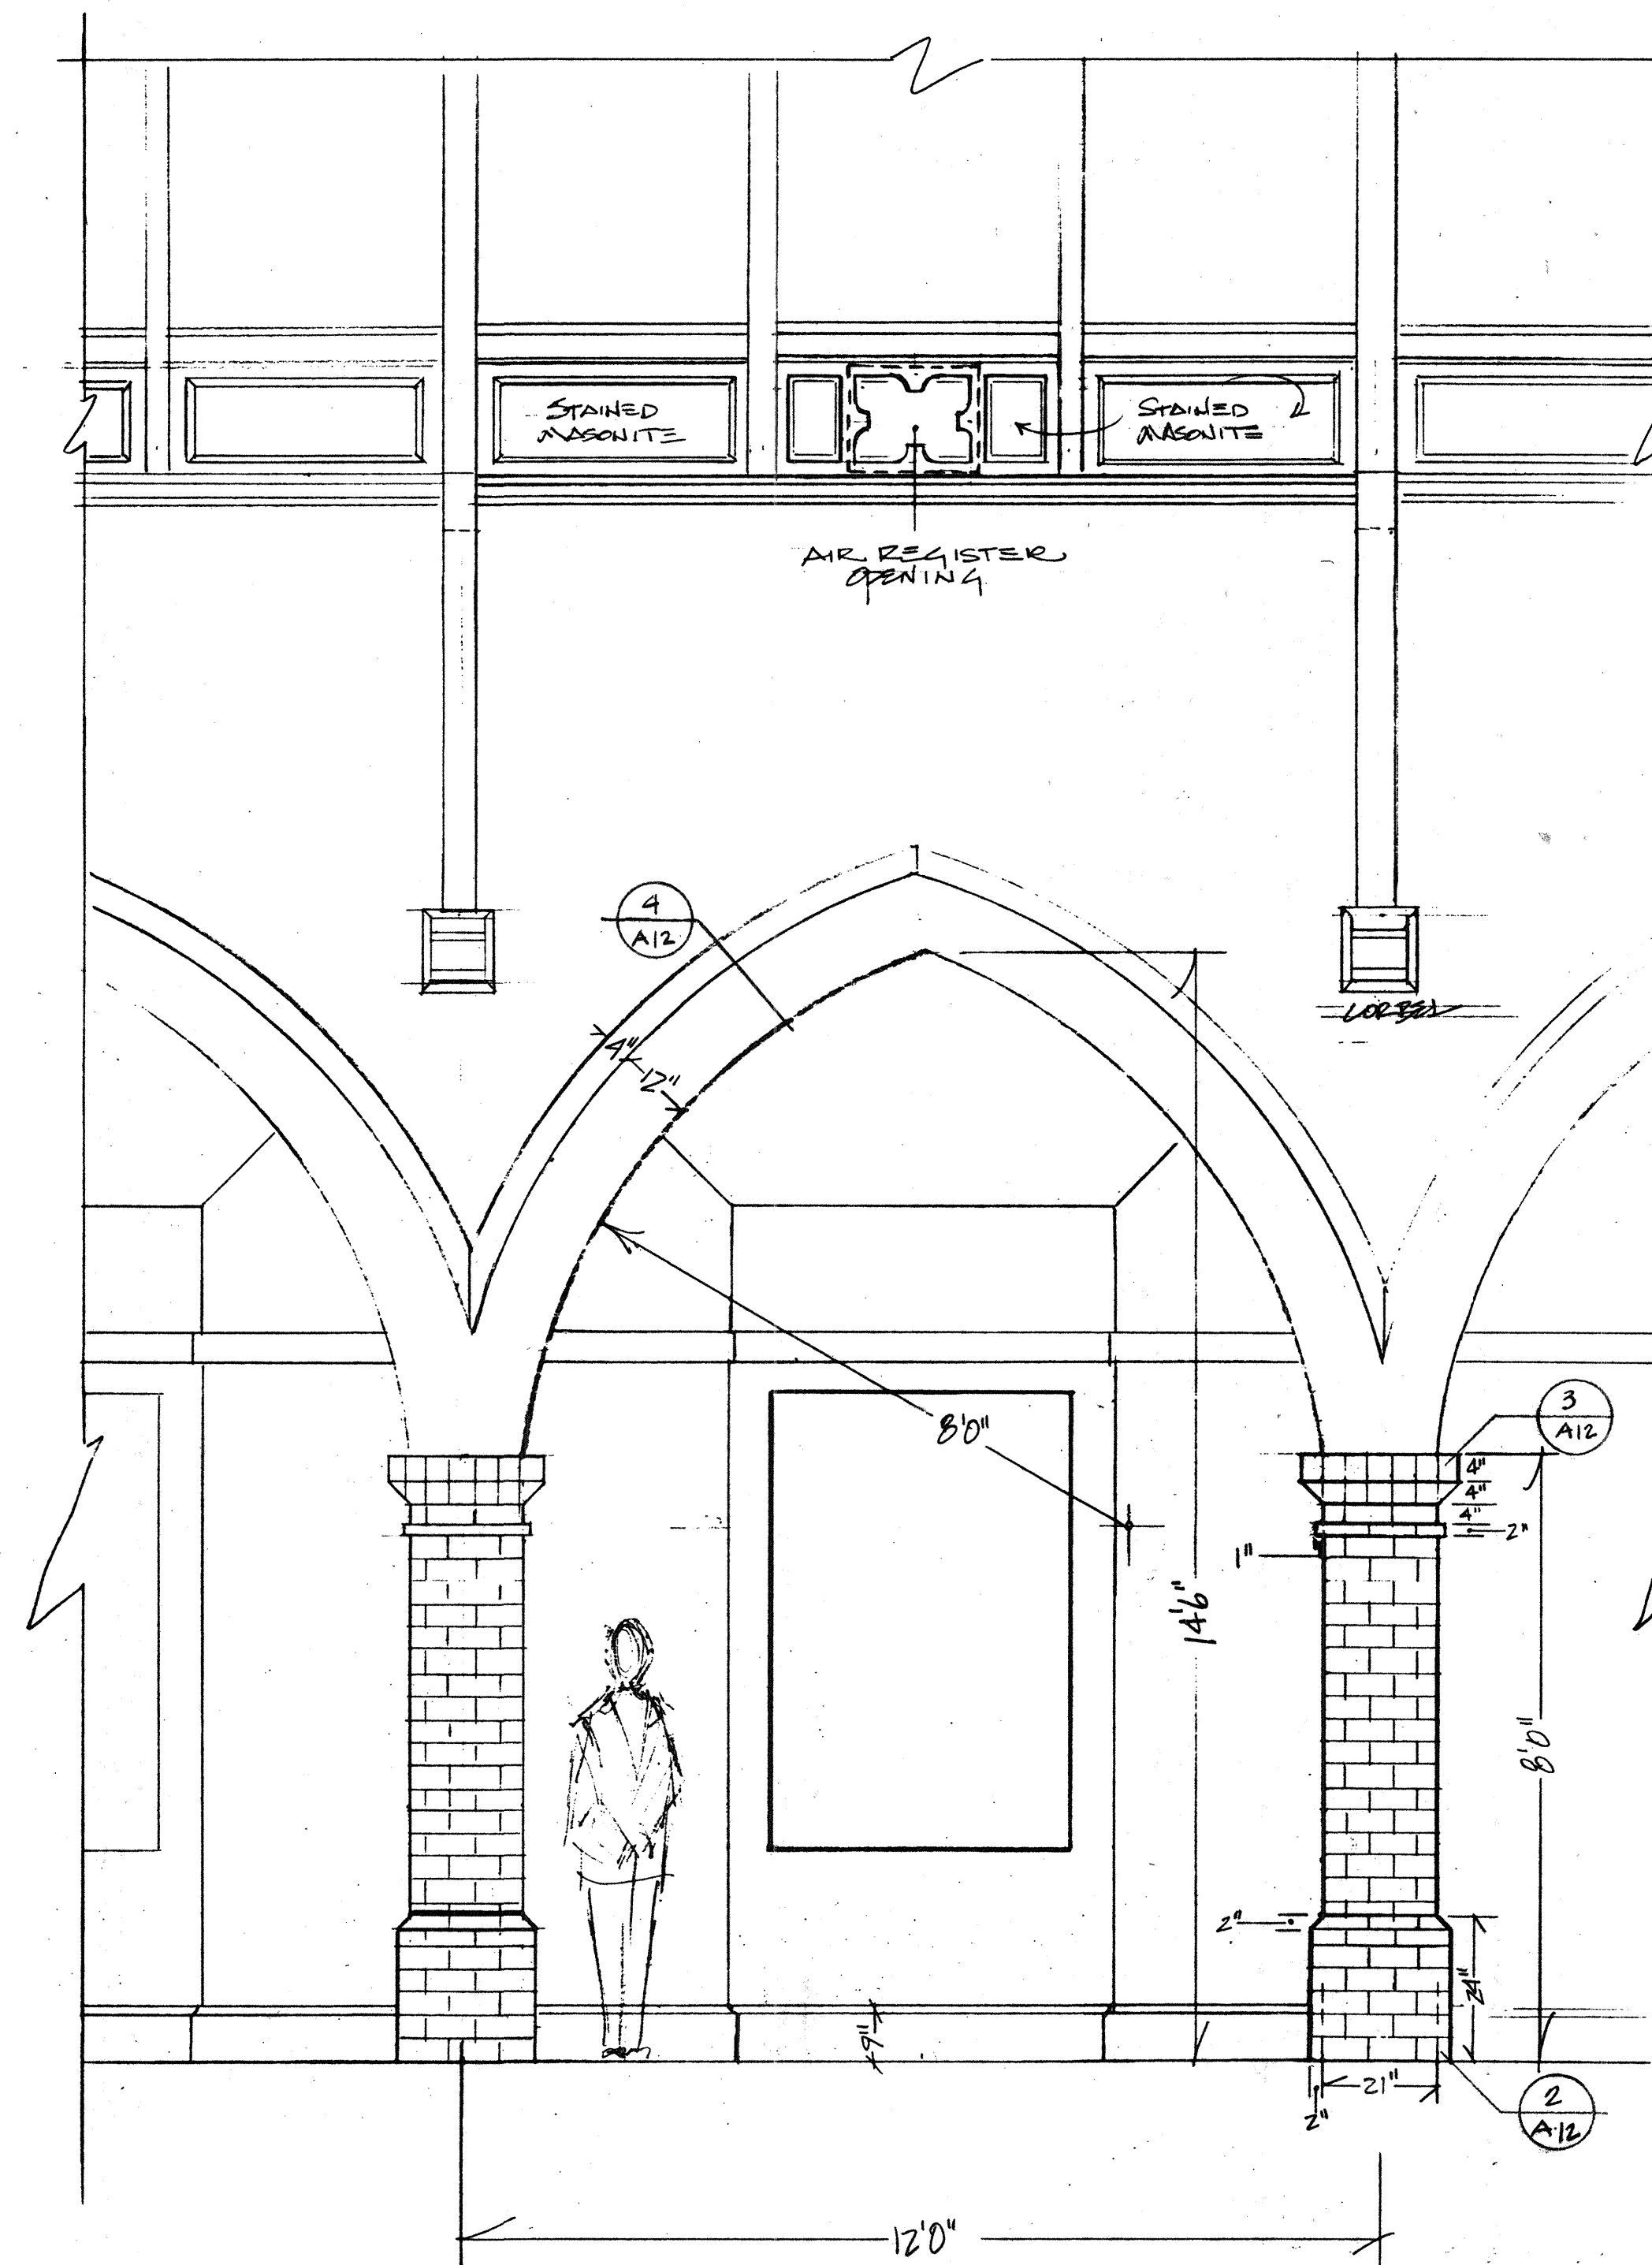


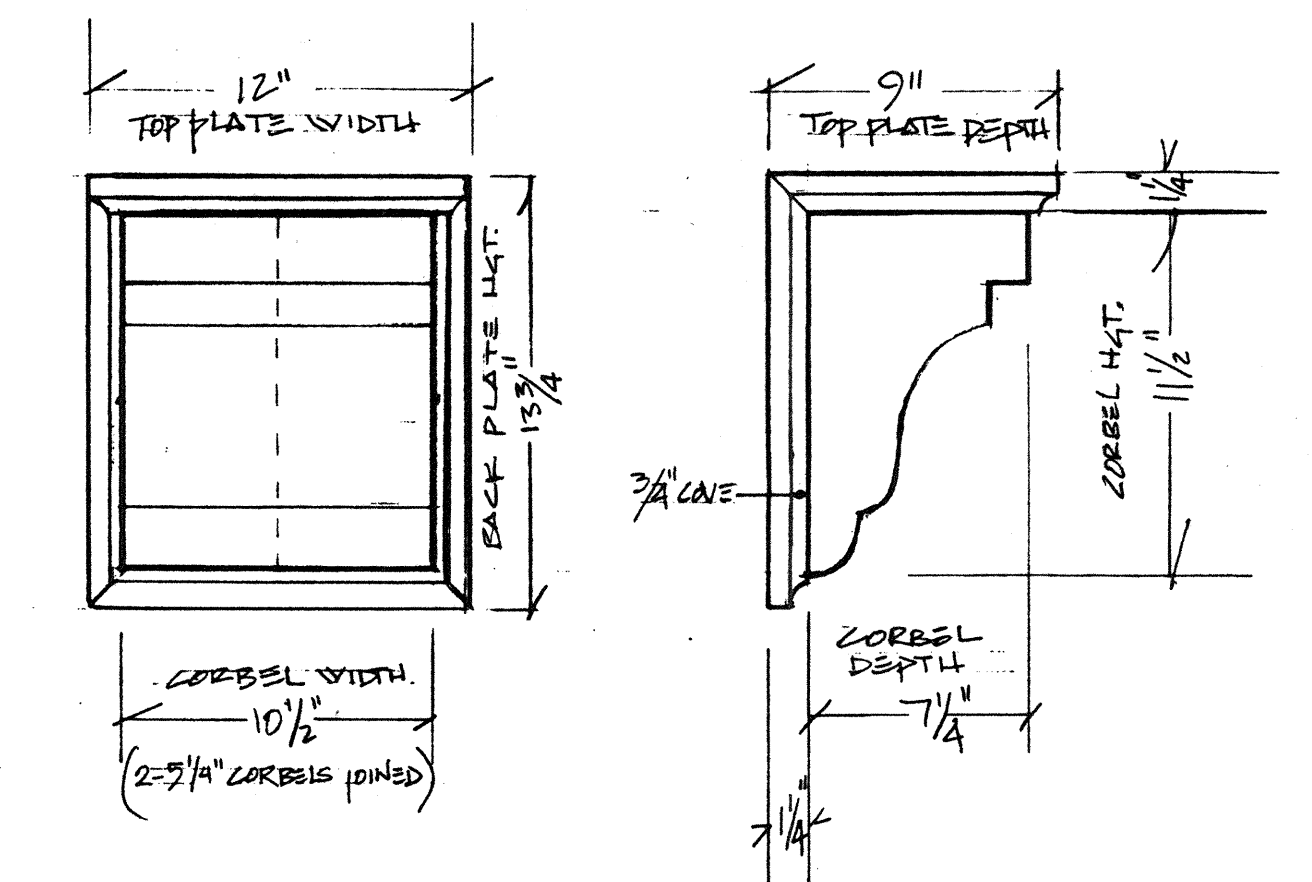

ARCADE BAY DETAIL FOR
ST EDMUND'S CHURCH, SAN MARINO
SCALE: 1/2" = 1'0" / 21 AUGUST 2000
PHOT JUDICE DESIGNS, PLEASANT A

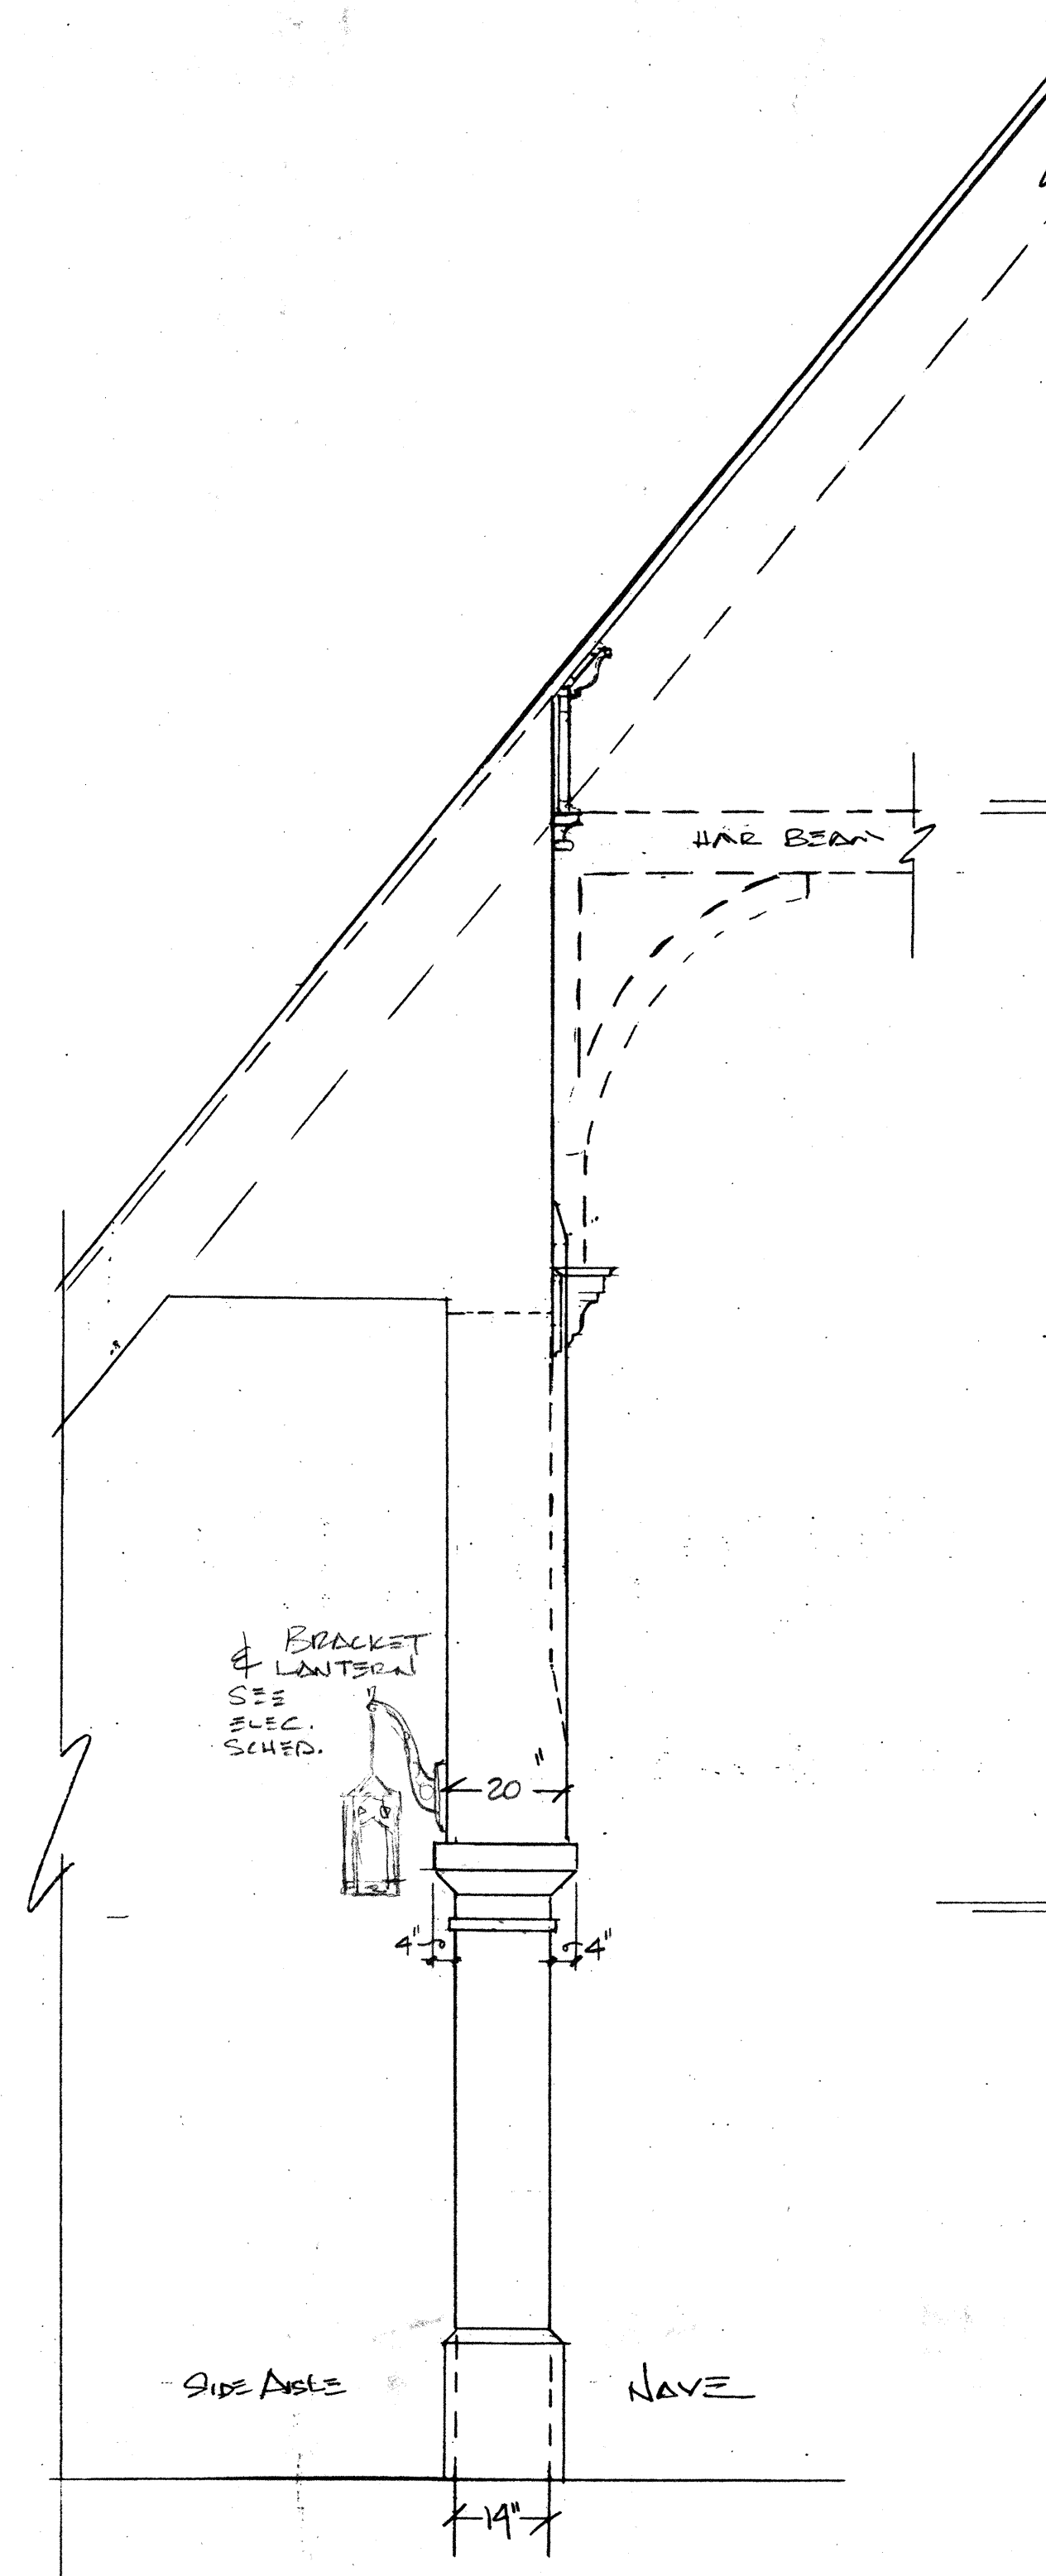

HAMMER BEAM
BAND SAWN CORBELS SCALE: 2" = 1'0"
(WITH APPLIED TOP & BACK PLATES)
PRODUCT #915 / MOULDING CENTER, NO. HOLLYWOOD
EACH CORBEL CONSISTS OF 2-5/8" CORBELS JOINED
BACK & TOP PLATES W/ 3/4" GROOVE IS APPLIED

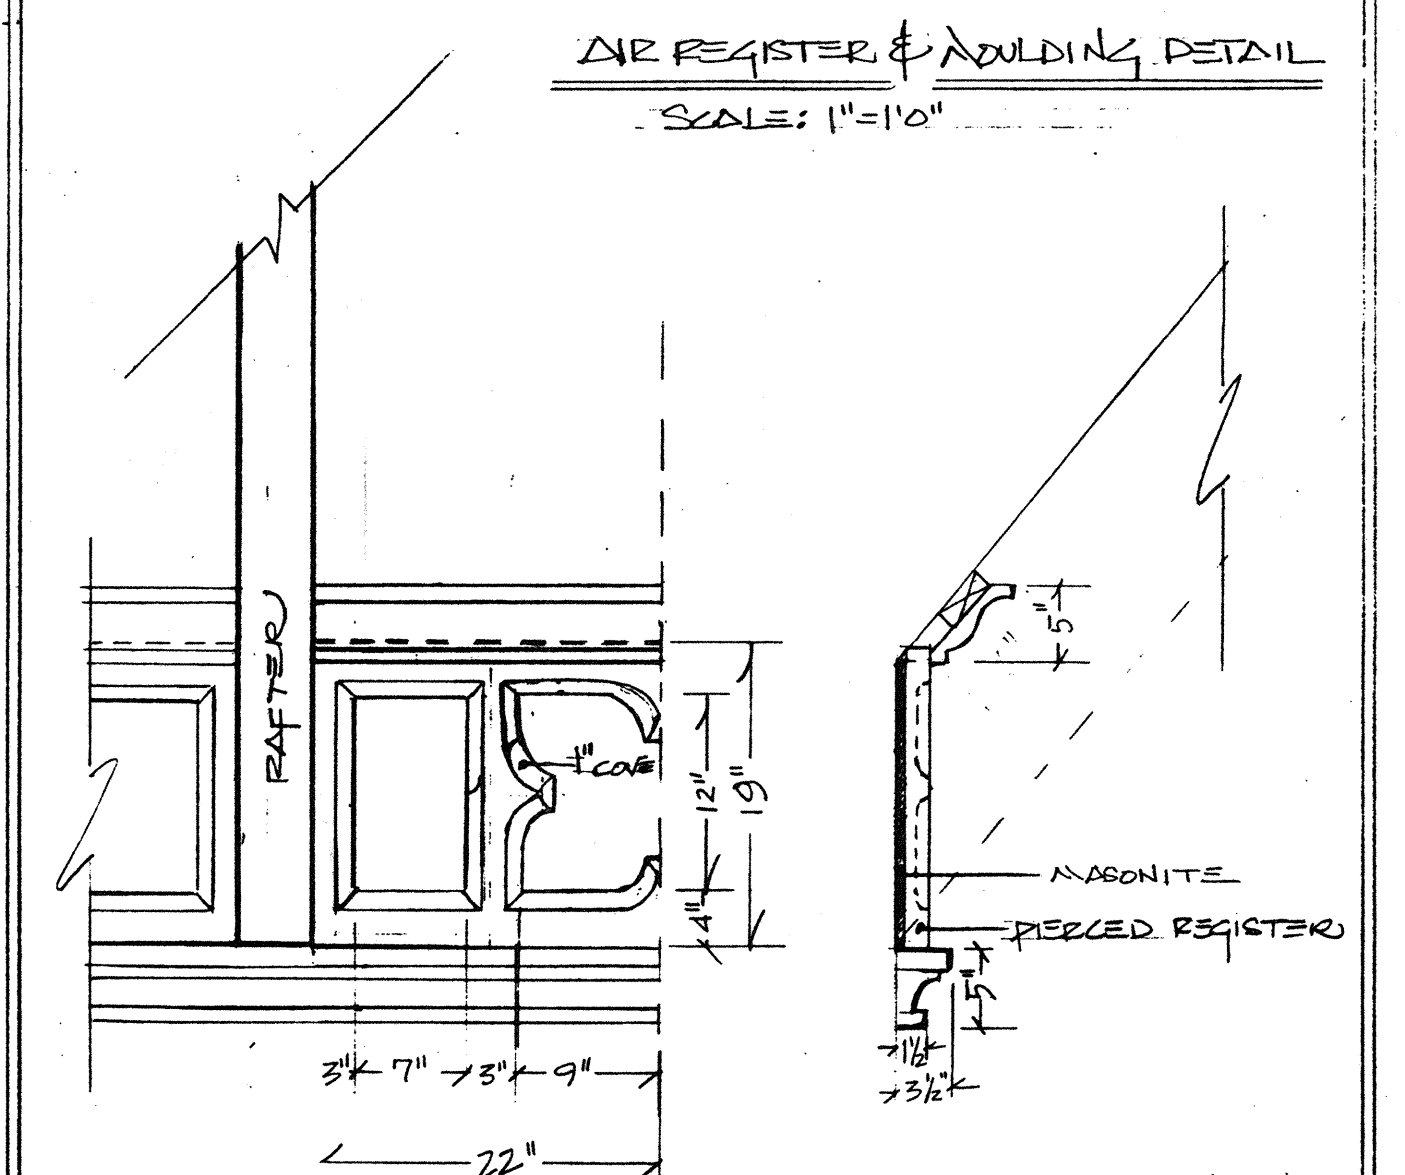

COVERED MILLWORK & MOULDING: ALDER OR BIRCH / STAINED
MASONITE PLATES STAINED COLOR OF MILLWORK

SHEET

ID-1

16 OF 44