



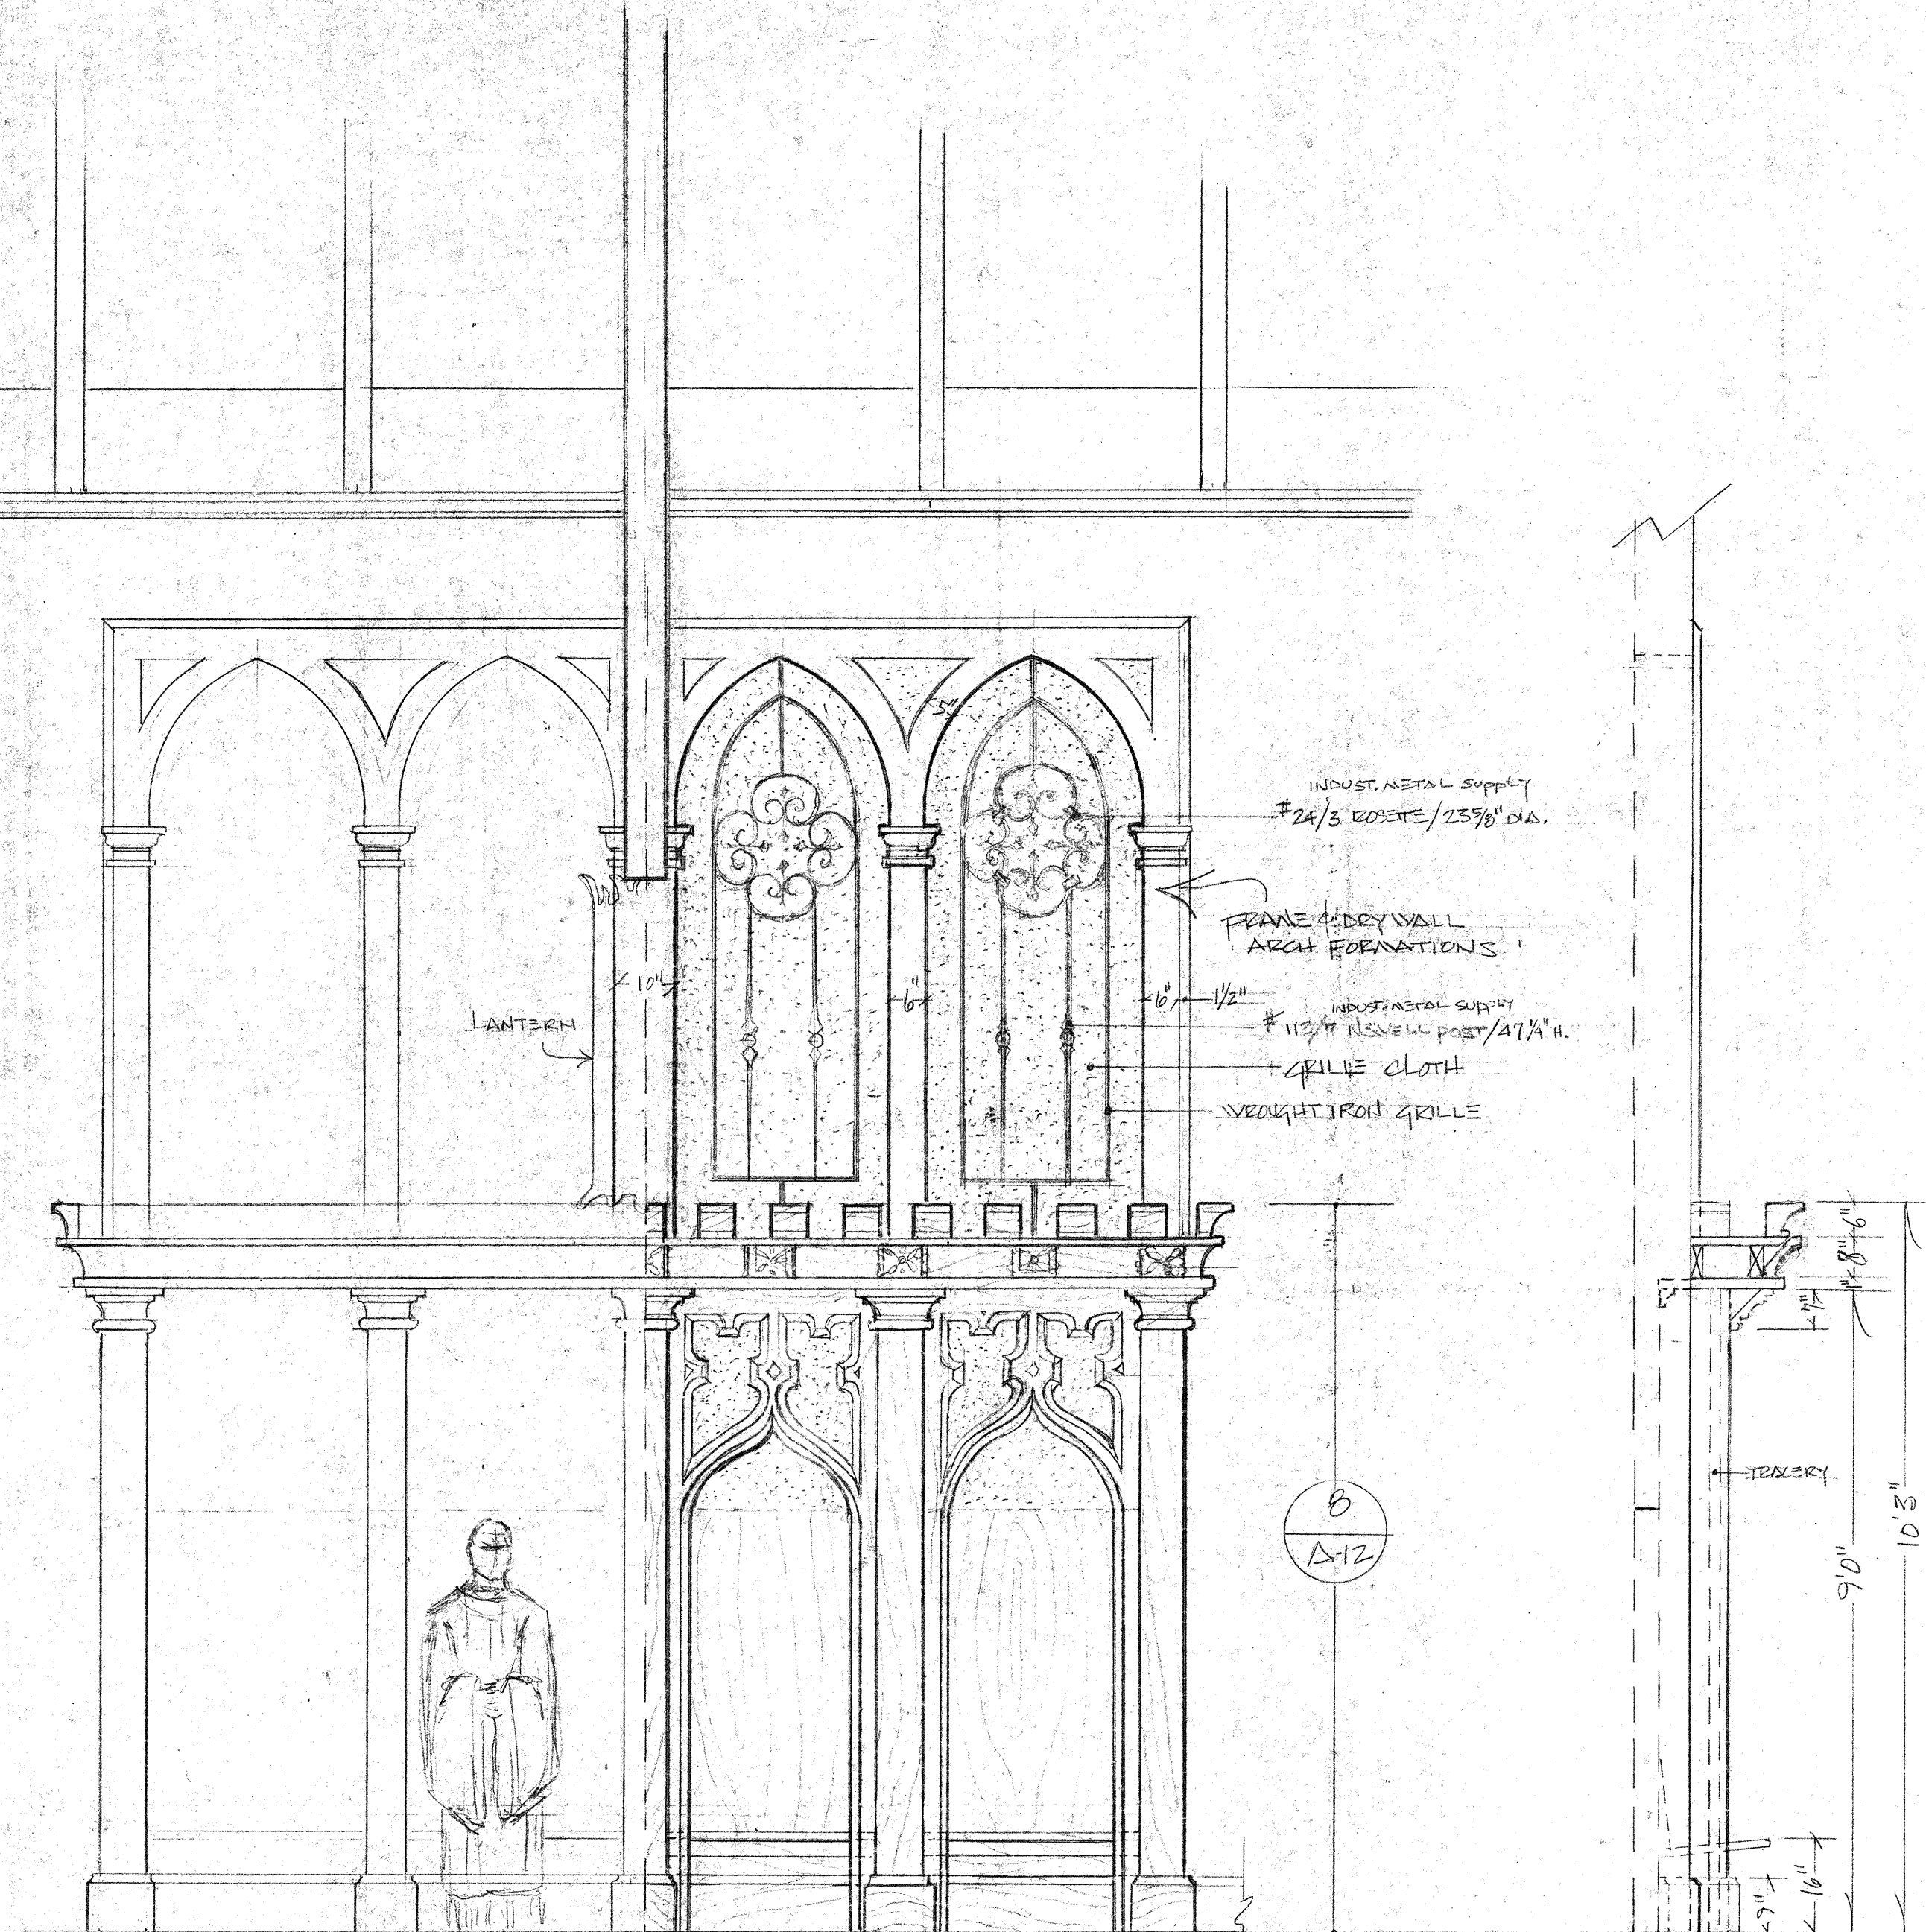


1 ELEVATION

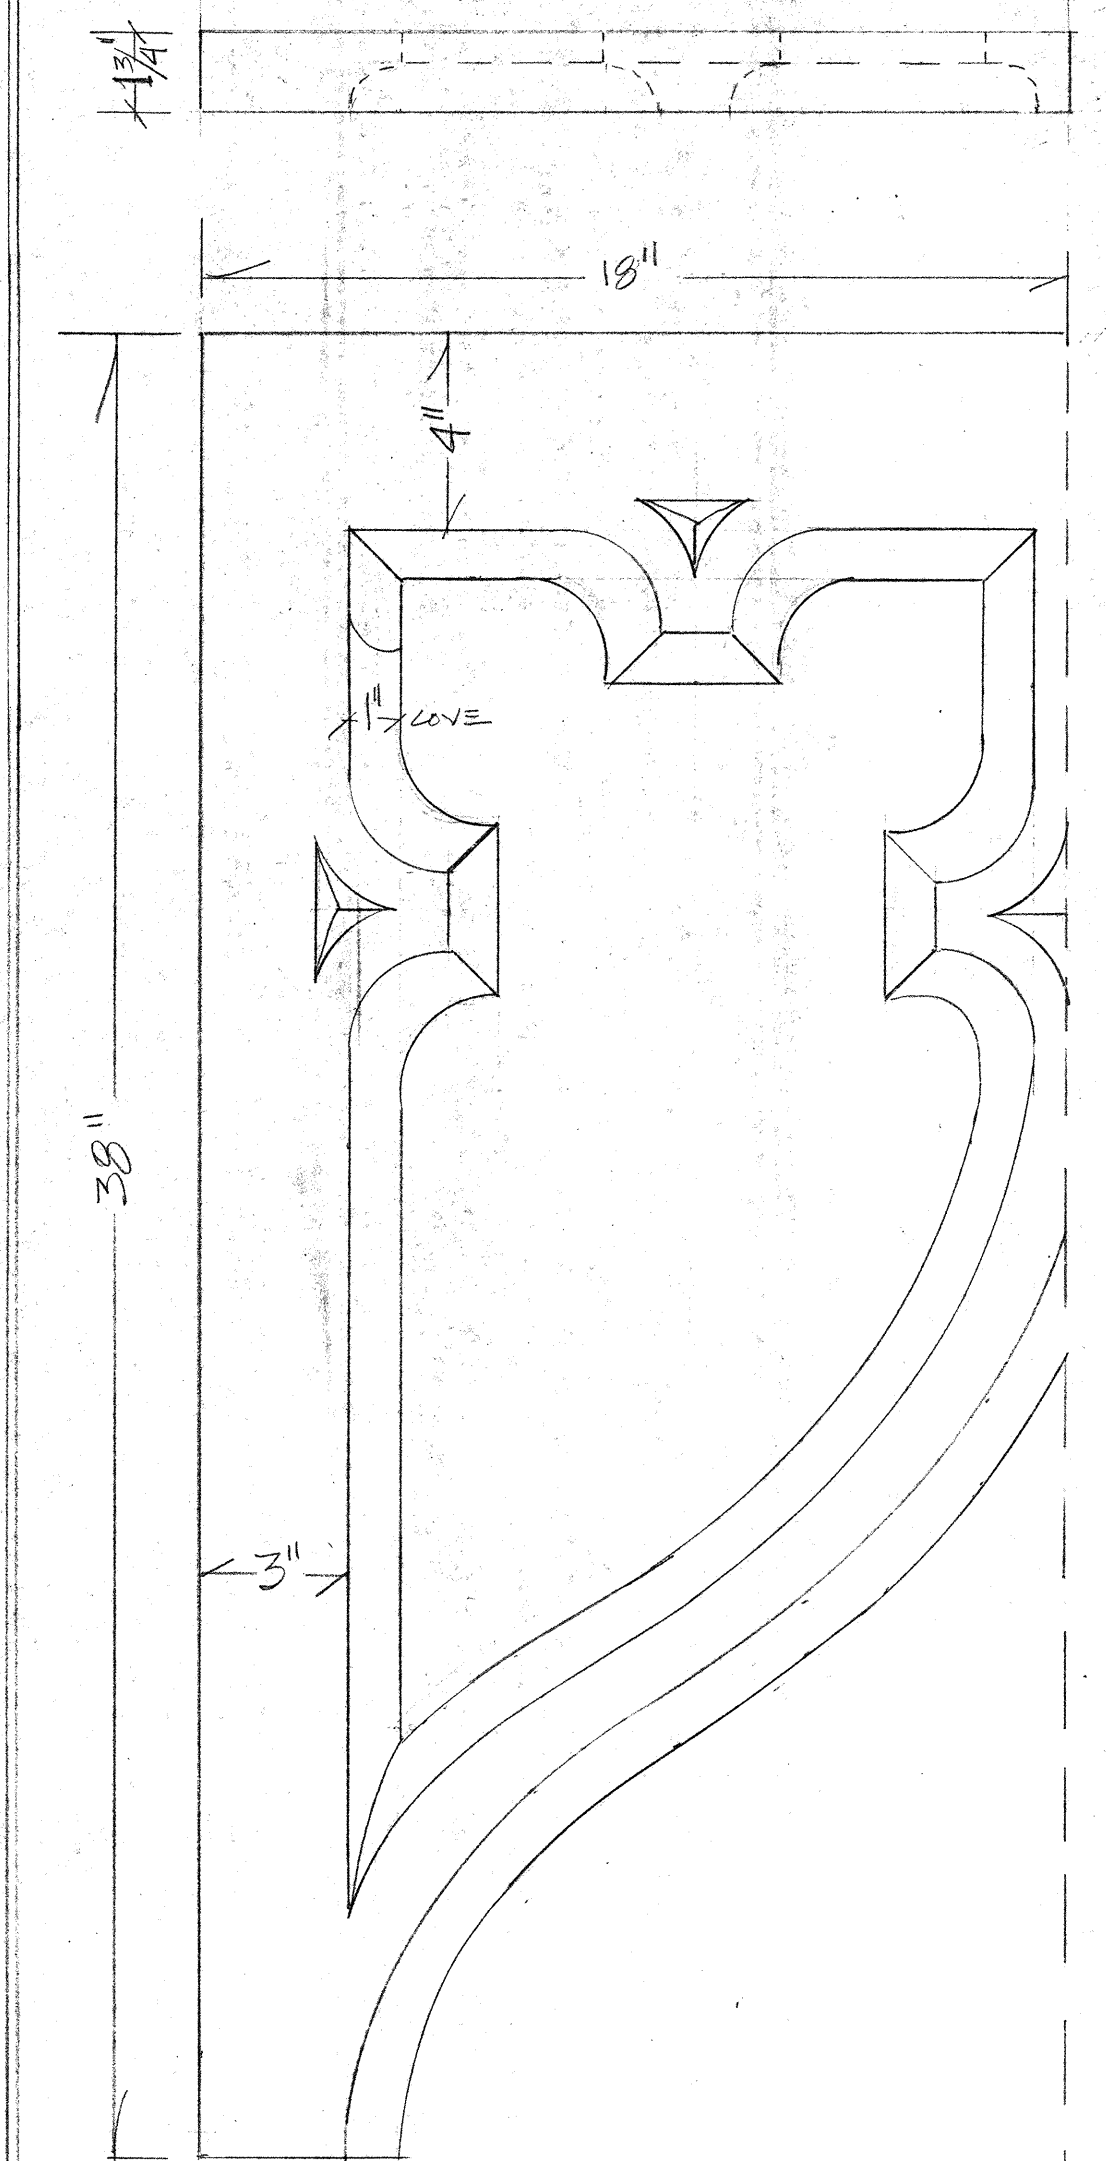

TRACERY DETAIL
SCALE: 1/4" = 1"
TEMPLATE PROVIDED TO WOODWORKERS
BY DESIGNER

2 DETAIL

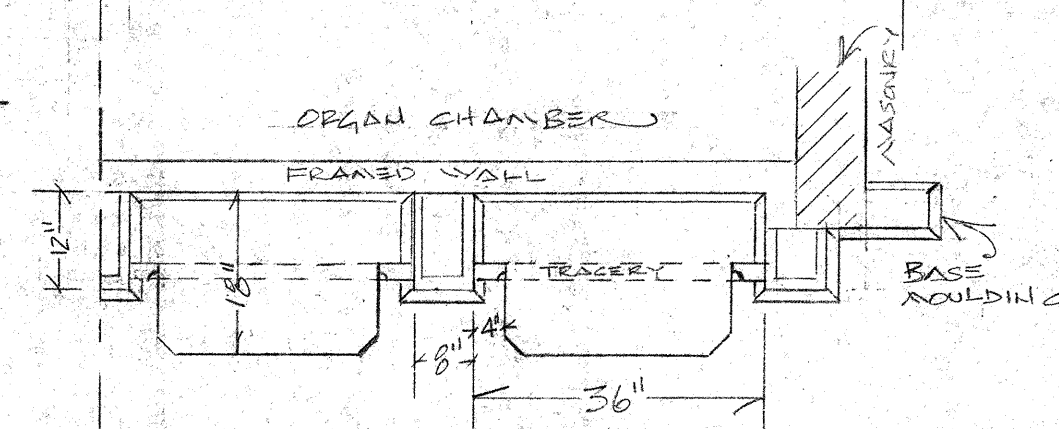

WEST WALL CHANCEL STALL & ORGAN CHAMBER GRILLE
SCALE: 1/2" = 1' 0"
ALL WOODWORK: WALNUT (ROUNDOFFS: MAPLE OR ALDER STAINED TO MATCH)
DUSTY DREAMS DESIGNS 24 AUGUST 2000

SHEET

ID-4

OF

19 OF 44