

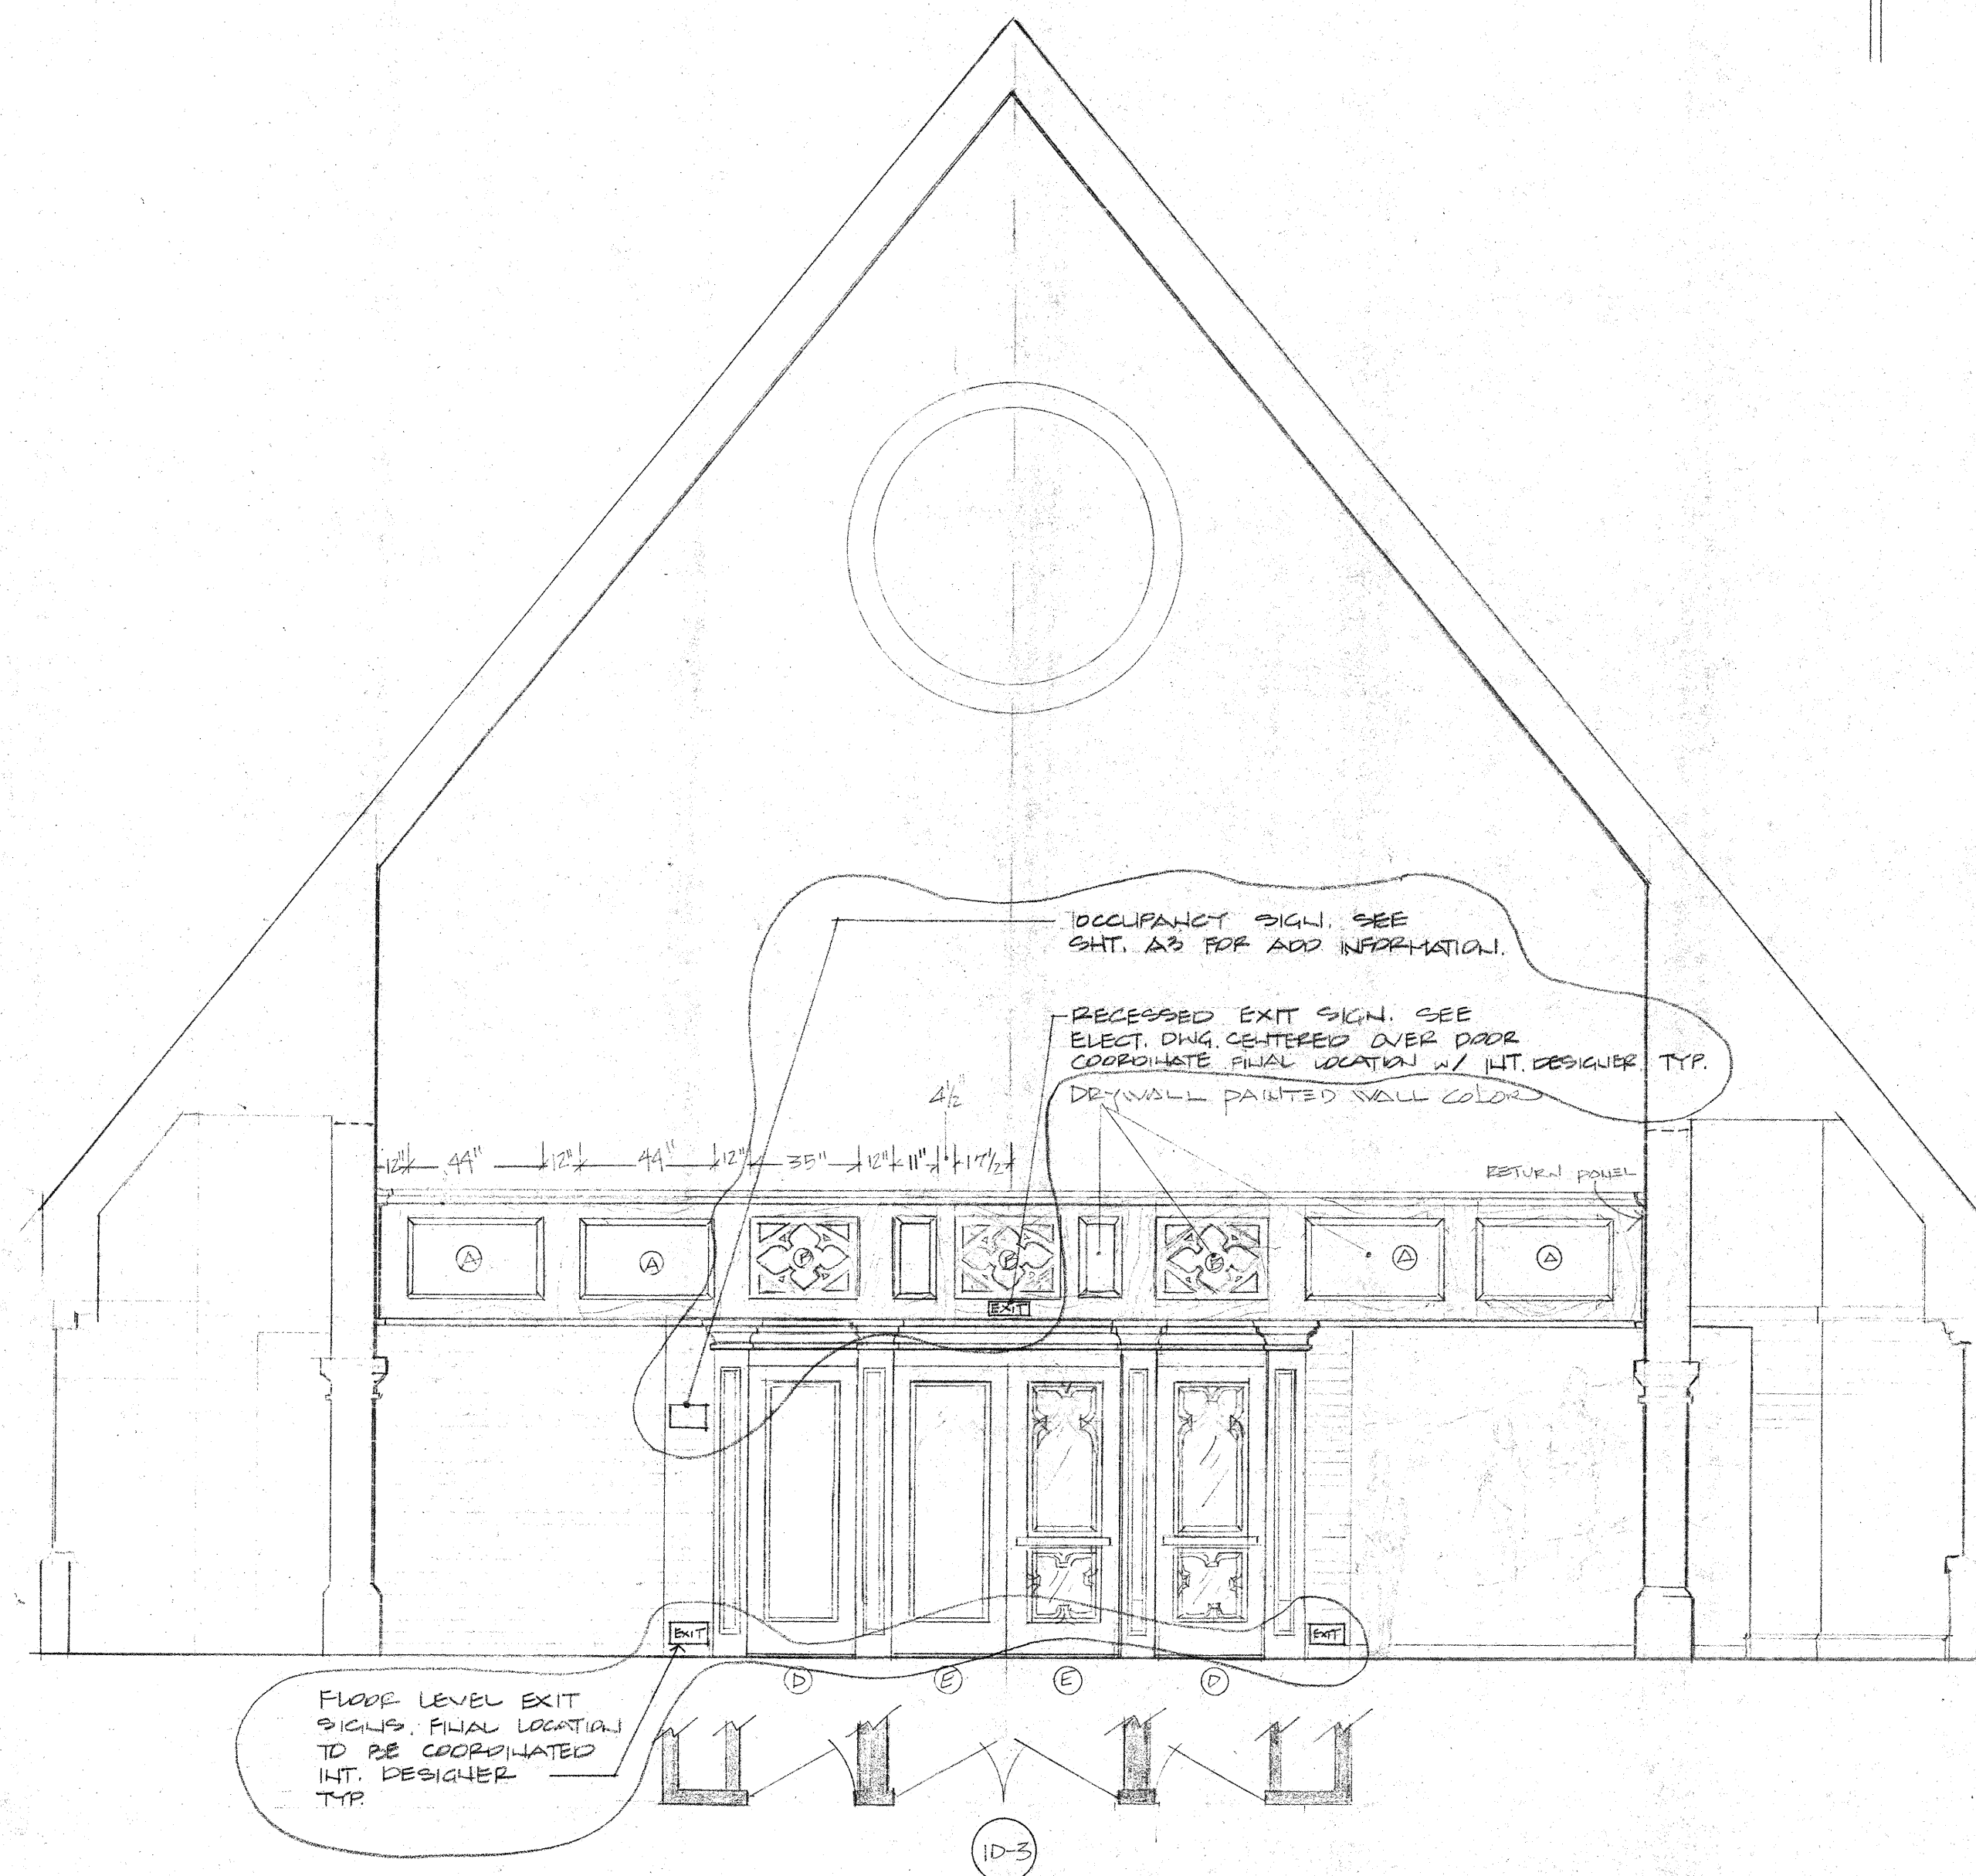


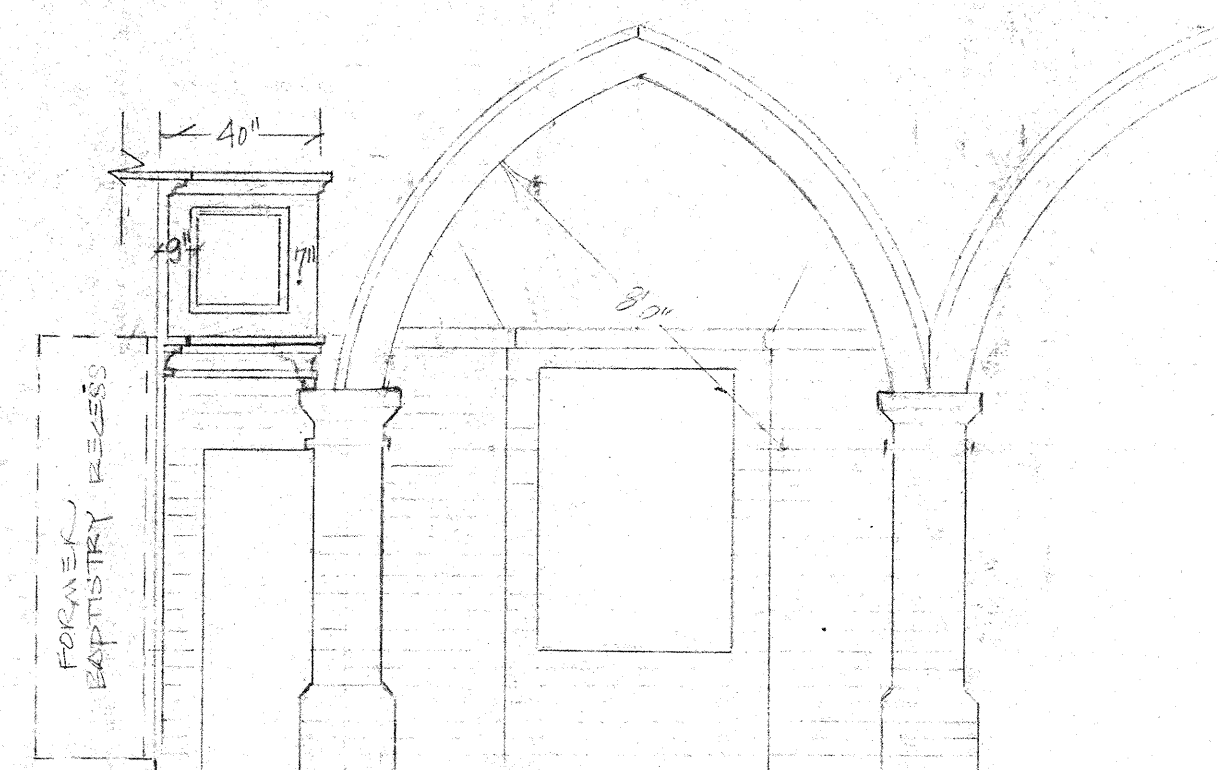


WOODWORK FOR NARTHEX DOORS' SURROUND  
AND  
GALLERY RAIL FACING  
FOR RENOVATION OF ST. EDMUND'S CHURCH  
SAN ANTONIO

SCALE: 1/4"=1'-0"

RHEIT UDICE, DESIGNER  
23.04.12.00

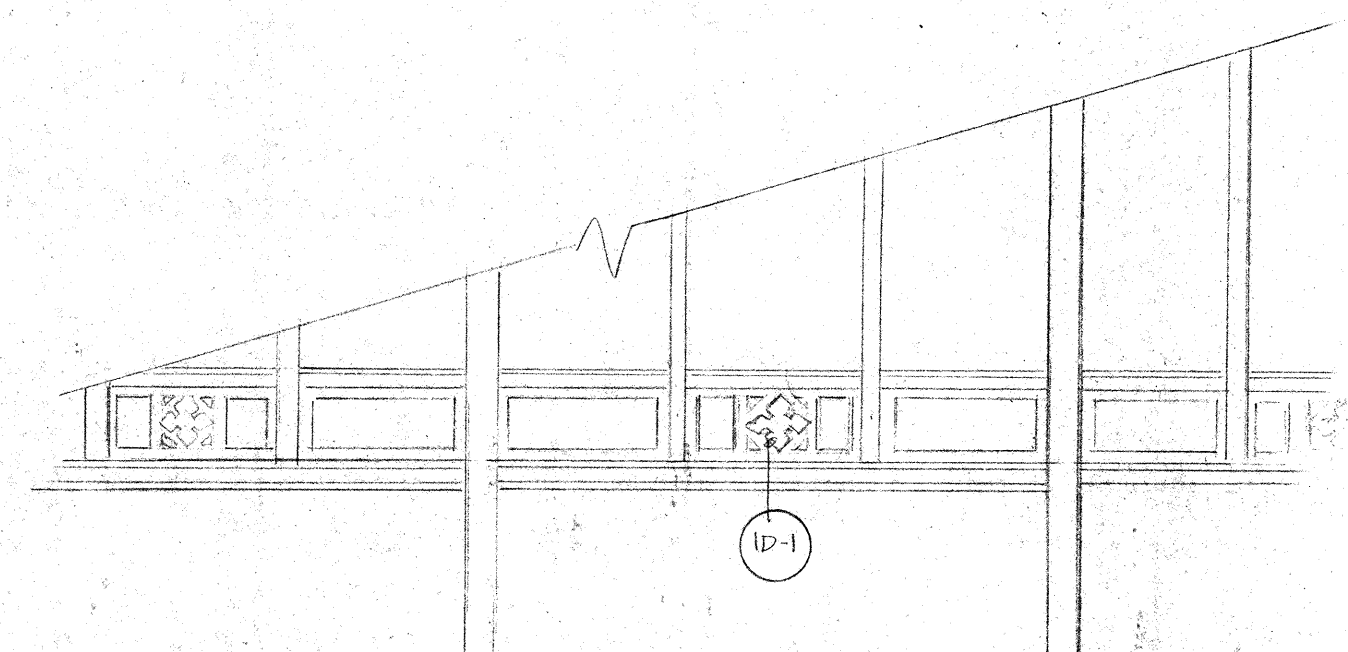

WEST WALL  
TRANSITION AT EAST END OF DECADE TO GALLERY FRONT

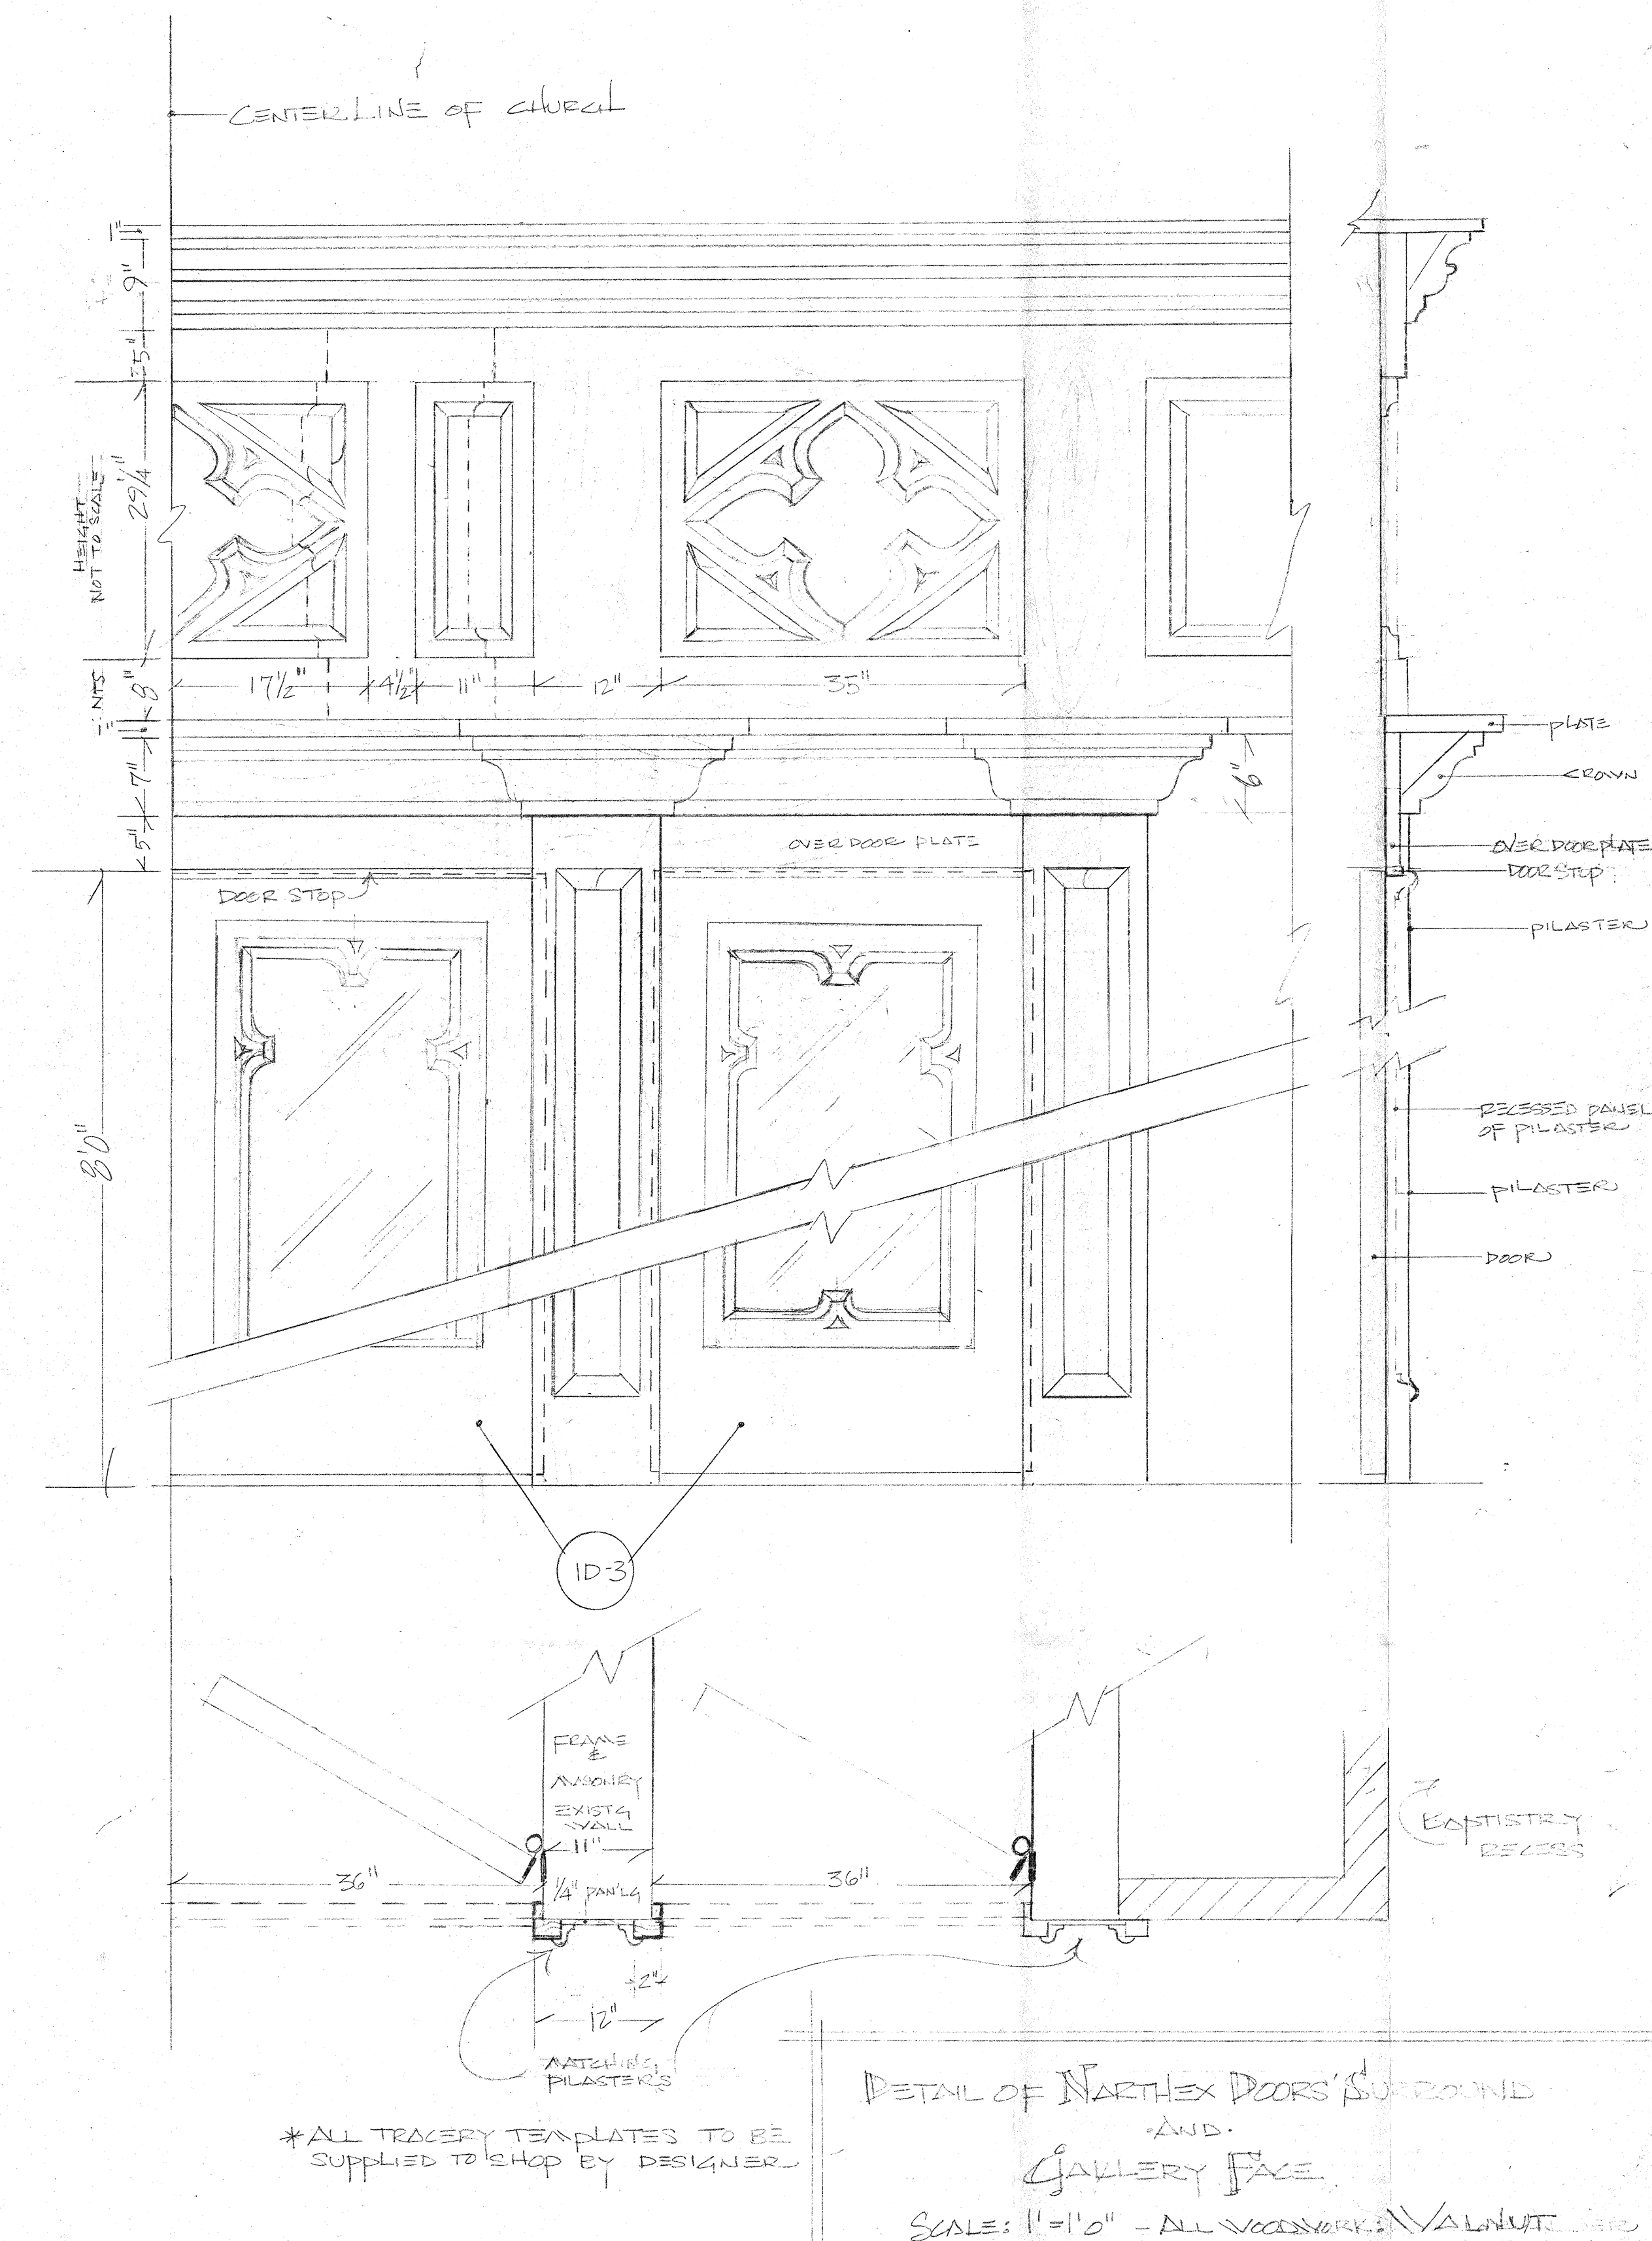

\*ALL TRACERY TEMPLATES TO BE SUPPLIED TO SHOP BY DESIGNER

DETAIL OF NARTHEX DOORS' SURROUND  
AND  
GALLERY FACE

SCALE: 1/2"=1'-0" - ALL WOODWORK: VALNUT