
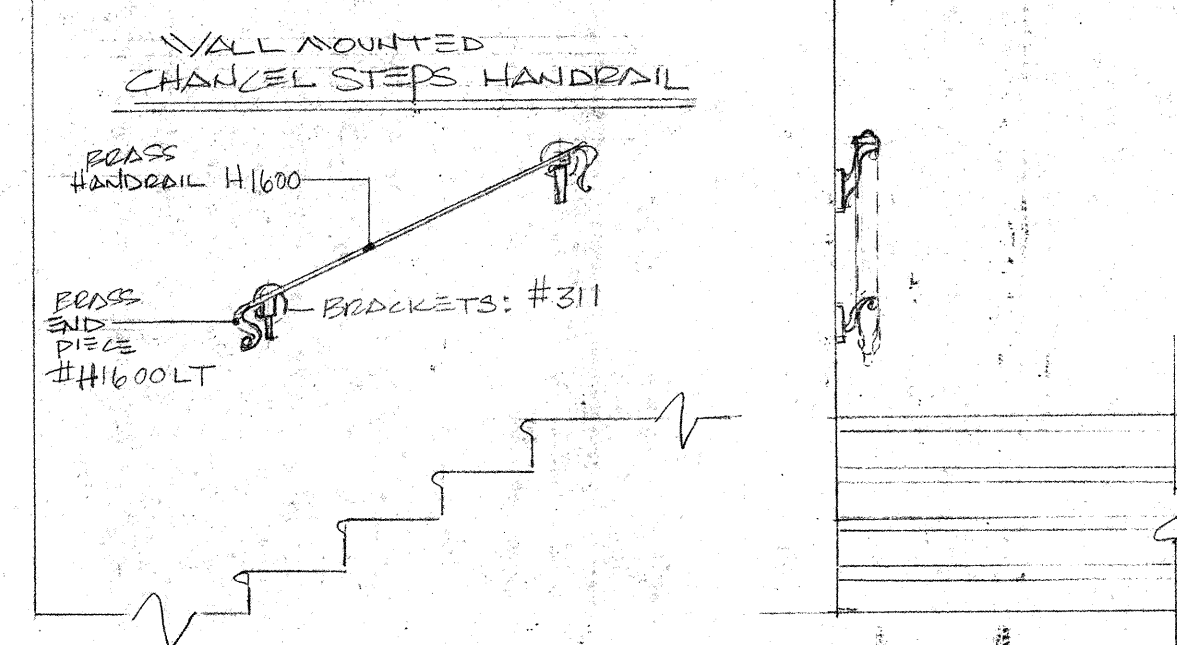


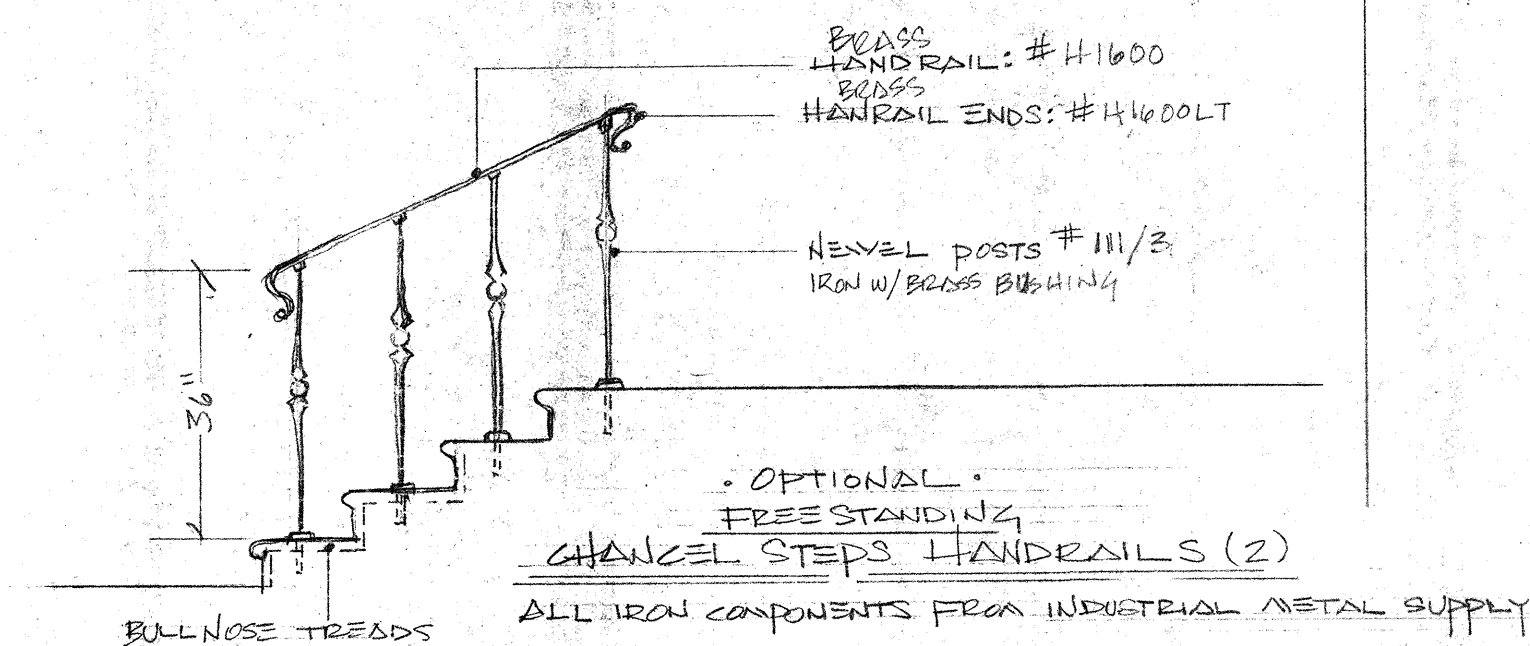


FLOORING COVERAGE


FIELD TILE:	NARTHEX - ENTRANCE & AISLE	210 SF
	NAVE - (INCLUDES SIDE AISLES)	3,900 SF
	CHANCEL - (EXCLUDING STEPS & HIGH ALTAR DAB)	1,046 SF
	CORRIDORS - SACRISTY	489 SF
	PREST SACRISTY	144 SF
	TOTAL:	5,348 SF

BULLNOSE STAIR TREADS FOR CHANCEL STEPS: 136 LF

CARPETING:	NARTHEX -	324 SF	LINOLEUM:	
	STAIR	- 152 SF		WORKING SACRISTY: 190 SF
	BRIDGE	- 323 SF		
	EAST CORRIDOR	- 134 SF		
	WEST CORRIDOR	- 240 SF		
	PREST SACRISTY	- 209 SF		
	TOTAL:	1,381 SF		

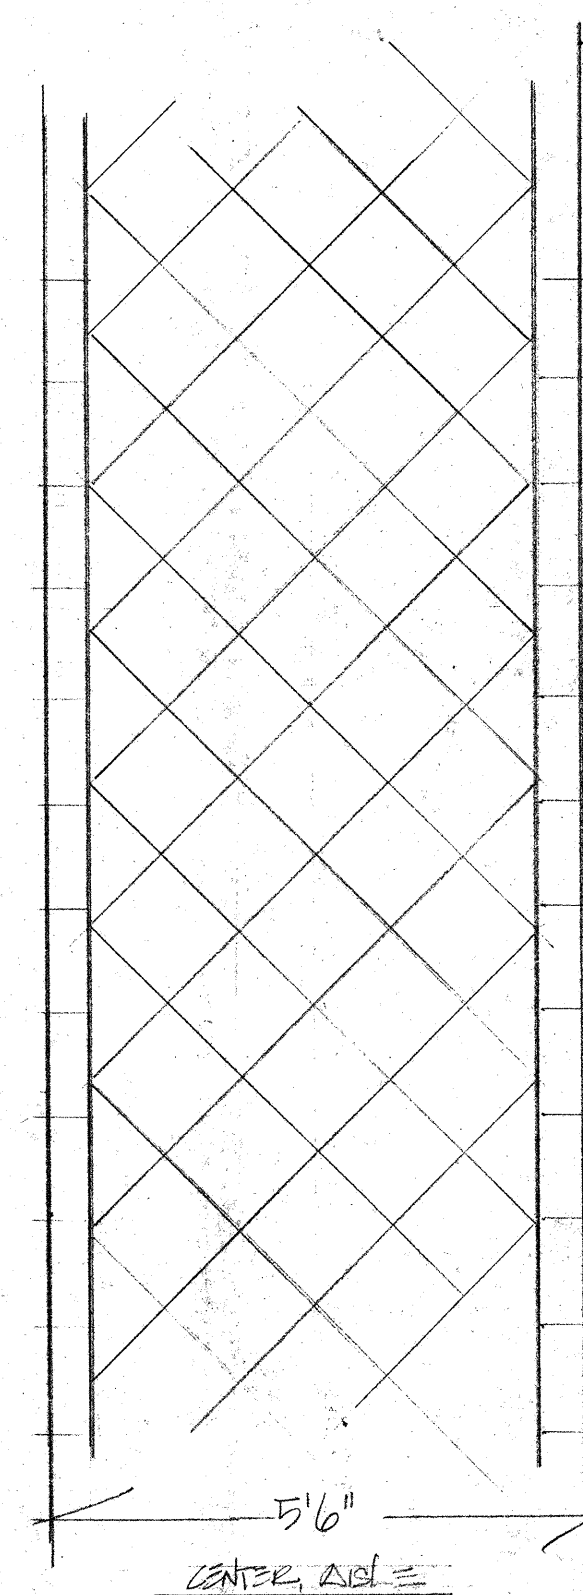

FIELD: 13" X 13" CERAMIC TILE SET DIAGONALLY
 BORDER: 4" X 13" CERAMIC TILE
 1/2" = 1'0"

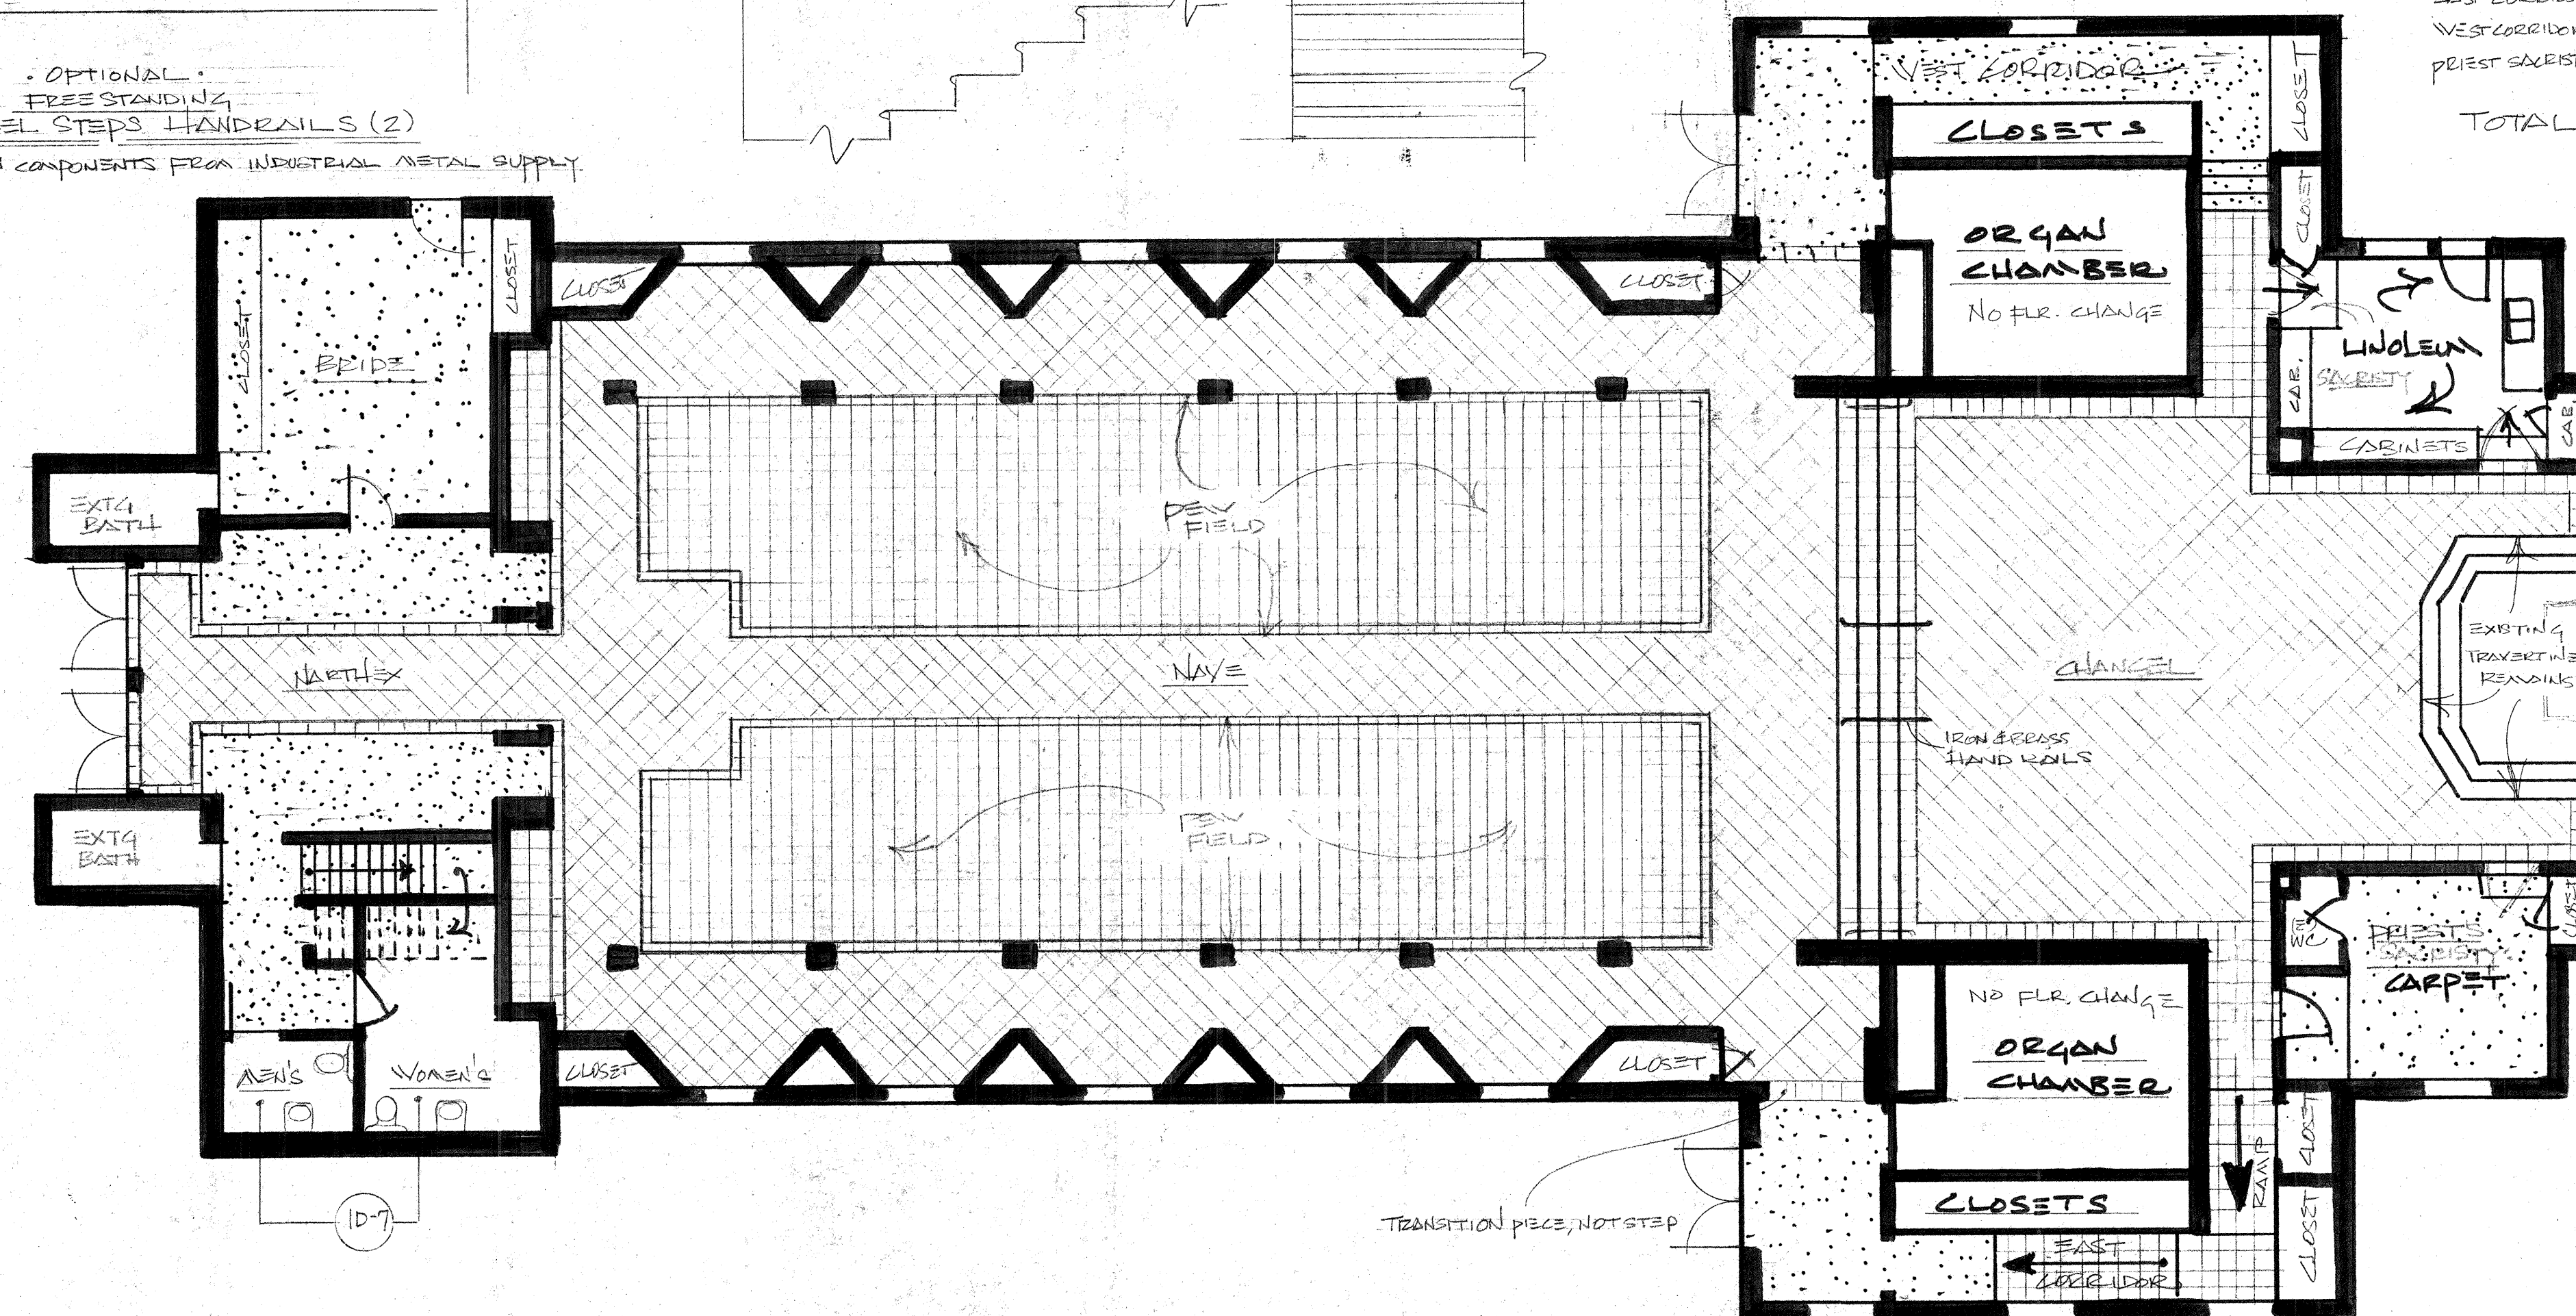

FLOORING SURFACES & PATTERNS
 FOR ST. EDMUND'S CHURCH, SAN MARINO
 DAVID VOICE, DESIGNER 1/8" = 1'0"

