

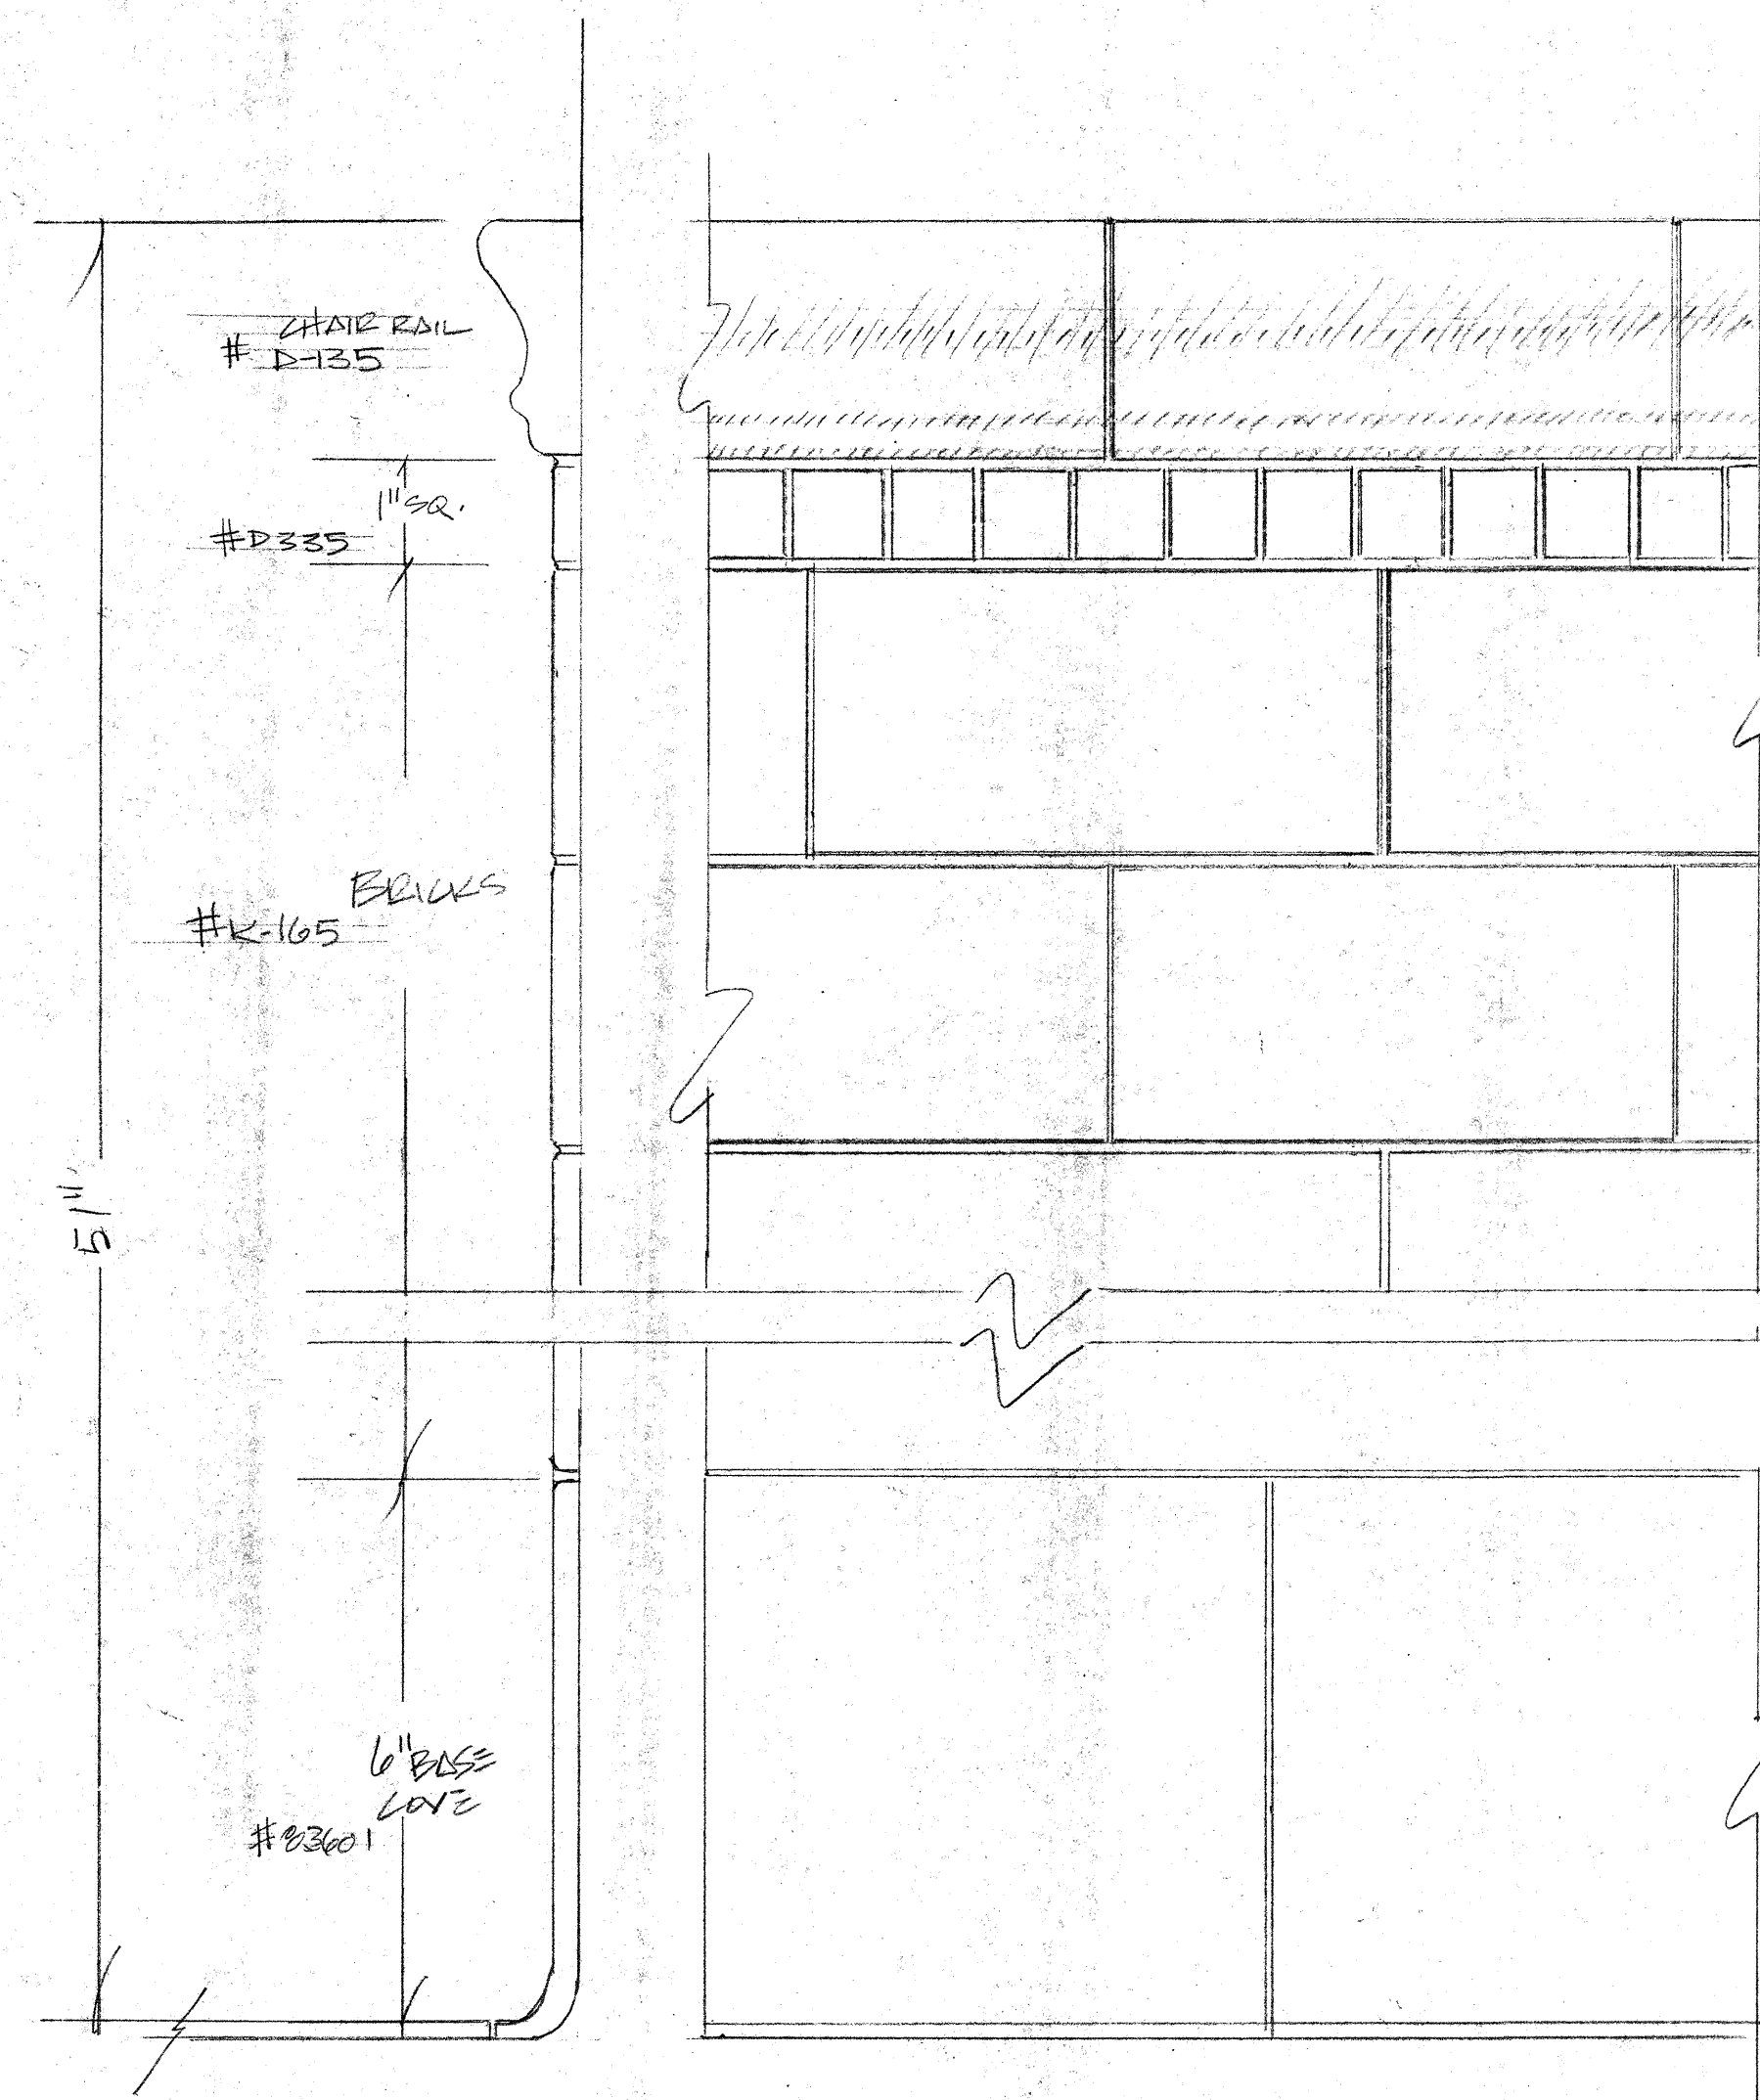
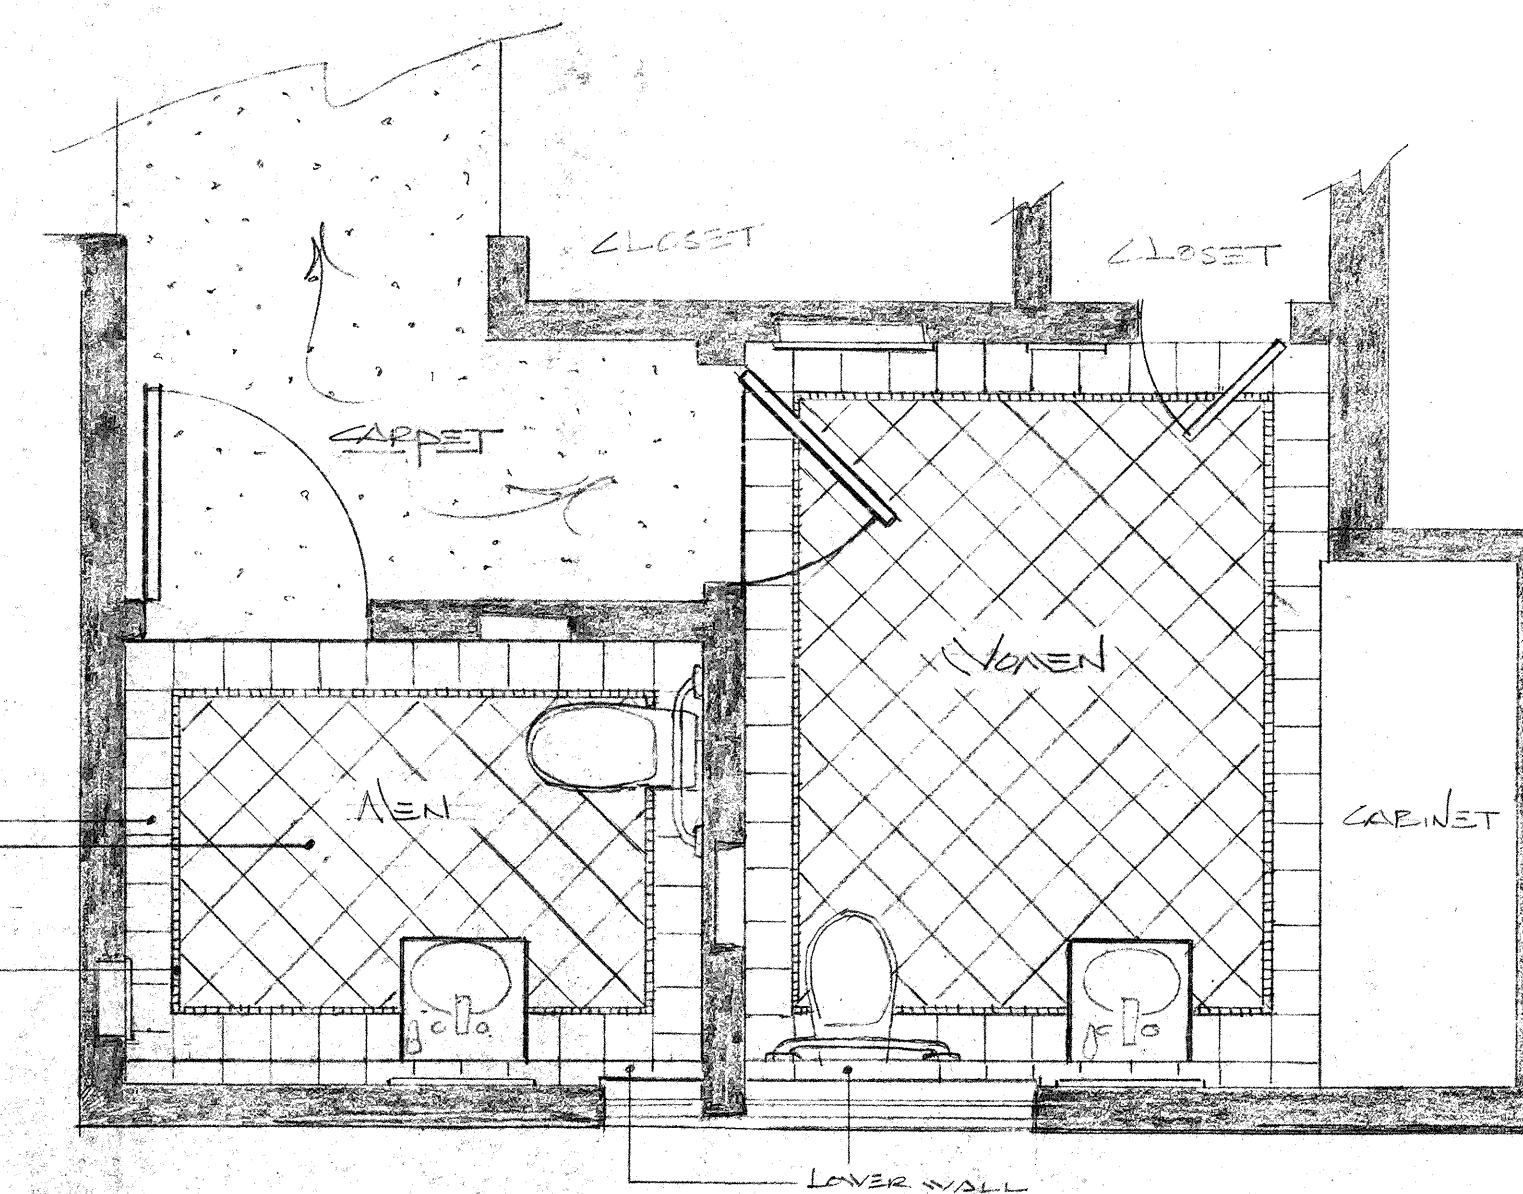
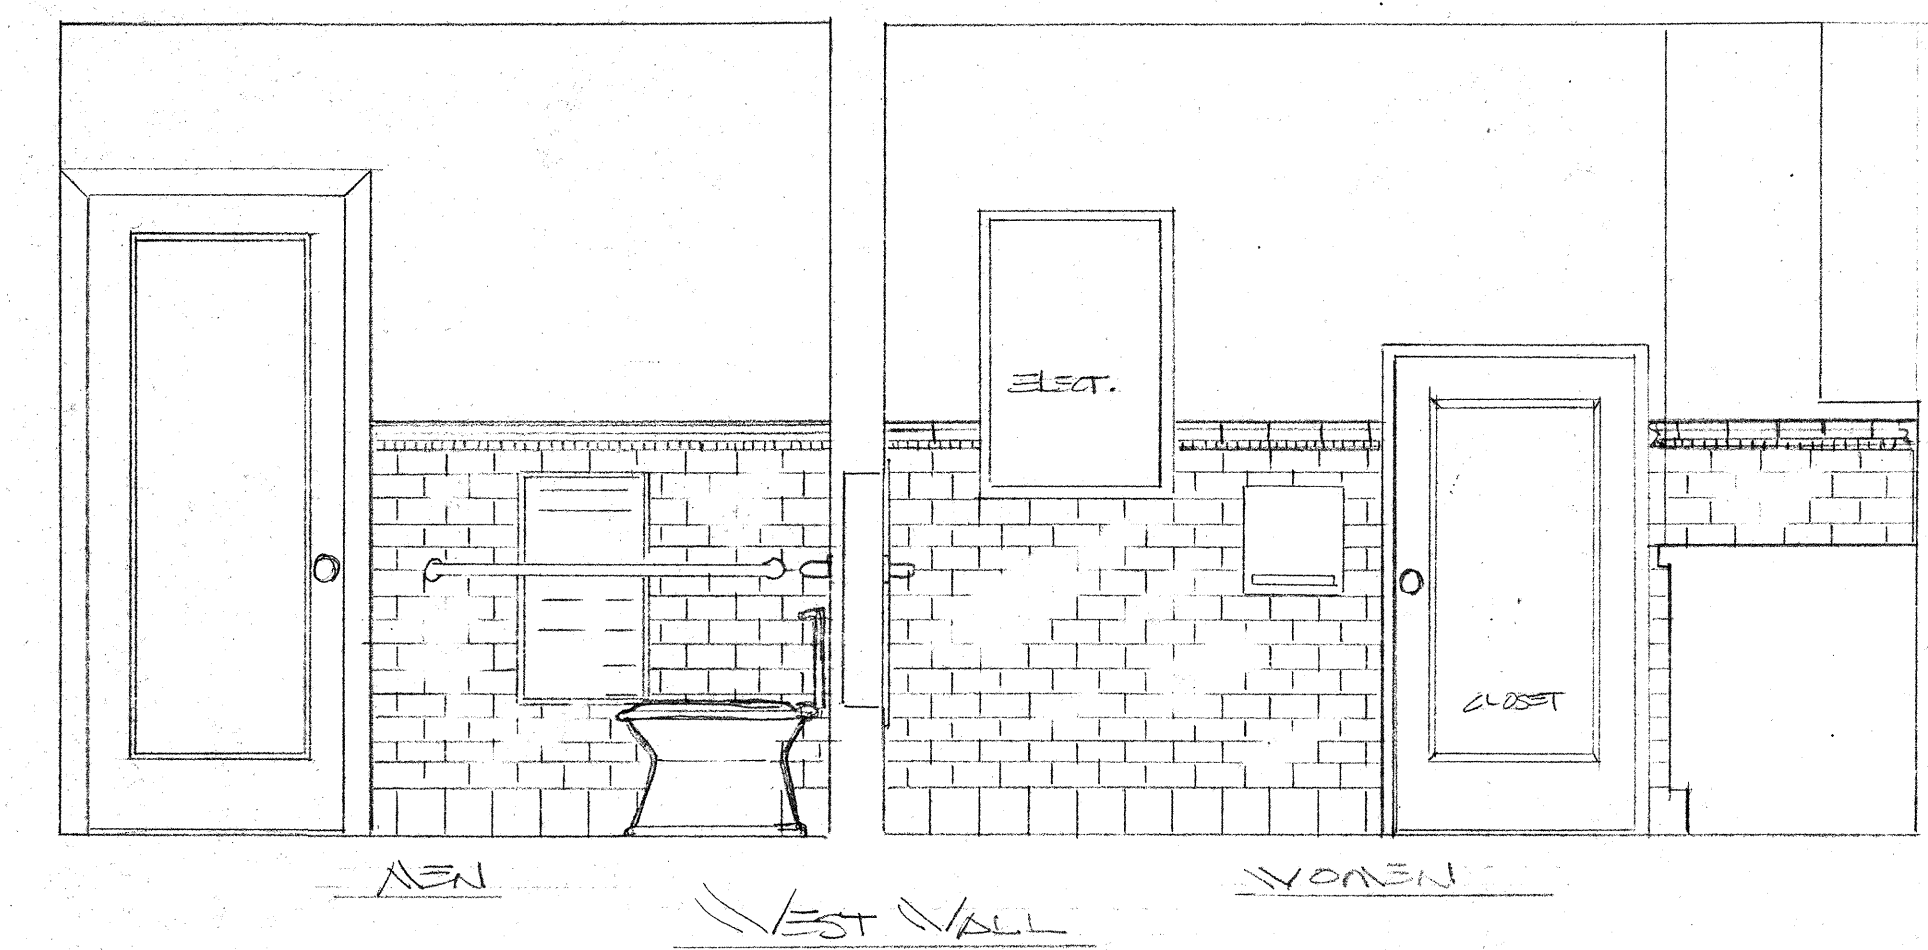


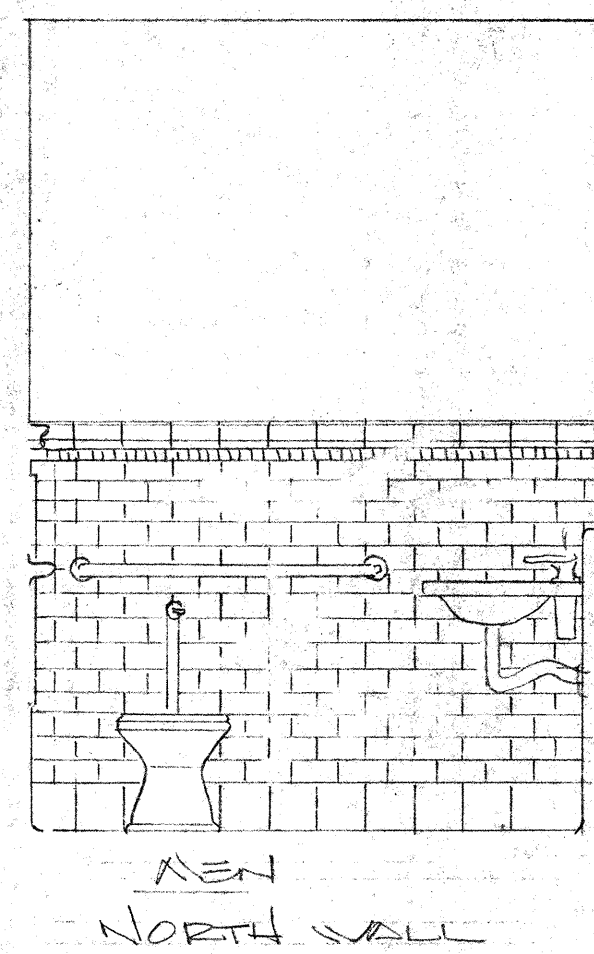

TILE VANSCOTTING DETAIL
1/2" = 1"

ALL TILE COLOR: ALMOND
SUPPLIER: DAL TILE

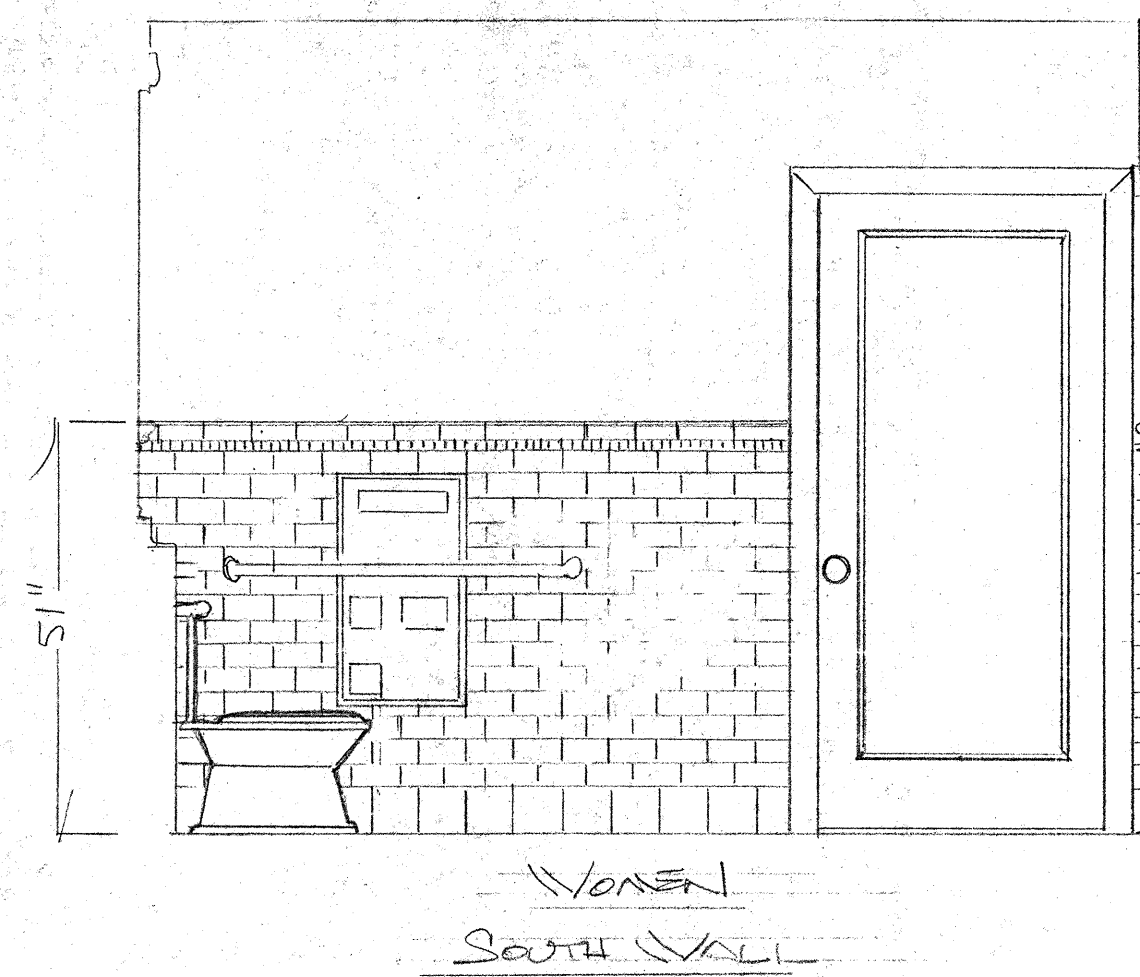

CONC. GRADE
NOTE FINISH - 8" x 8"
2007
1/4" = 1' 0"

TILE PATTERN FOR FLOOR USING 6" X 6" CONC. GR. NOTE FINISH

TILE DETAIL FOR NEW
MEN'S & WOMEN'S RESTROOMS
FOR FURTHER DETAILS SEE PG. (A8)
SCALE: 1/2" = 1' 0" EAST /UDICE