


V: DRAWINGS/SEE-1901/S-1.dwg Mon Dec 18 17:10:35 2000

ISSUE RECORD		
4-19-00	35%	
9-11-00	90%	
11-16-00	100%	
12-18-00	QC RESPONSE	

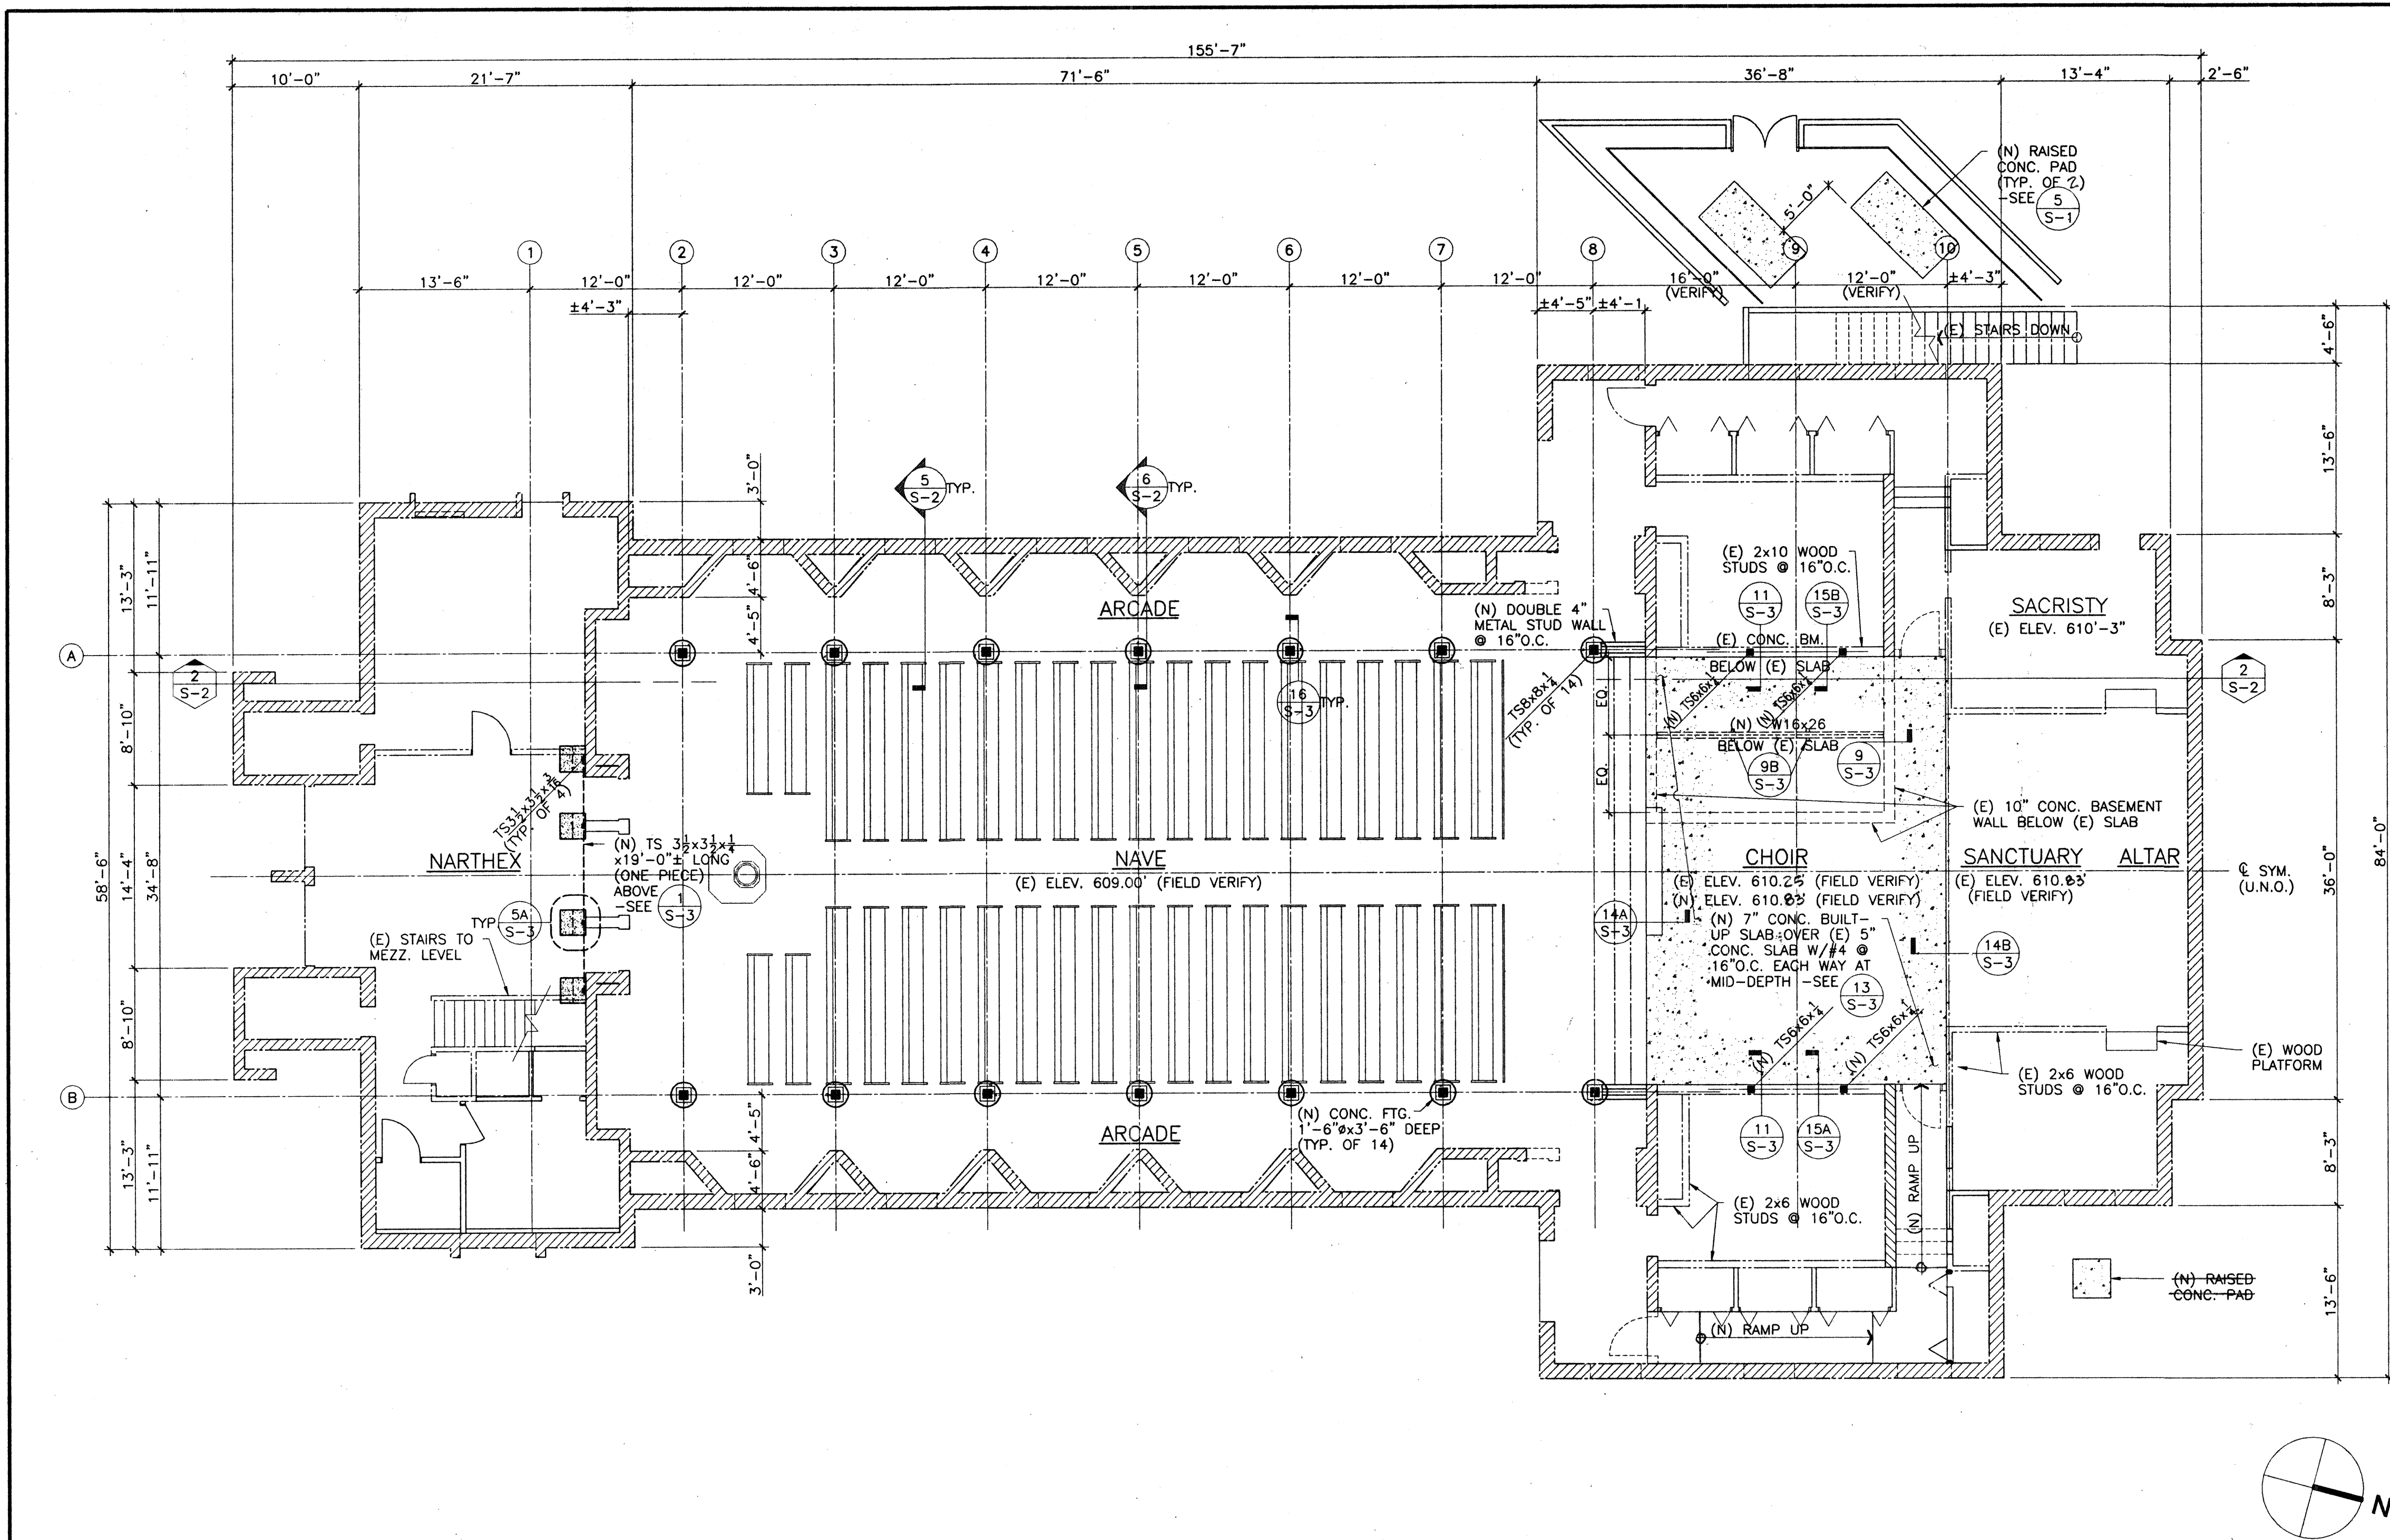

- GENERAL NOTES:**
1. VERIFY ALL DIMENSIONS AND CONDITIONS AT THE SITE.
 2. COORDINATE STRUCTURAL DETAILS AND DIMENSIONS WITH RELATED REQUIREMENTS ON OTHER DRAWINGS.
 3. THE ARCHITECT WILL INTERPRET THE INTENT OF THE DOCUMENTS IN CASE OF POSSIBLE CONFLICT OR DISCREPANCY BETWEEN STRUCTURAL AND OTHER DISCIPLINES.
 4. DETAILS NOTED AS "TYPICAL" OR "TYP" APPLY IN ALL CASES WHETHER OR NOT SPECIFICALLY REFERENCED.
 5. WORKMANSHIP AND MATERIALS SHALL CONFORM TO THE REQUIREMENTS OF THE 1997 UNIFORM BUILDING CODE.
 6. ASSUMED NATIVE SOIL TYPE: SAND - MODERATE TO DENSE. ASSUMED DESIGN SOIL BEARING: 1000 P.S.F. DL + LL. ASSUMED LATERAL PASSIVE PRESSURE: 150 P.S.F./FT. OF DEPTH.

- MATERIAL REQUIREMENTS**
- CONCRETE:** f'c = 2500 psi NORMAL WEIGHT AGGREGATES MINIMUM CEMENT CONTENT 5.5 SACKS PER CUBIC YARD, MAXIMUM WATER-CEMENT RATIO = 0.55
- REINFORCING STEEL:** ASTM A 615 GRADE 60 EXCEPT #3-GRADE 40
- STRUCTURAL STEEL:** ASTM A 36
- STRUCTURAL STEEL TUBES:** ASTM A500 GRADE B
- BOLTS :** ASTM A 307
- ANCHOR BOLTS :** ASTM A 307
- EXPANSION TYPE CONCRETE ANCHORS :** HDI (ICBO ER-2895) OR KWIK BOLT II (ICBO ER-4627) AS MANUFACTURED BY HILTI FASTENING SYSTEMS, INC.
- EPOXY DOWEL ANCHORS:** HY-150 (ICBO ER-5193) AS MANUFACTURED BY HILTI FASTENING SYSTEMS, INC.
- POWDER ACTUATED FASTENERS:** X-ZF (ICBO ER-4627) AS MANUFACTURED BY HILTI FASTENING SYSTEMS, INC.
- LIGHT GAGE STEEL FASTENERS:** TEKS SCREWS AS MANUFACTURED BY BUILDEX DIVISION, I.T.W., INC. (C.O.L.A. RR 23768)
- LIGHT GAGE STEEL:** ASTM A 570 GRADE 50
- METAL STUDS:** 4" WIDE, PUNCHED CEE STUDS, 20 GAGE WITH 1 5/8" FLANGES, CEMCO SERIES 'CS' (ICBO ER-3403P) OR EQUIVALENT.
- S4S TIMBER FRAMING:** DOUGLAS FIR/LARCH No.2 OR BETTER. PROVIDE PRESSURE TREATED DOUGLAS FIR FOR MEMBERS IN CONTACT WITH CONCRETE.
- PLYWOOD:** U.S. PRODUCT STD. PS 1-98, STRUCTURAL I RATED SHEATHING, EXPOSURE 1.

NOTE: THE CONTRACTOR IS RESPONSIBLE FOR CONSTRUCTION SAFETY. STRUCTURAL DRAWINGS AND SPECIFICATIONS DO NOT INCLUDE NECESSARY COMPONENTS FOR CONSTRUCTION SAFETY.

GENERAL NOTES

TABLE 23-II-B-1 NAILING SCHEDULE

CONNECTION	NAILING ¹
1. JOIST TO SILL OR GIRDER, TOENAIL	3-8d
2. BRIDGING TO JOIST, TOENAIL EACH END	2-8d
7. TOP PLATE TO STUD, END NAIL	2-16d
8. STUD TO SOLE PLATE	4-8d, TOENAIL OR 2-16d, END NAIL
9. DOUBLE STUDS, FACE NAIL	16d AT 24" (610mm) O.C.
10. DOUBLE TOP PLATES, TYPICAL FACE NAIL	16d AT 16" (406mm) O.C.
11. BRIDGING BETWEEN JOISTS OR RAFTERS TO TOP PLATE, TOENAIL	3-8d
12. RIM JOIST TO TOP PLATE, TOENAIL	8d AT 6" (152mm) O.C.
13. TOP PLATES, LAPS AND INTERSECTIONS, FACE NAIL	2-16d
14. CONTINUOUS HEADER, TWO PIECES	16d AT 16" (406mm) O.C. ALONG EACH EDGE
15. CEILING JOISTS TO PLATE, TOENAIL	3-8d
16. CONTINUOUS HEADER TO STUD, TOENAIL	4-8d
17. CEILING JOISTS, LAPS OVER PARTITIONS, FACE NAIL	3-16d
18. CEILING JOISTS TO PARALLEL RAFTERS, FACE NAIL	3-16d
19. RAFTERS TO PLATE, TOENAIL	3-8d
20. BUILT-UP CORNER STUDS	16d AT 24" (610mm) O.C.
26. WOOD STRUCTURAL PANELS AND PARTICLEBOARD: SUBFLOOR AND WALL SHEATHING (TO FRAMING): 19/32" - 3/4" (15mm - 19mm)	8d ³ OR 6d ³

¹COMMON OR BOX NAILS MAY BE USED EXCEPT WHERE OTHERWISE STATED.

FOUNDATION/FIRST FLOOR PLAN

1/8" = 1'

NAILING SCHEDULE

MATERIALS	SYMBOLS
CONCRETE	NUMBER REF. DETAIL OR SECTION SHEET REF.
MASONRY	NUMBER REF. WALL ELEVATION SHEET REF.
STEEL	FINISH ELEVATION
CONTINUOUS WOOD MEMBER	(E) INDICATES EXISTING
EARTH	(N) OR NO DESIGNATION INDICATES NEW

LEGEND

- S-1 FOUNDATION/FIRST FLOOR FRAMING PLAN AND DETAILS
- S-2 NEW INTERIOR WALL ELEVATIONS & SECTIONS
- S-3 SECTIONS & DETAILS

STRUCTURAL SHEET INDEX

TYP. EPOXY DOWEL DETAIL

2

SAWCUT DETAIL

3

-

-

TYP. RAISED CONC. PAD

5


Onuma & Associates

Architecture, Planning, Consulting
511 Mission Street
South Pasadena, CA 91030
tel 626. 799. 9920
fax 626. 799. 8260
e-mail: info@onuma.com

Consultants

KANDA | TSO

KANDA AND TSO ASSOCIATES
CONSULTING STRUCTURAL ENGINEERS
511 MISSION STREET
SOUTH PASADENA, CA 91030-3035
TEL (626) 441-1211
FAX (626) 441-1011

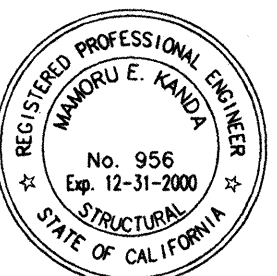

RENOVATION PROJECT FOR SAINT EDMUND'S EPISCOPAL CHURCH

1175 SAN GABRIEL BLVD., SAN MARINO, CA., 91108-8048

STAMPS

REVISIONS

DESCRIPTION	DATE	BY

PROJECT NUMBER **2000**

SCALE **AS NOTED**

PRINTED **12-18-00**

TITLE **FOUNDATION/FIRST FLOOR FRAMING PLAN AND DETAILS**

SHEET

S-1

23 OF 44