



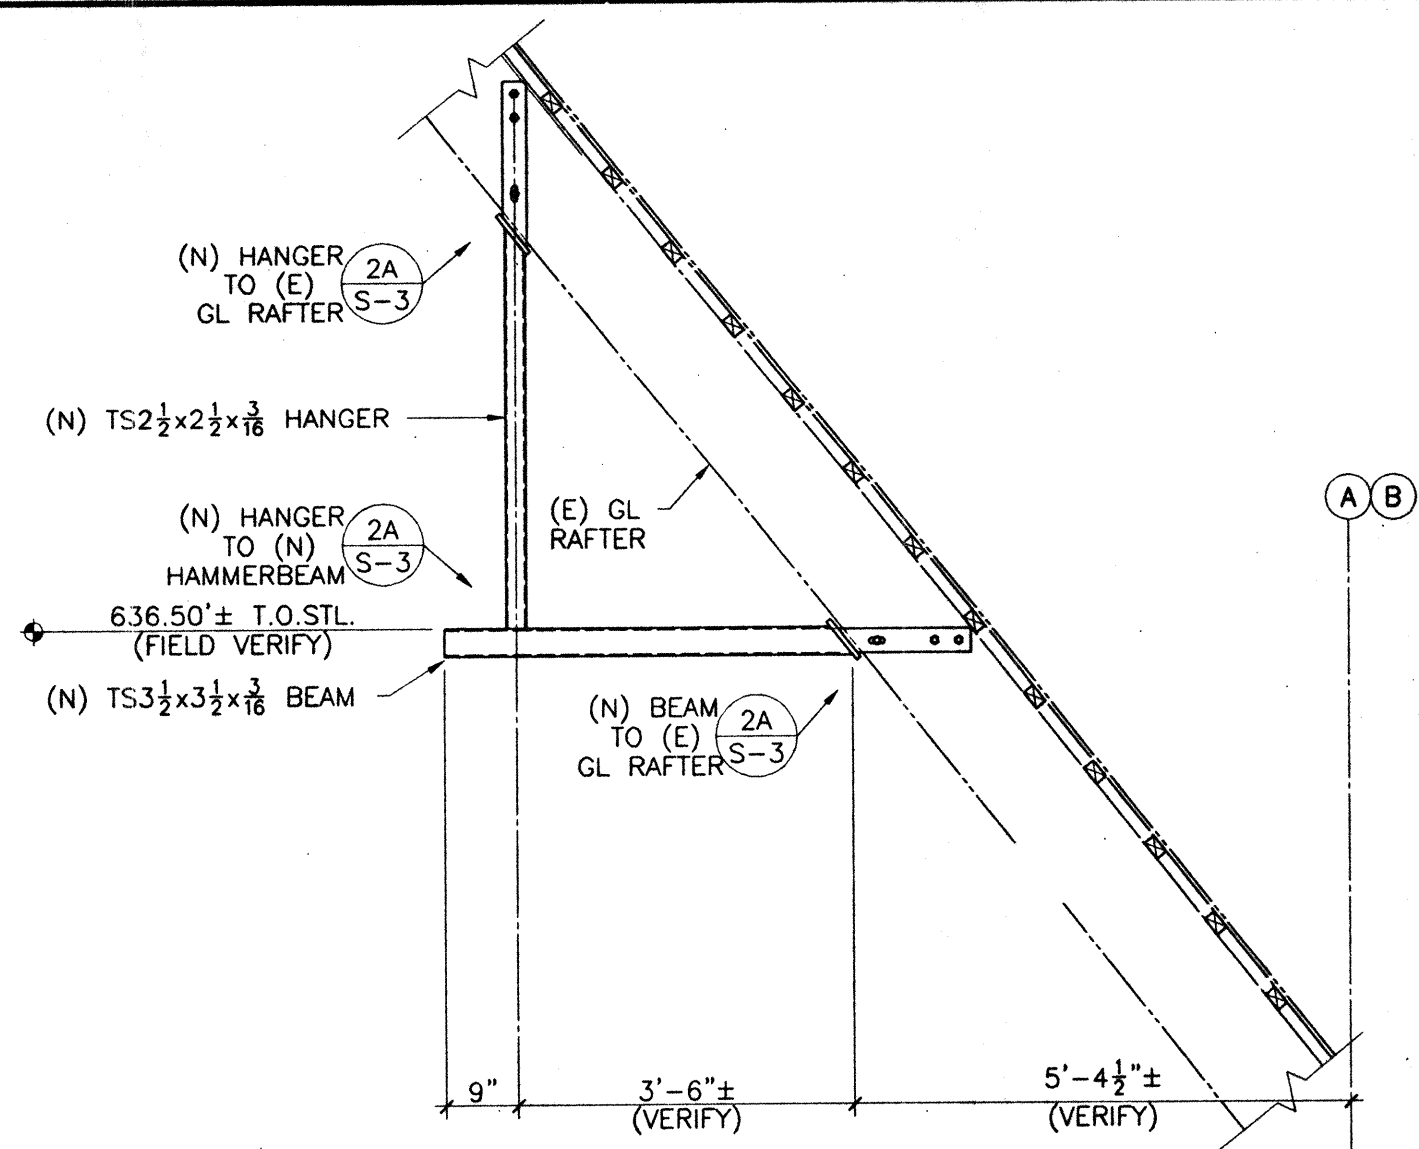


HAMMERBEAM AT SANCTUARY

1/2" 1

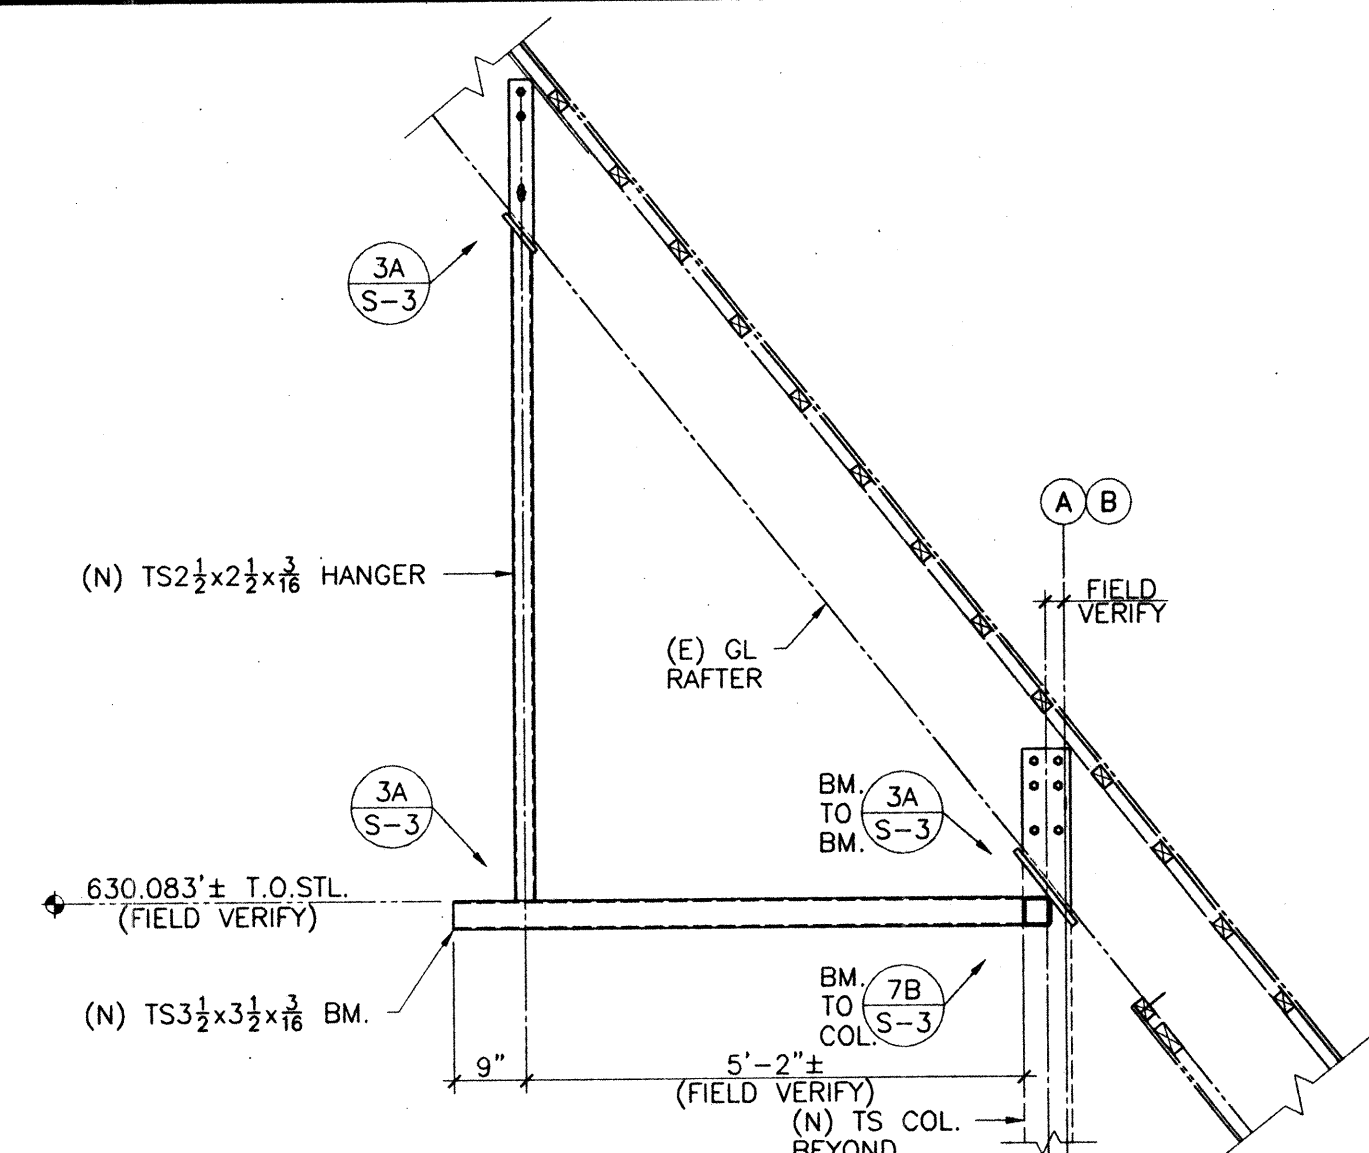


HAMMERBEAM AT CHOIR LEVEL

1/2" 3

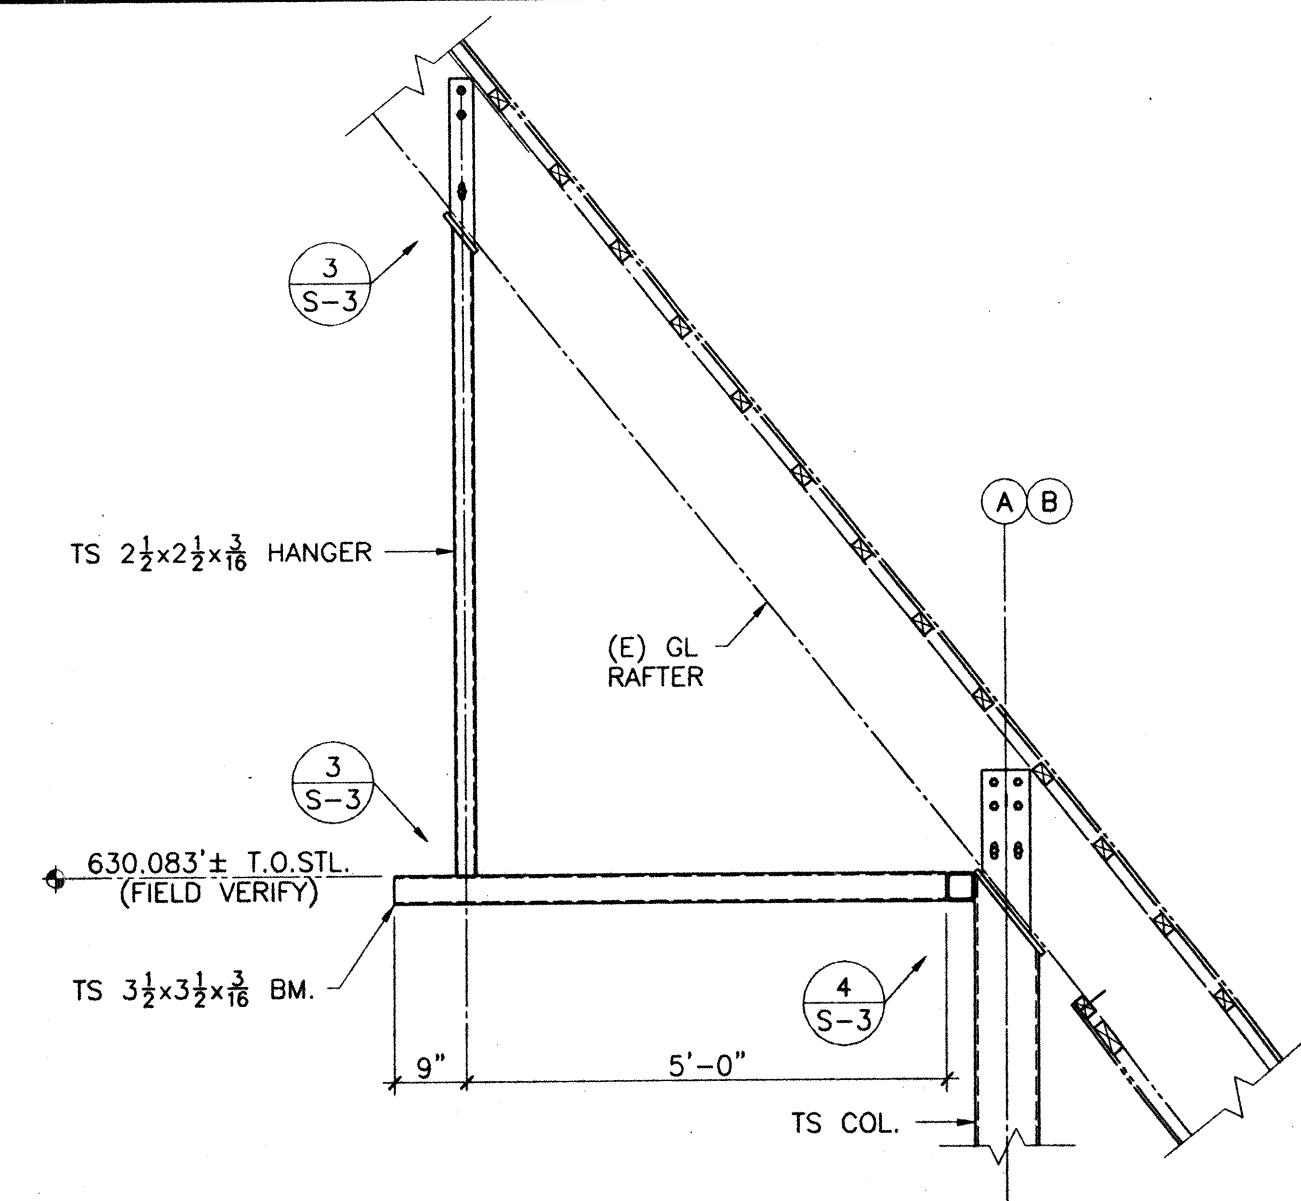


TYPICAL HAMMERBEAM AT NAVE

1/2" 4

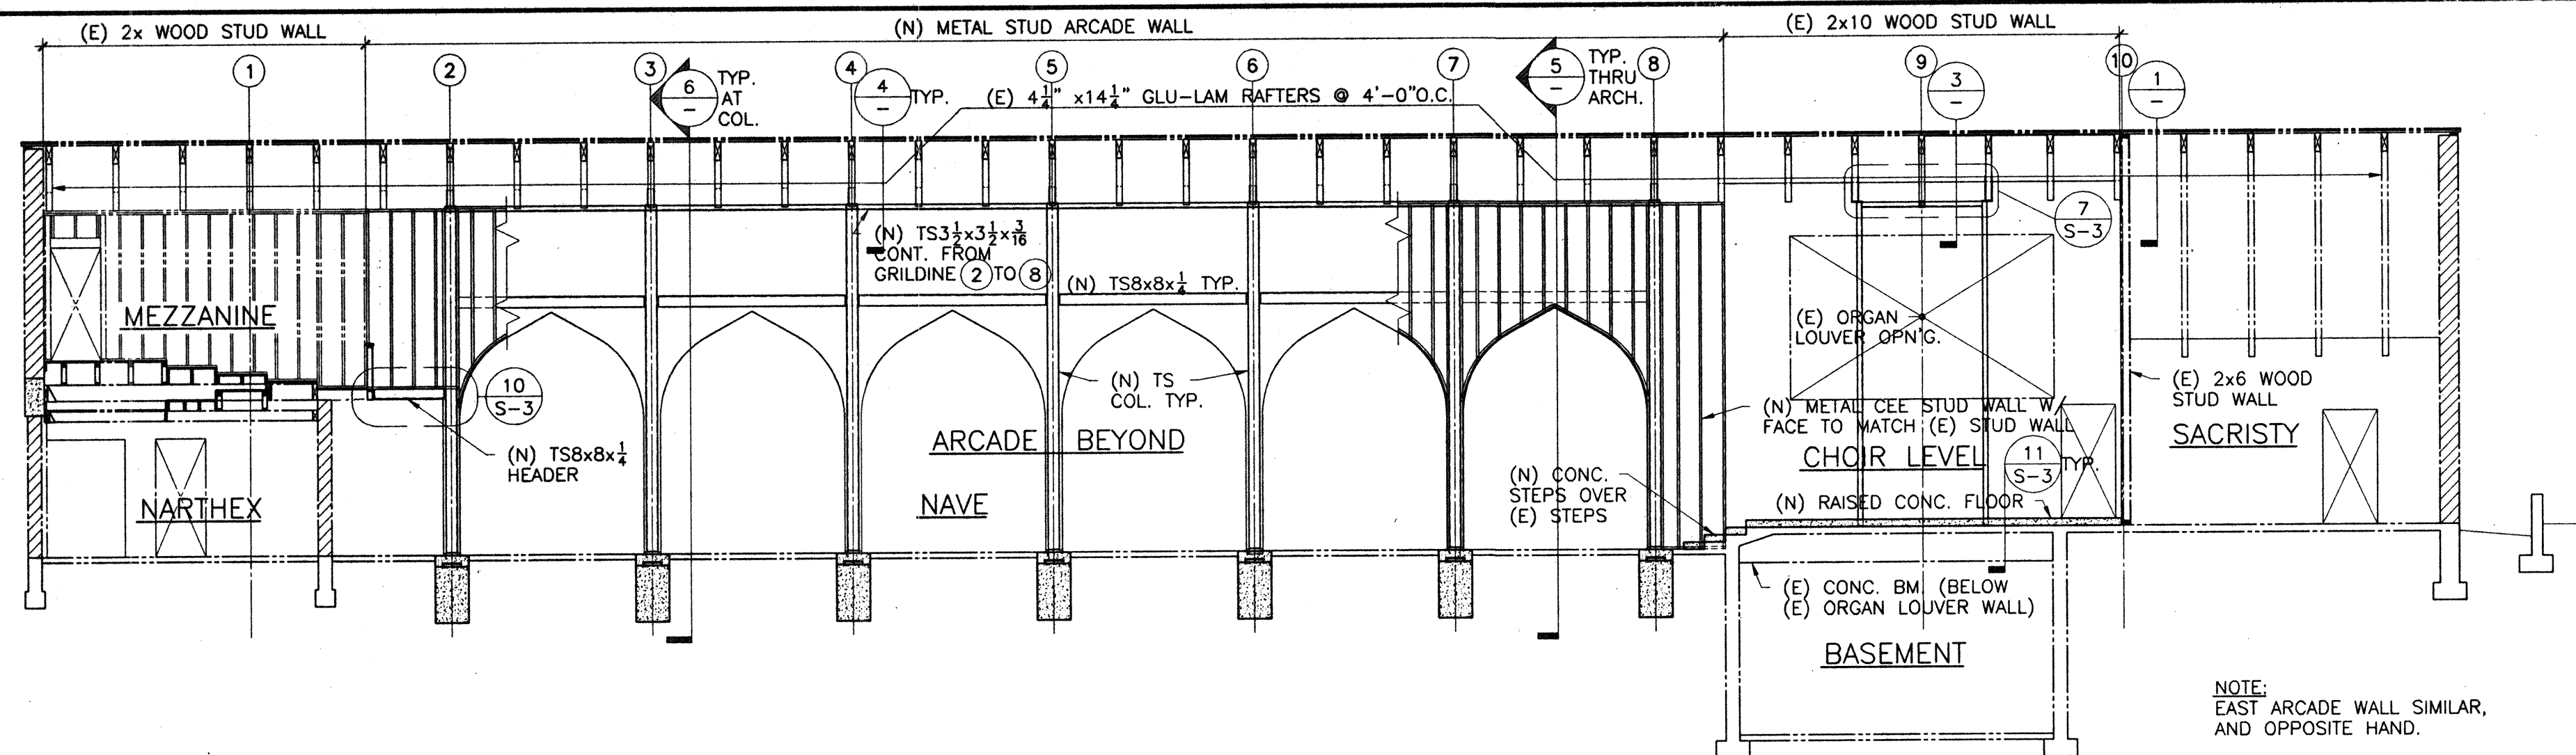


NEW INTERIOR WEST ARCADE WALL ELEVATION (LOOKING WEST)

1/8" 2

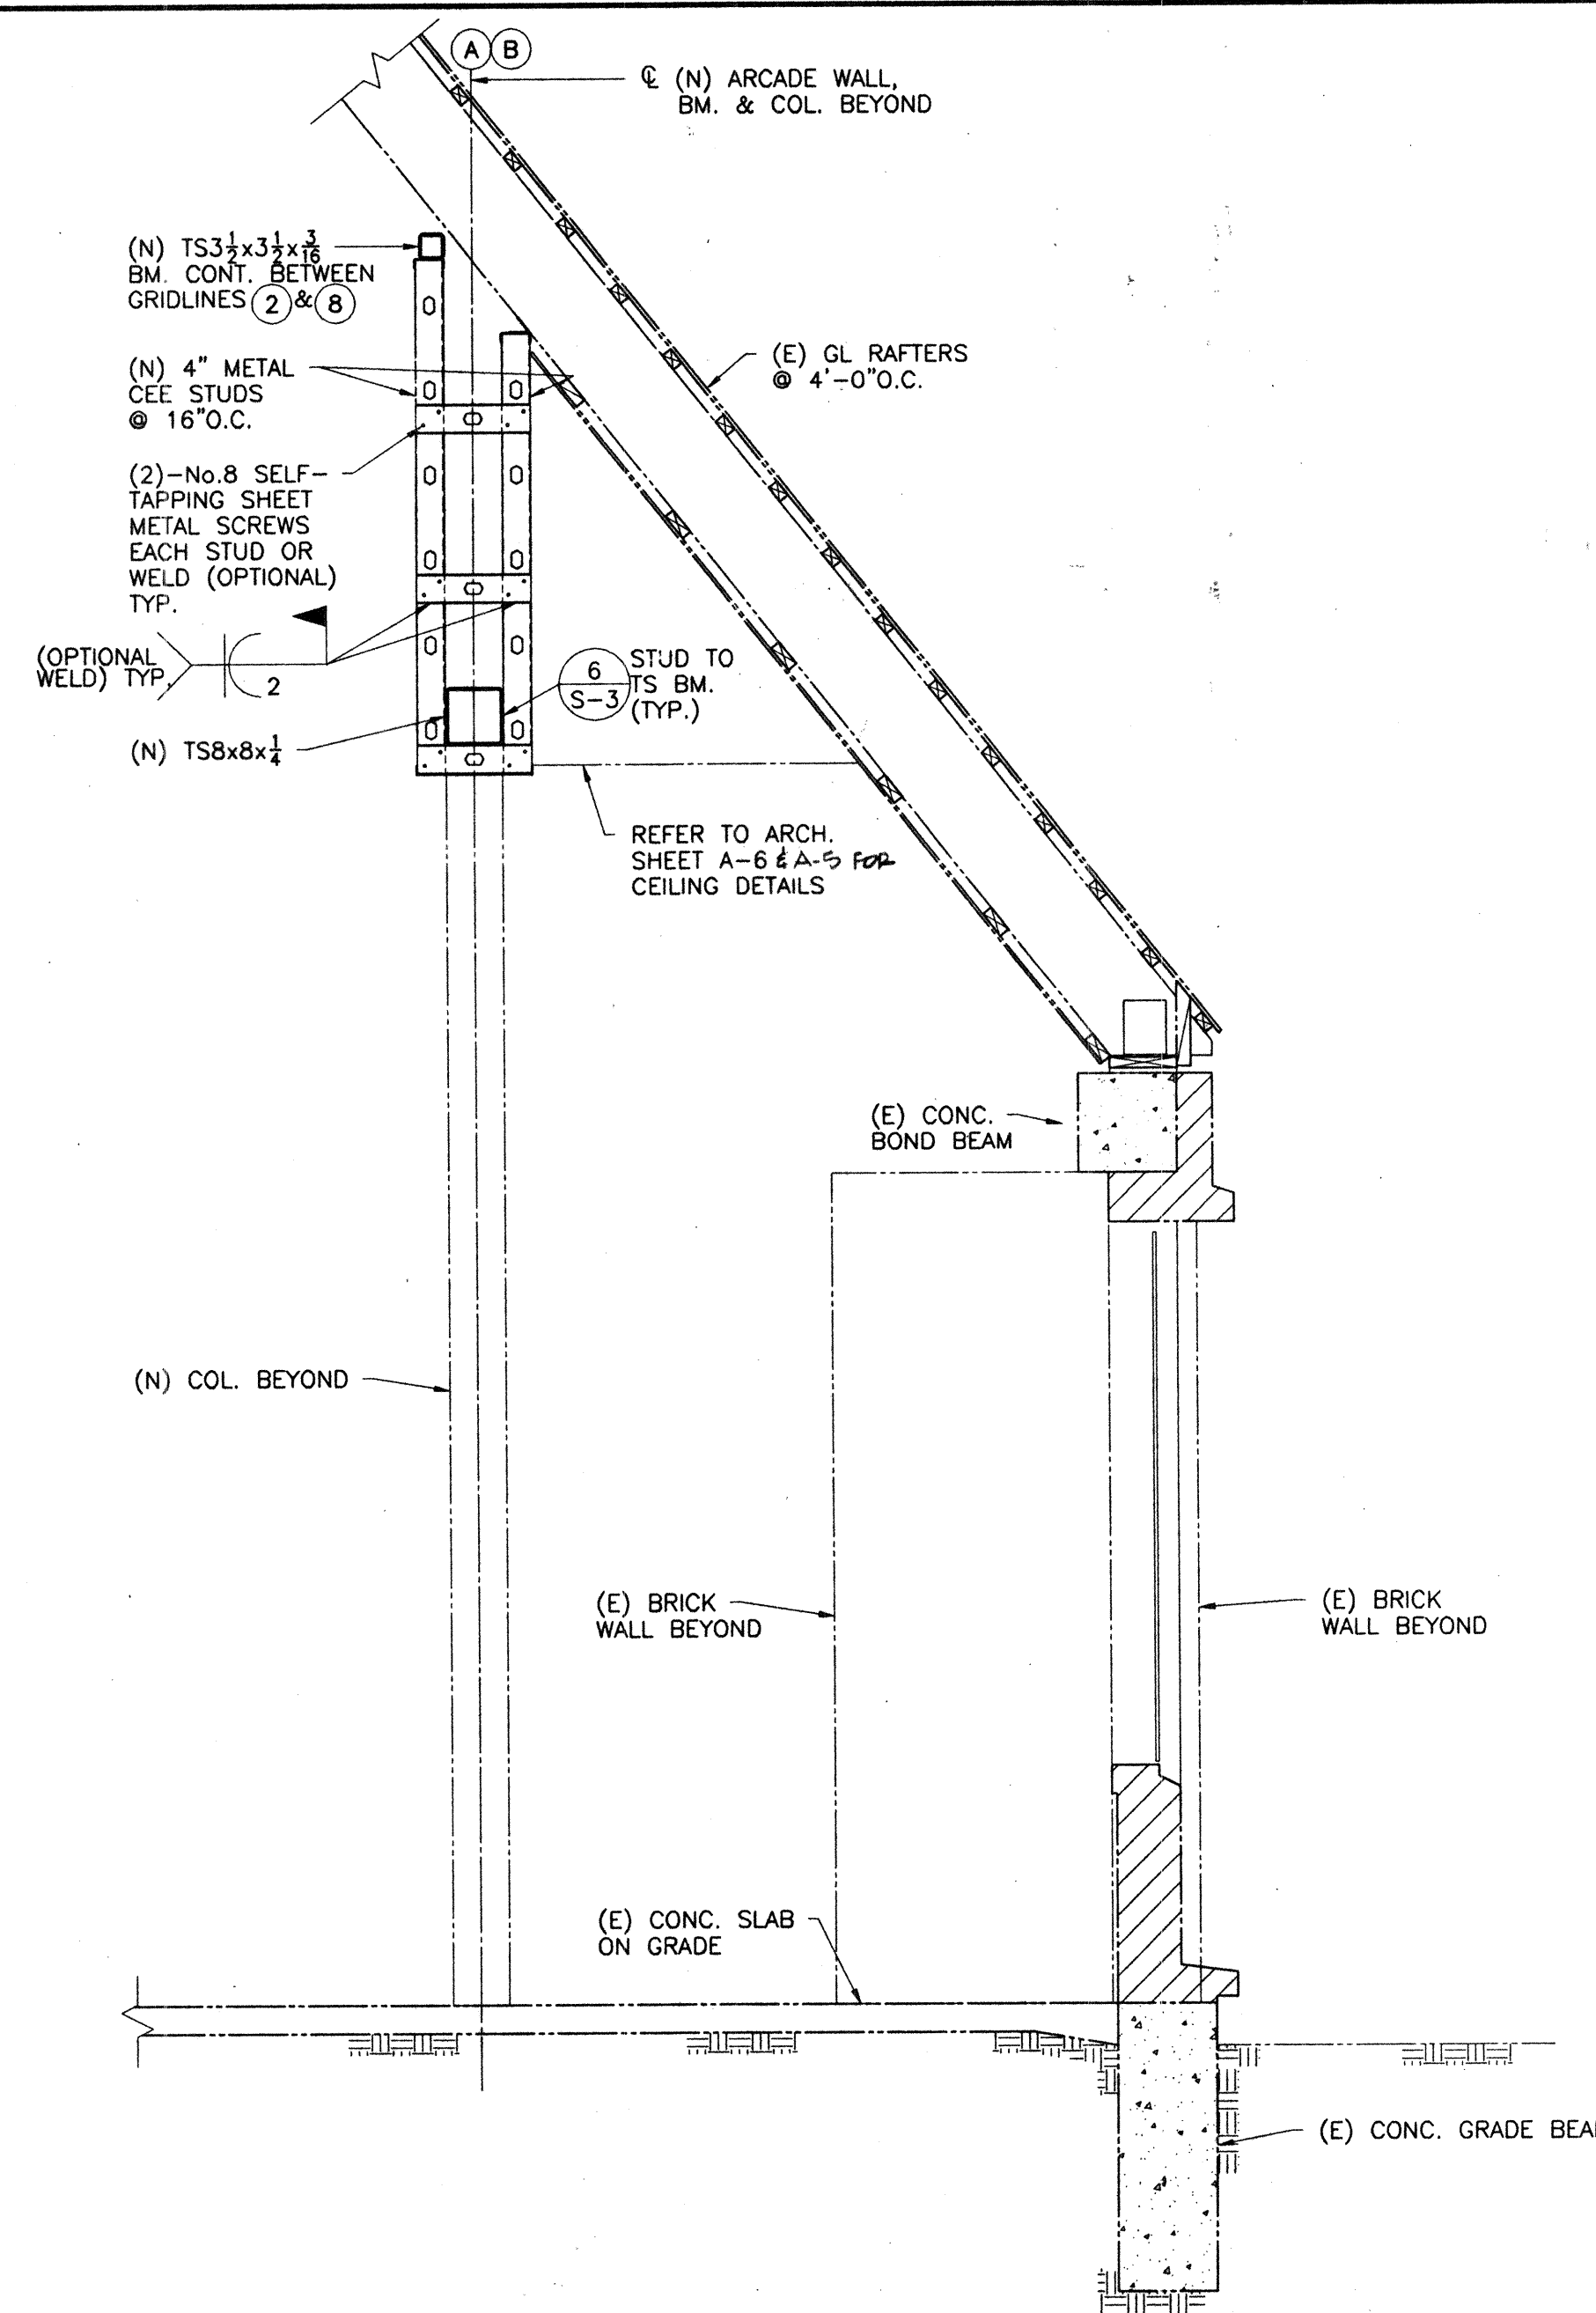

TYPICAL ARCADE WALL SECTION AT ARCH

1/2" 5

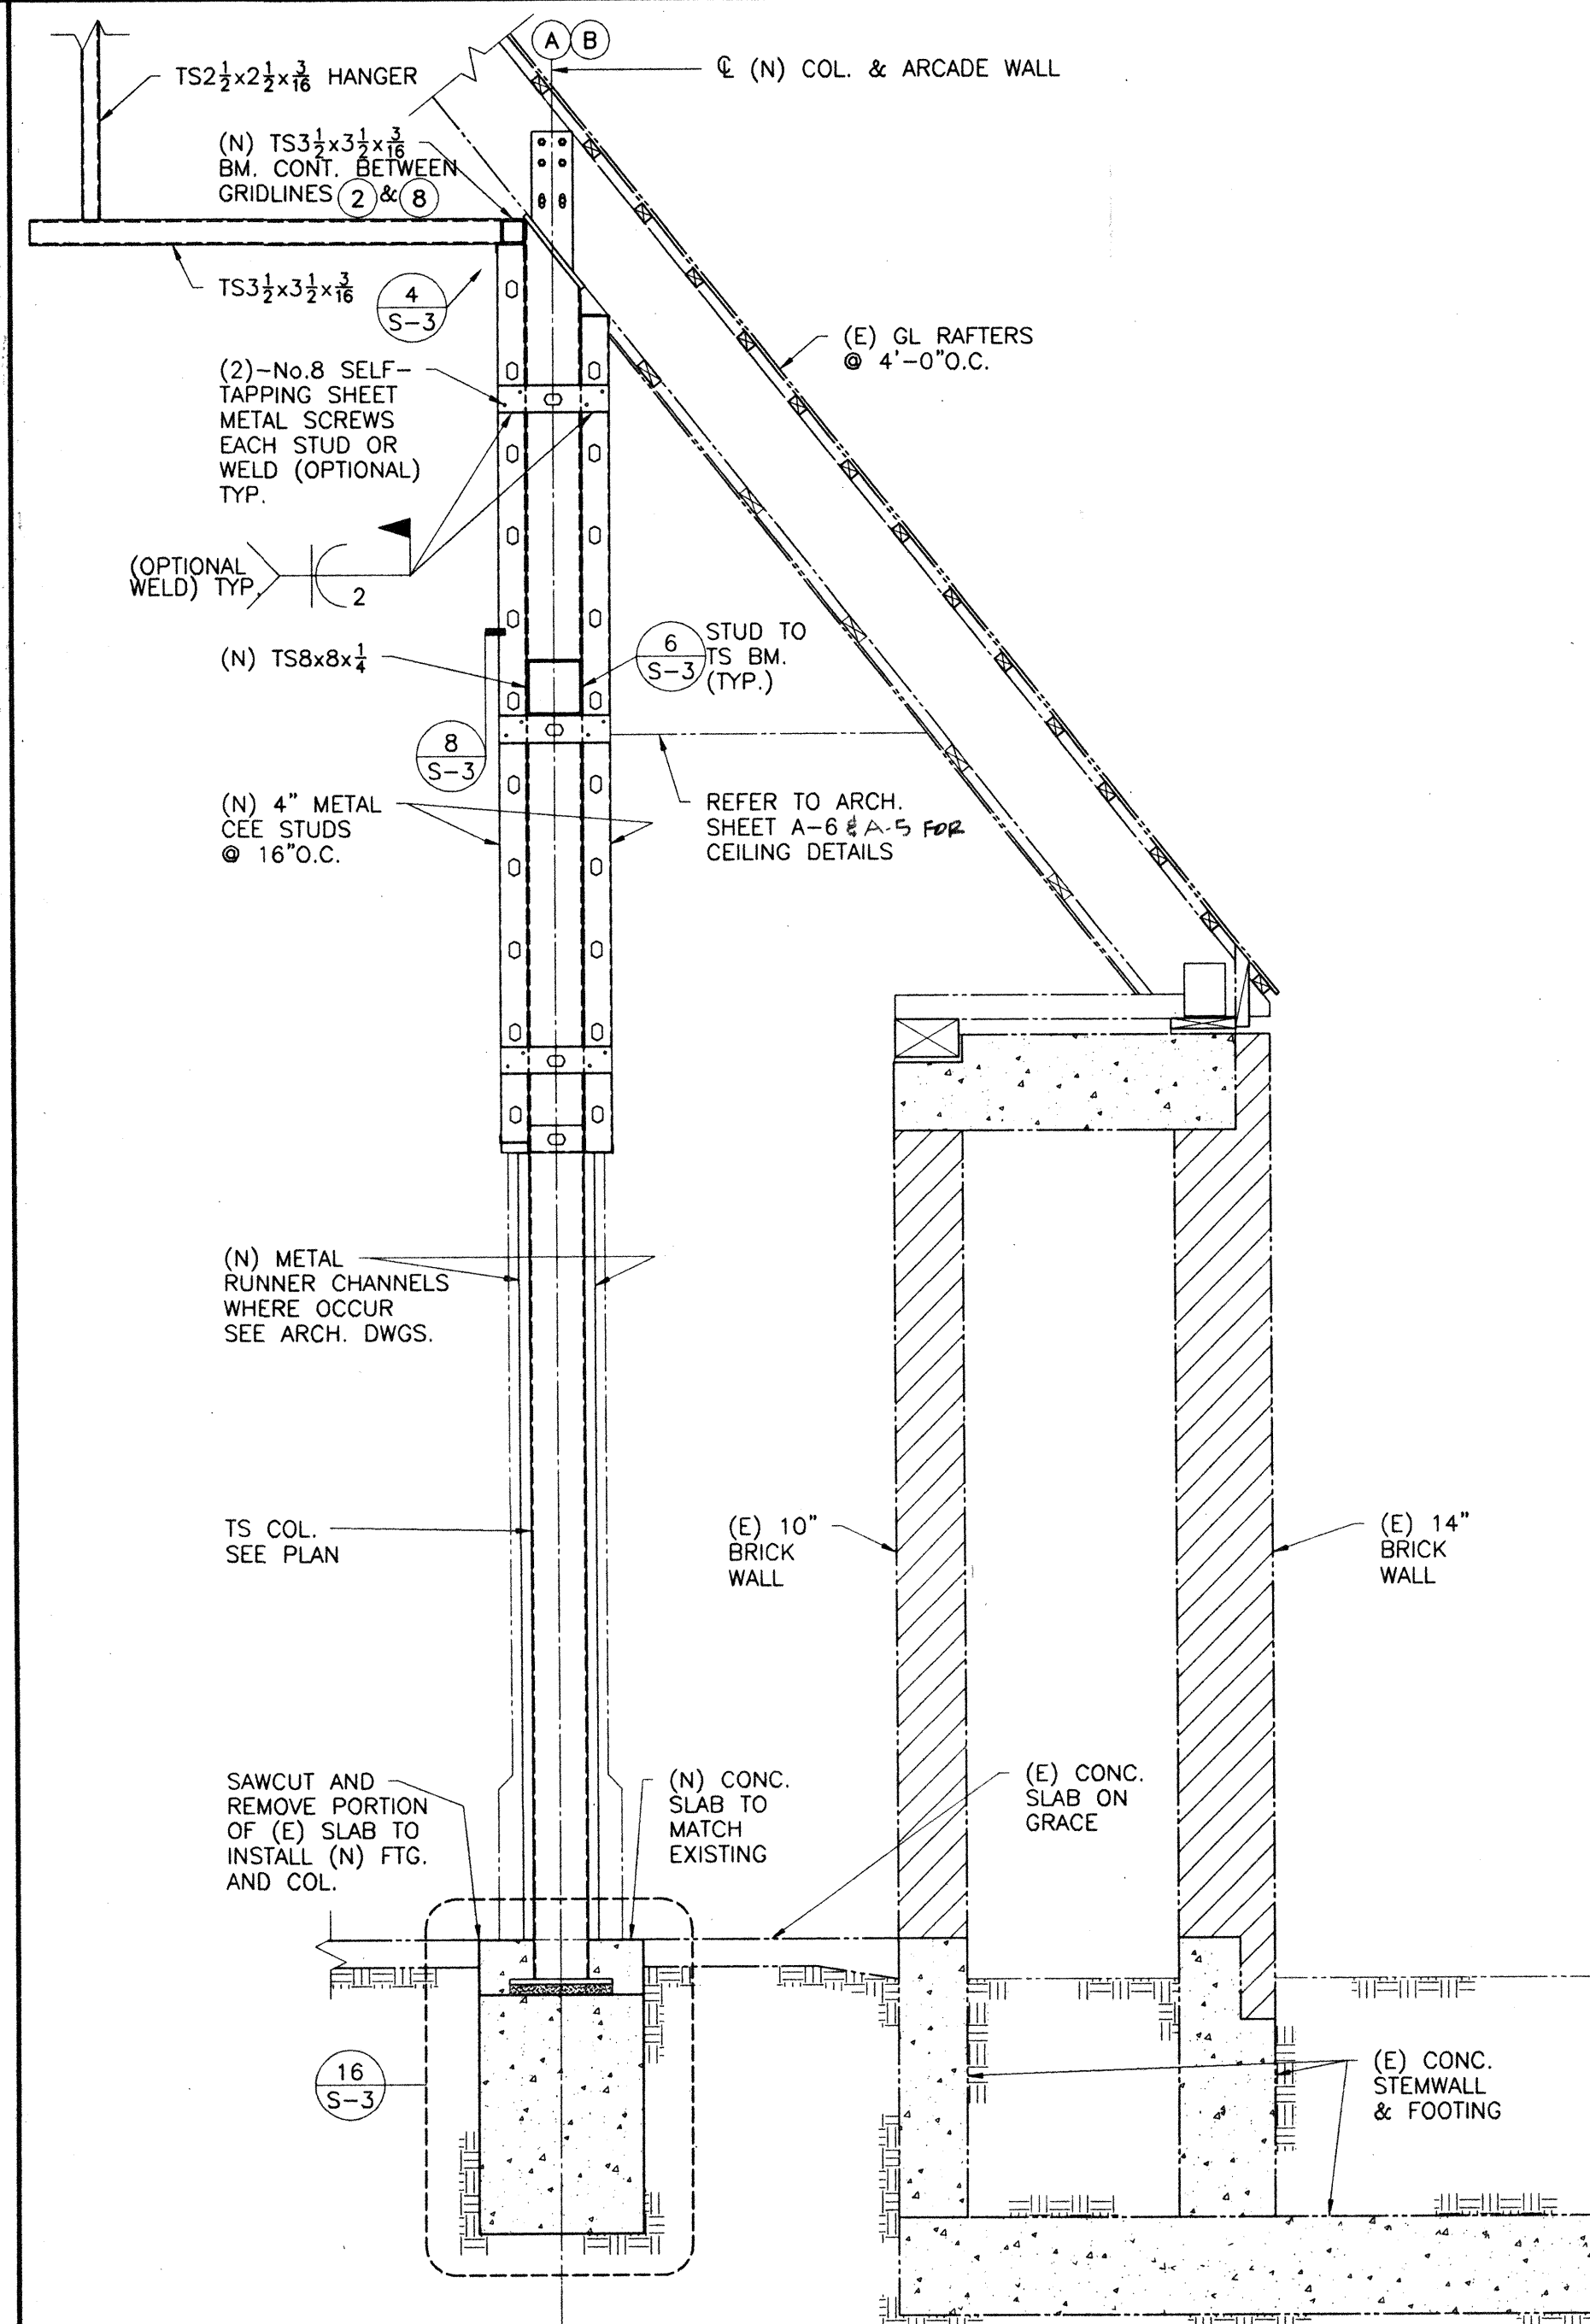

TYPICAL ARCADE WALL SECTION AT COLUMN

1/2" 6

| ISSUE RECORD |             |
|--------------|-------------|
| 4-19-00      | 35%         |
| 9-11-00      | 90%         |
| 11-16-00     | 100%        |
| 12/18/00     | QC RESPONSE |

**Onuma & Associates**  
Architecture, Planning, Consulting  
511 Mission Street  
South Pasadena, CA 91030  
tel 626.799.9920  
fax 626.799.8260  
e-mail: info@onuma.com

Consultants

**KANDA TSO**

KANDA AND TSO ASSOCIATES  
CONSULTING STRUCTURAL ENGINEERS  
511 MISSION STREET  
SOUTH PASADENA, CA 91030-3035  
TEL (626) 441-1211  
FAX (626) 441-1011



RENOVATION PROJECT  
FOR  
SAINT EDMUND'S  
EPISCOPAL CHURCH

1175 SAN GABRIEL BLVD., SAN MARINO, CA., 91108-8048

STAMPS

REVISIONS

| DESCRIPTION | DATE | BY |
|-------------|------|----|
|             |      |    |
|             |      |    |

PROJECT NUMBER  
**2000**

SCALE  
**AS NOTED**

PRINTED  
**12-18-00**

TITLE  
**NEW INTERIOR  
WALL ELEVATIONS  
& SECTIONS**

SHEET

**S-2**

24 OF 44