


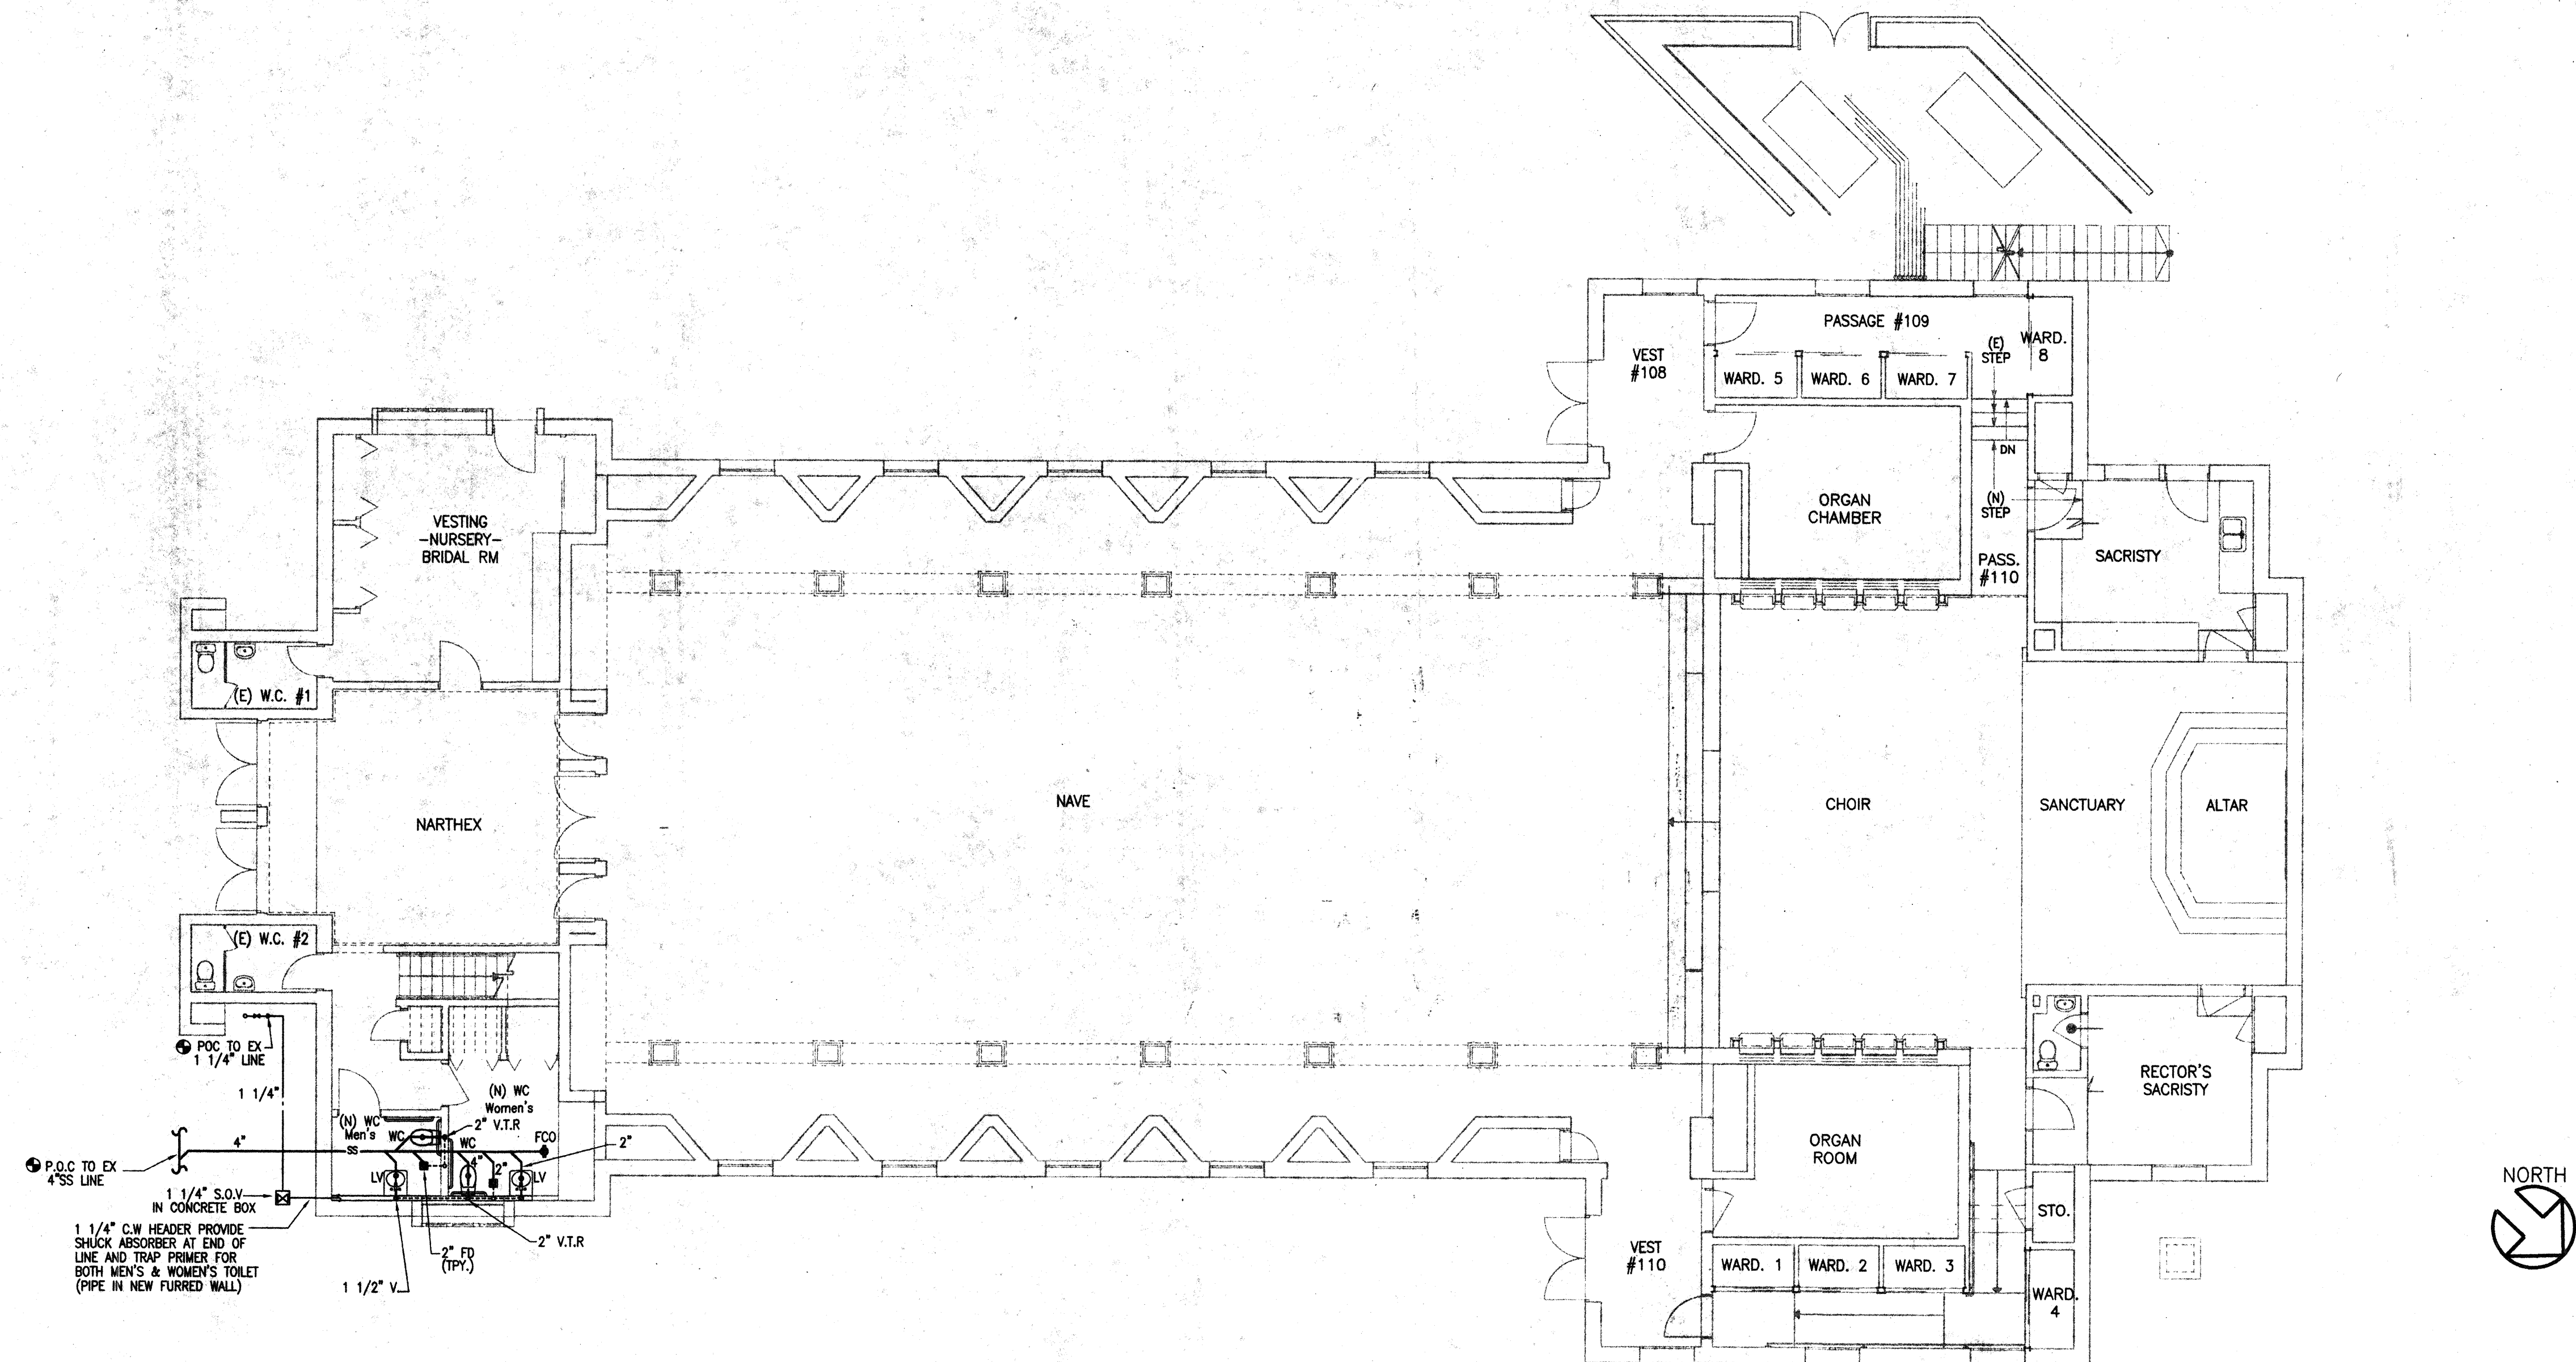

SCHEDULE OF LOCAL CONNECTION					
SYMBOL	FIXTURE	W.	V.	C.W.	REMARKS
WC	WATER CLOSET	4"	2"	3/4"	FLUSH VALVE
LV	LAVATORY	1 1/2"	1 1/4"	1/2"	
FD	FLOOR DRAIN	2"	2"	-	

FIRST FLOOR PLUMBING PLAN

SCALE: 1/8"=1'-0"


Onuma & Associates
Architecture, Planning, Consulting
 511 Mission Street
 South Pasadena, CA 91030
 tel 626.799.9920
 fax 626.799.8260
 e-mail: info@onuma.com

Consultants

DEBIL & ROSHANIAN INC.
 MECHANICAL & ELECTRICAL ENGINEERS
 10411 Laurel Canyon Blvd., Suite 202
 Van Nuys, CA 91411
 TEL: (818) 980-0837
 FAX: (818) 980-1251

REMODEL
 FOR
**SAINT EDMUND'S
 EPISCOPAL CHURCH**
 1175 SAN GABRIEL BLVD., SAN MARINO, CA., 91108-8048

STAMPS

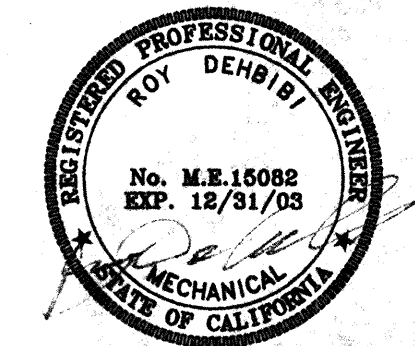

REVISIONS

DESCRIPTION	DATE	BY

PROJECT NUMBER
 2000

SCALE AS NOTED

PRINTED 11/12/00

TITLE
**FIRST FLOOR
 PLUMBING PLAN**
 SHEET

P-1
 36 OF 44