

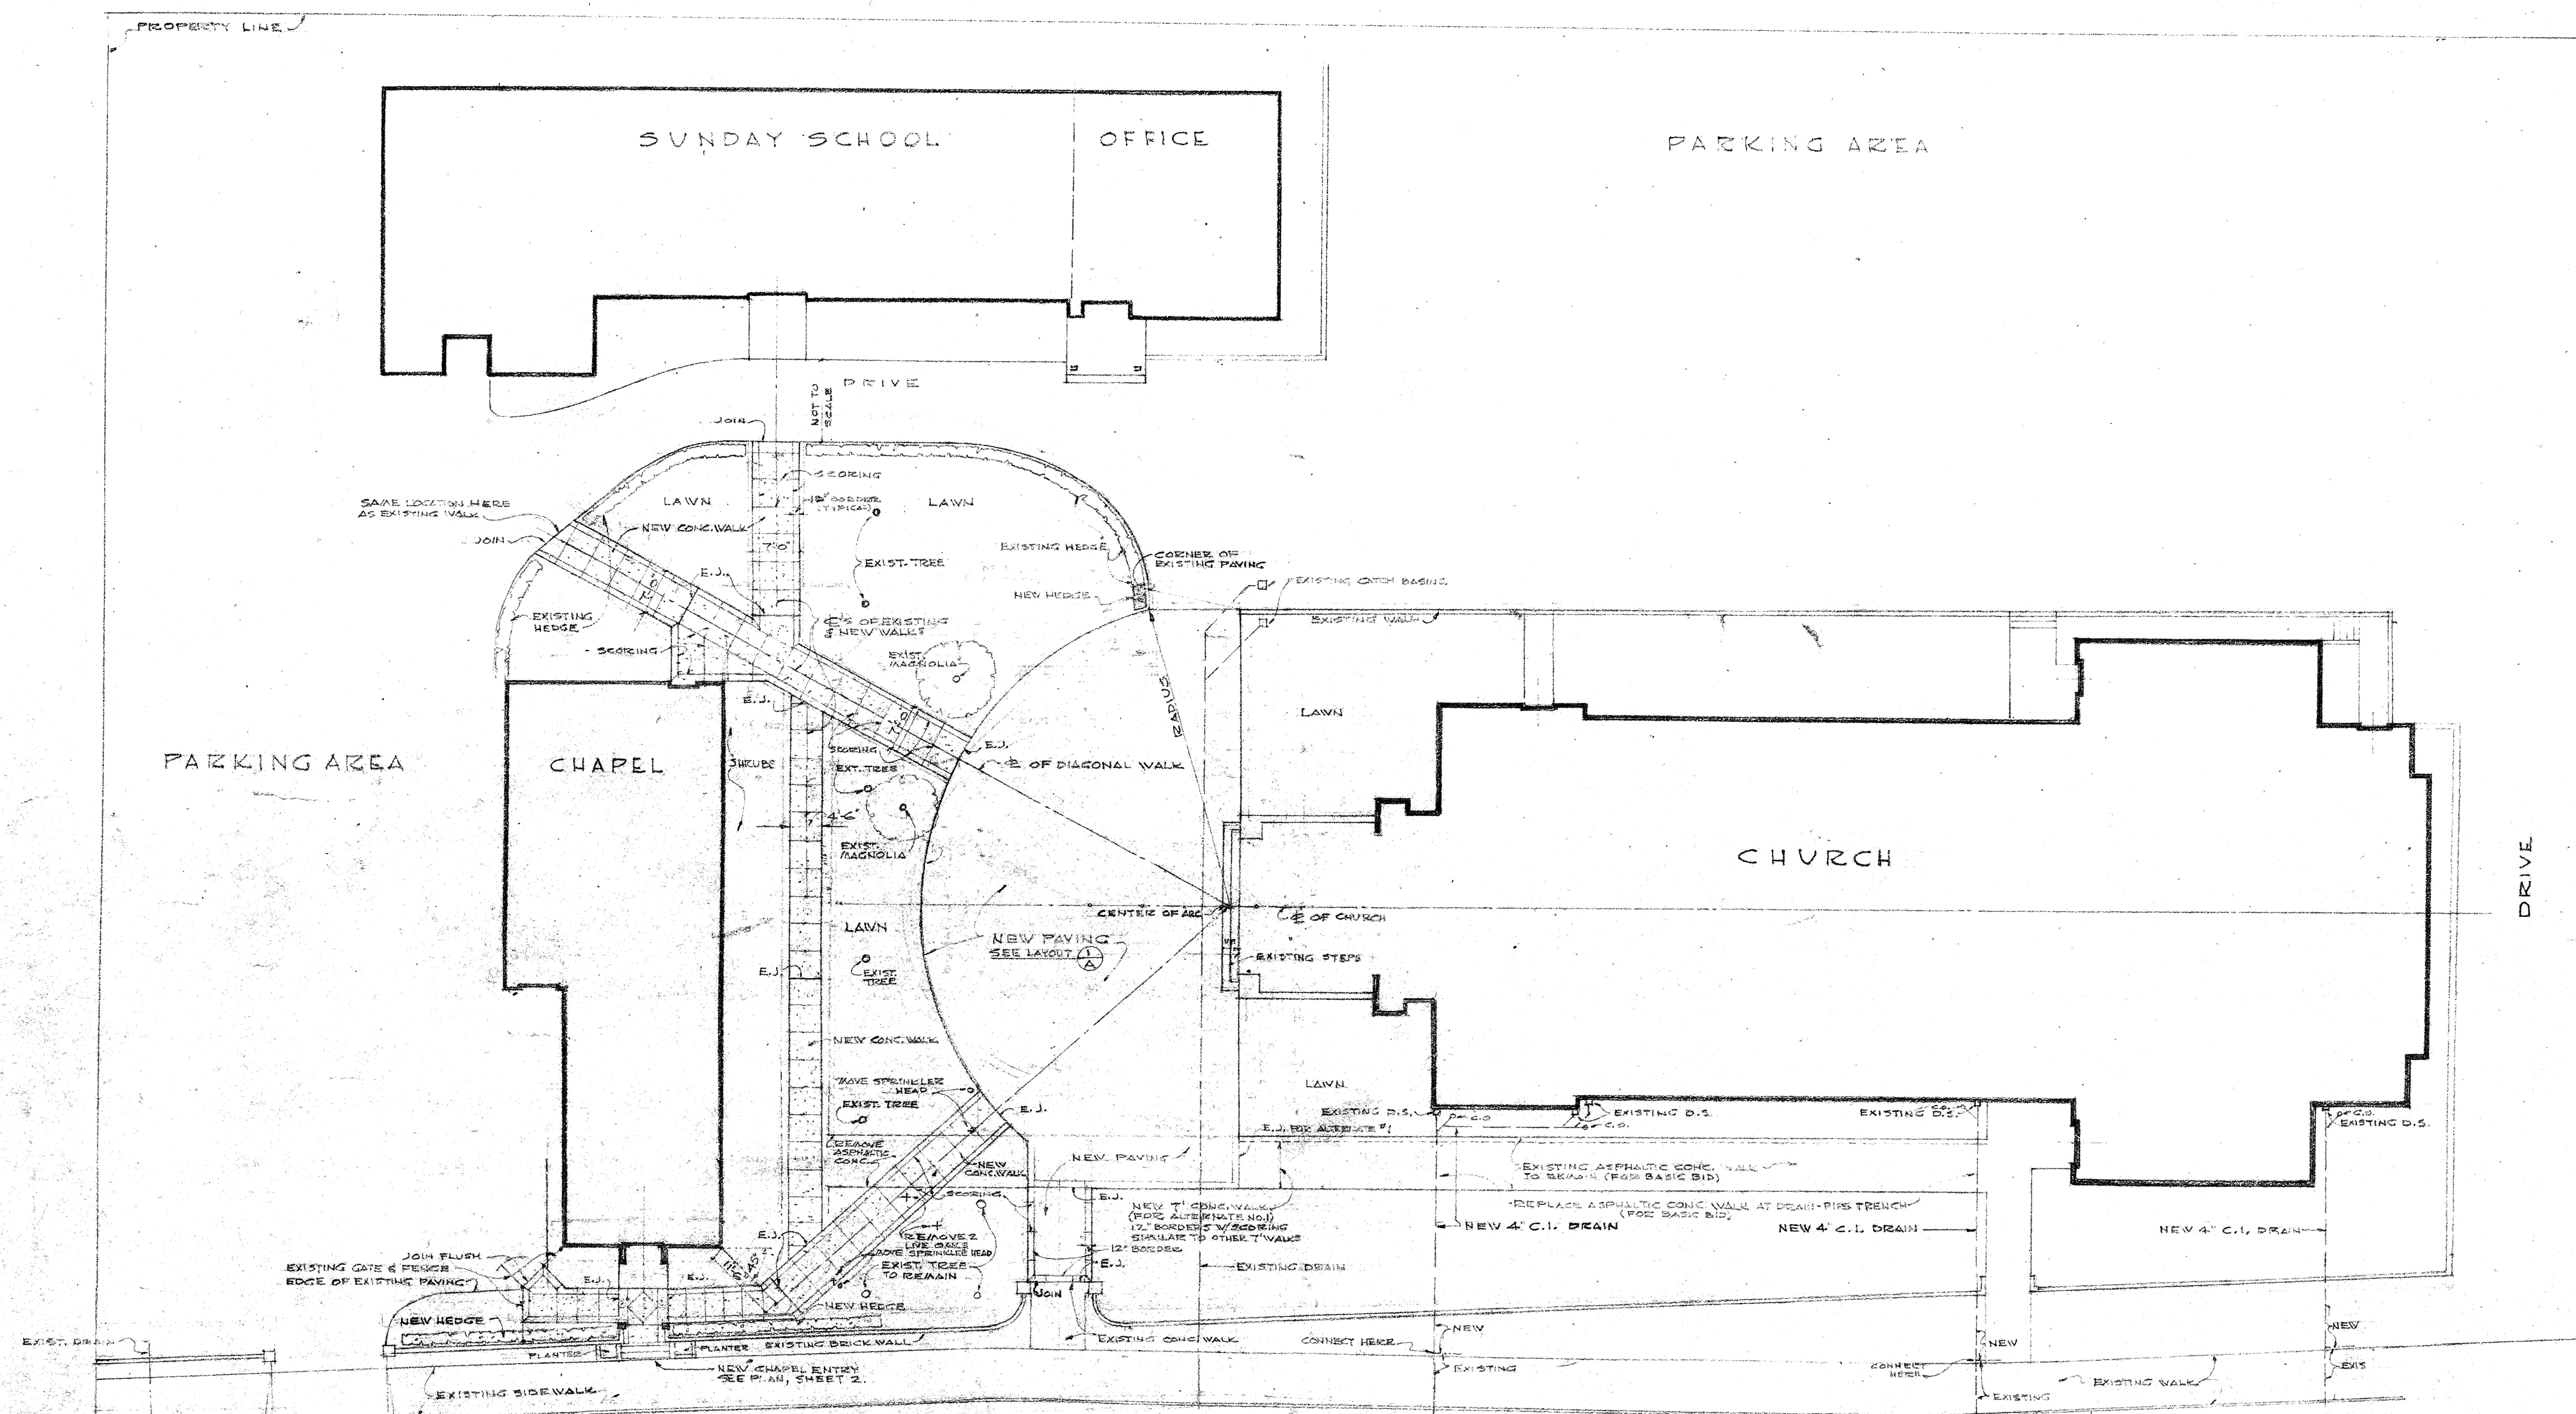
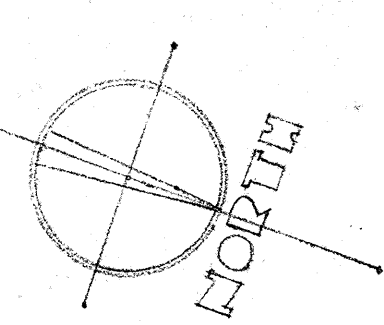
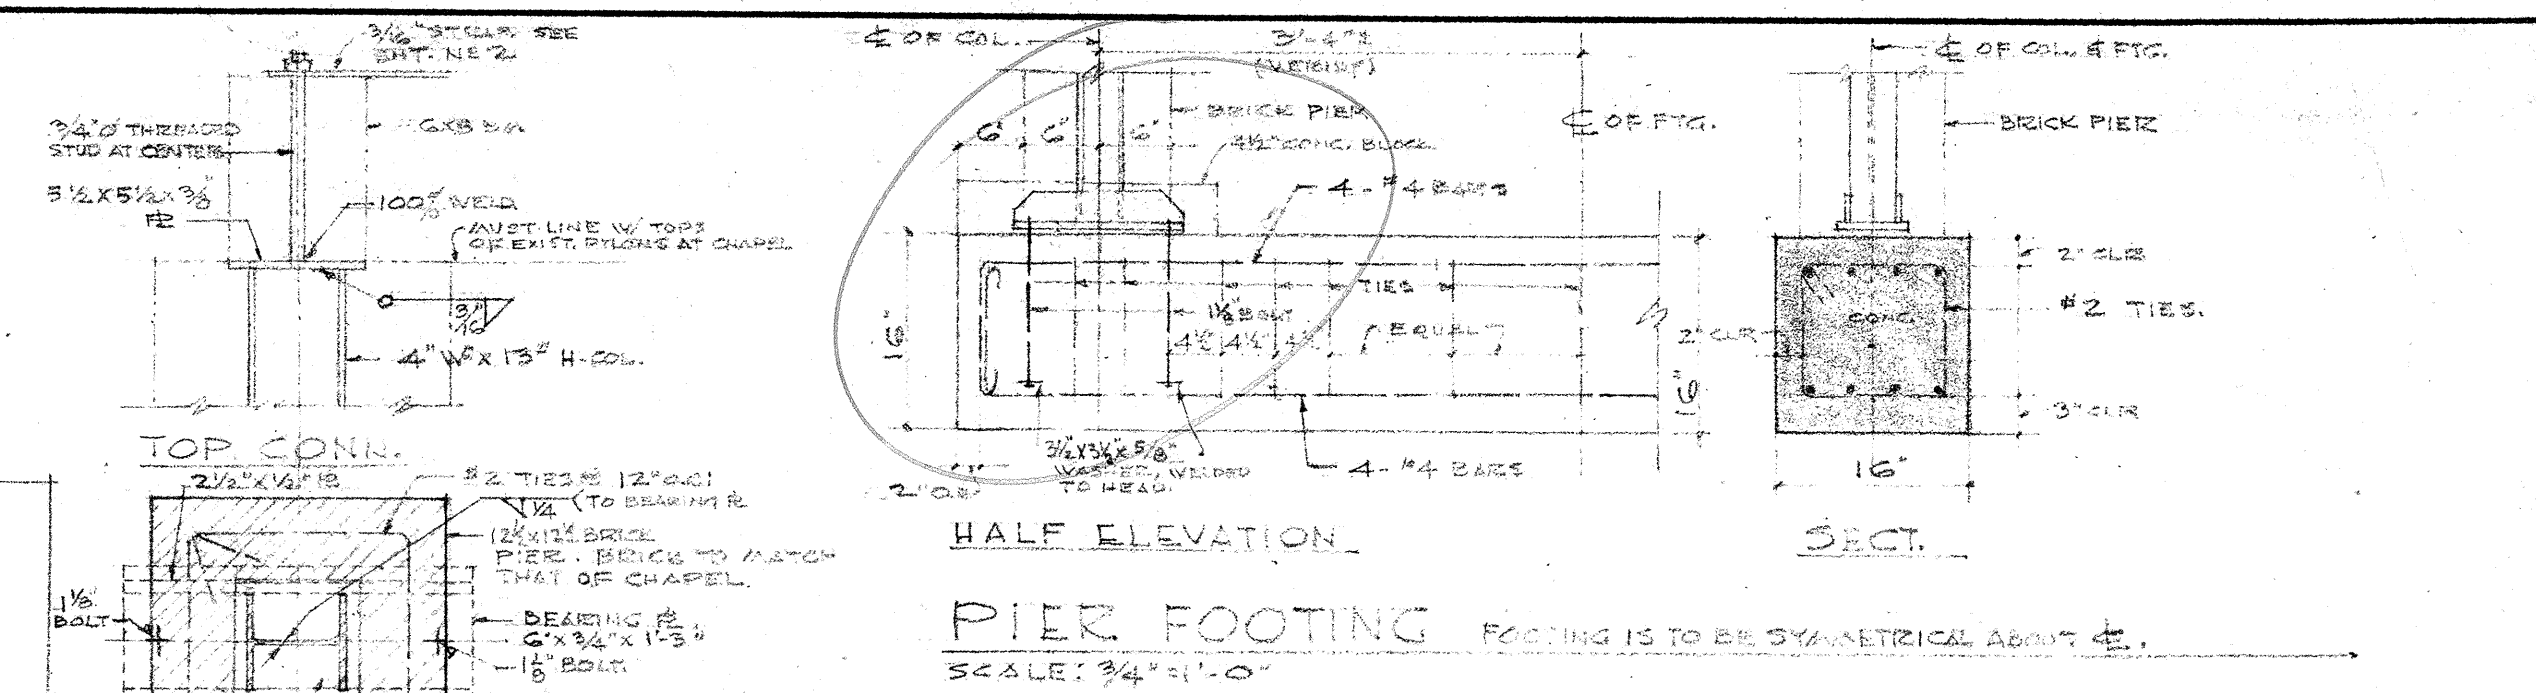
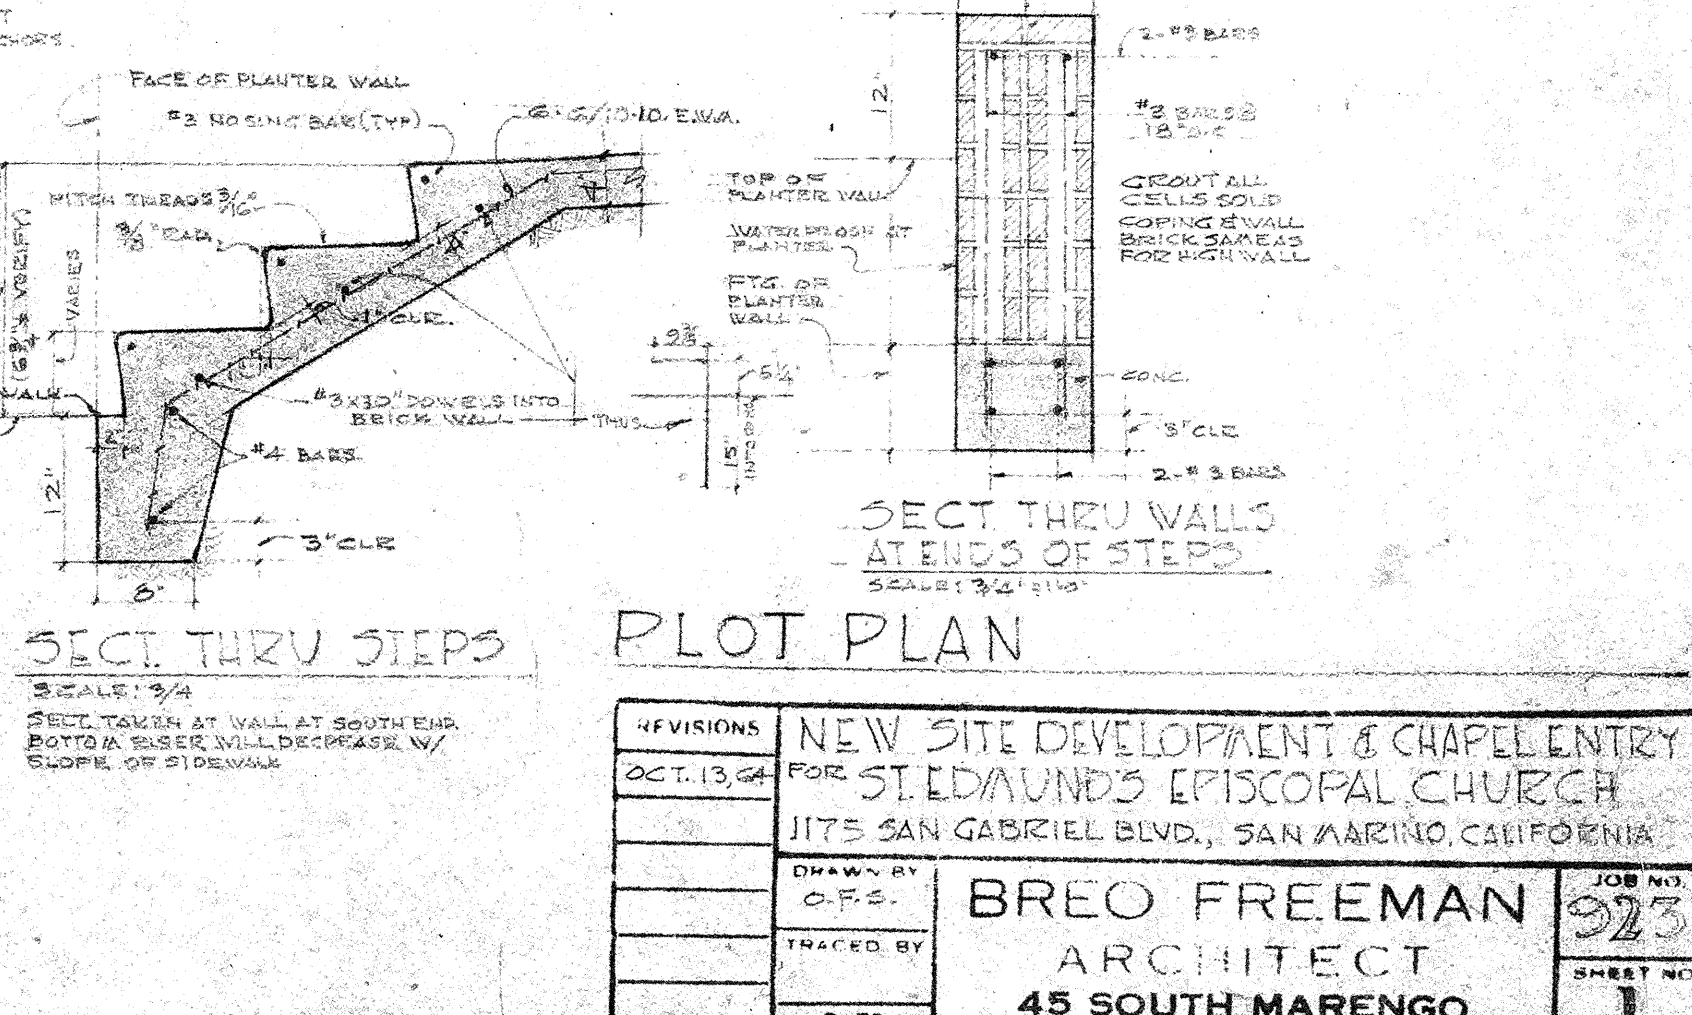
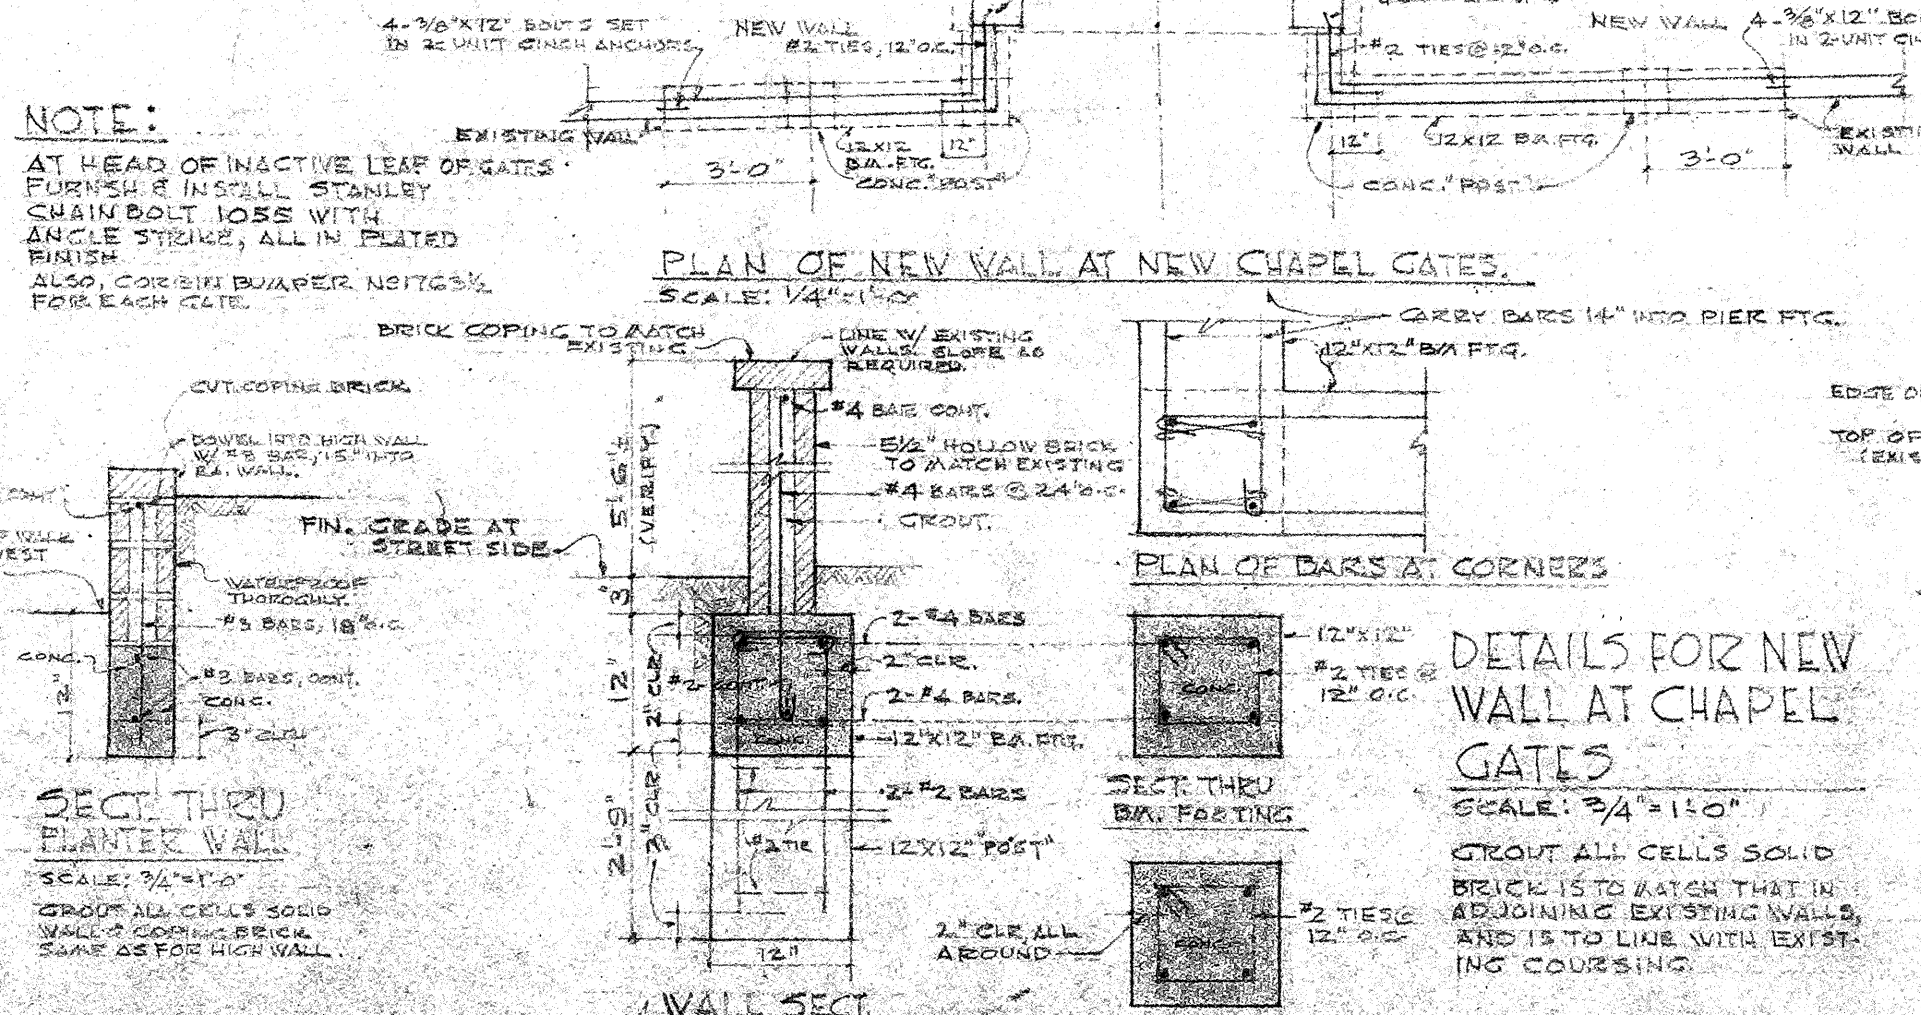


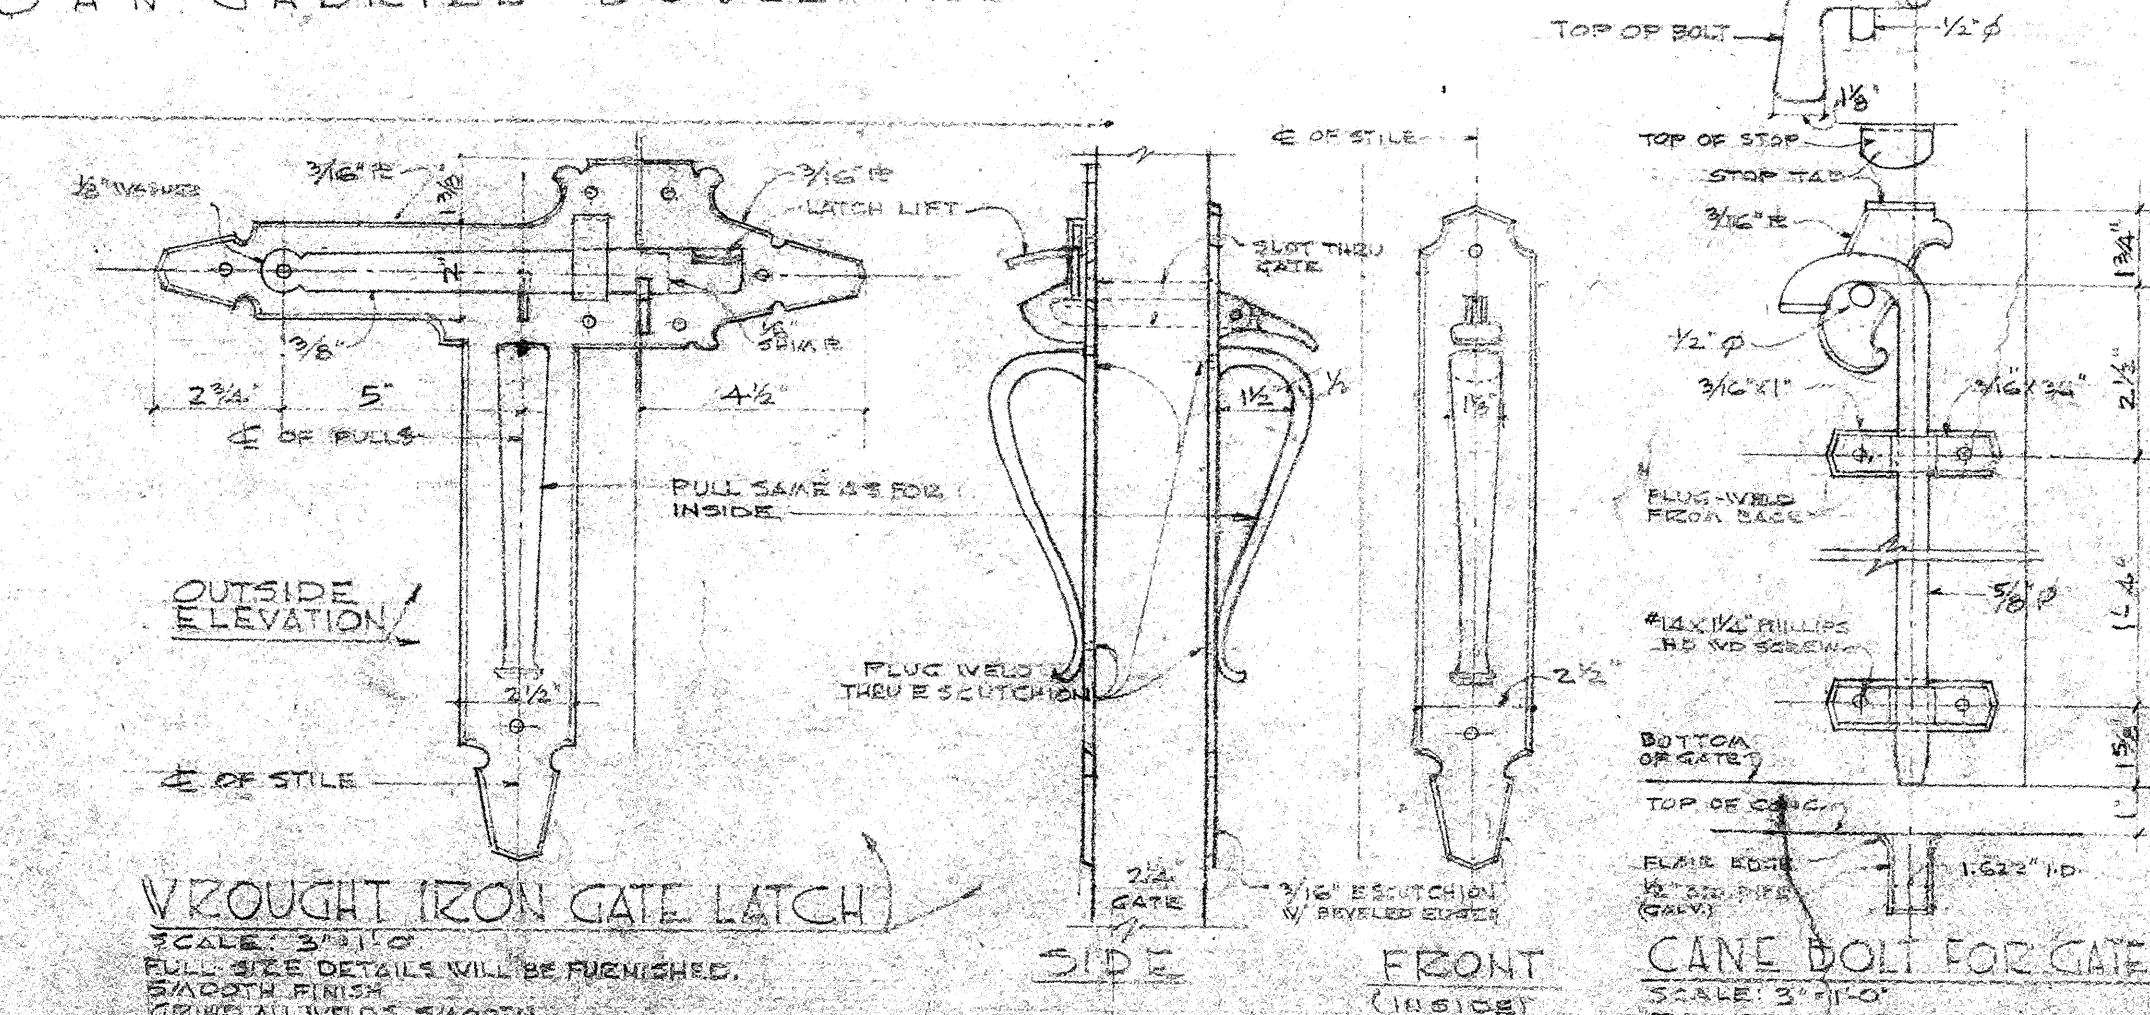

NOTE: "E.J." SIGNIFIES "EXPANSION JOINT"
"C.O." SIGNIFIES "CLEAN-OUT"
"C.I." SIGNIFIES "CAST IRON"

SAN GABRIEL BOULEVARD

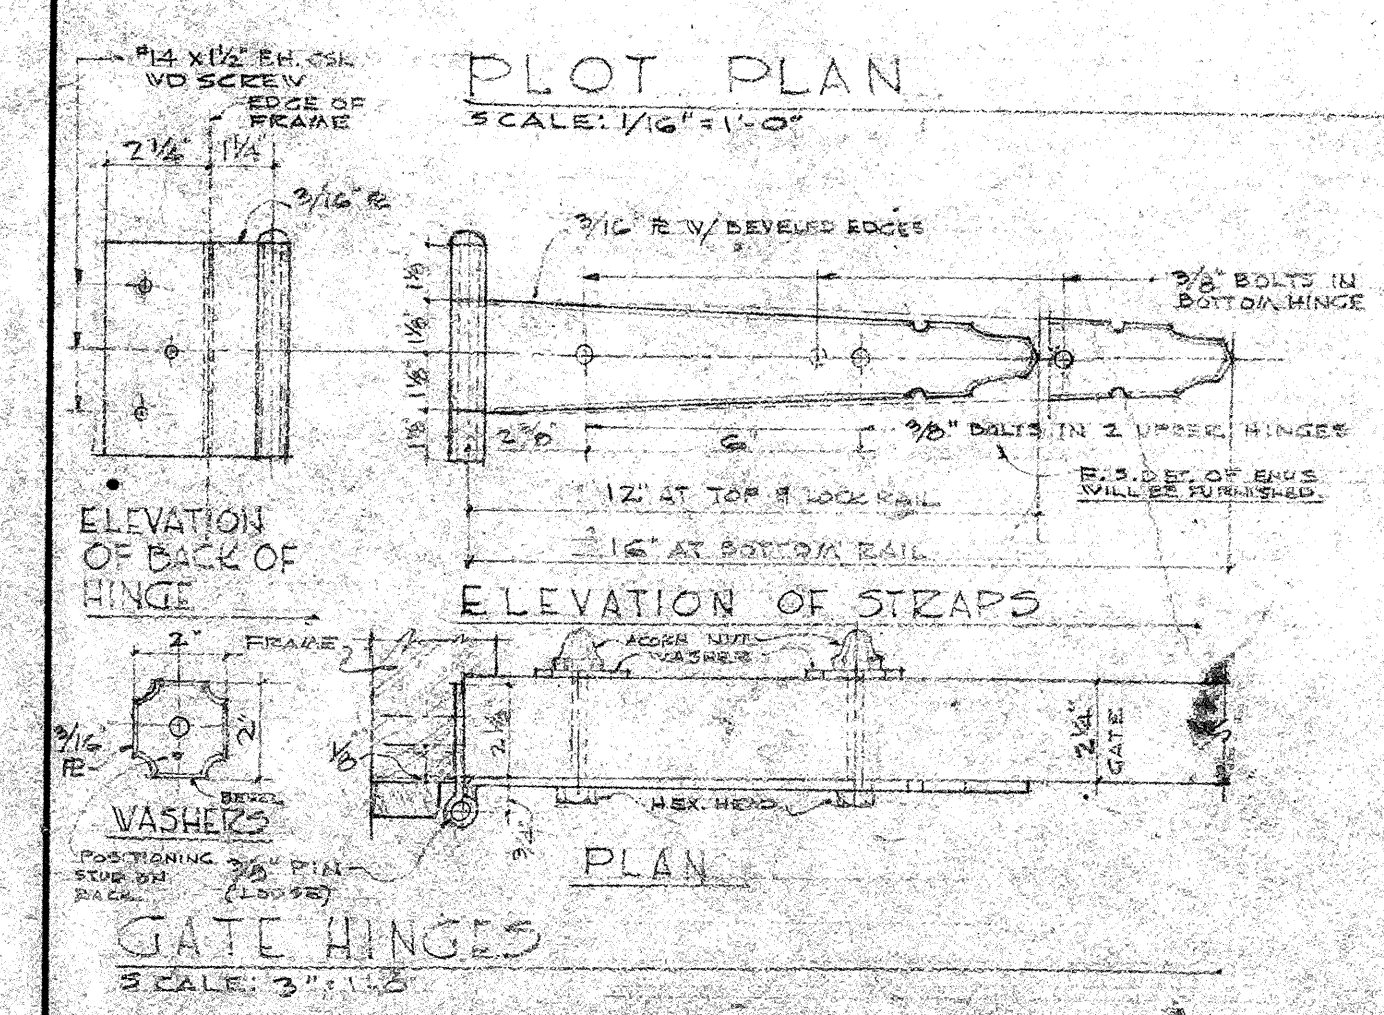

GENERAL NOTES

FOOTINGS:
ALL FOOTINGS ARE TO REST UPON FIRM, NATURAL, UNDISTURBED SOIL.

CONCRETE:
CEMENT SHALL BE TESTED PORTLAND CEMENT.
CONCRETE MIX SHALL BE DESIGNED FOR A MINIMUM COMPRESSIVE STRENGTH OF 2,500 P.S.I. AT 28 DAYS. USE NO MORE THAN 7 GALLONS OF WATER PER 1.0 CUBIC YARD OF CONCRETE. THIS APPLIES TO FOOTINGS FOR WALLS AND PIERS.
CONCRETE MIX FOR WALLS AND PIERS SHALL BE 1 PART CEMENT, 3 PARTS WASHED SAND, AND 4 PARTS BRICK CRUSH.

CROUT:
CROUT FOR MASONRY SHALL BE COMPOSED BY VOLUME, OF ONE PART CEMENT TO 3 PARTS SAND, TO WHICH MAY BE ADDED NOT MORE THAN ONE TENTH PART OF LIME. ADD WATER TO PRODUCE CONCRETE FOR CROUTING WITHOUT STIFFENING OF CONSTITUENTS OF CROUT.

STEEL:
STEEL UNDER STEEL BRACKET PLATES SHALL BE OF A STIFF CONSISTENCY.

REINFORCEMENT:
REINFORCEMENT SHALL BE DEFORMED BARS OF INTERMEDIATE GRADE STEEL, CONFORMING TO U.S.C. STANDARD NO. 20-6-C-1. USE NO BRACES.

ANCHORS:
3.00 INCH ANCHORS SHALL EXTEND 6" INTO WALL.
3.00 INCH ANCHORS SHALL EXTEND 4" INTO WALL.
ALL ANCHORS SHALL BE PROPERLY CROUTED IN PLACE.

STEEL:
STRUCTURAL STEEL SHALL CONFORM TO U.S.C. STANDARD 27-1-G-1. STEEL NOT SHOWN IN CROUT OR CONCRETE SHALL BE COVERED WITH SHOP COAT AND ONE FIELD COAT OF EPOXY INHIBITIVE PAINT. USE WASHERS UNDER ALL NUTS. THOSE BEARING ON STEEL SHALL BE LOCAL WASHERS. SEE DETAIL FOR WASHERS BEARING ON WOOD.

WOOD:
SEE DETAILS FOR SPECIES AND GRADES.

WALKS:
4" SLAB WITH 6-6/10-10 E.W.A. REINFORCING.

PLANS FILED 7-14-65 BY H. Rich
DATE
BUILDING PERMIT
ISSUED 7-15-65 BY H. Rich
DATE

APPROVED PLAN
7-15-65 BY R.W.M.
DATE
SAN MARINO BUILDING DEPT.

SUBMIT ELECTRICAL LOAD SCHEDULE

JOB PLAN
MUST BE KEPT ON JOB UNTIL OCCUPANCY

REVISIONS	NEW SITE DEVELOPMENT & CHAPEL ENTRY FOR ST. EDWARD'S EPISCOPAL CHURCH 1175 SAN GABRIEL BLVD., SAN MARINO CALIFORNIA
DRAWN BY	BREO FREEMAN
CHECKED BY	ARCHITECT
DATE	45 SOUTH MARENGO PASADENA 1, CALIFORNIA
DATE	1