



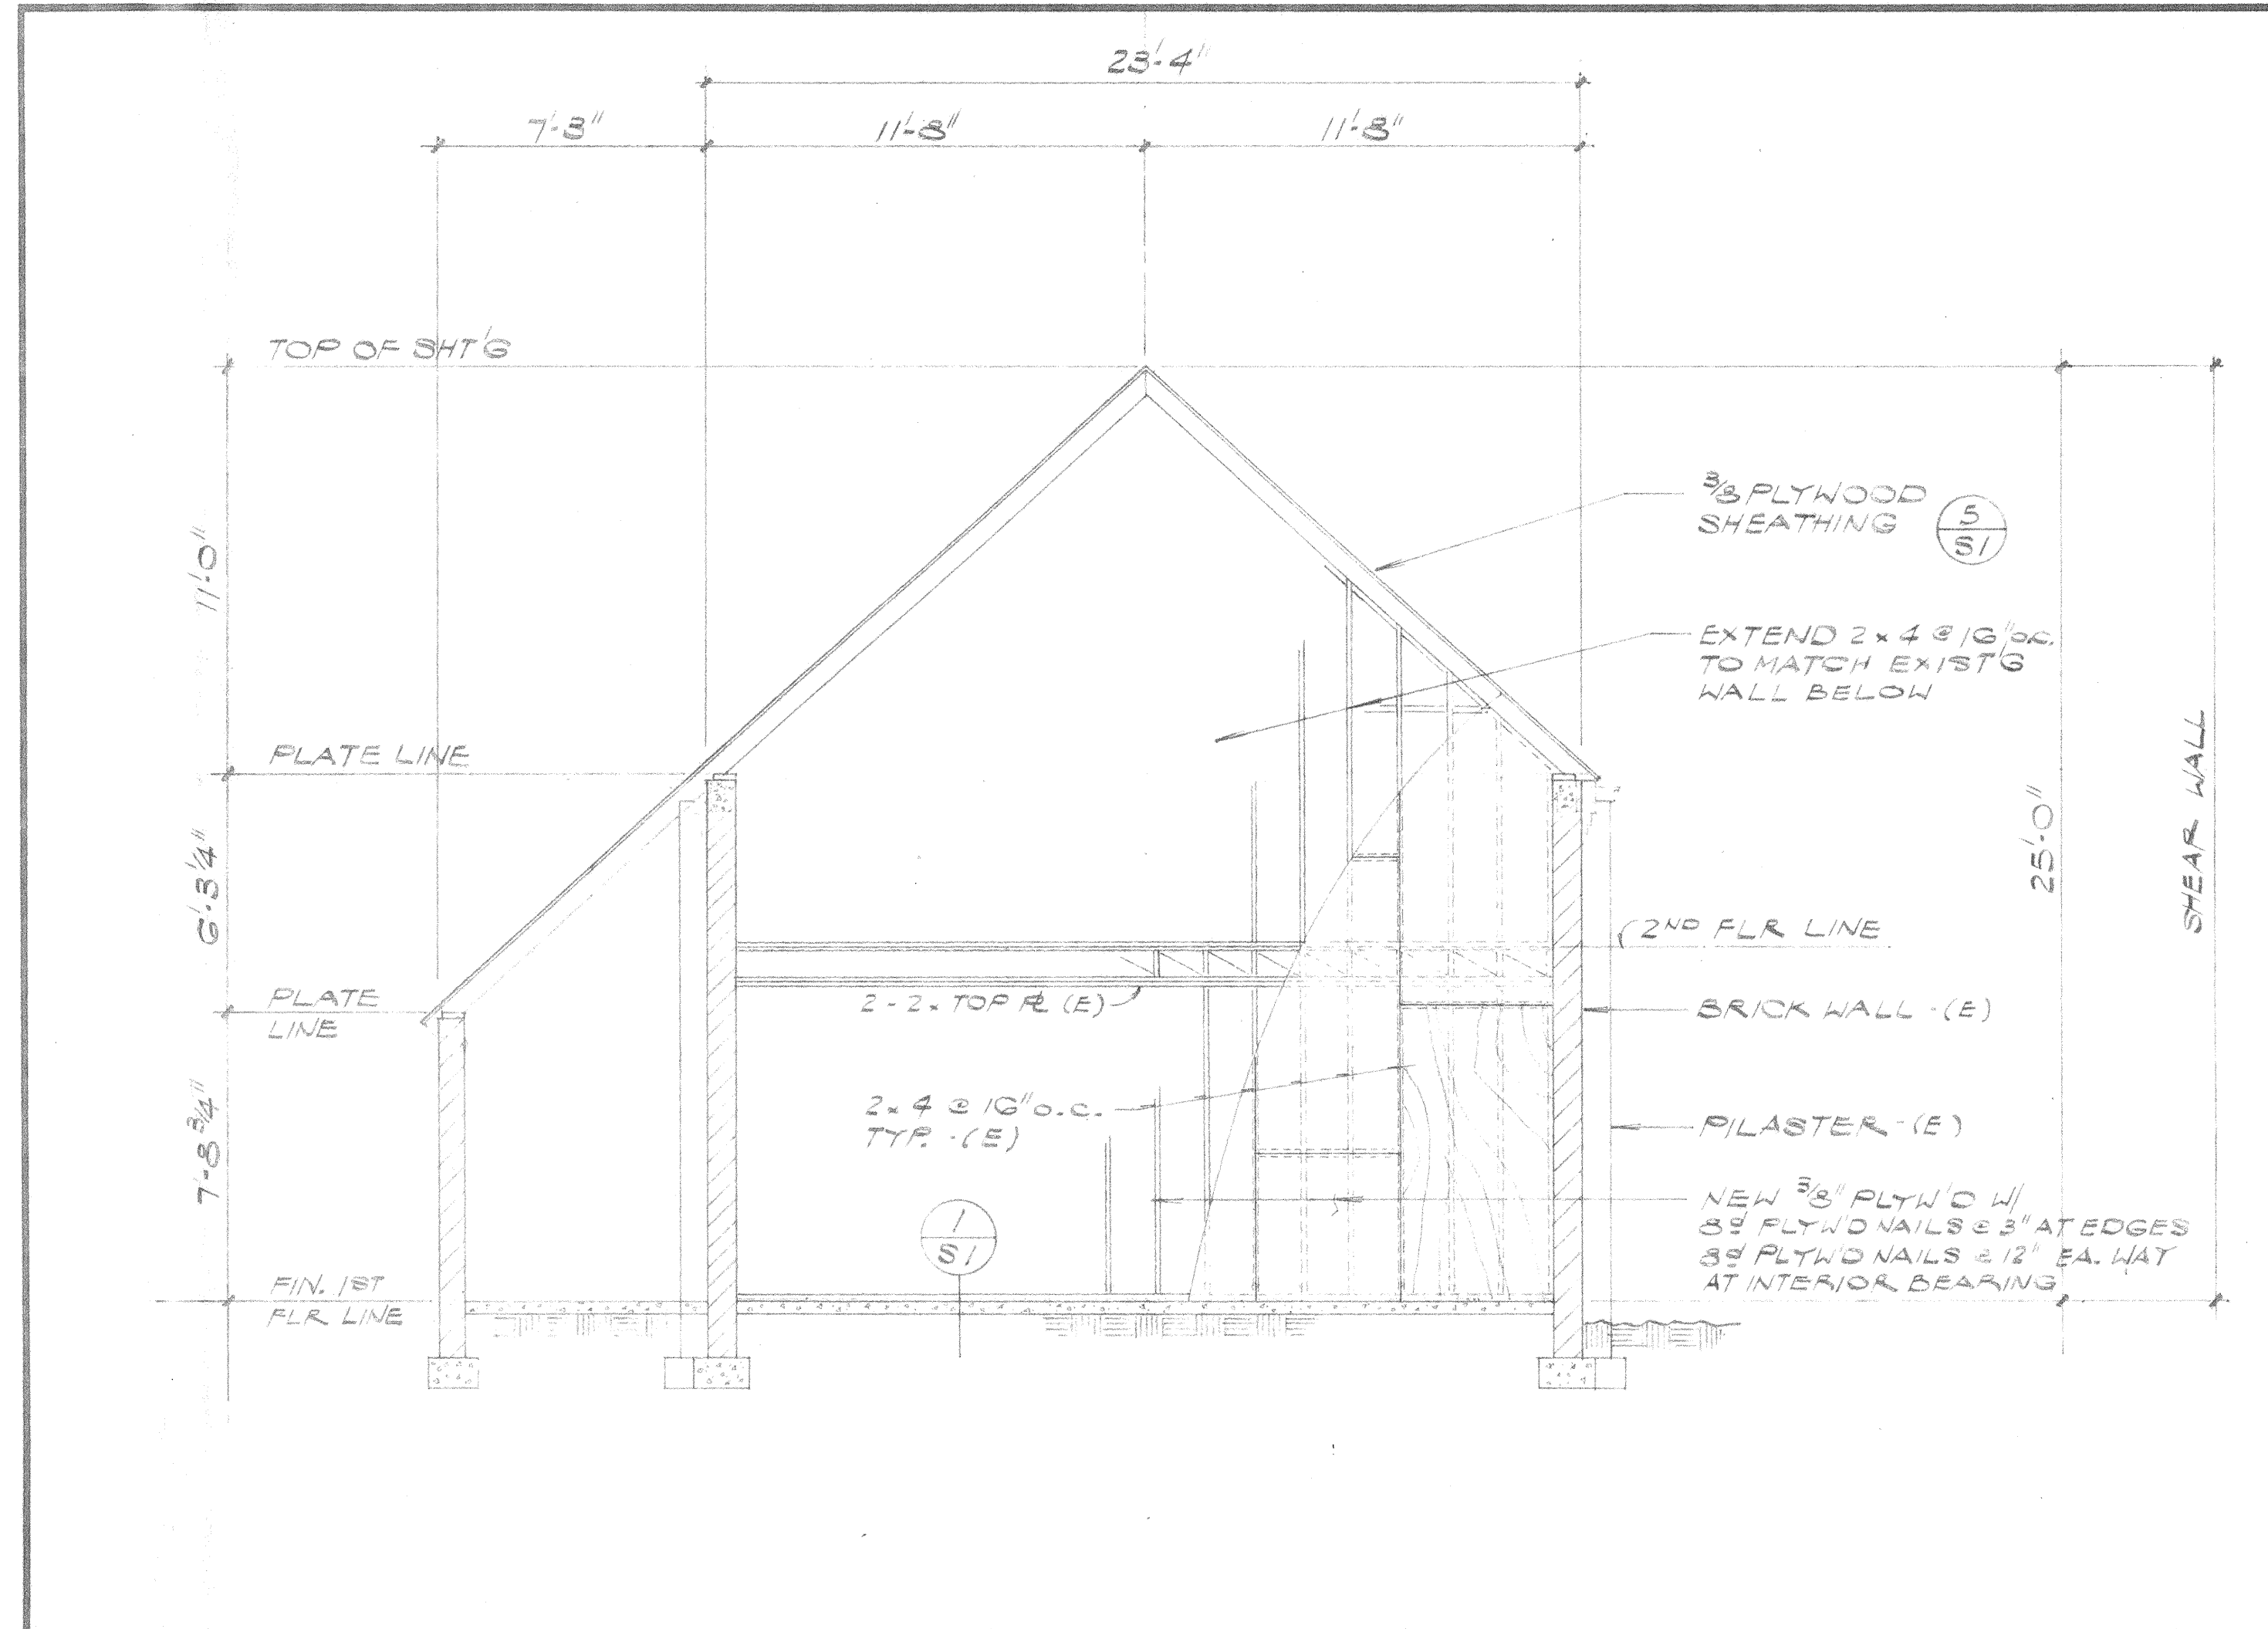


SHEAR WALL ELEVATION

1/4" 1

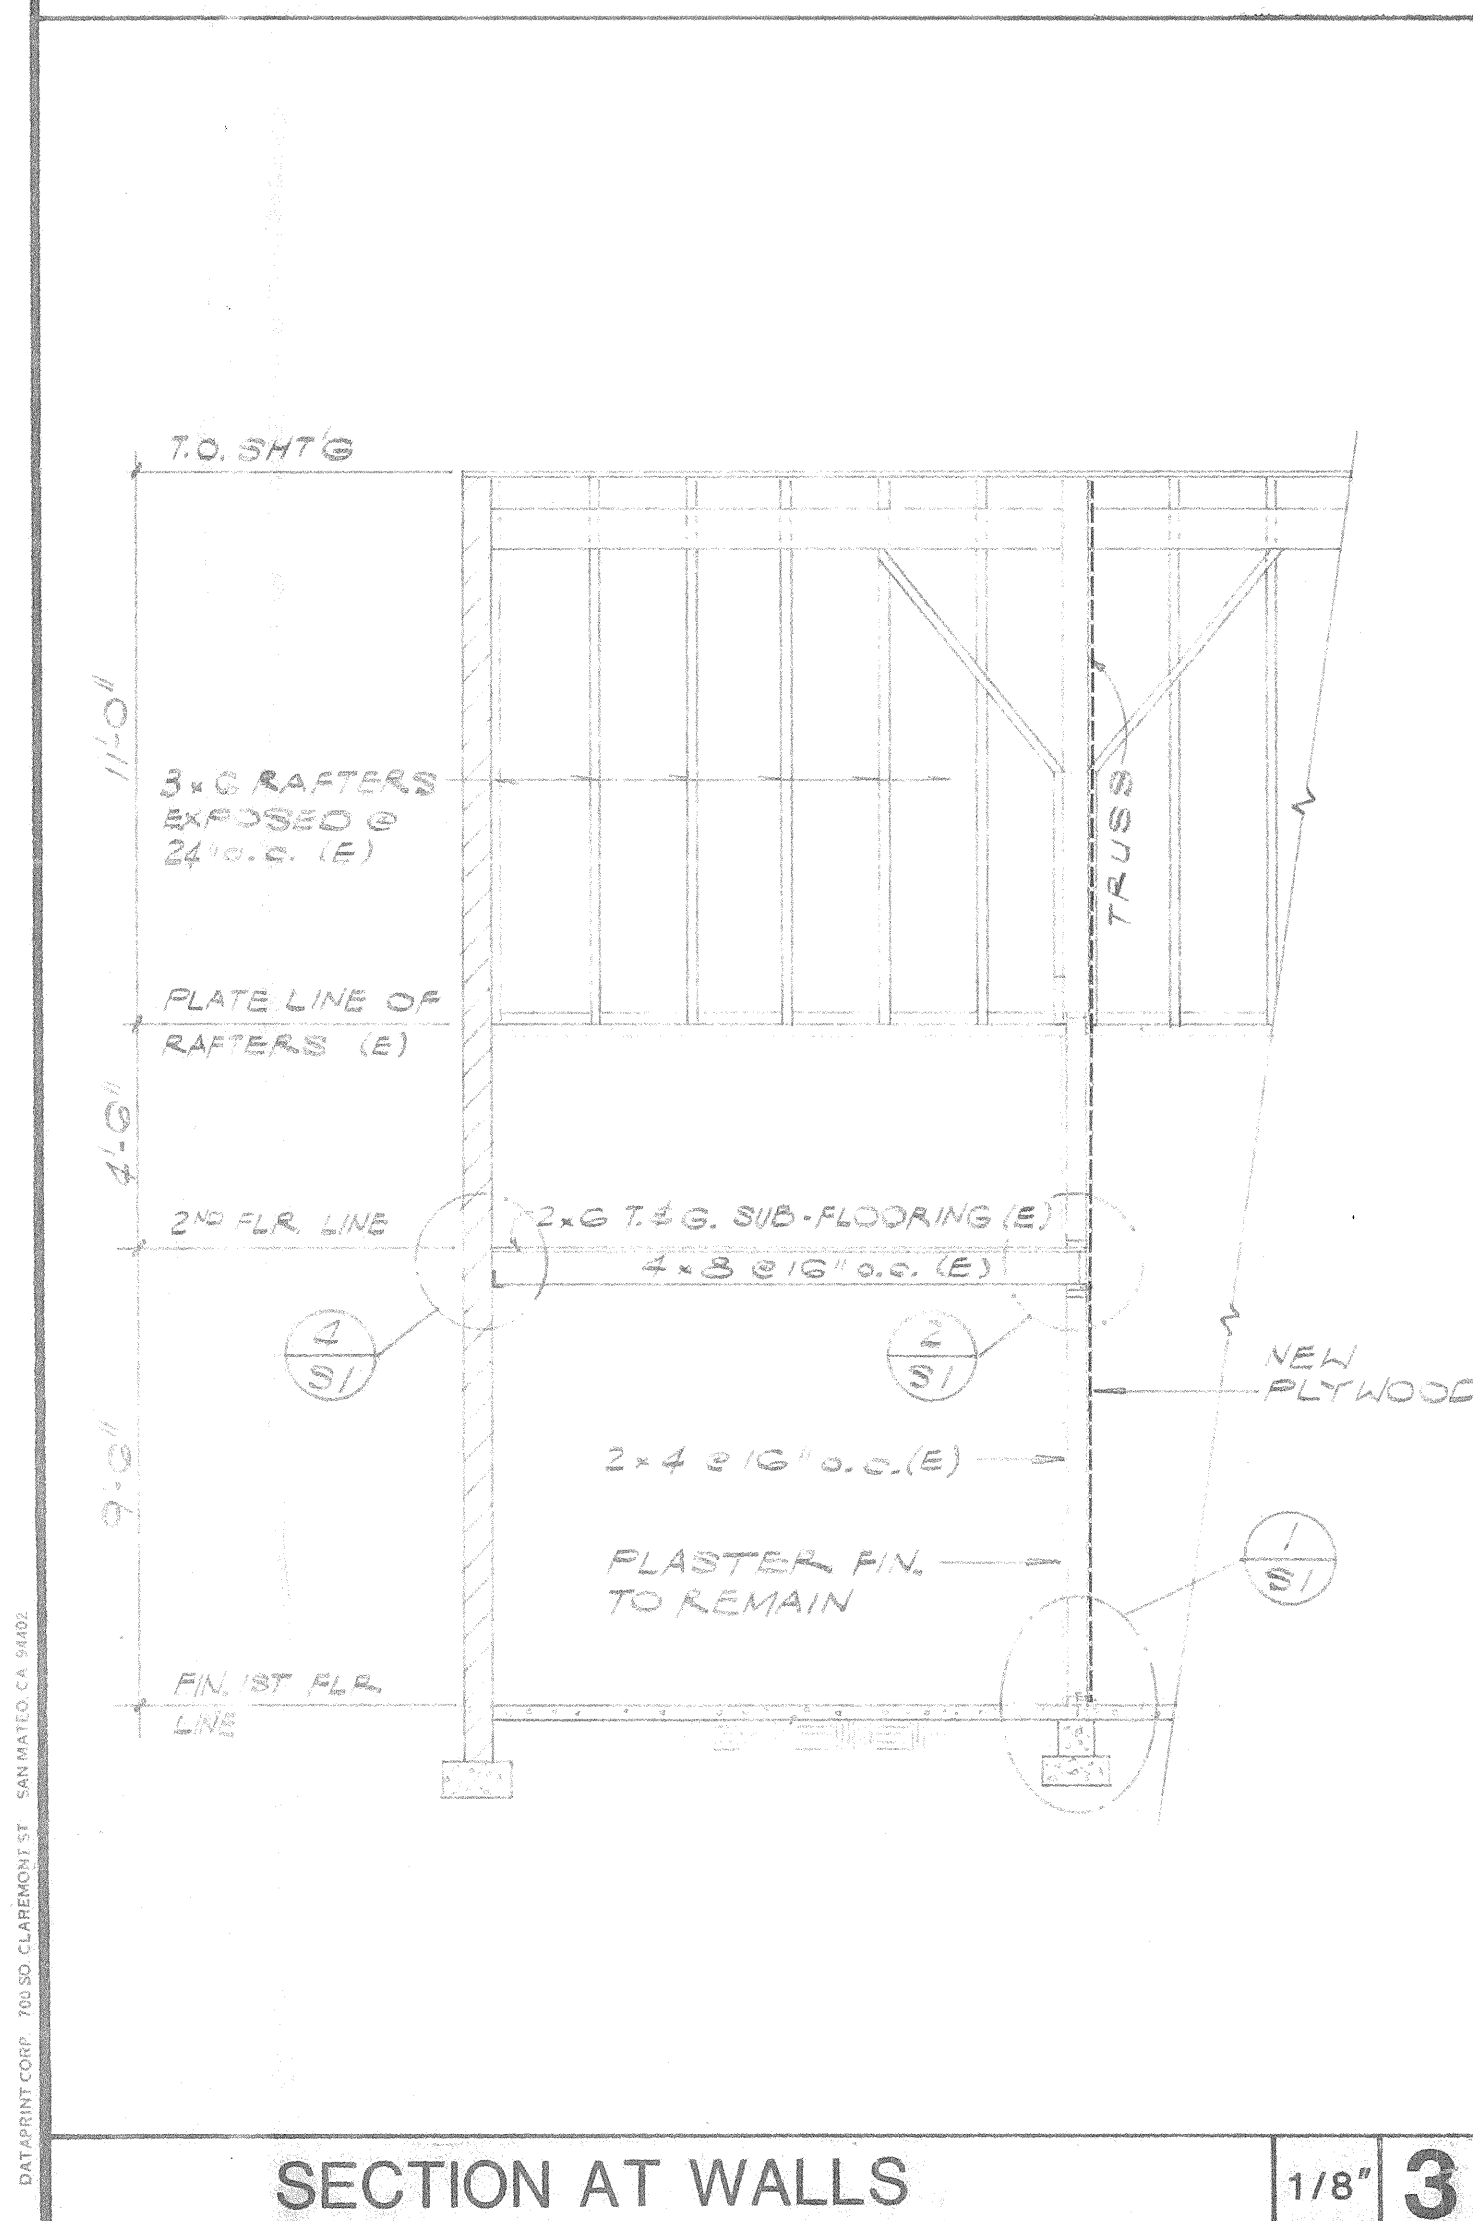


SECTION AT WALLS

1/8" 3

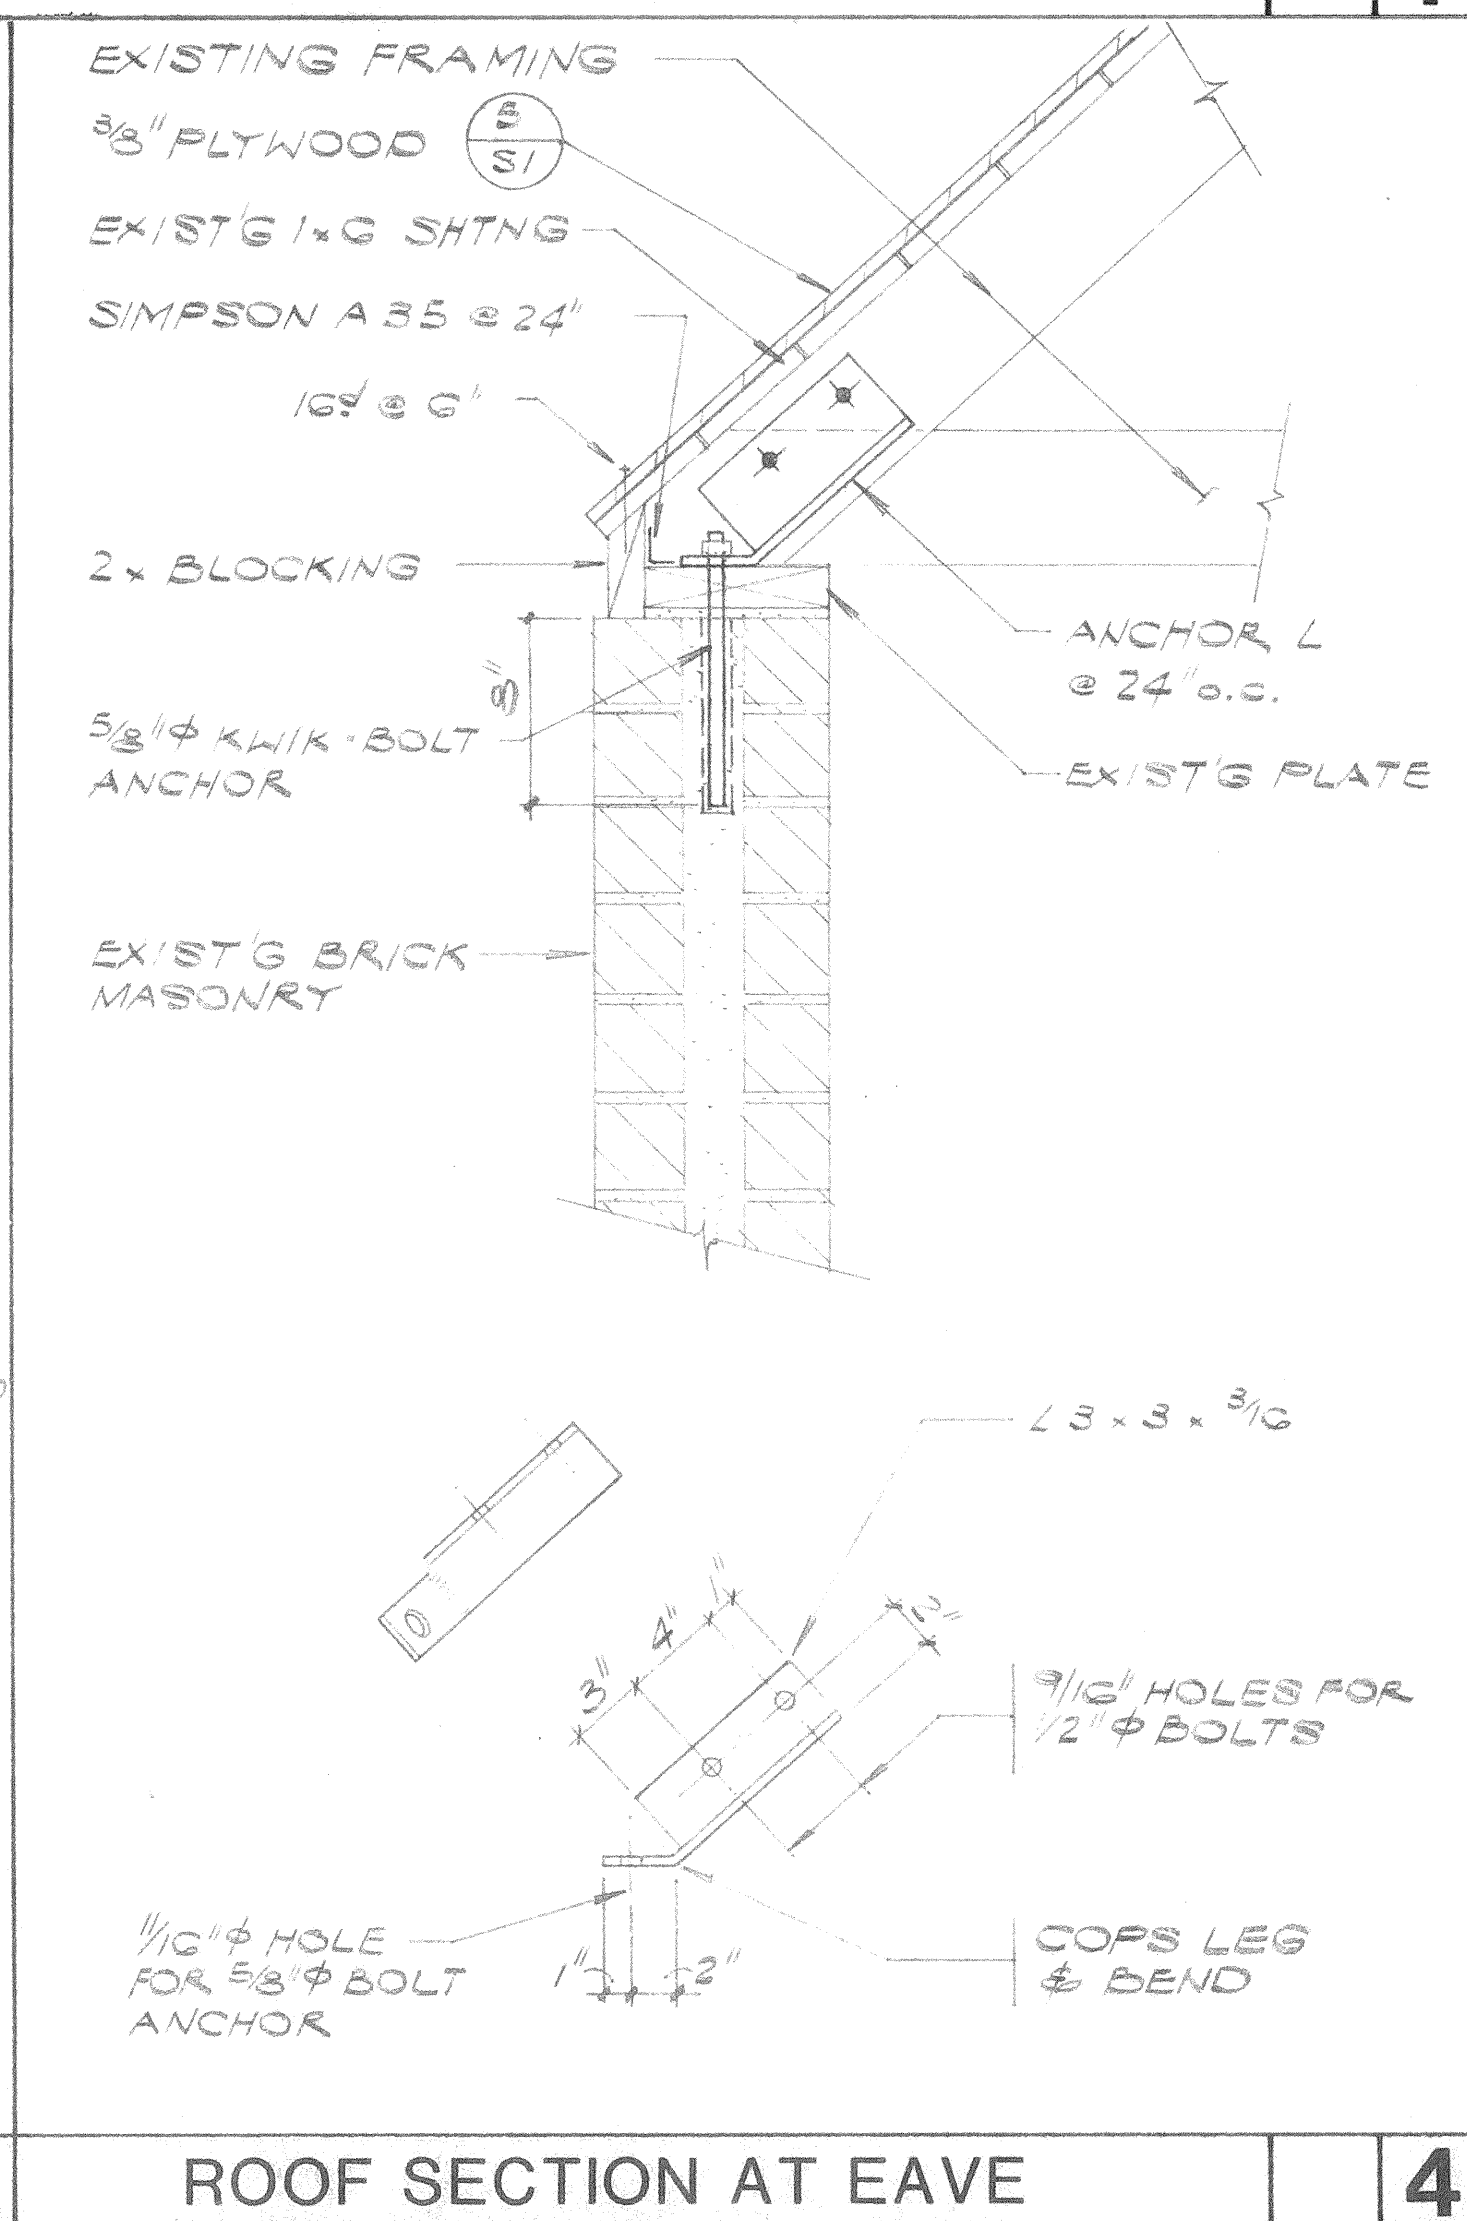


ROOF SECTION AT EAVE

4

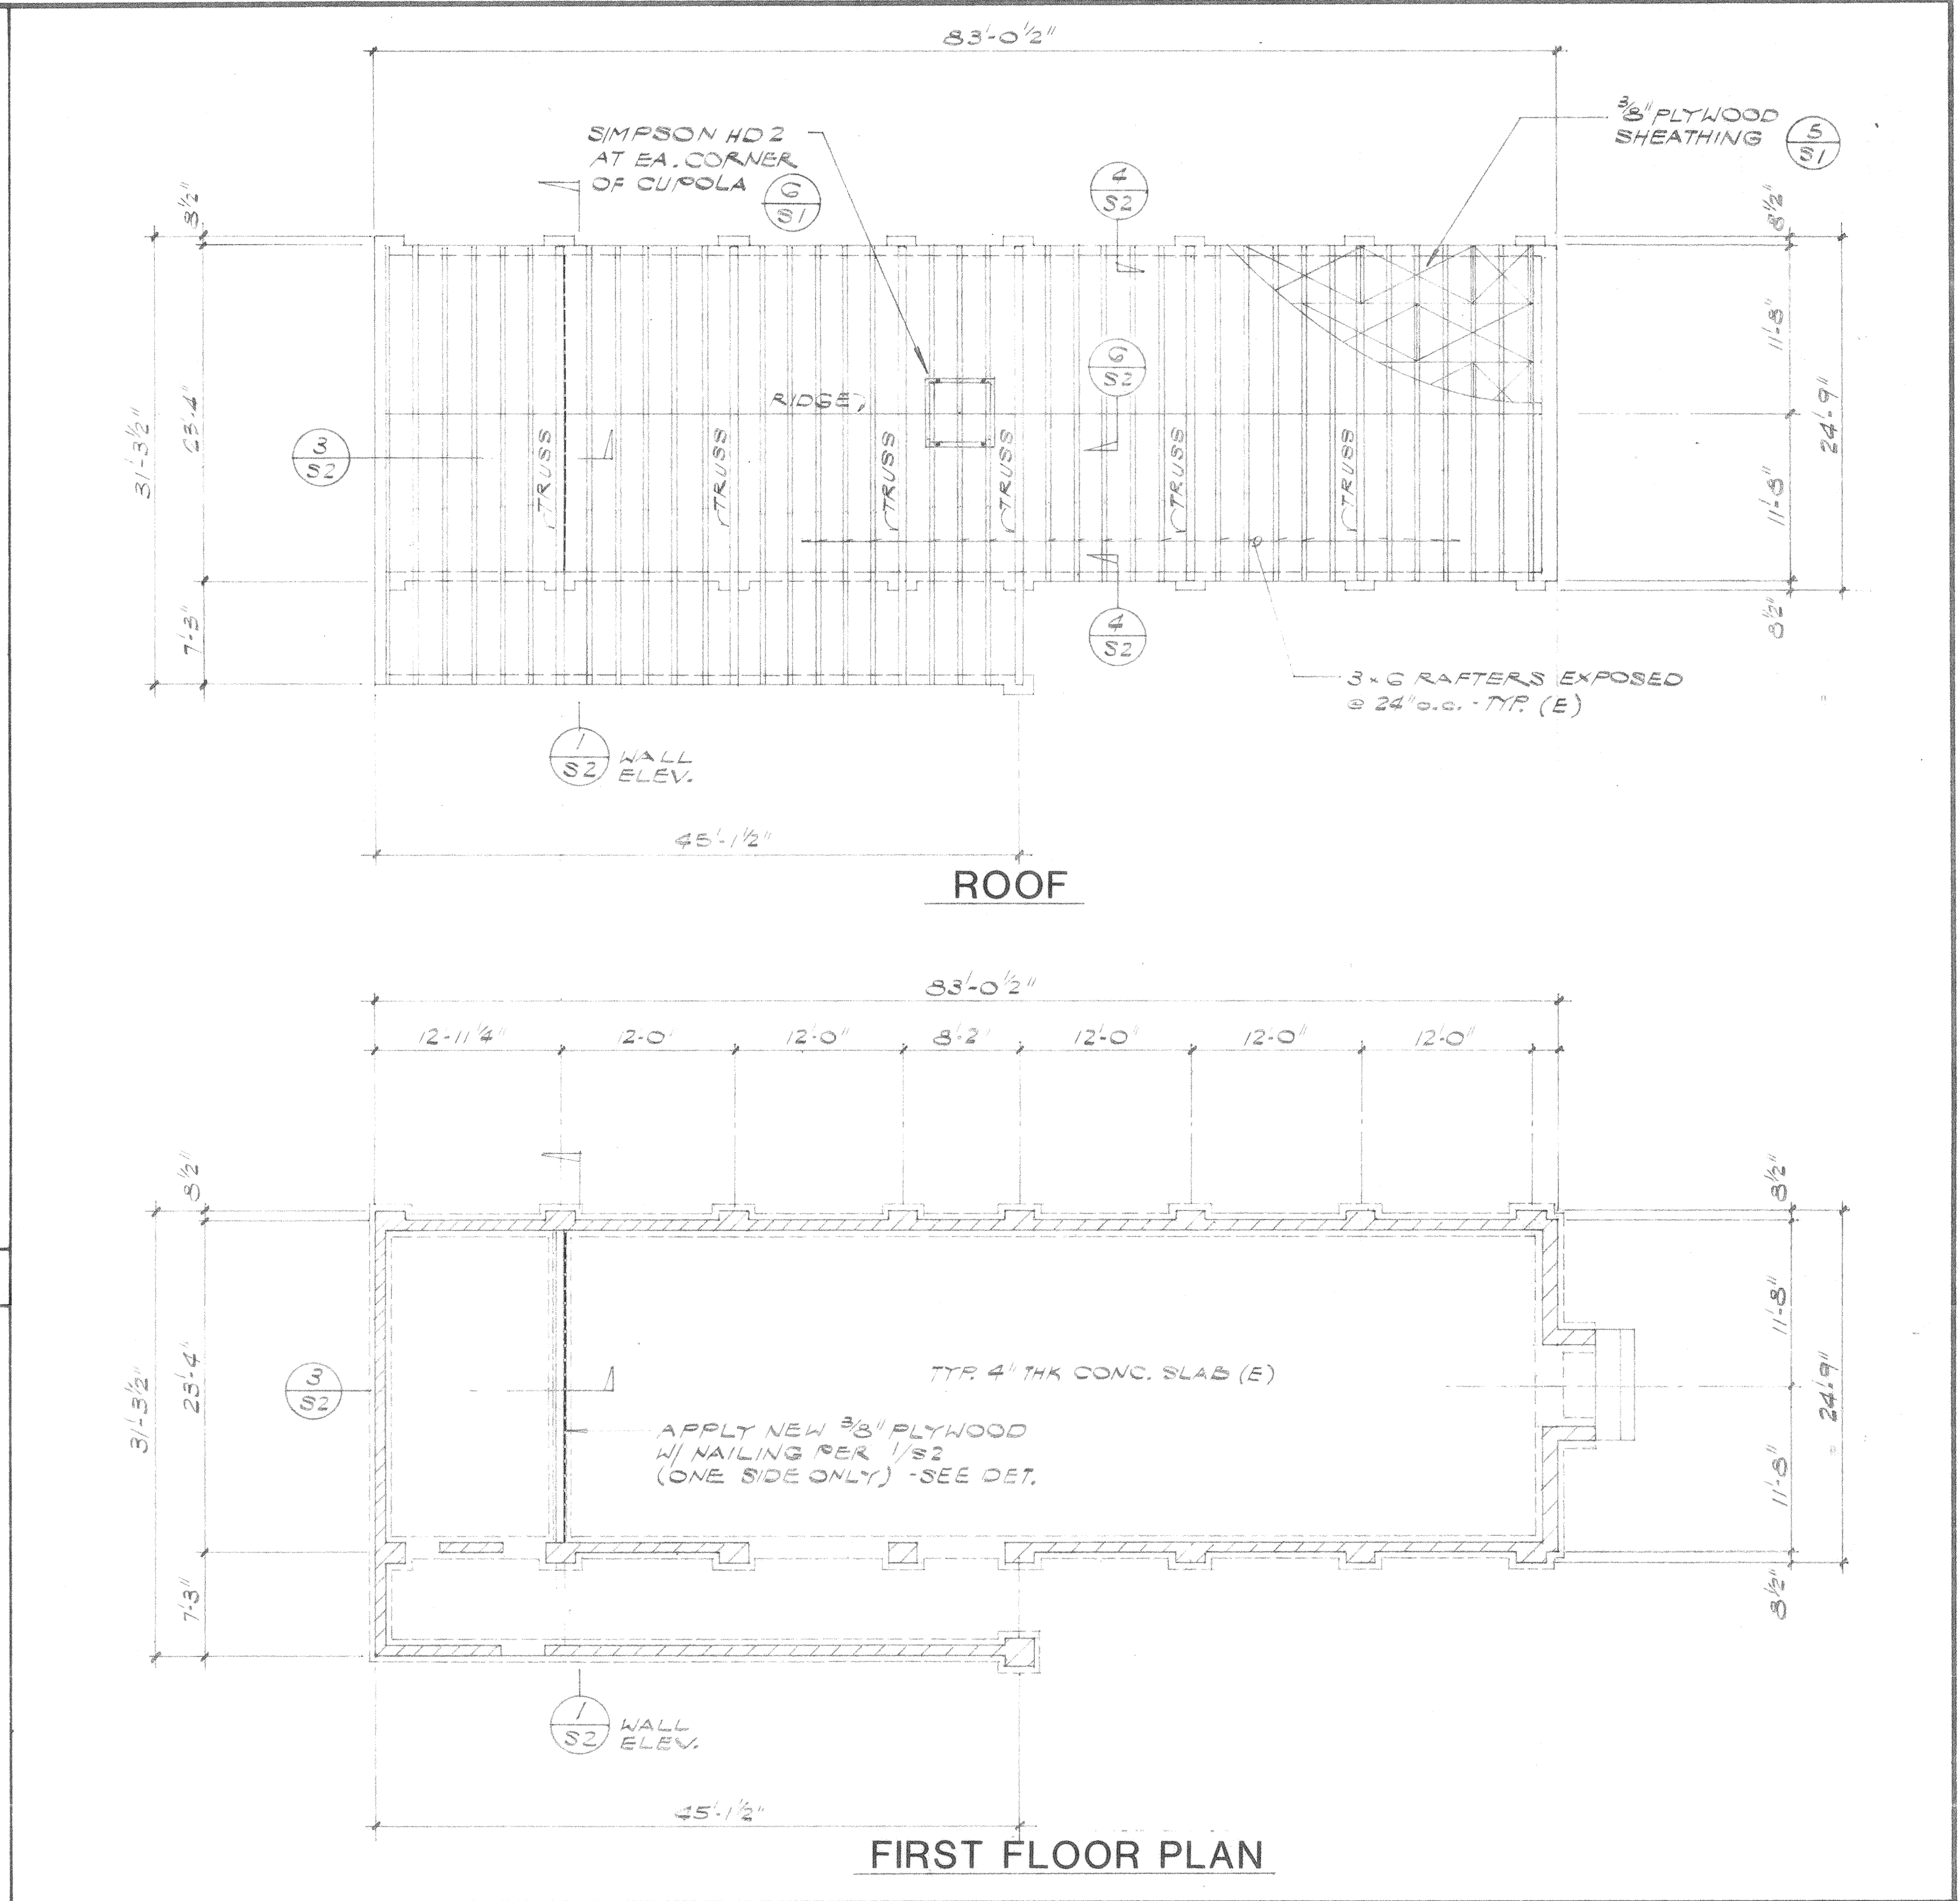


PLAN OF ROOF & FIRST FLOOR

1/8" 2

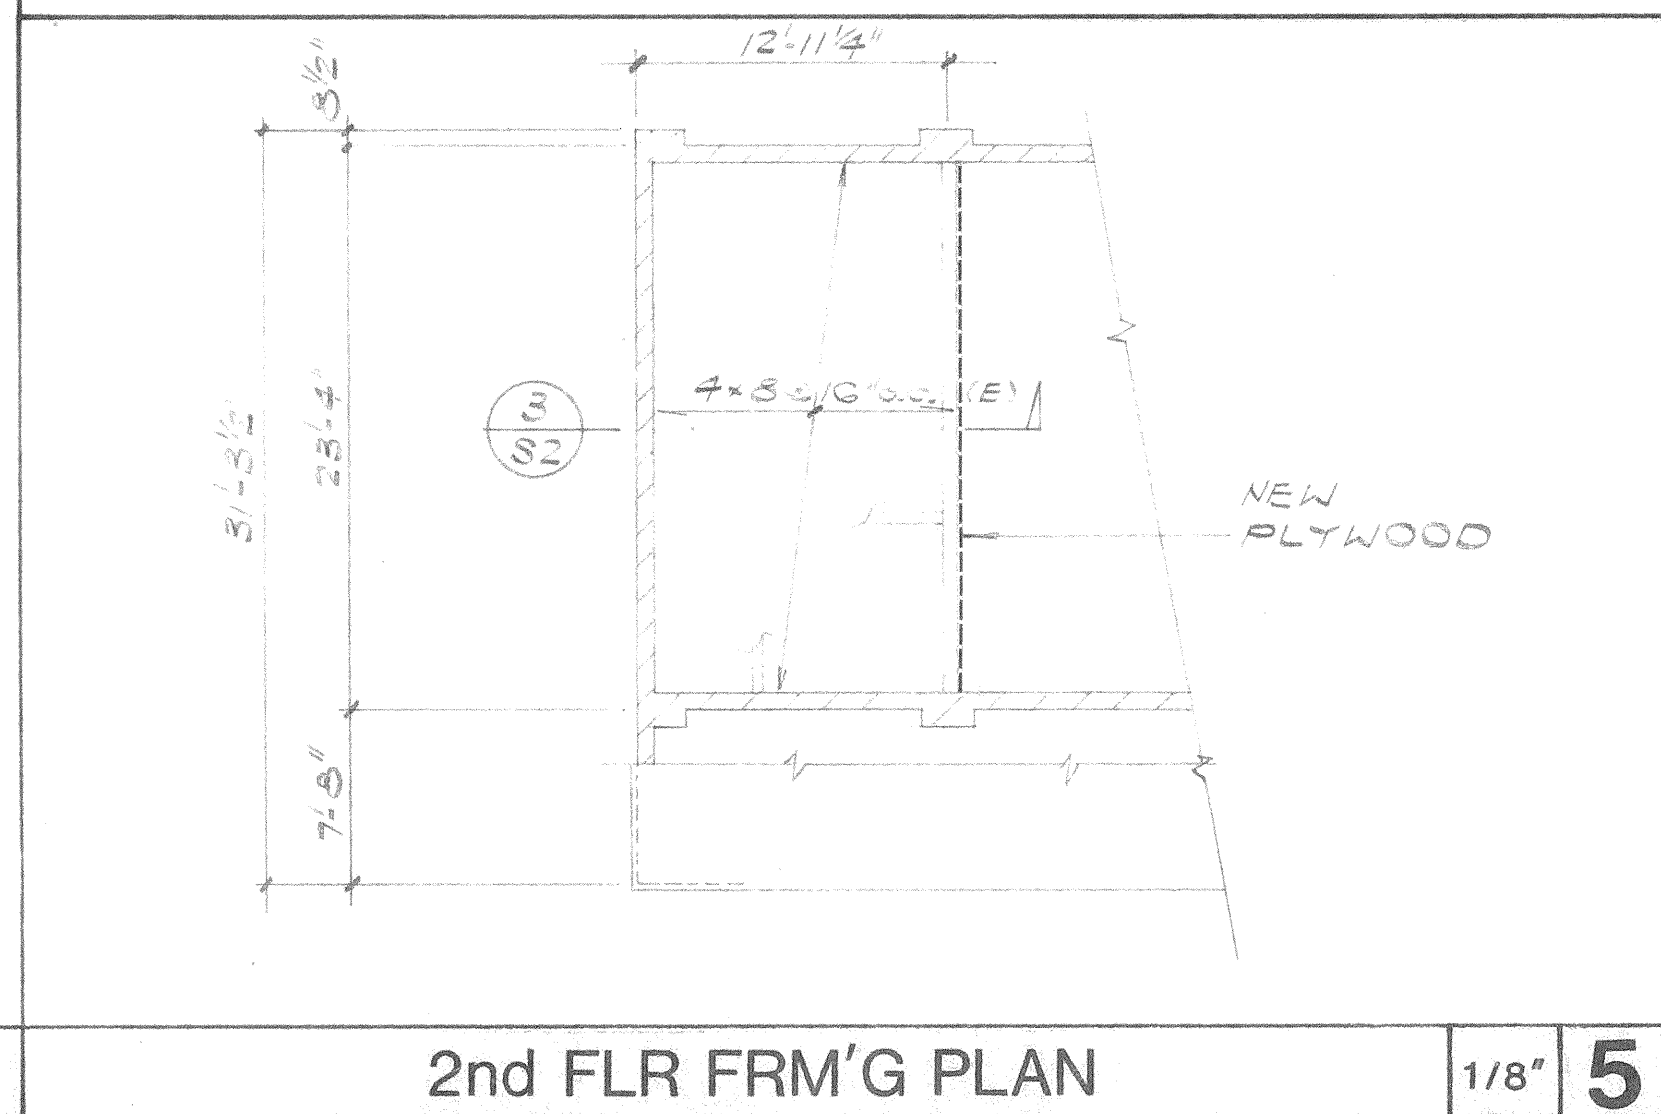

2nd FLR FRM'G PLAN

1/8" 5

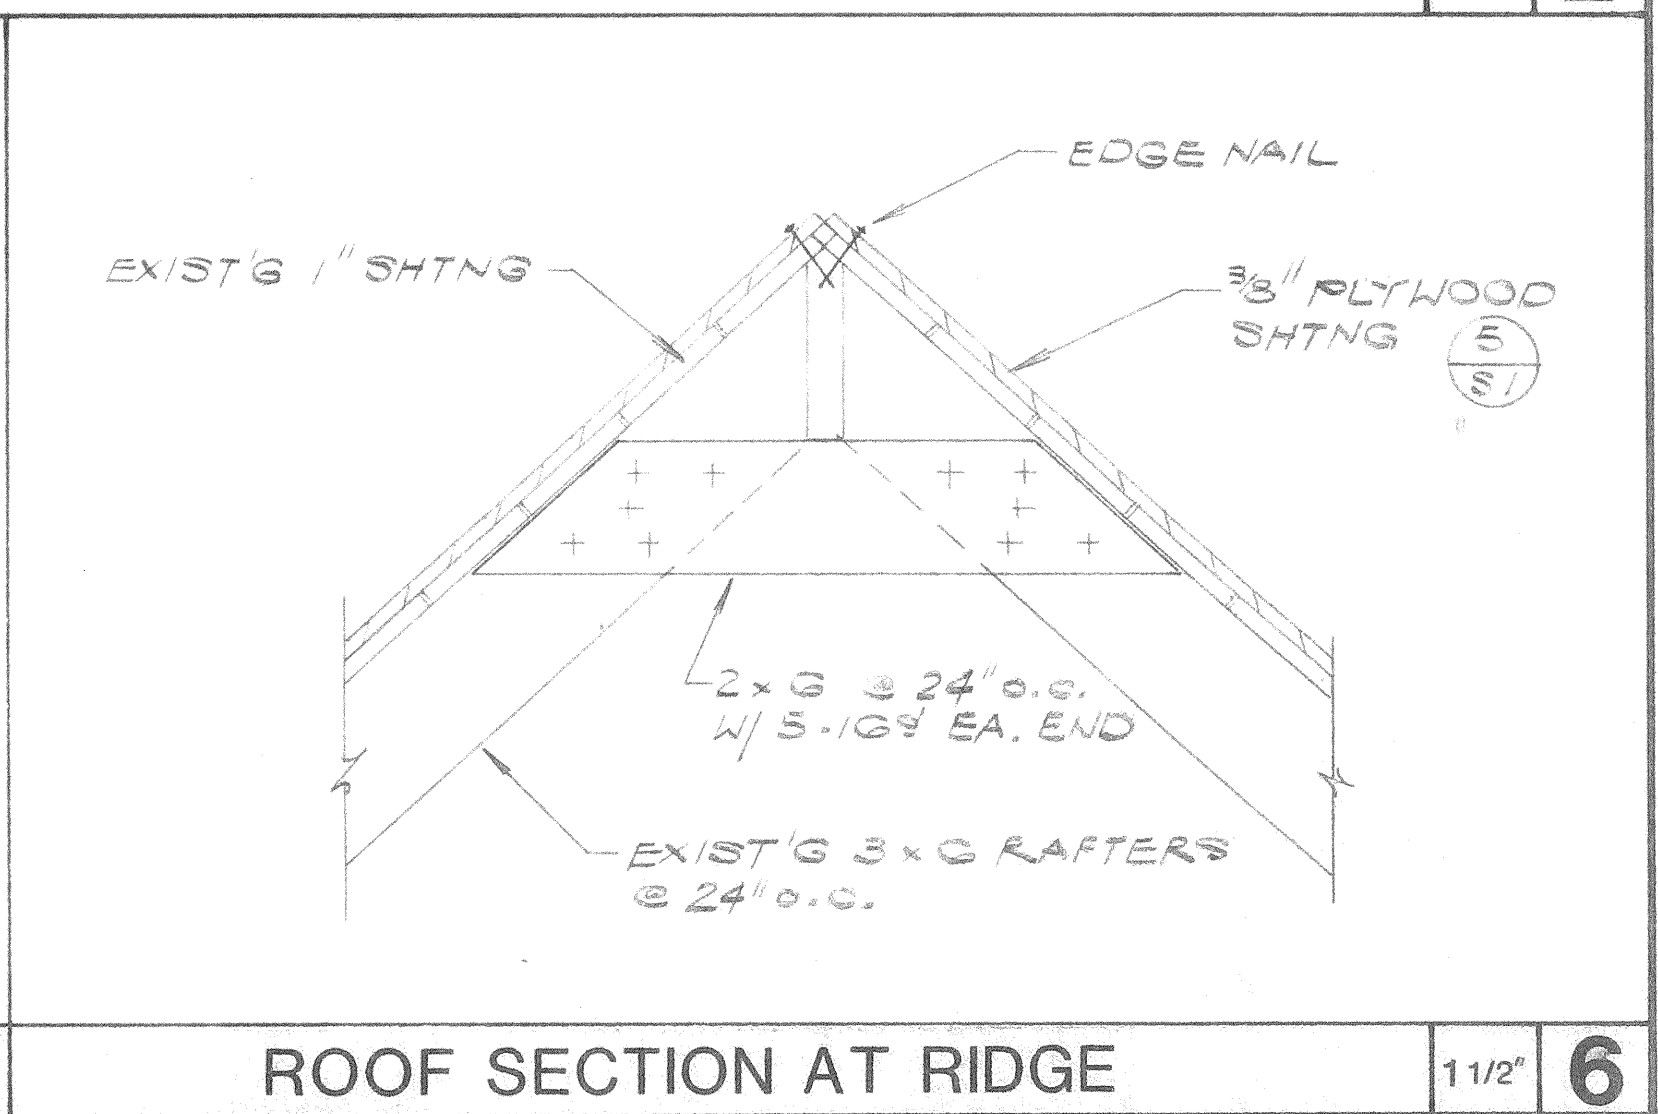

ROOF SECTION AT RIDGE

1 1/2" 6

REVISIONS		BY
6-7-90		HA

TAYLOR & GAINES
STRUCTURAL ENGINEERS
550 NORTH ROSEMEAD BOULEVARD
PASADENA, CALIFORNIA 91107-2192
(818) 351-8881

**SEISMIC UPGRADING OF THE
ST. EDMUND'S EPISCOPAL CHURCH
(CHAPEL BLDG.)**

SAN MARINO, CA. 91108

DATE		6-4-90
SCALE	NOTED	
DRAWN	HRA	
JOB		
SHEET	S-2	

OF 2 SHEETS