

# BIDDING NOTES

## DO NOT INCLUDE IN BID PRICE:



- ORNAMENTAL IRON WORK ATTACHED TO HANGER RODS,
- NEW SPEAKERS,
- NEW ELECTRICAL WORK,
- STAIN GLASS WINDOWS.

## INCLUDE IN BID PRICE:


- REMOVAL AND DISPOSAL OF EXISTING SMALL BALCONY AND FAN AT INTERIOR OF EAST WALL OF CHAPEL. ELECTRICAL CONDUITS TO REMAIN.

## SUBMIT SEPARATE BID FOR:

- REPAINTING INTERIOR OF EAST WALL OF CHAPEL TO MATCH EXISTING COLOR.

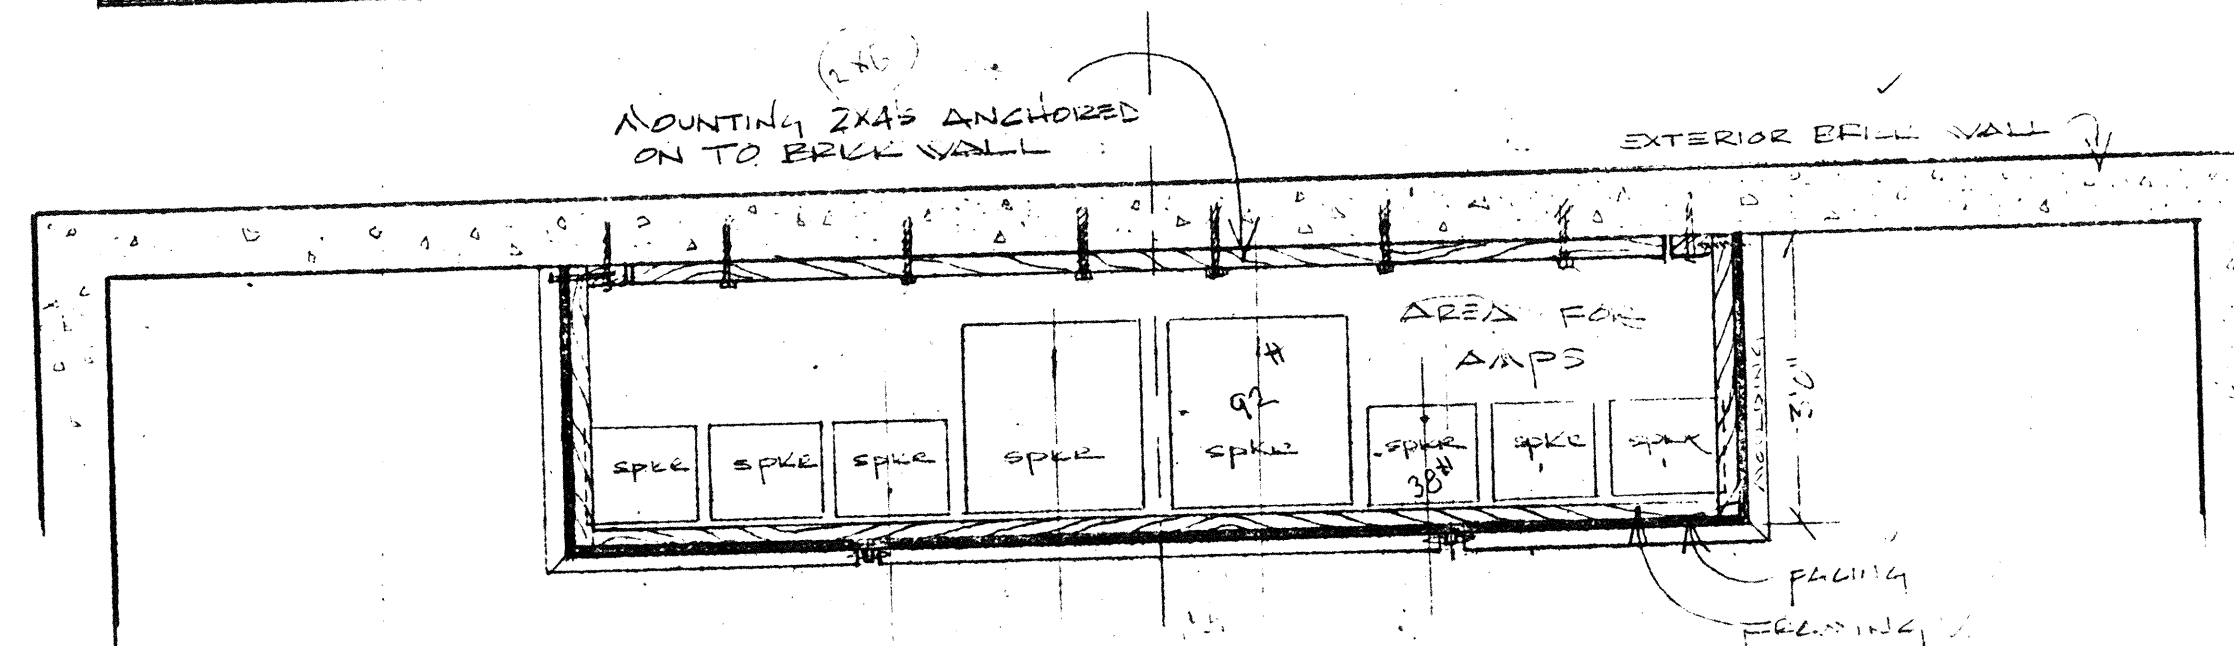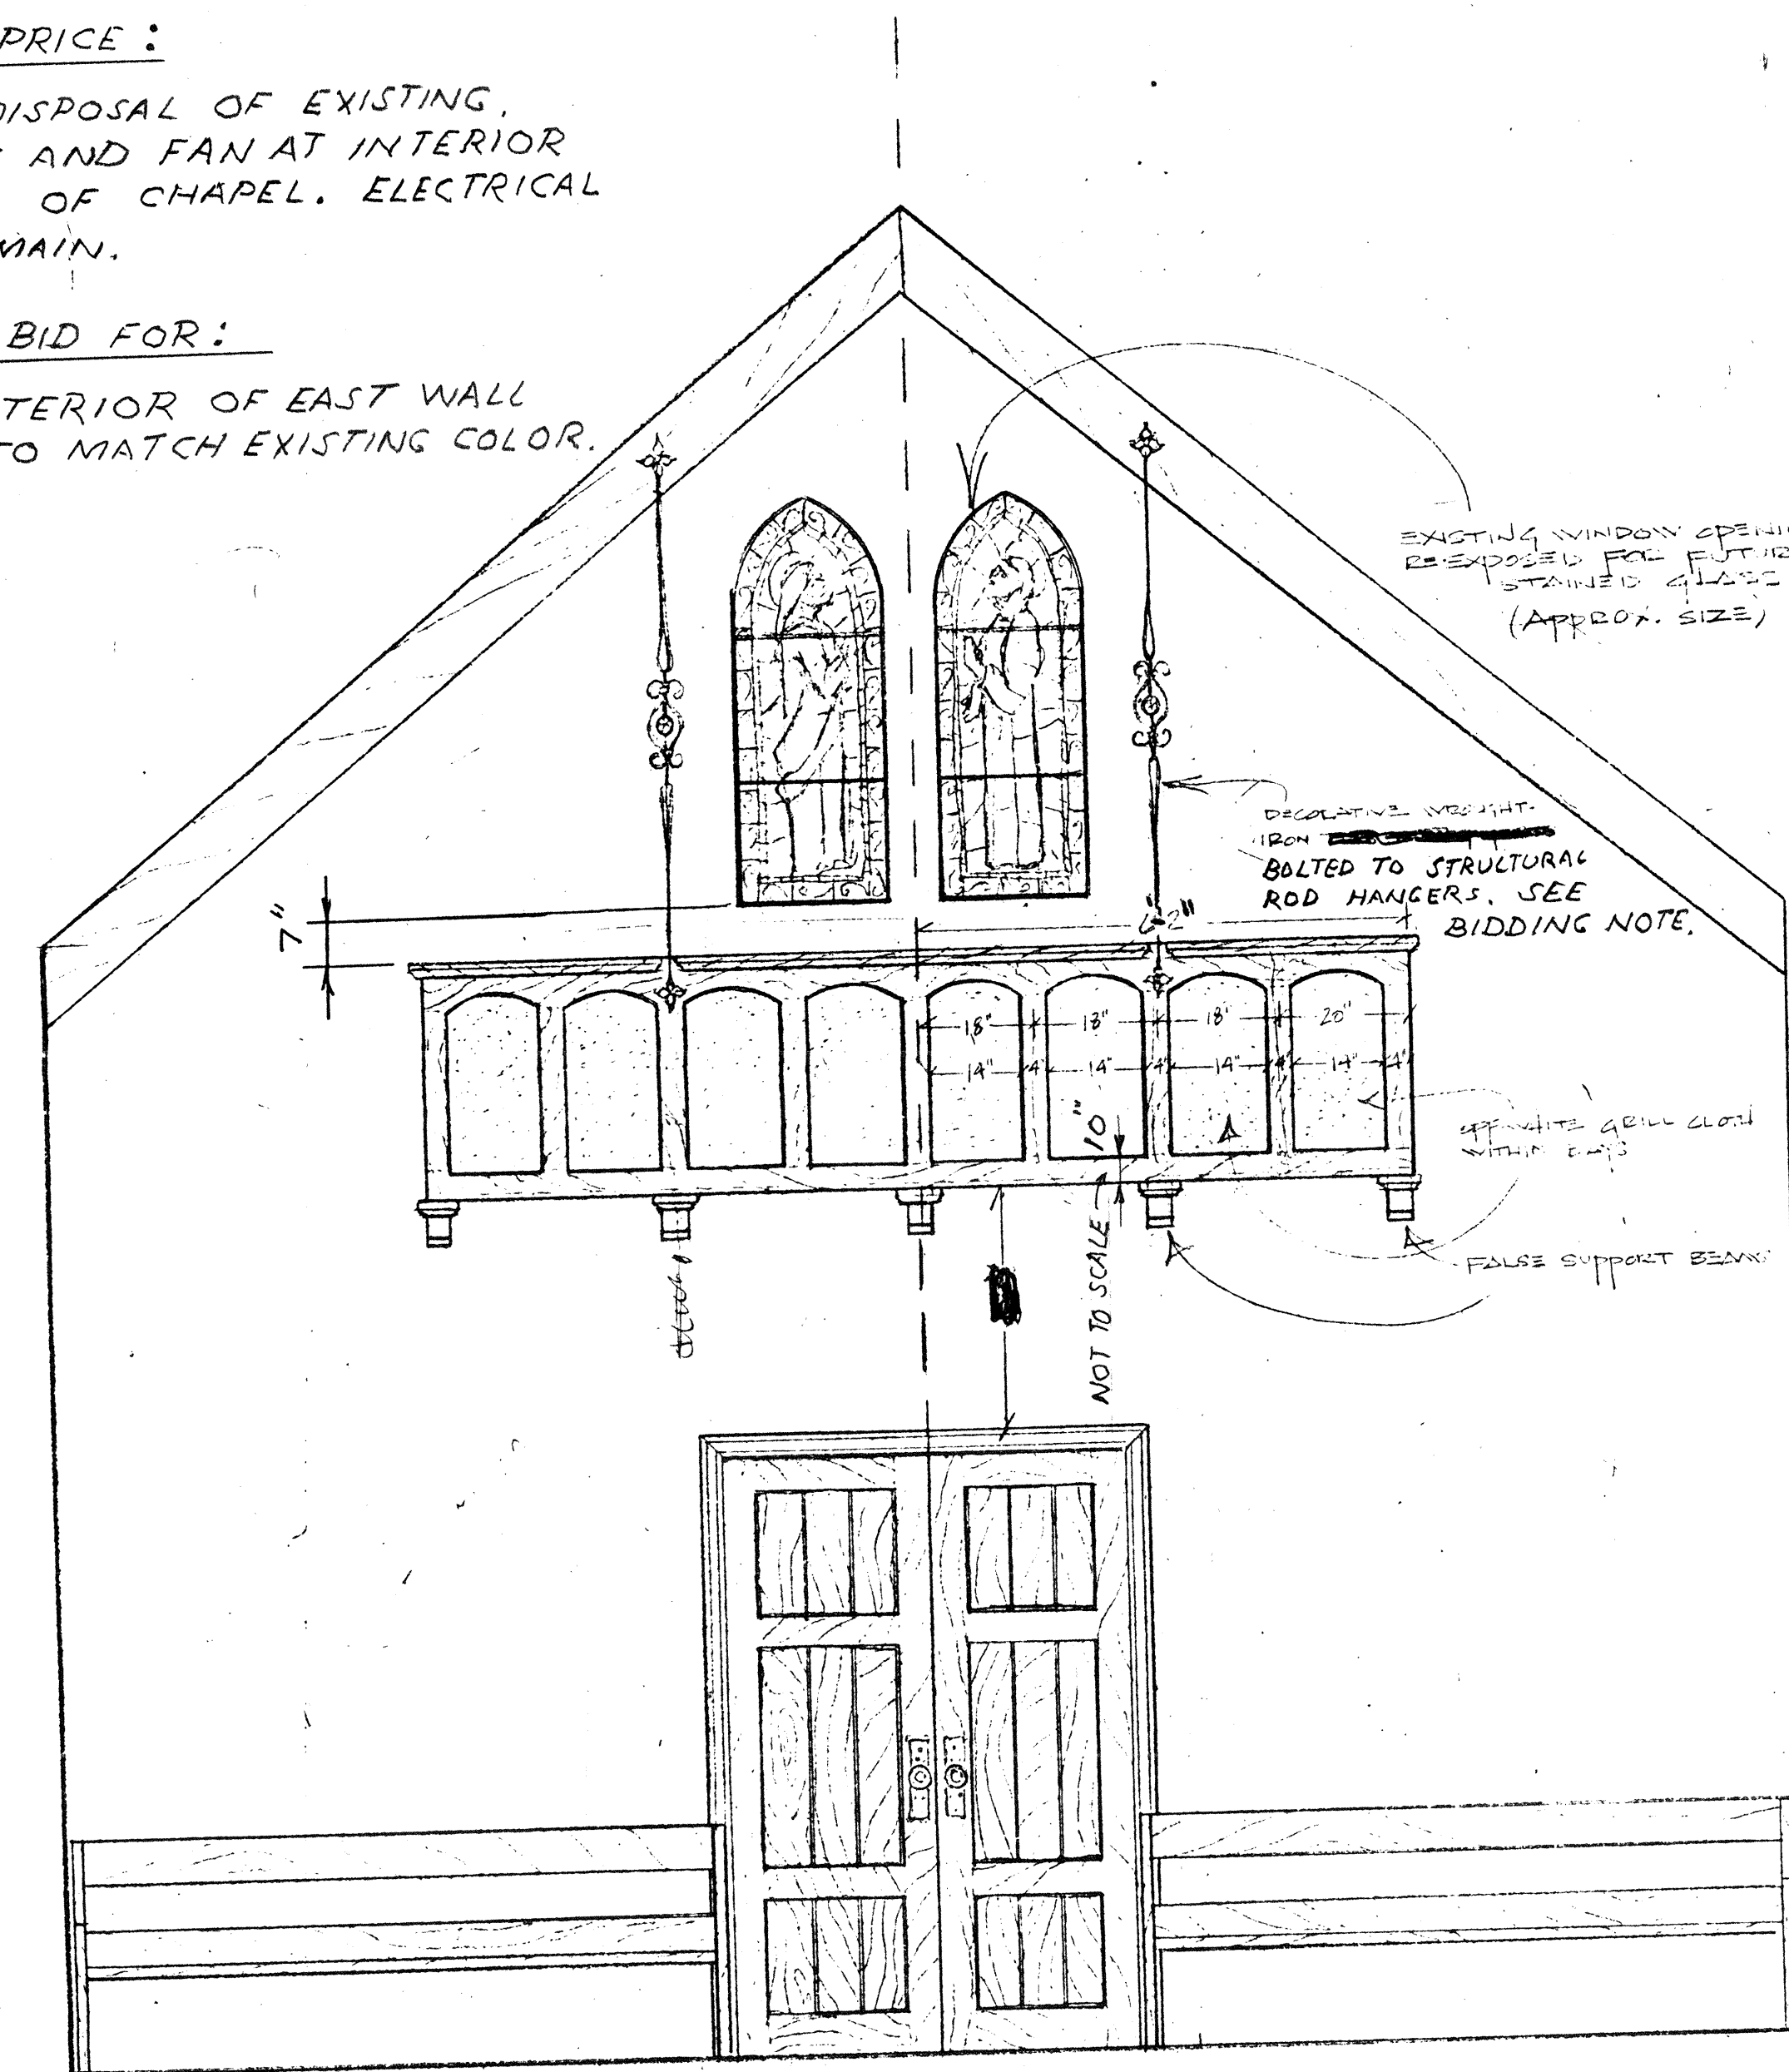

EAST WALL - PLAN & ELEVATION

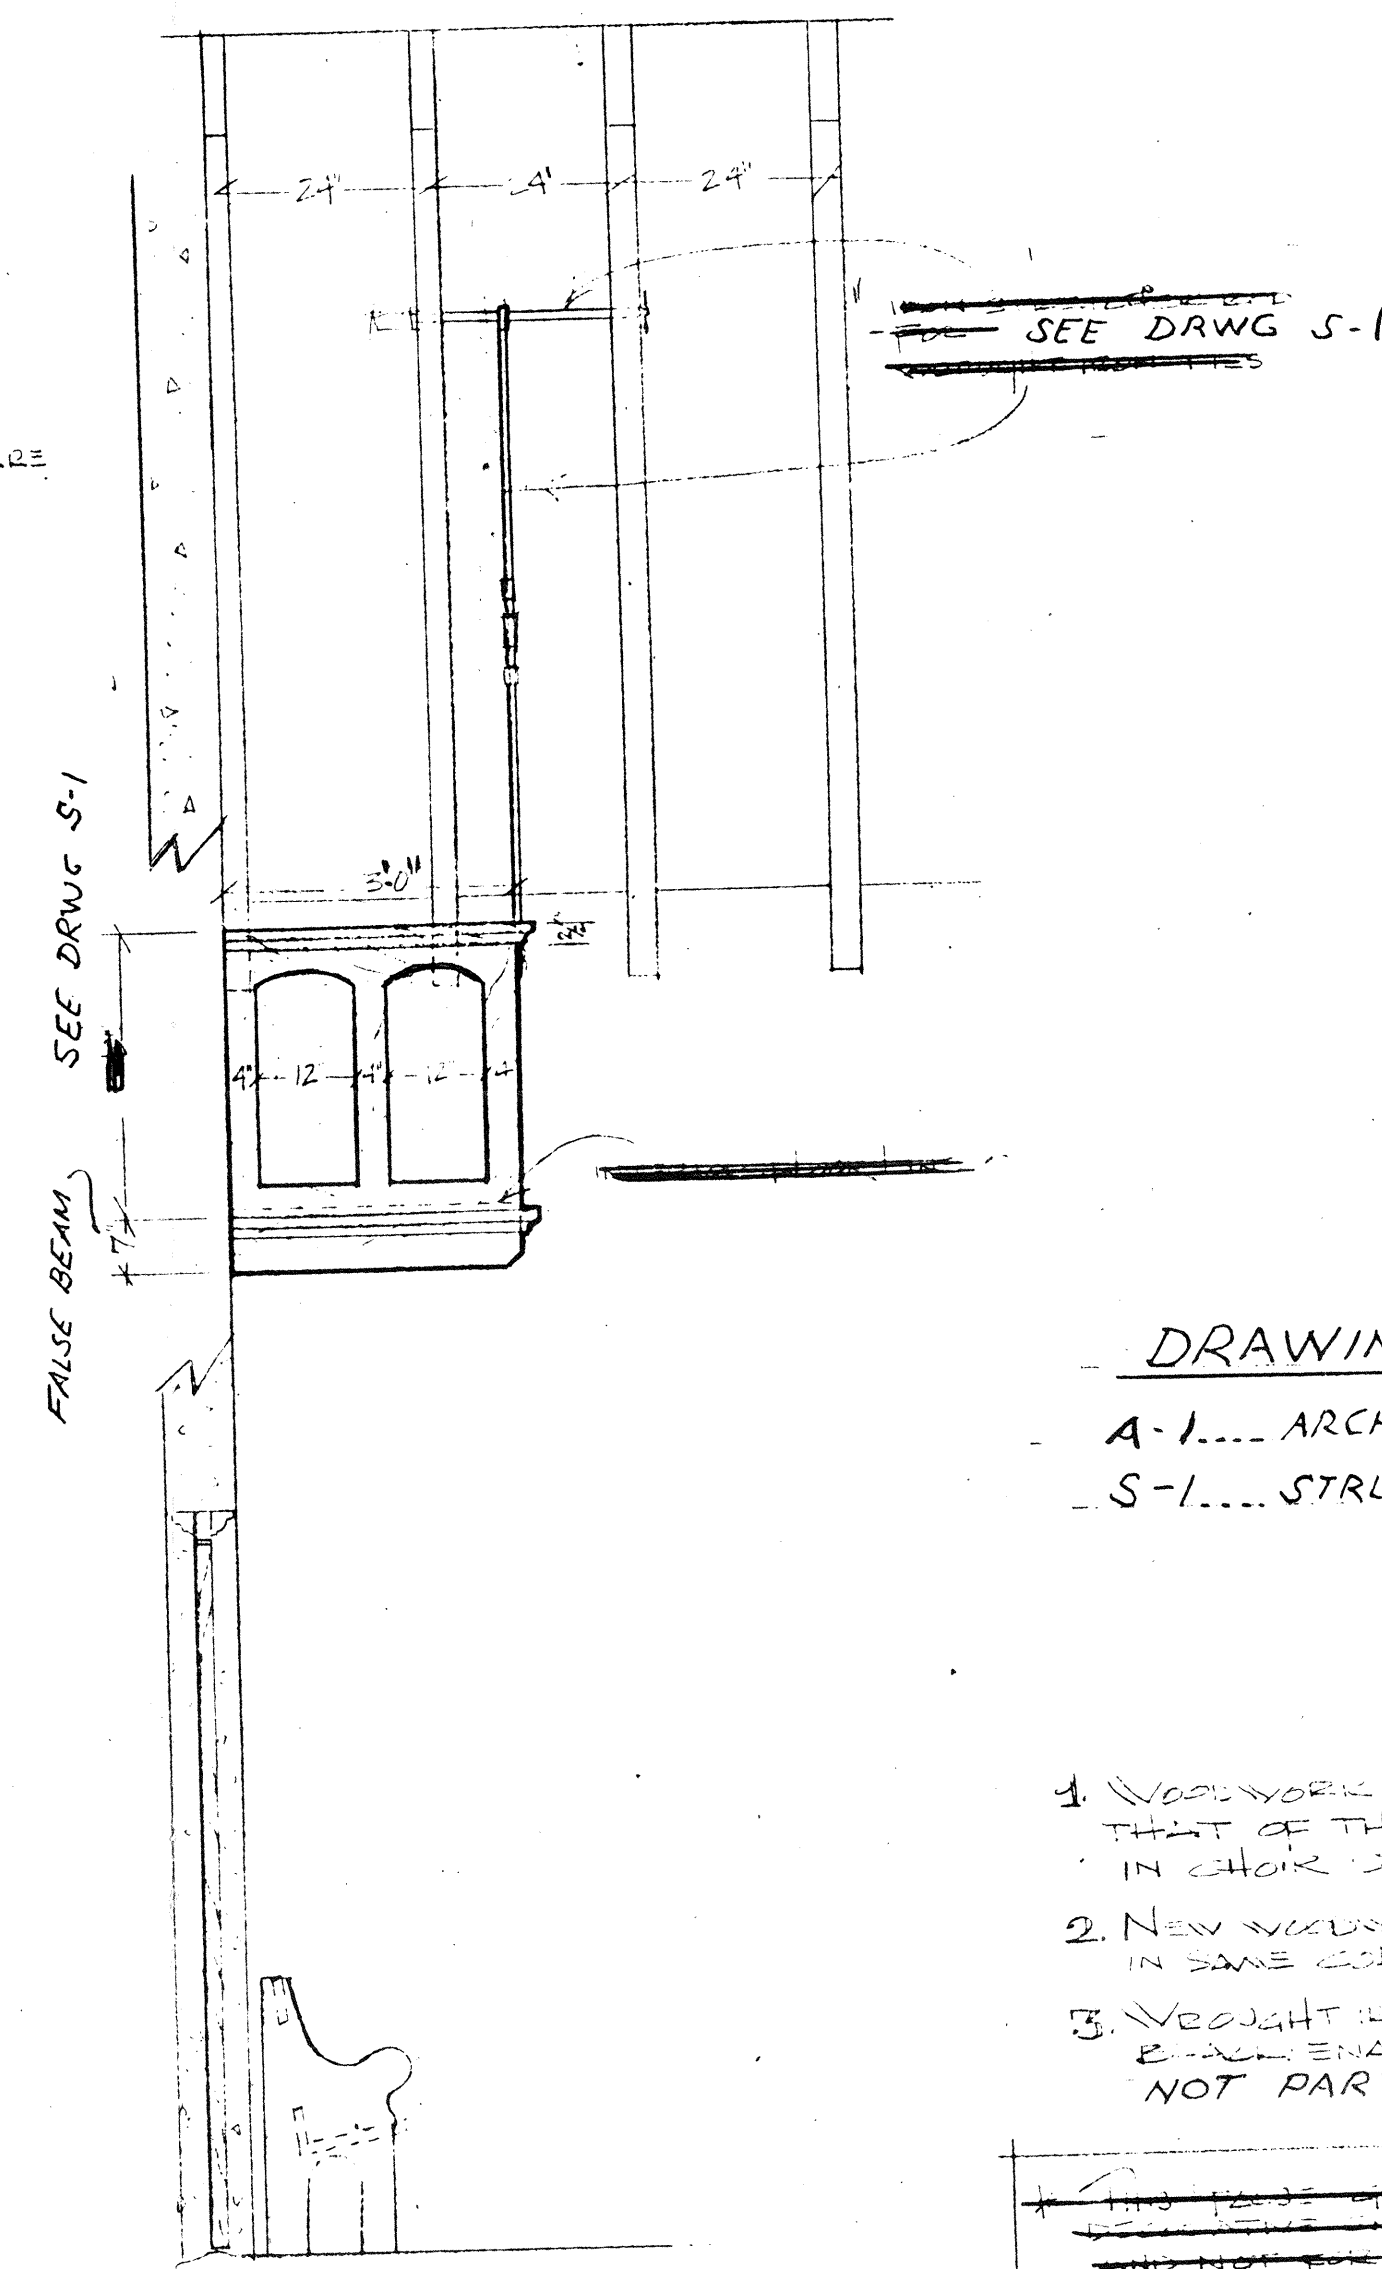


SECTION THRU EAST WALL

## DRAWING INDEX

- A-1... ARCHITECTURAL DETAILS
- S-1... STRUCTURAL DETAILS

1. WOODWORK DESIGN OF CHAIRS FOLLOWS THAT OF THE EXISTING ADJACENT CHAIRS IN CHOR STALLS
2. NEW WOODWORK TO BE STAINED & FINISHED IN SAME COLOR AS EXISTING WOODWORK
3. WROUGHT IRON TIES TO BE PAINTED IN BLACK ENAMEL WITH 4" WOOD DETAIL. NOT PART OF THIS CONTRACT BID.

THIS DRAWING IS THE PROPERTY OF THE ARCHITECT AND IS NOT TO BE REPRODUCED OR USED FOR ANY OTHER PROJECT WITHOUT THE WRITTEN CONSENT OF THE ARCHITECT.

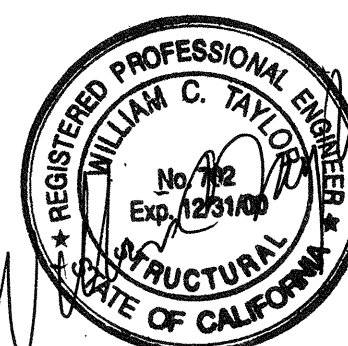

|   |                                                         |
|---|---------------------------------------------------------|
| <p>FALSE CHAIRS</p> <p>FOR NEW ORGAN SPEAKERS IN THE CHAPEL OF ST. EDWARDS CHURCH SAN MARINO</p> <p>14 AUGUST 1997 SCALE: 1/2"=10'</p> <p>RHETT JUDICE DESIGN &amp; PREPARED</p> | <p>DRAWING</p> <p>A-1</p> <p>1 OF 2</p> <p>5 NOV 97</p> |
|---|---------------------------------------------------------|

APPROVED PLAN  
11/18/97 by [Signature]  
SAN MARINO BUILDING DEPT.