
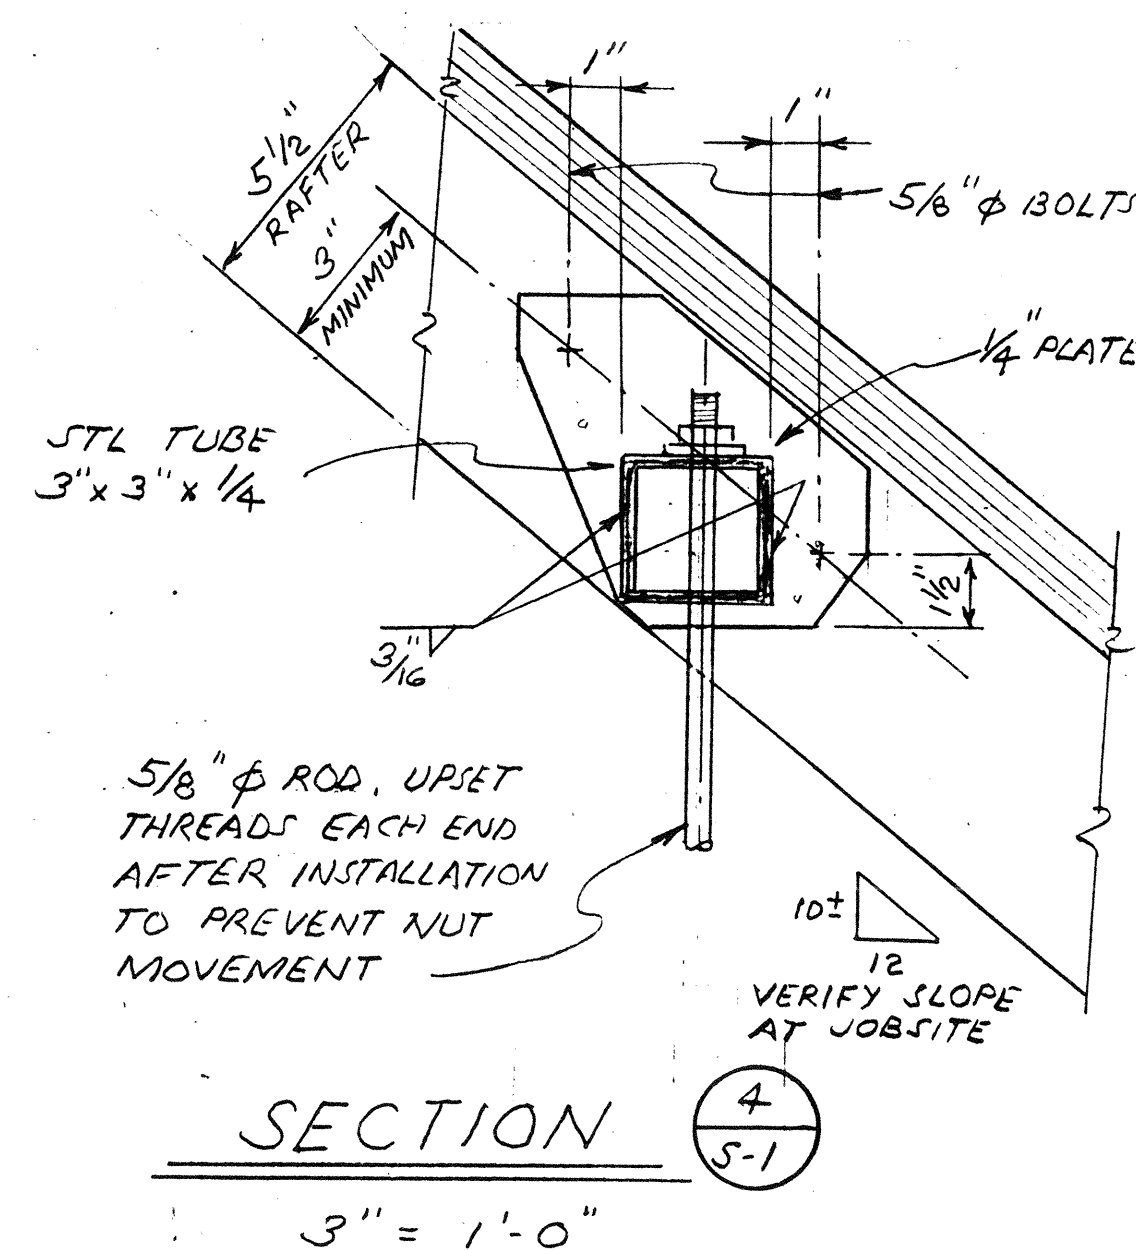
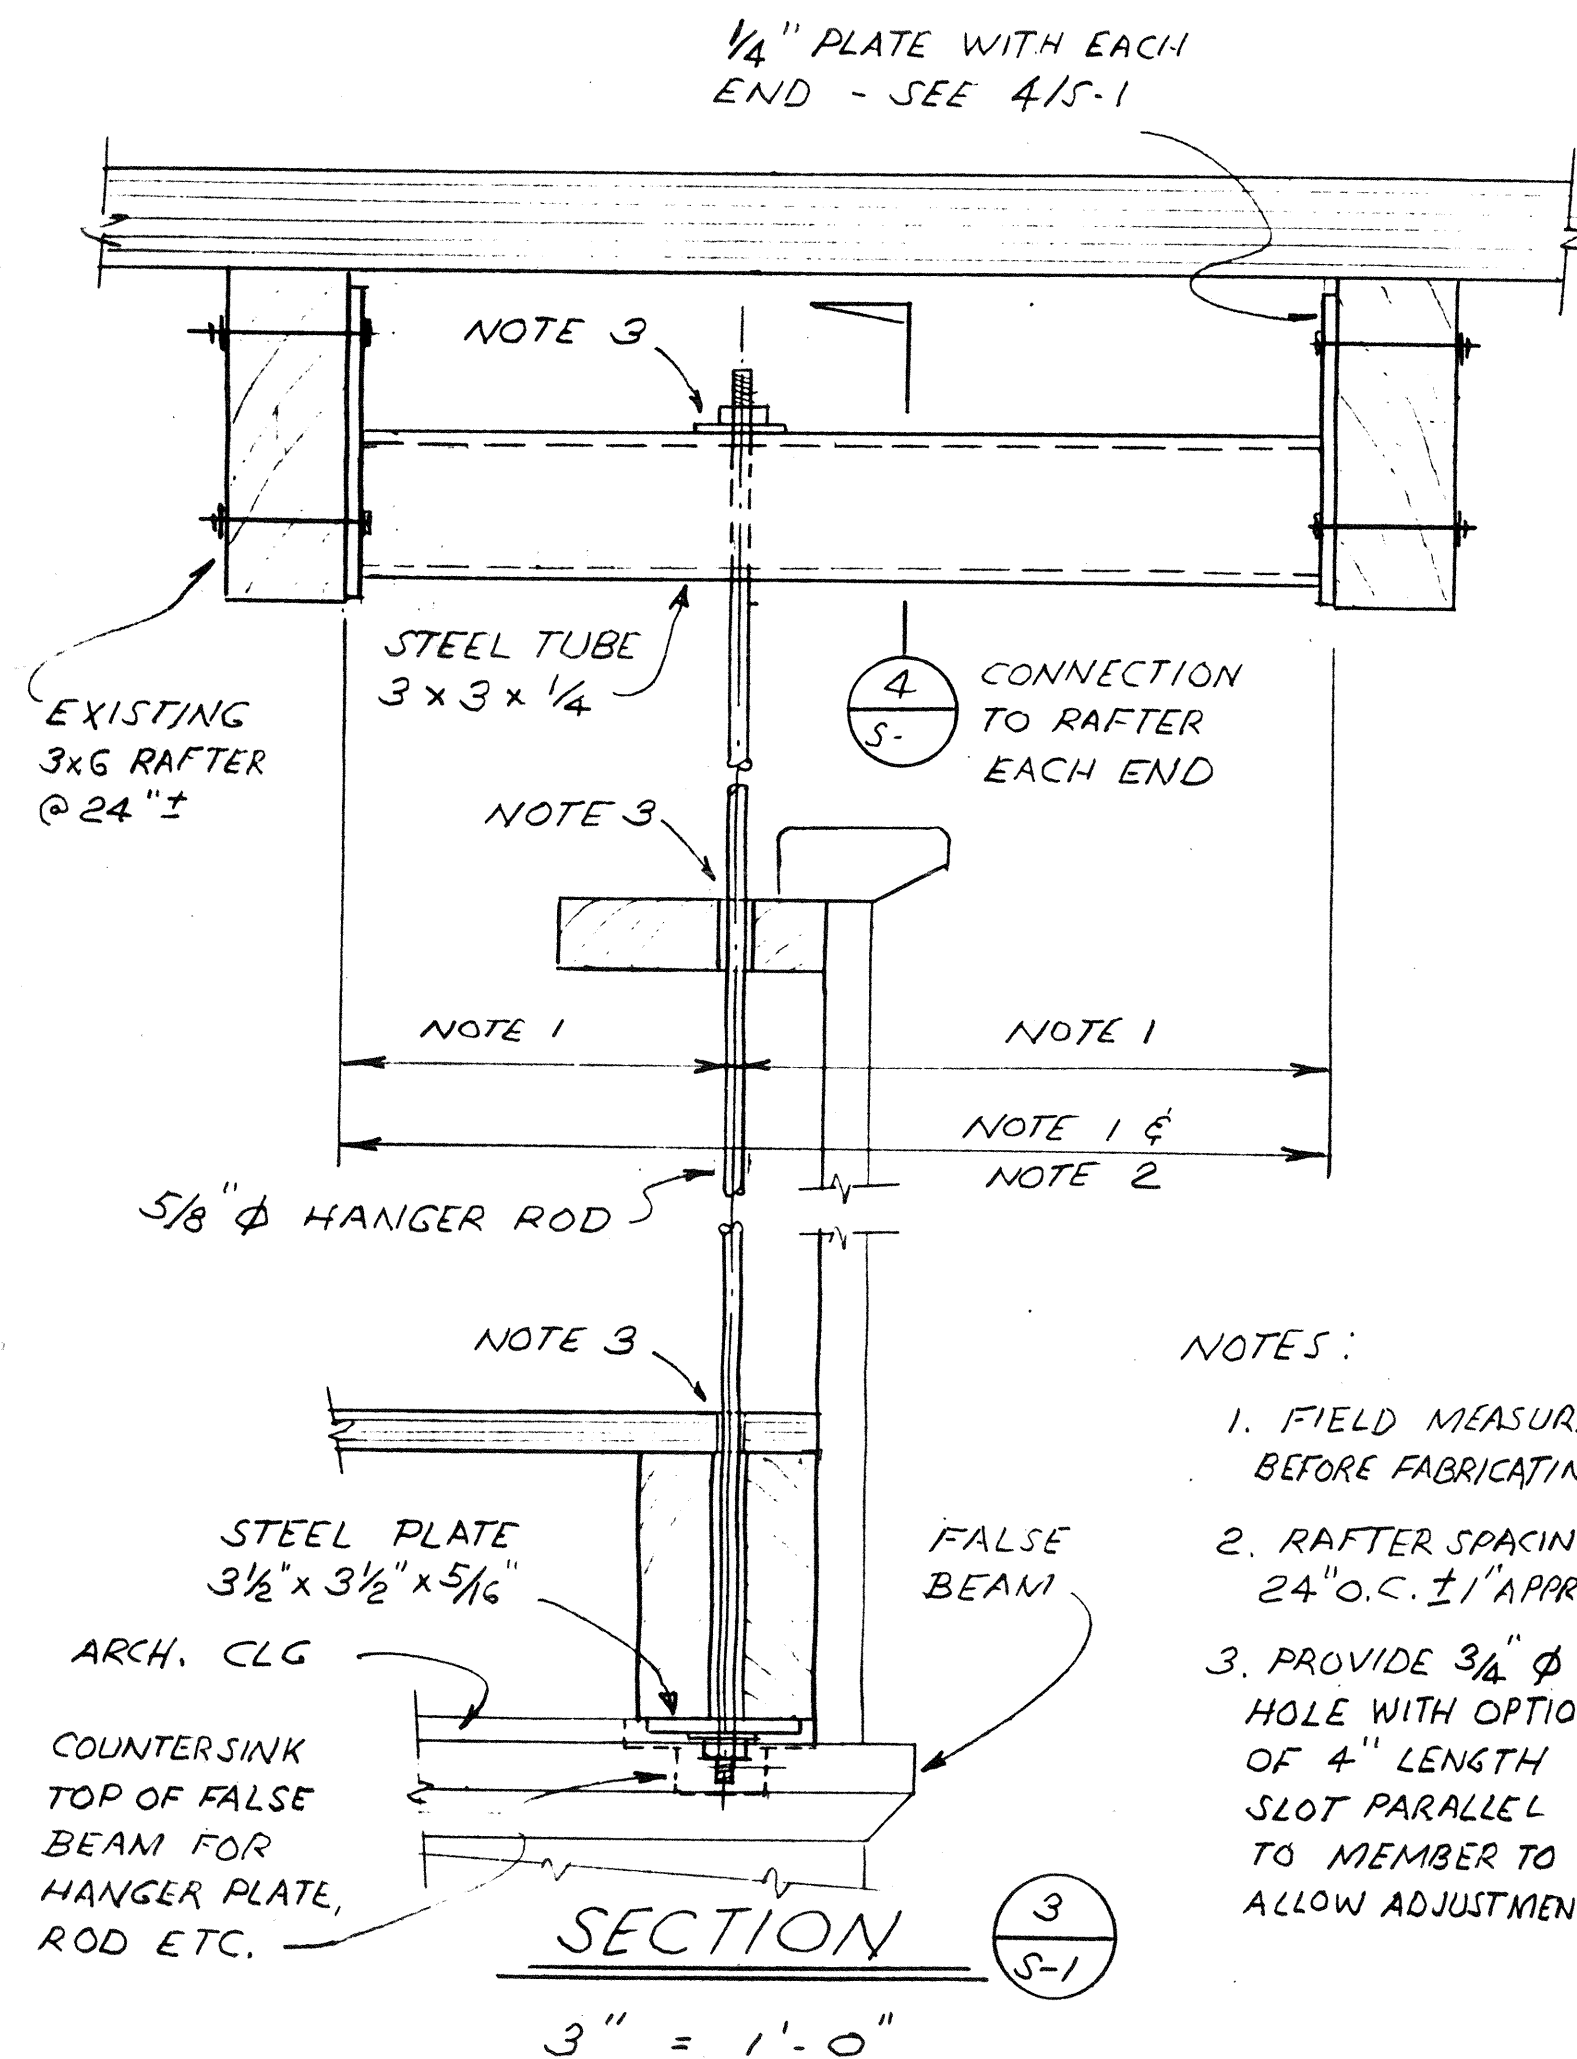
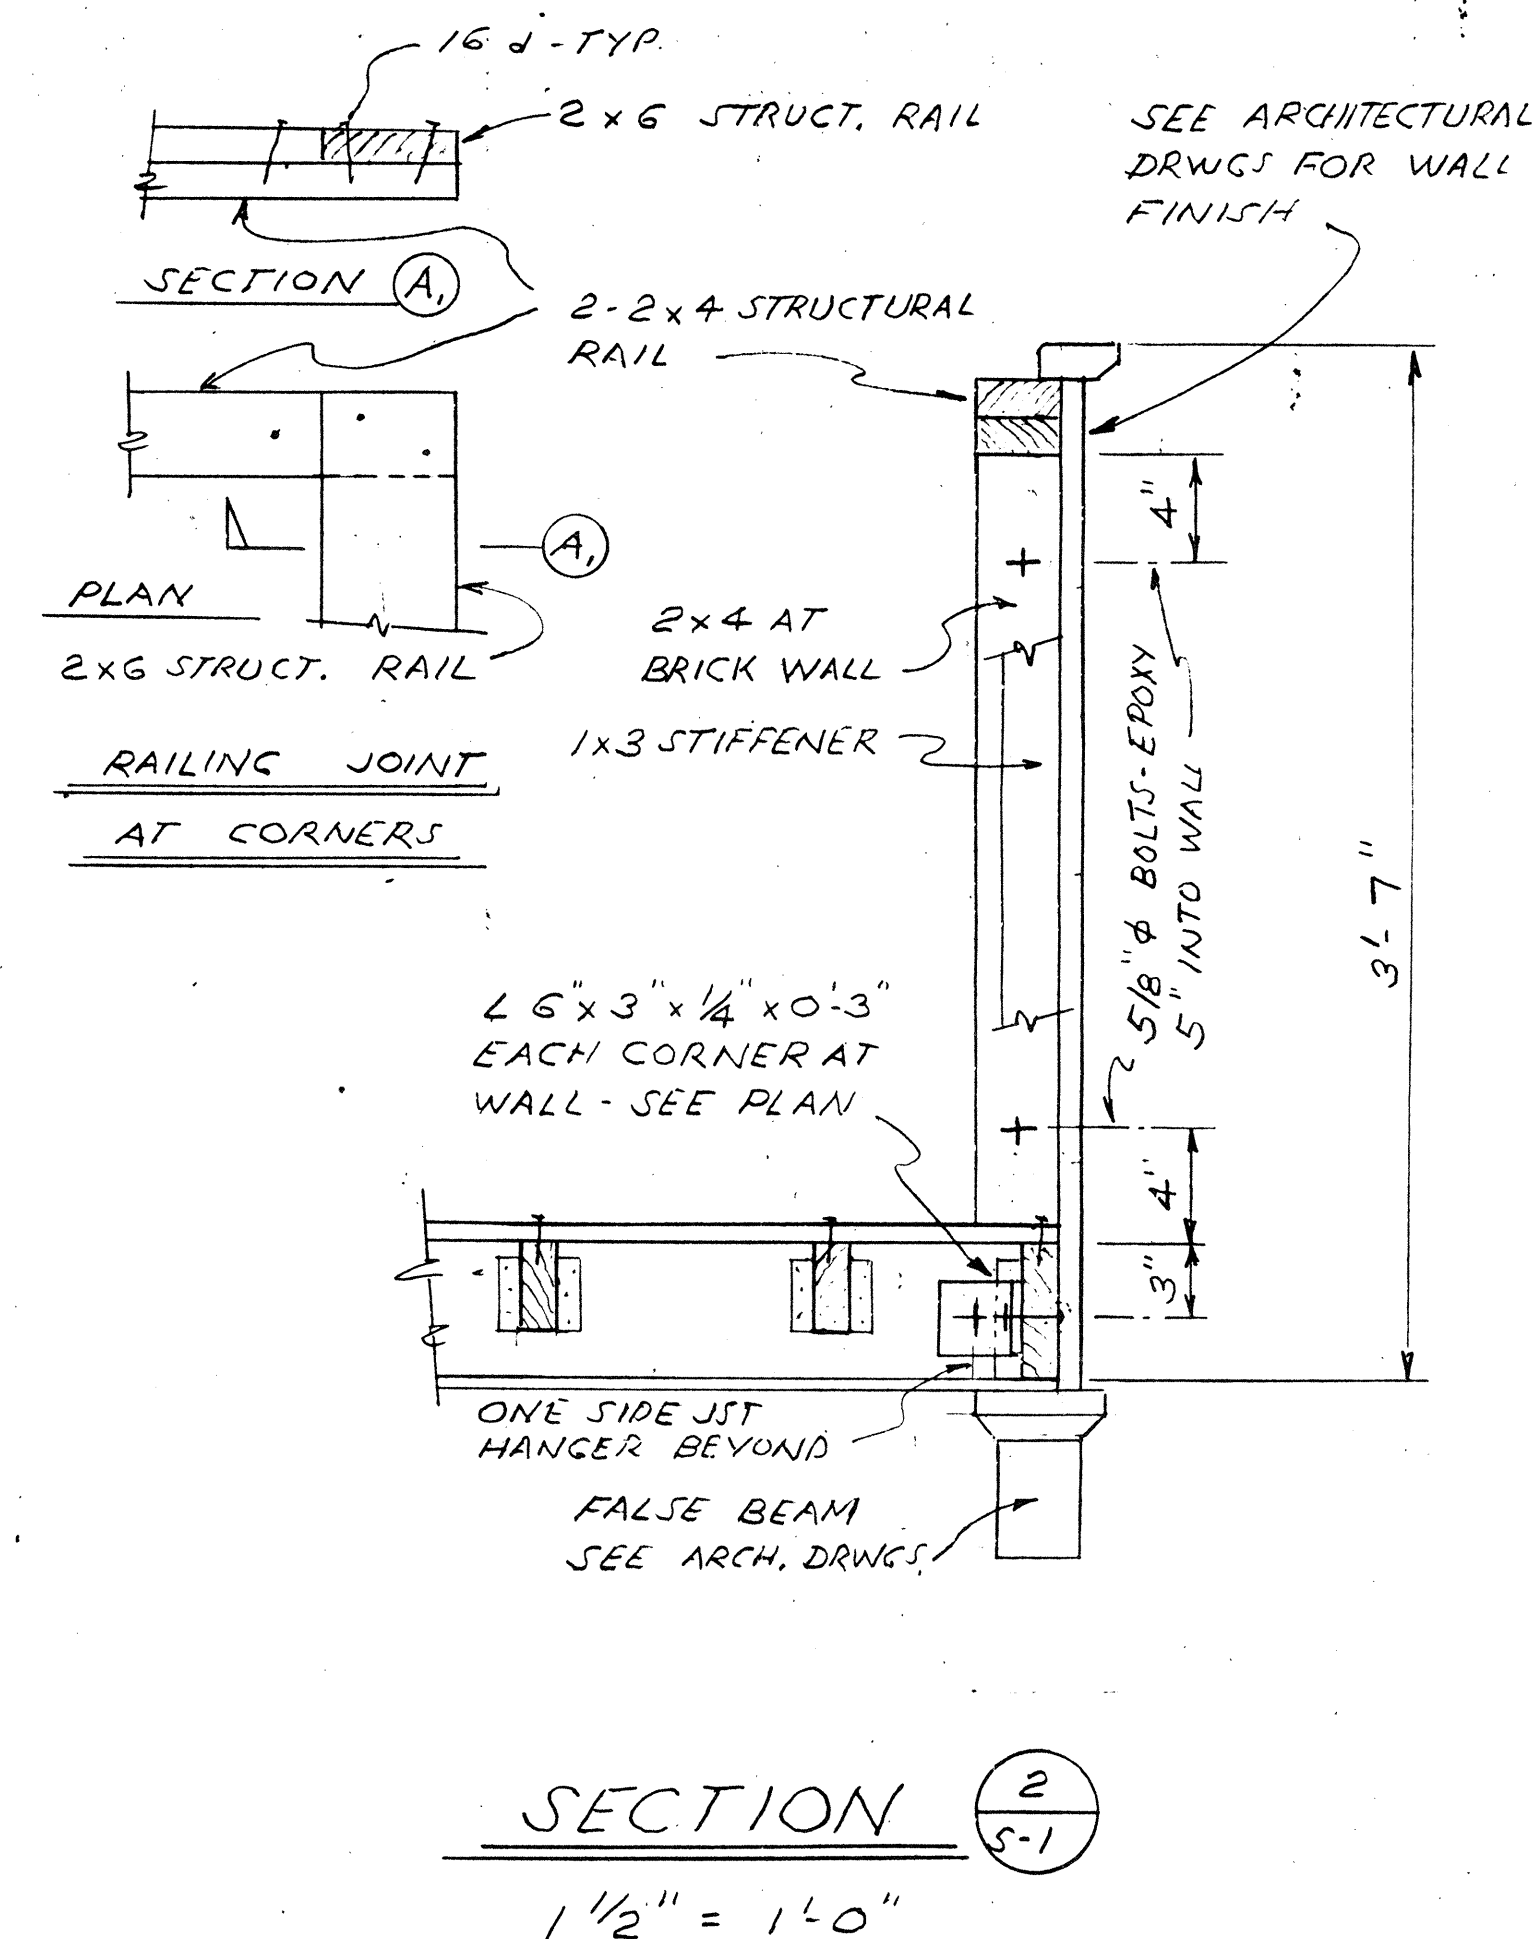
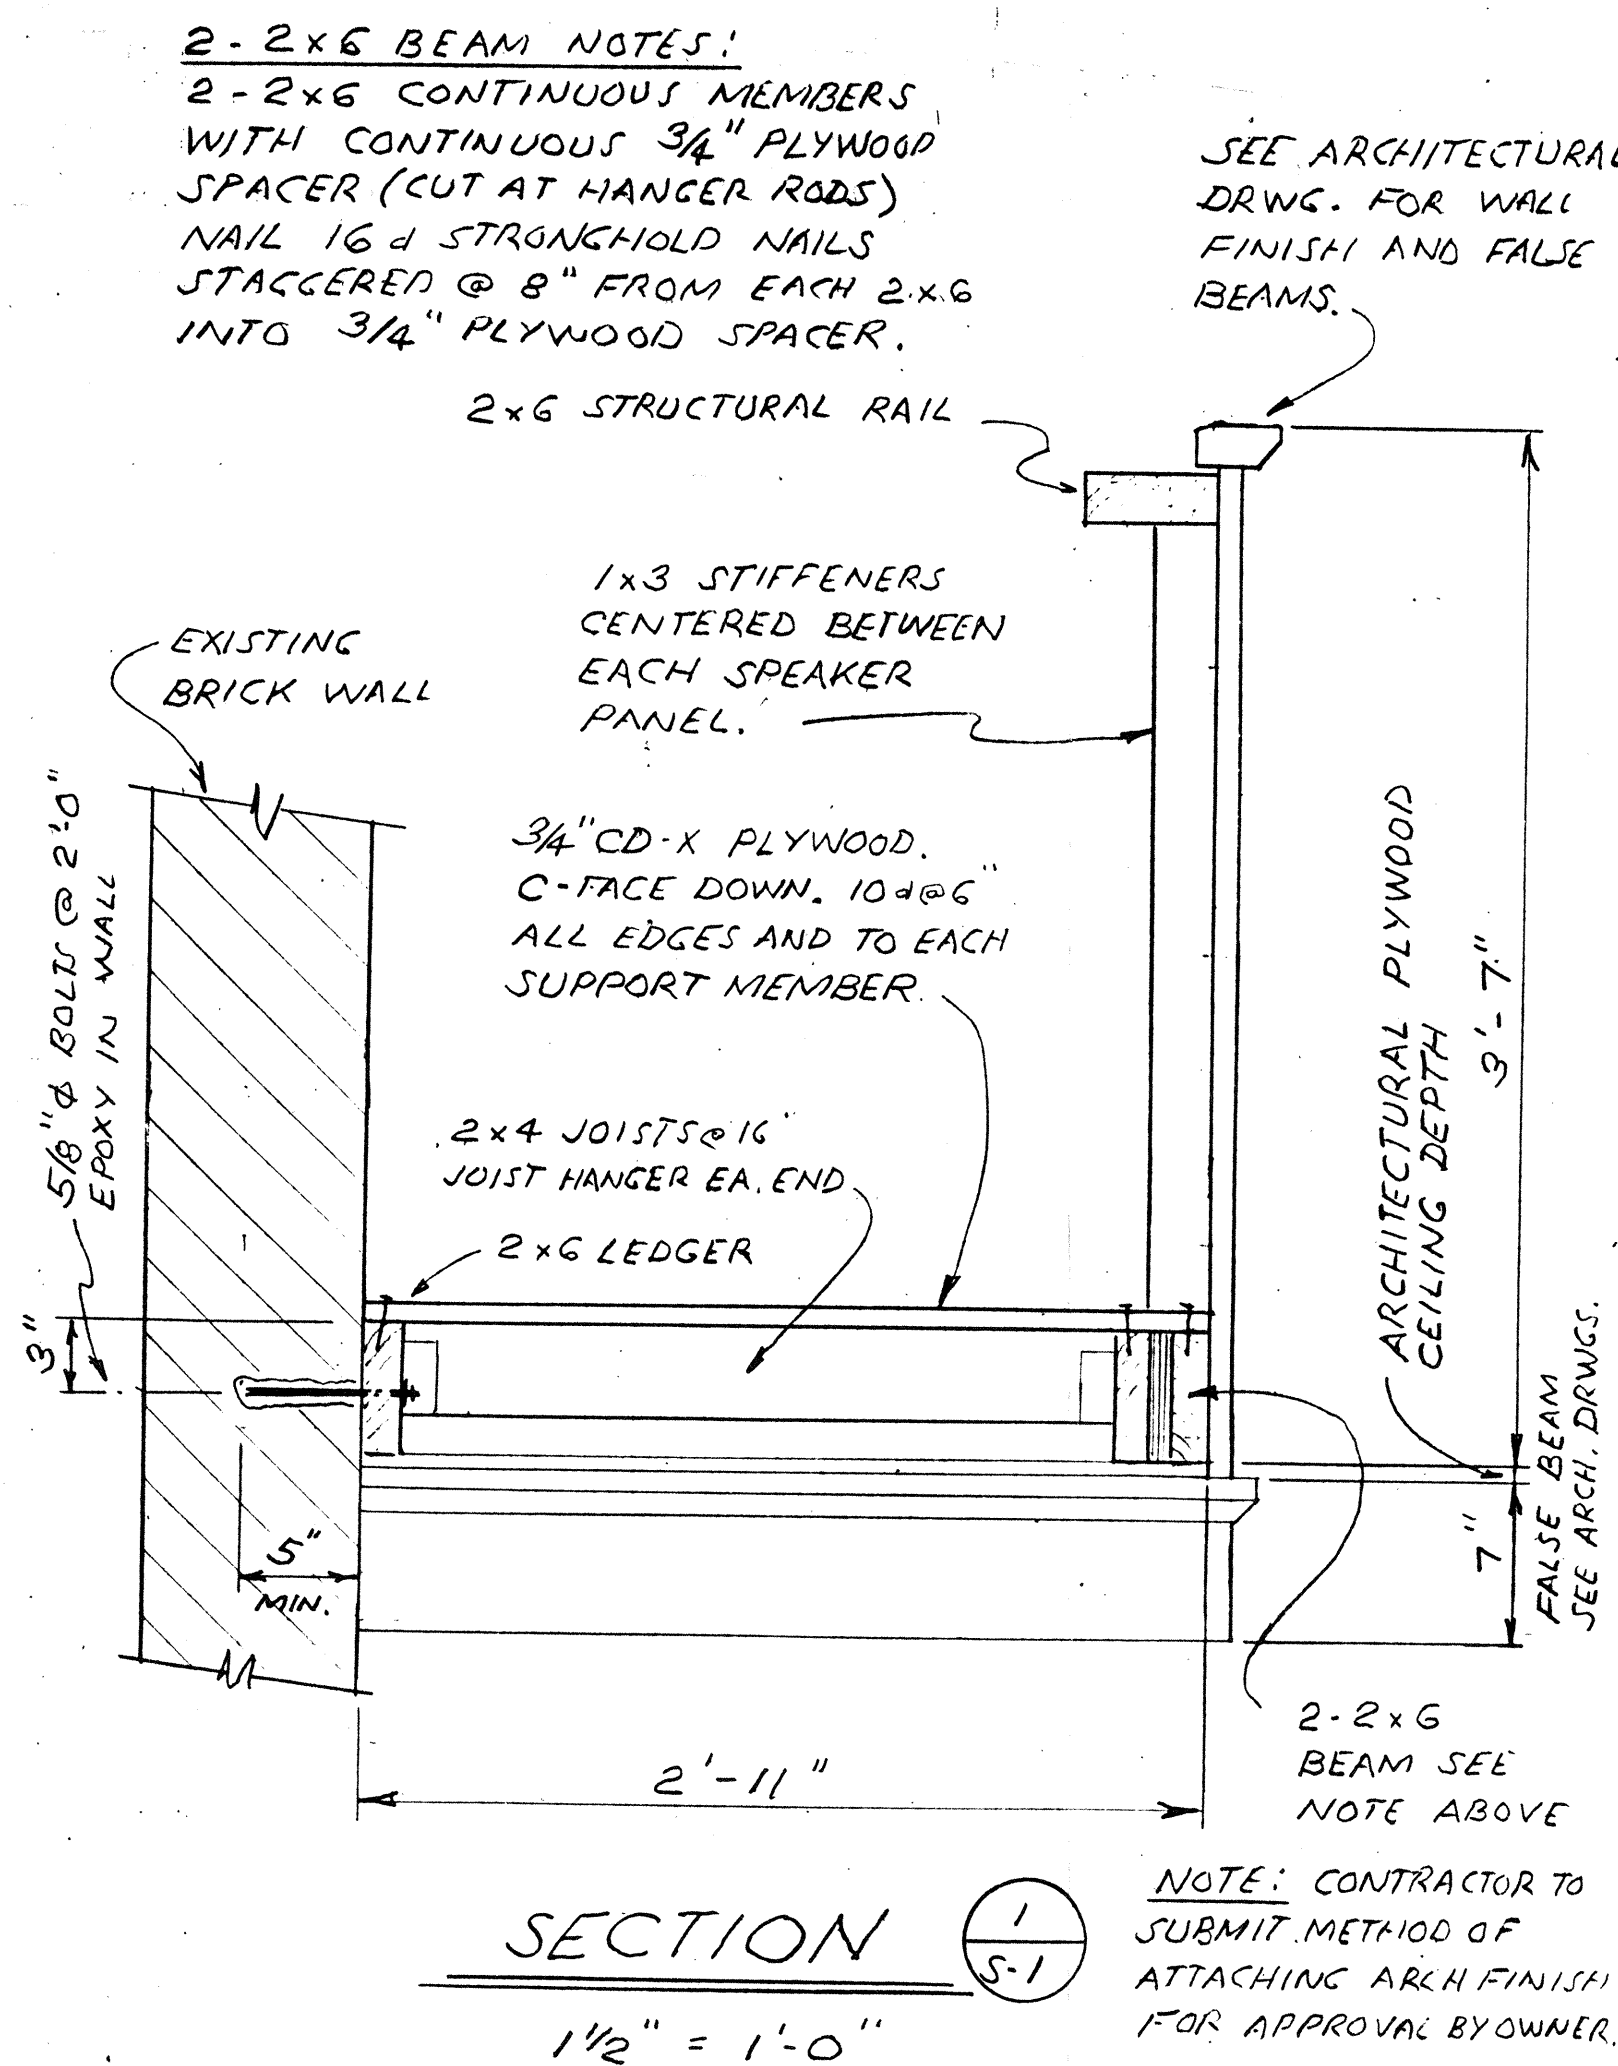


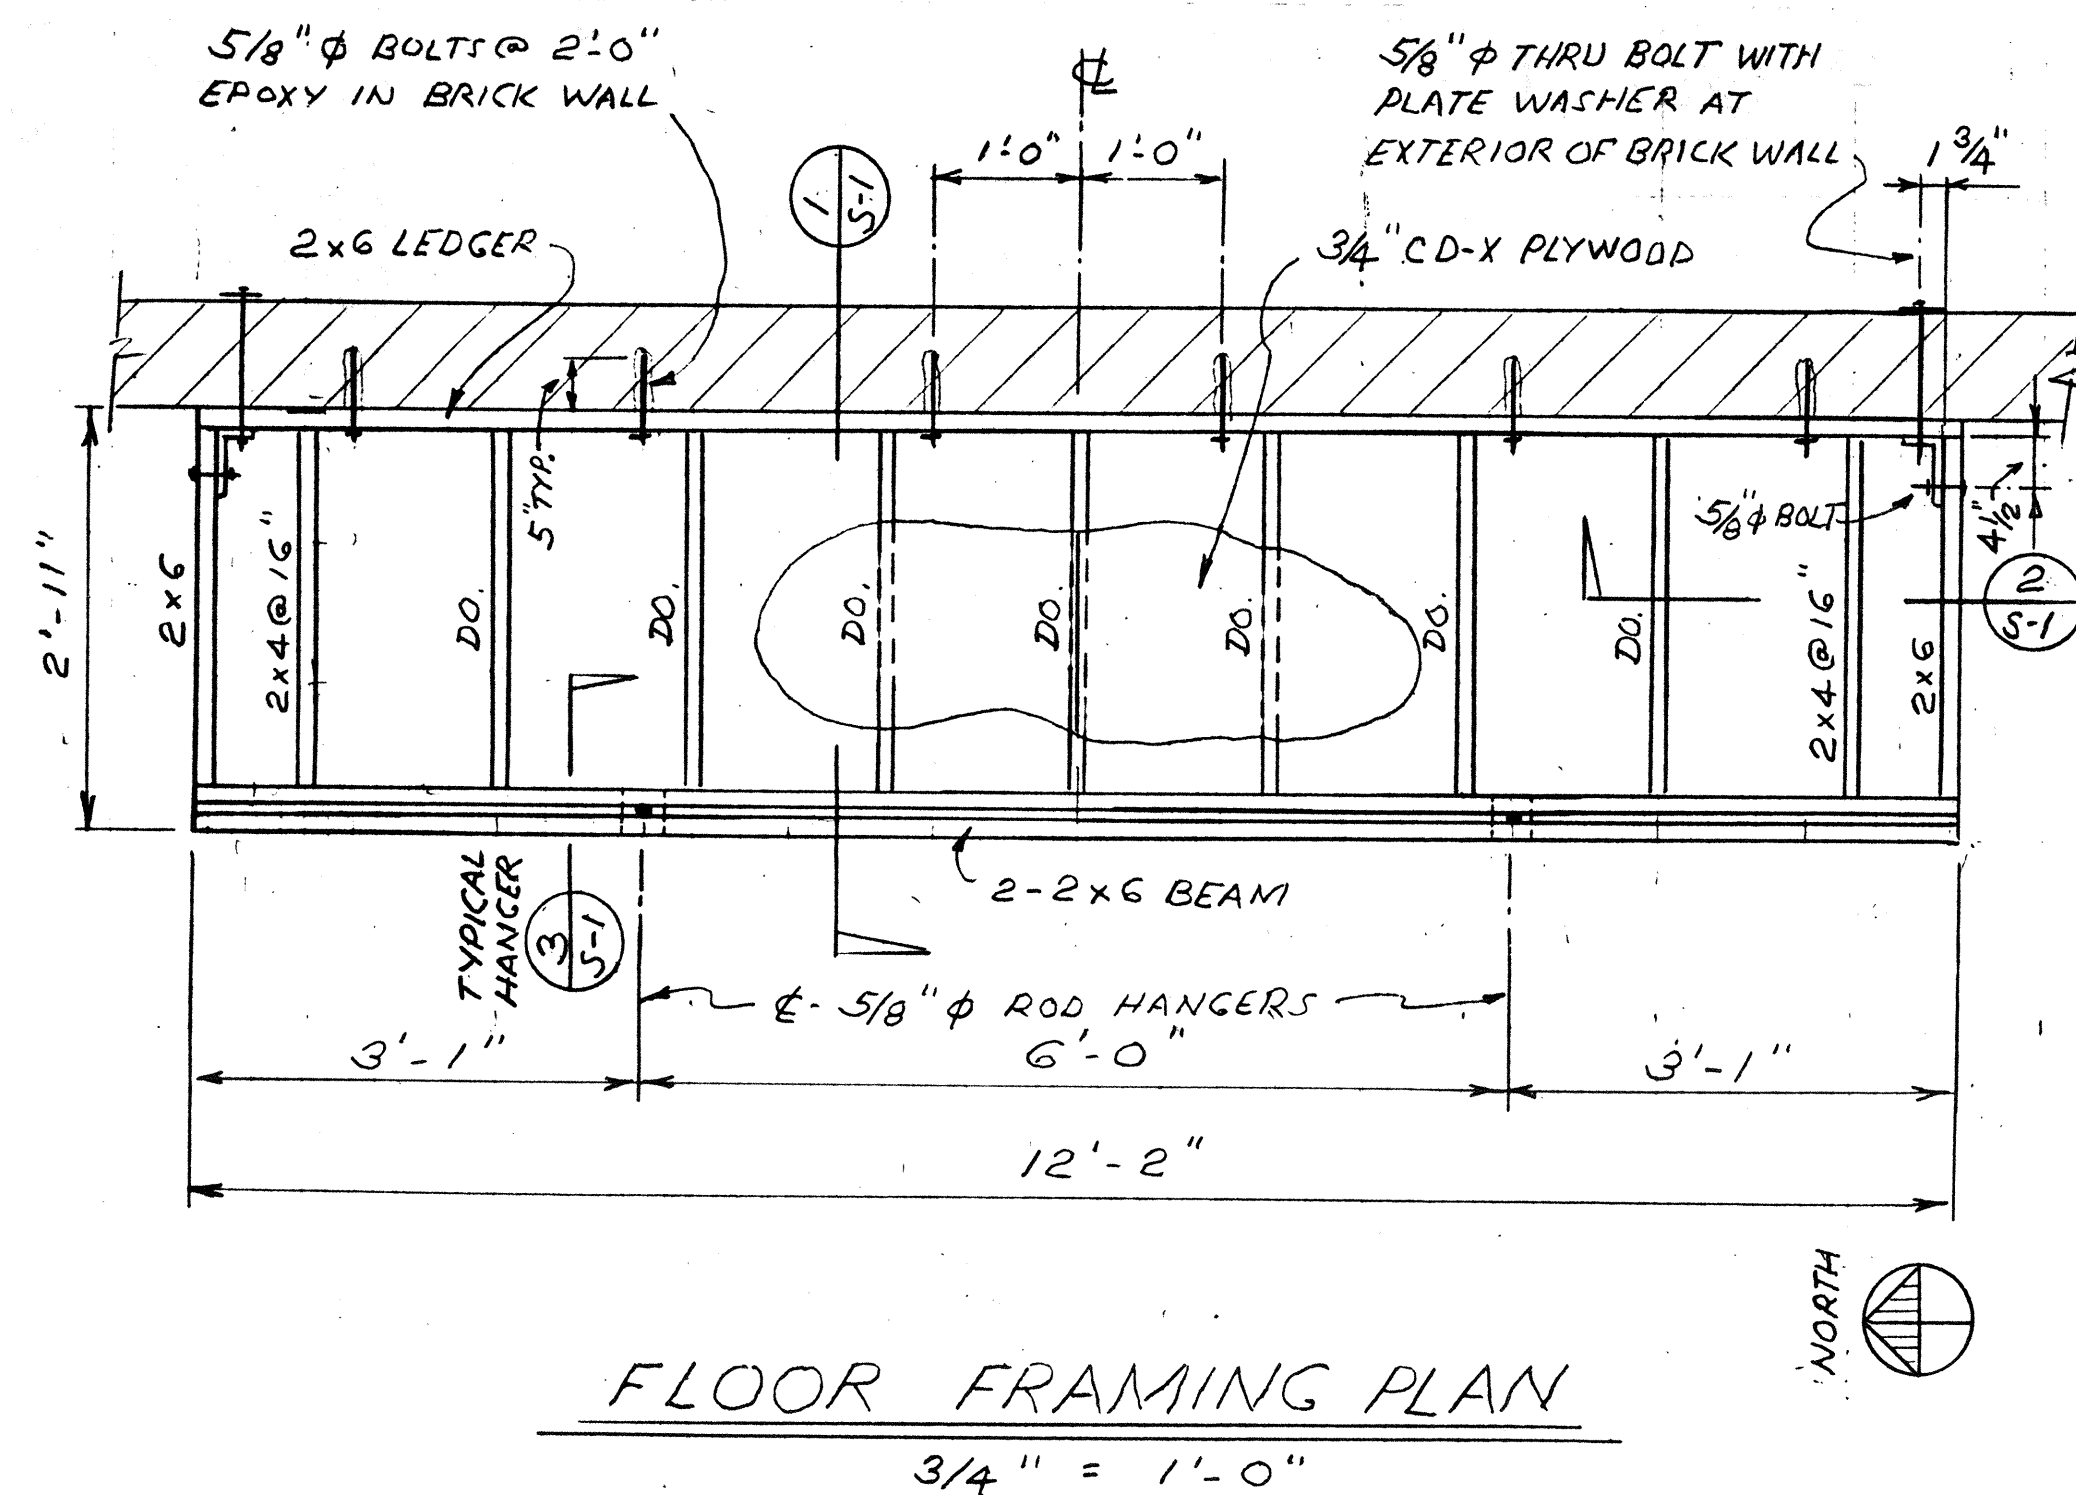

STRUCTURAL GENERAL NOTES:

MATERIALS:

STEEL:

PLATES TO BE A-36
RODS " " "
TUBES " " "
BOLTS " " A-307

WELDING:


- BY CERTIFIED WELDERS IN A SHOP
APPROVED BY A BUILDING DEPT.
- ELECTRODES TO BE E-70XX
HOLES TO BE DRILLED - NO BURNING
ALL BOLTS - WASHERS UNDER NUTS AND HEADS

WOOD

2x6 MEMBERS TO BE NO. 1 DOUGLAS FIR
2x4 " " " " "
3/4" PLYWOOD TO BE CDX
NAILS: - FULL LENGTH, BOX OR COMMON
- UBC NAILING SCHEDULE WHERE
NOT NOTED OTHERWISE.
- STRONGHOLD - WHERE NOTED

ALL WORK TO BE IN CONFORMANCE WITH
CITY OF SAN MARINO BUILDING CODE.

APPROVED PLAN
11/18/97
SAN MARINO BUILDING DEPT.

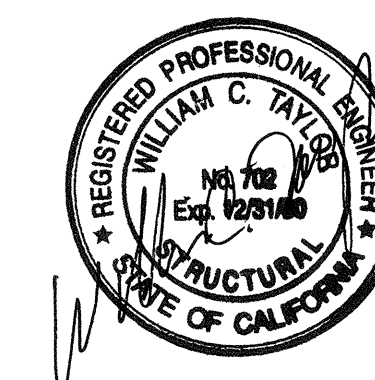

FALSE GALLERY
FOR CHAPEL AT
ST. EDMUND'S CHURCH
STRUCTURAL DETAILS

DRAWING
S-1
2 OF 2

5 NOV 97