

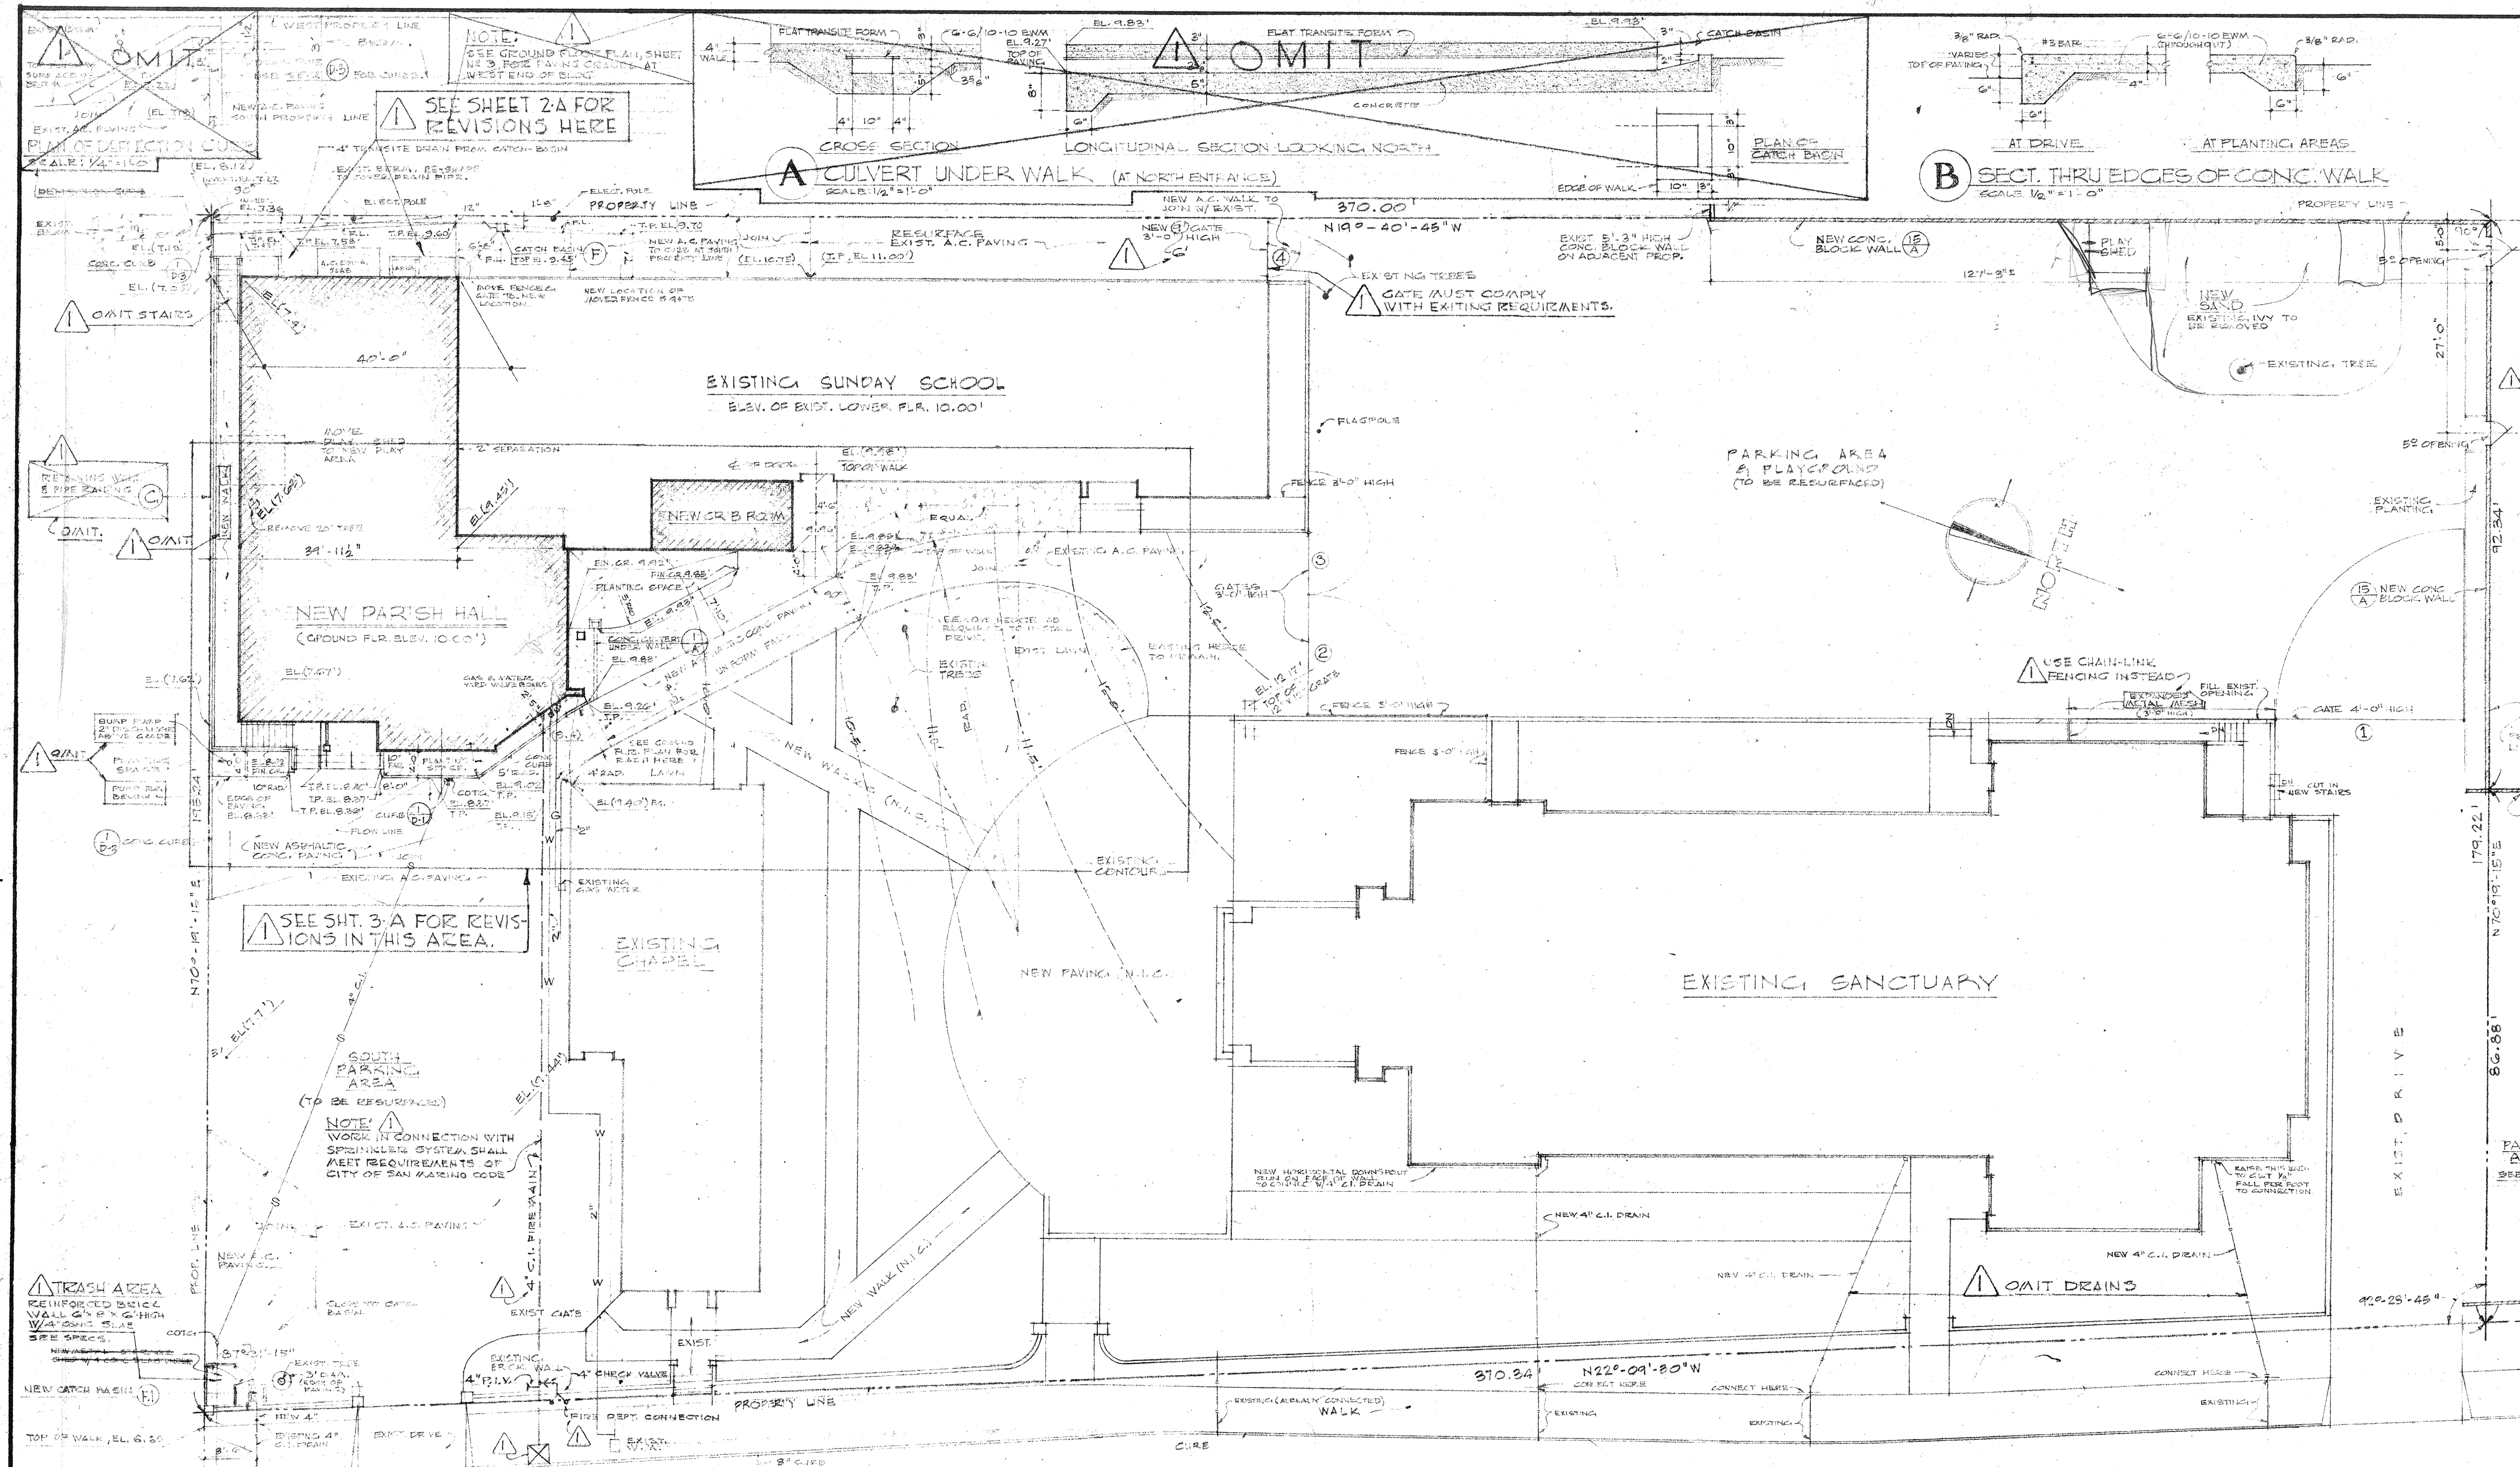


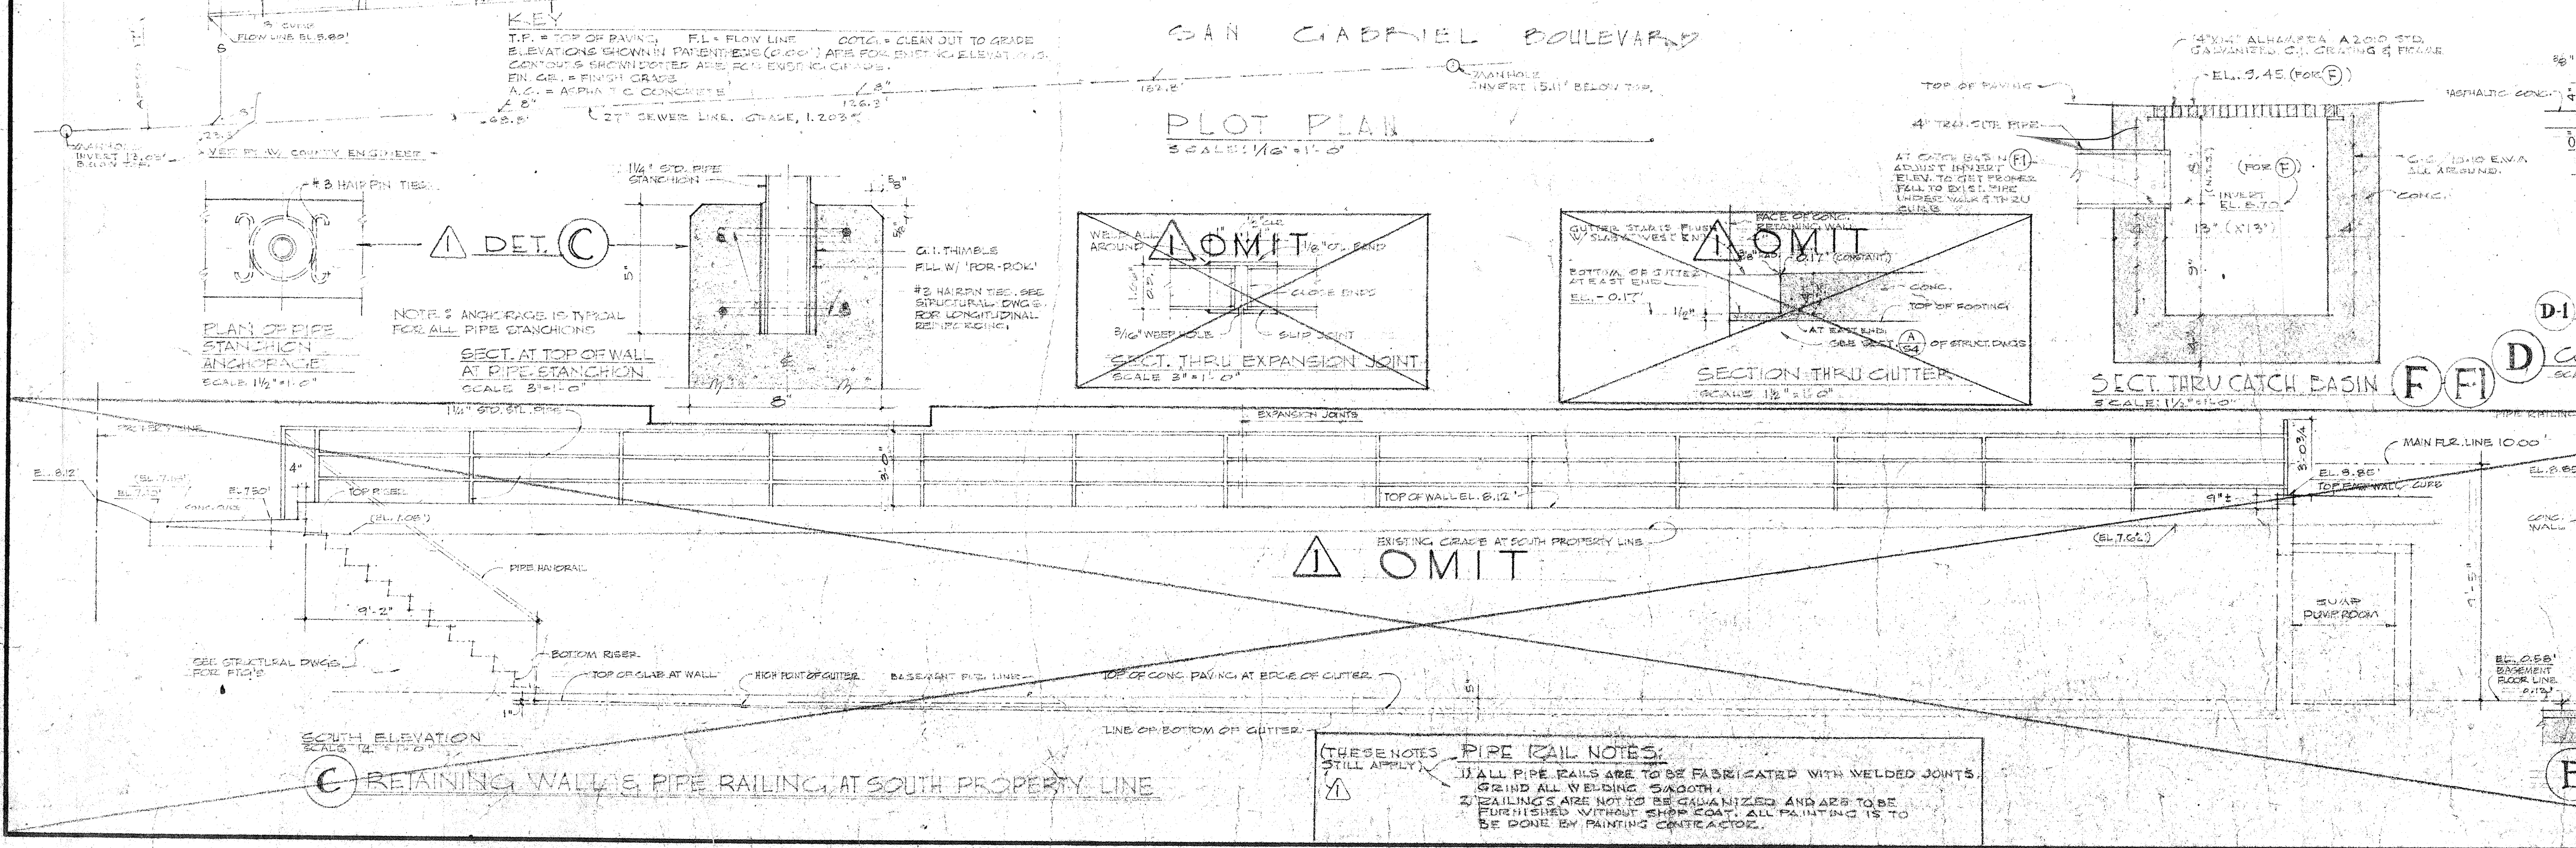

INDEX	
SHEET	TITLE
1	PLOT PLAN, INDEX, GENERAL NOTES & DETAILS
2	BASEMENT PLAN & INTERIOR FINISH SCHEDULE
3	GROUND FLOOR PLAN
4	ROOF PLAN
5	ELEVATIONS
6	ELEVATION & LONGITUDINAL SECTION
7	BUILDING SECTIONS
8	DOOR SCHEDULE & DETAILS
9	WINDOW SCHEDULE & DETAILS
10	INTERIORS & KITCHEN PLANS
11	BASEMENT SECTIONS & PLATFORM DETAILS
12	CASE DETAILS & INSULATION SCHEDULE
13	WALL SECTION & DETAILS
14	DETAILS
15	PARKING AREA & APPROPRIATIONS
16	PARKING PLAN
17	REVISIONS
18	SPRINKLER LAYOUT
19	REVISIONS
20	REVISIONS
21	REVISIONS
22	REVISIONS
23	REVISIONS
24	REVISIONS

- ### GENERAL NOTES
1. FINISHED GROUND FLOOR IS TO LINE WITH THAT OF EXISTING ADJOINING BUILDING. ELEV. OF FLOOR IS 10.00'
 2. BRICK: SIZE IS TO BE COMMON 1 1/2" HIGH X 3 3/4" WIDE X 8 1/4" LONG, MATCHING AS CLOSELY AS POSSIBLE THE COLOR & TEXTURE OF THE EXISTING ADJOINING CLERESTORY BUILDING. NOTE THAT EXTERIOR BRICK FOR CLOSING WINDOW OPENINGS IS TO BE THAT SALVAGED FROM BRICKWORK REMOVED.
 3. THE COURSEWORK OF THE CHURCH ROOM WALLS IS TO LINE WITH THAT OF THE ADJOINING WALLS OF THE EXISTING BUILDING. THE HEIGHT OF THE COURSEWORK FOR ALL OTHER BRICKWORK IS TO BE 8" (1/2" JOINT).
 4. UNLESS OTHERWISE NOTED, ALL STUP WALLS ARE TO BE FRAMED WITH 2" X 4" AT 16" O.C.
 5. DAMPPROOFING: EXCEPT AT THE OUTSIDE WALLS OF THE CHURCH ROOM AT NORTH SIDE, DAMPPROOF THE EXTERIOR WALLS, BELOW GRADE, OF ALL EXTERIOR WALLS RETAINING BATH, INCLUDING THE EXTERIOR WALLS OF THE NORTH WALL OF THE CHURCH ROOM. ALSO DAMPPROOF THE INTERIOR FACE OF THE BATH WALLS. BEHIND THE PANELING AT THE WEST WALL OF THE CHURCH ROOM.
 6. THERMAL INSULATION: INSTALL THE THERMAL INSULATION SPECIFIED IN THE FOLLOWING LOCATIONS:
 - a. BETWEEN THE CEILING BATTERS OF THE CHURCH ROOM, AT THE NORTH END OF THE CHURCH ROOM AND BETWEEN STUDS AT THE EAST SIDE OF THE CHURCH ROOM OVER PLATFORM.
 - b. BETWEEN THE CEILING BATTERS OF THE CHURCH ROOM, EXCEPT OVER BATH PLATFORM AT EAST ENTRANCE.
 - c. BETWEEN JOINTS OF RUSSED CEILING OVER CLOSET 104 AND CHAIRWAY, ALSO BETWEEN STUDS AT NORTH WALL OF CLOSET 104 AT EAST END OF CHURCH ROOM.
 - d. BETWEEN CEILING JOINTS & BETWEEN STUDS AT TOP OF EACH PARISH HALL DOORWAY AND ON TOP OF THE SHEATHING IN THE SPACES BETWEEN DOORWAY WINDOWS & AT THE END SPACES.
 - e. ON TOP OF THE SHEATHING UNDER THE BUILD-UP ROOF OF SADDLE AT THE NORTH SIDE OF PARISH HALL.
 - f. BETWEEN CEILING JOINTS OVER CR. B. ROOM AND OVER NEW RUSSED CEILING ABOVE EXIST. PORCH.
 7. ALL GYP. BOARD CALLED FOR ON THE DRAWING IS TO BE TYPE APPROVED FOR 1 HR. FIRE PROTECTION.
 8. ALL CONC. WALLS ARE TO BE 4" THICK, REINFORCED WITH #4 @ 10" O.C. E.W.M. THROUGHOUT.
 9. MEASUREMENTS ON CONCRETE STEPS ARE TAKEN FROM THE FACE OF THE CURBS AT TOP.
 10. ALL EXPOSED CONCRETE IS TO BE FORMED WITH PLYWOOD OR WITH TEMPLATES HAVING EXPOSED FORM LINING.
 11. HARDWOOD: HARDWOOD & HARDWOOD PLYWOOD AT PLATFORM IN PARISH HALL SHALL BE IN SELECT RED OAK.
 12. ROOM CAPACITY SIGN: A PERMANENT ROOM CAPACITY SIGN SHALL BE LOCATED IN EACH CHURCH PLACE NEAR MAIN ENTRANCE OF PARISH HALL IN ACCORDANCE WITH BUILDING CODE SECTION 3301.
 13. LAY ONE LAYER OF BUILDING PAPER UNDER ALL MASONRY FLOORING BETWEEN 1" LAYERS OF PLYWOOD FOR FLOOR.
 14. WHERE EXISTING PAVING IS REMOVED FOR PIPE TRENCHES, REPLACE IT WITH NEW ASPHALTIC CONCRETE.
 15. REMOVE EXISTING PAVING IN AREAS TO BE COVERED BY NEW WALKS OR PAVING.
 16. STUDS ARE TO BE 2" X 4" @ 16" O.C. EXCEPT WHERE NOTED OTHERWISE.
 17. ALL LATHING, PLASTERING AND ALL SUSPENDED CEILING OF PARISH HALL & CHURCH ARE TO CONFORM TO CHAPTER 47 OF THE UNIFORM BUILDING CODE, ALL TO GIVE ONE-HOUR FIRE PROTECTION.
 18. EXCEPT IN PORTION OF STAIRCASE ROOM 103A AND HALL 103, WEST OF THE 2" SEPARATION, WHERE 1" MEAT WOOD FIBER PLASTER ON METAL LATH IS CALLED FOR.

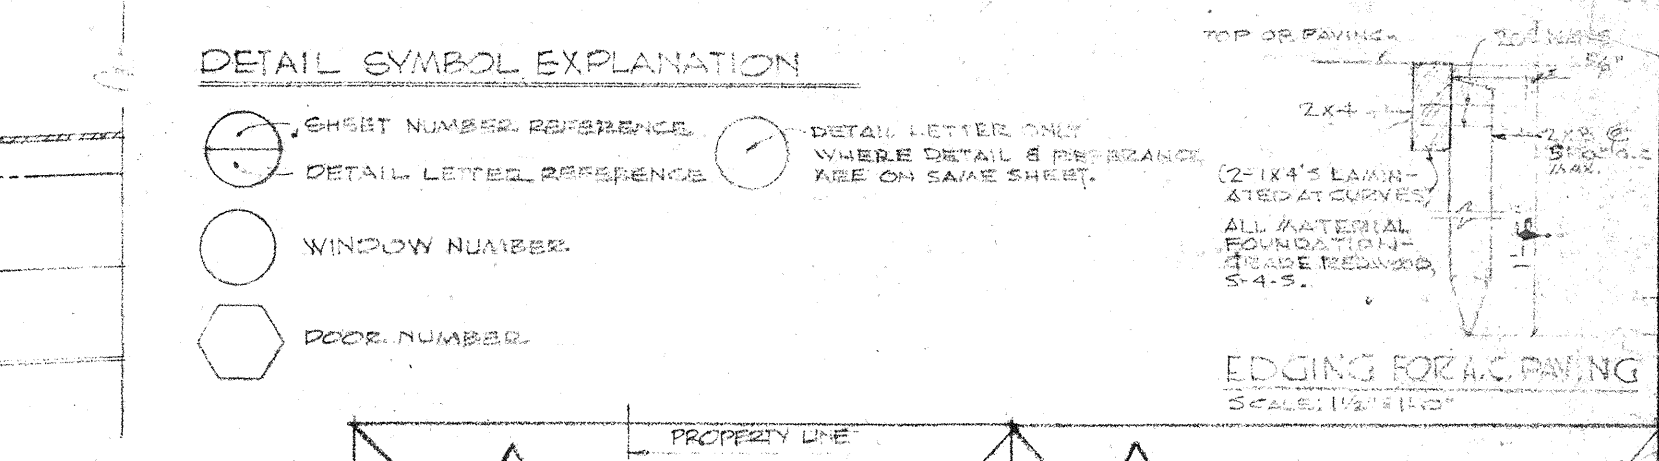

LEGAL DESCRIPTION:

TRACT NO. 8828 LOT 10, S. 22° 30' 30" E. 145.77 FT. FROM S.E. TERMINUS OF A CURVE CONCAVE TO SW AT INTERSECTION OF S.E. LINE OF CHANNELED CREEK DR. W. S.W. LINE OF SAN GABRIEL BLVD. WITH A RADIUS OF 167' AND A LENGTH OF 122.11 FT. THENCE ON S.D. S.W. LINE 370.34 FT. TH. S. 10° 15' 15" W. 105.24 FT. N. 10° 45' 45" W. 370 FT. TH. NORTH 70° 15' 15" E. 179.22 FT. TO BEG. PART OF LOT 2.

PLOT PLAN, INDEX & GENERAL NOTES

REVISIONS	PARISH HALL ADDITION
1	ST. EDWARD'S EPISCOPAL CHURCH
2	1175 SAN GABRIEL BLVD., SAN MARINO, CALIFORNIA
3	DRAWN BY: B.F.F.
4	TRACED BY: C.B.F.
5	DATE: 12-30-65

BREO FREEMAN ARCHITECT

45 SOUTH MARENGO
PASADENA 1, CALIFORNIA

JOB NO. 927
SHEET NO. 1