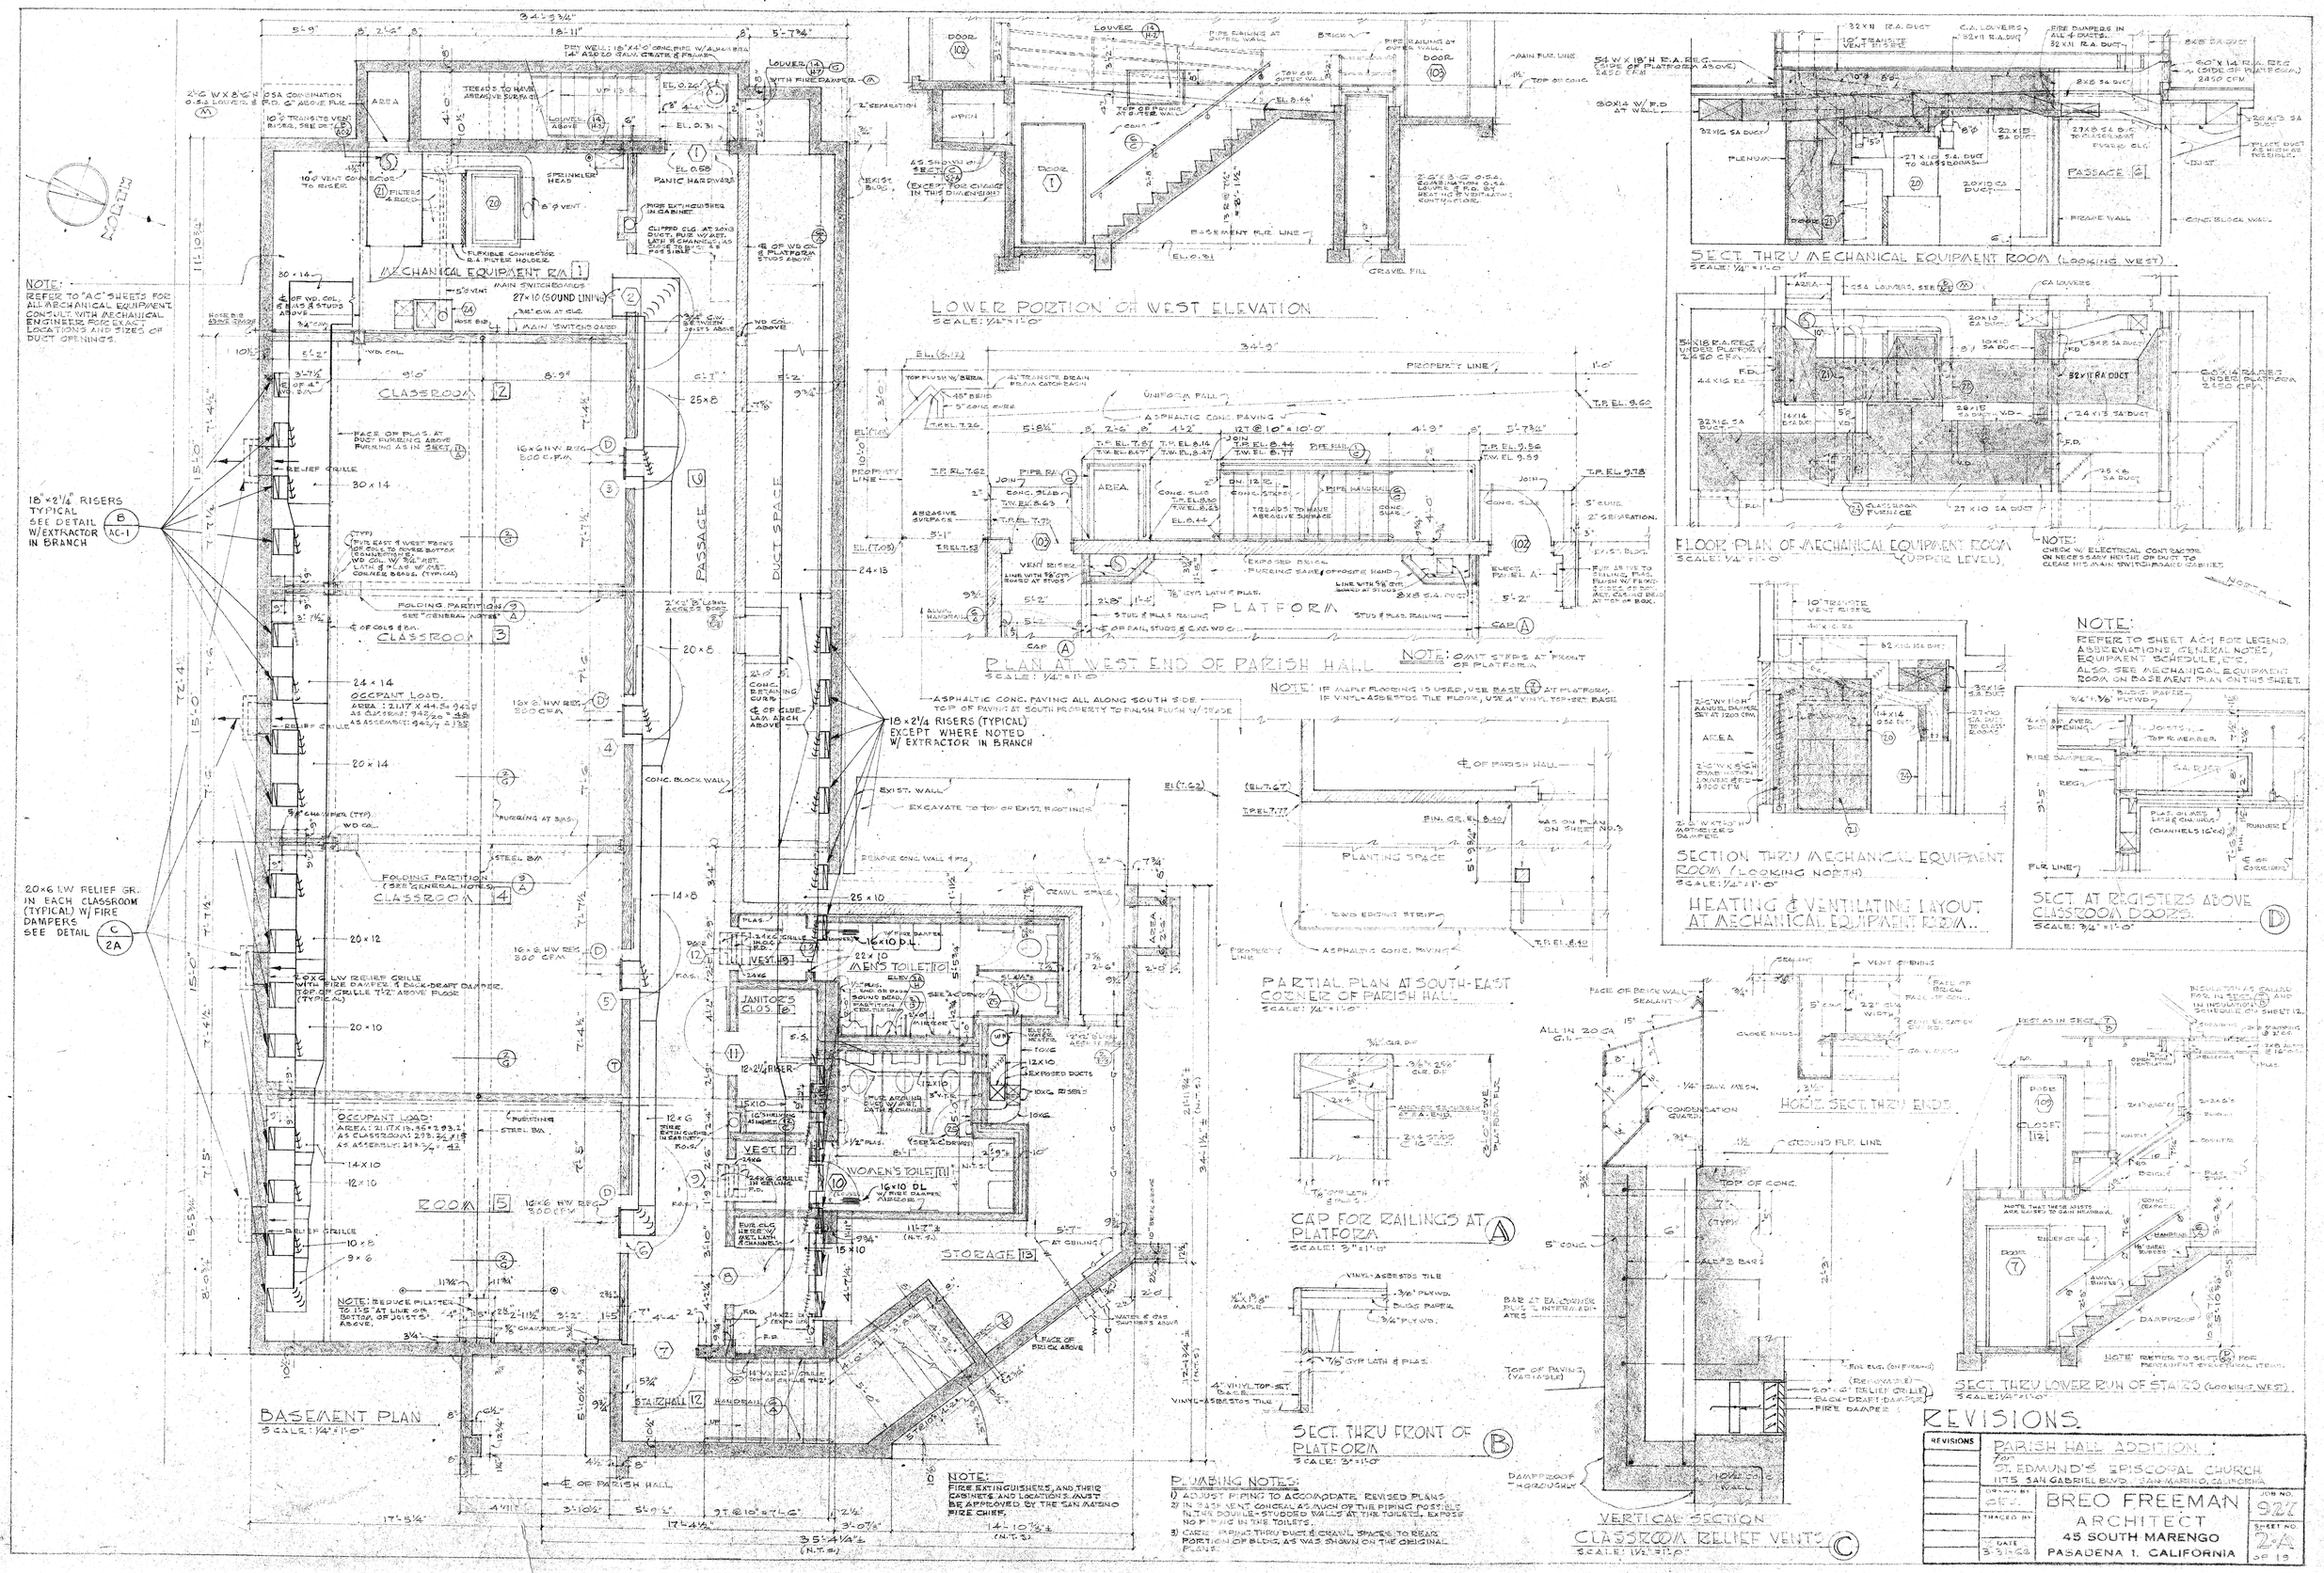

NOTE: REFER TO "AC" SHEETS FOR ALL MECHANICAL EQUIPMENT. CONSULT WITH MECHANICAL ENGINEER FOR EXACT LOCATIONS AND SIZES OF DUCT OPENINGS.
MECHANICAL EQUIPMENT RM 1
CLASSROOM 2
CLASSROOM 3
CLASSROOM 4
ROOM 5
PASSAGE 6
DUCT SPACE
18"x2¼" RISERS TYPICAL SEE DETAIL B/AC-1 W/EXTRACTOR IN BRANCH
20x6 LW RELIEF GR. IN EACH CLASSROOM (TYPICAL) W/ FIRE DAMPERS SEE DETAIL C/2A
18x2¼ RISERS (TYPICAL) EXCEPT WHERE NOTED W/ EXTRACTOR IN BRANCH
MEN'S TOILET 10
WOMEN'S TOILET 11
JANITOR'S CLOS. 8
STORAGE 13
STAIRHALL 12
BASEMENT PLAN
SCALE: ¼"=1'-0"
LOWER PORTION OF WEST ELEVATION
SCALE: ¼"=1'-0"
PLAN AT WEST END OF PARISH HALL
SCALE: ¼"=1'-0"
PLATFORM
NOTE: OMIT STEPS AT FRONT OF PLATFORM
NOTE: IF MAPLE FLOORING IS USED, USE BASE AT PLATFORM. IF VINYL-ASBESTOS TILE FLOOR, USE 4" VINYL TOP-SET BASE
PARTIAL PLAN AT SOUTH-EAST CORNER OF PARISH HALL
SCALE: ¼"=1'-0"
CAP FOR RAILINGS AT PLATFORM
SCALE: 3"=1'-0"
SECT. THRU FRONT OF PLATFORM
SCALE: 3"=1'-0"
SECT. THRU MECHANICAL EQUIPMENT ROOM (LOOKING WEST)
SCALE: ¼"=1'-0"
FLOOR PLAN OF MECHANICAL EQUIPMENT ROOM (UPPER LEVEL)
SCALE: ¼"=1'-0"
NOTE: CHECK W/ ELECTRICAL CONTRACTOR ON NECESSARY HEIGHT OF DUCT TO CLEAR HIS MAIN SWITCHBOARD CABINET.
NOTE: REFER TO SHEET AC-1 FOR LEGEND, ABBREVIATIONS, GENERAL NOTES, EQUIPMENT SCHEDULE, ETC. ALSO SEE MECHANICAL EQUIPMENT ROOM ON BASEMENT PLAN ON THIS SHEET.
SECTION THRU MECHANICAL EQUIPMENT ROOM (LOOKING NORTH)
SCALE: ¼"=1'-0"
HEATING & VENTILATING LAYOUT AT MECHANICAL EQUIPMENT ROOM
SECT. AT REGISTERS ABOVE CLASSROOM DOORS
SCALE: ¾"=1'-0"
HORIZ. SECT. THRU ENDS
VERTICAL SECTION CLASSROOM RELIEF VENTS
SCALE: 1½"=1'-0"
SECT. THRU LOWER RUN OF STAIRS (LOOKING WEST)
SCALE: ¼"=1'-0"
NOTE: FIRE EXTINGUISHERS, AND THEIR CABINETS AND LOCATIONS MUST BE APPROVED BY THE SAN MARINO FIRE CHIEF.
PLUMBING NOTES:
1) ADJUST PIPING TO ACCOMODATE REVISED PLANS.
2) IN BASEMENT CONCEAL AS MUCH OF THE PIPING POSSIBLE IN THE DOUBLE-STUDDED WALLS AT THE TOILETS. EXPOSE NO PIPING IN THE TOILETS.
3) CARRY PIPING THRU DUCT & CRAWL SPACES TO REAR PORTION OF BLDG. AS WAS SHOWN ON THE ORIGINAL PLANS.
REVISIONS
PARISH HALL ADDITION
for ST. EDMUND'S EPISCOPAL CHURCH
1175 SAN GABRIEL BLVD. SAN MARINO, CALIFORNIA
BREO FREEMAN ARCHITECT
45 SOUTH MARENGO
PASADENA 1, CALIFORNIA
JOB NO. 927
SHEET NO. 2A OF 19