


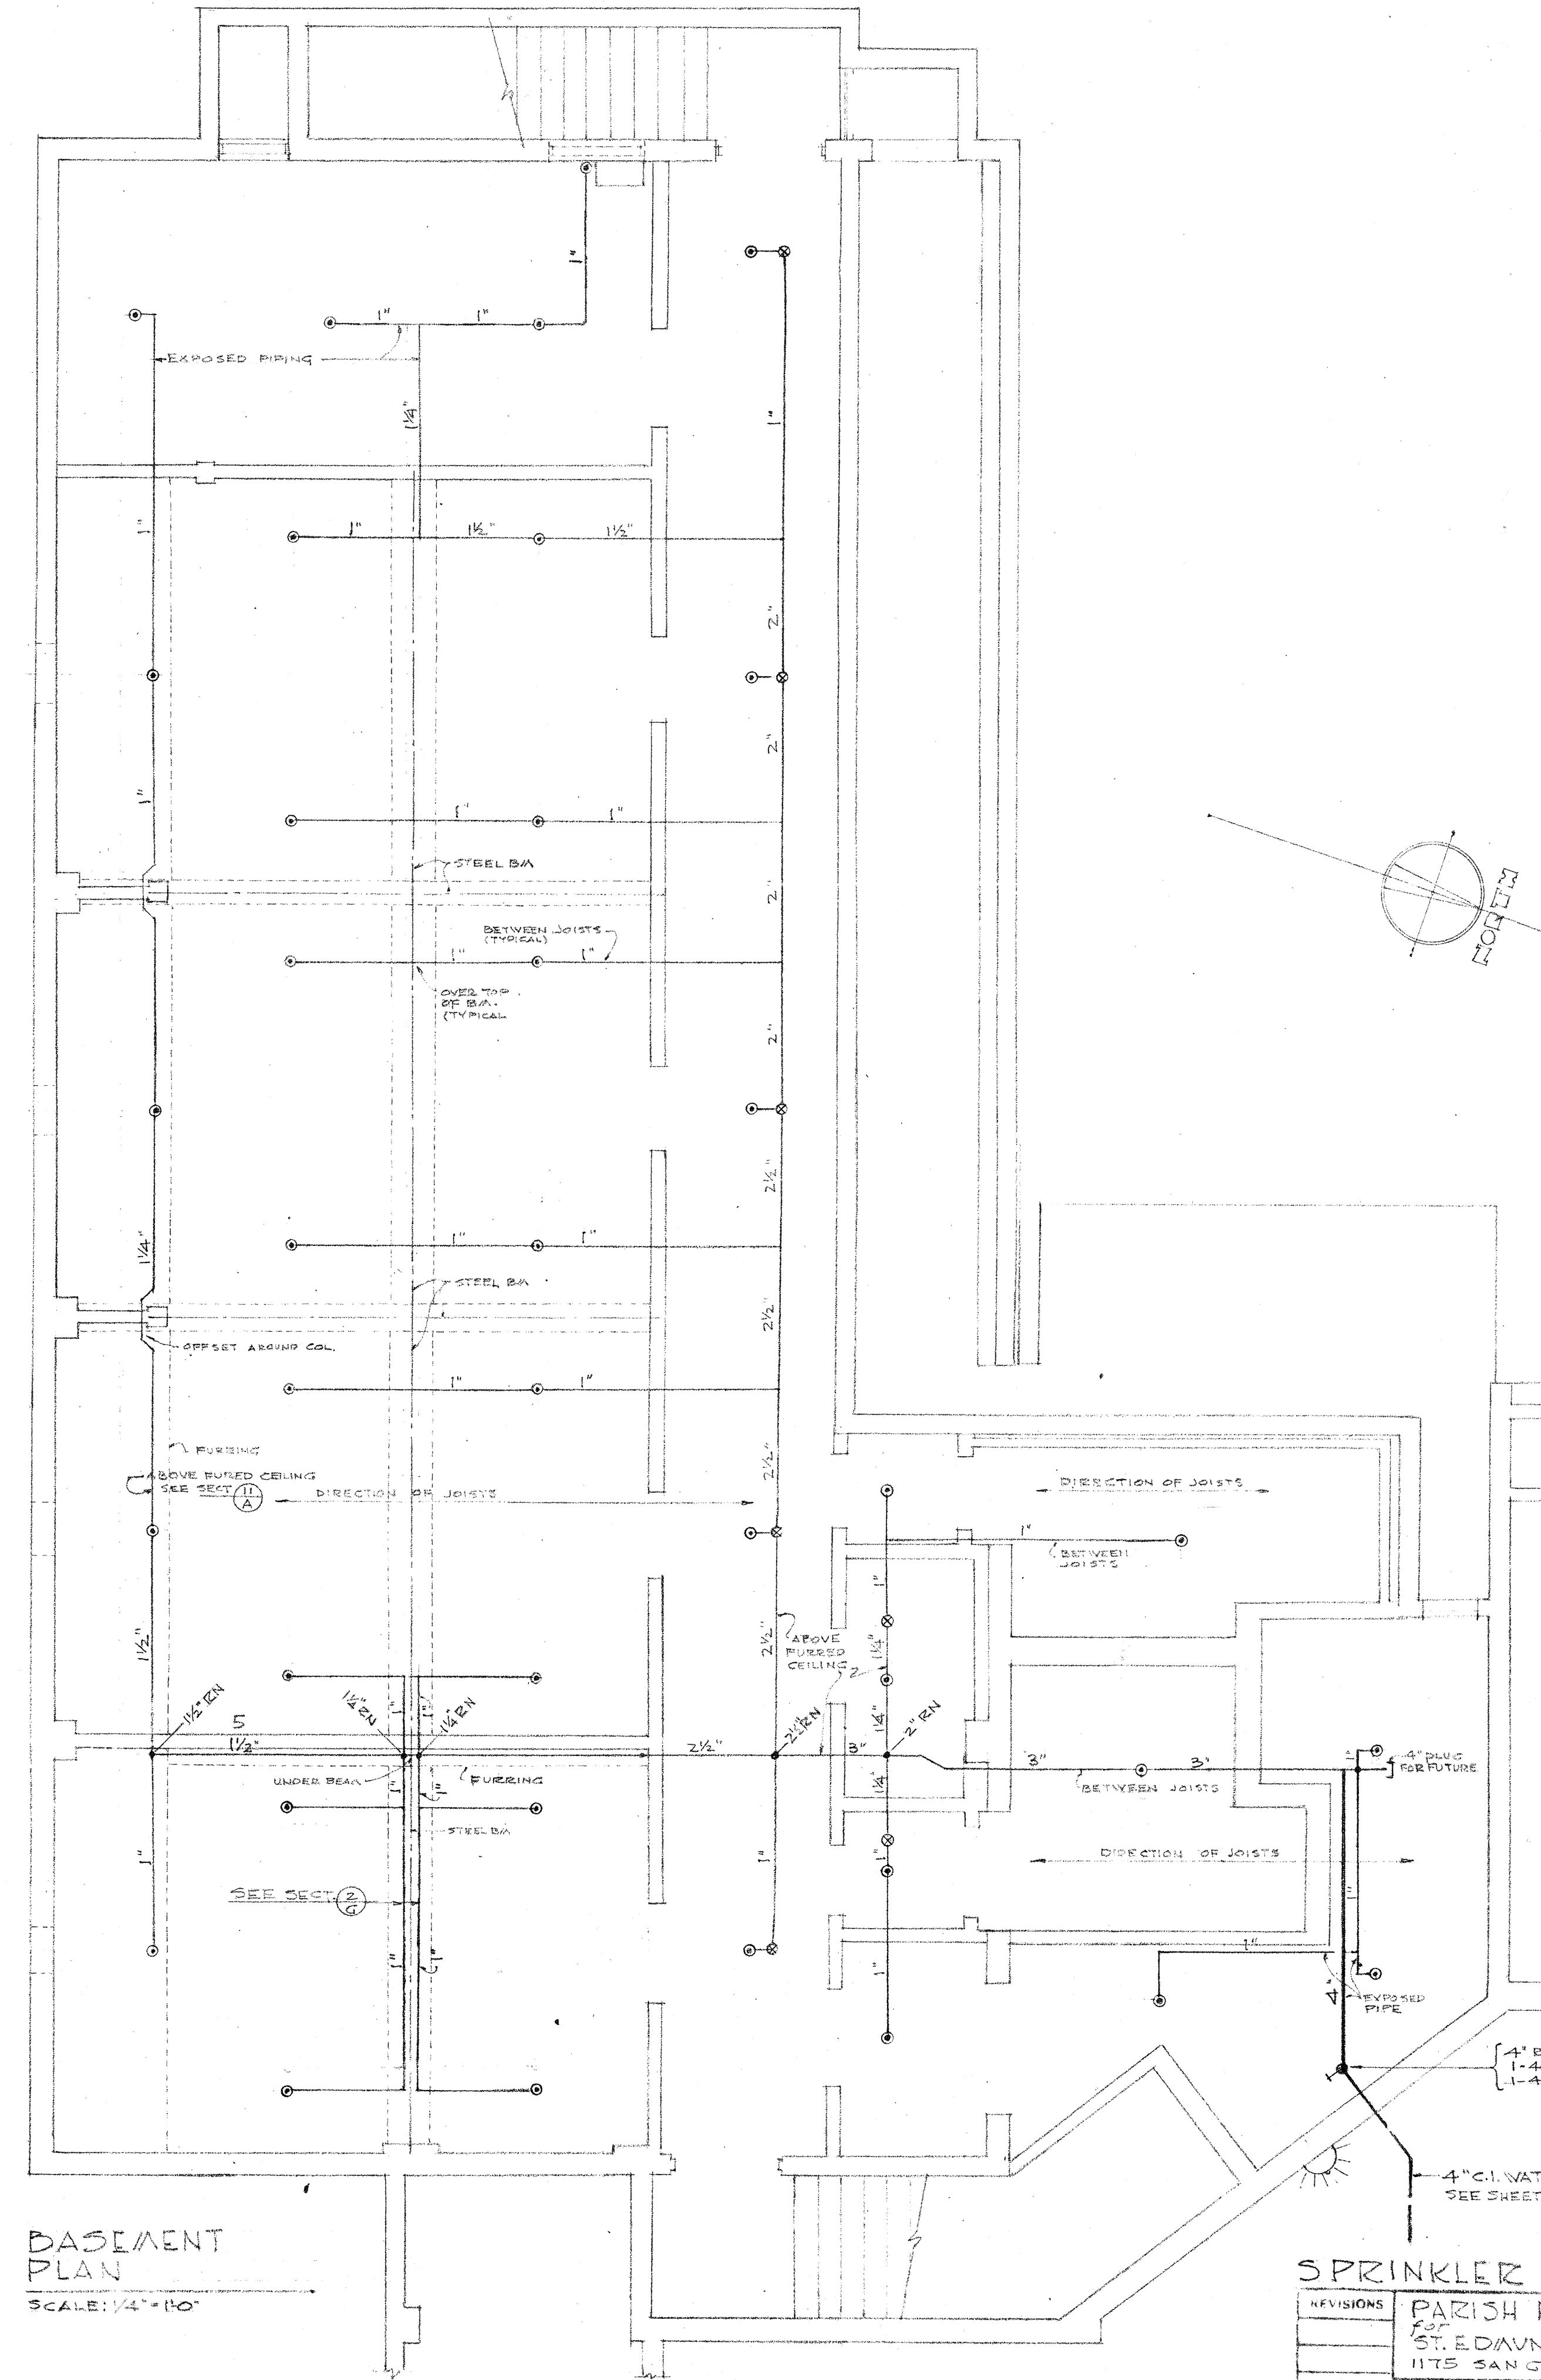

BASIMENT
PLAN
SCALE: 1/4" = 1'-0"

NOTE:
THIS SHEET COVERS ADDITIONAL WORK
NOT SHOWN ON THE ORIGINAL SET.

- SYMBOLS:
- PENDENT HEAD ——— = STAG
 - ⊗ HEAD ABOVE FURRED CEILING = H & S

NOTE:
WORK IN CONNECTION WITH SPRINKLER
SYSTEM SHALL MEET REQUIREMENTS OF
CITY OF SAN MARINO CODE.
THIS LAYOUT AND ITS INSTALLATION
MUST BE APPROVED BY THE SAN MARINO
FIRE CHIEF.

REVISIONS		SPRINKLER LAYOUT	
		PARISH HALL ADDITION	
		ST. EDWARD'S EPISCOPAL CHURCH	
		1175 SAN GABRIEL BLVD, SAN MARINO, CALIFORNIA	
DRAWN BY		BREG FREEMAN	
TRACED BY		ARCHITECT	
DATE		3-31-66	
		45 SOUTH MARENGO	
		PASADENA 1, CALIFORNIA	
		JOB NO. 927	
		SHEET NO. 2-B	
		OF 15	