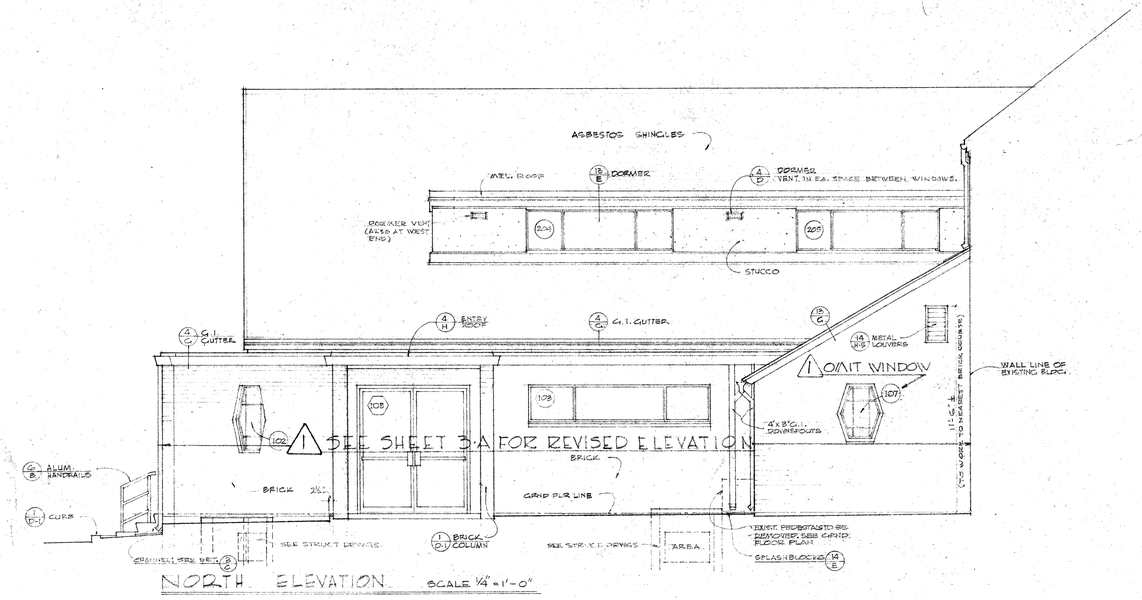

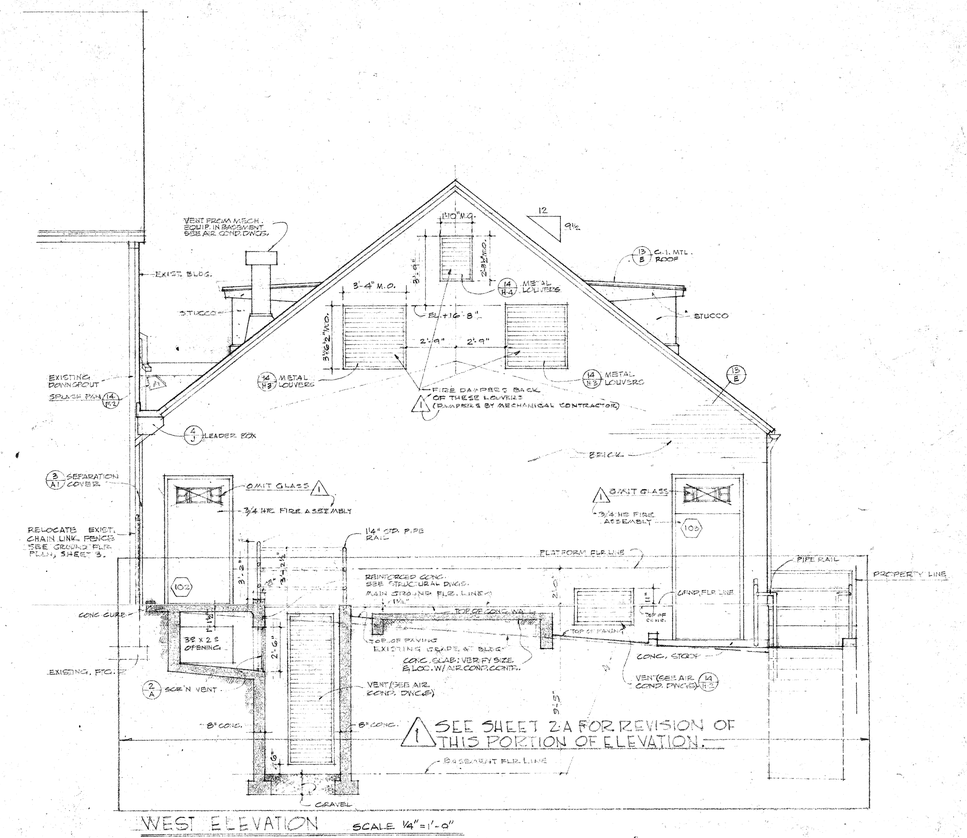

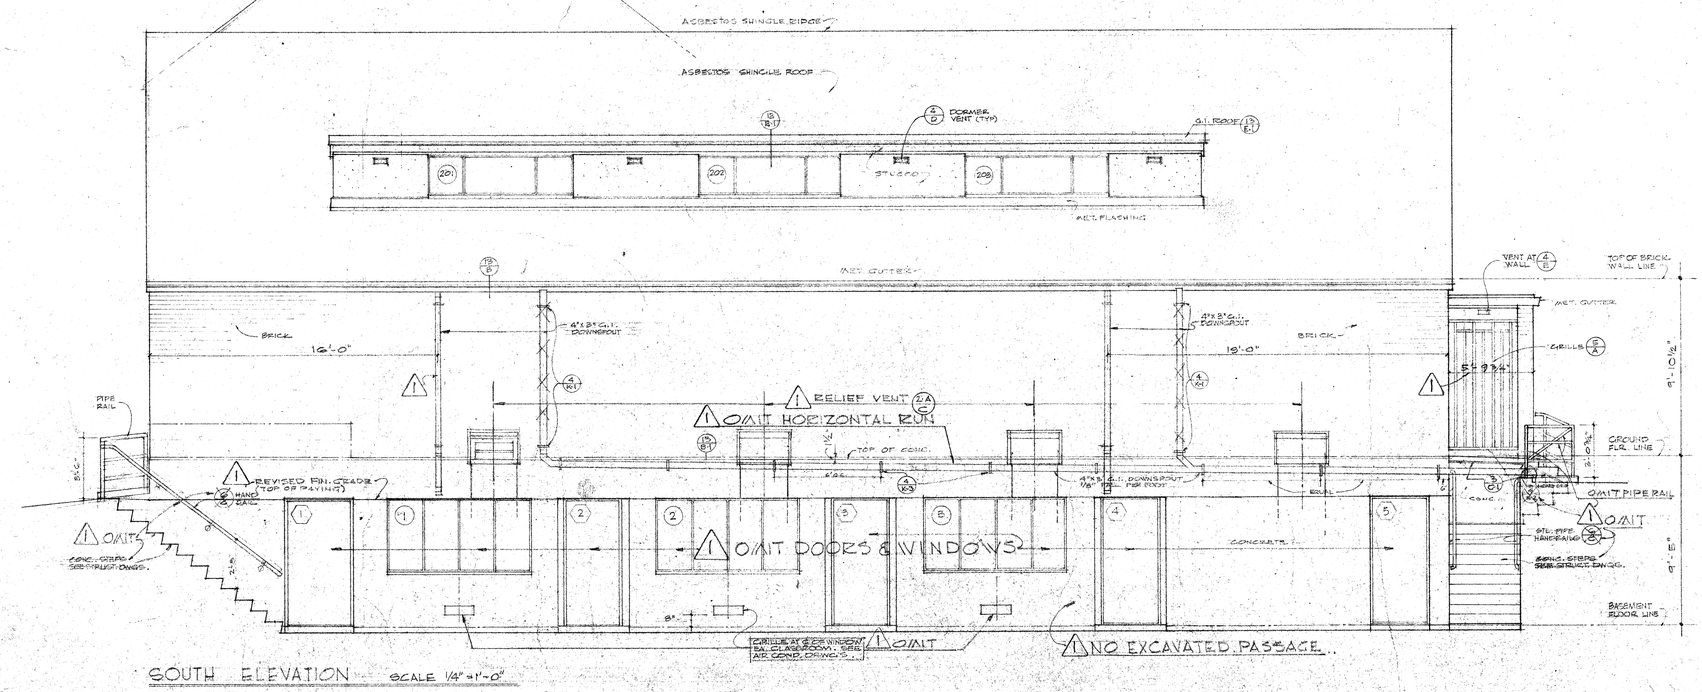

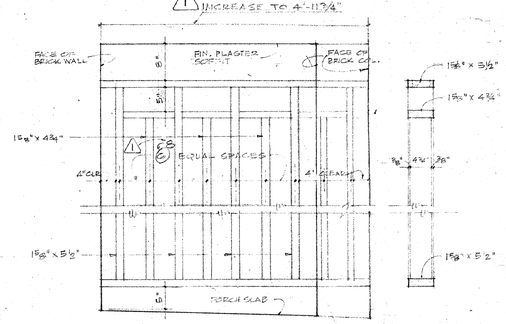

A GRILLE FOR EAST ENTRANCE PORCH

ELEVATIONS

REVISIONS	PARISH HALL ADDITION
1 2-21-64	for ST. EDMUND'S EPISCOPAL CHURCH
	1175 SAN GABRIEL BLVD. SAN MARINO, CALIFORNIA
DRAWN BY B.F.-G.	BREO FREEMAN ARCHITECT
TRACED BY G.E.-G.	45 SOUTH MARENGO PASADENA 1, CALIFORNIA
DATE 12-30-63	JOB NO. 927 SHEET NO. 5 OF 13 SHTS