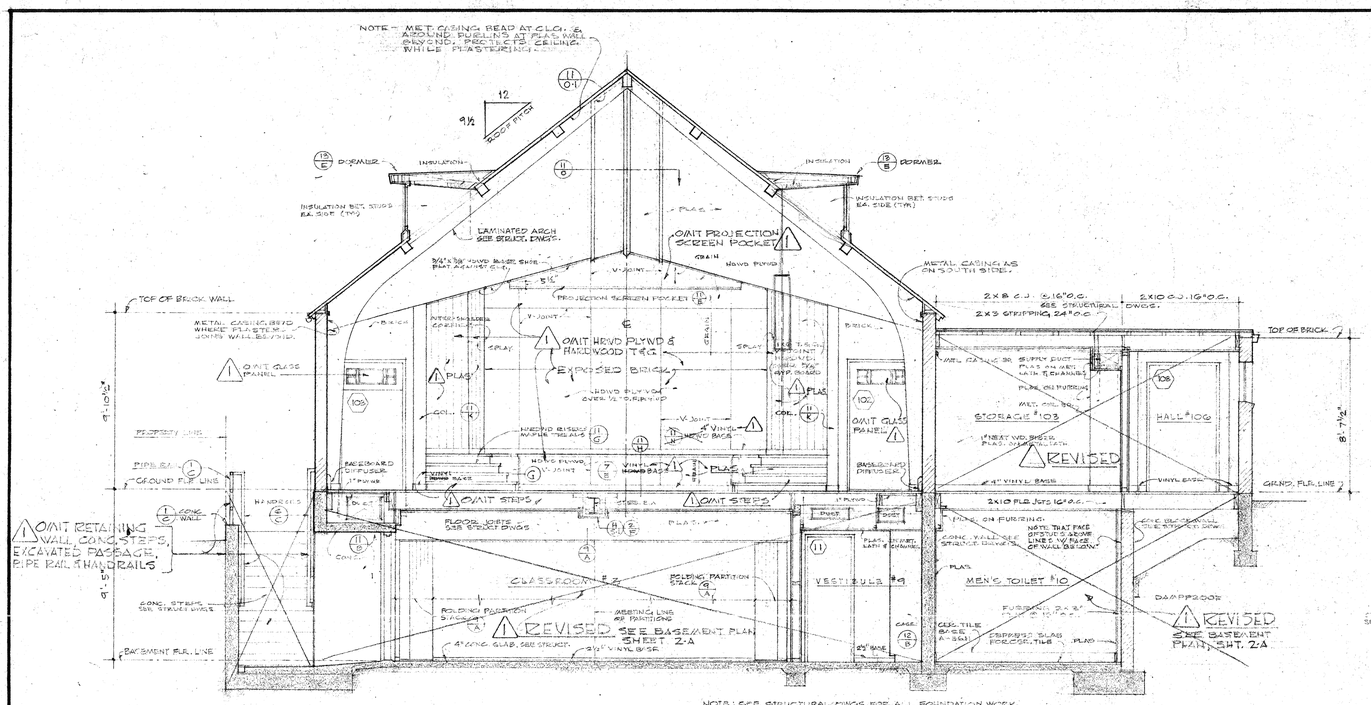

A CROSS SECTION-1
SCALE: 1/4" = 1'-0"

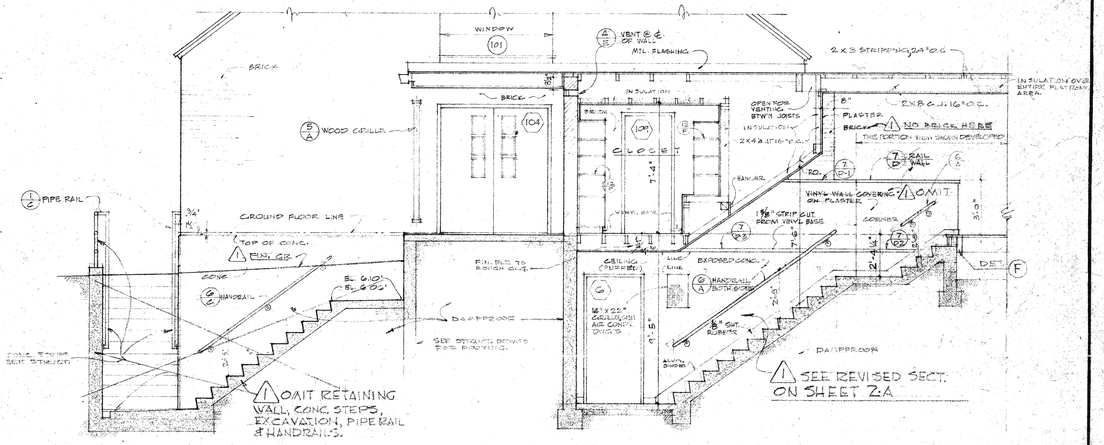

B SECTION AT EAST END OF PARISH HALL
SCALE: 1/2" = 1'-0"

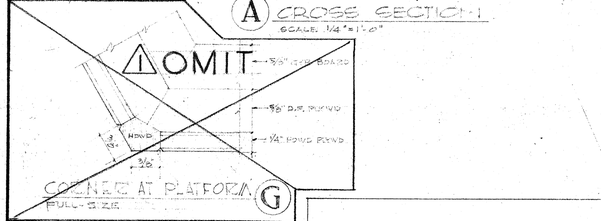

CONNEC AT PLATFORM G
FULL SIZE

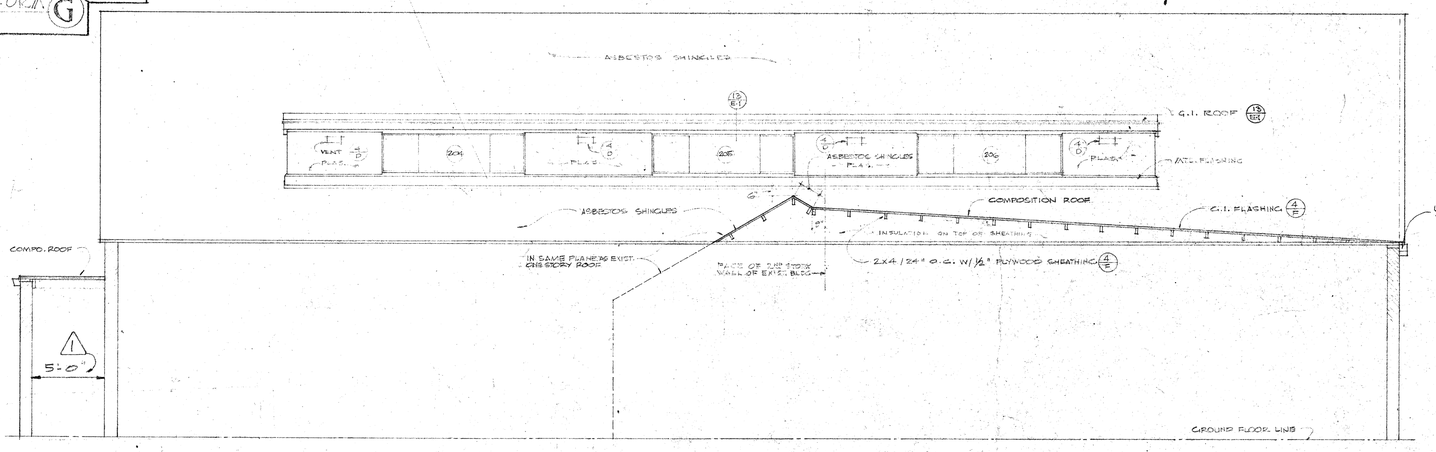

C SECTION THRU ROOF SADDLE AT NORTH WALL & EXISTING BUILDING
SCALE: 1/4" = 1'-0"

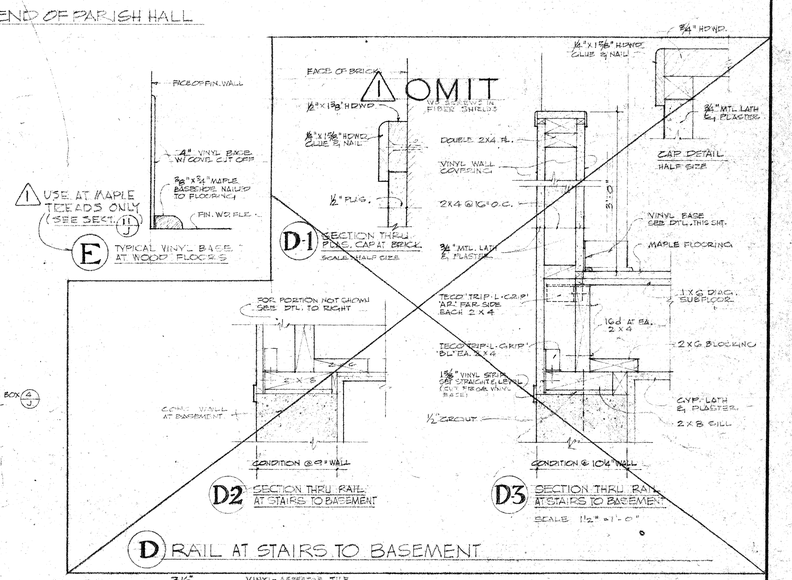

D RAIL AT STAIRS TO BASEMENT

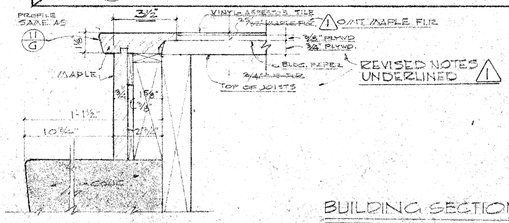

F SECT. THRU TOP RISER OF STAIRS IN FOYER 105
SCALE: 3"=1'-0"

BUILDING SECTIONS

REVISIONS	PARISH HALL ADDITION for ST. EDMUND'S EPISCOPAL CHURCH 1175 SAN GABRIEL BLVD. SAN MARINO, CALIFORNIA
3-31-66	
DRAWN BY O.F.S.	BREO FREEMAN ARCHITECT 45 SOUTH MARENGO PASADENA 1, CALIFORNIA
TRACED BY C.B.C.	JOB NO. 927
DATE 12-30-65	SHEET NO. 7 of 13 3-66