


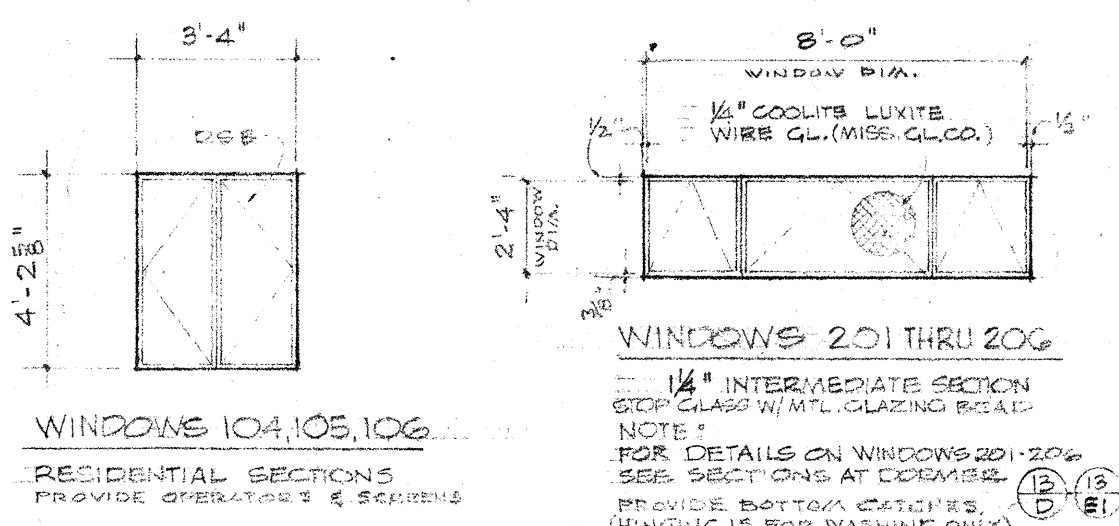


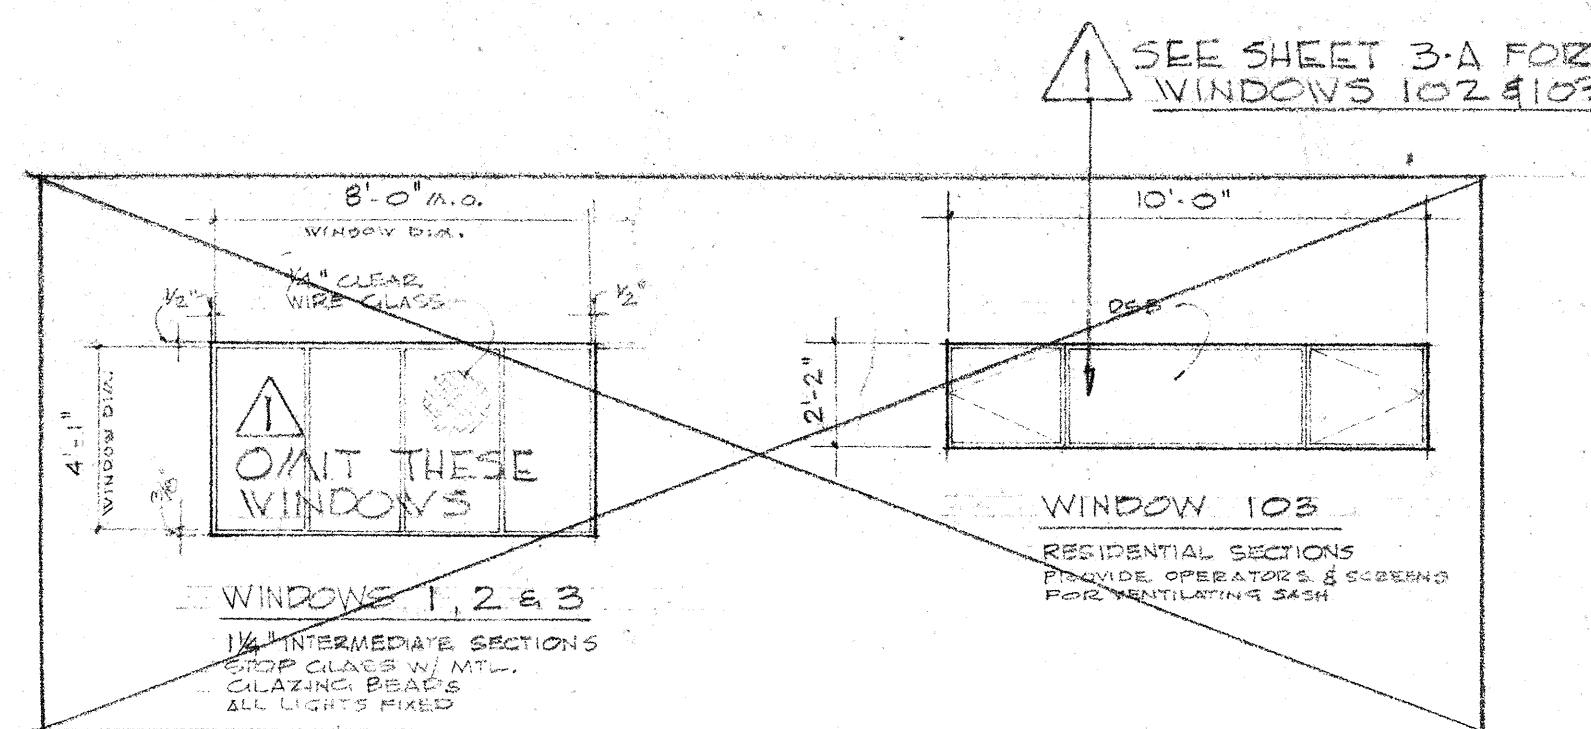


WINDOW ELEVATIONS SCALE 3/4" = 1'-0"

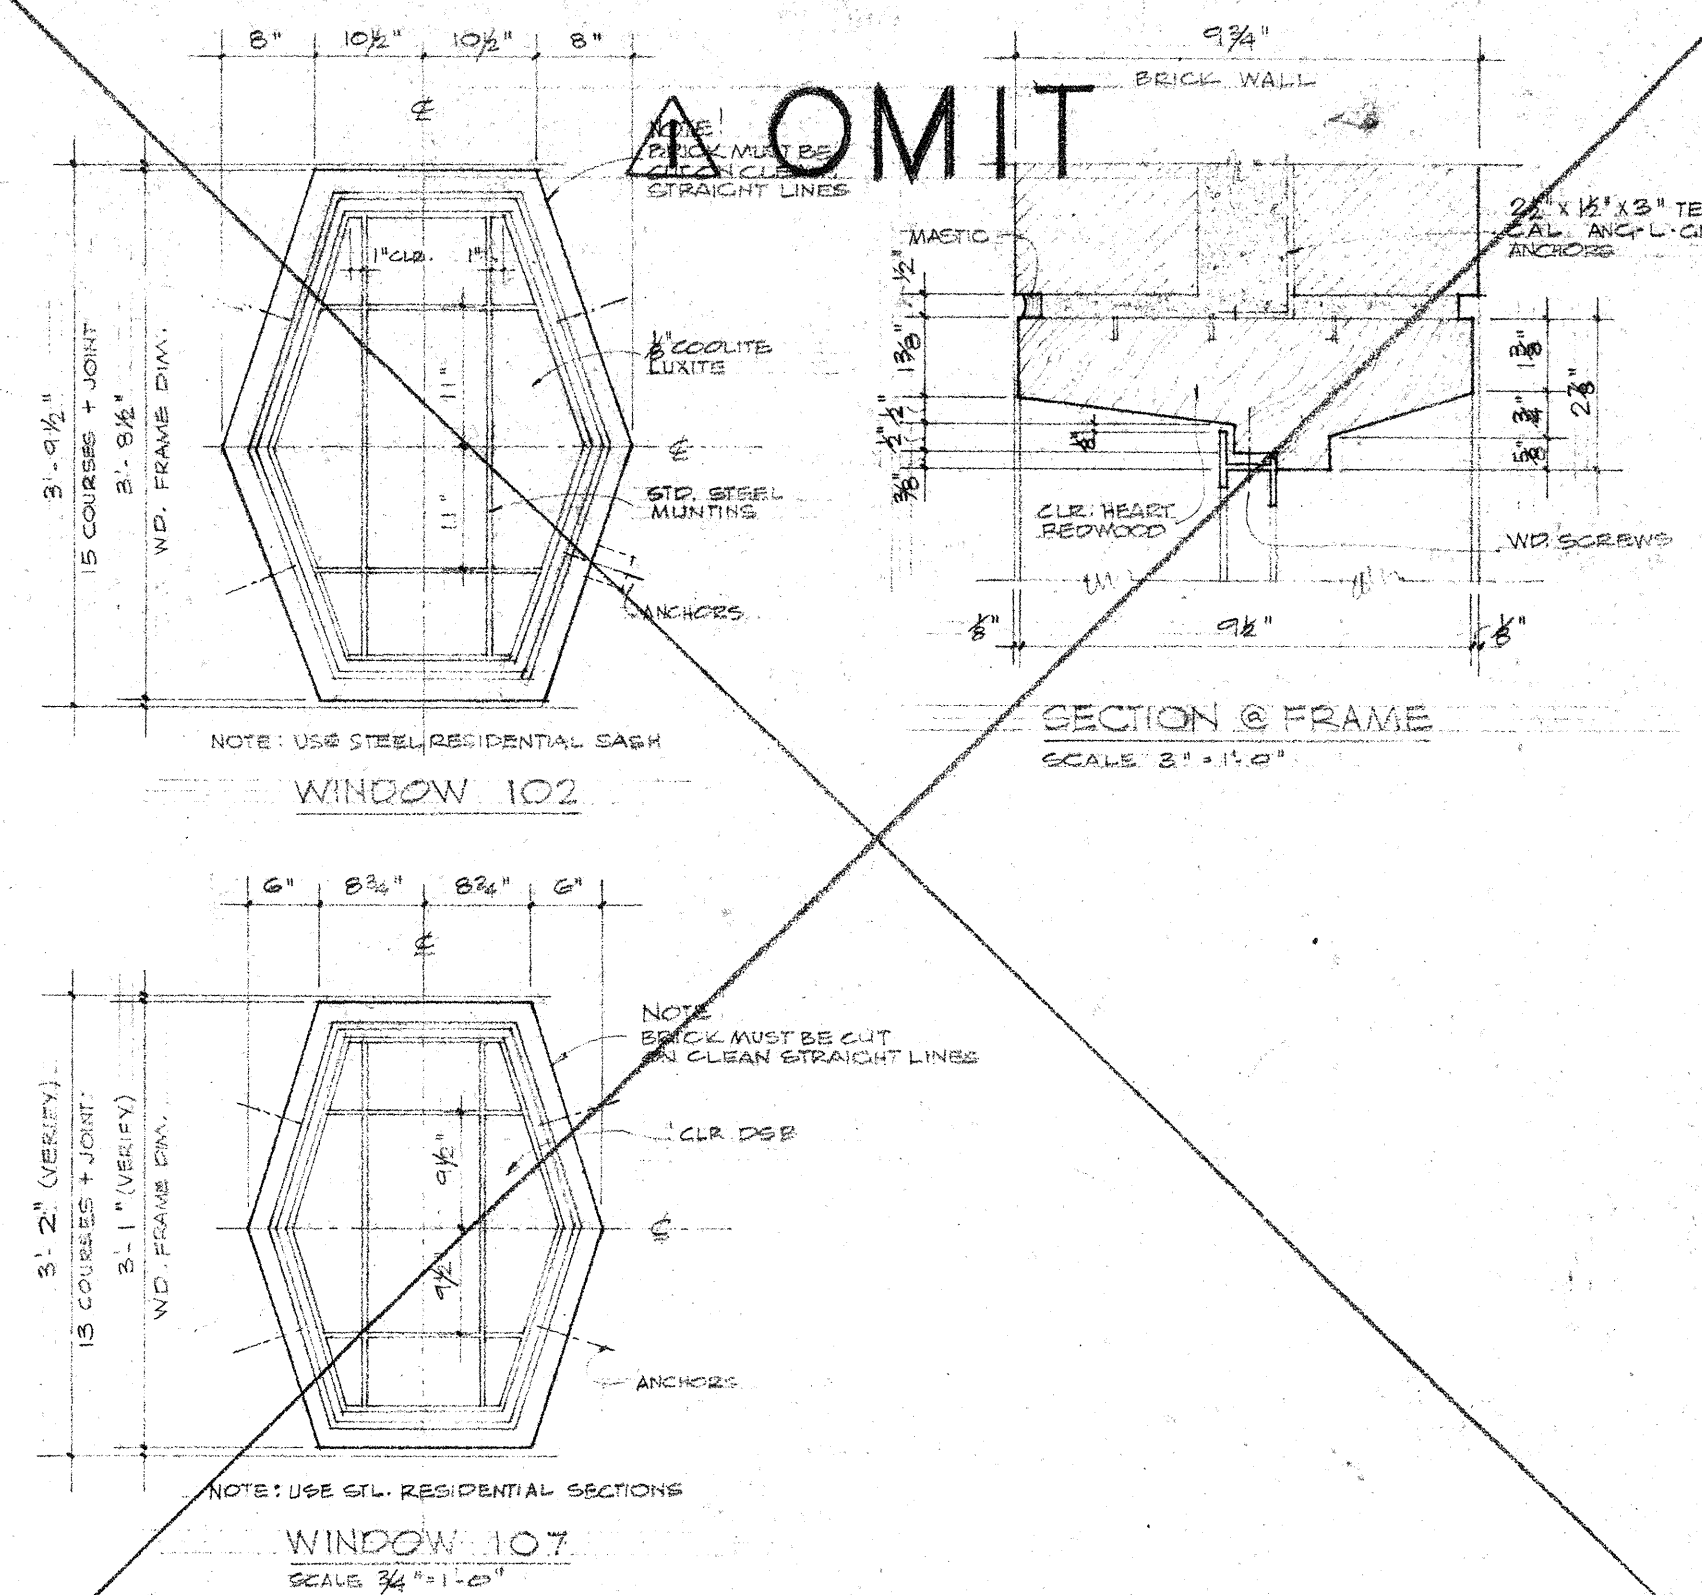


WINDOWS 102 & 107 ELEVATIONS & SECTION

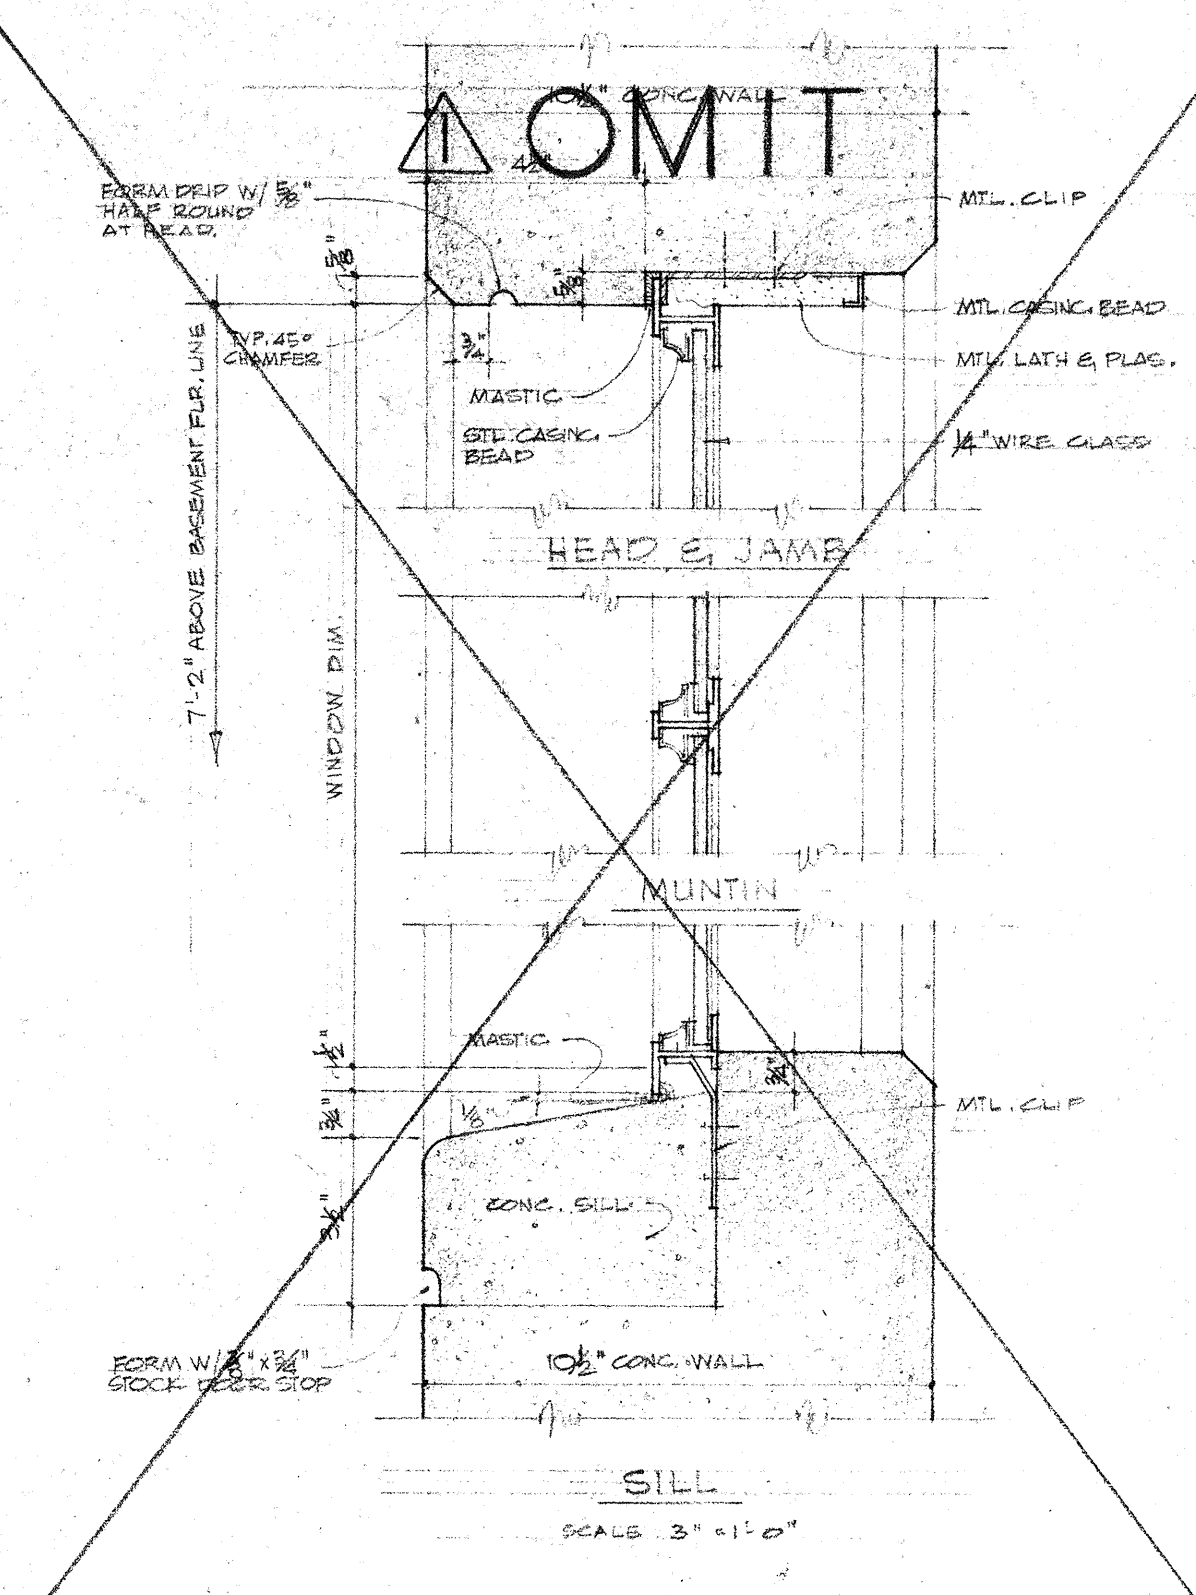

WINDOWS 1, 2 & 3 SECTIONS

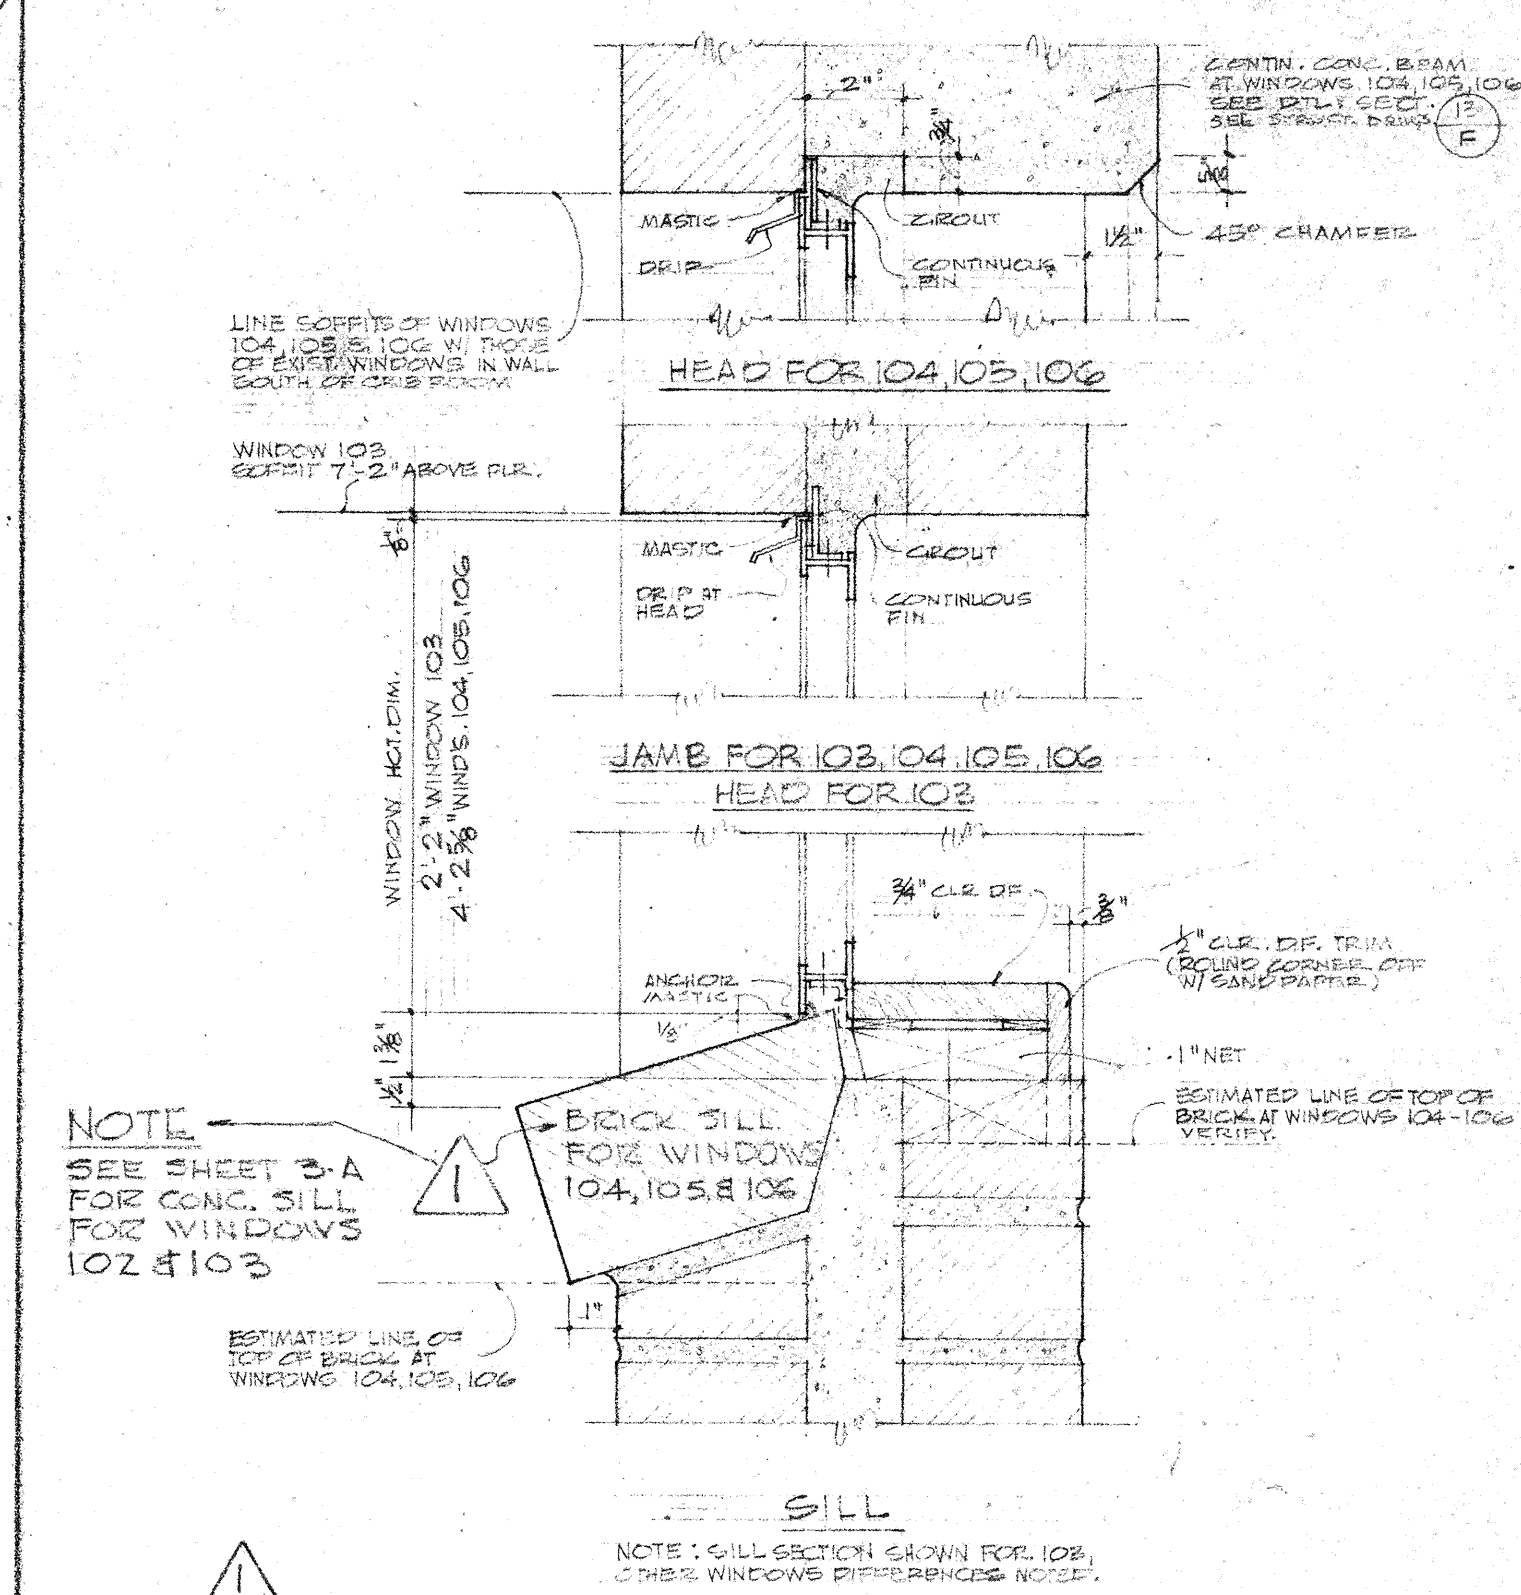


WINDOWS 103, 104, 105, 106 SECTIONS

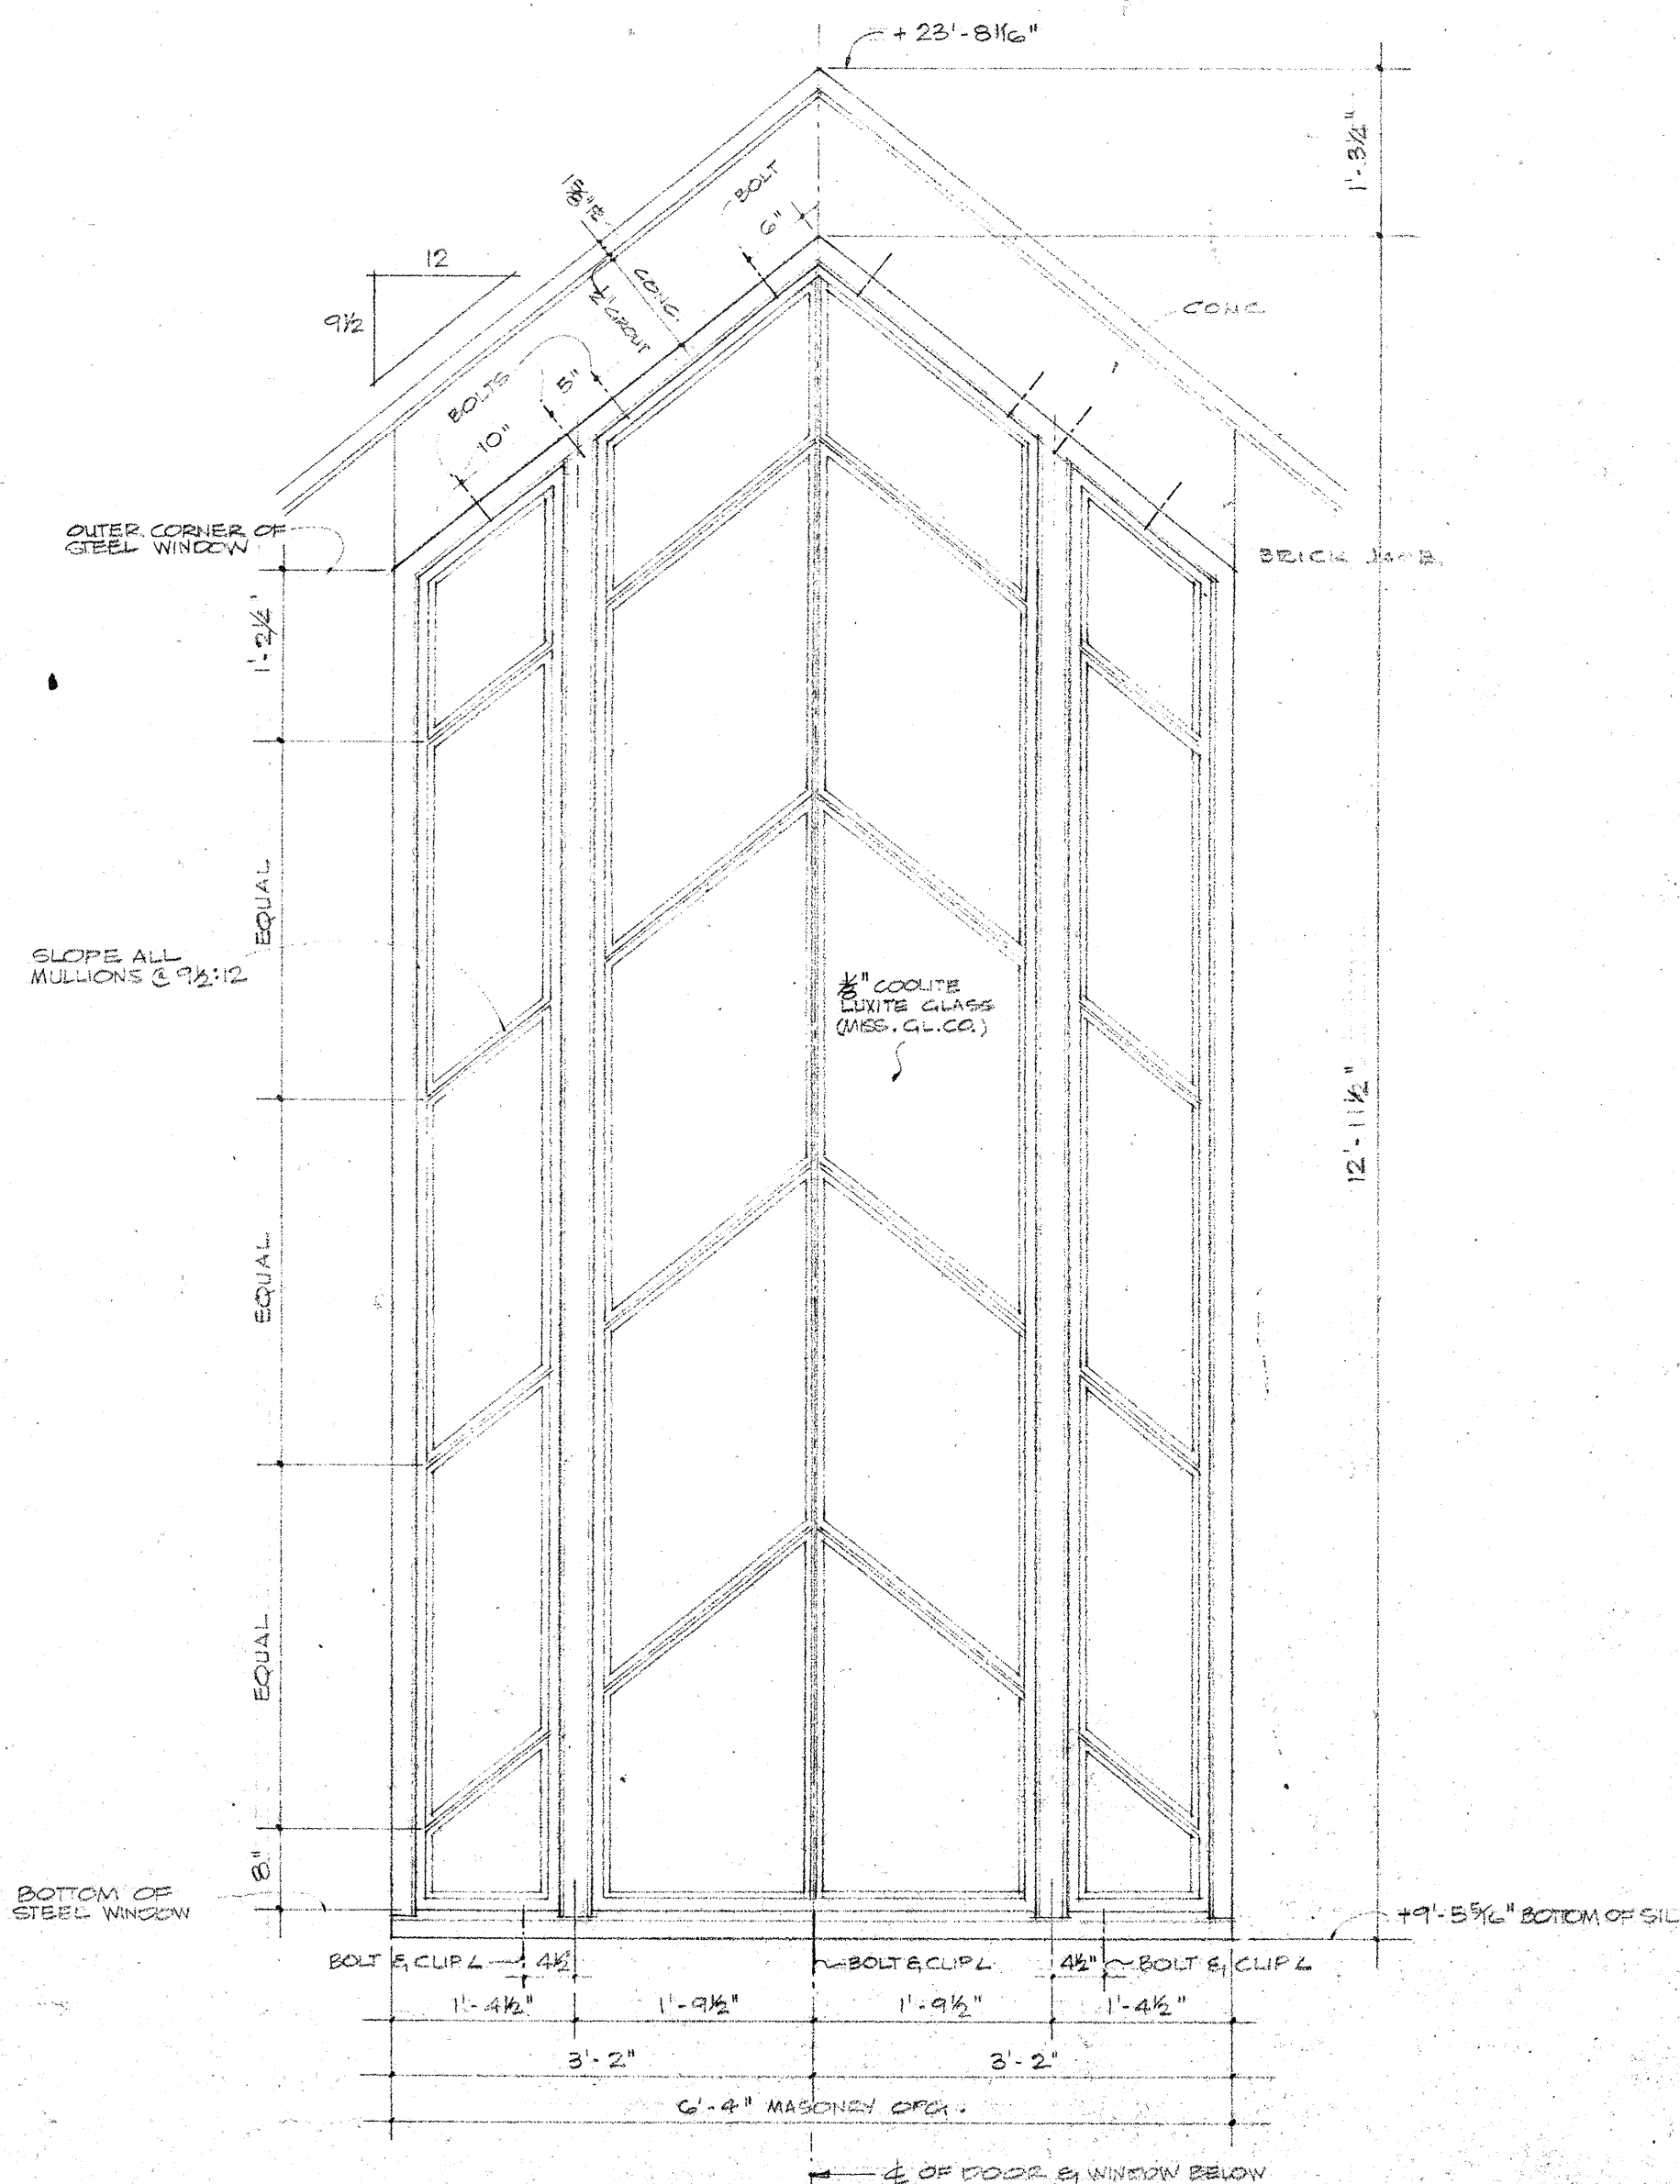


1/4" INTERMEDIATE SECTIONS (STEEL)

WINDOW 101 ELEVATION
SCALE 3/4" = 1'-0"

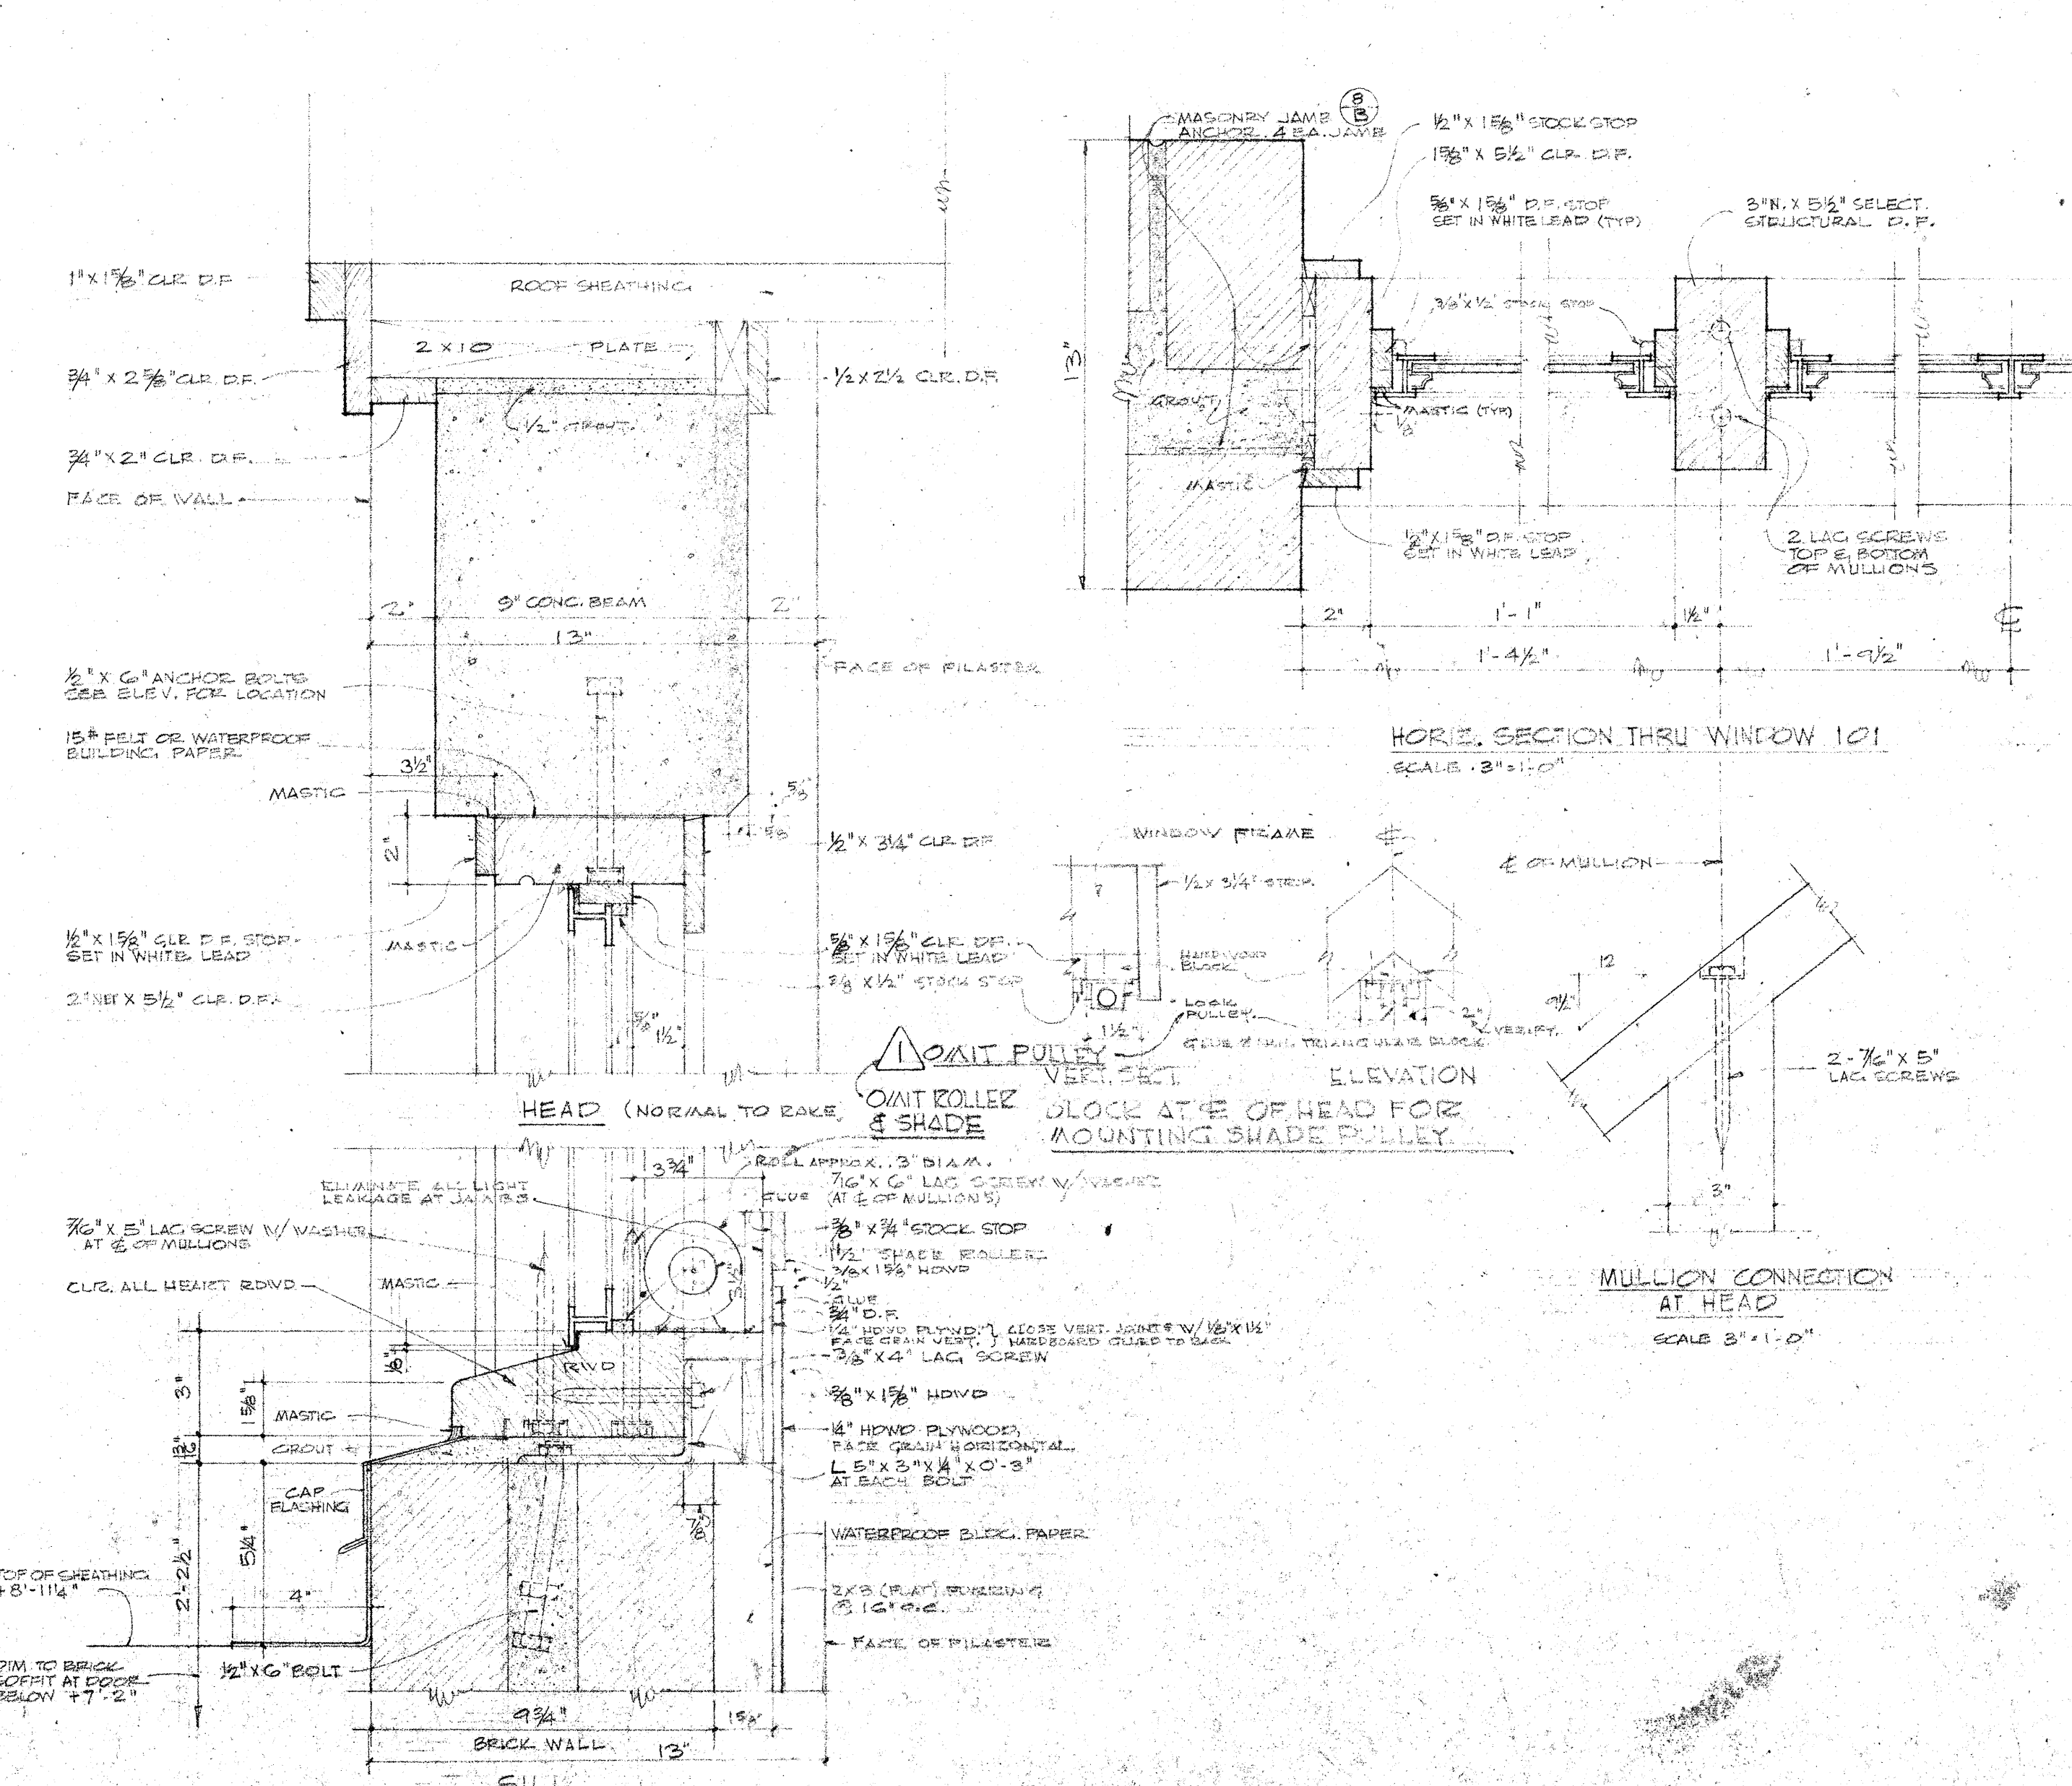

WINDOW 101 SECTIONS
SCALE 3/4" = 1'-0"

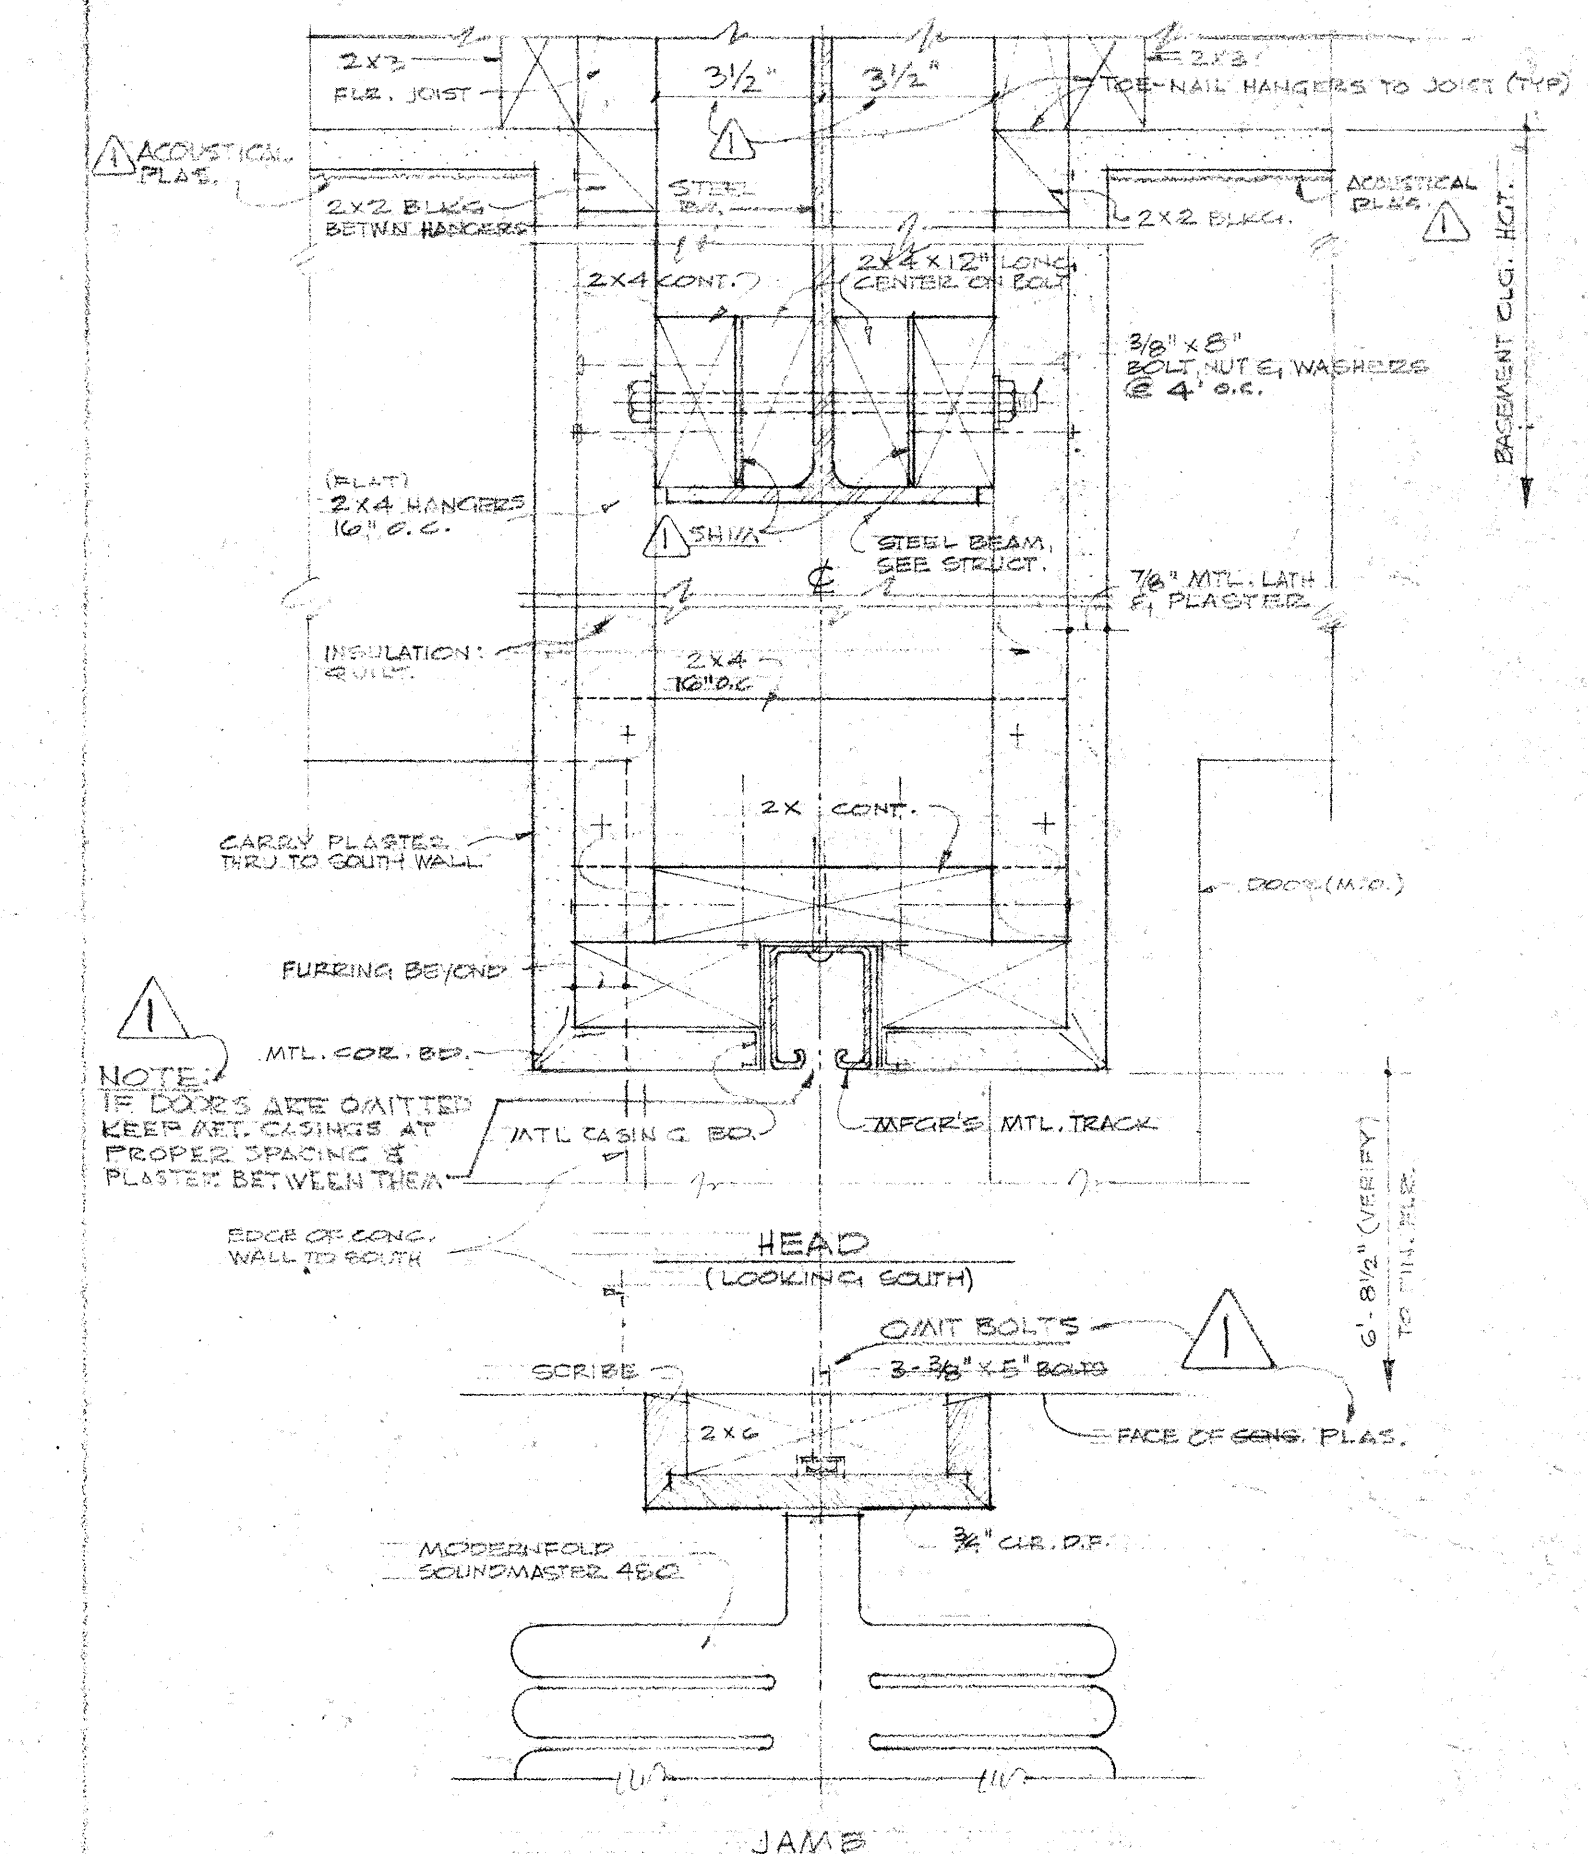

MODERNEFOLD FOLDING PARTITIONS
SCALE: 3/4" = 1'-0"

REVISIONS	PARISH HALL ADDITION
1	FOR
2	ST. EDWARD'S EPISCOPAL CHURCH
3	1175 SAN GABRIEL BLVD., SAN MARINO, CALIFORNIA
4	DRAWN BY
5	BREO FREEMAN
6	ARCHITECT
7	45 SOUTH MARENGO
8	PASADENA, CALIFORNIA
9	JOB NO. 927
10	DATE 12-30-66
11	9 15
12	40