




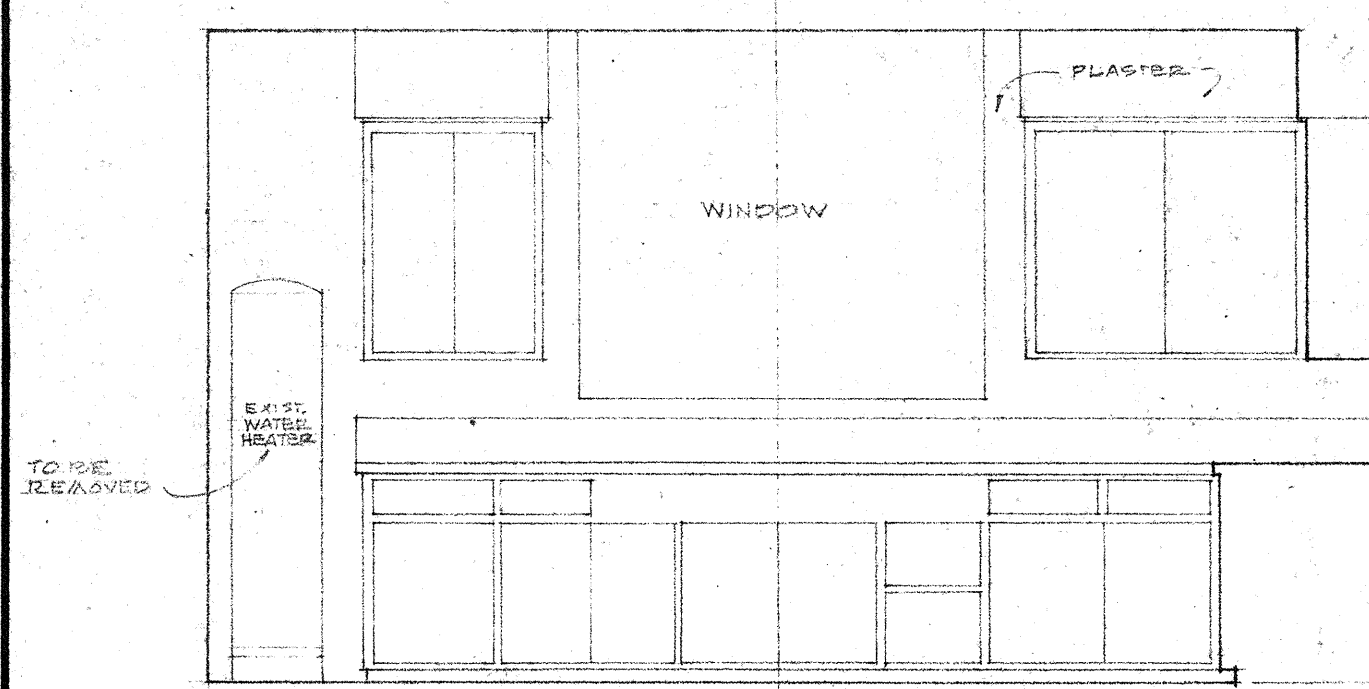


WEST
ELEV. OF EXISTING KITCHEN
SCALE 3/8" = 1'-0"

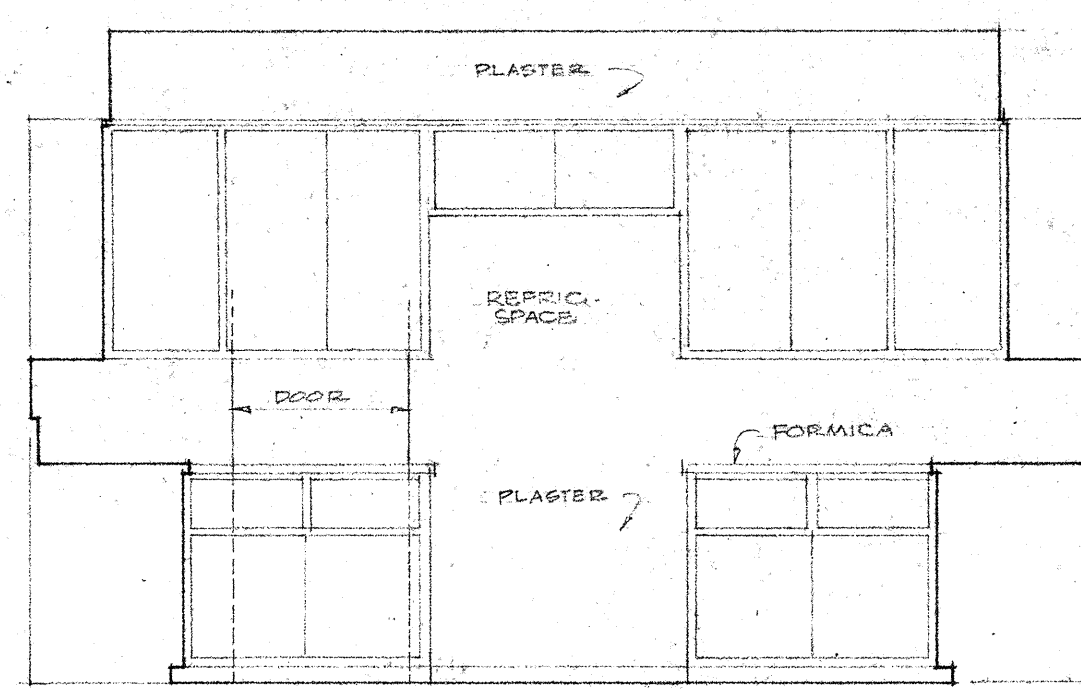


NORTH
NOTE: LOWER CASES HAVE ONE SHELF, UPPER CASES HAVE 3 SHELVES

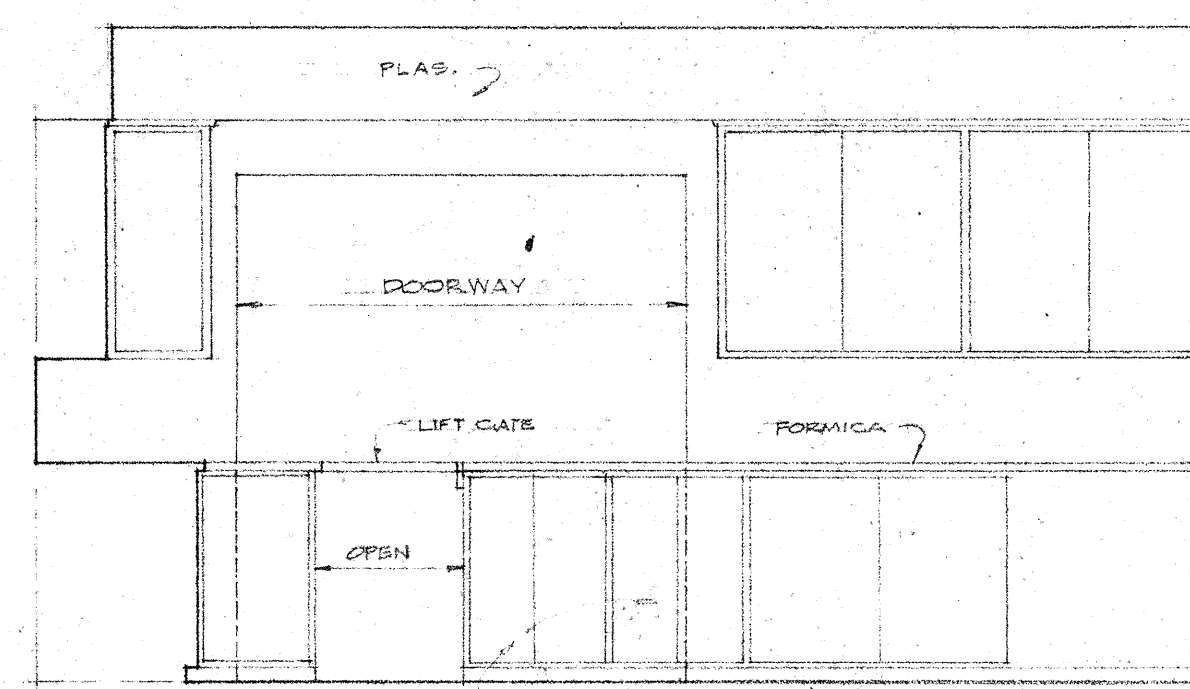


EAST

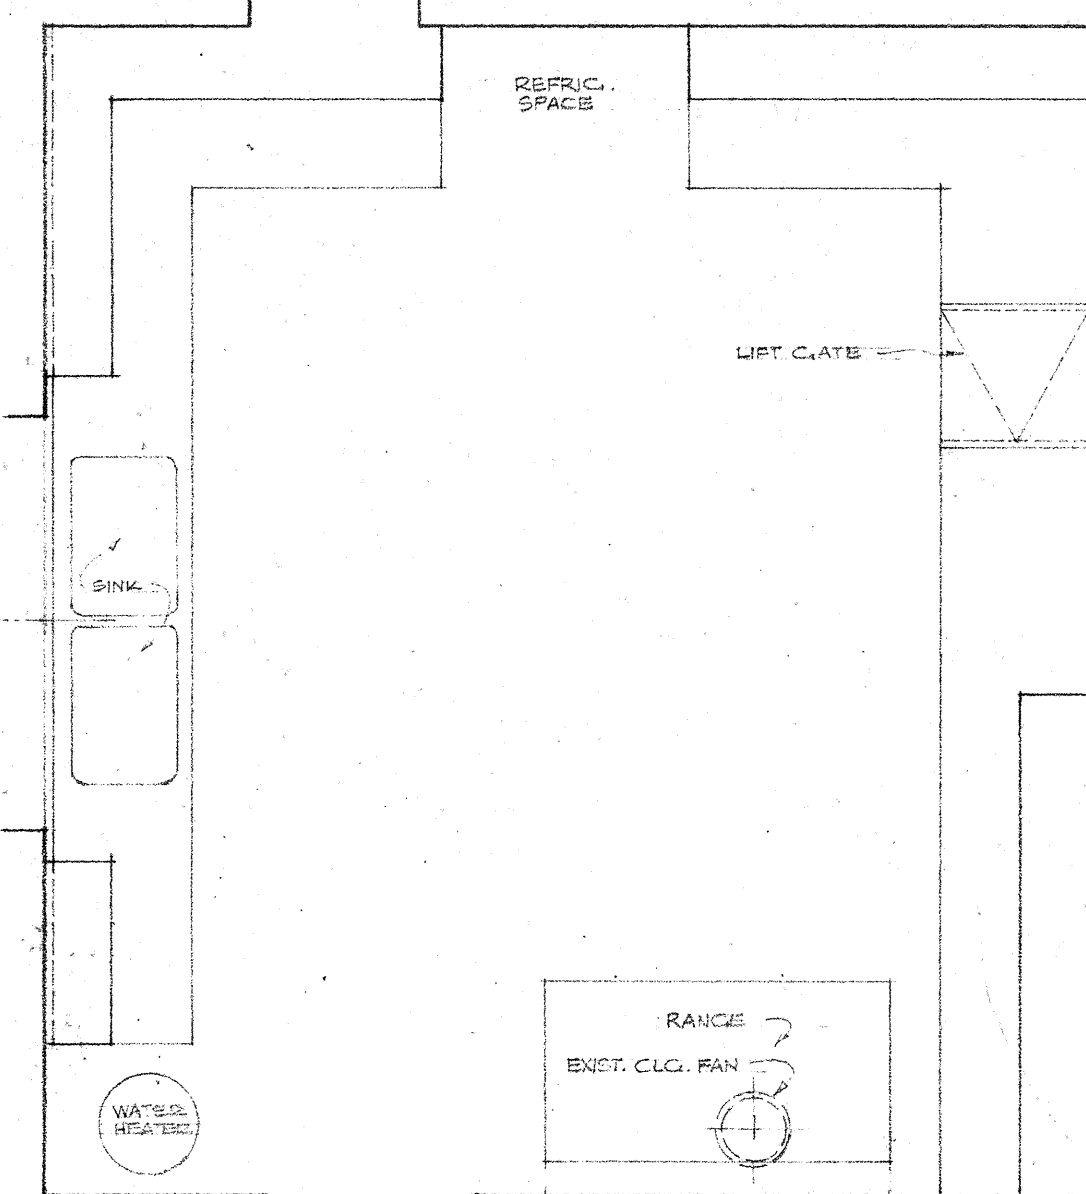


PLAN OF KITCHEN 'AS IS'

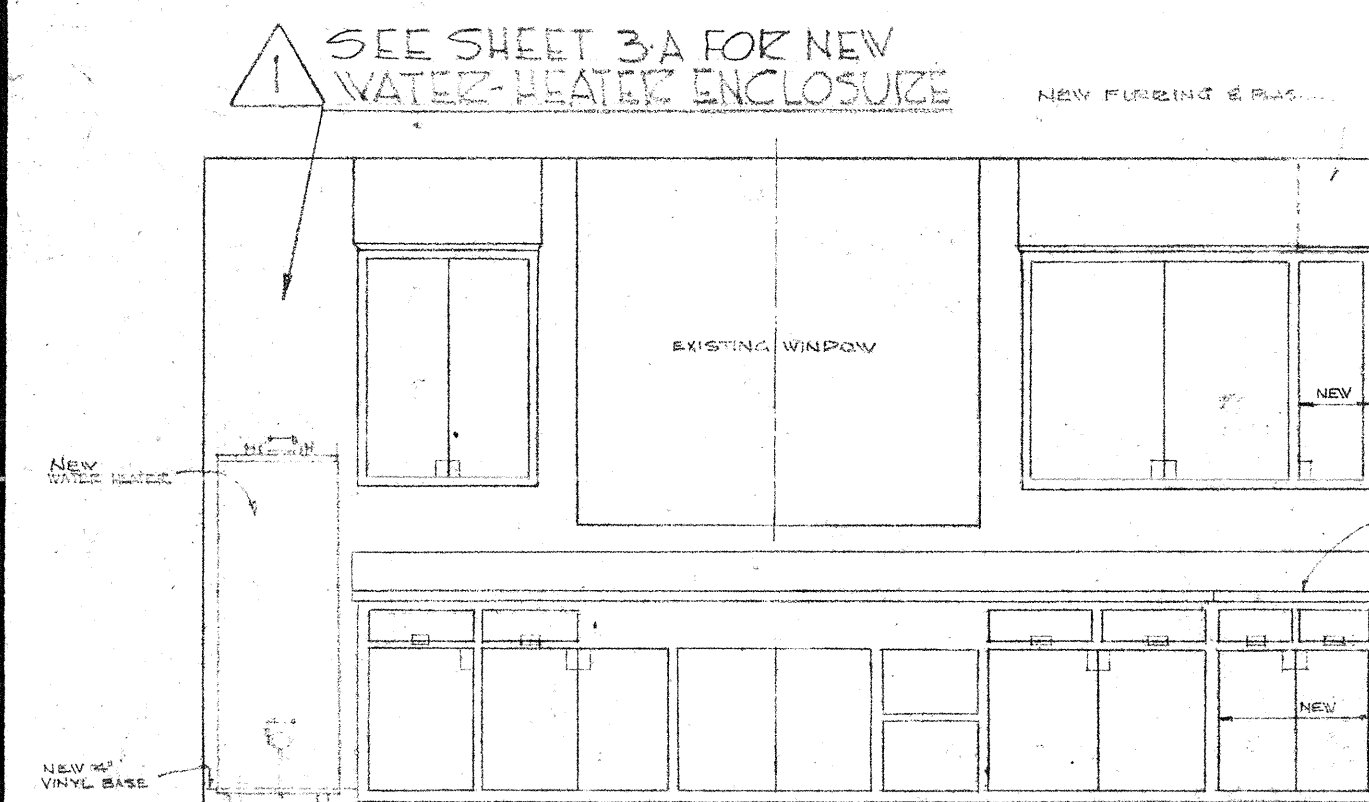


WEST
NOTE: INTEGRAL PULLS ON DRAWERS & CABINET DOORS TO MATCH EXISTING.

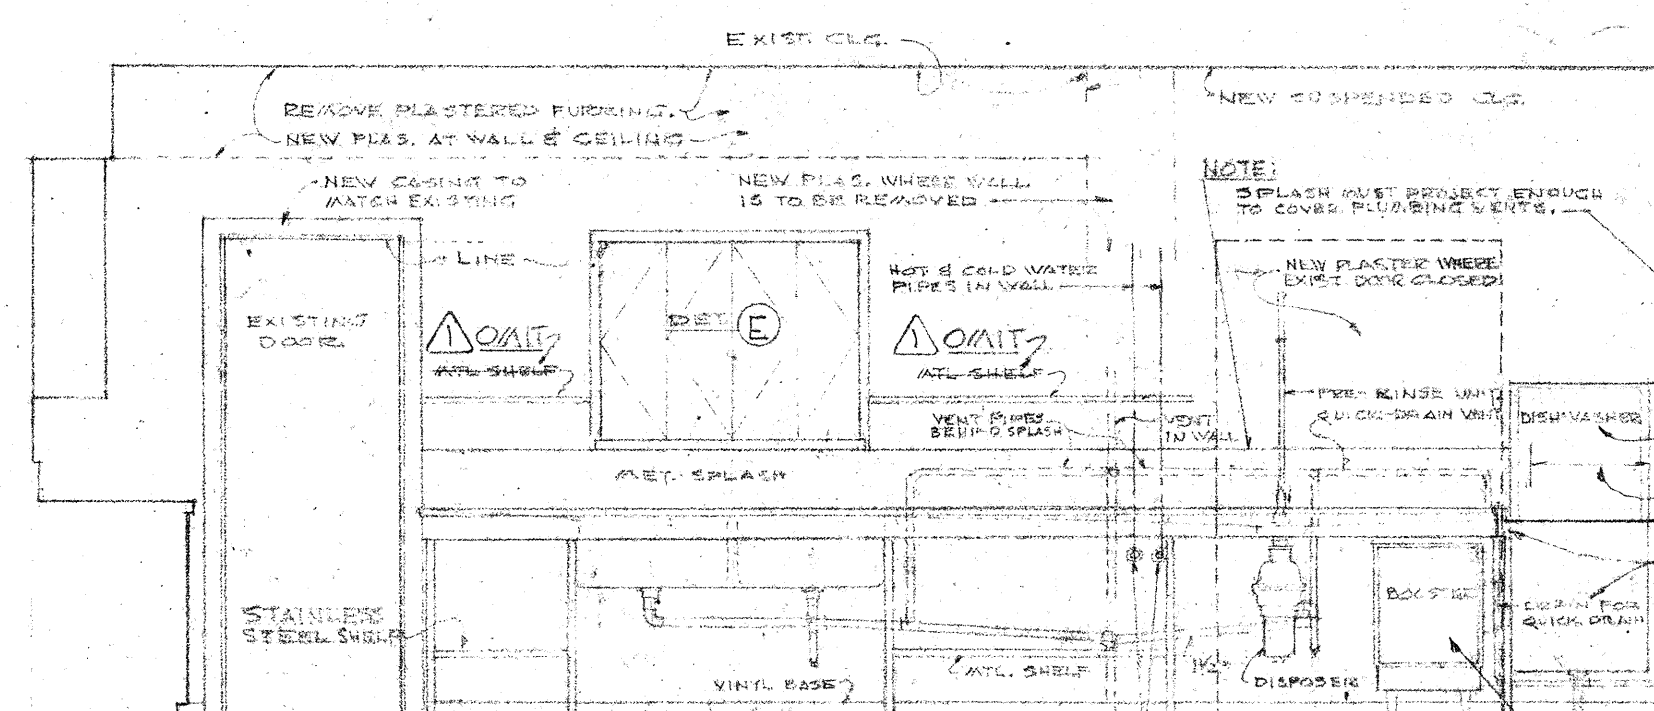


NORTH
ADJUST ELEVATION TO AGREE WITH PLAN ON SHEET 3-A

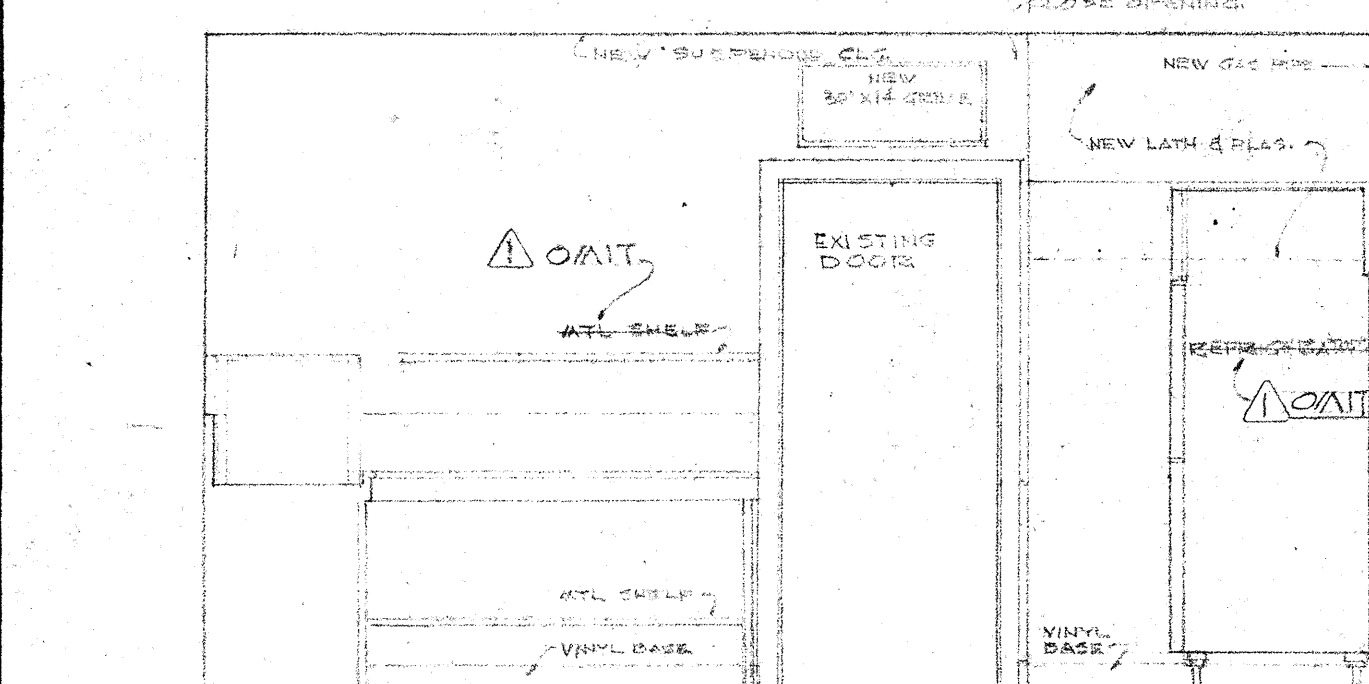


EAST
ELEV. OF NEW KITCHEN
SCALE 3/8" = 1'-0"

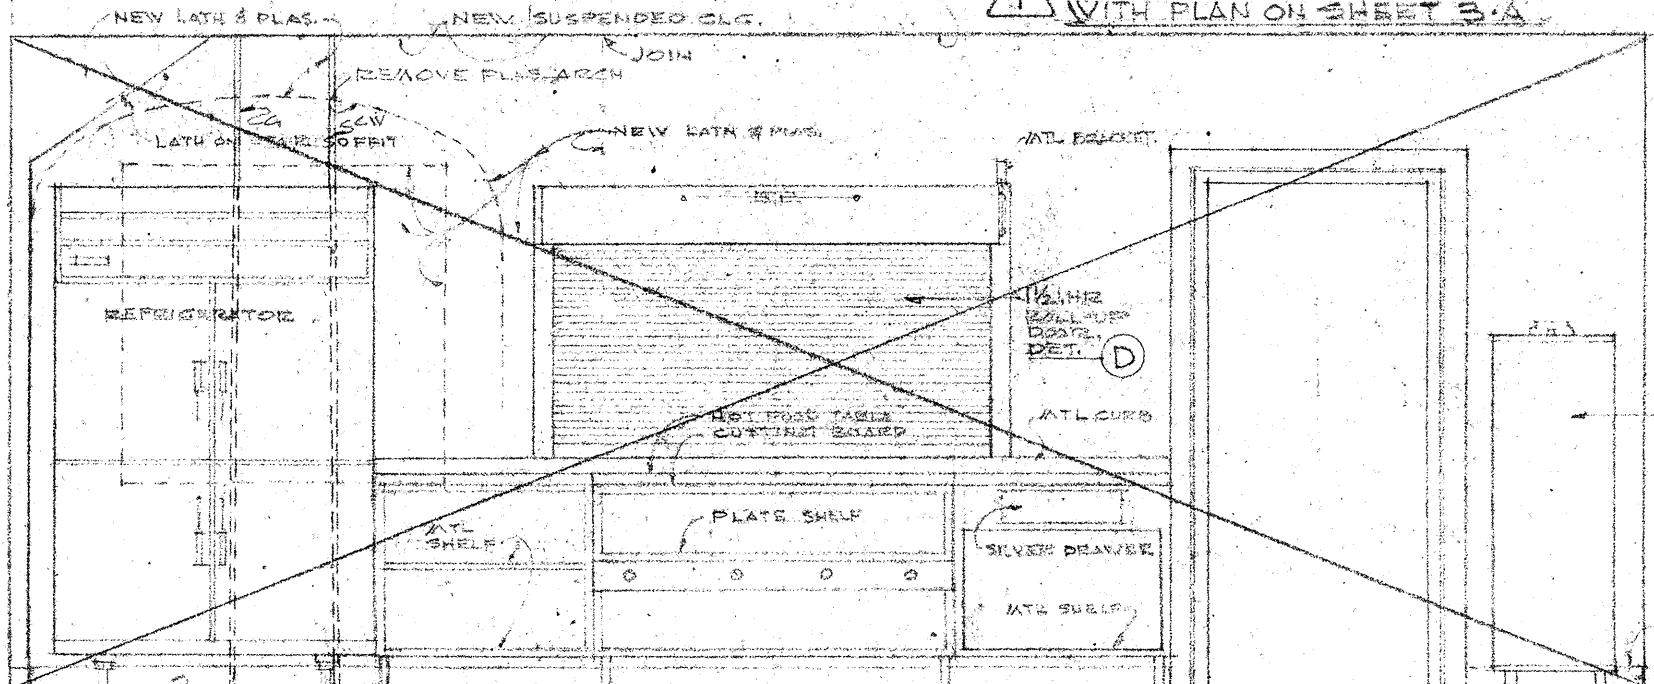


SOUTH
SEE ELEVATION ON SHEET 3-A

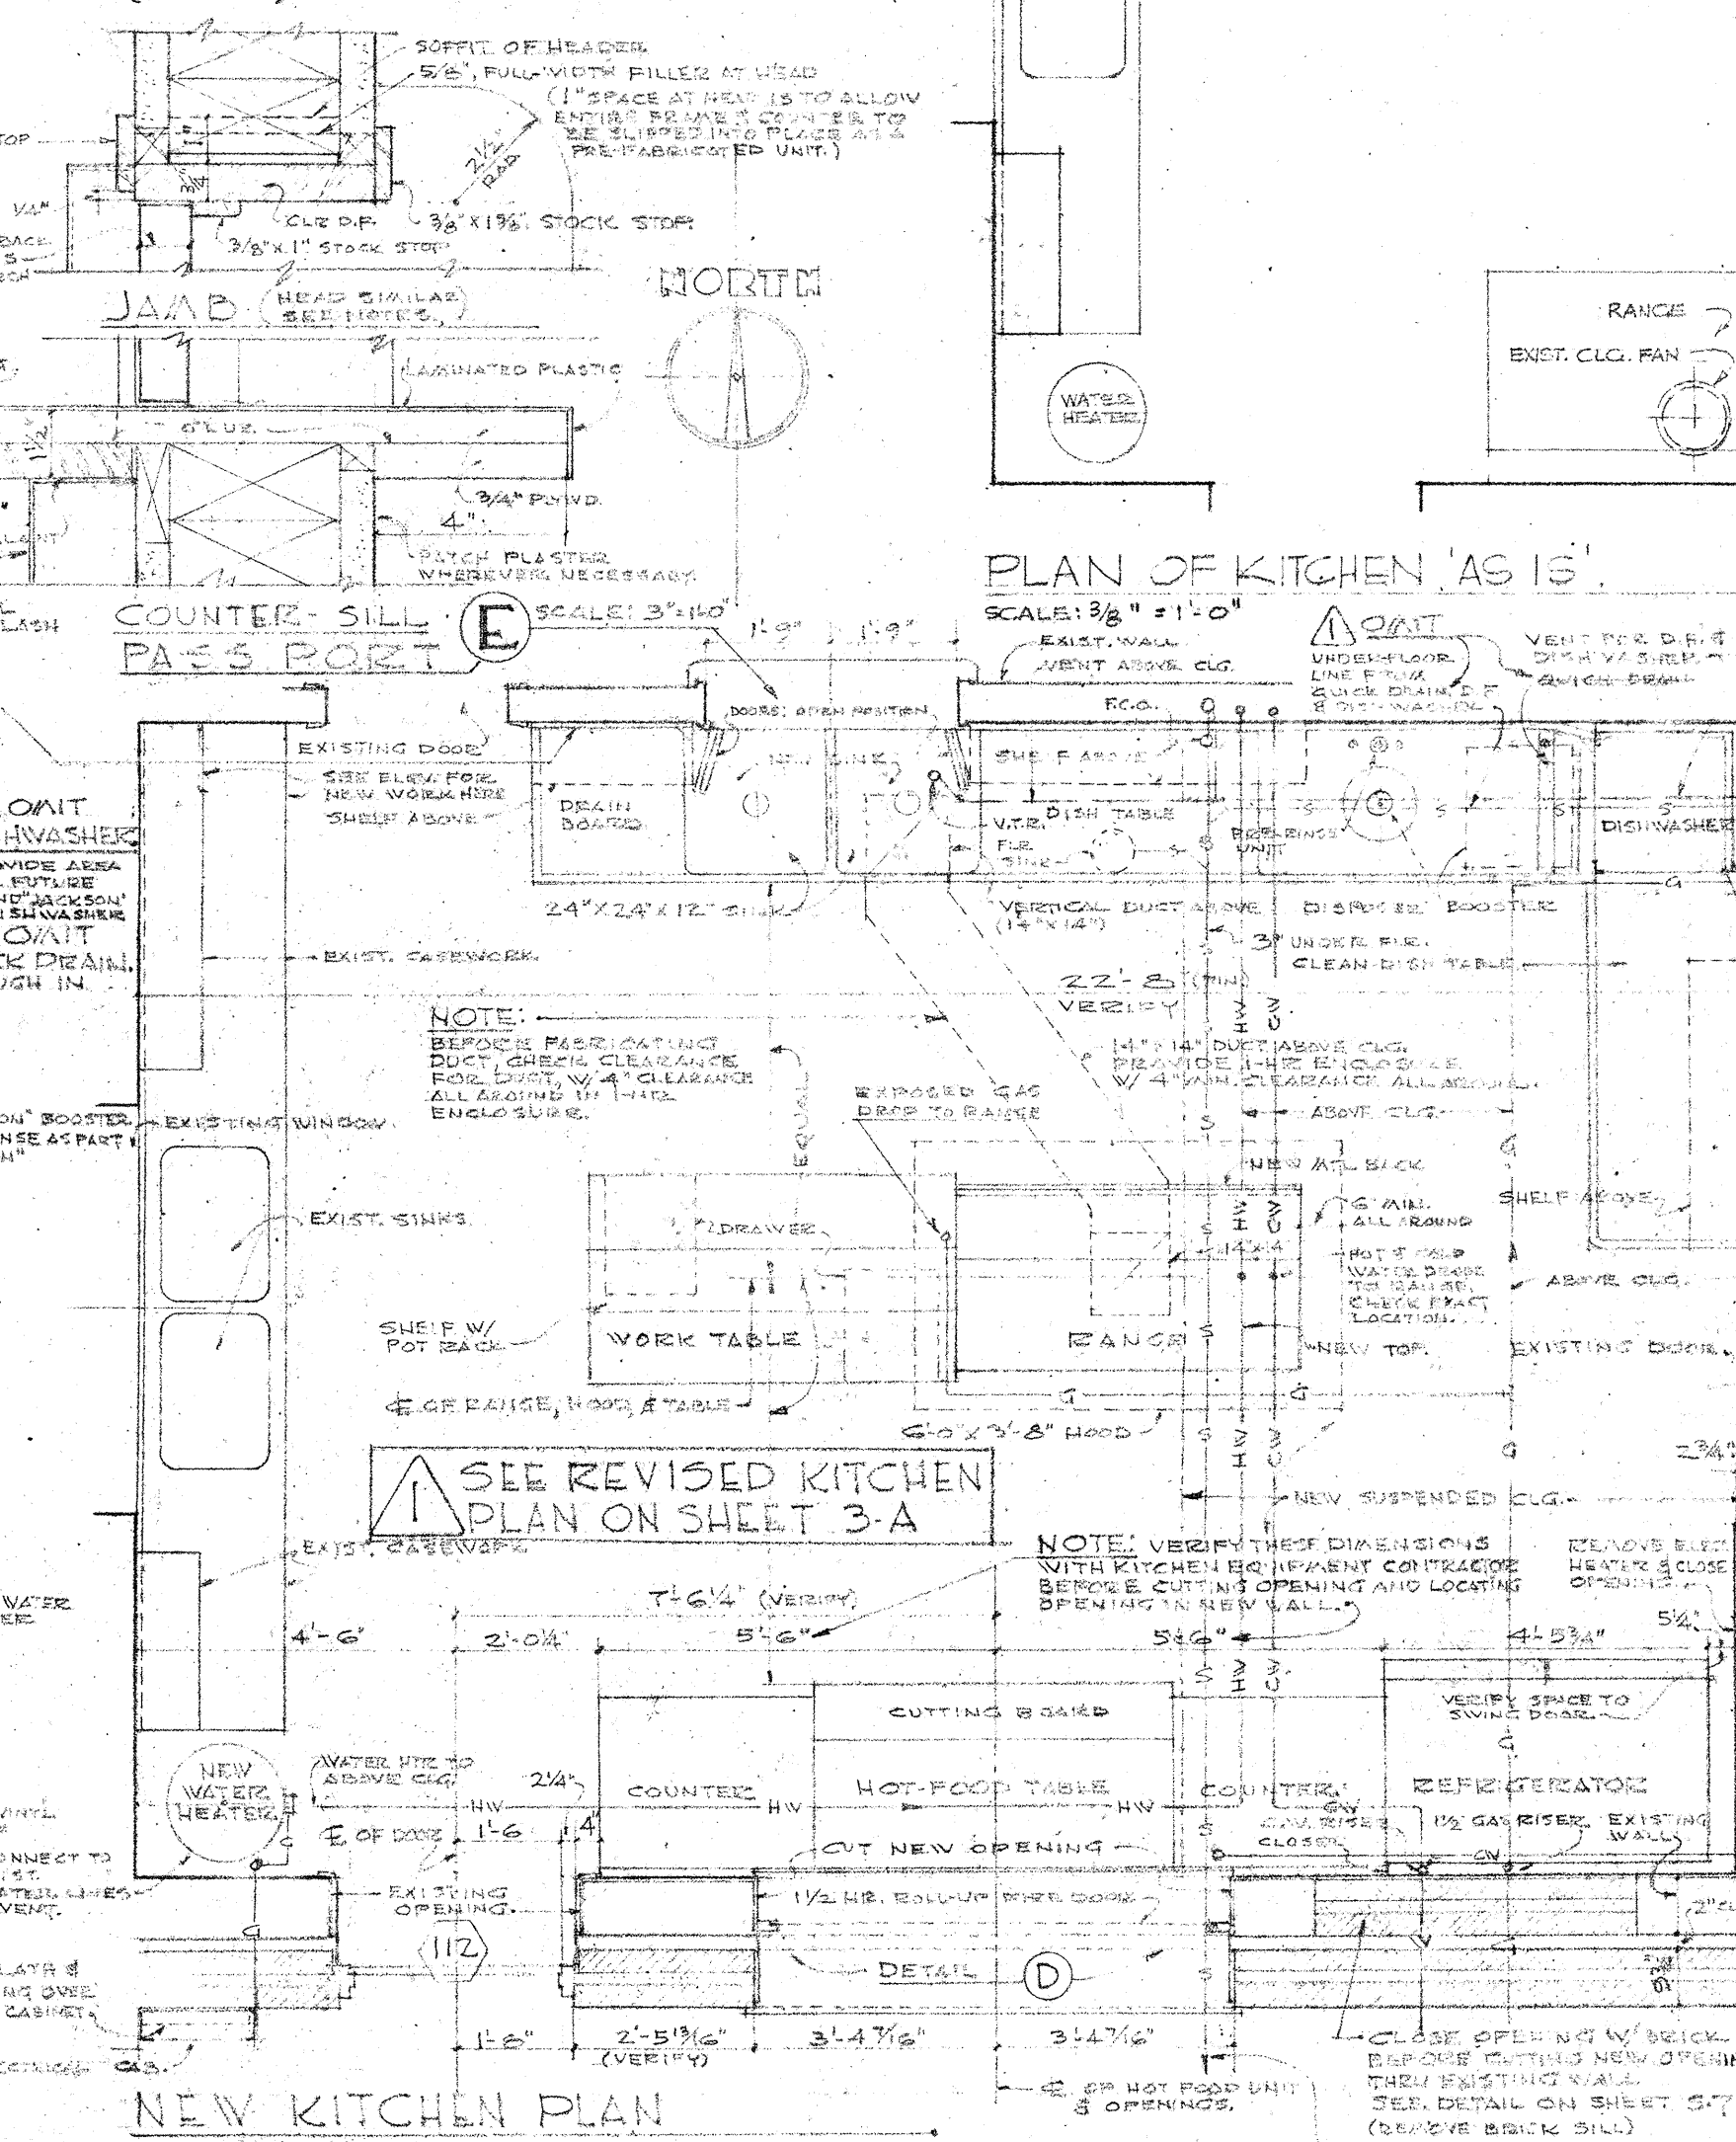


NEW KITCHEN PLAN
SCALE 3/8" = 1'-0"

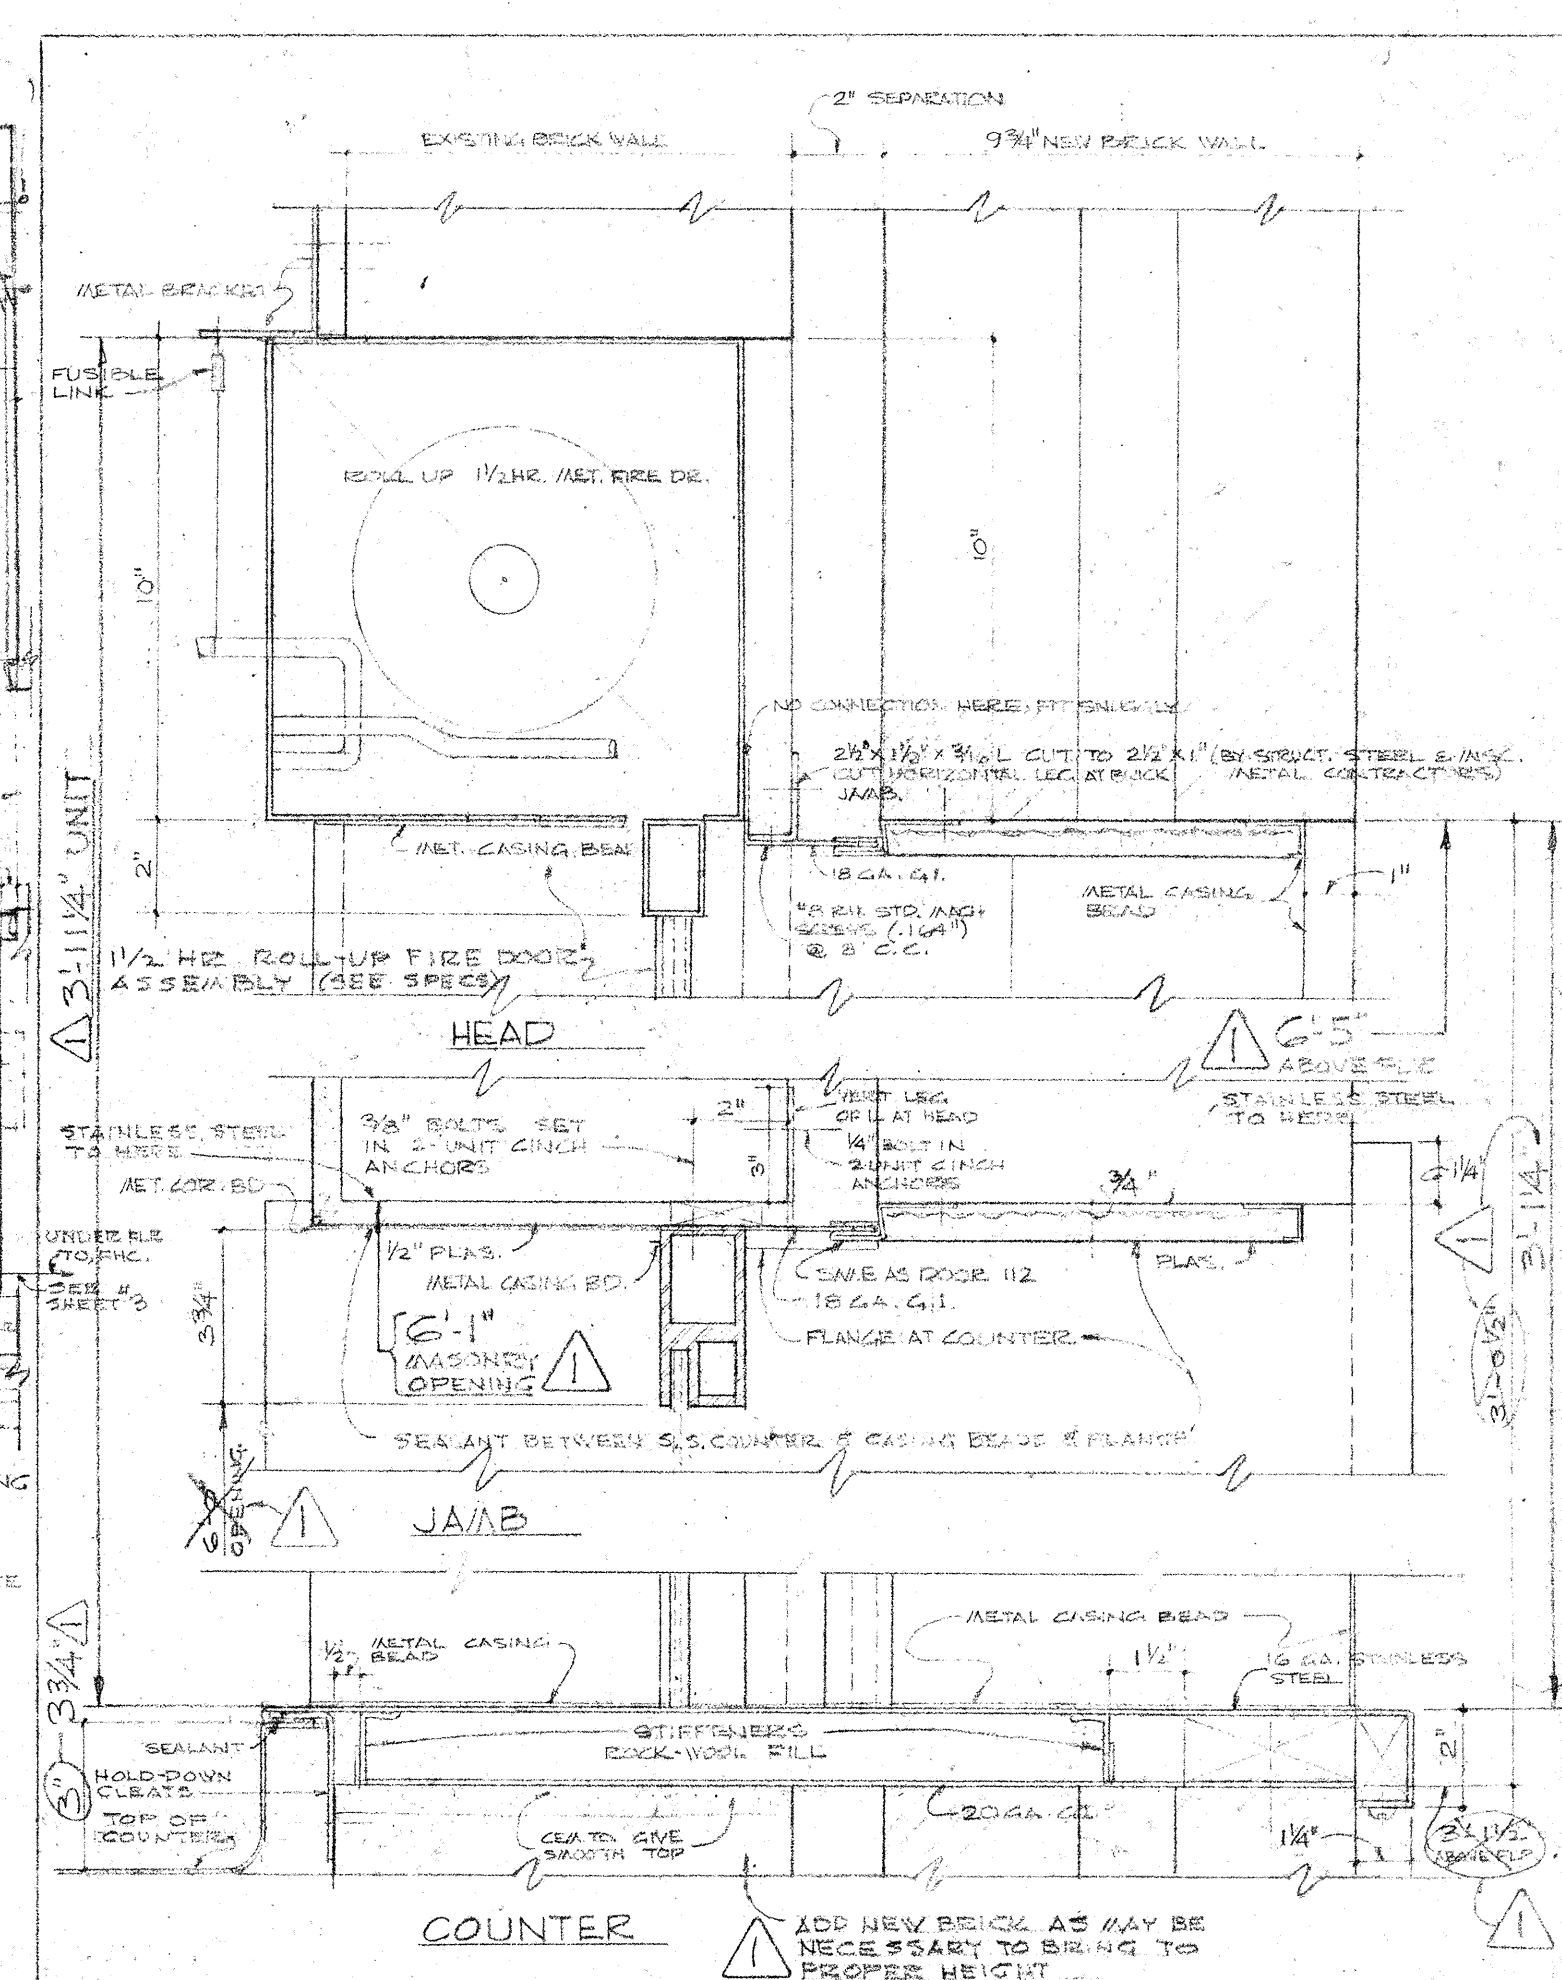


PASS PORT BETWEEN KITCHEN & PARISH HALL
SCALE 3/8" = 1'-0"

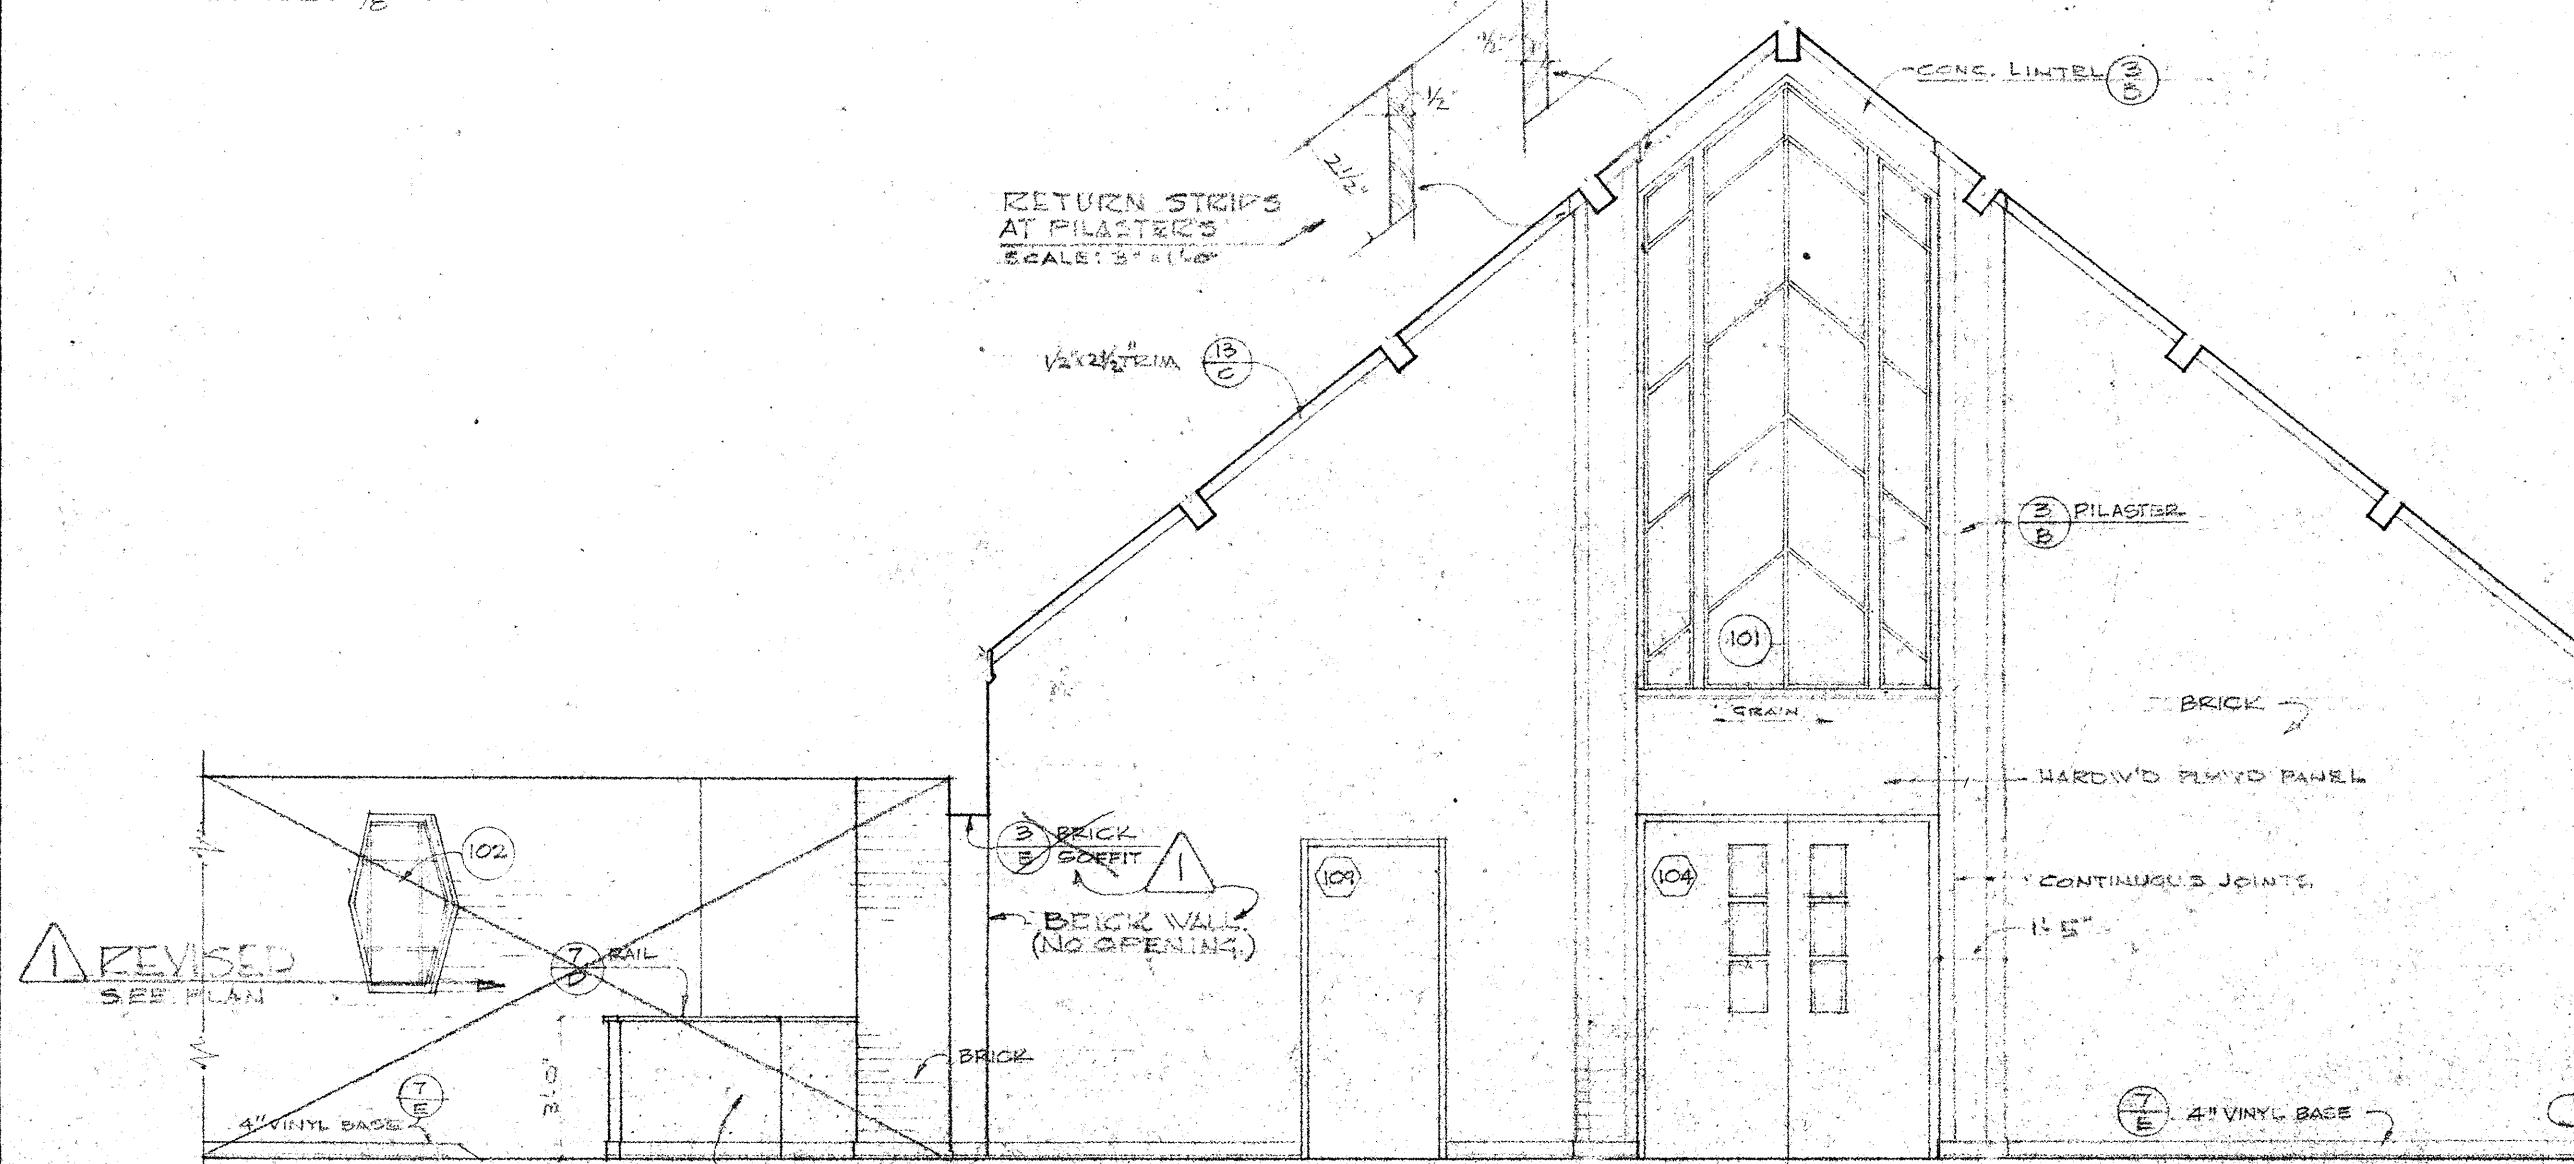

INTERIOR ELEVATION AT EAST WALL OF FOYER & PARISH HALL
SCALE 1/4" = 1'-0"

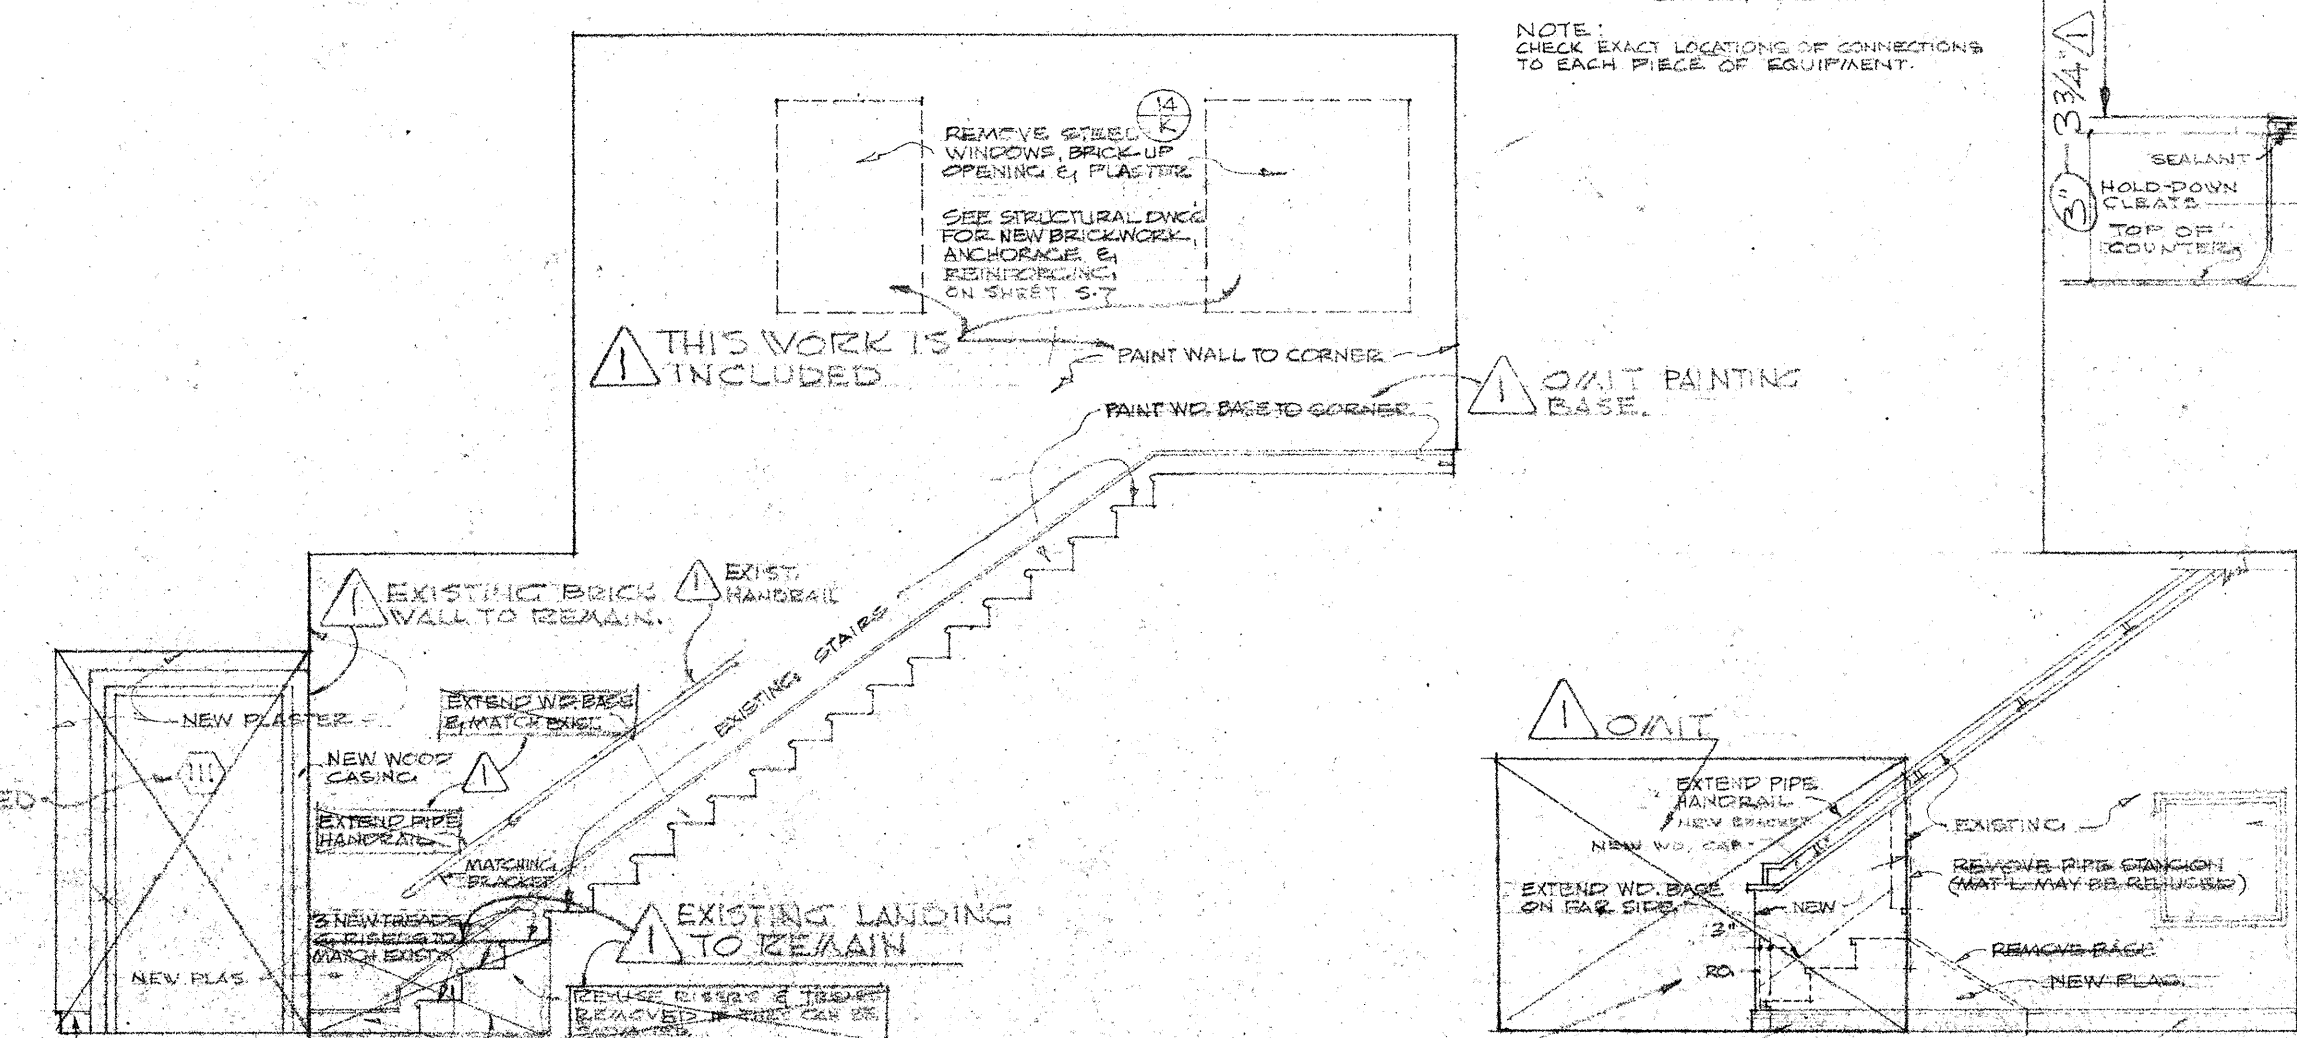

SECT. THRU EXISTING STAIRS W/ NEW STEPS ADDED
SCALE 1/4" = 1'-0"

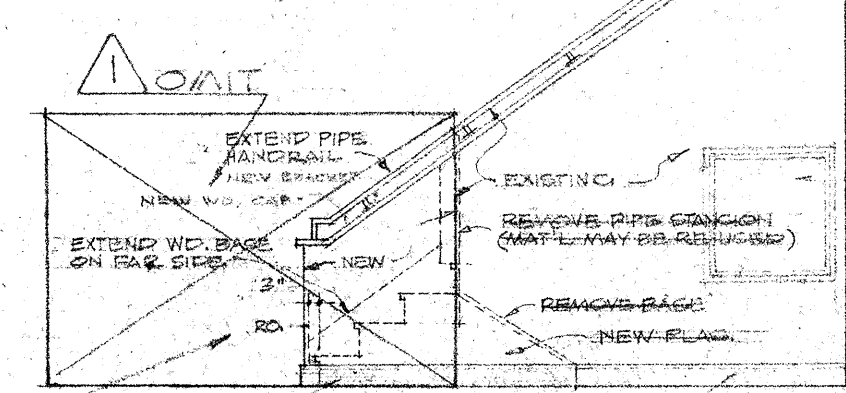

ELEV. OF ALTERED STAIRWAY

INTERIORS			
REVISIONS	DATE	BY	FOR
1	3-2-52	BF	PARISH HALL ADDITION
2	3-2-52	BF	ST. EDMUND'S EPISCOPAL CHURCH
3	3-2-52	BF	1175 SAN CARLOS BLVD. SAN MARINO, CALIFORNIA
4	3-2-52	BF	BREO FREEMAN ARCHITECT
5	3-2-52	BF	45 SOUTH MARENGO PASADENA 1, CALIFORNIA
6	3-2-52	BF	DATE 12-30-55
7	3-2-52	BF	JOB NO. 927
8	3-2-52	BF	SHEET NO. 10
9	3-2-52	BF	OF 10