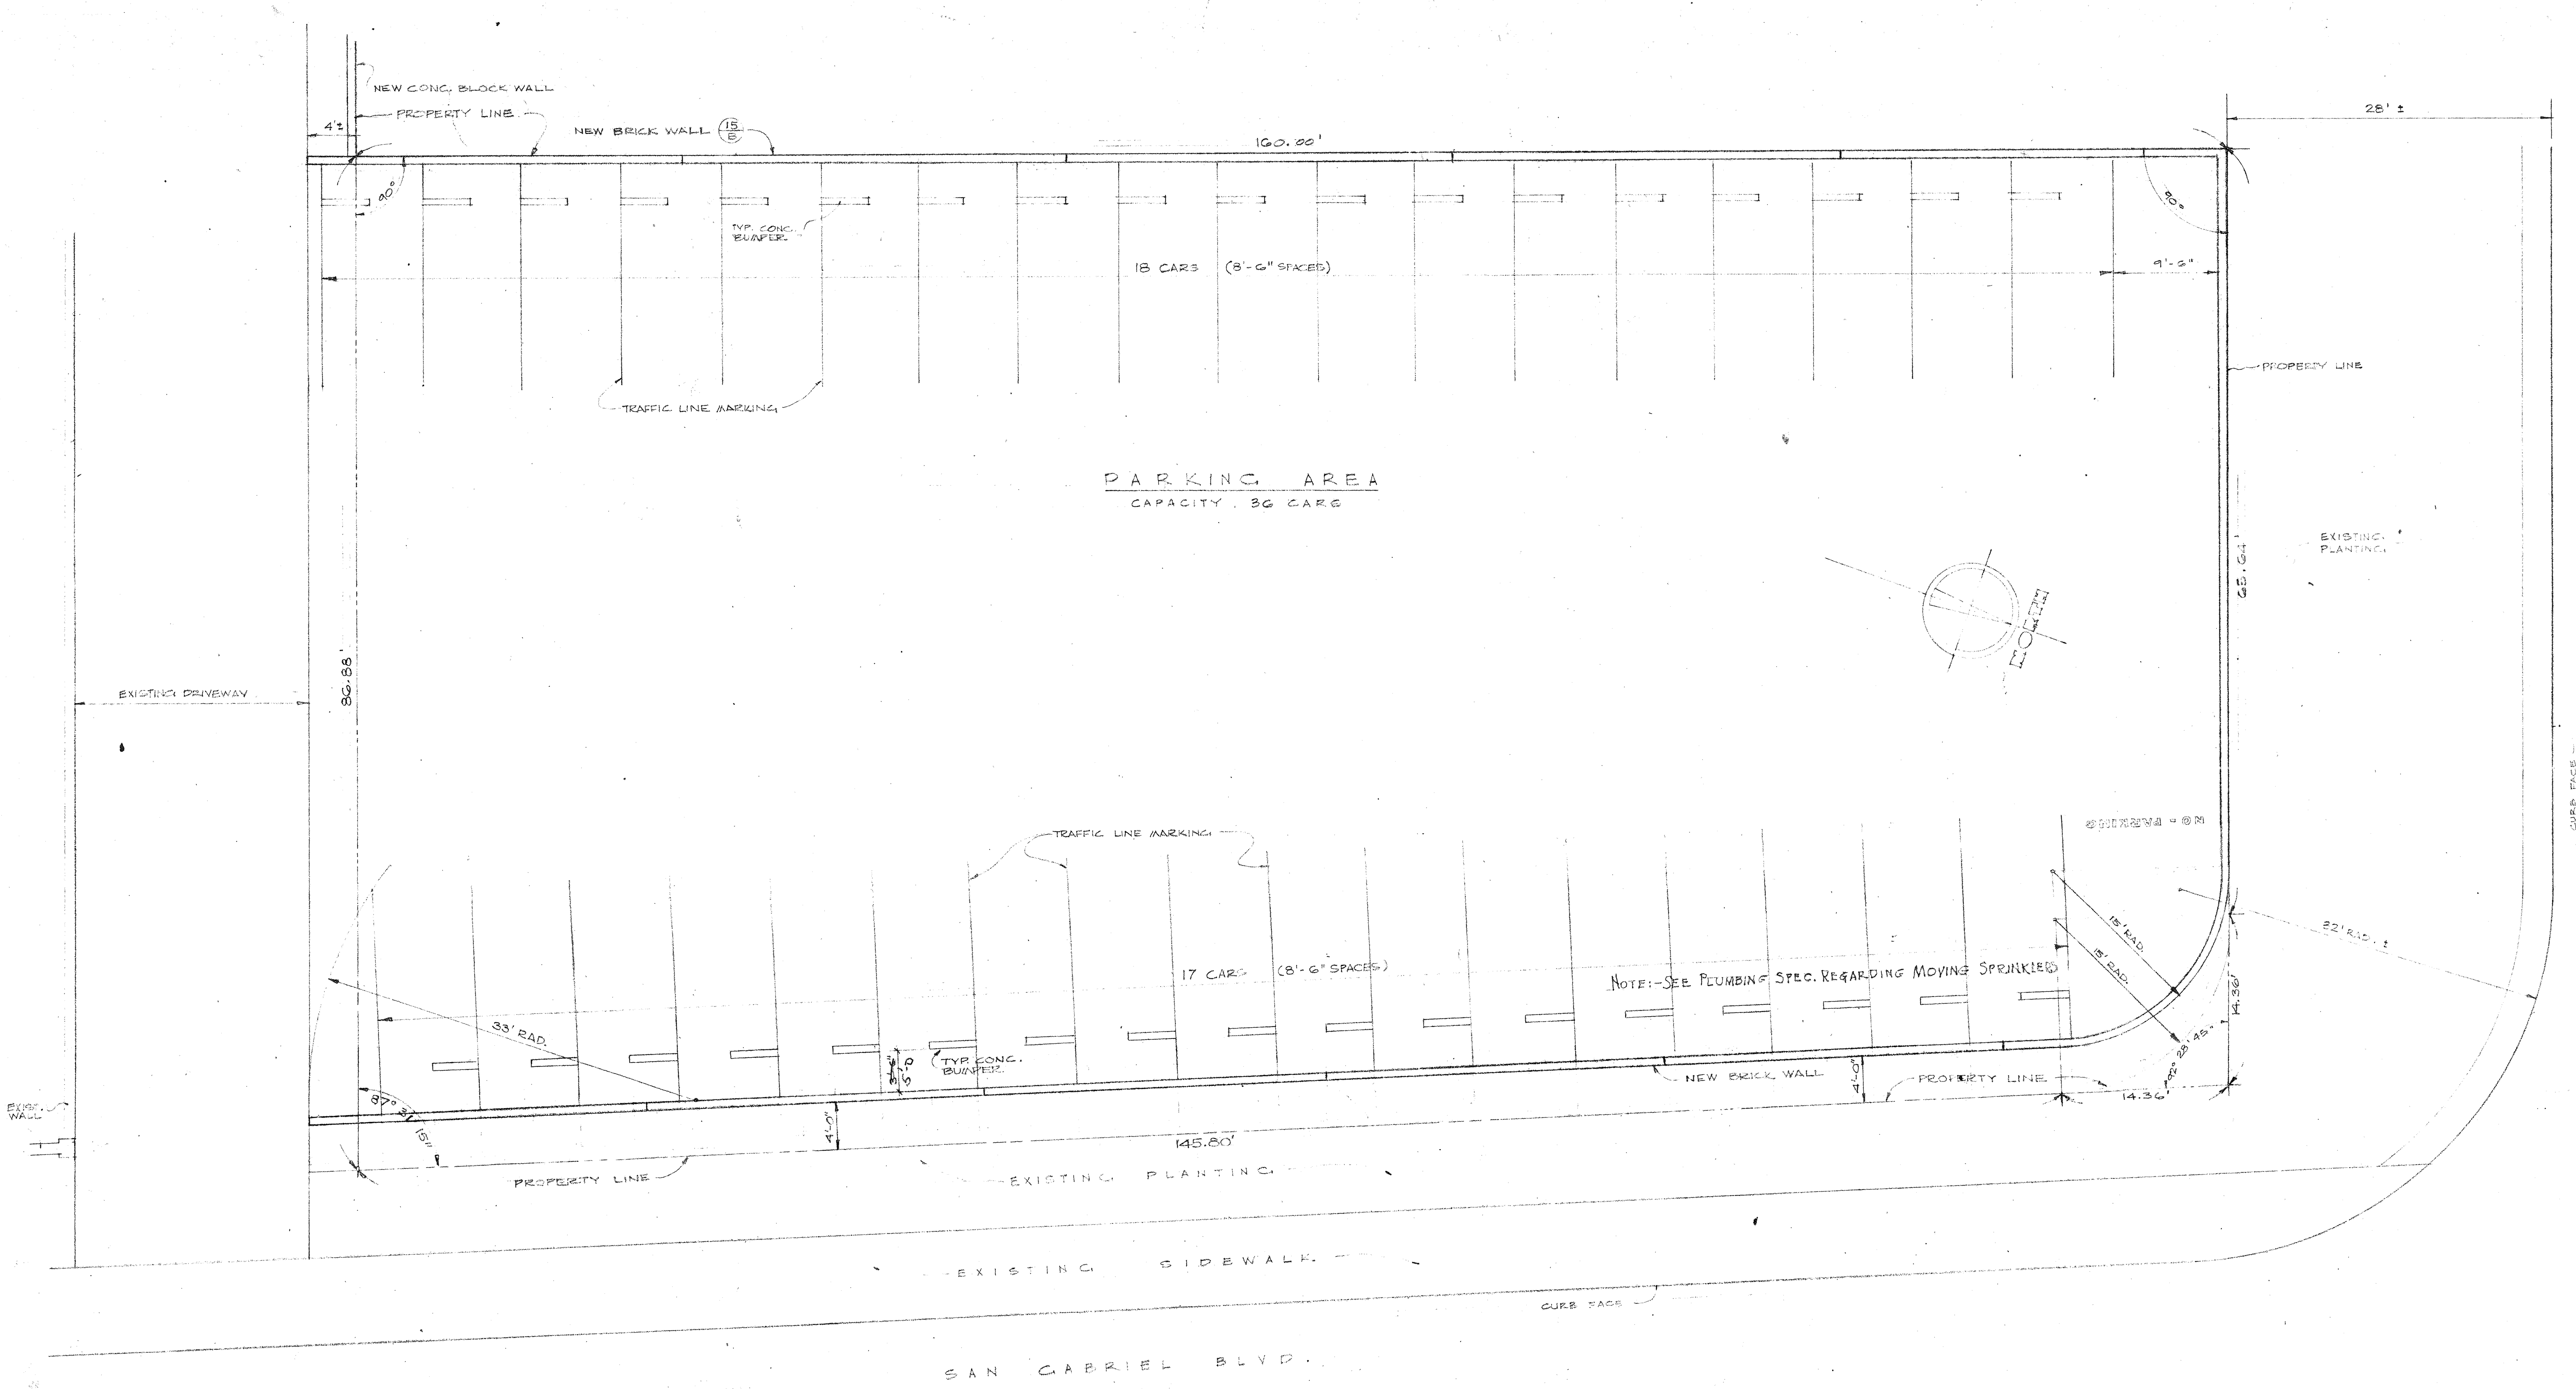

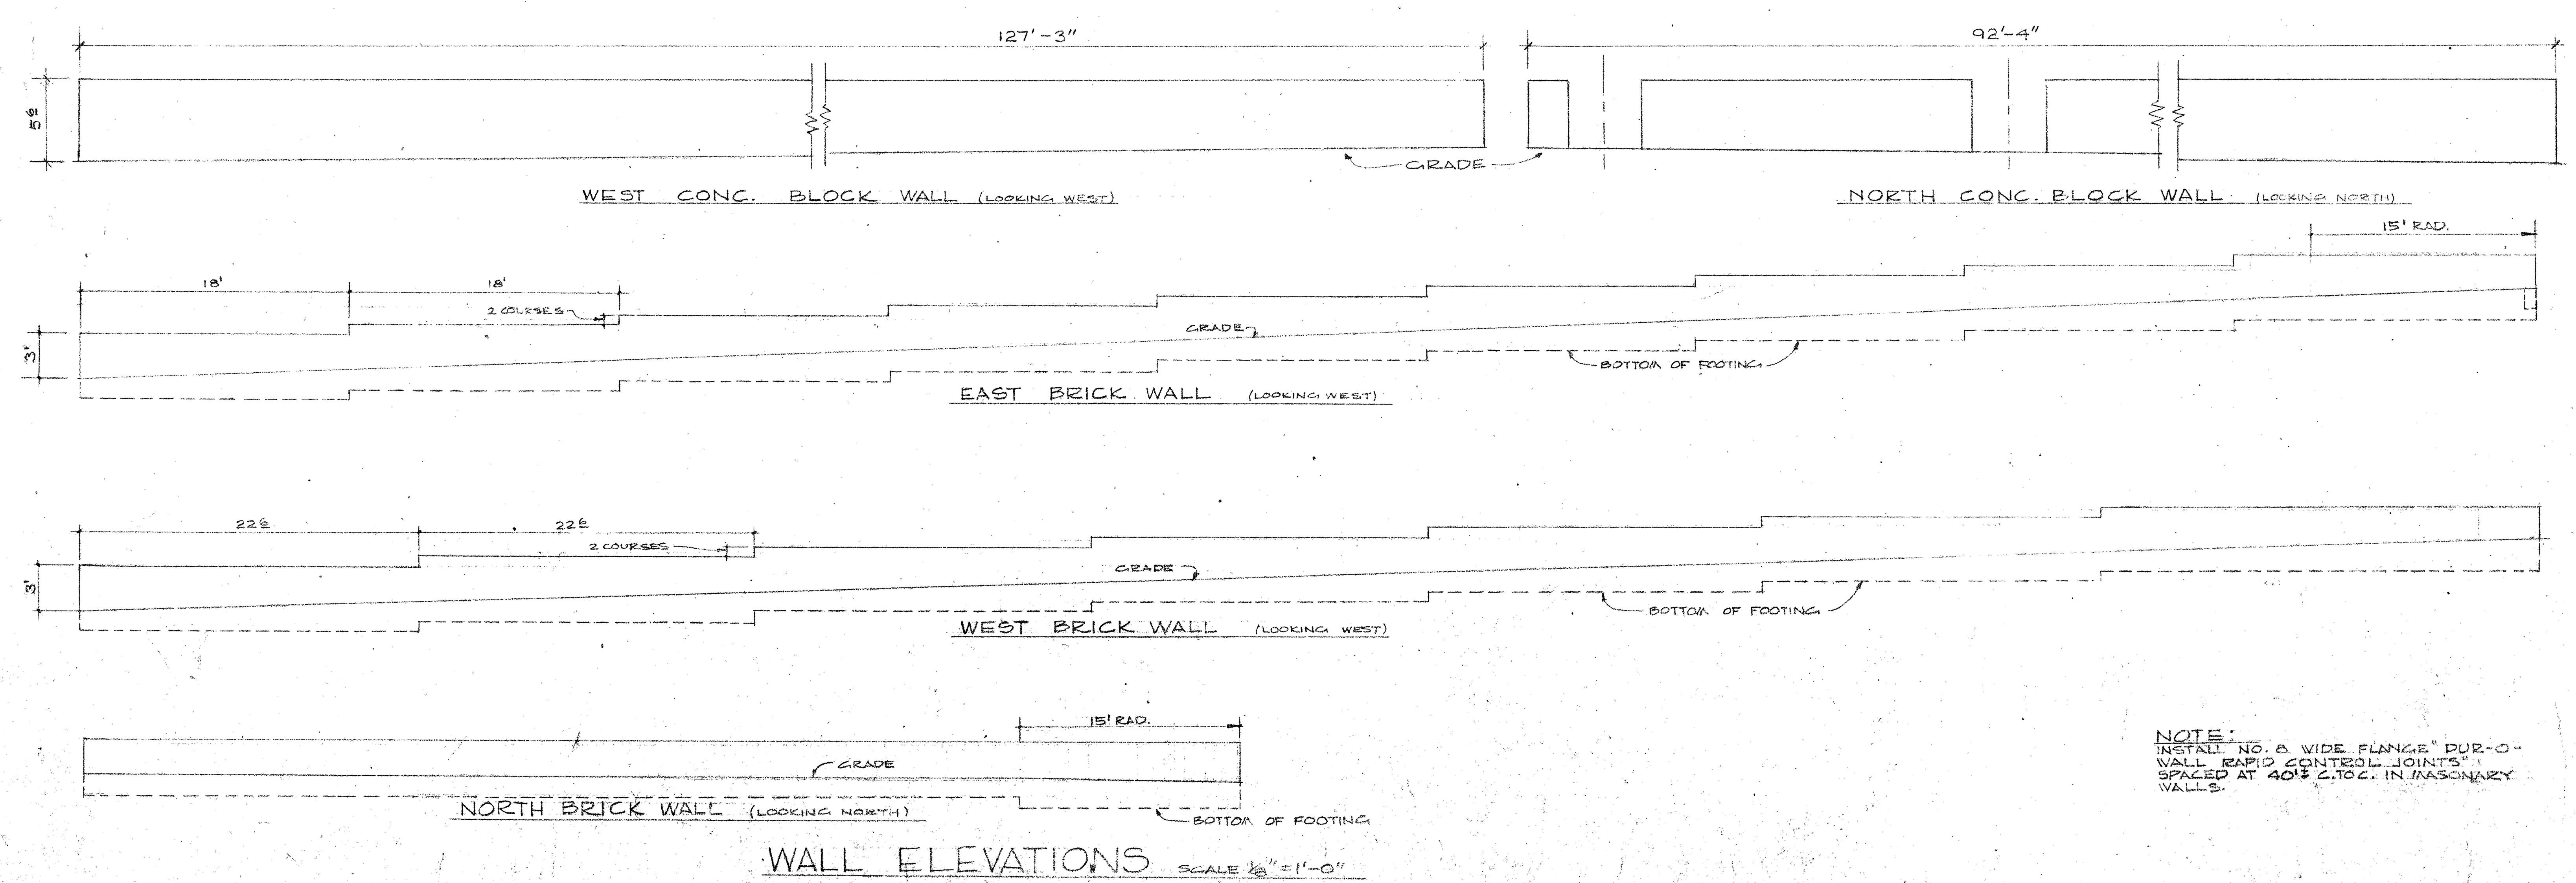

NOTE:
INSTALL NO. 6 WIDE FLANGE "DUR-O-WALL RAPID CONTROL JOINTS" SPACED AT 40'± C.TO C. IN MASONARY WALLS.

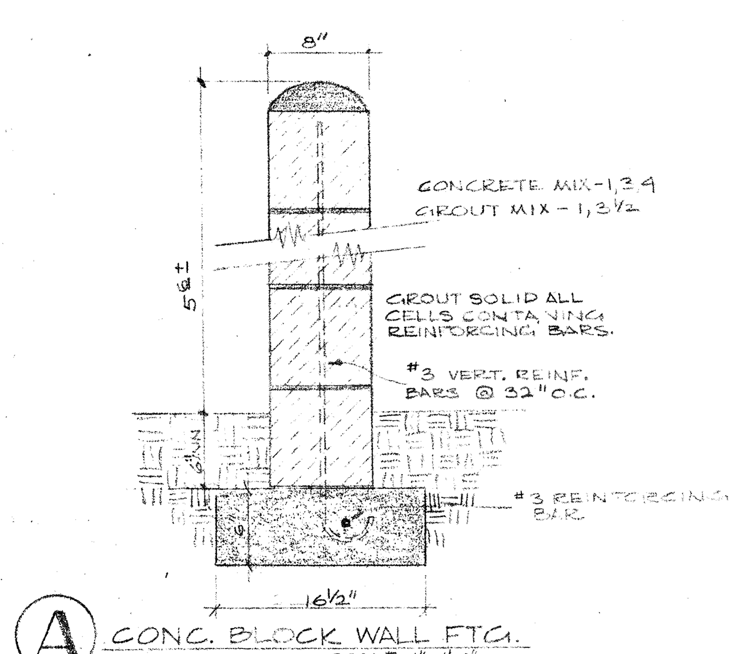

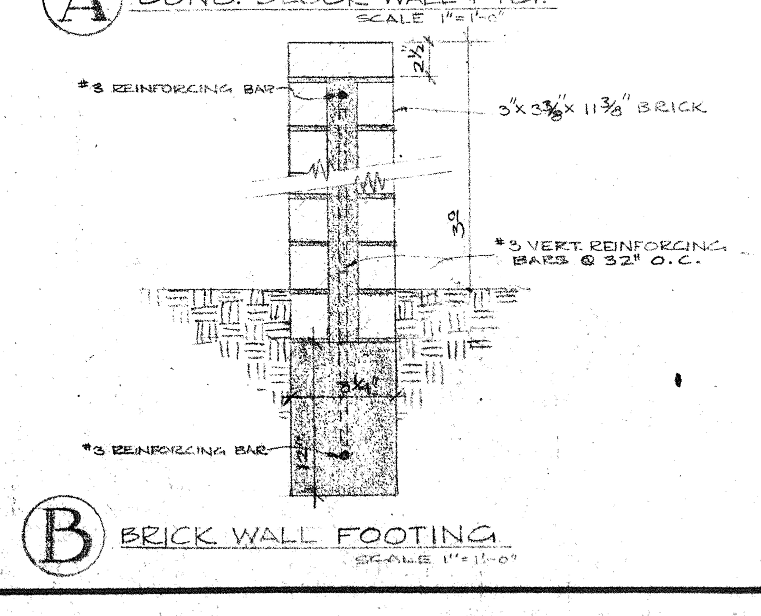

PARKING AREA

SCALE 1/8"=1'-0"

LEGAL DESCRIPTION: (THIS LOT ONLY!)
TRACT # 8329 LOT ON SE LINE OF GAINSBOROUGH DR. COM. NE AT R/A 295 FT. FROM C/L OF PALOMAR RD TH NE ON SD SE LINE 65.625 FT. TH SE ON A CURVE CONCAVE TO SW RAD. EQ. 15 FT., 22.91 FT, TH S. 22° 09'30" E. 145.79 FT. TH S 70° 19'15" W TO A PT. S 19° 40'45" E FROM BEG. TH NW TO BEG. PART OF LOT B.

ABBREVIATIONS

ALUM.	ALUMINUM
APPROX.	APPROXIMATE
BD.	BEAD
BLDG.	BUILDING
BLK.	BLOCK
BLKG.	BLOCKING
BM.	BEAM
CEIL.	CEILING
CER.	CERAMIC
C.I.	CAST IRON
CLG.	CEILING
CLR.	CLEAR
℄	CENTER LINE
C.O.	CLEAN OUT
COL.	COLUMN
COMPO.	COMPOSITION
CONC.	CONCRETE
COND.	CONDITIONING
CONT.	CONTINUOUS
CONTR.	CONTRACTOR
COR.	CORNER
CSK.	COUNTERSUNK
DBLE	DOUBLE
D.F.	DOUGLAS FIR
DIA.	DIAMETER
DIAG.	DIAGONAL
DIM.	DIMENSION
DN	DOWN
DSB	DOUBLE STRENGTH 'B'
D.S.	DOWNSPOUT
DR.	DOOR
DTL.	DETAIL
DWGS	DRAWINGS
EA.	EACH
ELEC.	ELECTRIC
ELEV.	ELEVATION
EL.	ELEVATION
EQUIP	EQUIPMENT
EQ.	EQUAL
E.W.M.	ELECTRIC WELDED MESH
EXIST.	EXISTING
EXT.	EXTERIOR
F.H.	FLAT HEAD
FIN.	FINISH
FLR.	FLOOR
FNDN.	FOUNDATION
F.O.S.	FACE OF STUDS
F.S.	FULL SIZE
FTG(S)	FOOTING(S)
GA.	GAUGE
GALV.	GALVANIZED
G.I.	GALVANIZED IRON
GL.	GLASS
GR.	GRADE
GRND	GROUND
GYP.	GYPSUM
HD.	HEAD
HDWD	HARDWOOD
HGT.	HEIGHT
HORIZ.	HORIZONTAL
HR.	HOUR
HTR.	HEATER
LOC	LOCATION
MATL.	MATERIAL
MAX.	MAXIMUM
MECH.	MECHANICAL
MFGR.	MANUFACTURER
MIN.	MINIMUM
M.O.	MASONRY OPENING
MTL.	METAL
MET.	METAL
N.I.C.	NOT IN CONTRACT
N.T.S.	NOT TO SCALE
O.A.	OVERALL
O.C.	ON CENTER
OPG.	OPENING
PL.	PLATE
PLAS.	PLASTER
PLY.	PLYWOOD
PLYWD.	PLYWOOD
PROP.	PROPERTY
PT.	POINT
R.	RISERS
RAD.	RADIUS
REFRIG.	REFRIGERATOR
REG.	REGISTER
REQ.	REQUIRED
R.H.	ROUND HEAD
RM.	ROOM
RND.	ROUND
RO.	ROUGH
RWD.	REDWOOD
SCHED.	SCHEDULE
SCR.	SCREW
SCRN.	SCREEN
SECT.	SECTION
SPECS.	SPECIFICATIONS
STD.	STANDARD
STL.	STEEL
STRUCT.	STRUCTURAL
SYM.	SYMBOL
SEP.	SEPARATION
T.	TREADS
T & G	TONGUE & GROOVE
THKNS	THICKNESS
TYP.	TYPICAL
T.P.	TOP OF PAVING
VERT.	VERTICAL
VEST.	VESTIBULE
W/	WITH
WD.	WOOD
WTR.	WATER

PARKING AREA & ABBREVIATIONS

REVISIONS	PARISH HALL ADDITION for ST. EDMUND'S EPISCOPAL CHURCH, 1175 SAN GABRIEL BLVD., SAN MARINO, CALIFORNIA		
3-31-66	DRAWN BY: G.F.G.	BREO FREEMAN ARCHITECT	JOB NO. 927
	TRACED BY: G.E.C.	45 SOUTH MARENGO	SHEET NO. 15
	DATE: 12-30-65	PASADENA 1, CALIFORNIA	19 of 26