




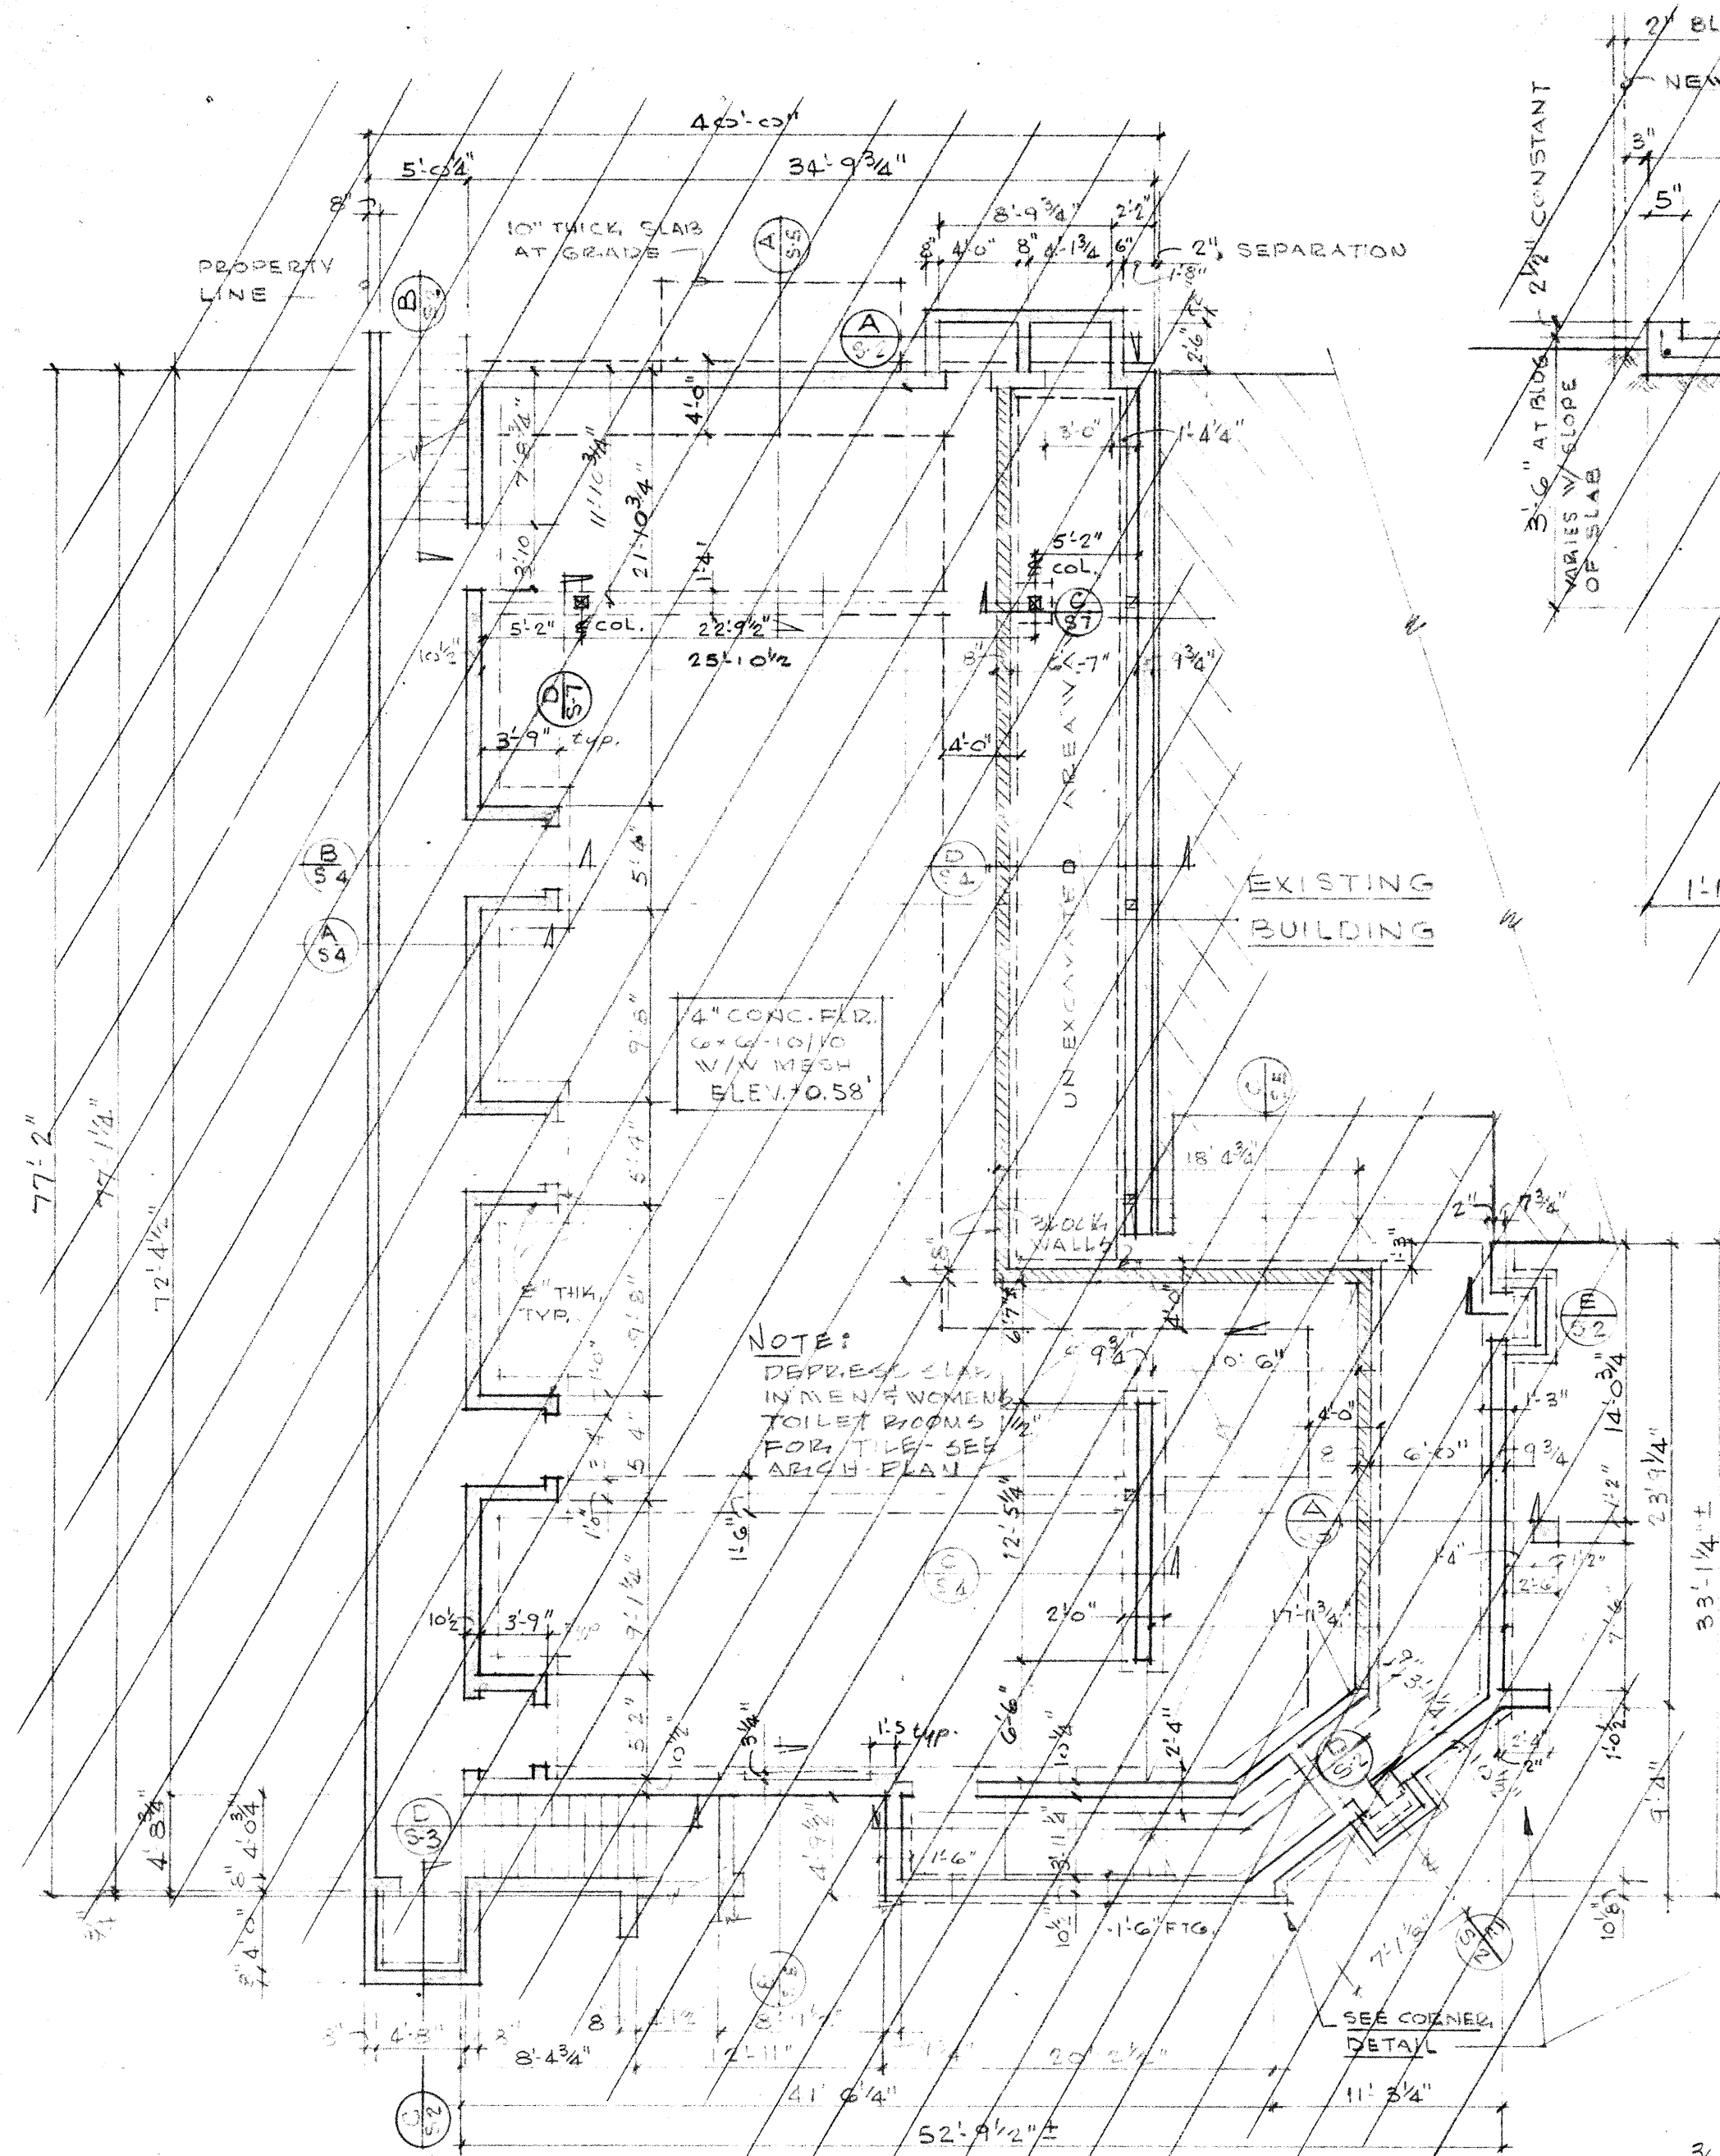


FOUNDATION PLAN

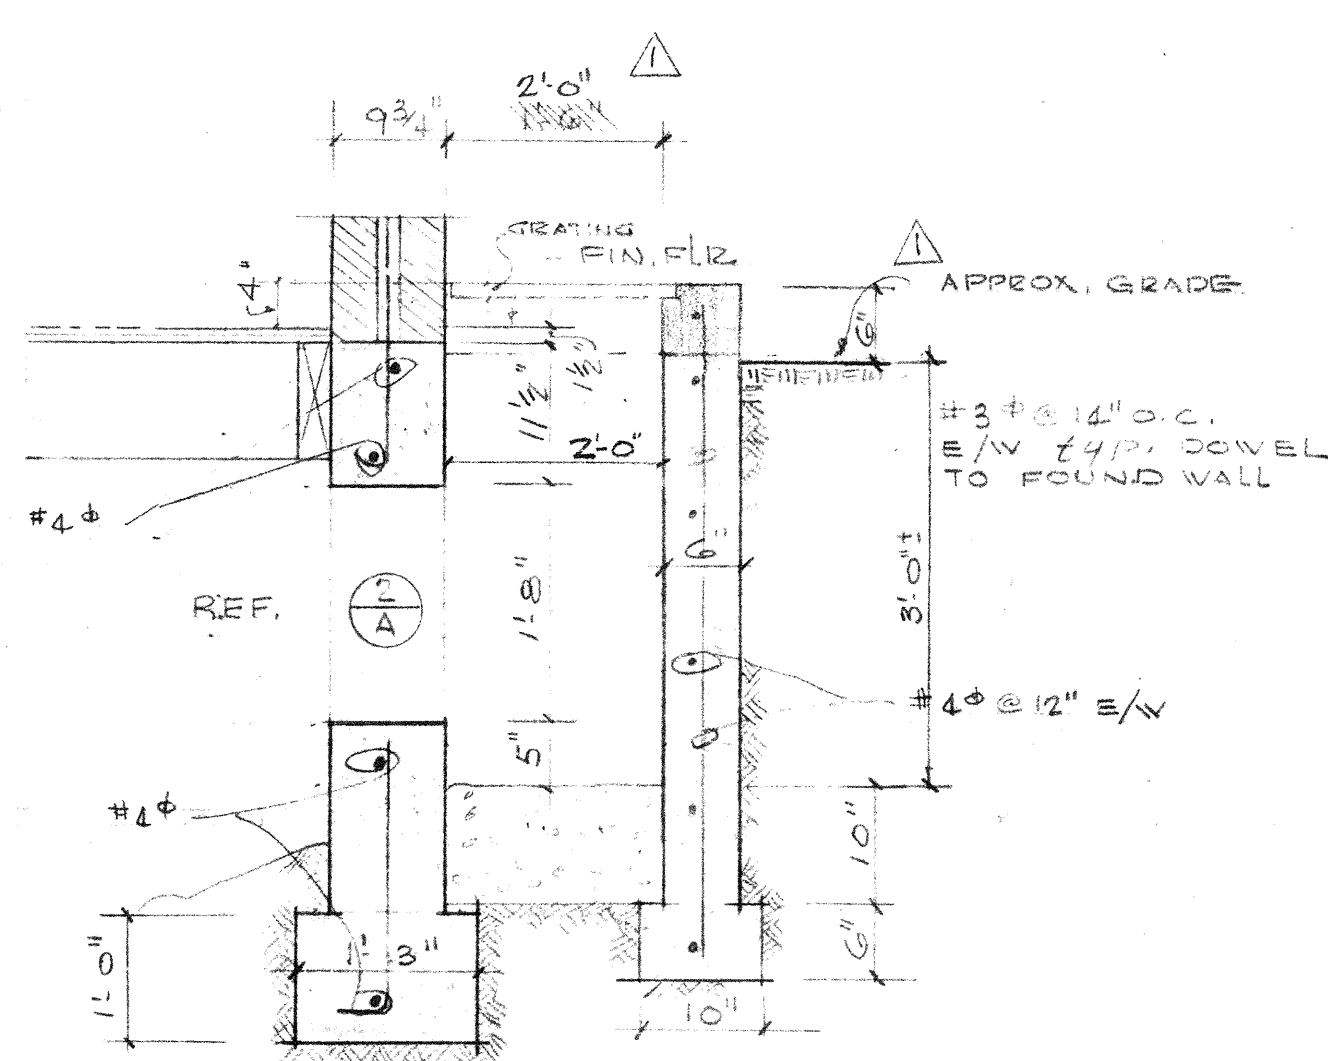


NORTH-EAST AREA VIEW

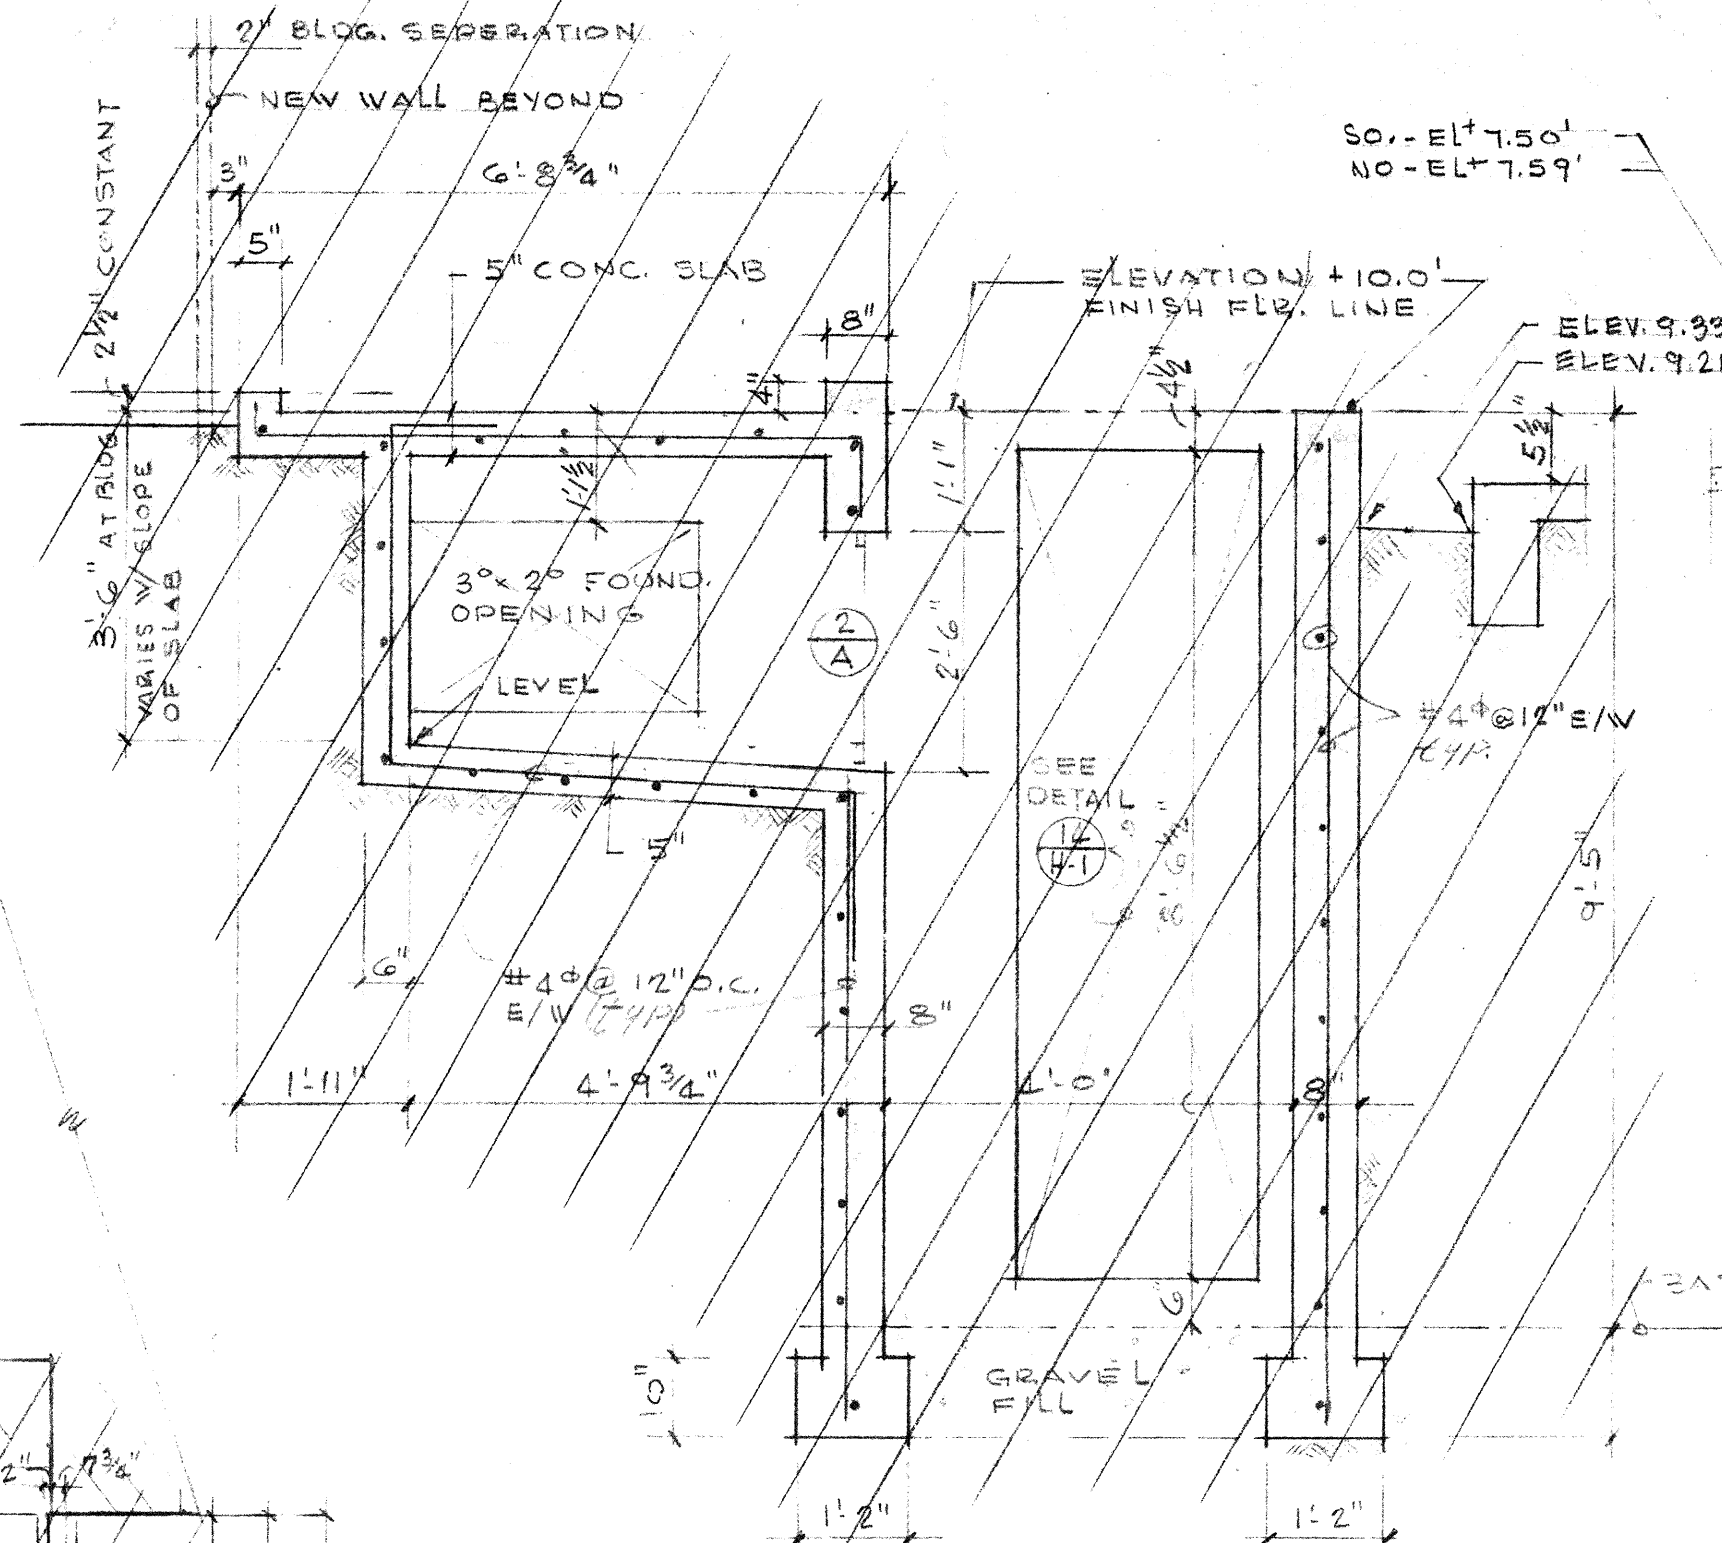


OMIT SECTION 1/2" = 1'-0"

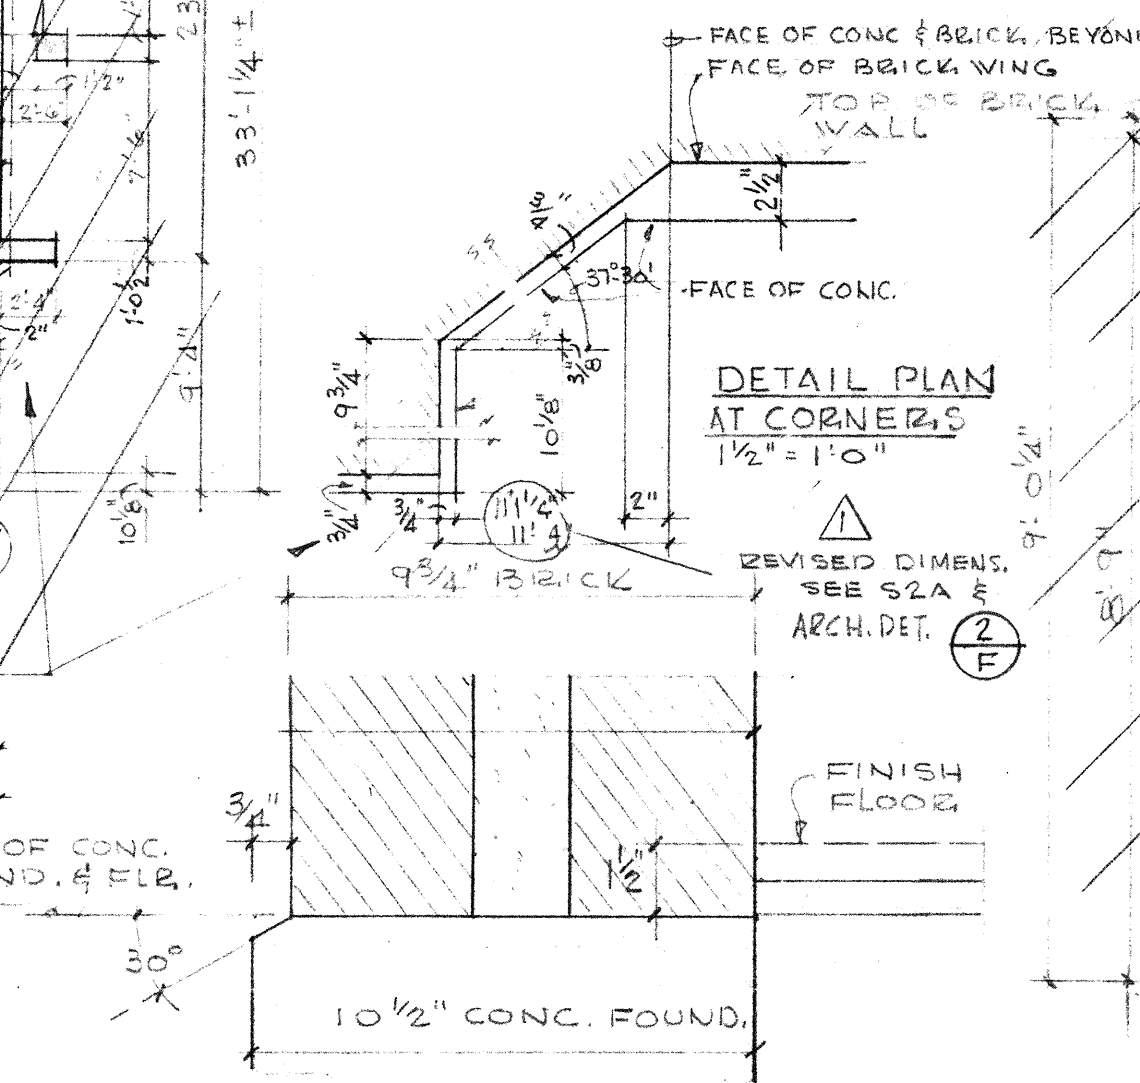


FOUND. TO BRICK WALL REFER. TO FLR. ELEV. 3" = 1'-0"

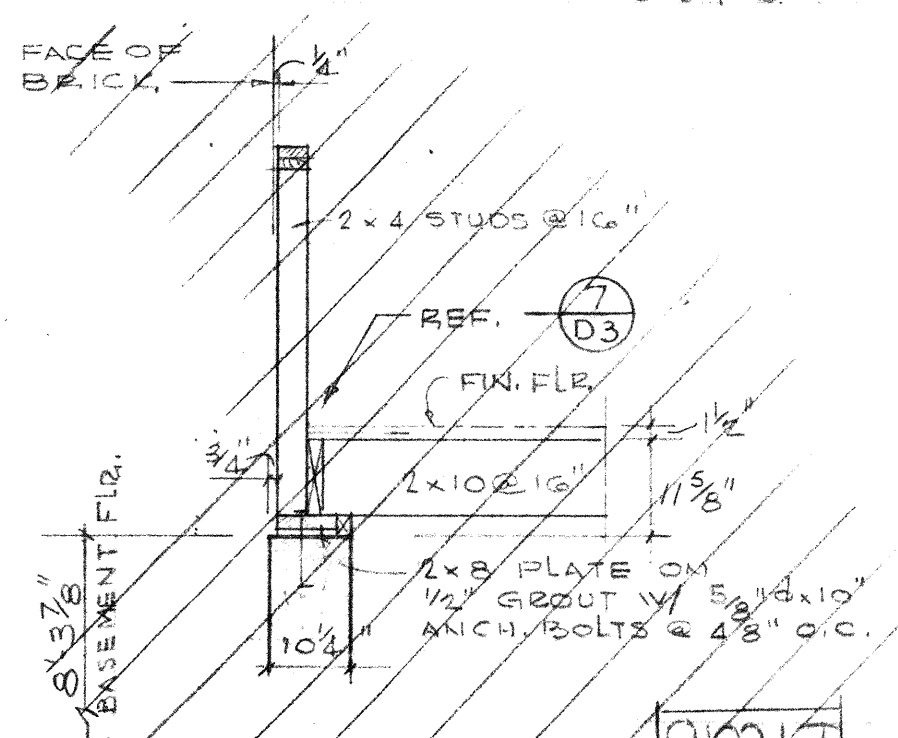


SECTION 1/2" = 1'-0"

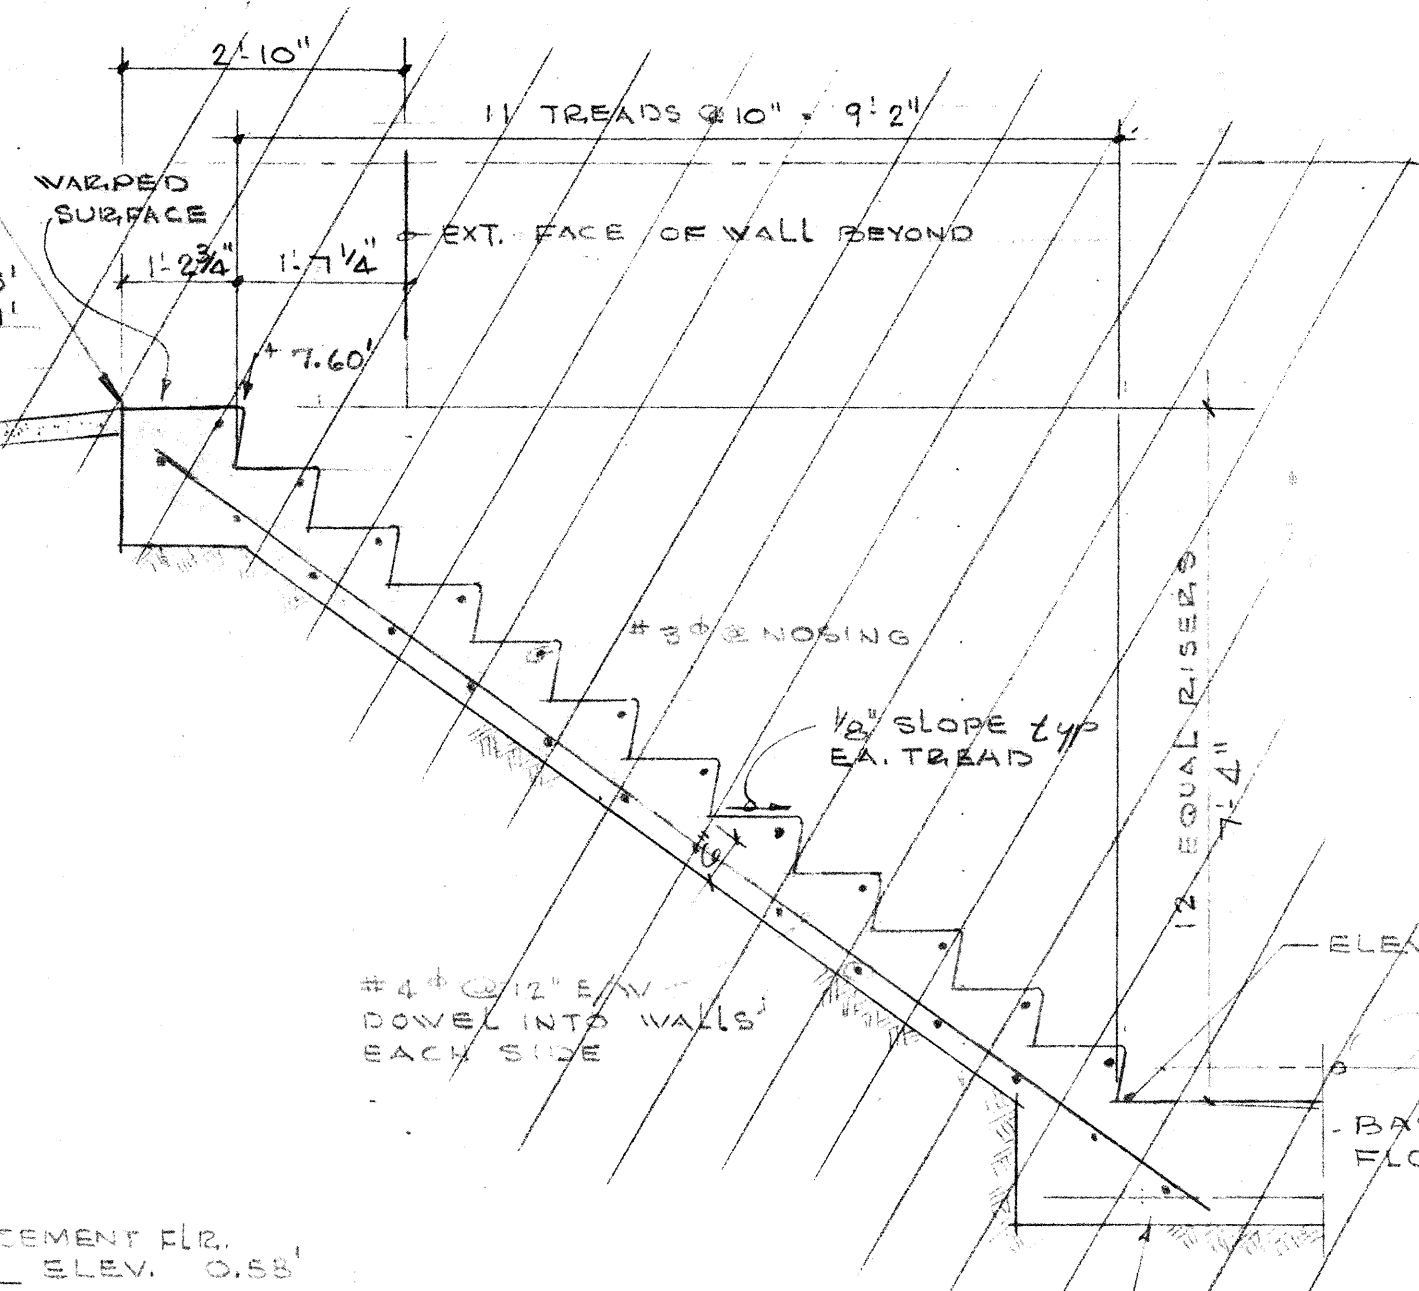

OMIT STAIR SECTION 1/2" = 1'-0"

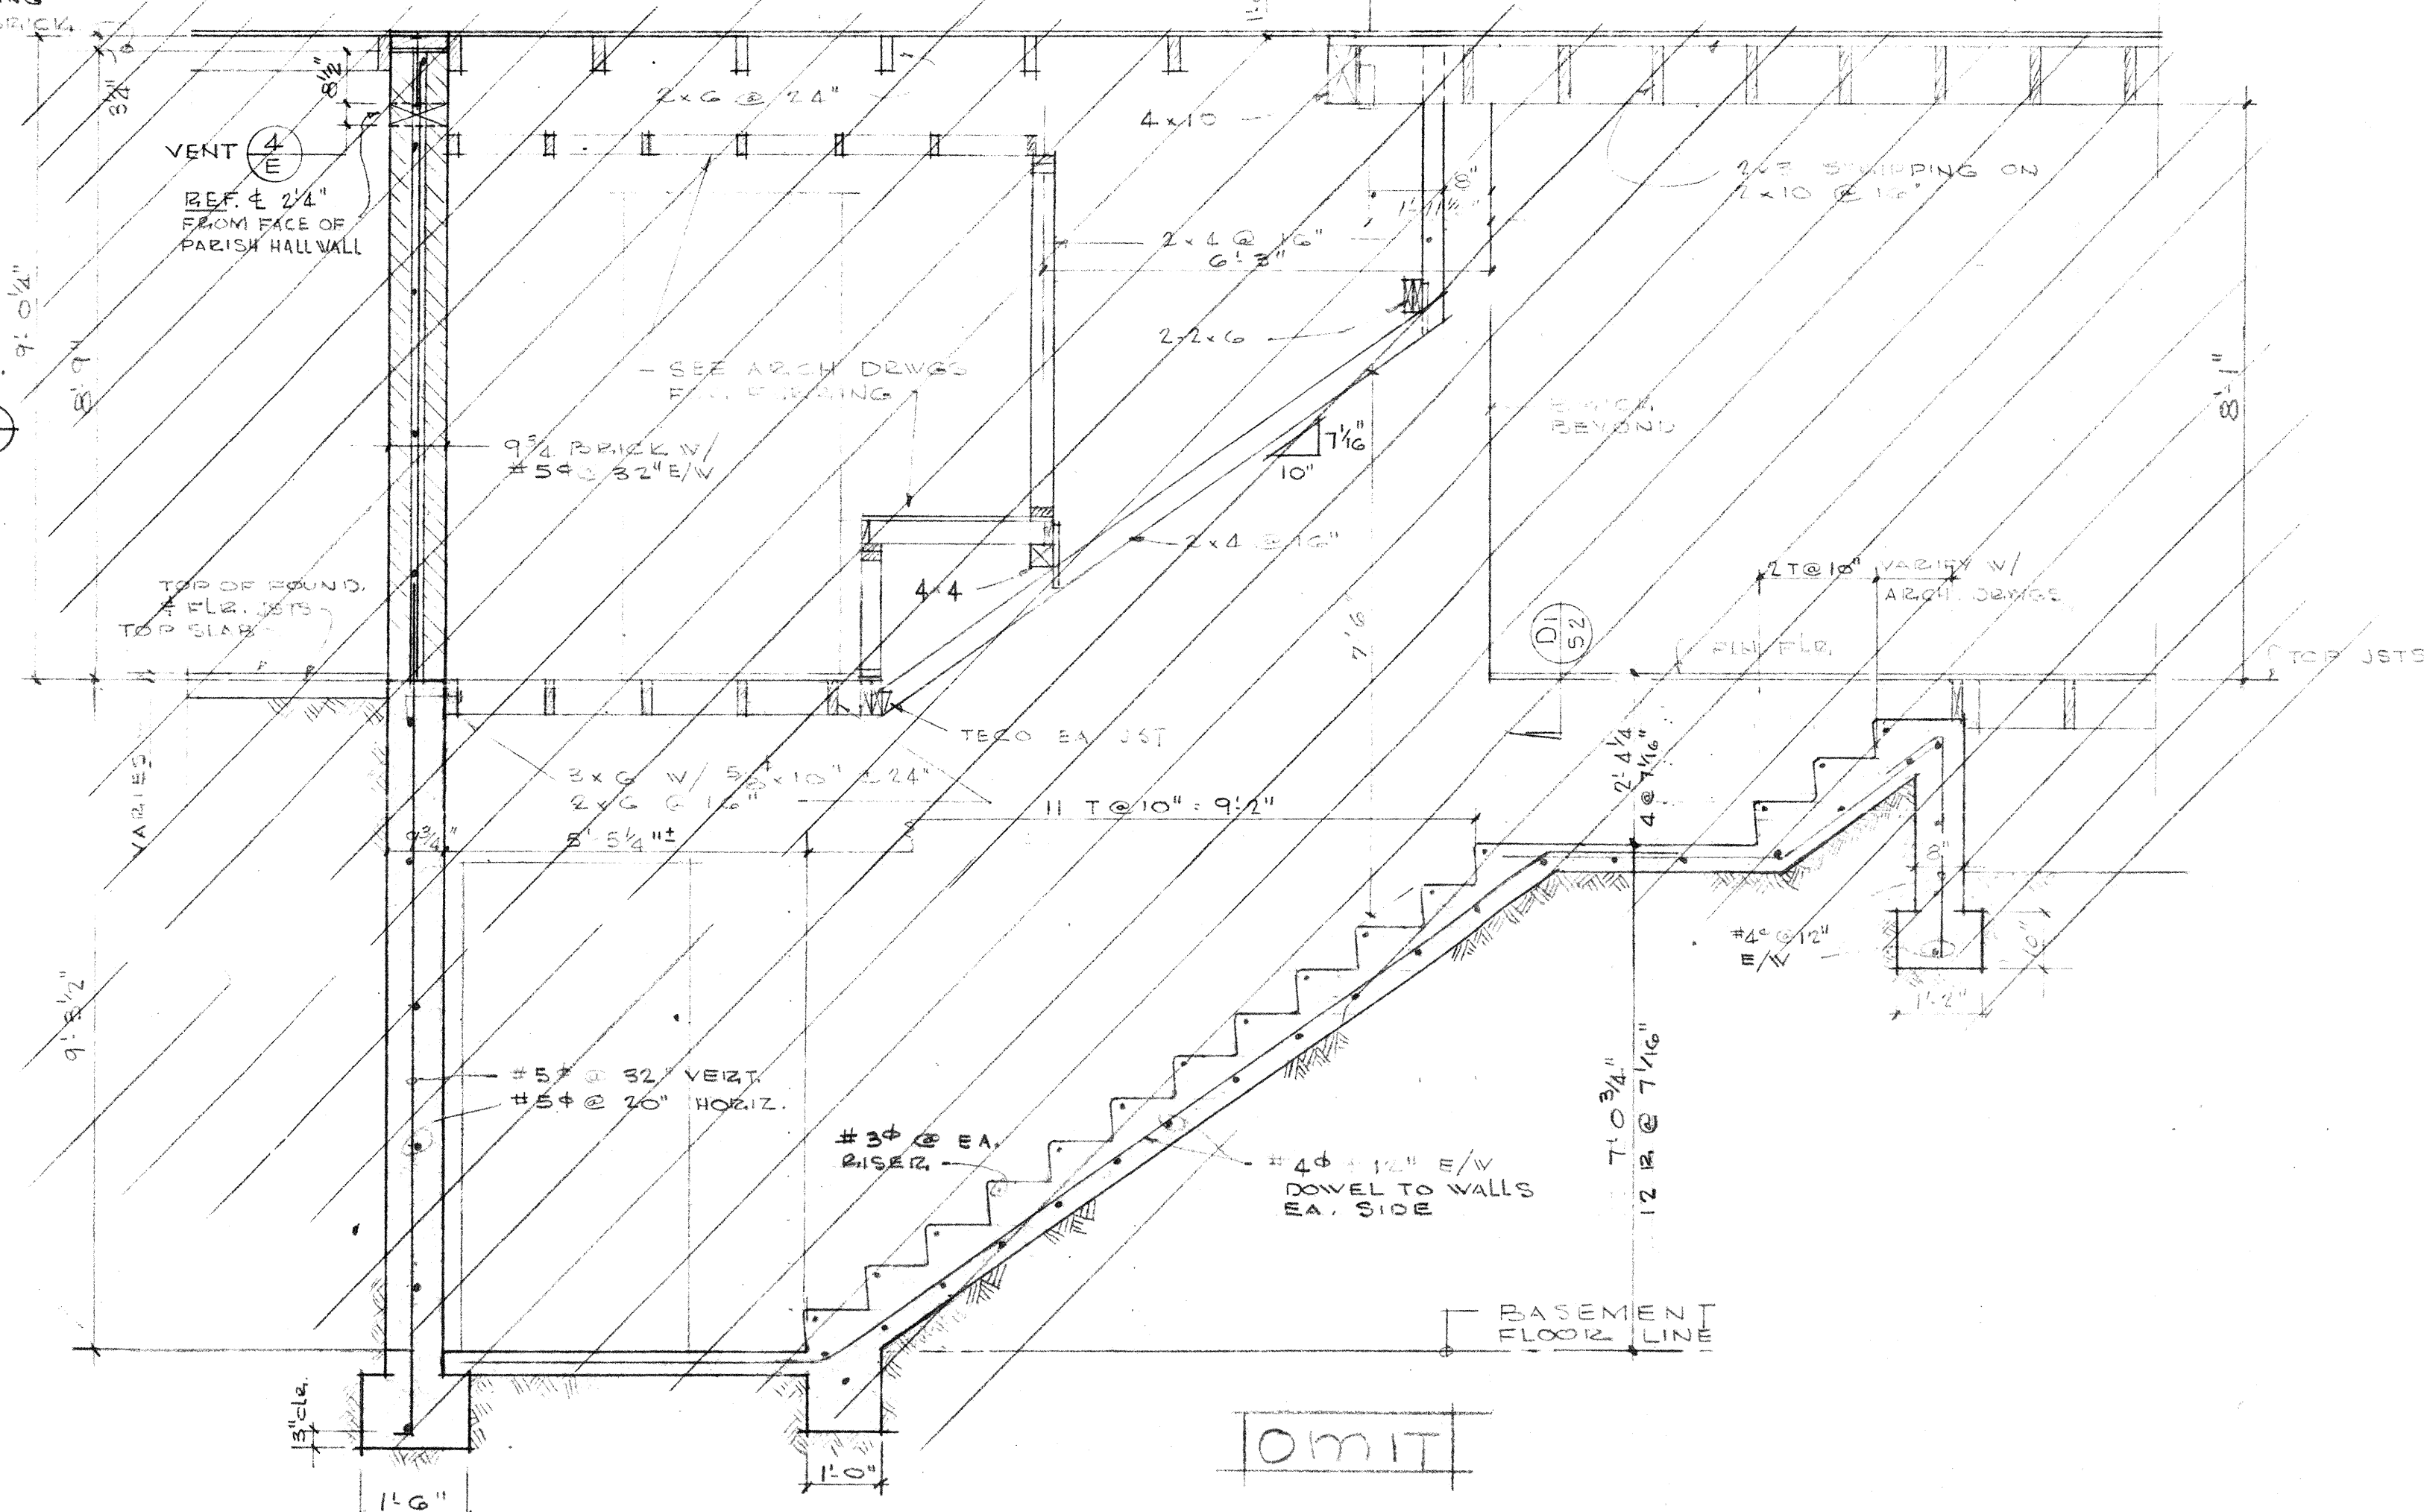

SECTION 1/2" = 1'-0"

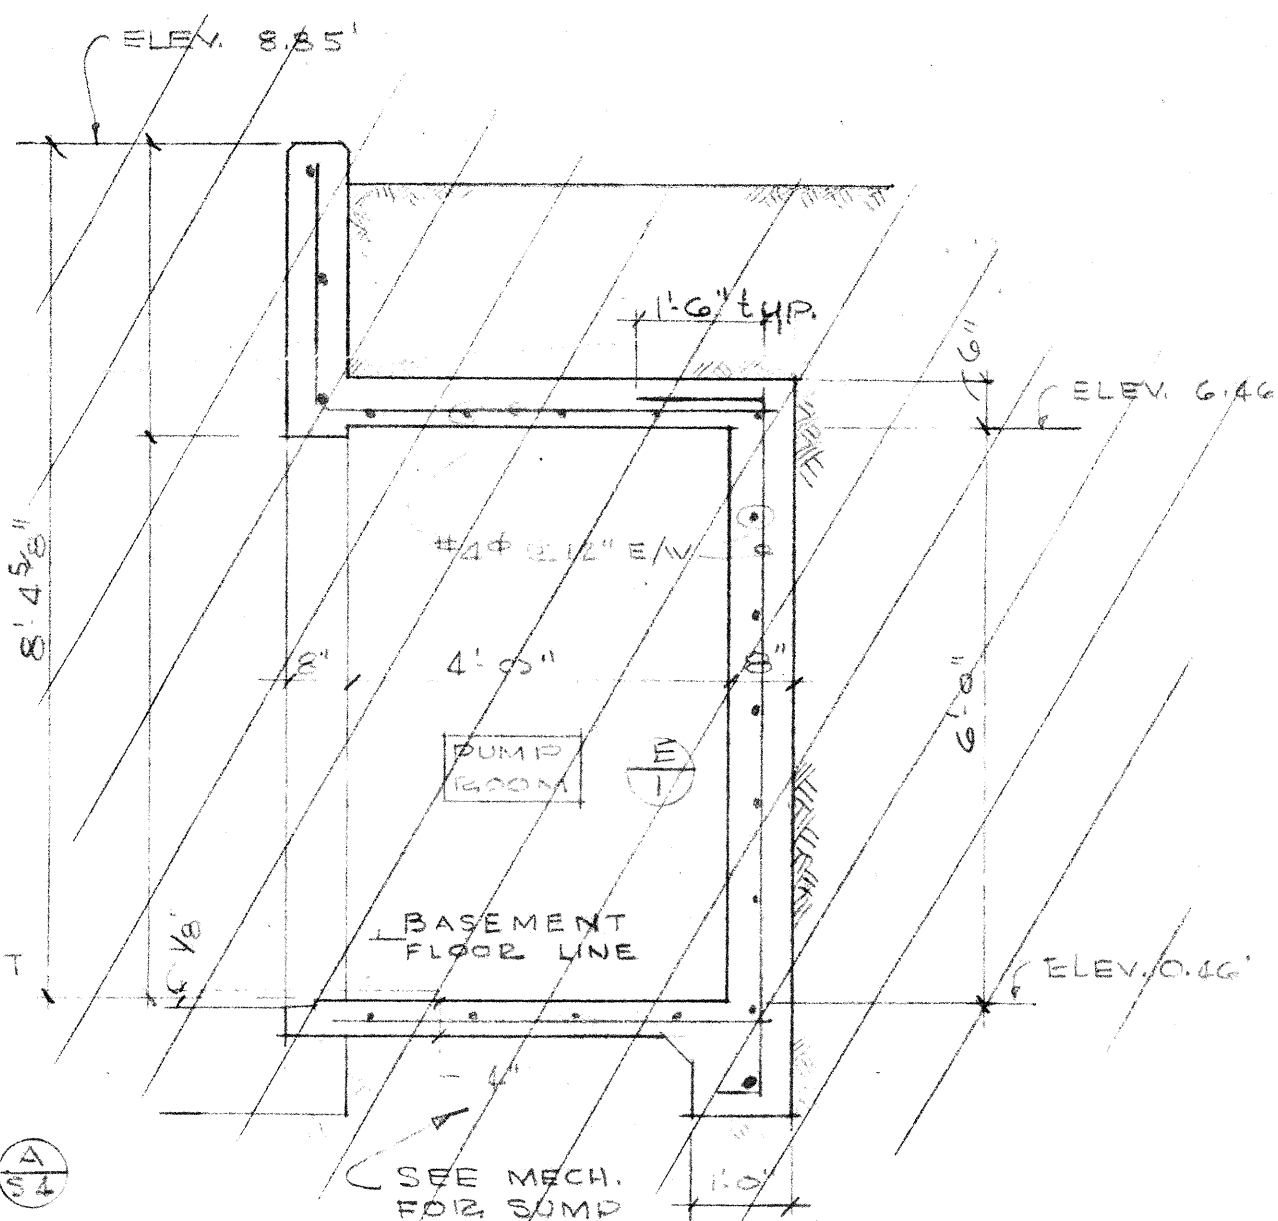

OMIT SECTION 1/2" = 1'-0"

REVISIONS		PARISH HALL ADDITION	
1	3-3-65	For	ST EDMUND'S EPISCOPAL CHURCH
2		1175 SAN GABRIEL BLVD. SAN MARINO, CALIFORNIA	
3		BREO FREEMAN	927
4		ARCHITECT	5-2
5		45 SOUTH MARENGO	OF 9
6		PASADENA 1, CALIFORNIA	
7	12-30-65		