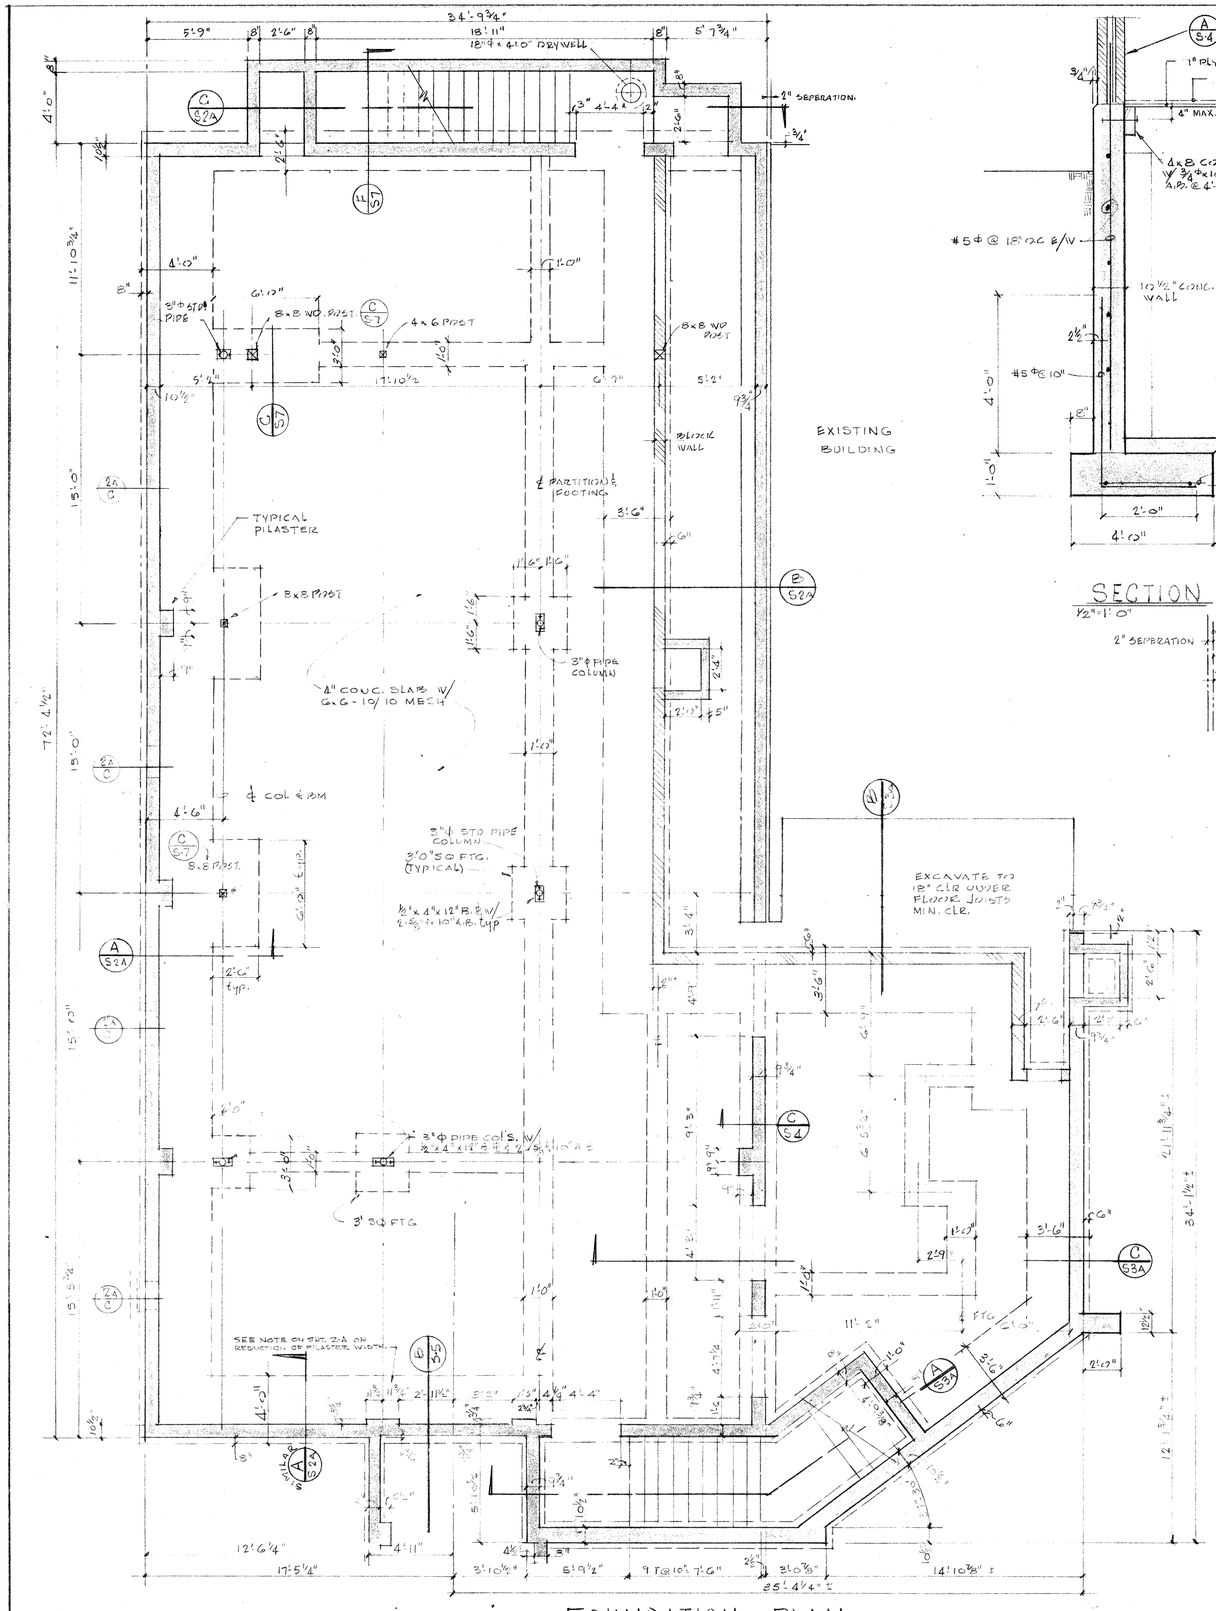

FOUNDATION PLAN
1/4" = 1'-0"

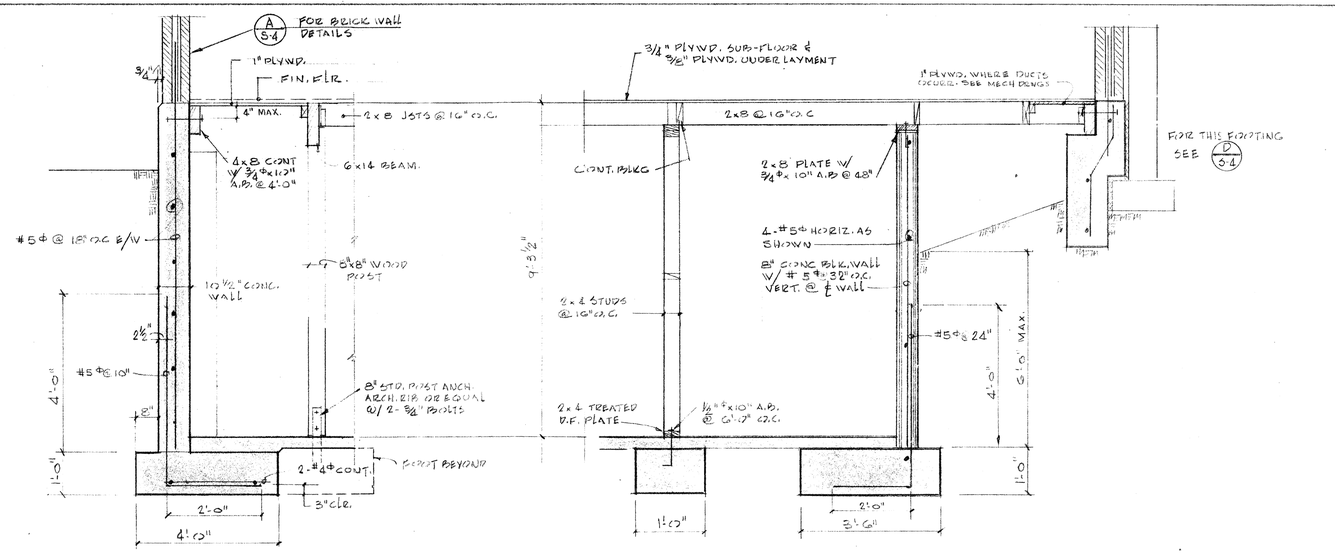

SECTION A/S2A
1/2" = 1'-0"

SECTION B/S2A
1/2" = 1'-0"

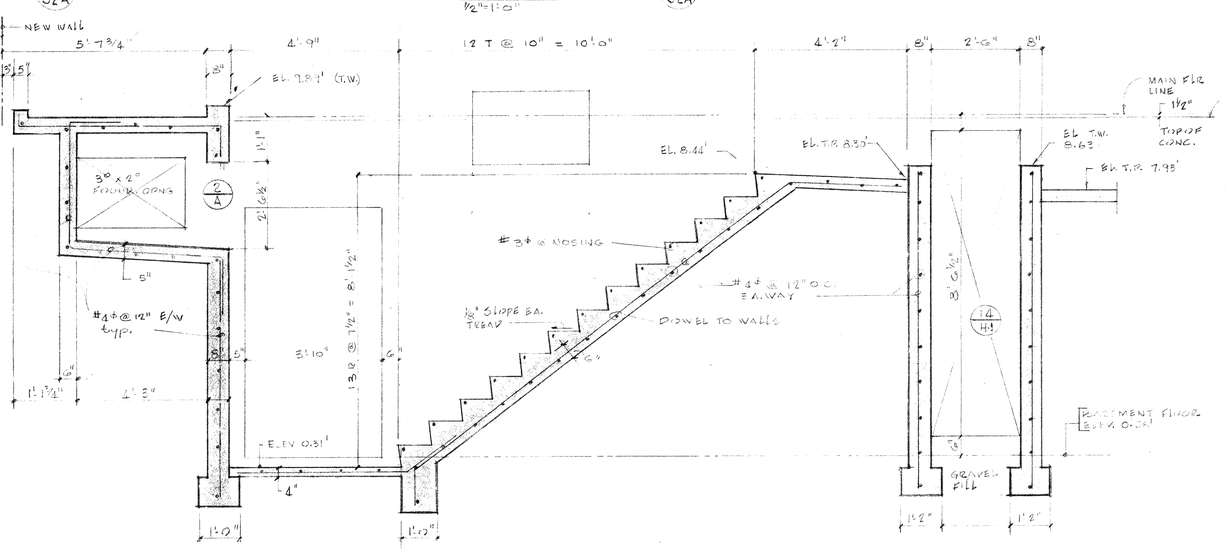

STAIR SECTION C/S2A
1/2" = 1'-0"

REVISIONS

PARISH HALL ADDITION
for
ST. EDMUND'S EPISCOPAL CHURCH
1175 SAN GABRIEL BLVD. SAN MARINO, CALIFORNIA

BRED FREEMAN
ARCHITECT
45 SOUTH MARENGO
PASADENA 1, CALIFORNIA

3-31-66

927

S2A
OF 9