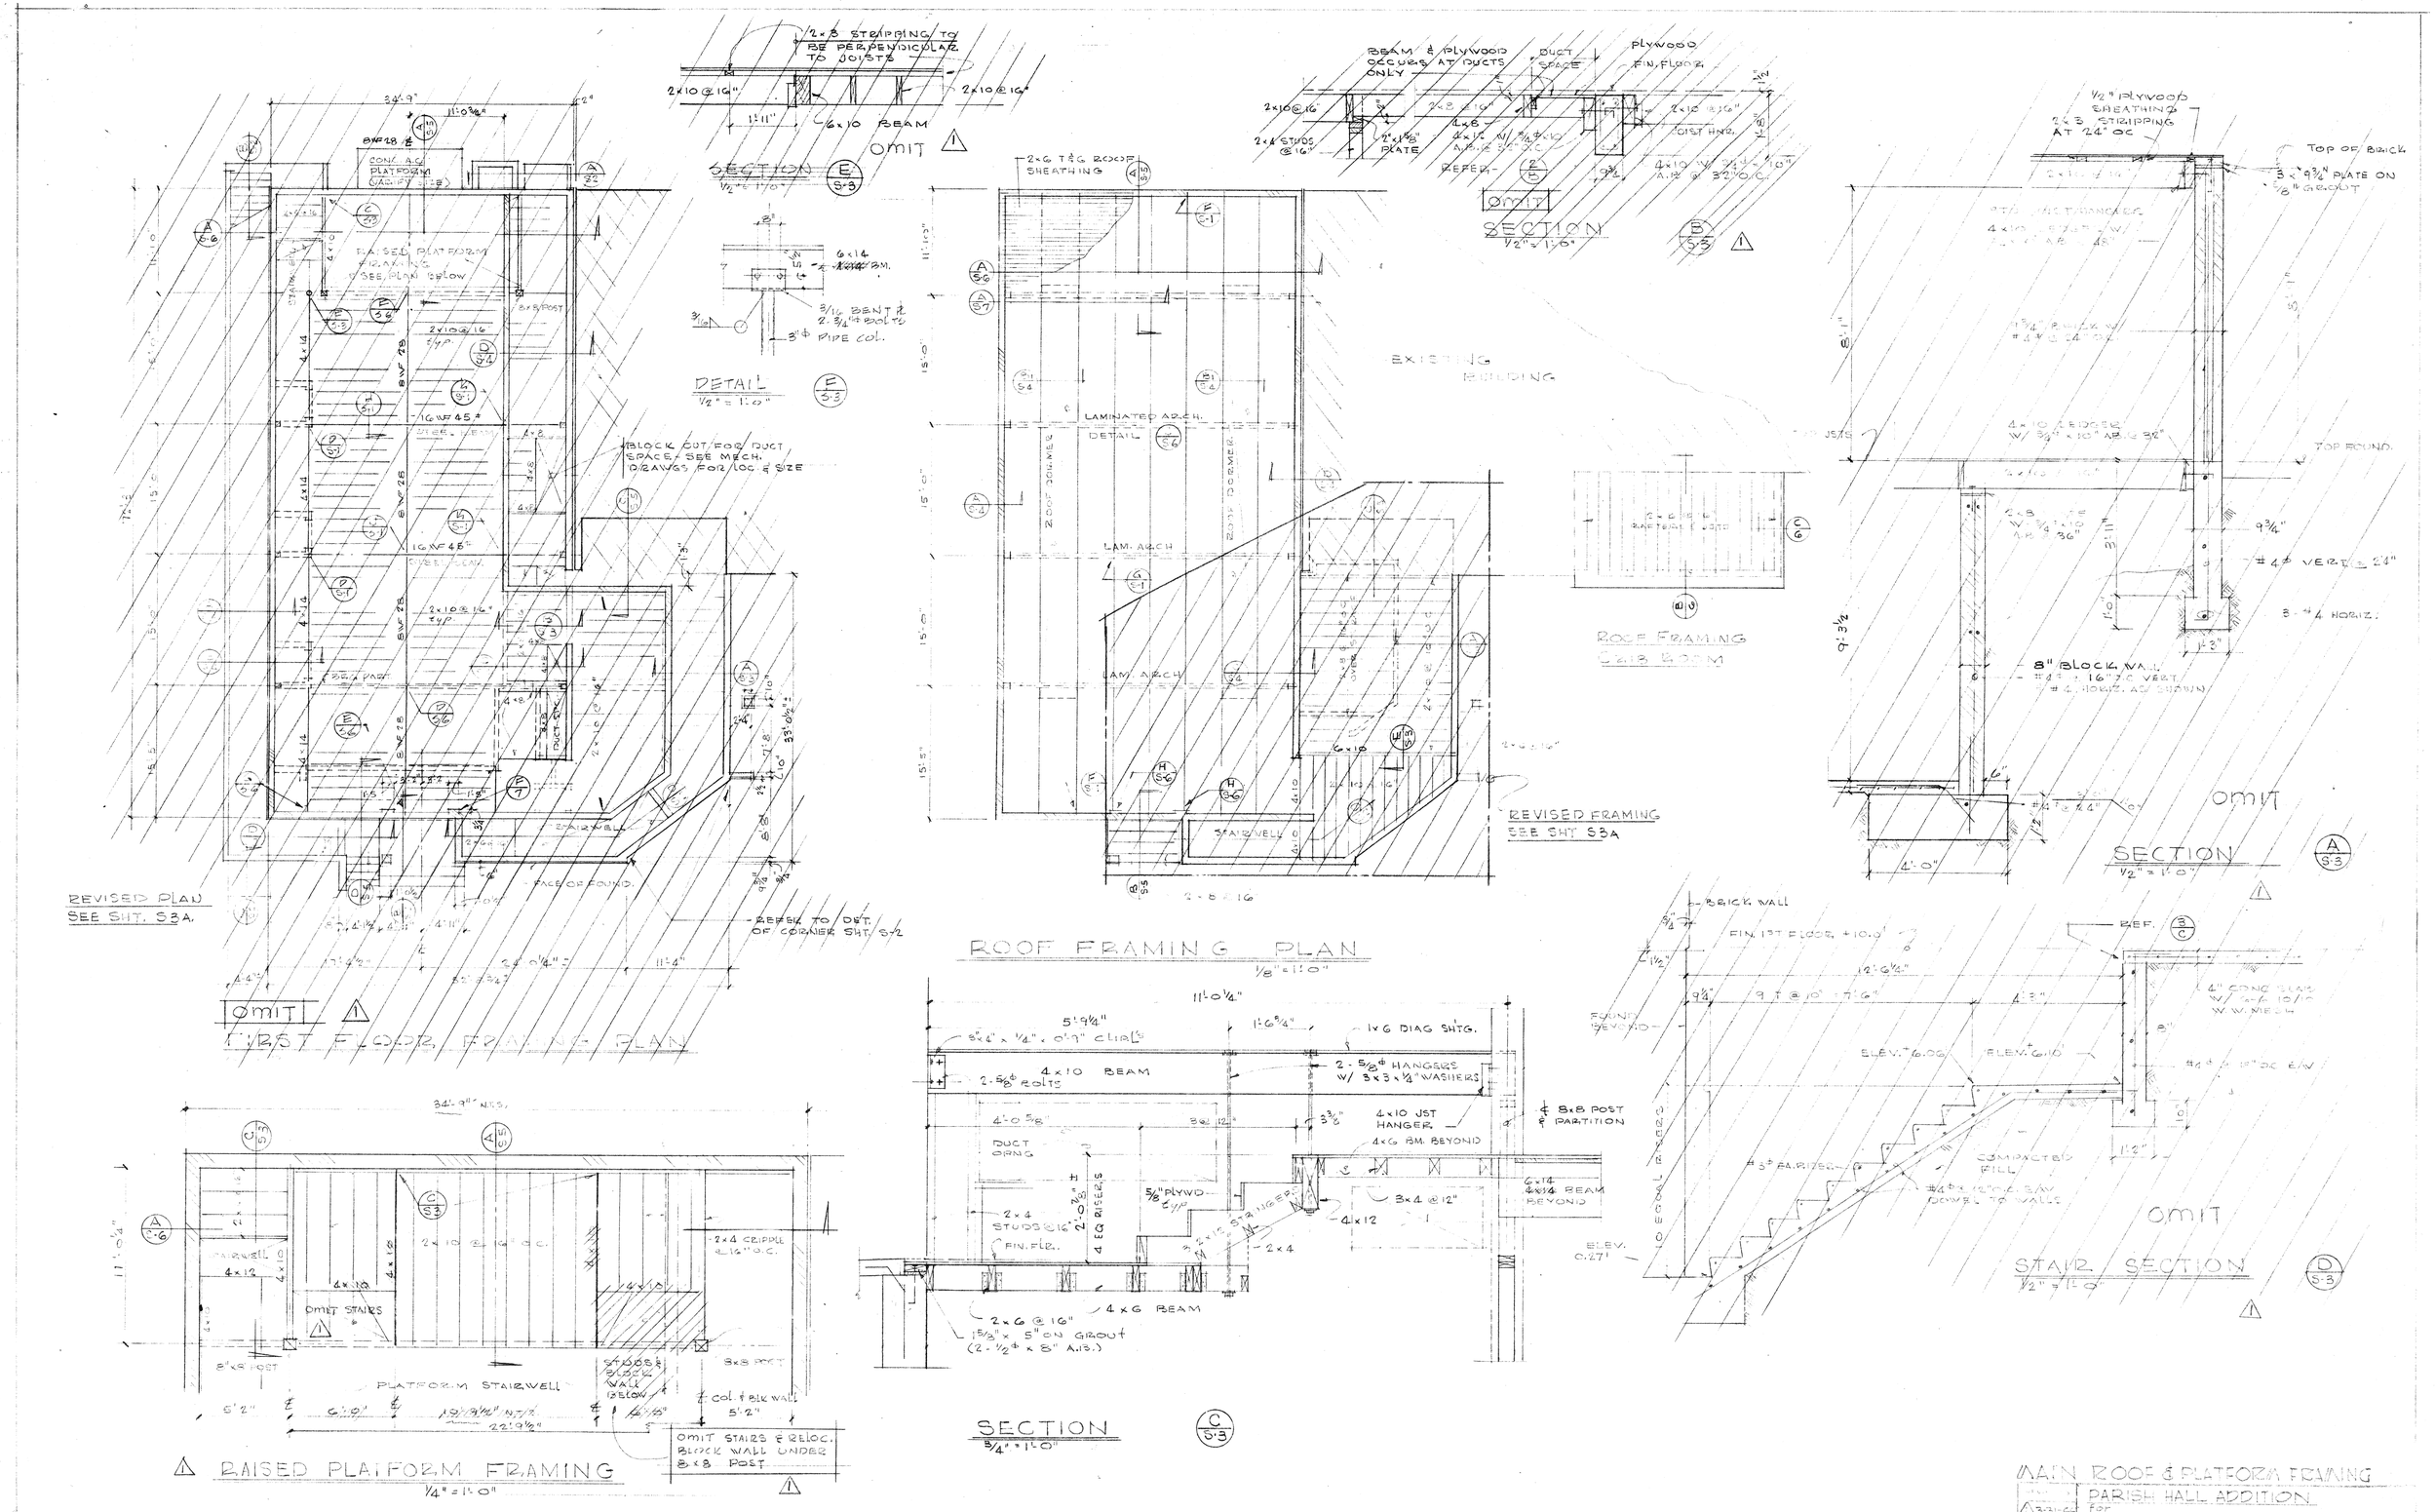

MAIN ROOF & PLATFORM FRAMING

PARISH HALL ADDITION
for
ST EDMUND'S EPISCOPAL CHURCH
1175 SAN GABRIEL BLVD SAN MARINO, CALIFORNIA

BREO FREEMAN
ARCHITECT
45 SOUTH MARENGO
PASADENA, CALIFORNIA

927

S-3 of 9

12-30-65

HUGH BROOKS ASSOCIATES
CONSULTING ENGINEERS / 616 SO. FREMONT AVE., ALHAMBRA, CALIF. CU 3-4418