

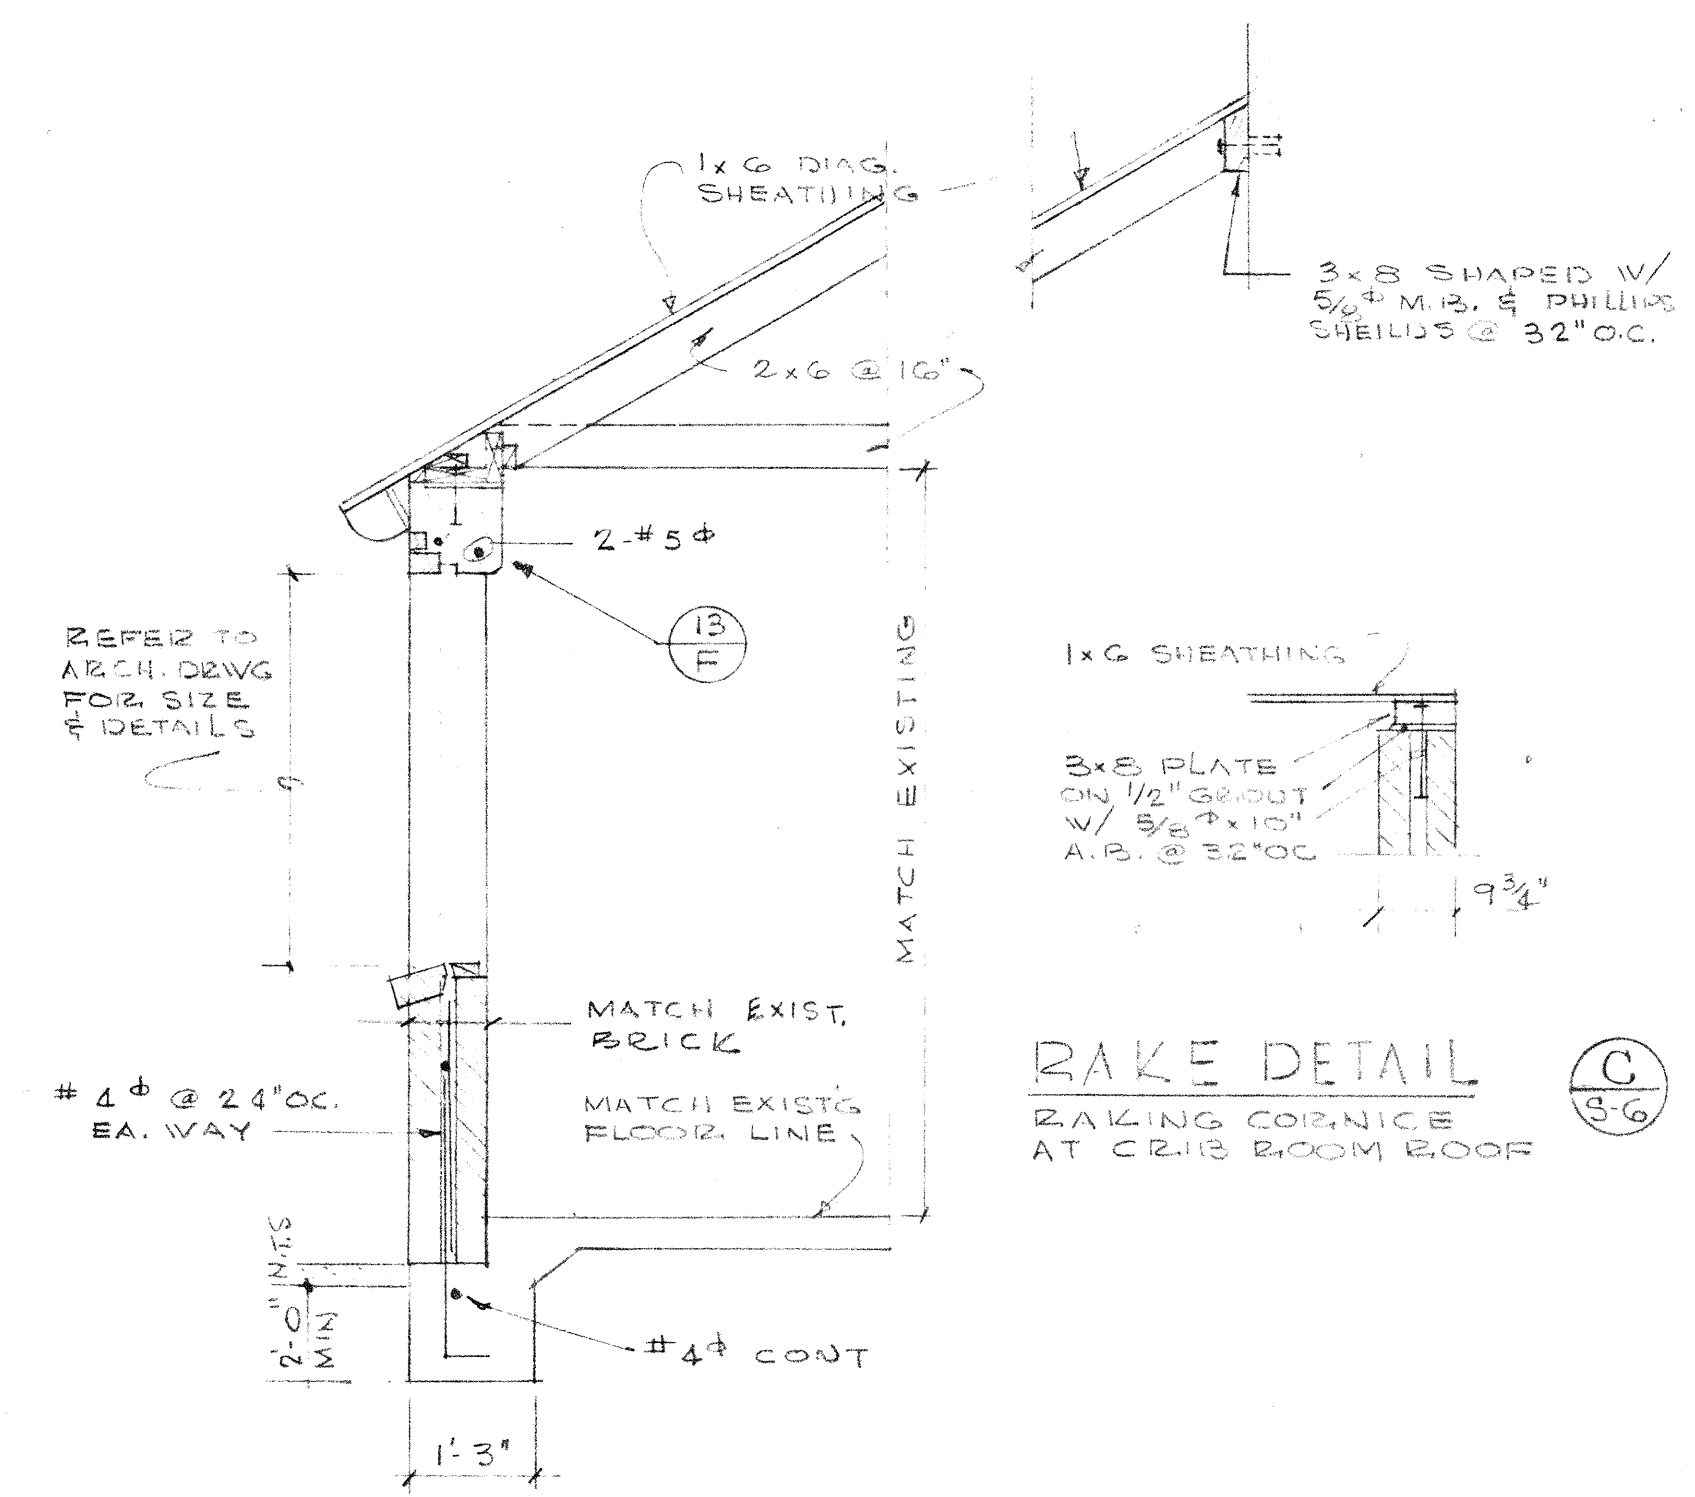


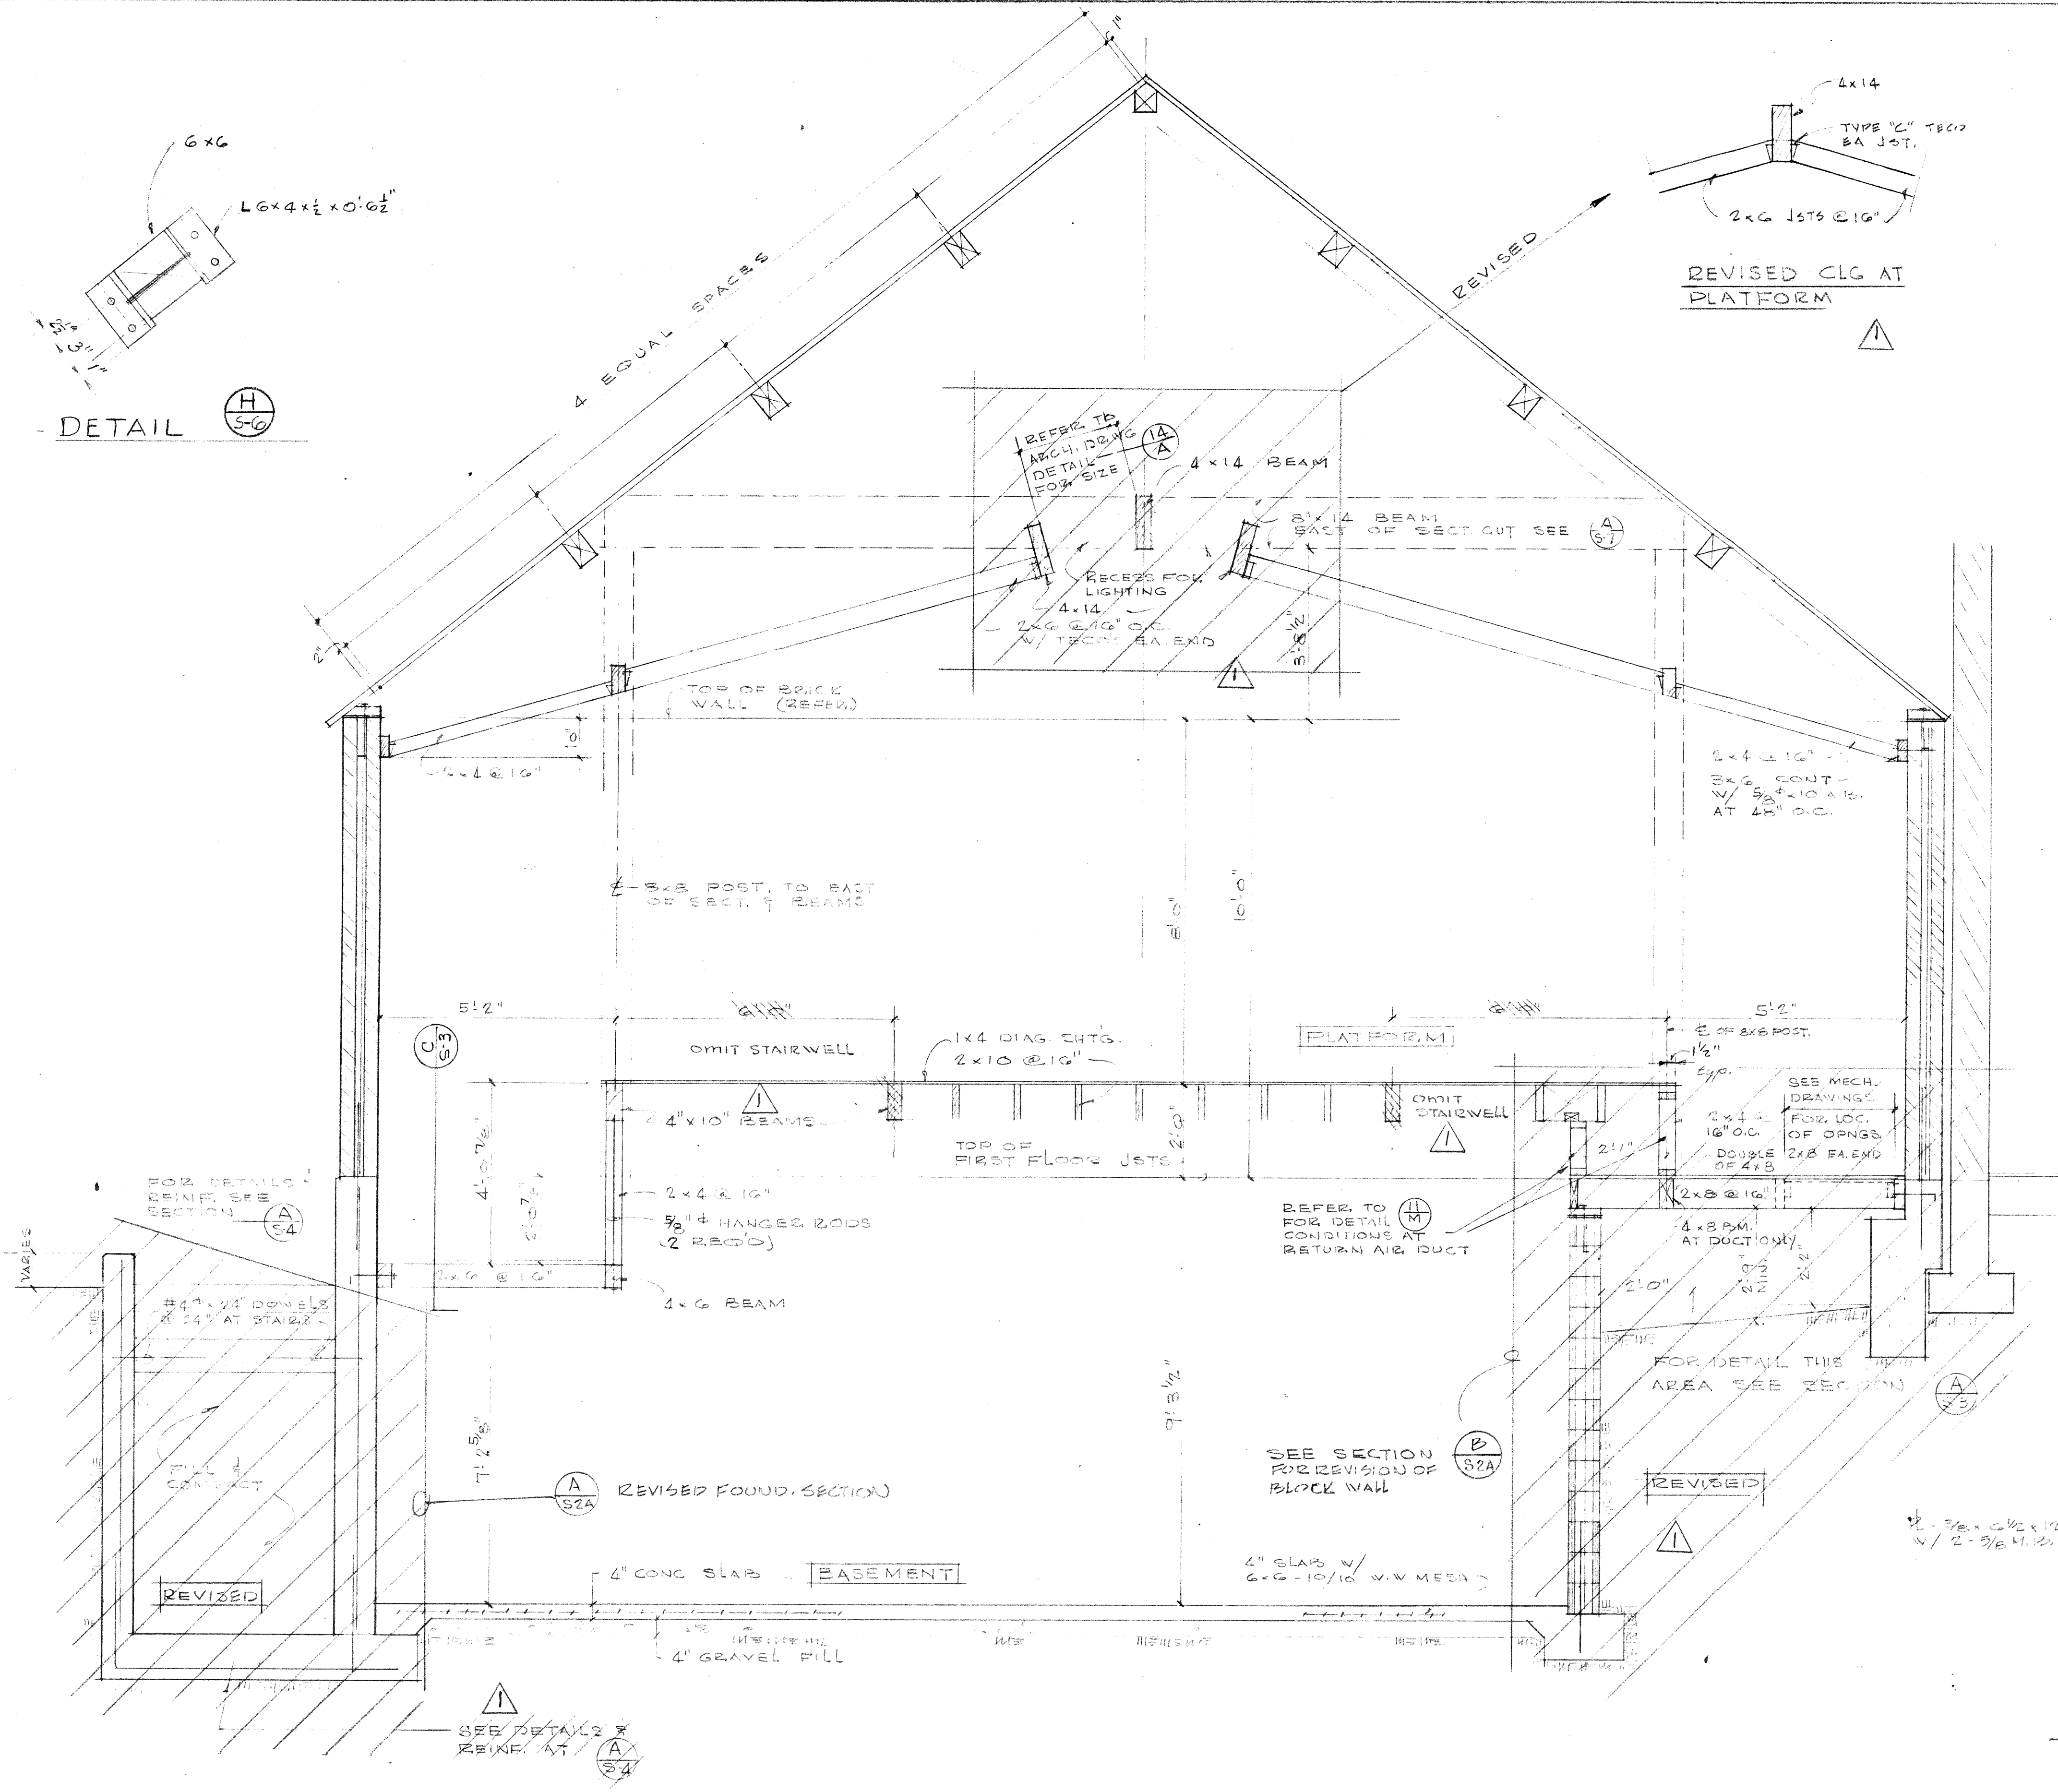


SECTION B
1/2" = 1'-0"

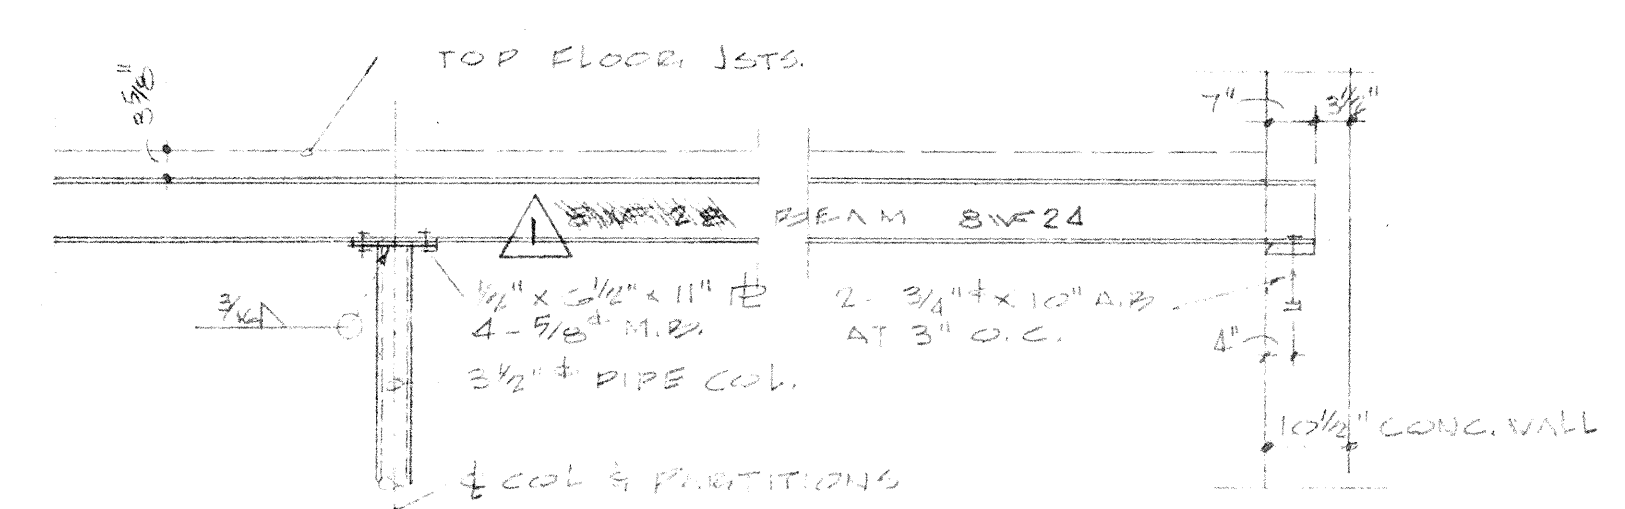


DETAIL A
1/2" = 1'-0"

DETAIL E
1/2" = 1'-0"

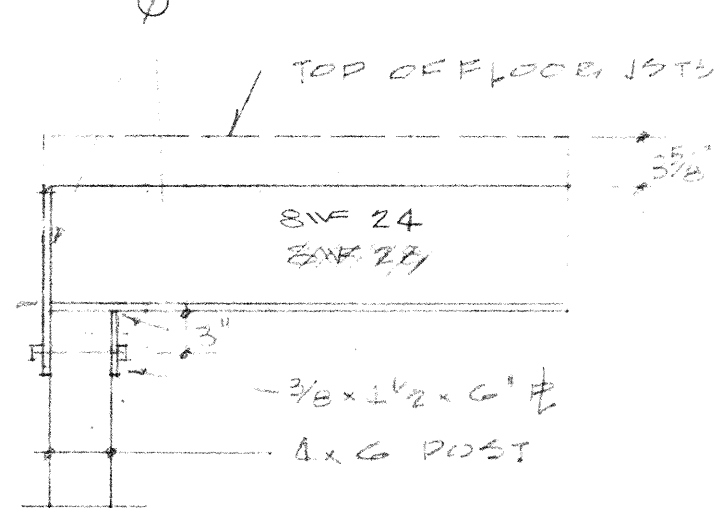

DETAIL F
1" = 1'-0"

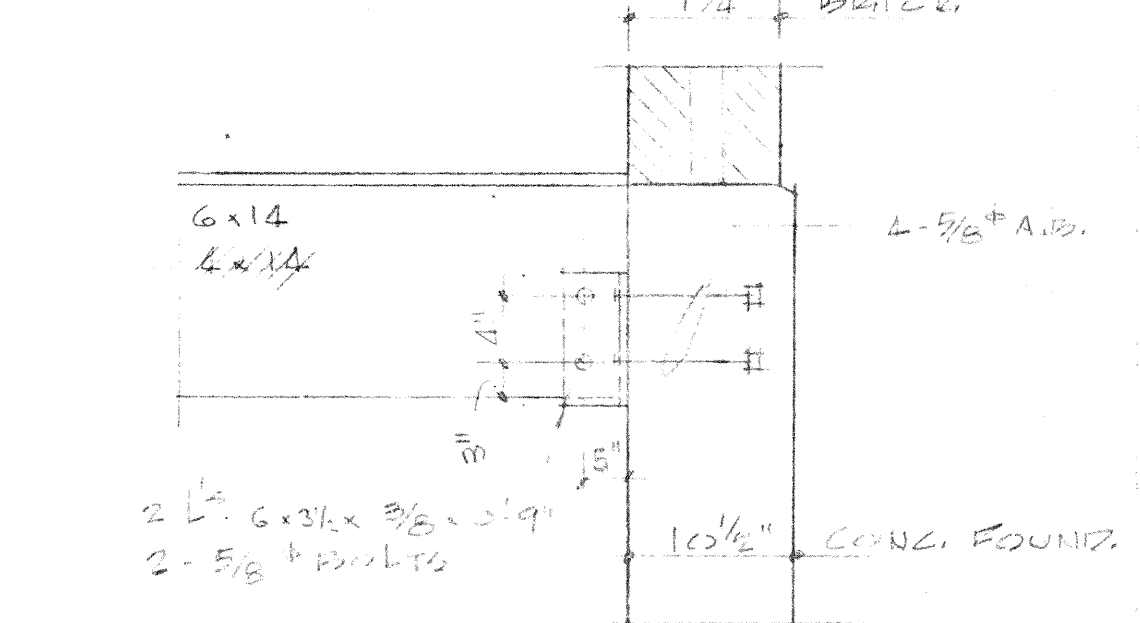

DETAIL G
1" = 1'-0"

SECTION A
1/2" = 1'-0"

STRUCTURAL SECTIONS	
PARISH HALL ADDITION	
ST. EDMUND'S EPISCOPAL CHURCH	
1175 SAN CARLOS BLVD. SAN MARINO, CALIFORNIA	
BRED FREEMAN	927
ARCHITECT	5-6
45 SOUTH MARENGO	9-9
HARRISBURG, ALABAMA VIA	