



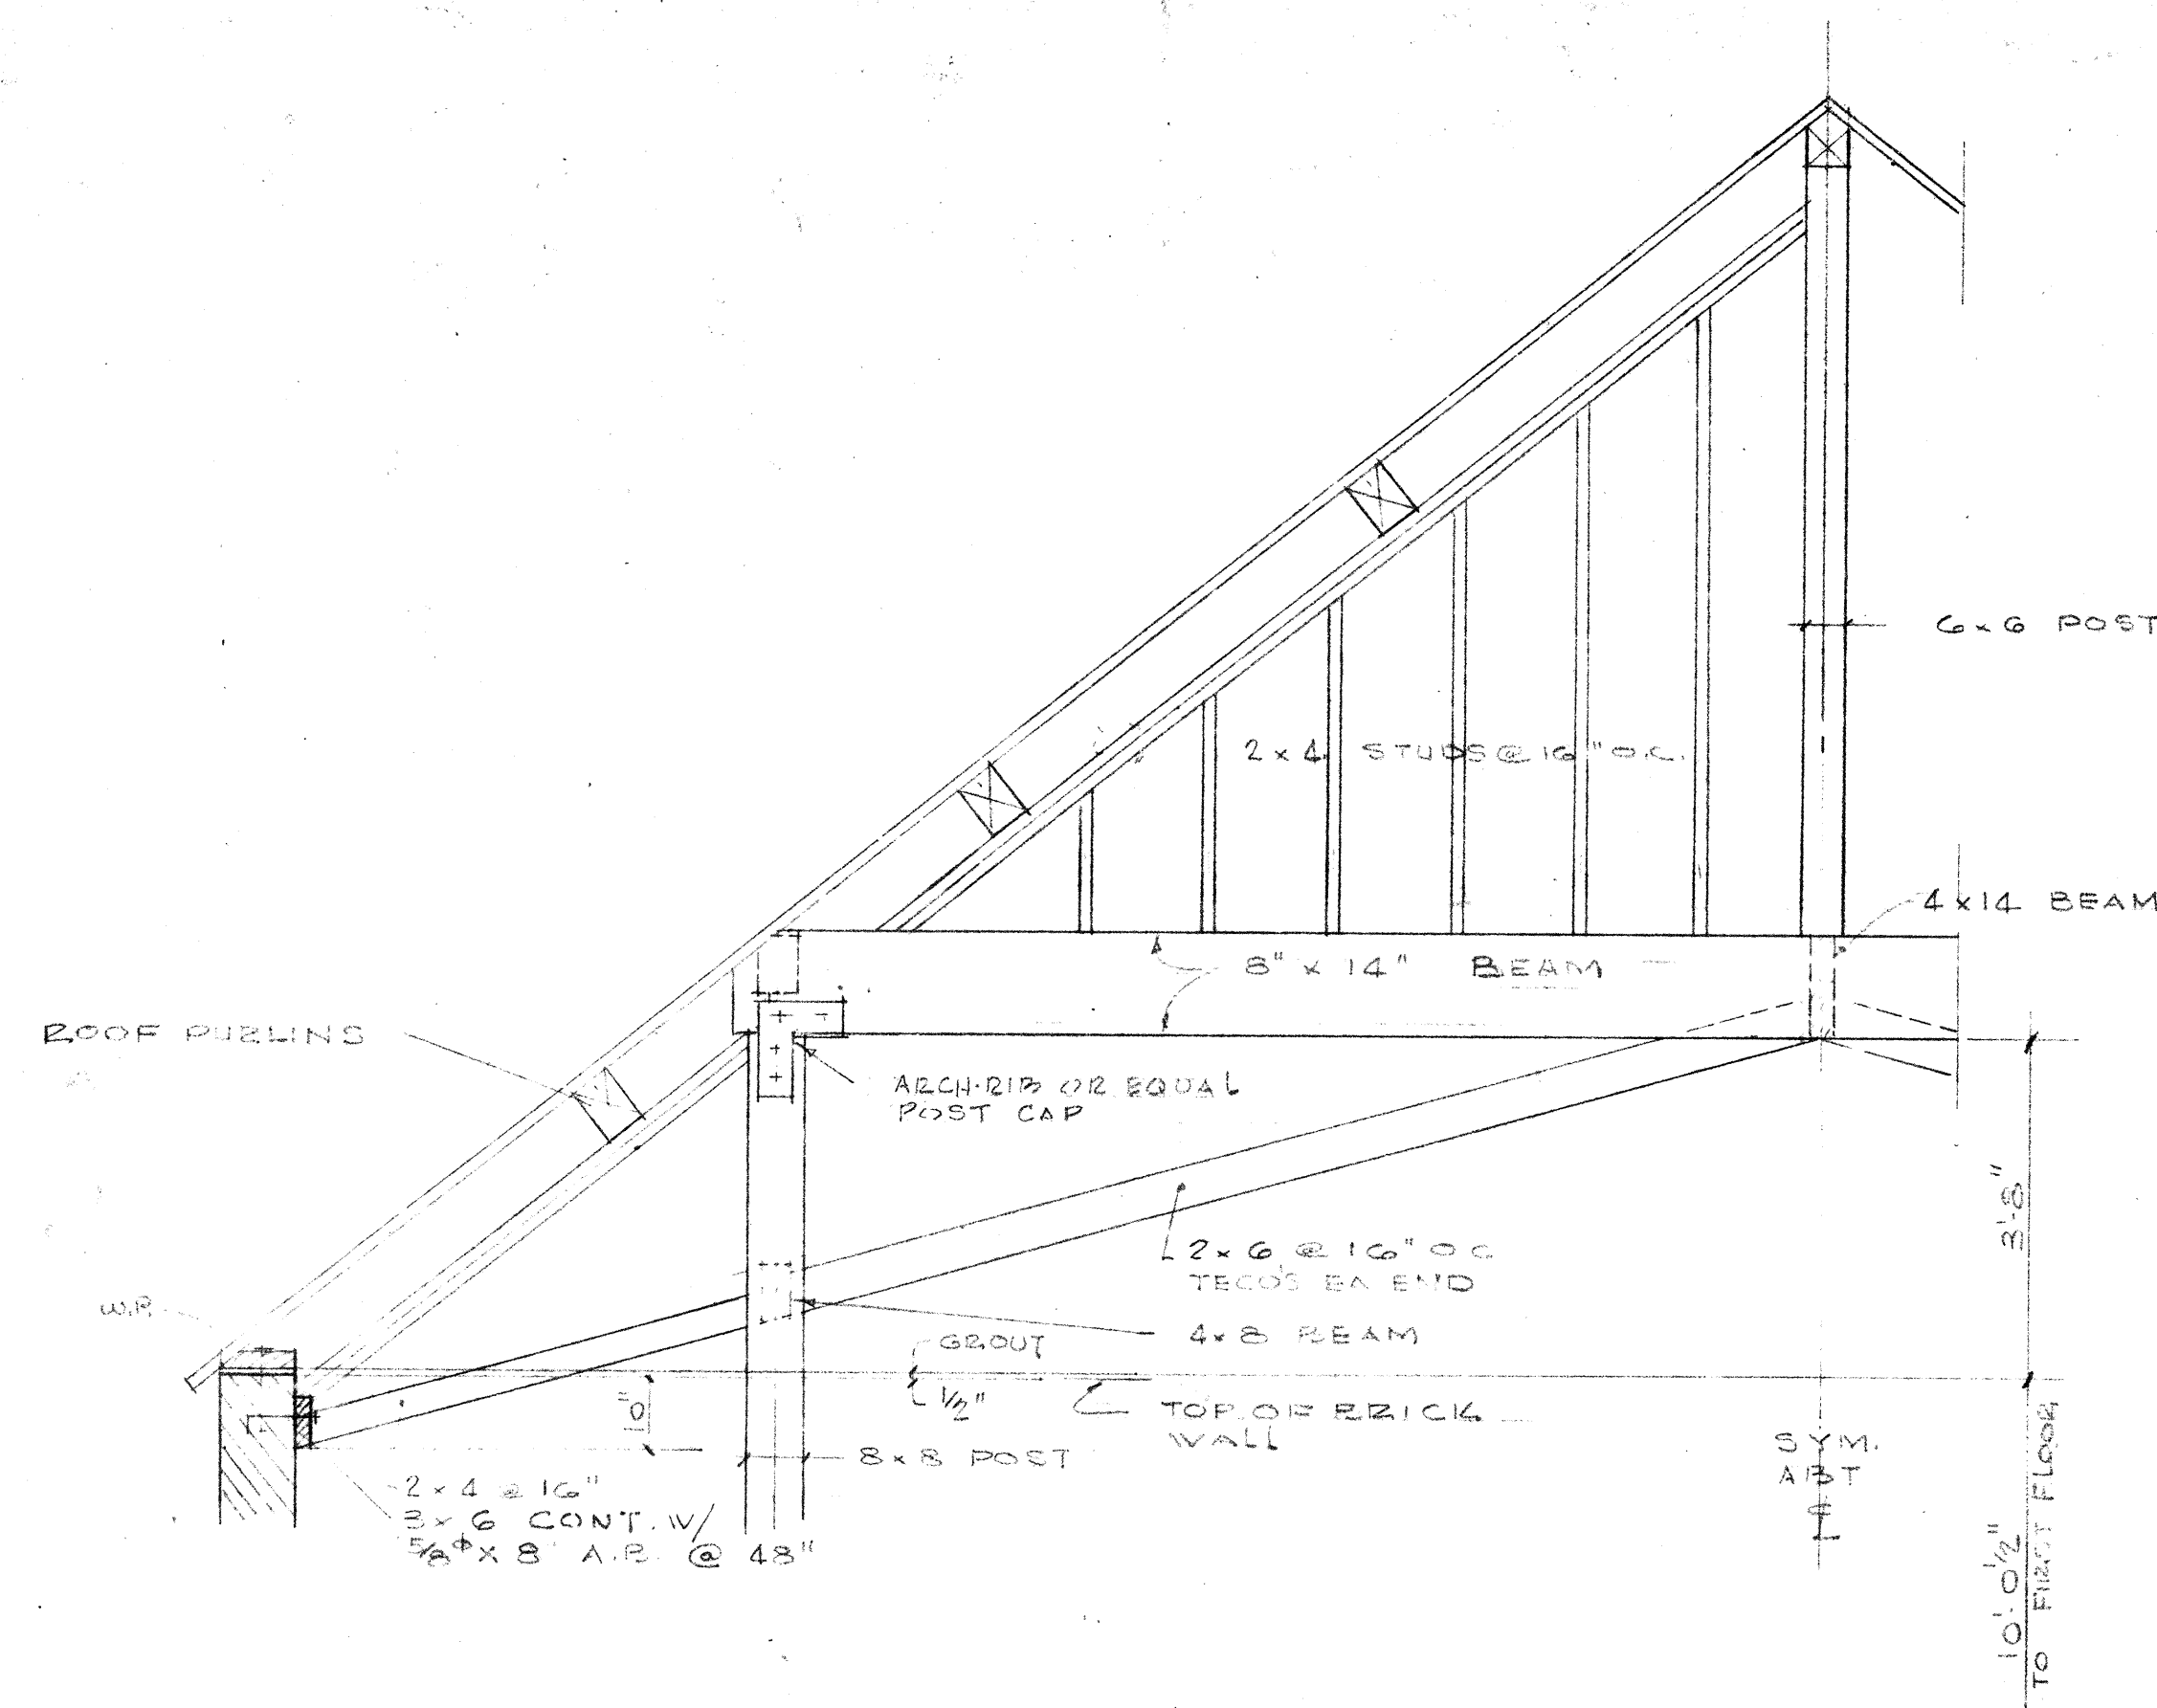


SECTION
1/2" = 1'-0"

(A)
S7

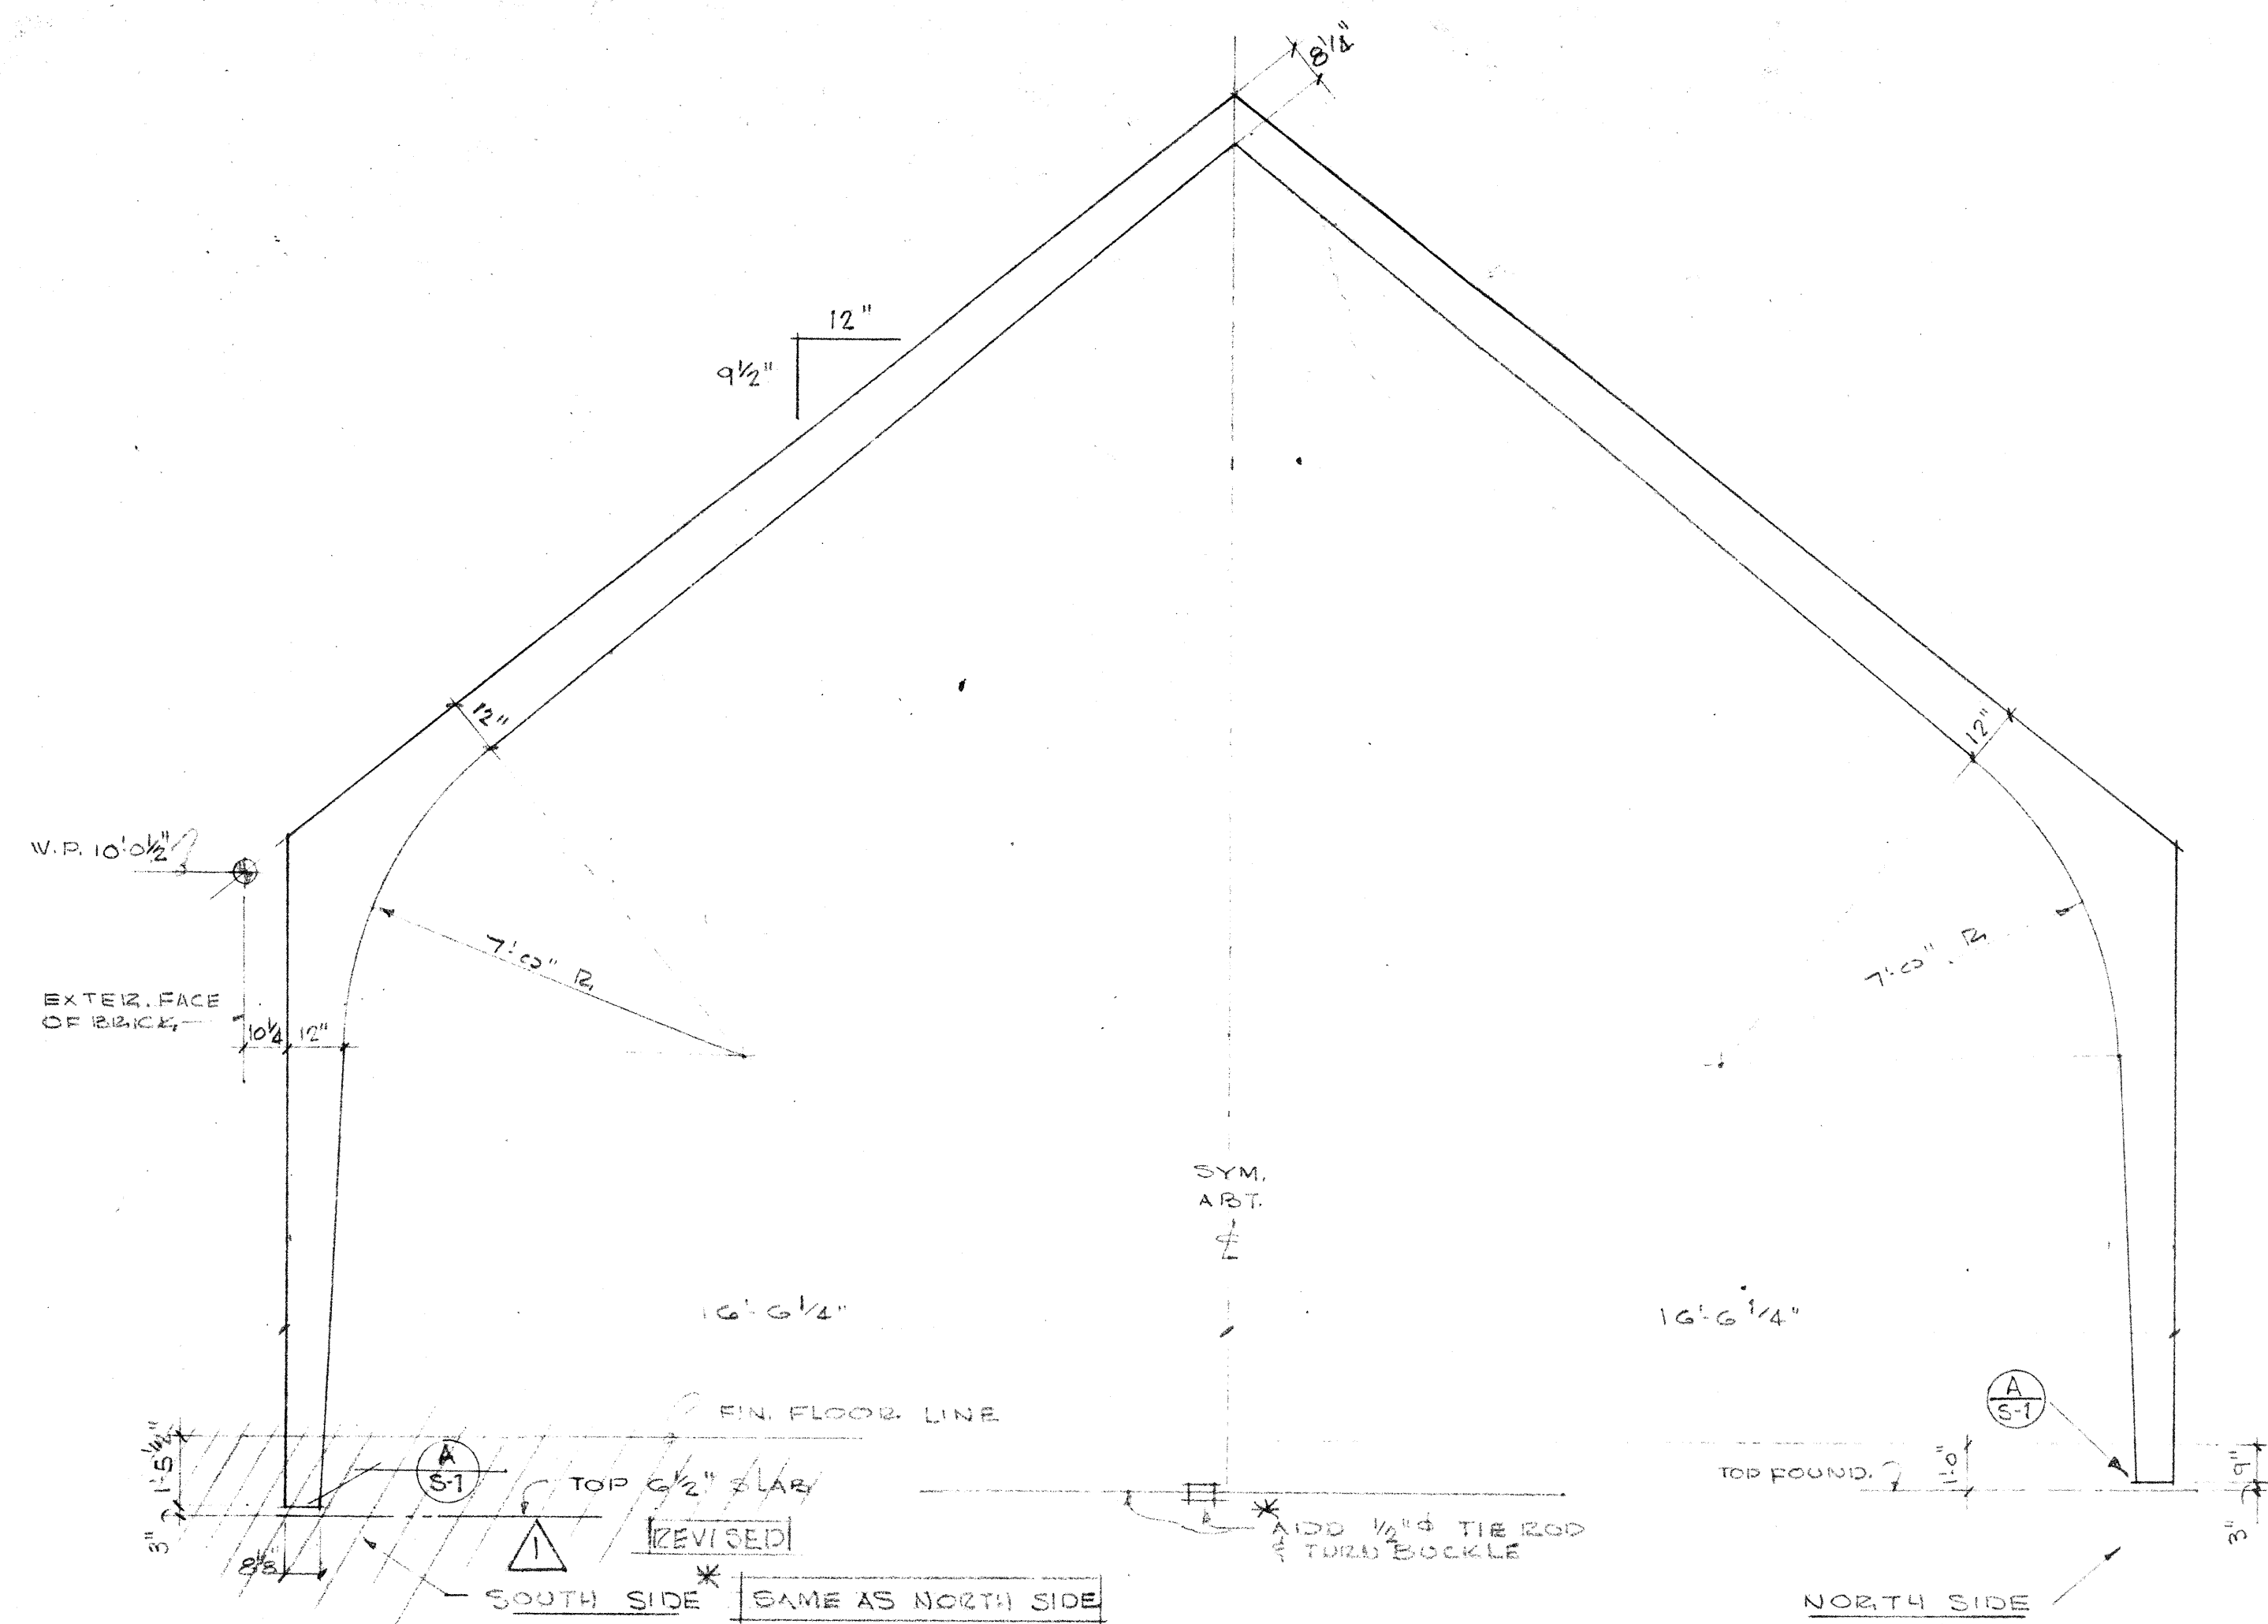


LAMINATED ARCH DETAIL

(B)
S7

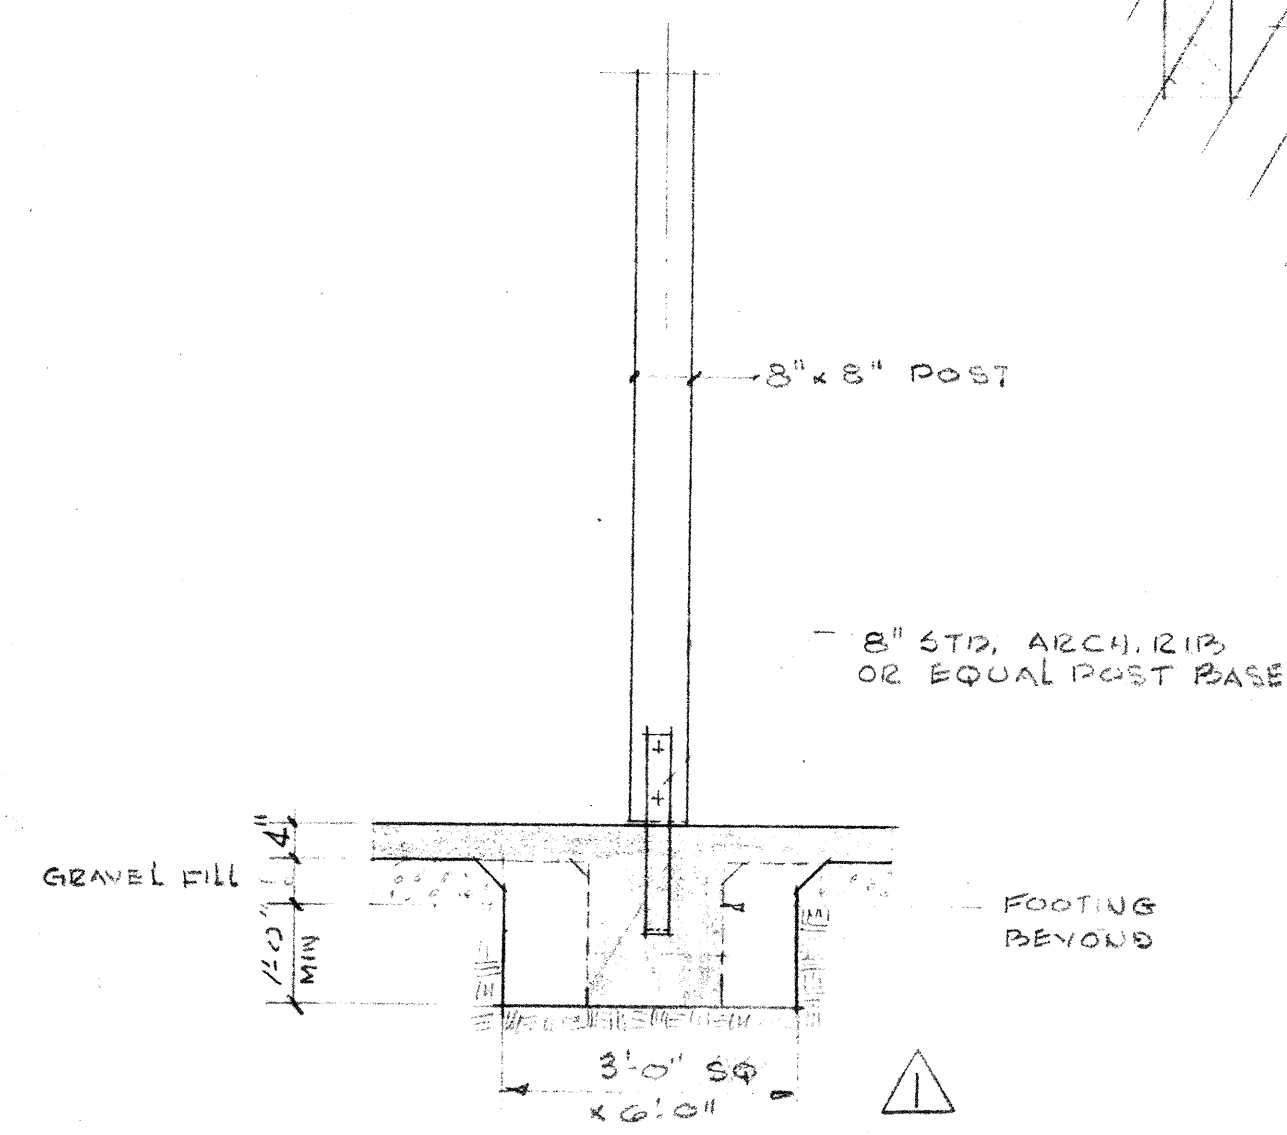


SECTION

(C)
S7

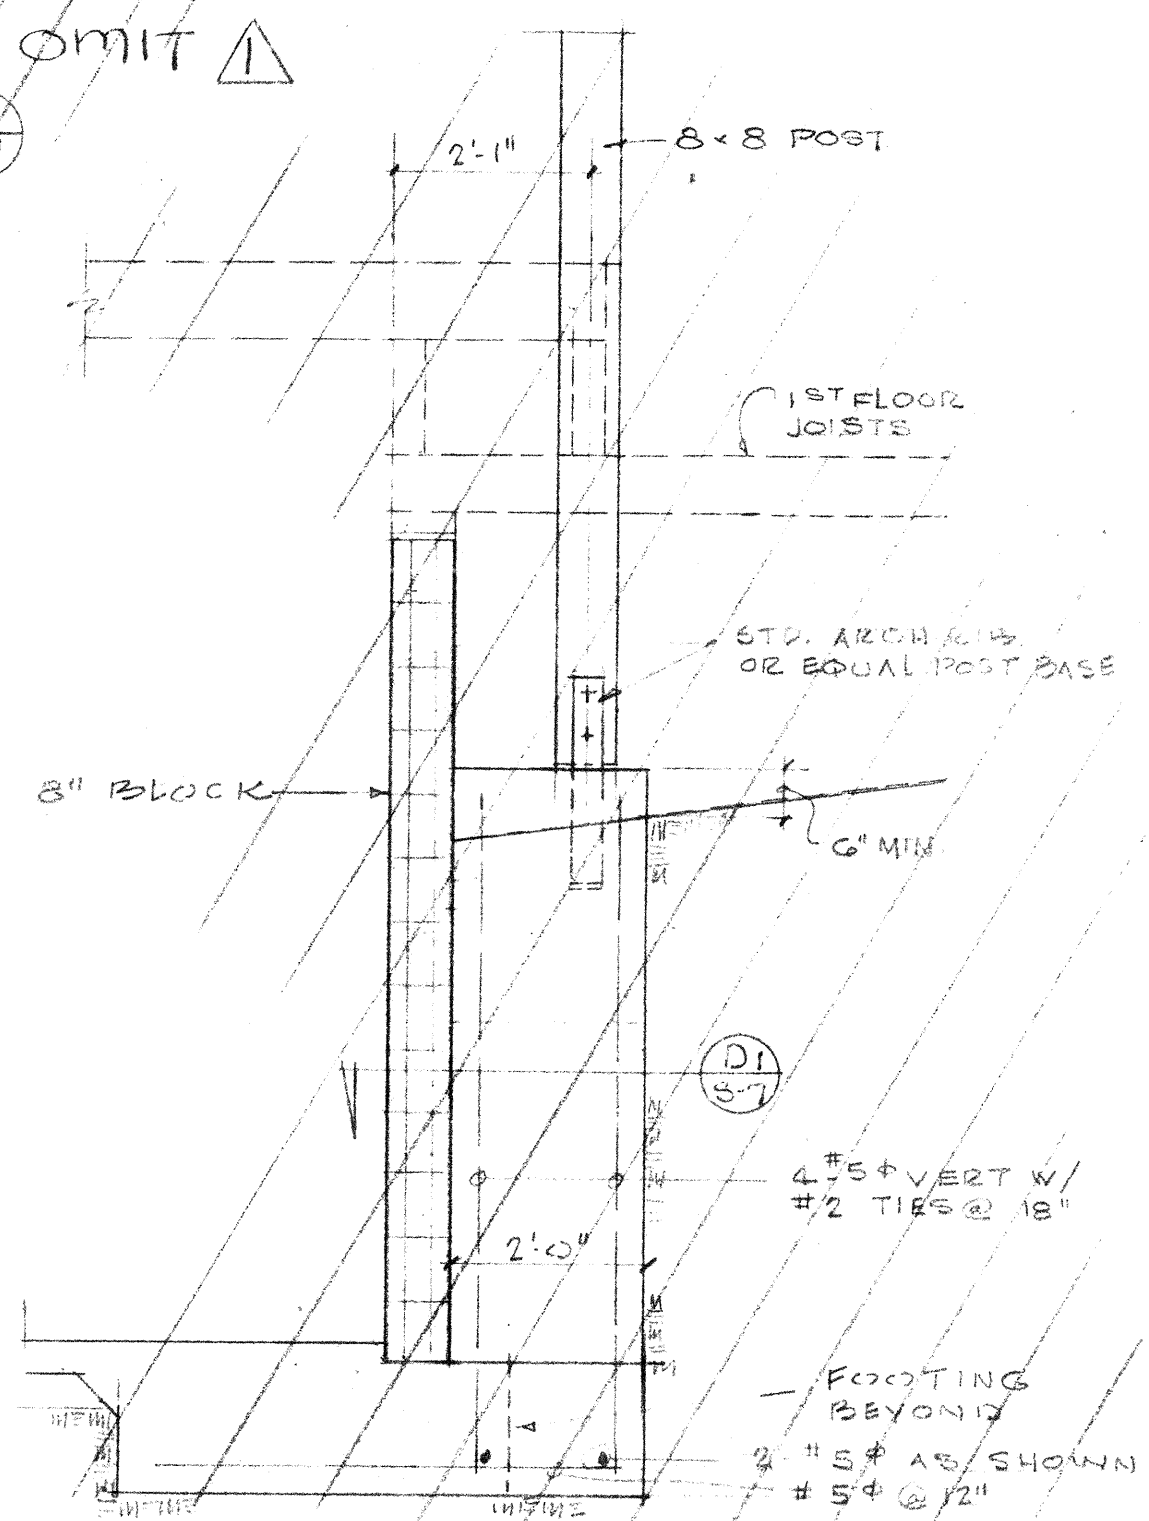


SECTION

(D)
S7

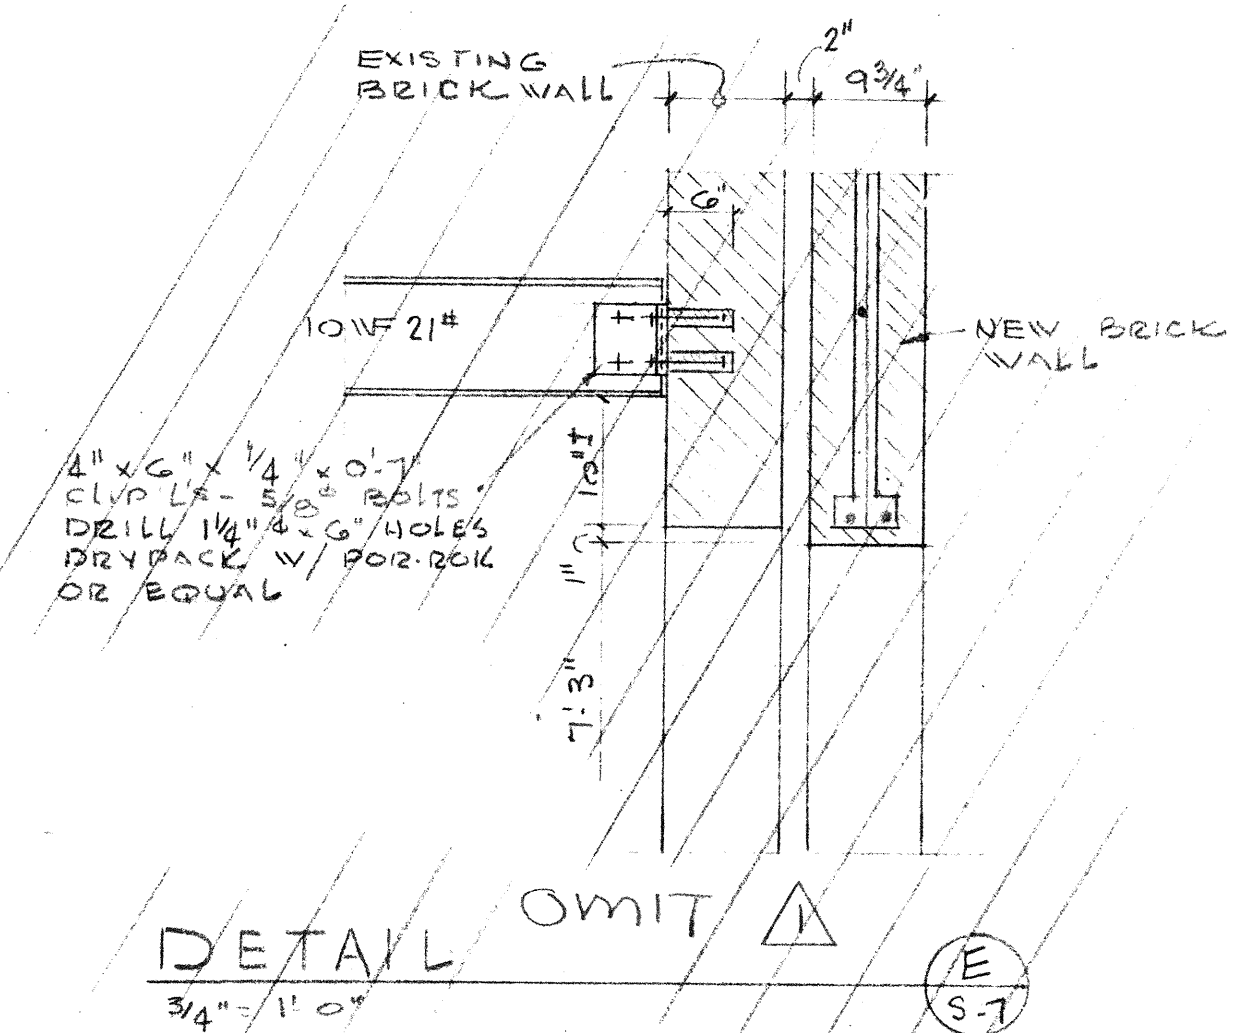


DETAIL OMIT
3/4" = 1'-0"

(E)
S7

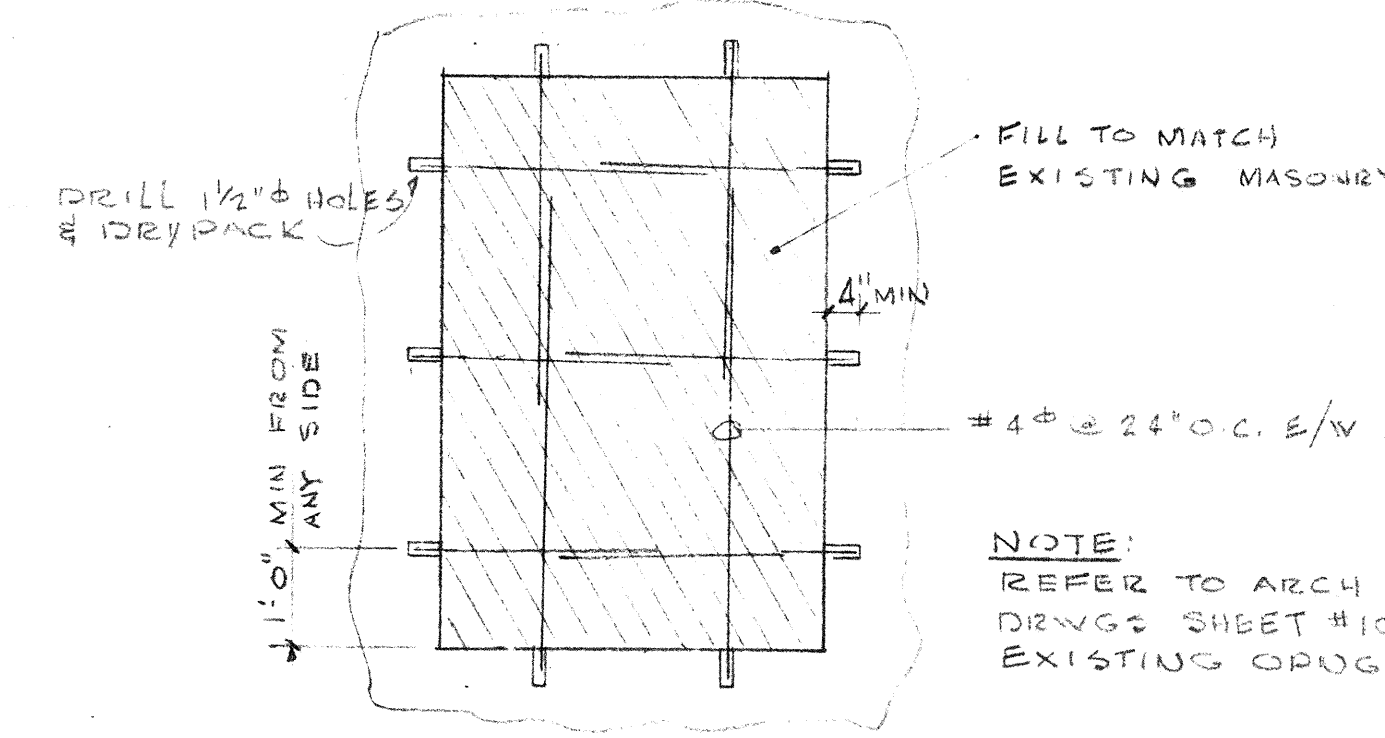

CLOSE EXISTING MASONRY OPNGS.
NO SCALE

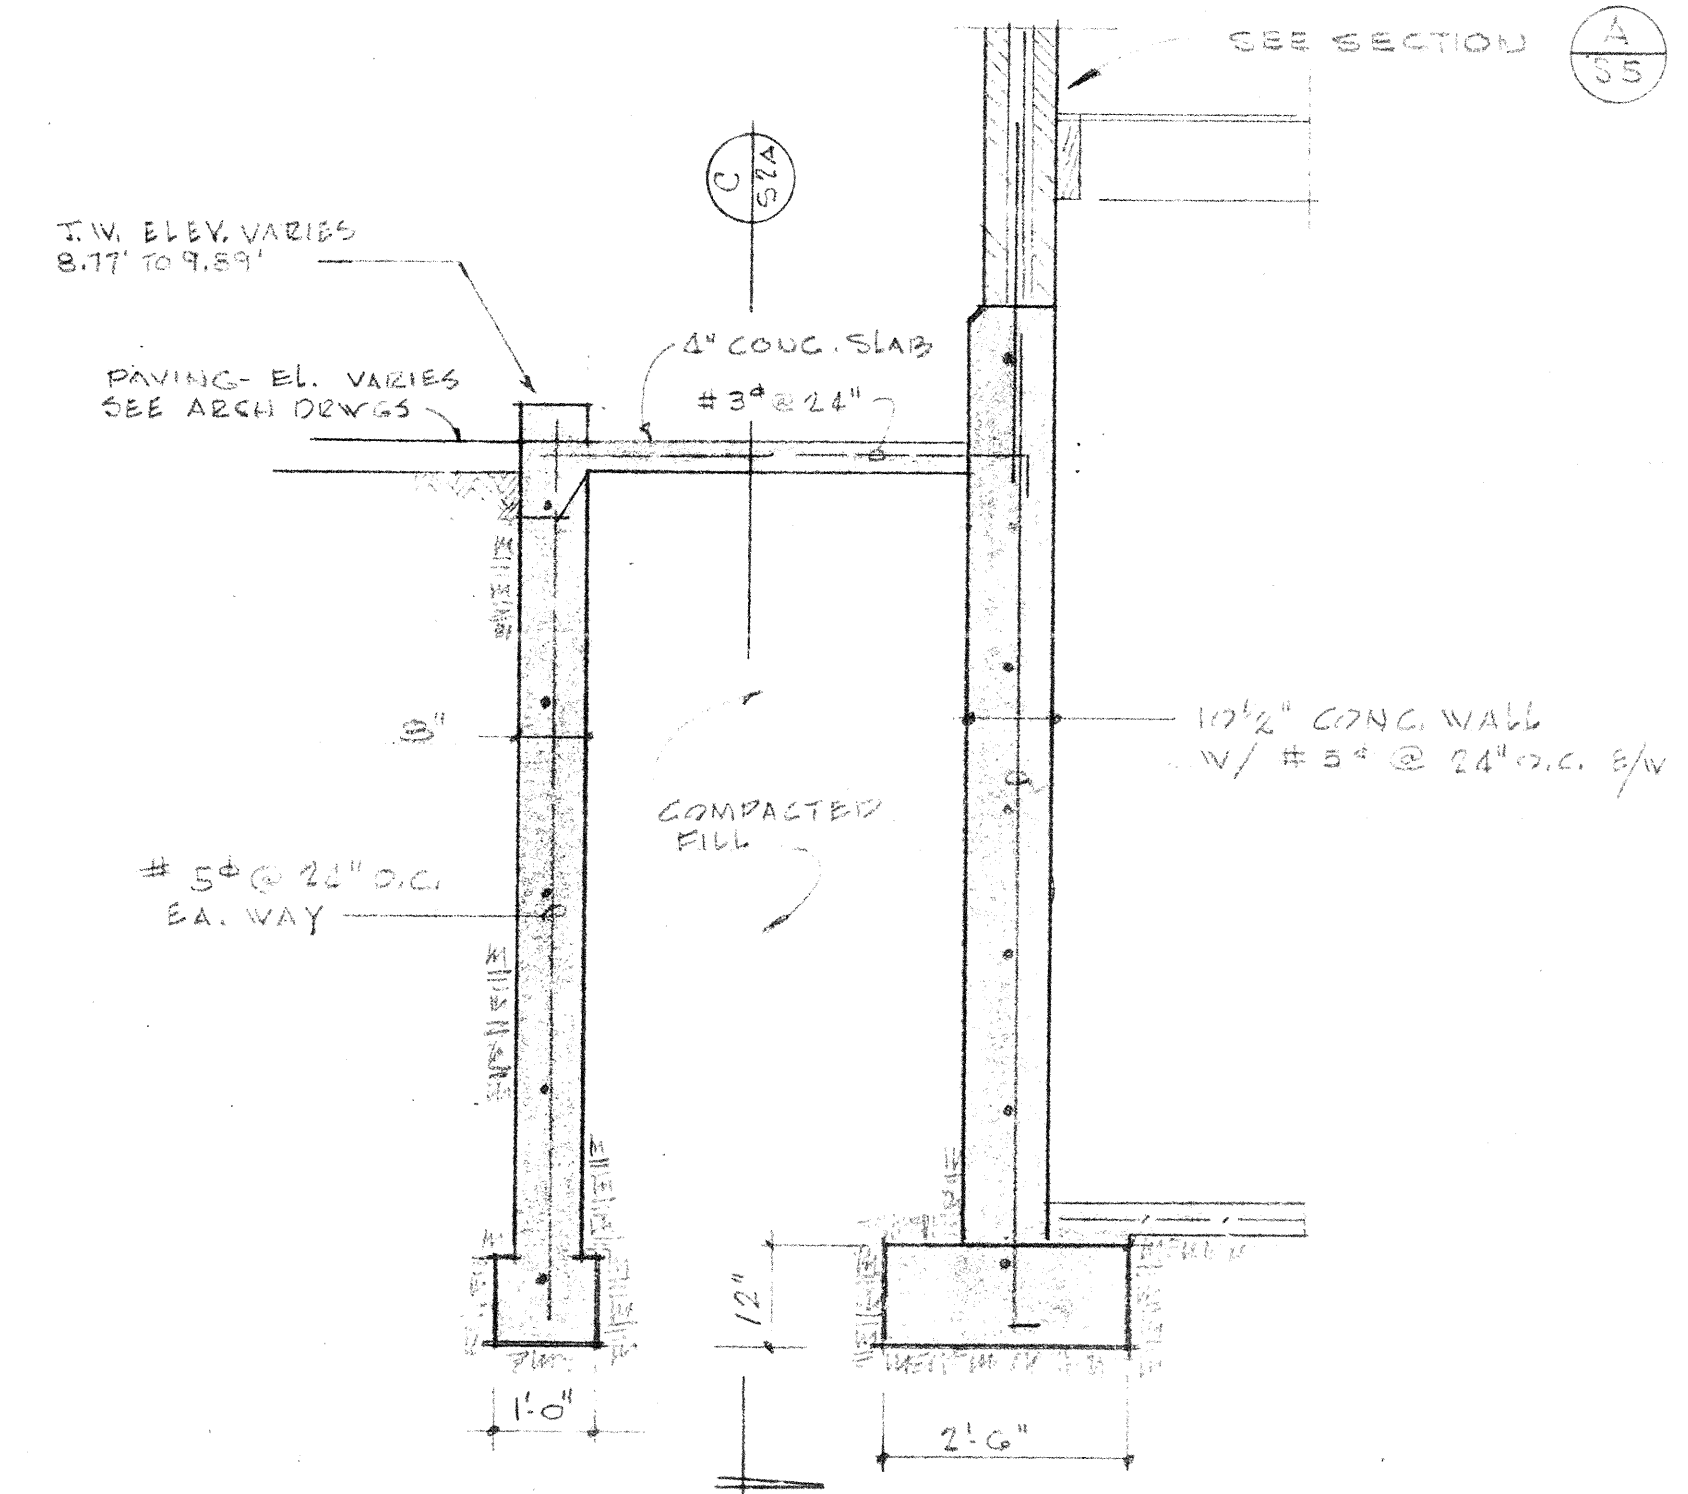

SECTION

(F)
S7

STRUCTURAL SECTIONS

REVISION:	PARISH HALL ADDITION	DATE:	12-30-25
FOR:	ST. EDMUND'S EPISCOPAL CHURCH	BY:	BREO FREEMAN
PROJECT:	1175 SAN GABRIEL BLVD. SAN MARINO, CALIFORNIA	ARCHITECT:	45 SOUTH MARENGO
DATE:	12-30-25	PASADENA 1, CALIFORNIA	927
			S-7
			of 9