

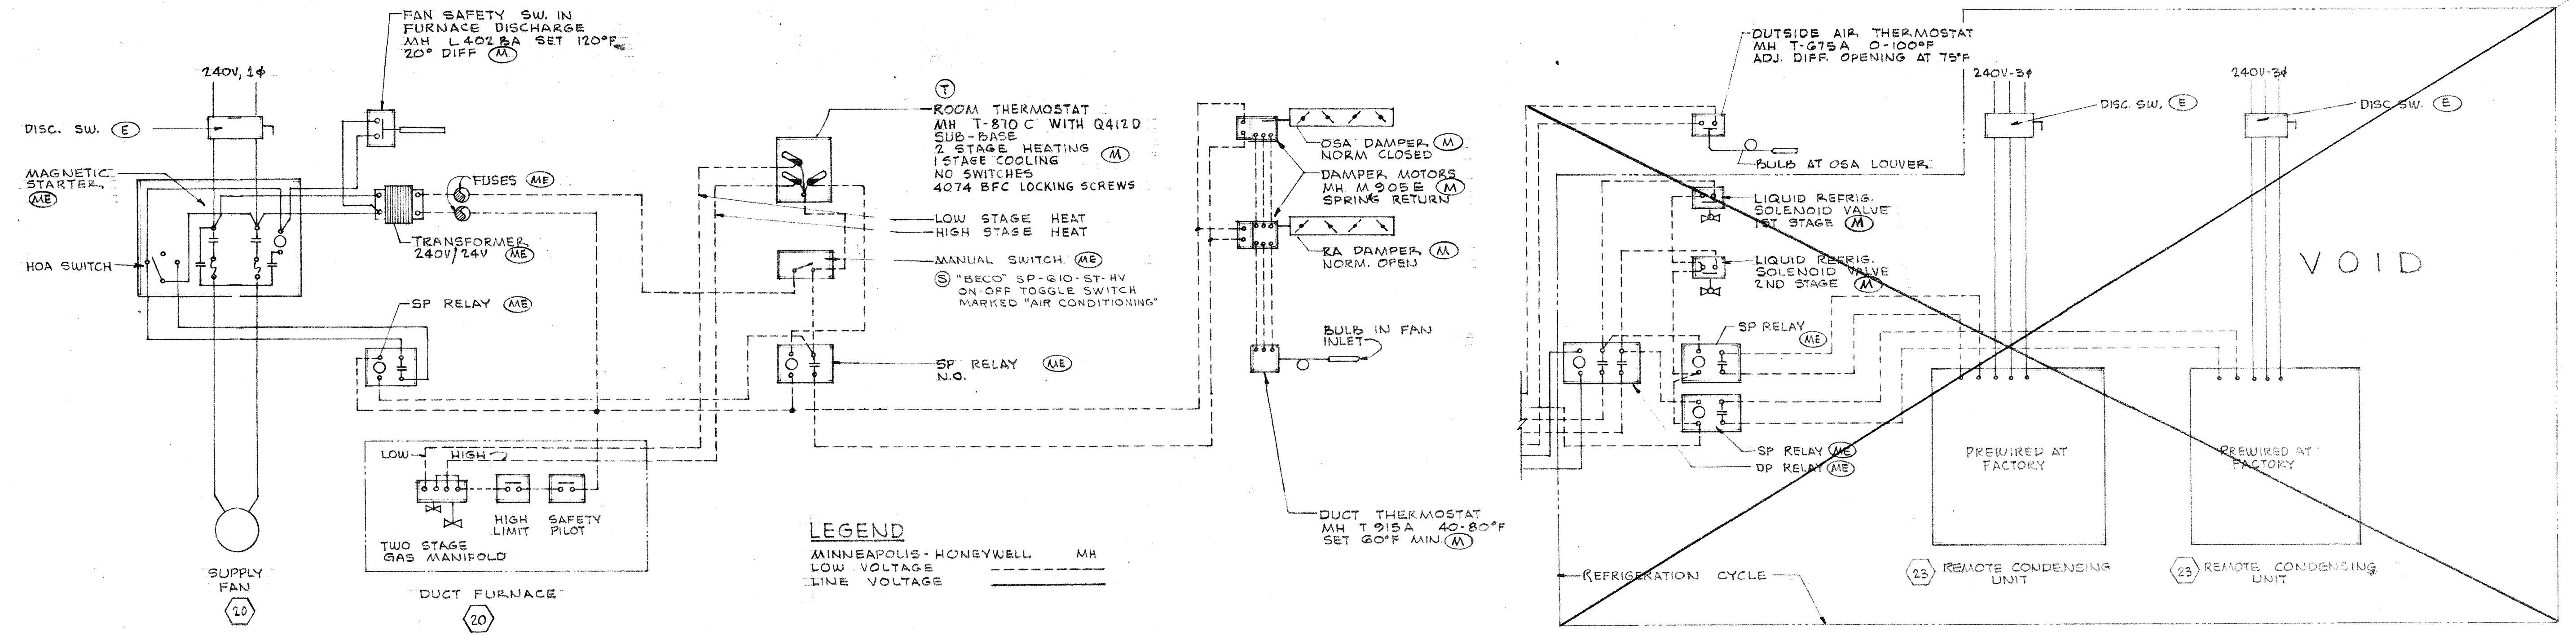


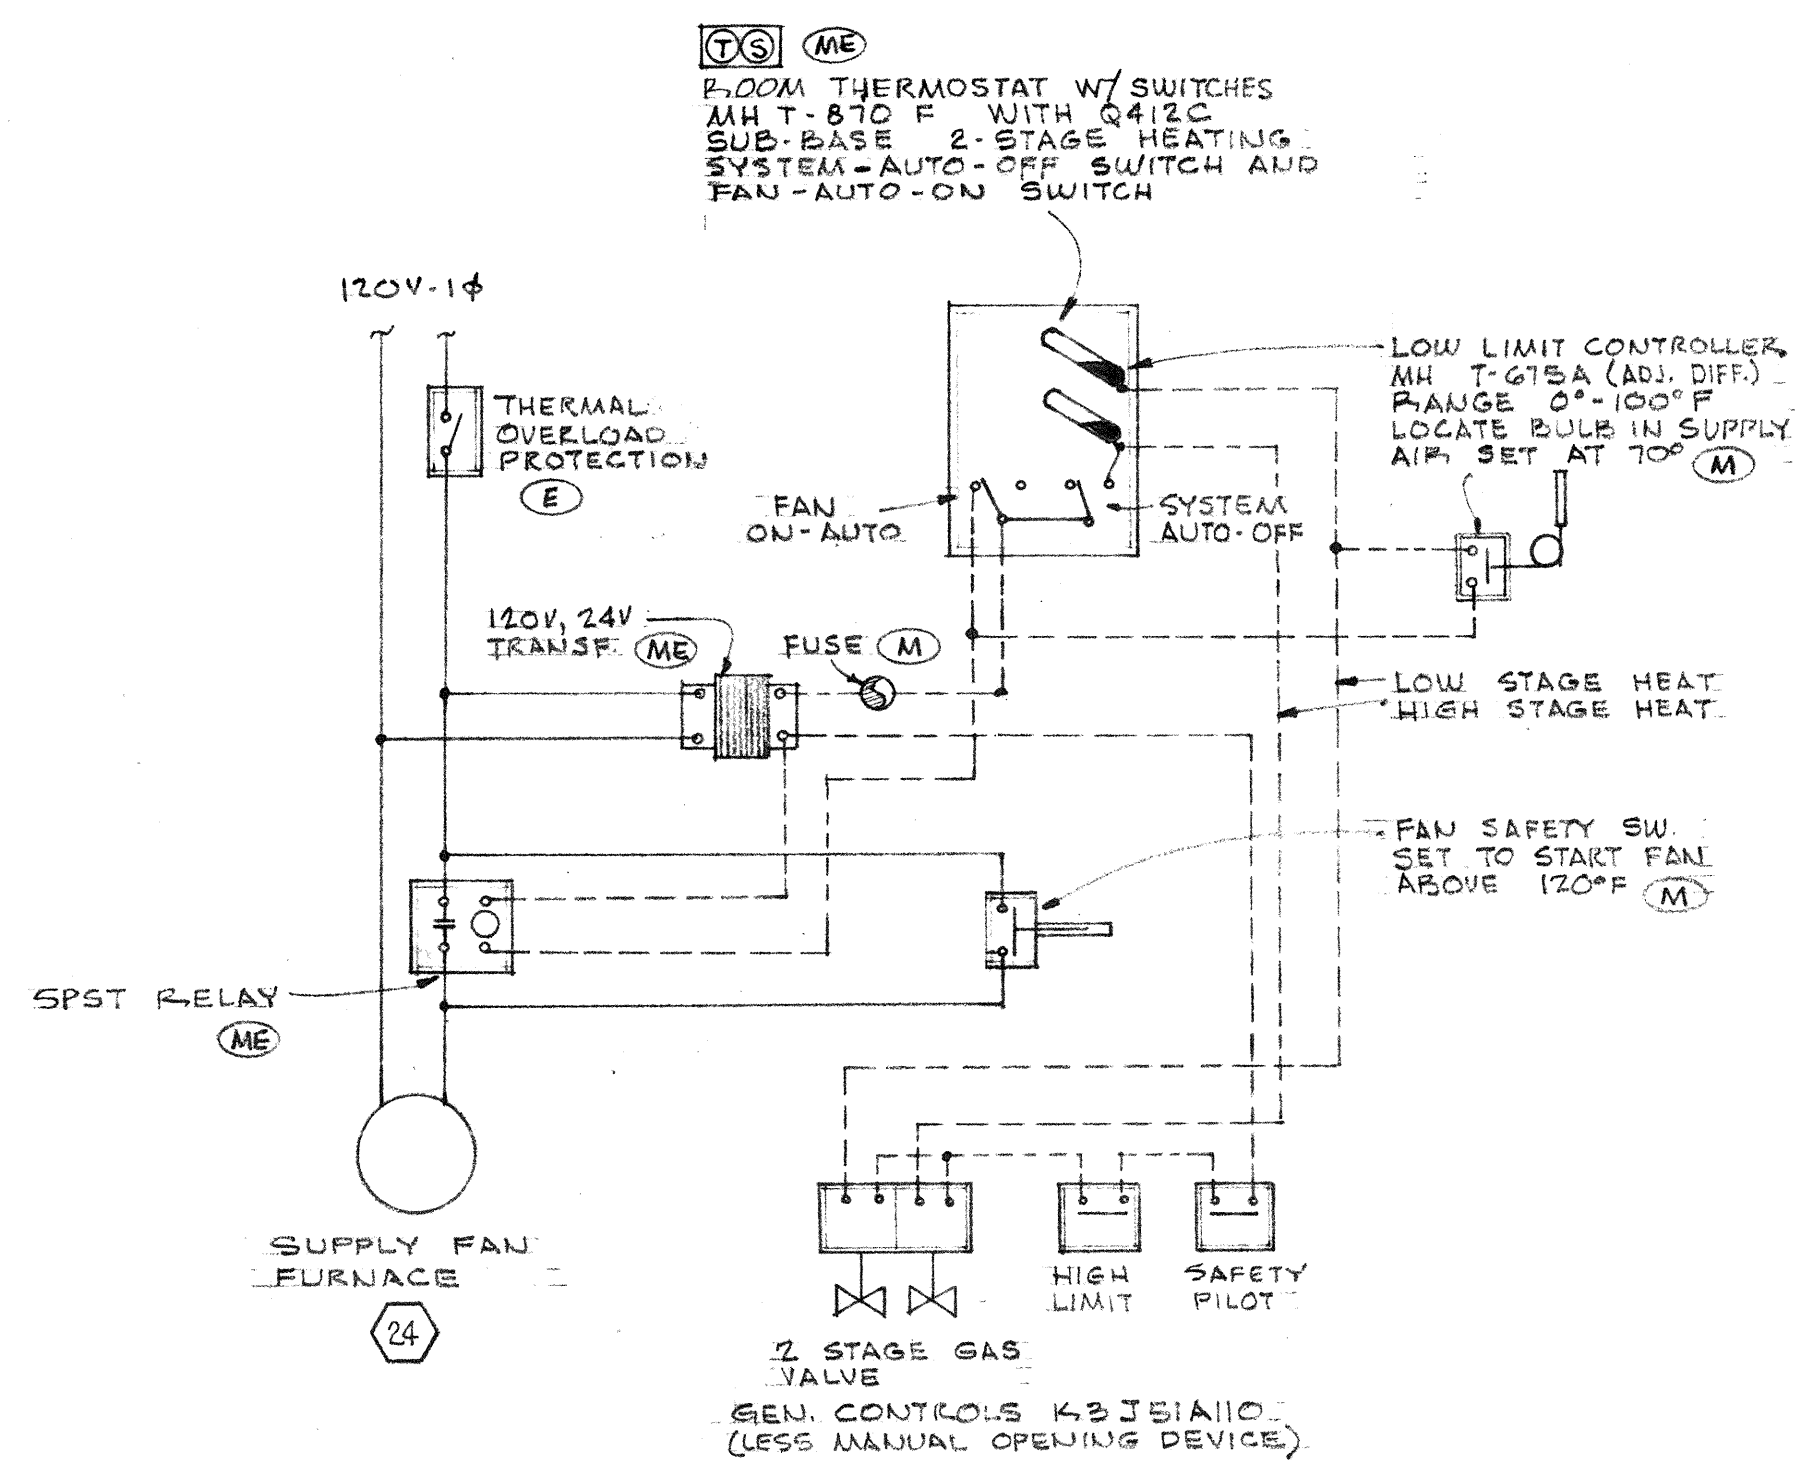


C O N T R O L D I A G R A M

SCALE NONE (A)

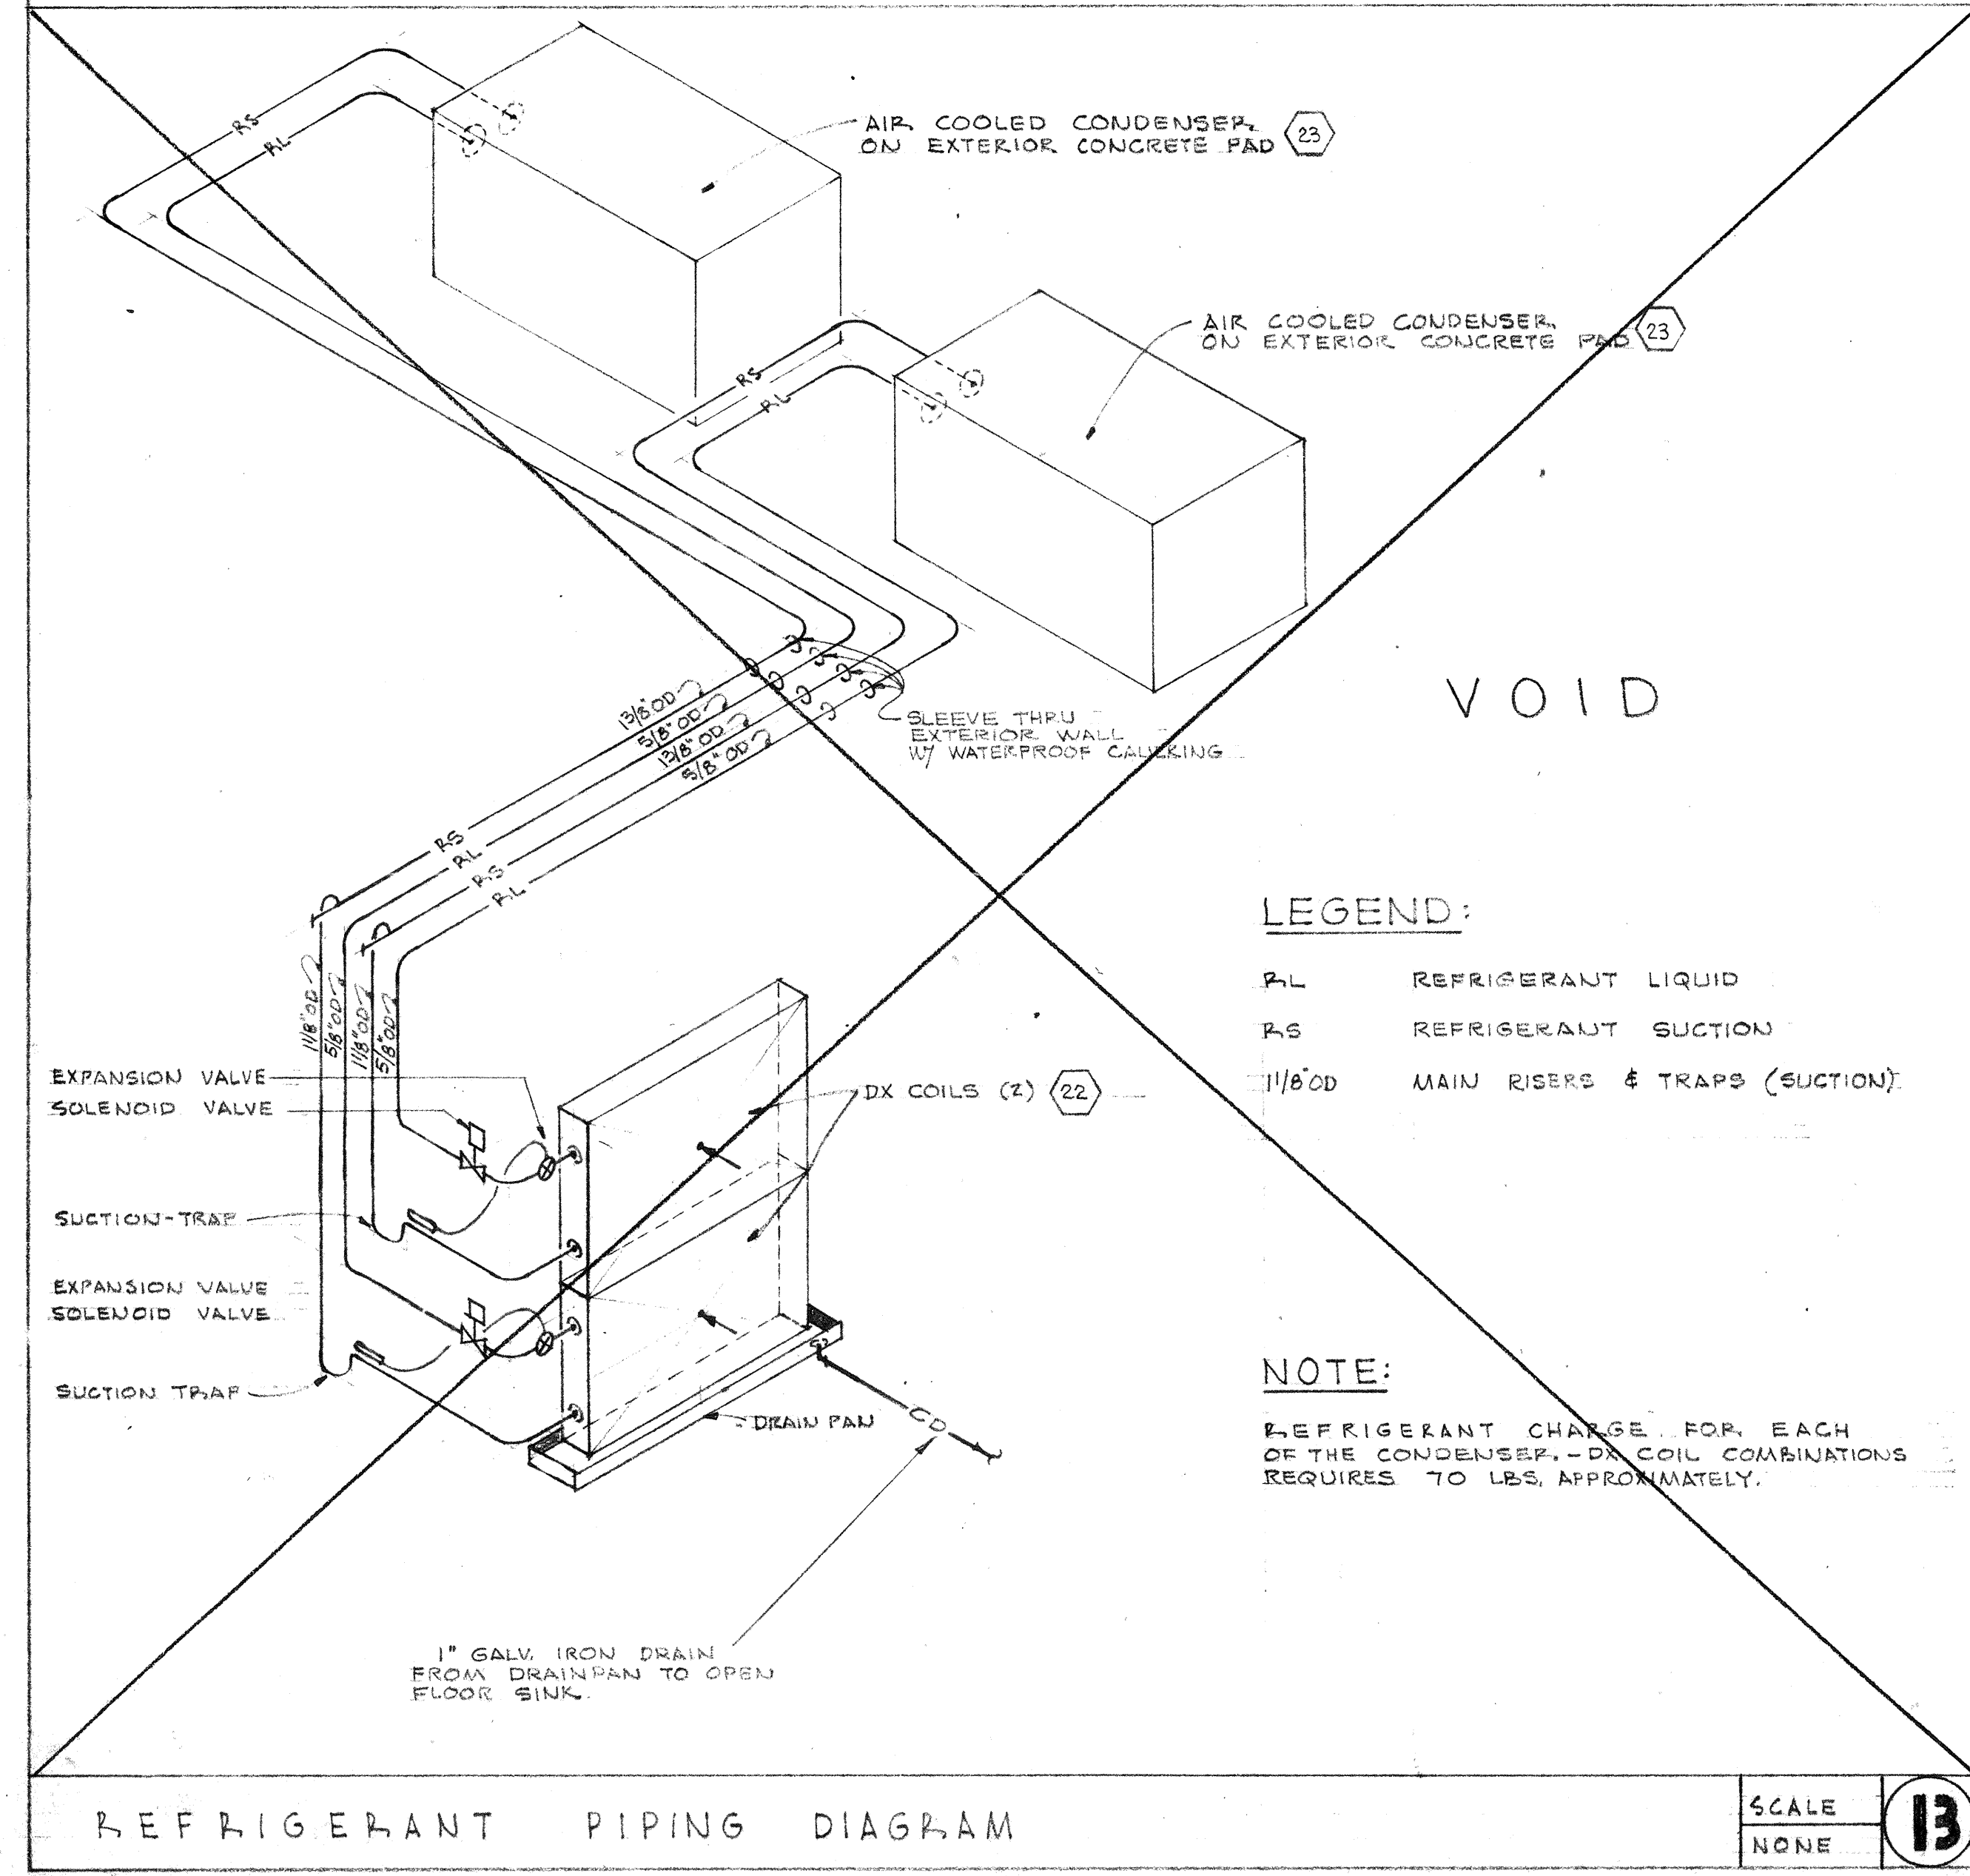

FURNACE CONTROL DIAGRAM

SCALE NONE (C)

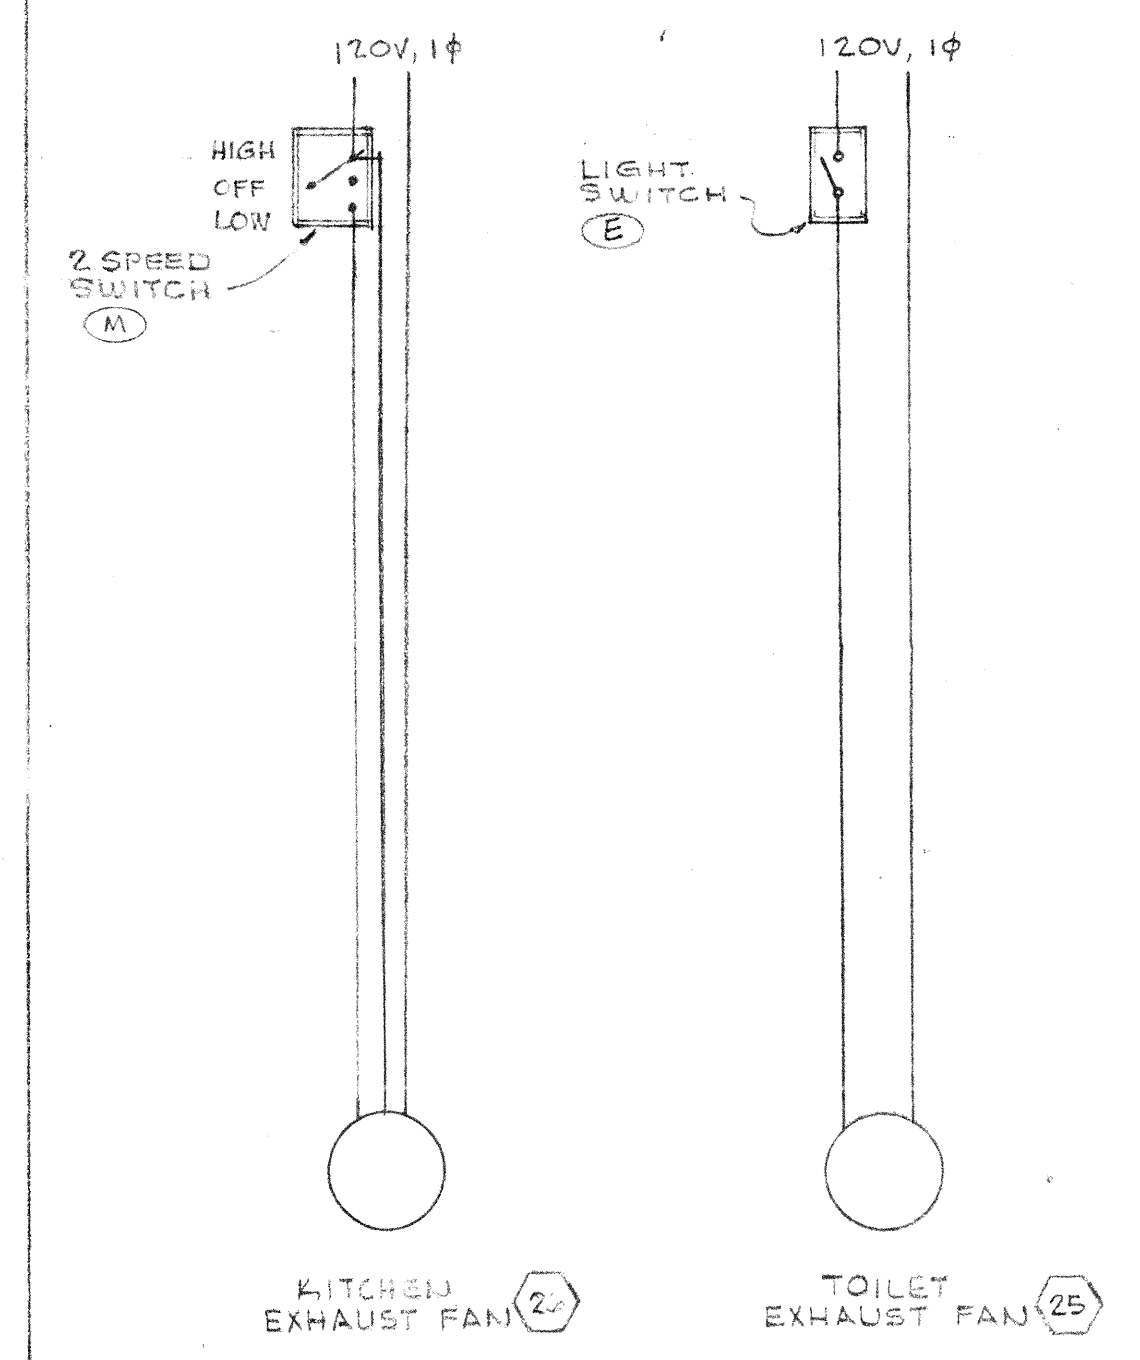

KITCHEN & TOILET EXHAUST FAN CONTROL DIAGRAMS

SCALE NONE (D)

CONTROL AND PIPING DIAGRAMS

|   |  |                      |   |  |
|---|--|----------------------|---|--|
| THOMAS H. PARRY & ASSOCIATES<br>CONSULTING MECHANICAL ENGINEERS<br>327 NORTH LAKE AVENUE<br>PASADENA, CALIFORNIA |  | REVISIONS<br>3-31-65 | PARISH HALL ADDITIONS<br>FOR<br>ST. EDMUND'S EPISCOPAL CHURCH<br>1175 SAN GABRIEL BLVD., SAN MARINO, CALIFORNIA |  |
| BREO FREEMAN<br>ARCHITECT<br>45 SOUTH MARENGO<br>PASADENA 1, CALIFORNIA                                          |  | 927<br>AC-3<br>OF 2  |   |  |