


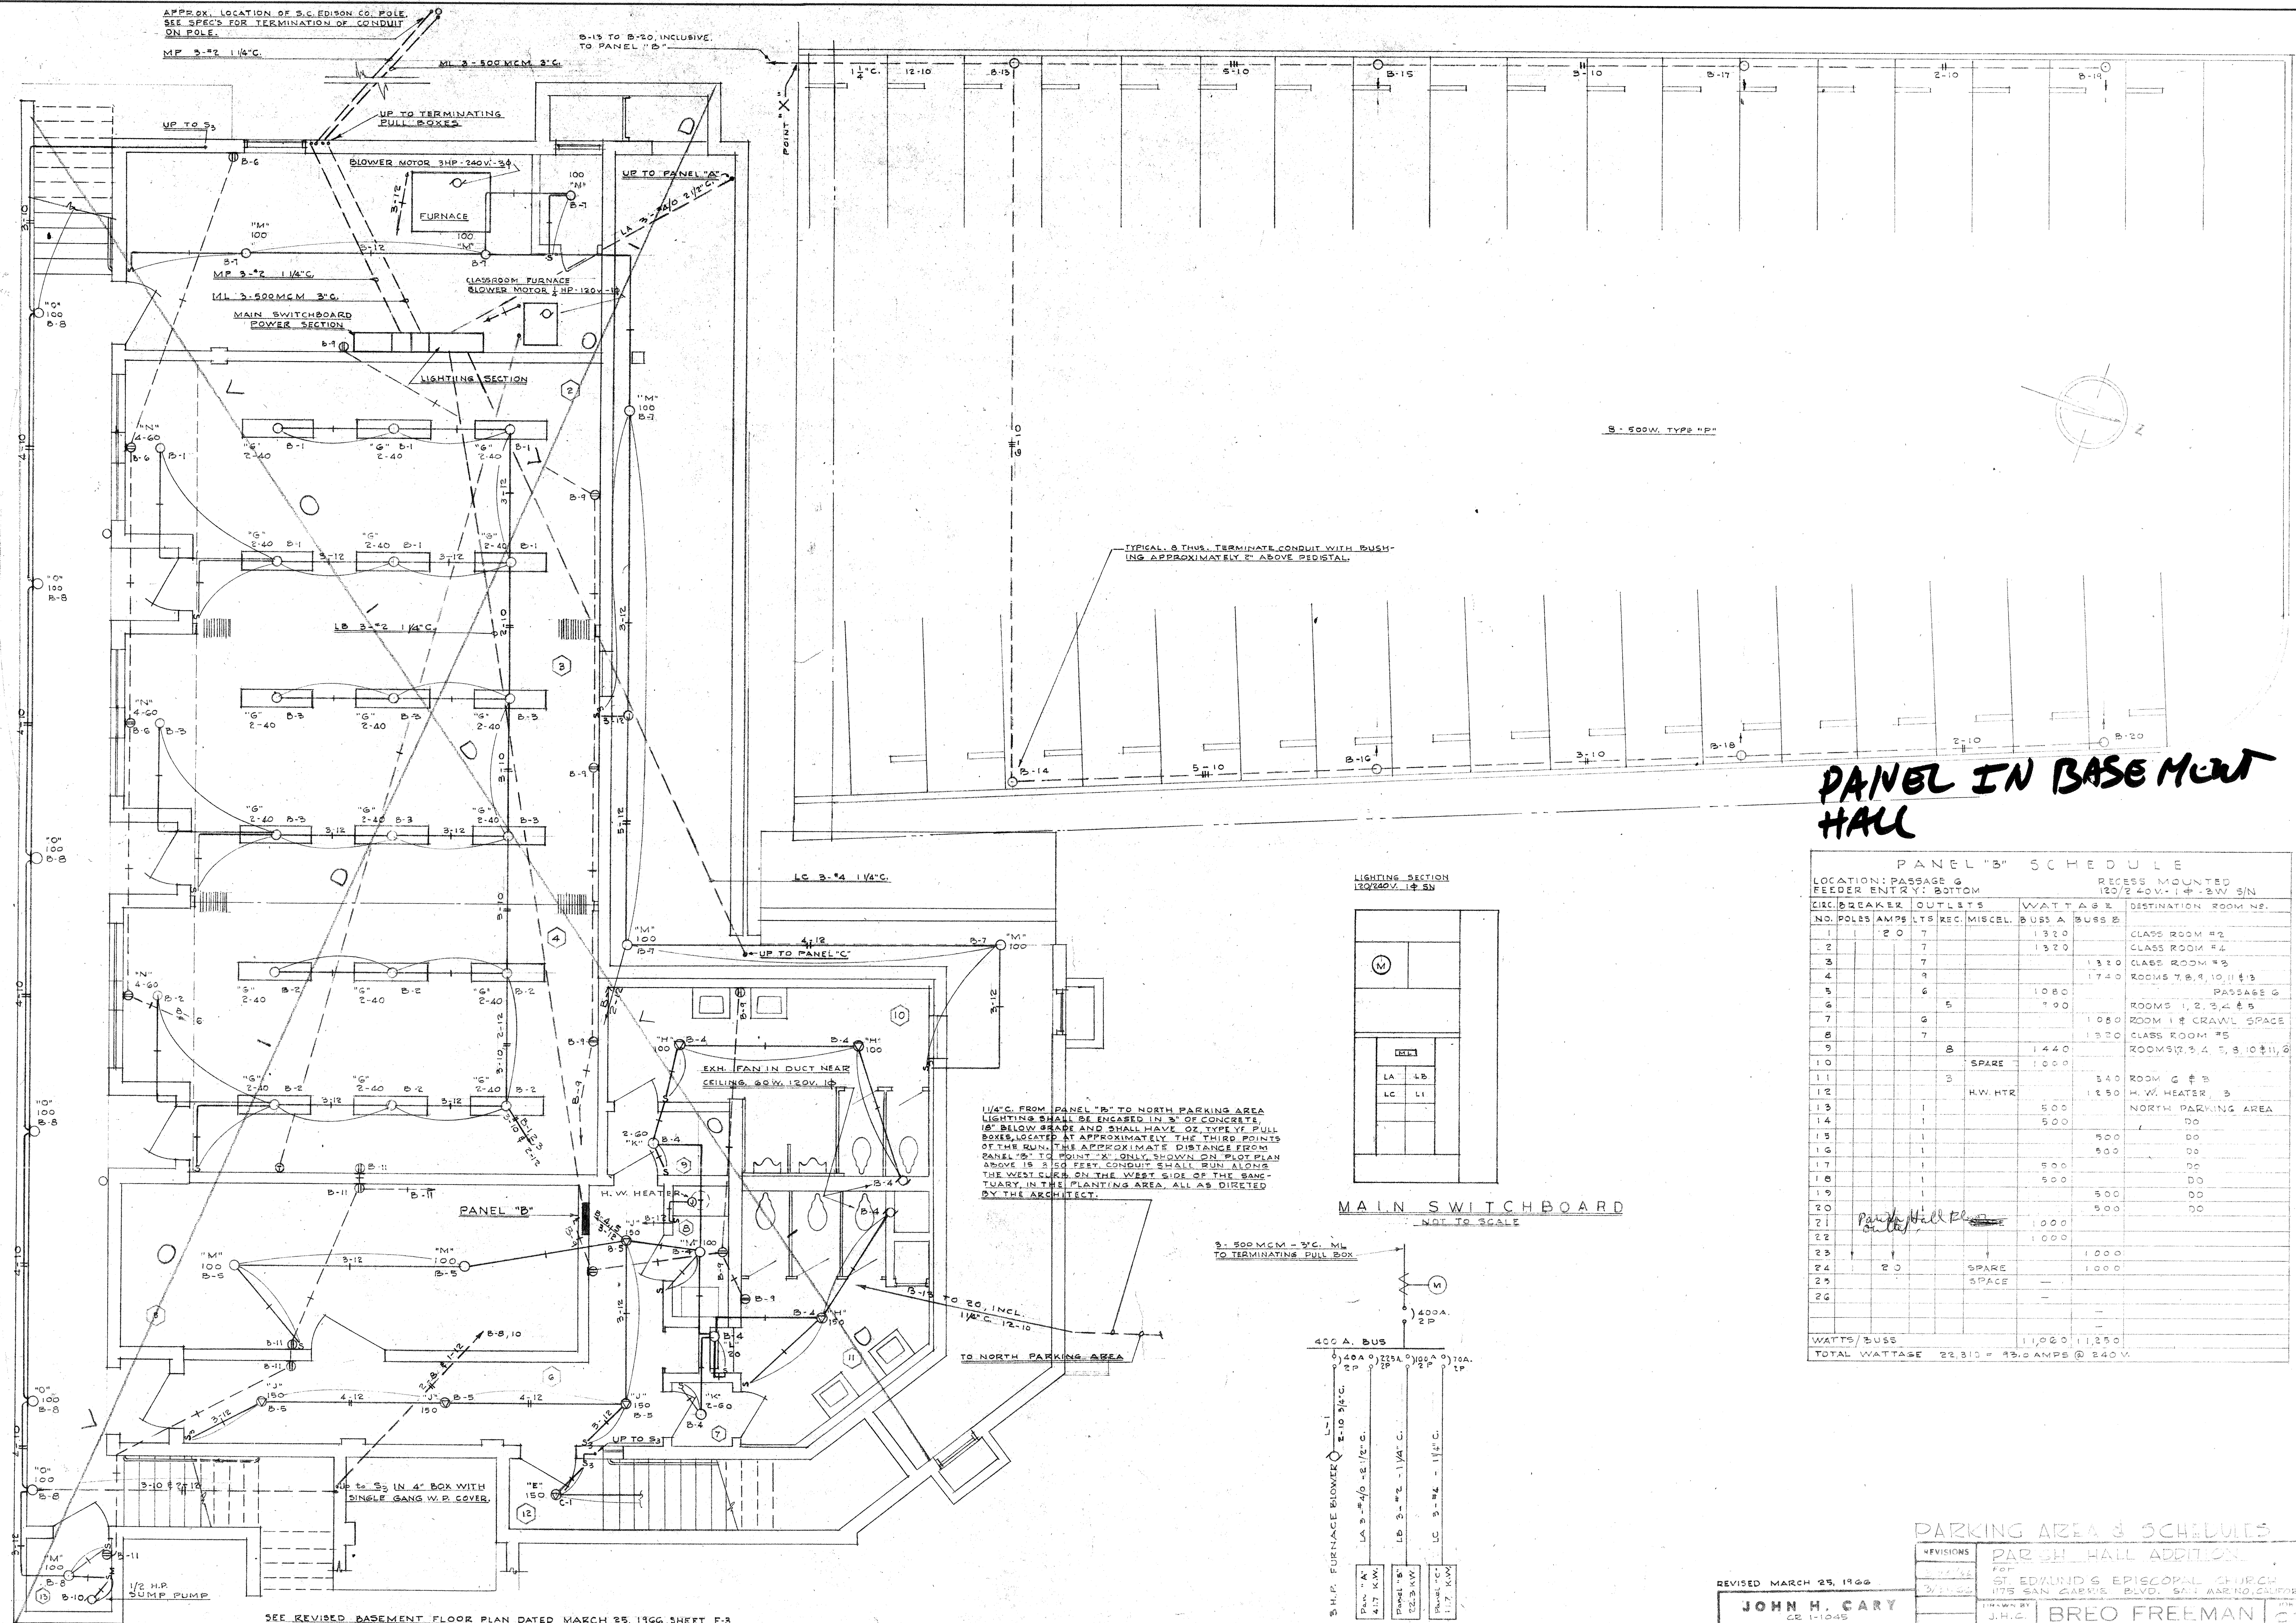

SEE REVISED BASEMENT FLOOR PLAN DATED MARCH 25, 1966, SHEET E-3

B A S E M E N T F L O O R

SCALE 1/4" = 1'-0"

F E E D E R D I A G R A M

PANEL "B" SCHEDULE									
LOCATION: PASSAGE G					RECESS MOUNTED				
FEED ENTRY: BOTTOM					120/240V. 1P-3W 5N				
CIRCUIT BREAKER OUTLSTS					WATTAGE DESTINATION ROOM NO.				
NO.	POLES	AMPS	LTS	REC.	MISC.	BUSS A	BUSS B		
1	1	20	7			1320		CLASS ROOM #2	
2	1		7			1320		CLASS ROOM #4	
3	1		7				1320	CLASS ROOM #5	
4	1		9				1740	ROOMS 7,8,9, 10, 11 & 12	
5			6			1080		PASSAGE G	
6				5		700		ROOMS 1,2,3,4 & 5	
7			7				1080	ROOM 1 & CRAWL SPACE	
8			7				1320	CLASS ROOM #5	
9				8		1440		ROOMS 7,8,9, 5, 8, 10 & 11, 12	
10					SPARE	1000			
11				3			540	ROOM G & B	
12					H.W. HTR		1350	H. W. HEATER 3	
13			1			500		NORTH PARKING AREA	
14			1			500		DO	
15			1				500	DO	
16			1				500	DO	
17			1			500		DO	
18			1			500		DO	
19			1				500	DO	
20							500	DO	
21						1000			
22						1000			
23							1000		
24			20		SPARE		1000		
25					SPARE				
26									
						11000	11350		
WATTS/BUSS									
TOTAL WATTAGE 22,310 = 130 AMPS @ 240 V.									

REVISIONS		PARISH HALL ADDITION	
1-11-66		FOR ST. EDWARD'S EPISCOPAL CHURCH	
2-15-66		1175 SAN GABRIEL BLVD. SAN MARINO, CALIFORNIA	
DRAWN BY J.H.C.		BRET FREEMAN	
CHECKED BY		ARCHITECT	
DATE 12-30-68		45 SOUTH MARENGO PASADENA 1, CALIFORNIA	
		SHEET NO. 1 OF 5	