



ML 3 - 500 MCM 3" C

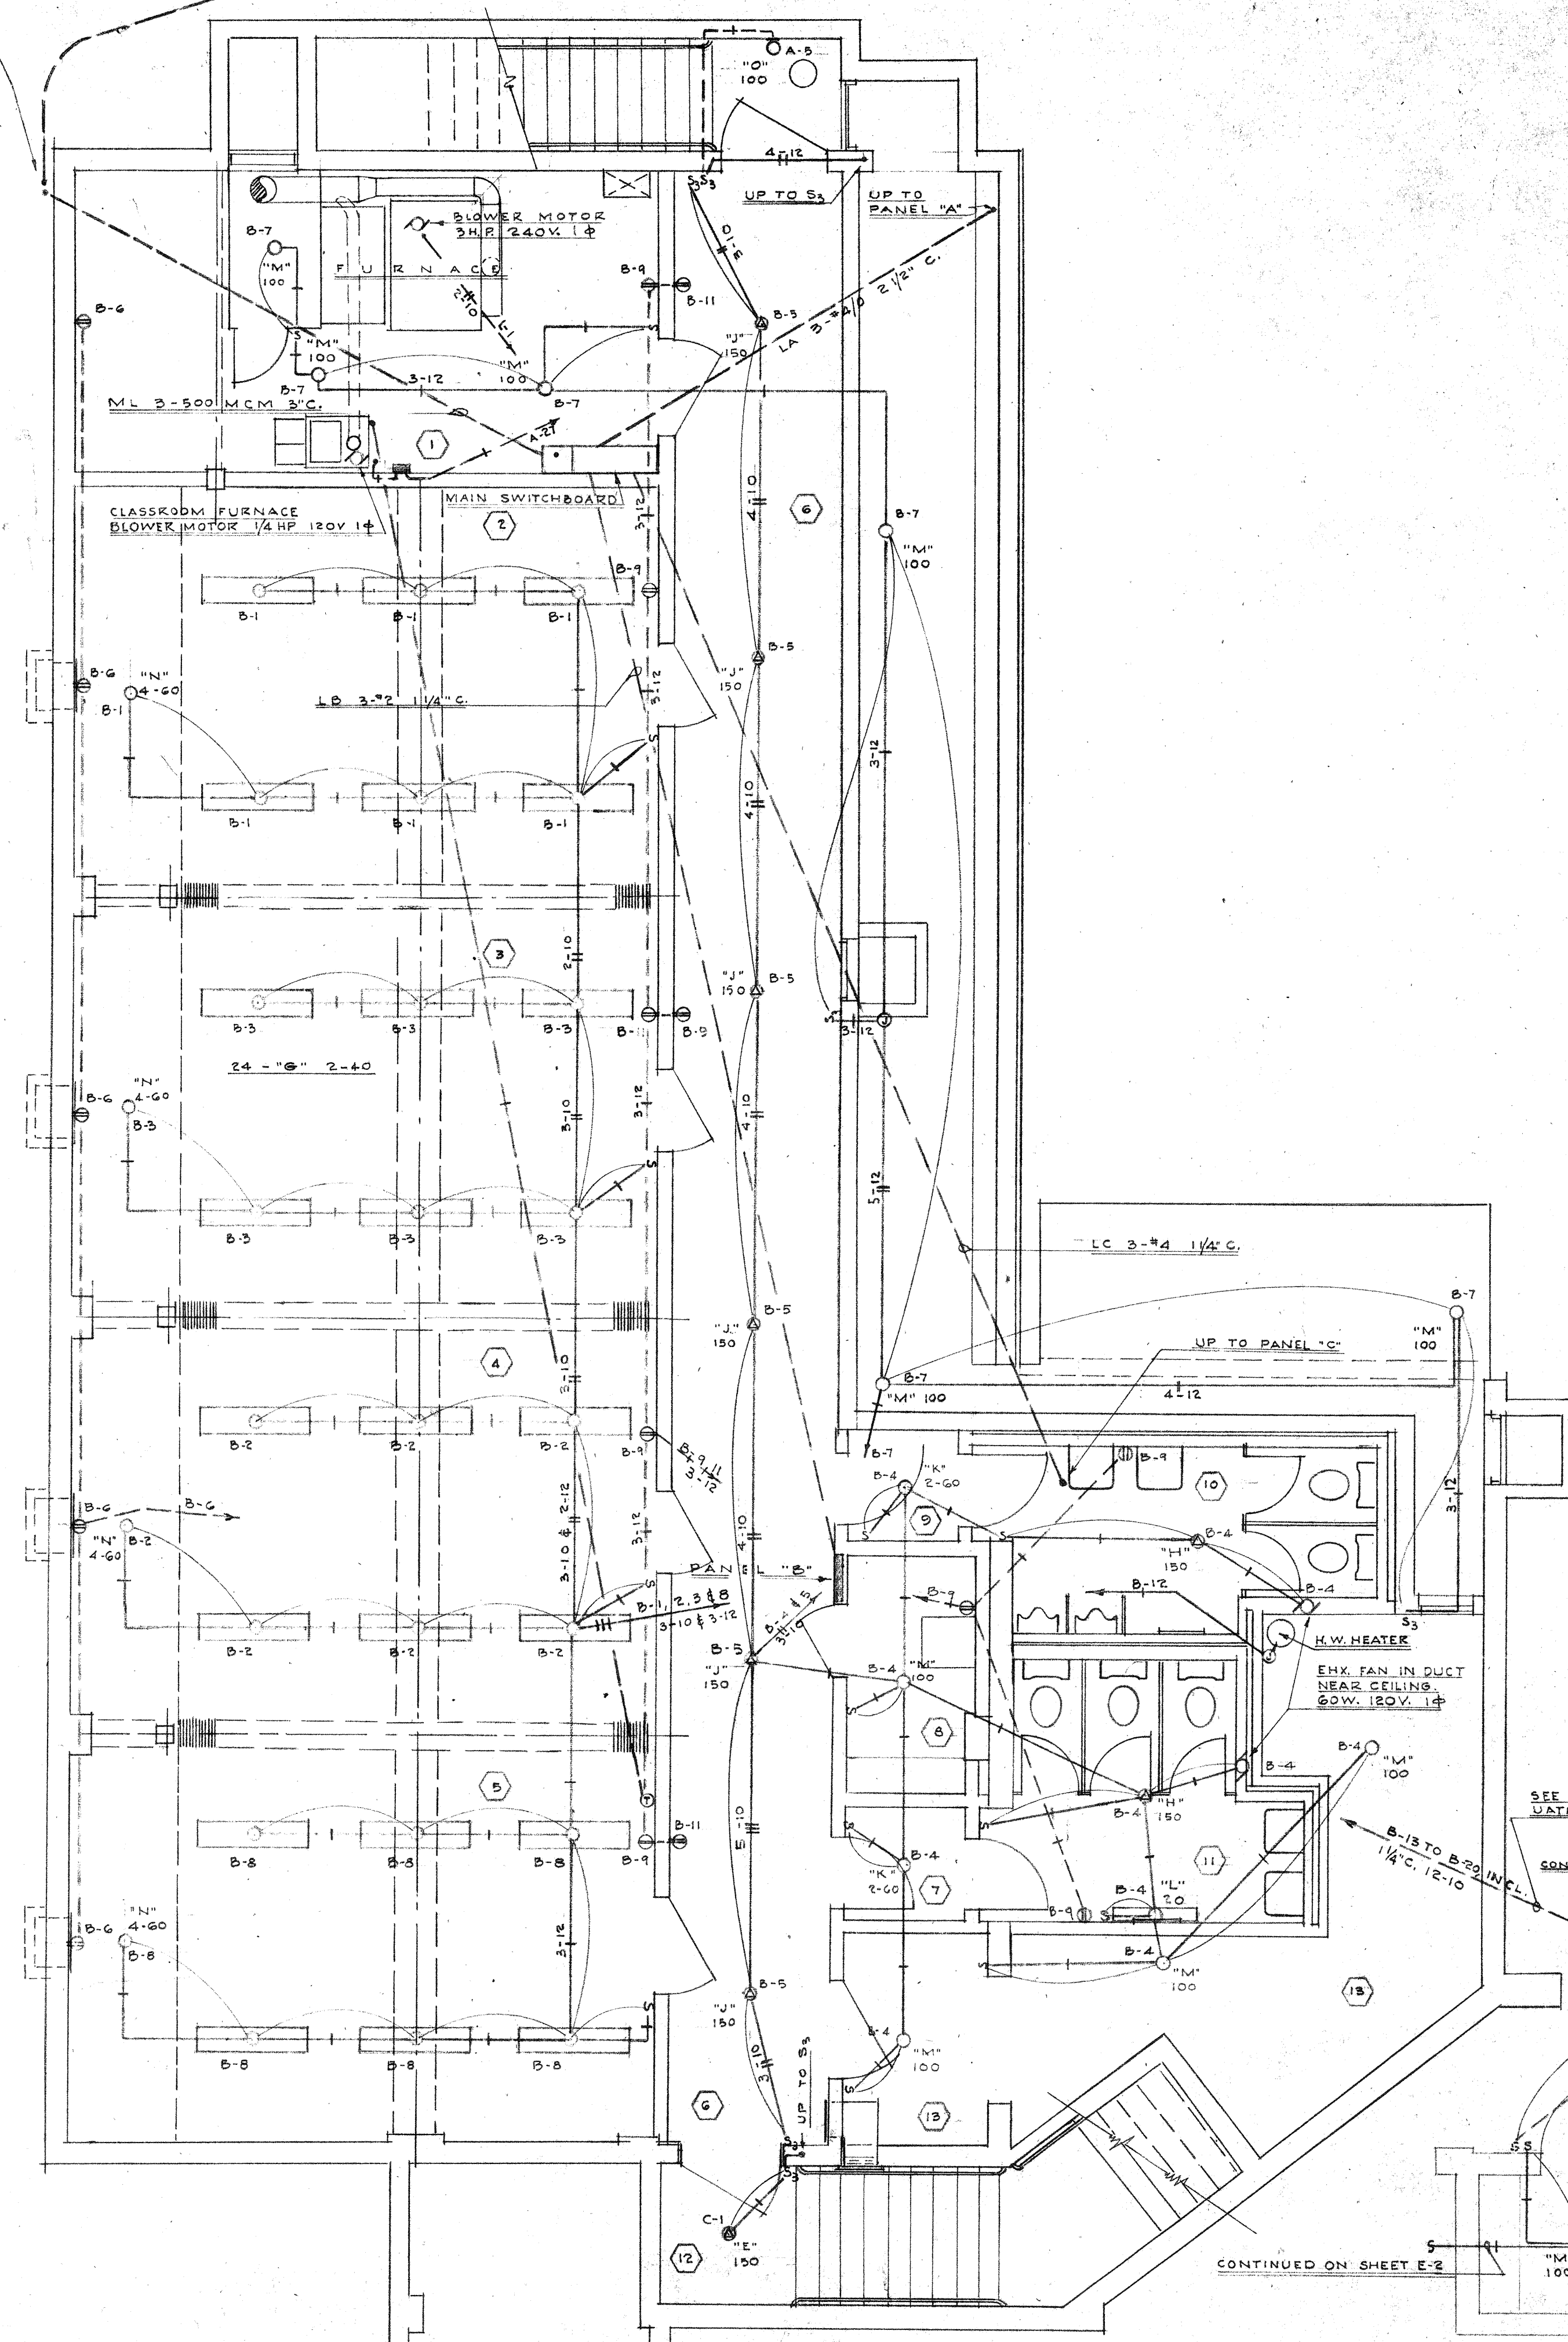

B A S E M E N T P L A N

S C A L E 1/4" = 1'-0"

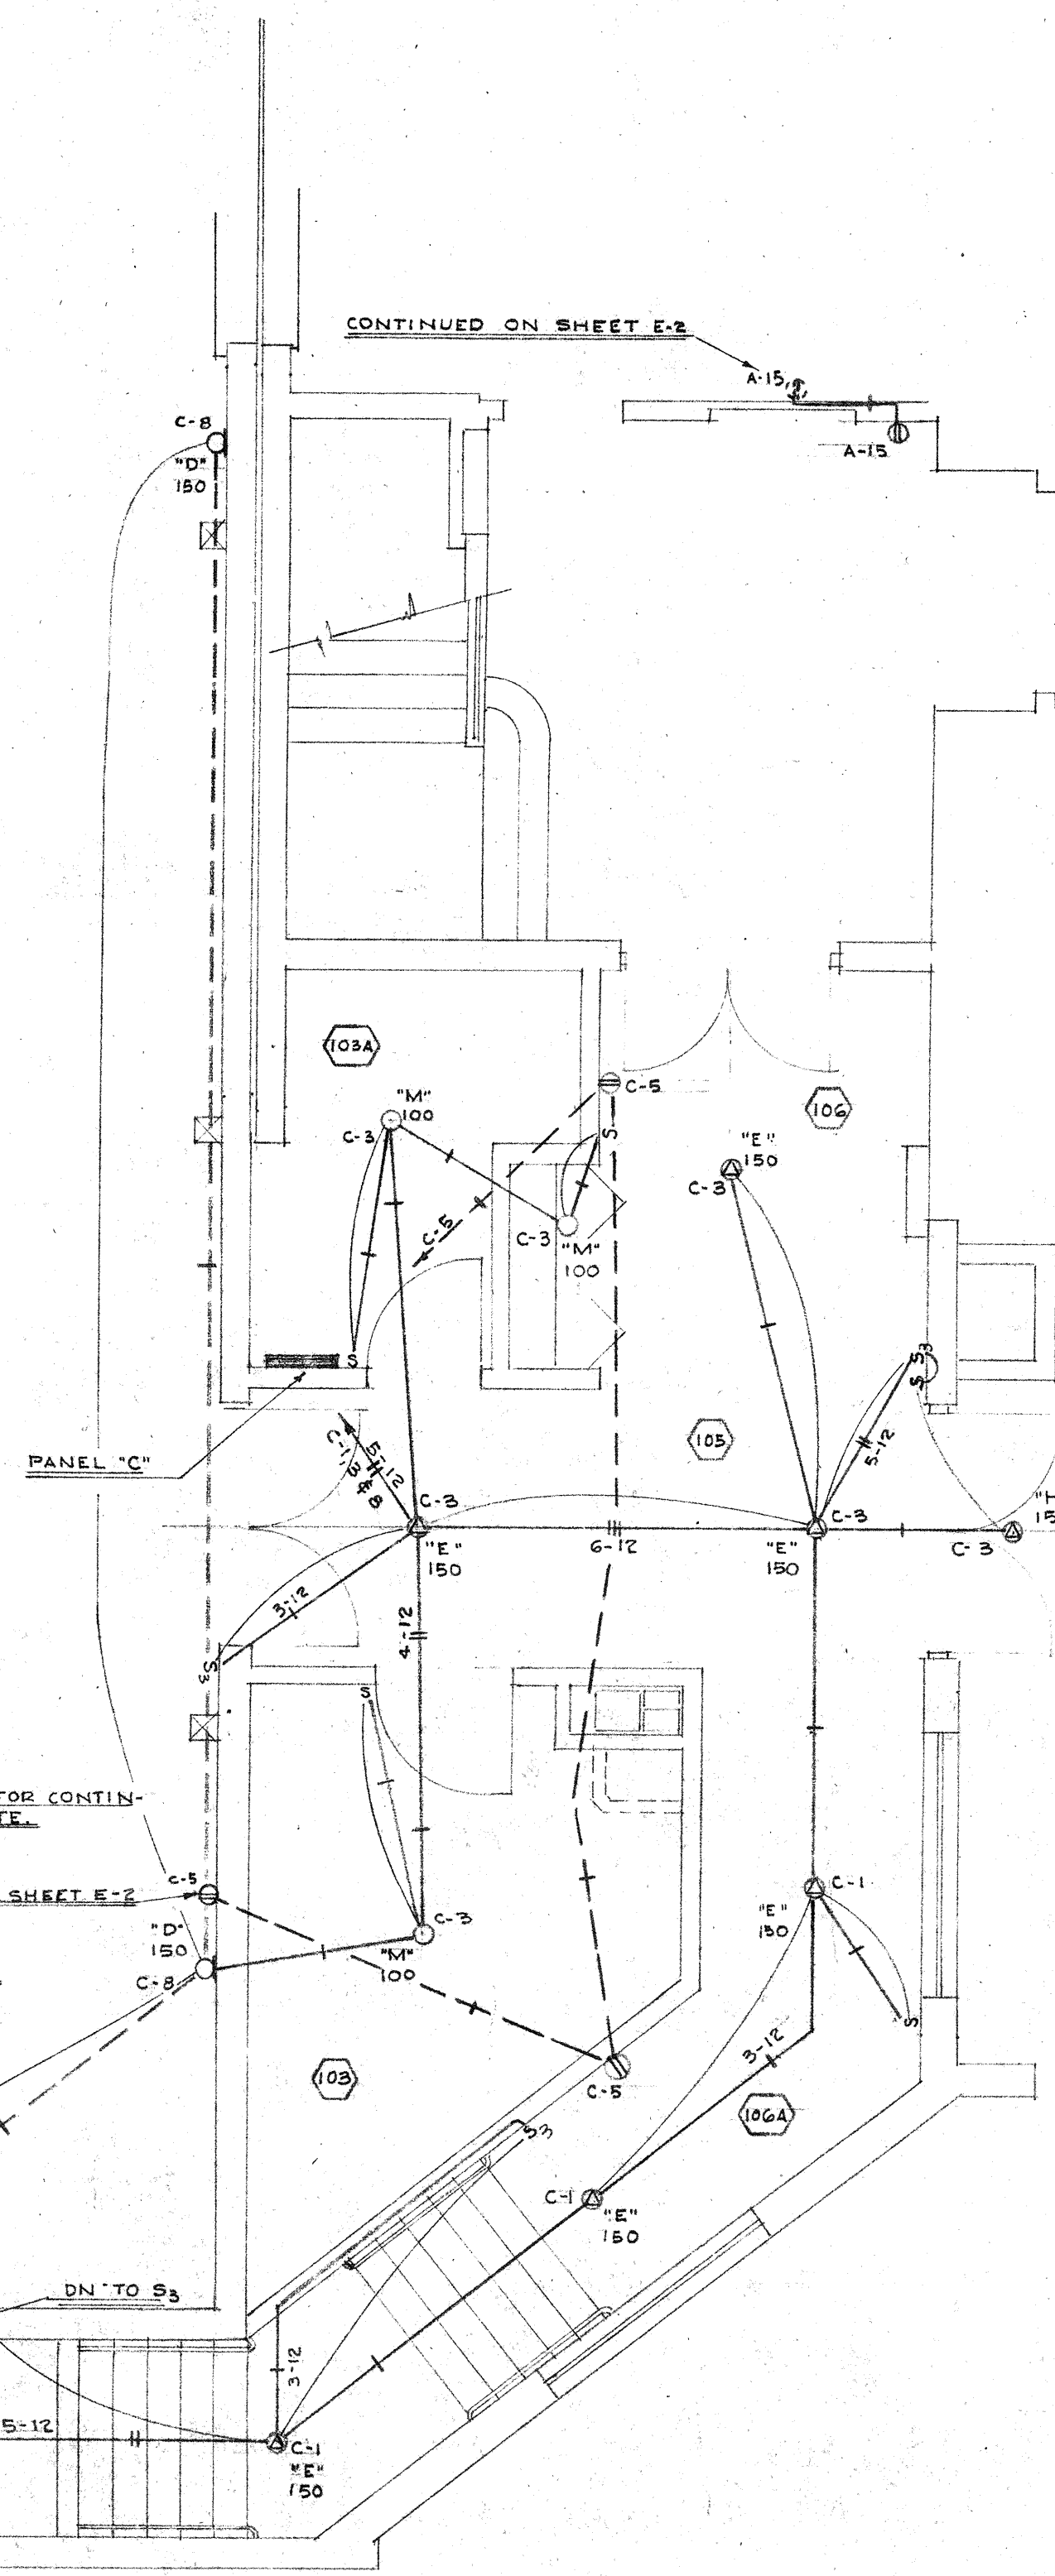

GROUND FLOOR

S C A L E 1/4" = 1'-0"

c 3 has
cub. 150
150
150
100 } closed
100 }

REVISÉD BASEMENT & PORTION OF GROUND FLOOR

7	4	REVISIONS	PARISH HALL ADDITION	DATE	3.25/66	FILE NO.	927
6	3	FOR	ST. EDMUND'S EPISCOPAL CHURCH	DATE	3.25/66	FILE NO.	927
5	2	BY	SAN CARLOS BLVD. SAN MARINO, CALIF.	DATE	3.25/66	FILE NO.	927
4	1	DRAWN BY	BREO FREEMAN	DATE	3.25/66	FILE NO.	927
3		J.H.C.	ARCHITECT	DATE	3.25/66	FILE NO.	927
2		TRACED BY	45 SOUTH MARENGO	DATE	3.25/66	FILE NO.	927
1			PASADENA 1, CALIFORNIA	DATE	3.25/66	FILE NO.	927