
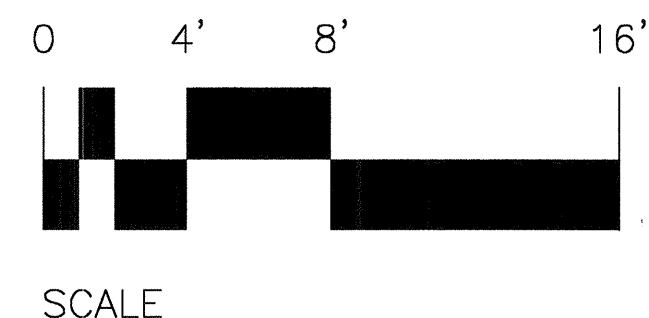
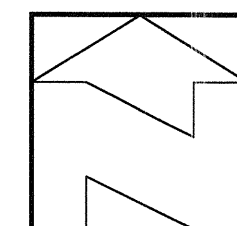
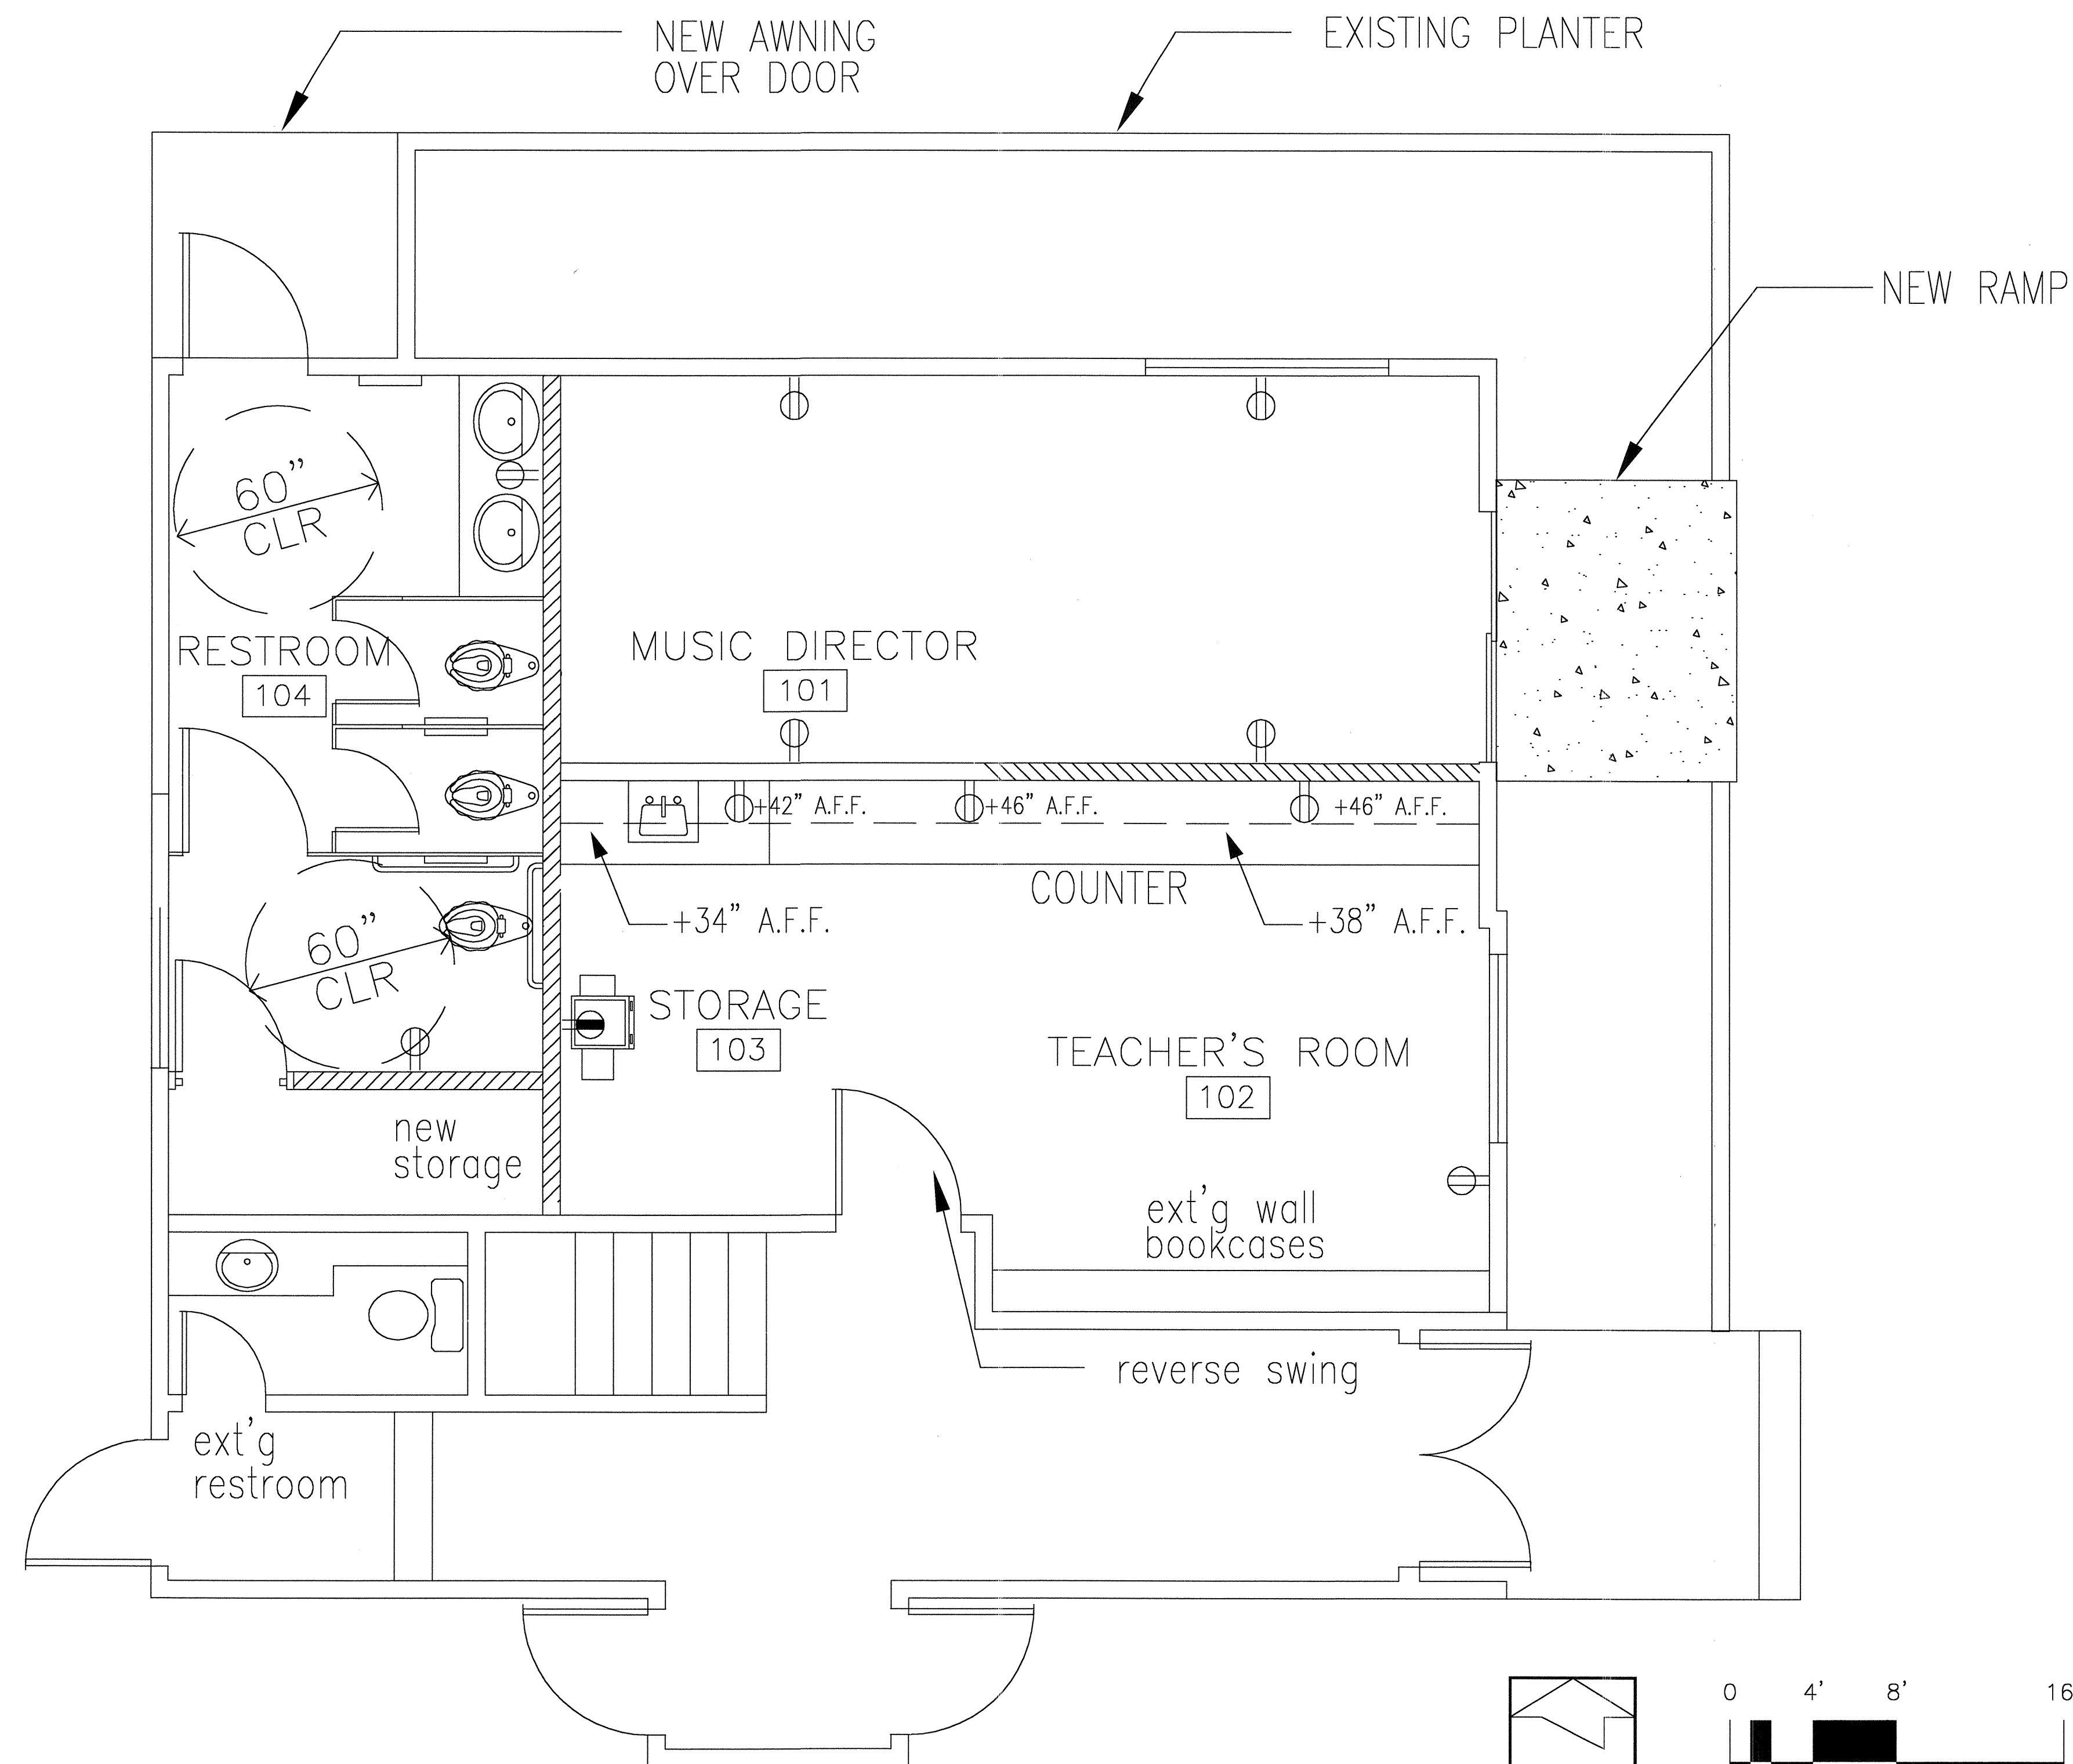


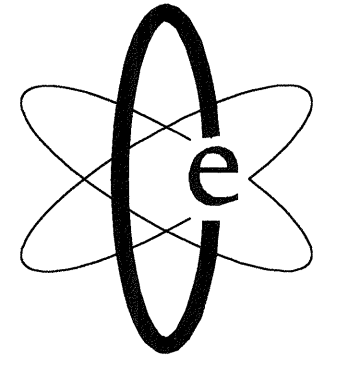

LEGEND	
***ALL DEVICES ARE NEW UNLESS NOTED OTHERWISE	
E	EXISTING DEVICE TO REMAIN
⊙	BLANK PLATE
⊕	DEDICATED QUADROPLEX OUTLET
▽	DATA/PHONE OUTLET
⊕	DUPLEX OUTLET
⊕	DEDICATED DUPLEX OUTLET
⊕	QUADROPLEX OUTLET

POWER & TELEPHONE NOTES:	
1.	ALL ELECTRICAL WORK SHALL BE DONE UNDER THE PRESENT LAWS, REGULATIONS, ORDINANCES, AND ADOPTED CODES OF THE CITY OF LOS ANGELES.
2.	ELECTRICAL CONTRACTOR SHALL PROVIDE NYLON PULL STRINGS IN ALL EMPTY CONDUITS.
3.	THE CENTER OF ALL NEW RECEPTACLES AND OUTLETS SHALL BE INSTALLED 18" ABOVE THE FLOOR, UNLESS OTHERWISE NOTED. THE CENTER HEIGHT OF ALL SWITCHES SHALL BE 4'0" MAXIMUM ABOVE THE FLOOR.
4.	ALL TEL/DATA CABLES IN PLENUM AREA MUST BE TEFLON.
5.	NO "BACK-TO-BACK" OUTLETS ARE PERMITTED WITHIN A WALL. OUTLETS MUST BE STAGGERED IN LOCATION. WHERE RECEPTACLES AND OUTLETS ARE SHOWN SIDE-BY-SIDE ON THE PLAN, THEY SHALL BE PLACED 6" ON CENTER APART.
6.	GROUPED OUTLETS SHALL BE LOCATED 6" O.C. UNLESS OTHERWISE INDICATED.
7.	LOCATION OF ALL REQUIRED EXIT SIGNS TO BE VERIFIED BY LOCAL FIRE DEPARTMENT FIELD INSPECTOR PRIOR TO INSTALLATION.
8.	CONTRACTOR TO REROUTE AND PROVIDE PROTECTION FOR ALL EXISTING PHONE, COMPUTER AND ELECTRICAL WIRING WHICH MUST REMAIN ACTIVE DURING ALL PHASES OF CONSTRUCTION.
9.	ANY ACTIVE NON-PLENUM RATED CABLE SHALL BE PUT IN CONDUIT OR BE REPLACED WITH PLENUM RATED CABLE.
10.	DO NOT SCALE OUTLETS ON PLAN.
11.	CONTRACTOR TO REROUTE AND PROVIDE PROTECTION FOR ALL EXISTING PHONE, COMPUTER AND ELECTRICAL WIRING WHICH MUST REMAIN ACTIVE DURING ALL PHASES OF CONSTRUCTION.
12.	PROVIDE 2" CONDUIT FROM BUILDING TELEPHONE CLOSET TO TELEPHONE BACKBOARD AT COPY 1113.
13.	PROVIDE 3" CONDUIT STUB TO PLENUM FROM COPY 1113.

A	ISSUED FOR XXX	10.20.03
REVISION #	SUBMISSION	DATE
ST. EDMUNDS CHURCH NURSERY SCHOOL 2975 HUNTINGTON DR. SAN MARINO, CA		
 Creative Energy architecture and interiors 61 East Colorado Boulevard Suite 200 Pasadena California 91105 phone 626.304.0505 fax 626.304.0715		
DRAWING TITLE: POWER & TELEPHONE		
SEAL	DATE: 10.20.03	PROJECT NO: XXX
		SCALE: 3/8"=1'-0"
	DRAWING NUMBER	REVISION
	A-3	A